

1601 Fifth Avenue, Suite 1600
Seattle, WA 98101
206.622.5822
kpff.com

SUPERIMPOSED DEAD LOAD SCHEDULE			
TYPE MARK	DESCRIPTION	LOAD, PSF	TYPE COMMENTS
1	TYP ROOF	30	NOTE 7
2	TYPICAL FLOOR	15	-
3	CONCRETE TOPPING	90	-
4	CANOPIES	15	-
5	SKYLIGHT	10	-

LOAD SCHEDULE NOTES:

1. INDICATES LIVE LOAD AND SUPERIMPOSED DEAD LOAD PER SCHEDULES. LOADING OCCURS WITHIN REGIONS BOUND BY BOLD LINES.

2. (R) INDICATES LIVE LOADS ARE REDUCED IN ACCORDANCE WITH BUILDING CODE PROVISIONS.

3. **→ XX** INDICATES CLADDING SUPERIMPOSED DEAD LOAD APPLIED AT BUILDING PERIMETER IN POUNDS PER LINEAR FOOT.

4. EXTERIOR BALCONIES AND DECKS ARE DESIGNED FOR THE SAME LIVE LOAD AS THE OCCUPANCY SERVED.


5. SOIL INCLUDES 5 PSF FOR PV PANELS WHERE NOTED.

6. PAD = 40 PSF IN OPEN AREAS.

7. REFER TO TABLE 1607.1 IN THE IRC FOR RELEVANT CONCENTRATED LIVE LOADS.

8. SOIL INCLUDES 5 PSF FOR PV PANELS WHERE NOTED.





9. ALL ROOF/TOP STRUCTURE ROOFERS ARE DESIGNED FOR 25 PSF LIVE AND 15 PSF SUPERIMPOSED DEAD LOAD.

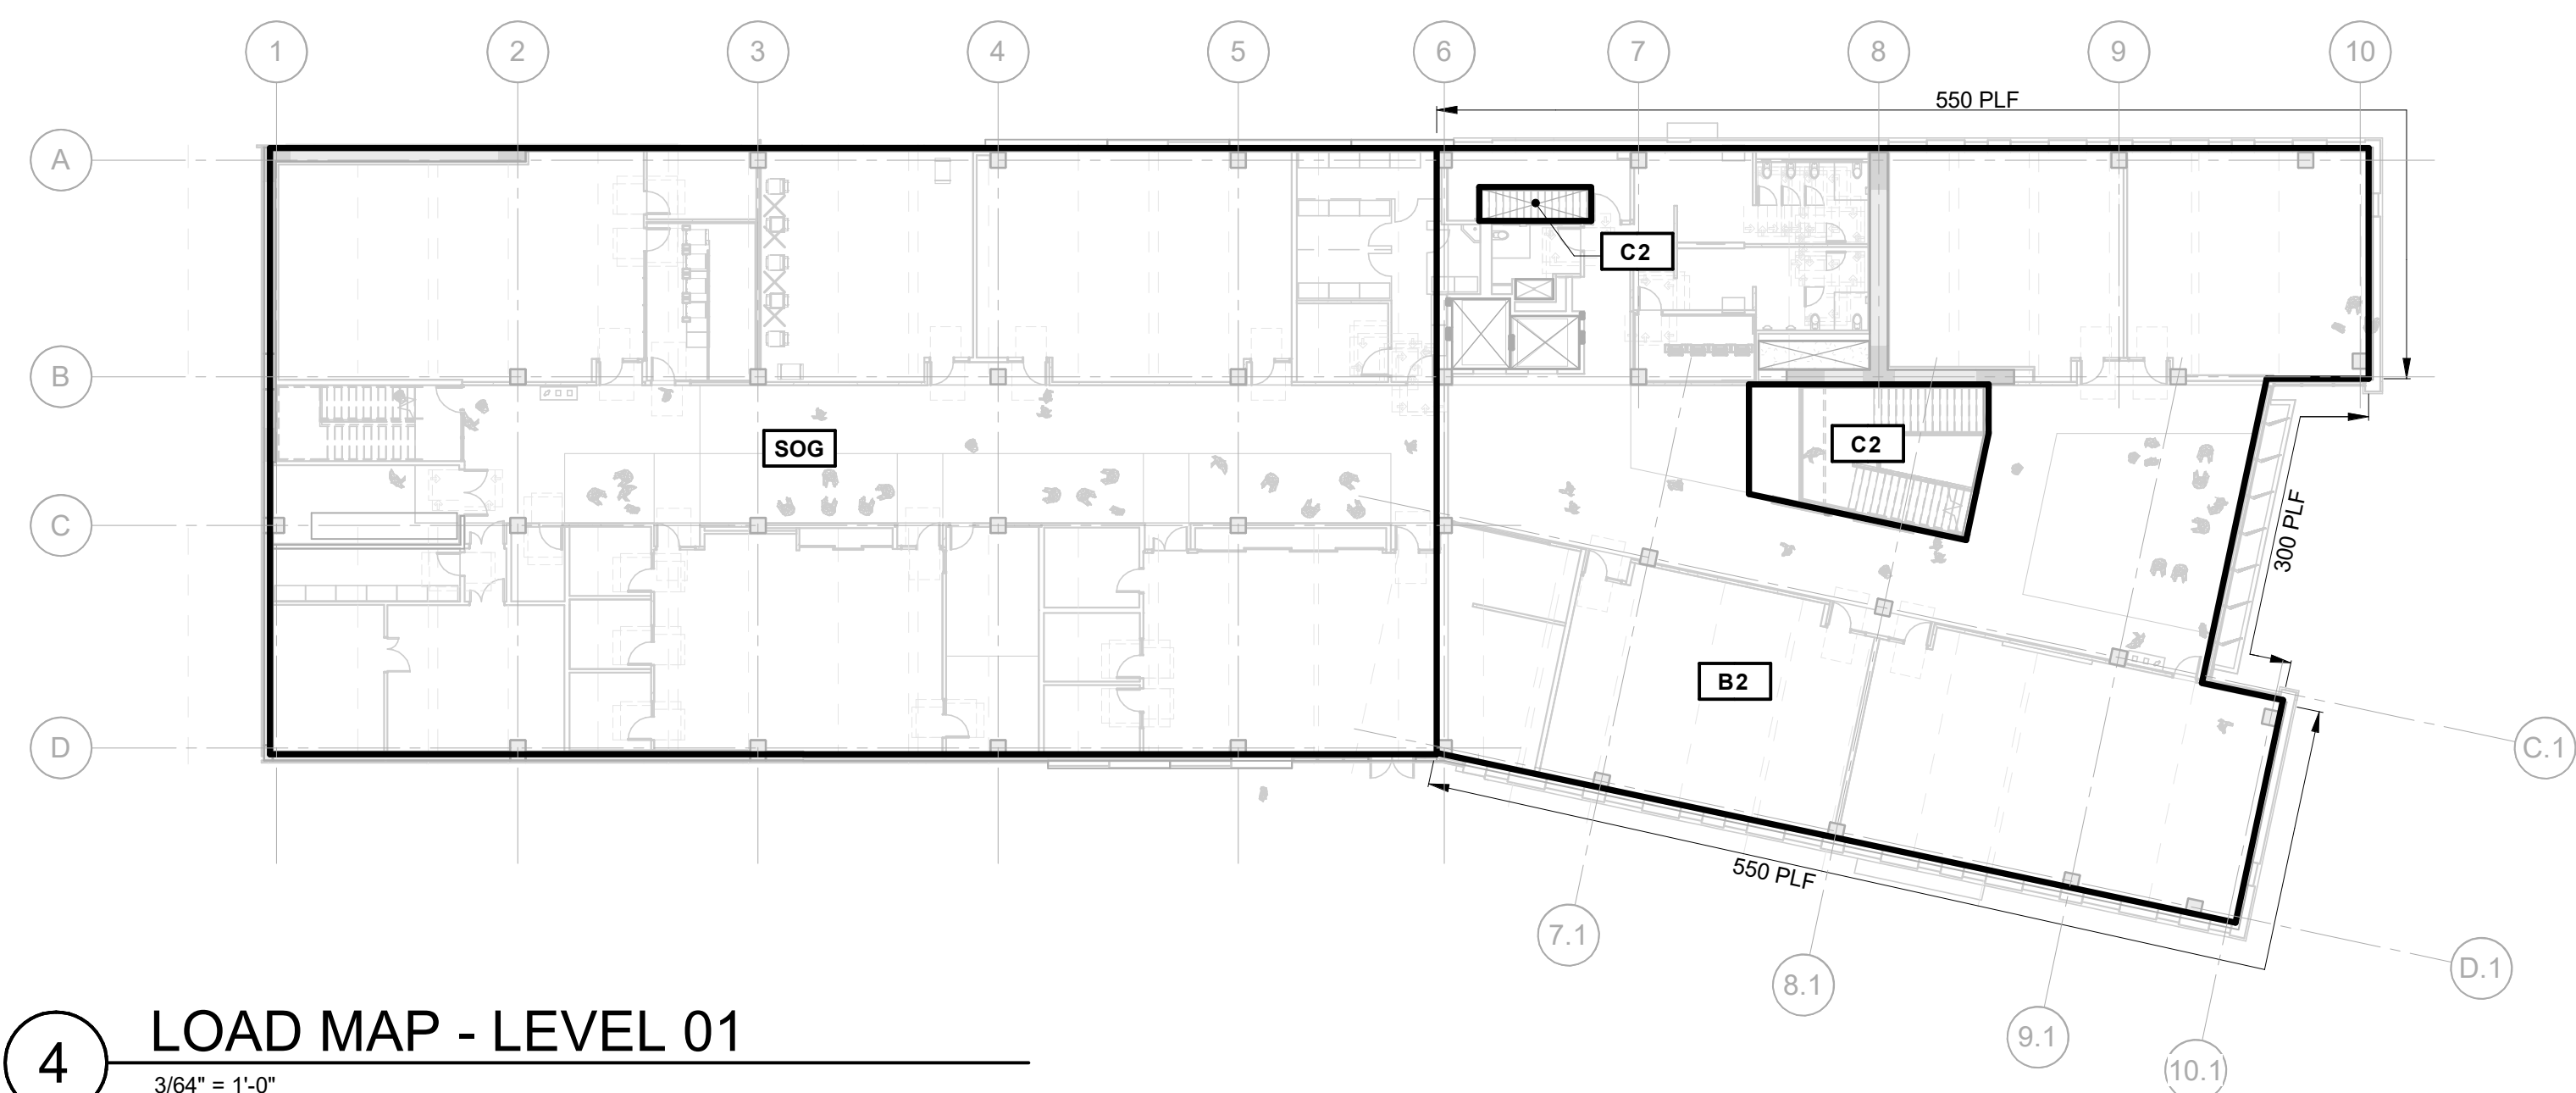

DESIGN PARTNER
KPF CONSULTING ENGINEERS
PROJECT MANAGER
MMM
PROJECT ARCHITECT
PROJECT DESIGNER
JTM
PROJECT TEAM MEMBERS
CDL
CHECK

SHEET NUMBER
S0.10
80% DESIGN
© 2021 MITHUN, INC.

THIS DRAWING IS FOR THE EXCLUSIVE USE OF MCCLONE CONSTRUCTION COMPANY, ON THIS PROJECT ONLY. UTILIZATION OF THIS DRAWING BY OTHER PARTIES AND/OR ON OTHER PROJECTS WITHOUT THE EXPRESSED WRITTEN CONSENT OF MCCLONE CONSTRUCTION COMPANY IS STRICTLY PROHIBITED.

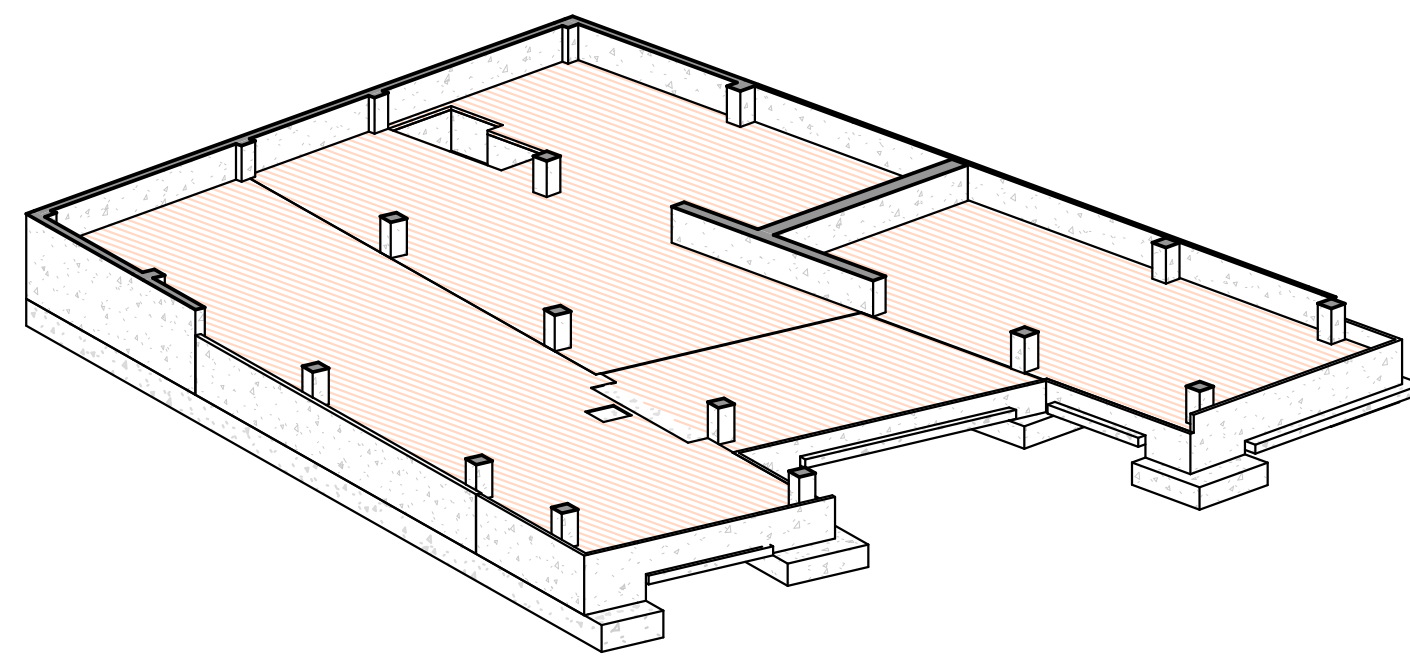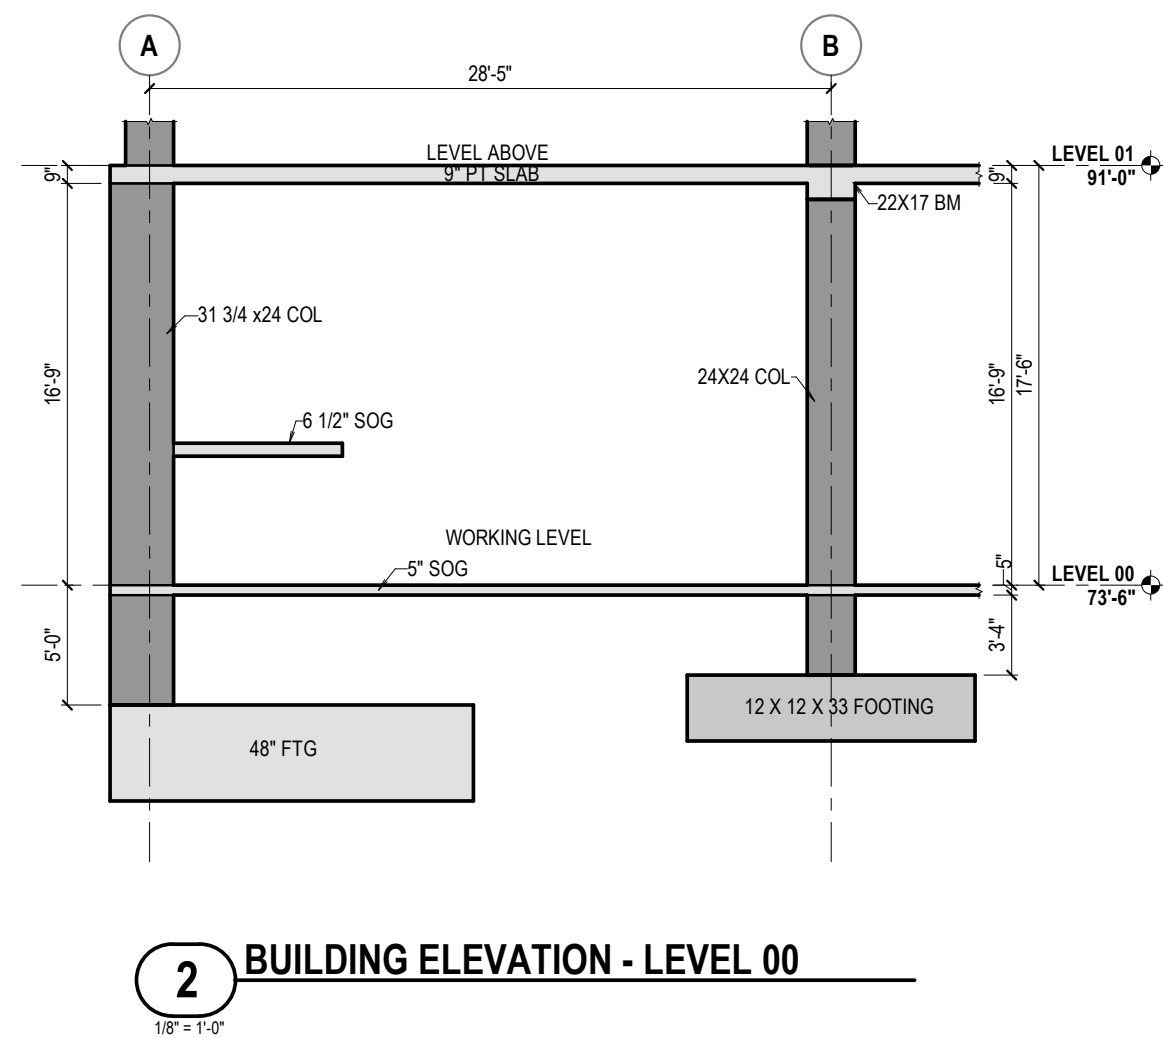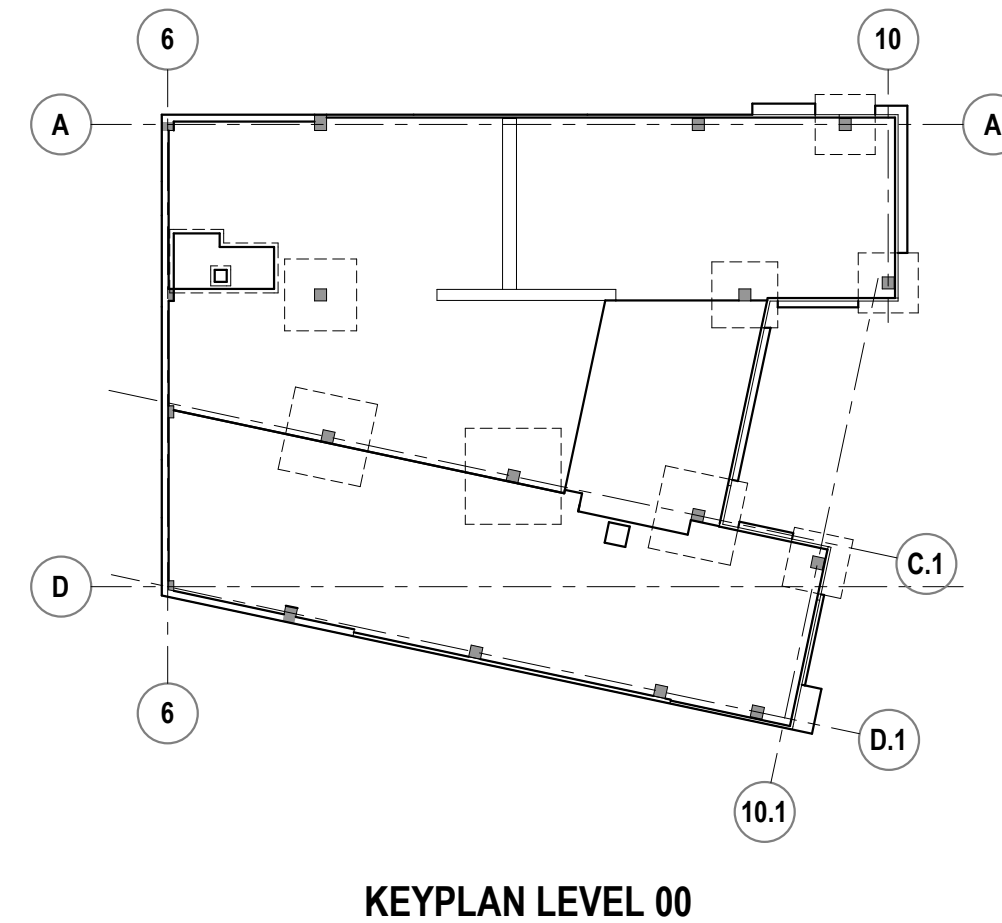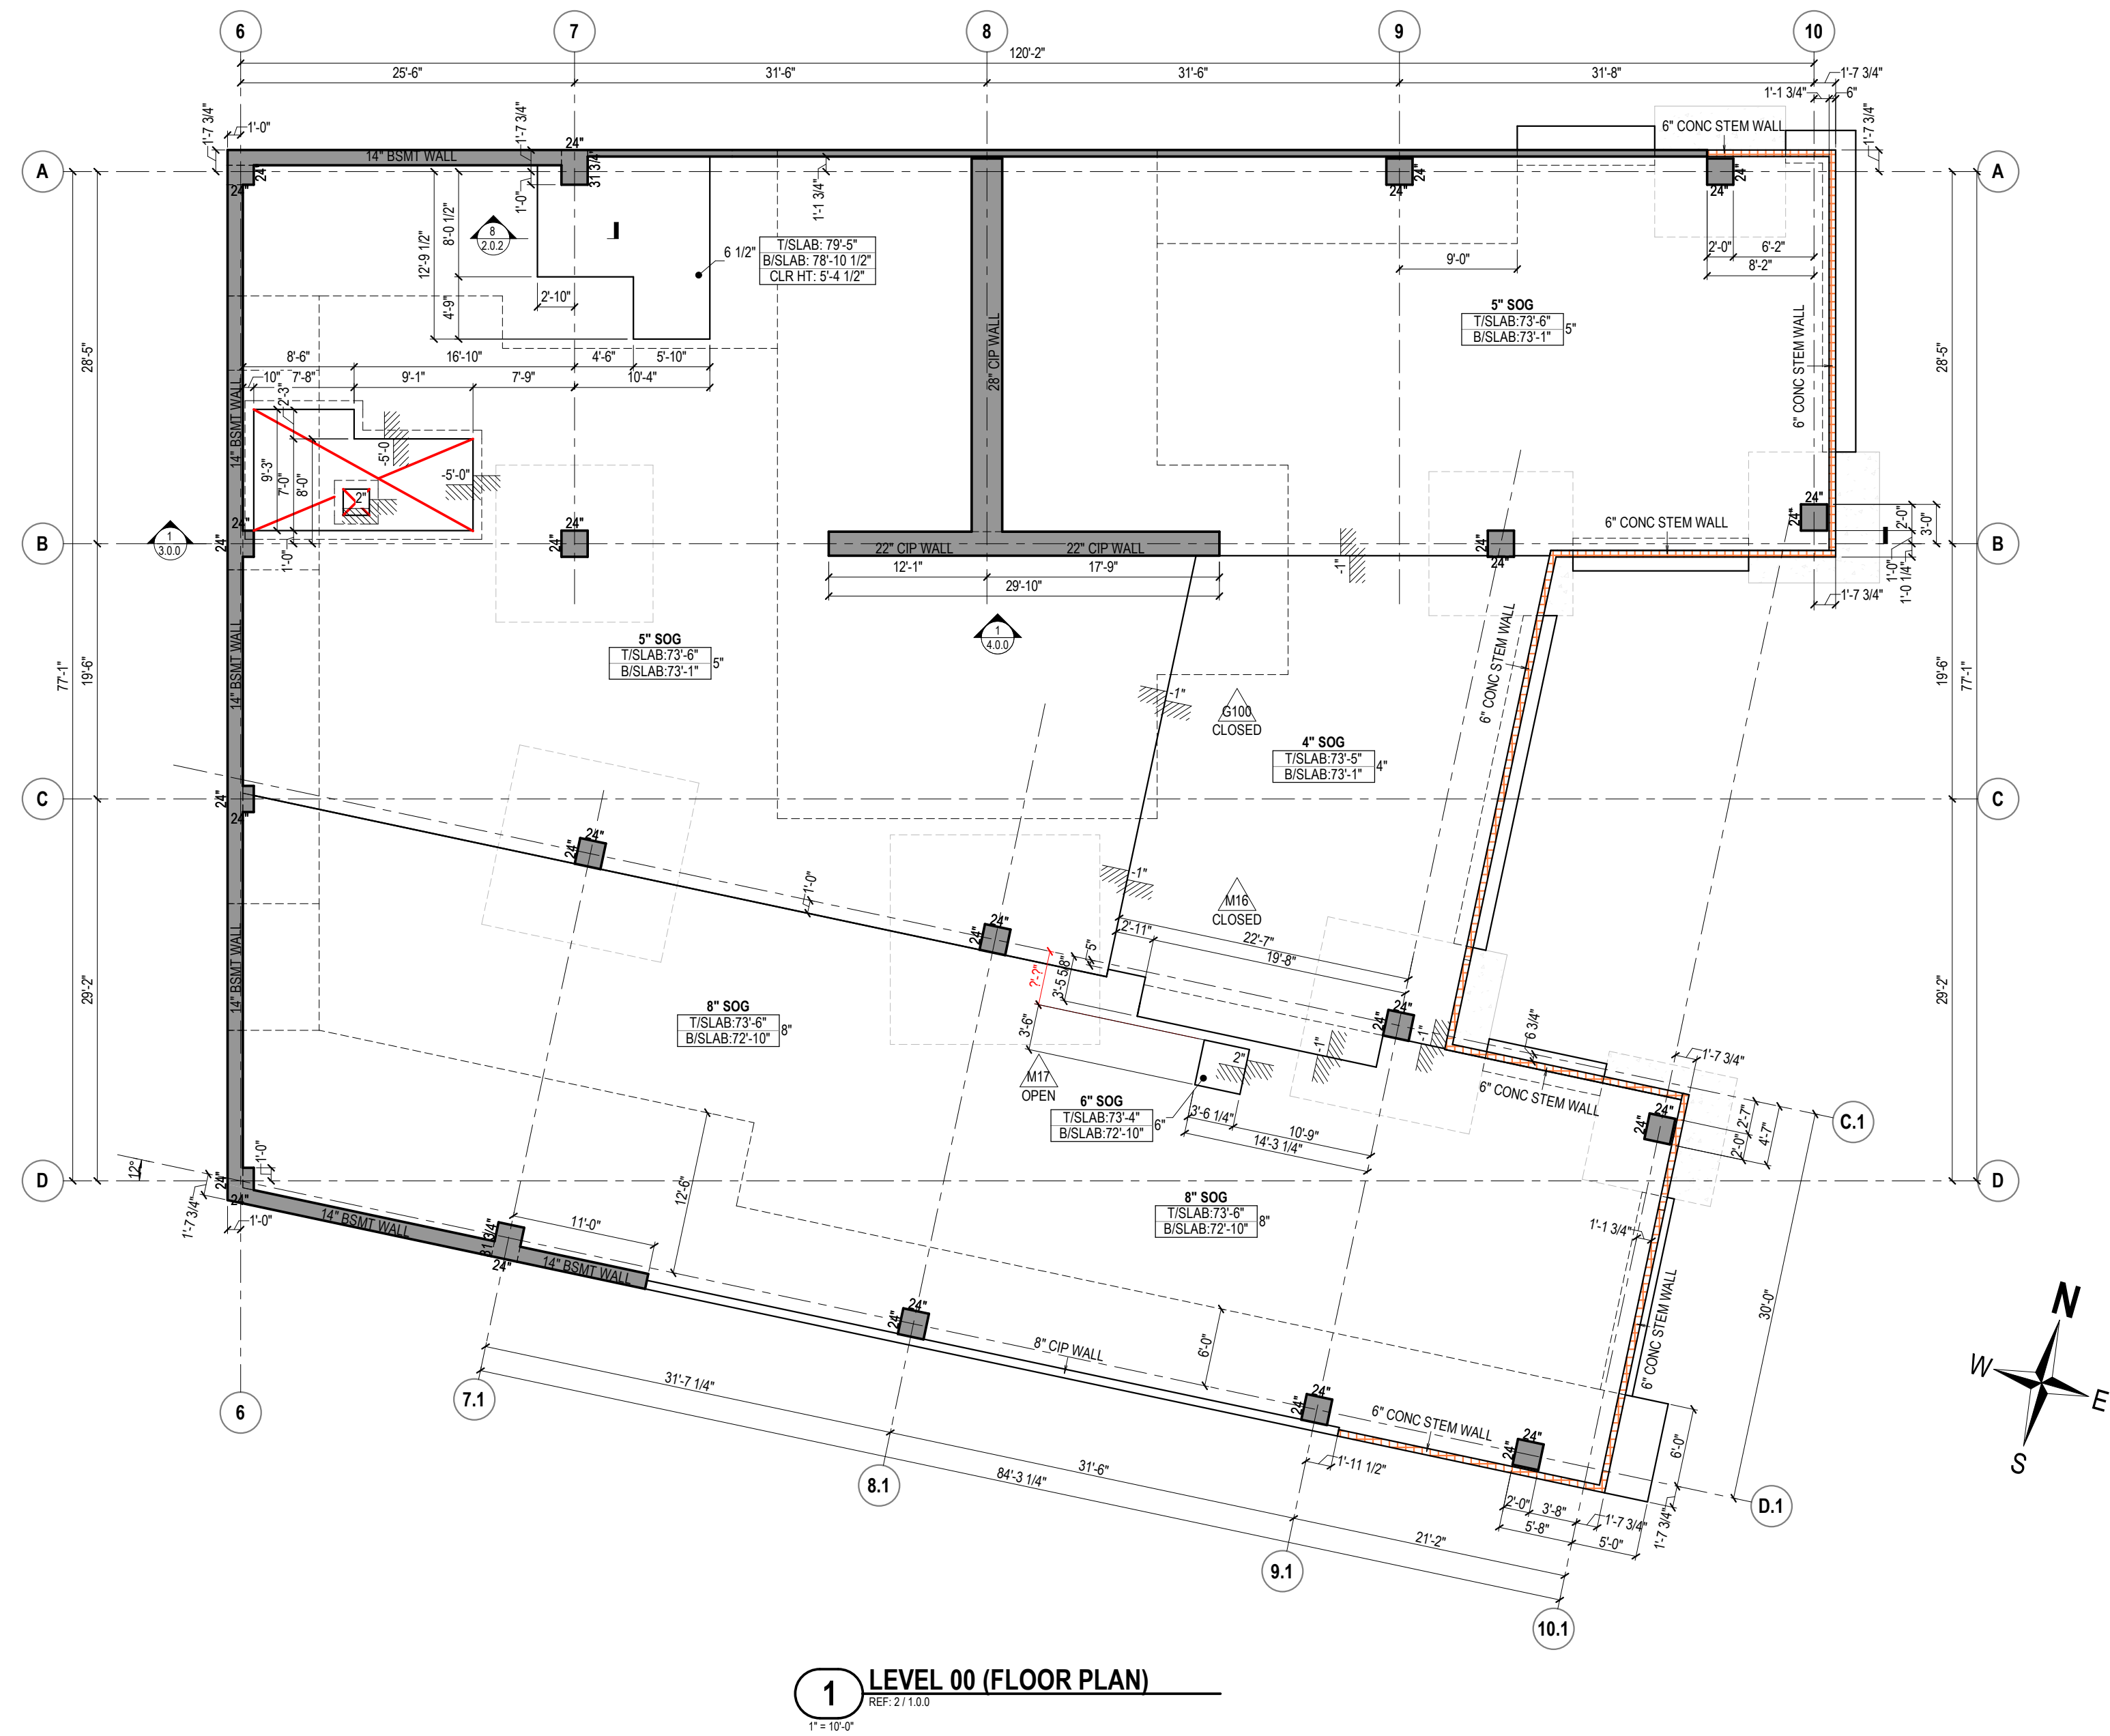


- NOTES:**
- 3/4" CHAMFER ON ALL EXPOSED CONCRETE CORNERS TYP.
 - ALL COLUMNS ARE CENTERED ON GRID LINES U.N.O.
 - ALL BEAMS ARE CENTERED ON GRID LINES U.N.O.
 - SLAB THICKNESS IS 5" TYP. U.N.O.
 - DO NOT SCALE THIS DRAWING. USE DIMENSIONS PROVIDED.


SYMBOLS		SHADE DESIGNATIONS	
1-BOX (ROUND-ENDS) TOP OF CONCRETE ELEVATIONS	(TOP ELEV)	FOOTINGS OR FOUNDATIONS	
1-BOX BOTTOM OF CONCRETE ELEVATIONS	(BOT ELEV)	WALLS OR COLUMNS	
2-BOX (PLAN VIEWS) TOP & BOTTOM ELEVATIONS D - DEPTH OF CONC MEMBER	(TOP ELEV) (BOT ELEV) 1"	CMU WALLS	
3-BOX (FLOOR PLANS) TOP & BOTTOM ELEVATIONS COLUMN ELEVATION ABOVE REF. LEVEL D - DEPTH OF CONC MEMBER	(TOP ELEV) (BOT ELEV) (TO COL ELEV) 1"	DELAY STRIP OR CLOSURE POUR	
SECTION VIEW	Ref 1:10	GRADE OR SOIL	
ELEVATION VIEW	Ref 1:10	6" STEM WALL	
DETAIL NUMBER		LINE DESIGNATIONS	
		INDICATES TOP OF FTG CHANGE OR EDGE OF FTG	
		INDICATES BOTTOM OF FTG CHANGE	
		INDICATES CONSTRUCTION JOINT	
		INDICATES GRID LINE	

THIS DRAWING IS FOR THE EXCLUSIVE USE OF MCCLONE CONSTRUCTION COMPANY, ON THIS PROJECT ONLY. UTILIZATION OF THIS DRAWING BY OTHER PARTIES AND/OR ON OTHER PROJECTS WITHOUT THE EXPRESSED WRITTEN CONSENT OF MCCLONE CONSTRUCTION COMPANY IS STRICTLY PROHIBITED.


PLOT DATE/TIME STAMP: 5/21/2022 10:03:31 AM
Z:\Shared\WAP\Projects\1175 Botell STEB\1175 Botell STEB.dwg
Model: 1175 - Botell STEB 1175

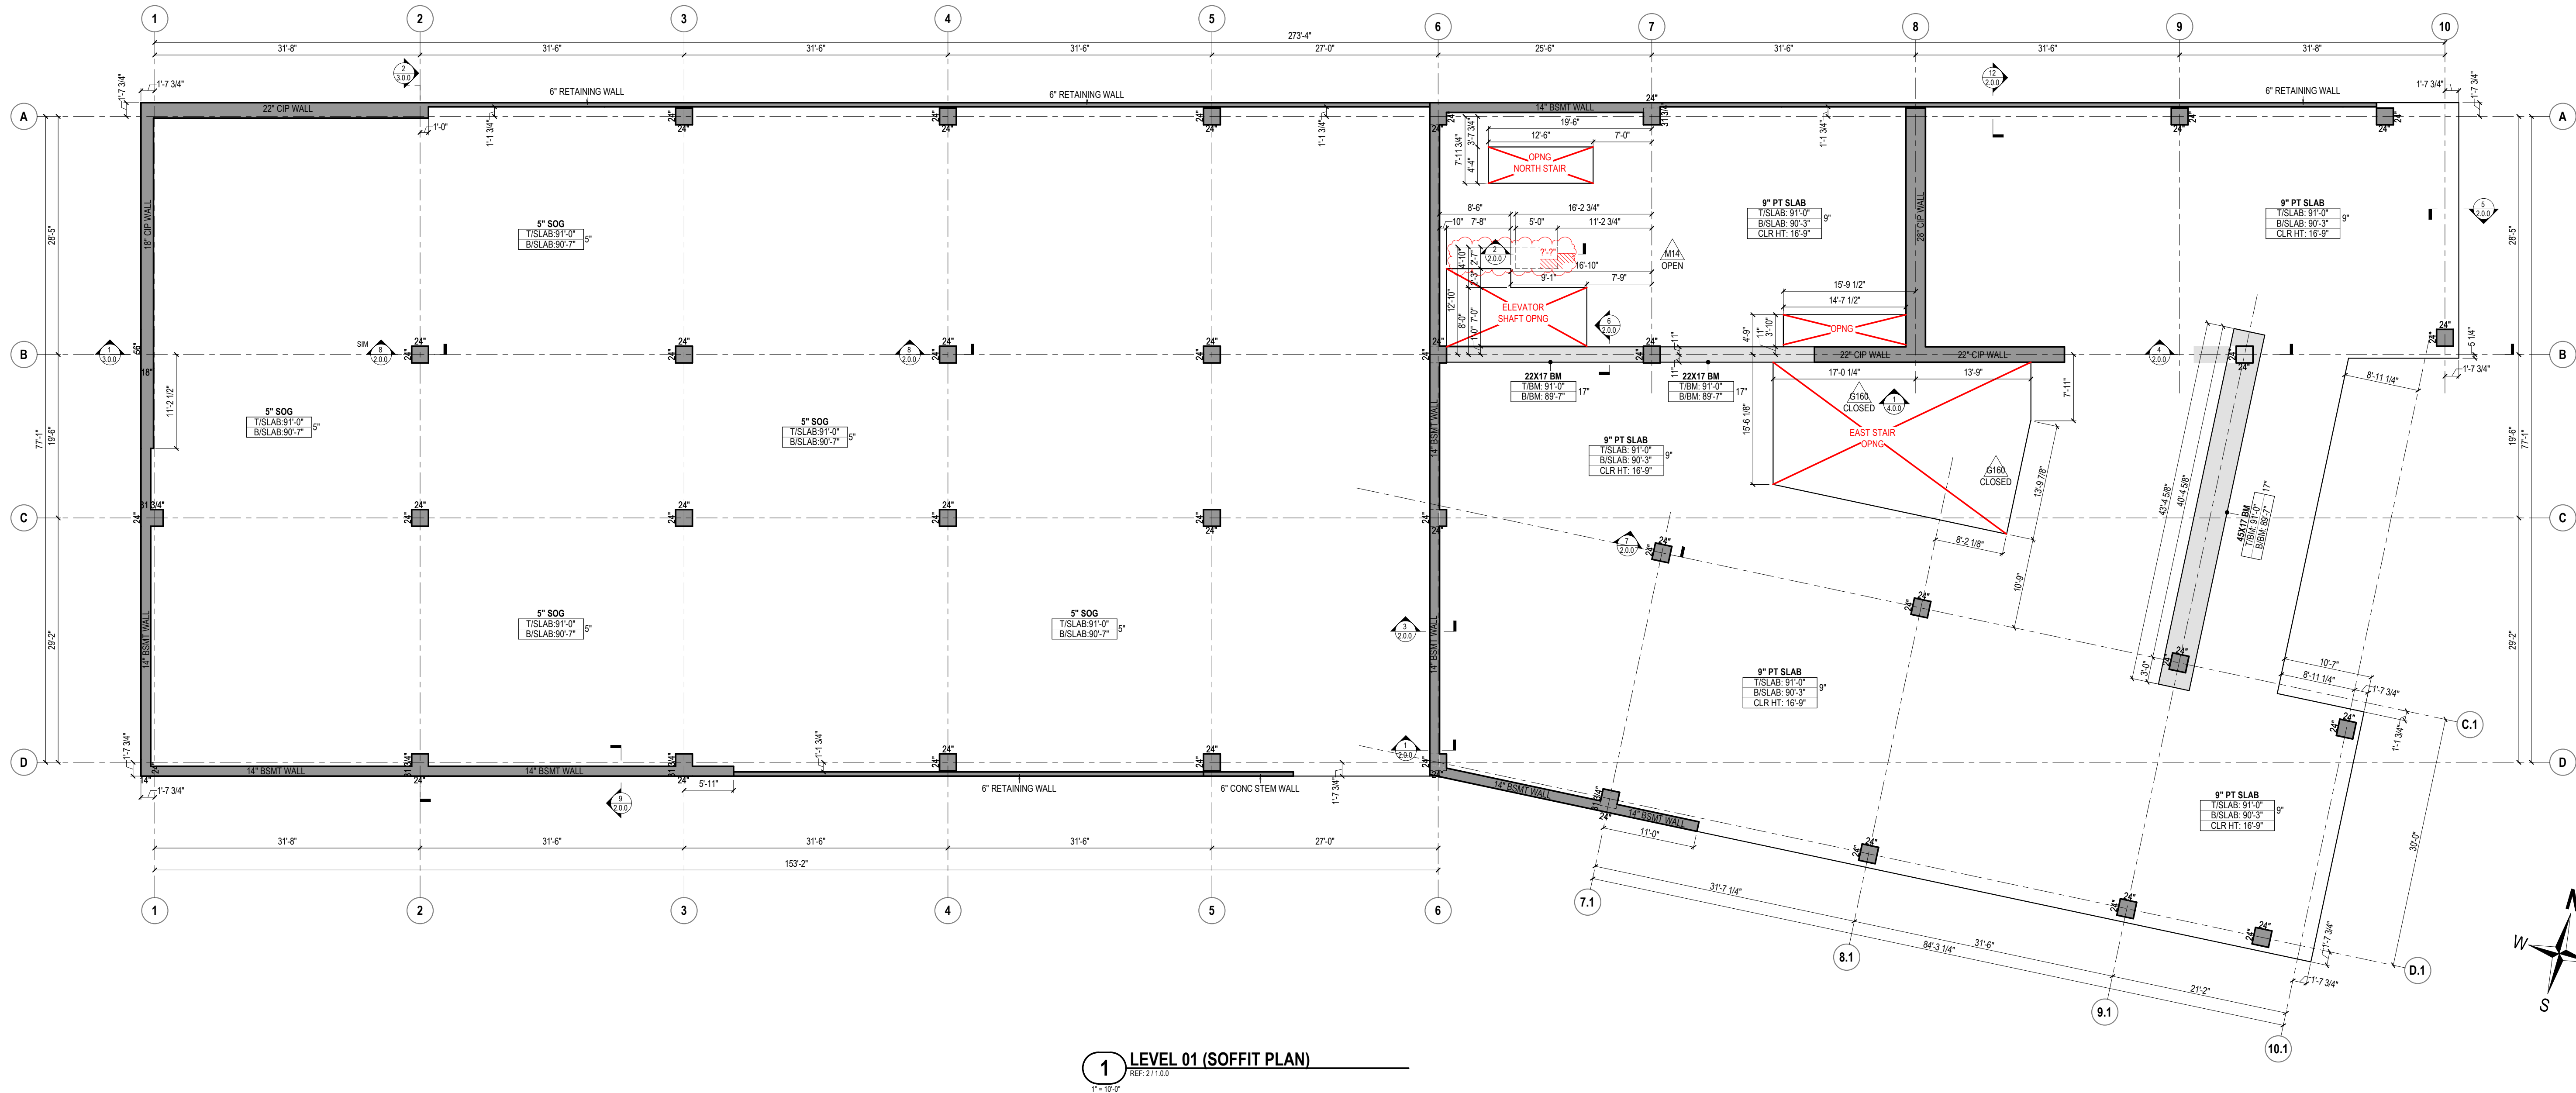


1 LEVEL 01 (SOFFIT PLAN)
REF: 2.1, 11.0, 8
1" = 10'-0"

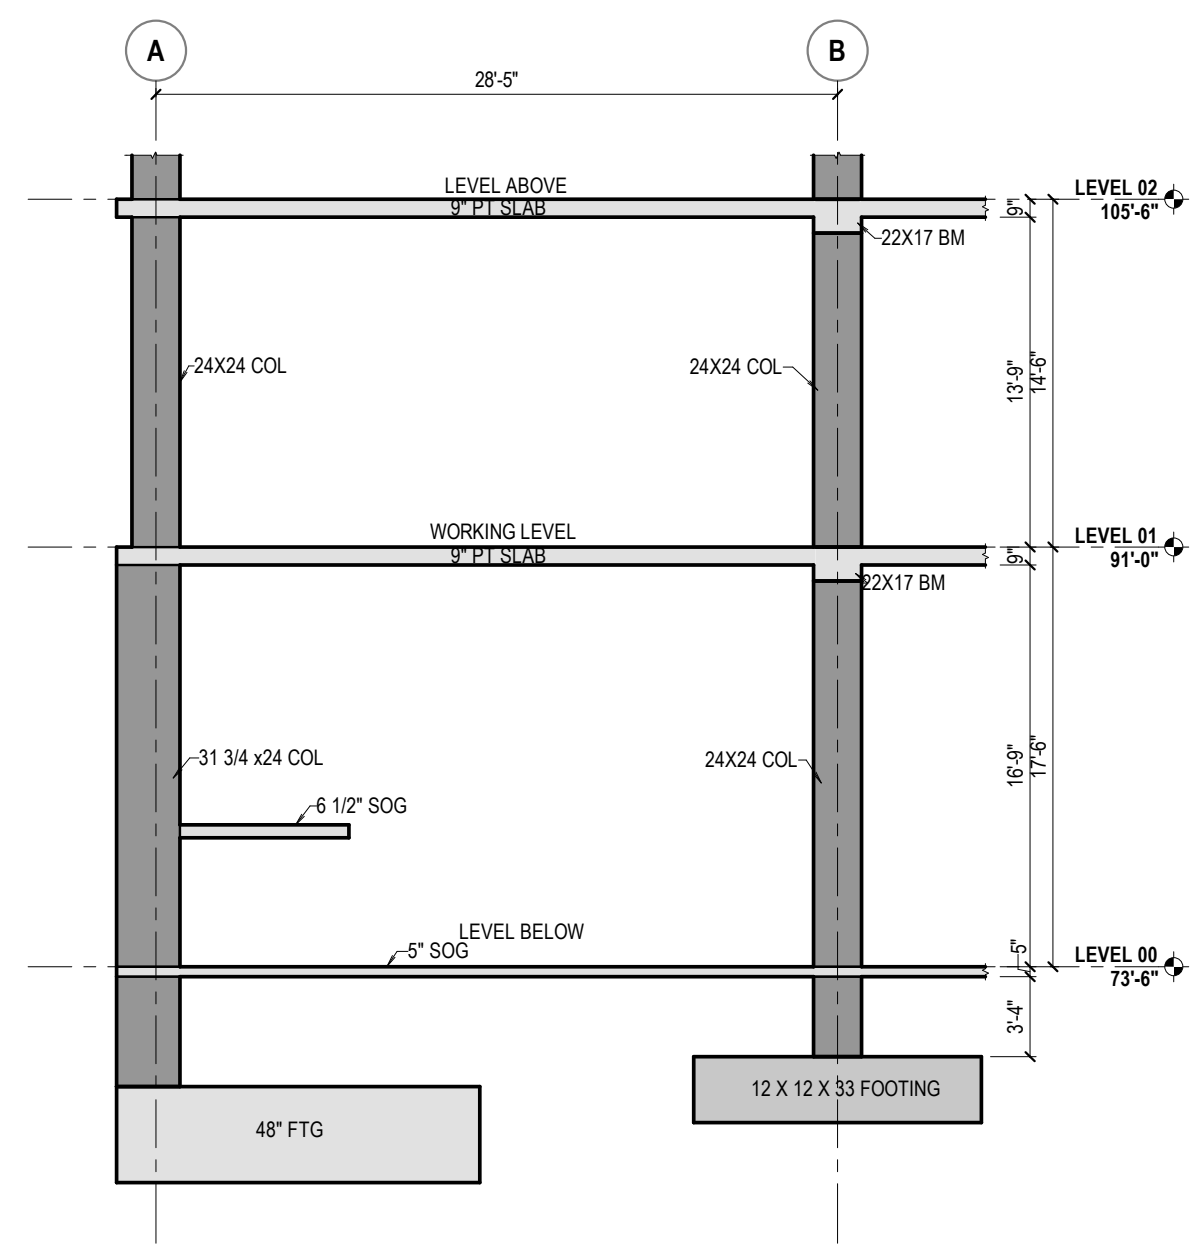

2 BUILDING ELEVATION - LEVEL 01
1/8" = 1'-0"

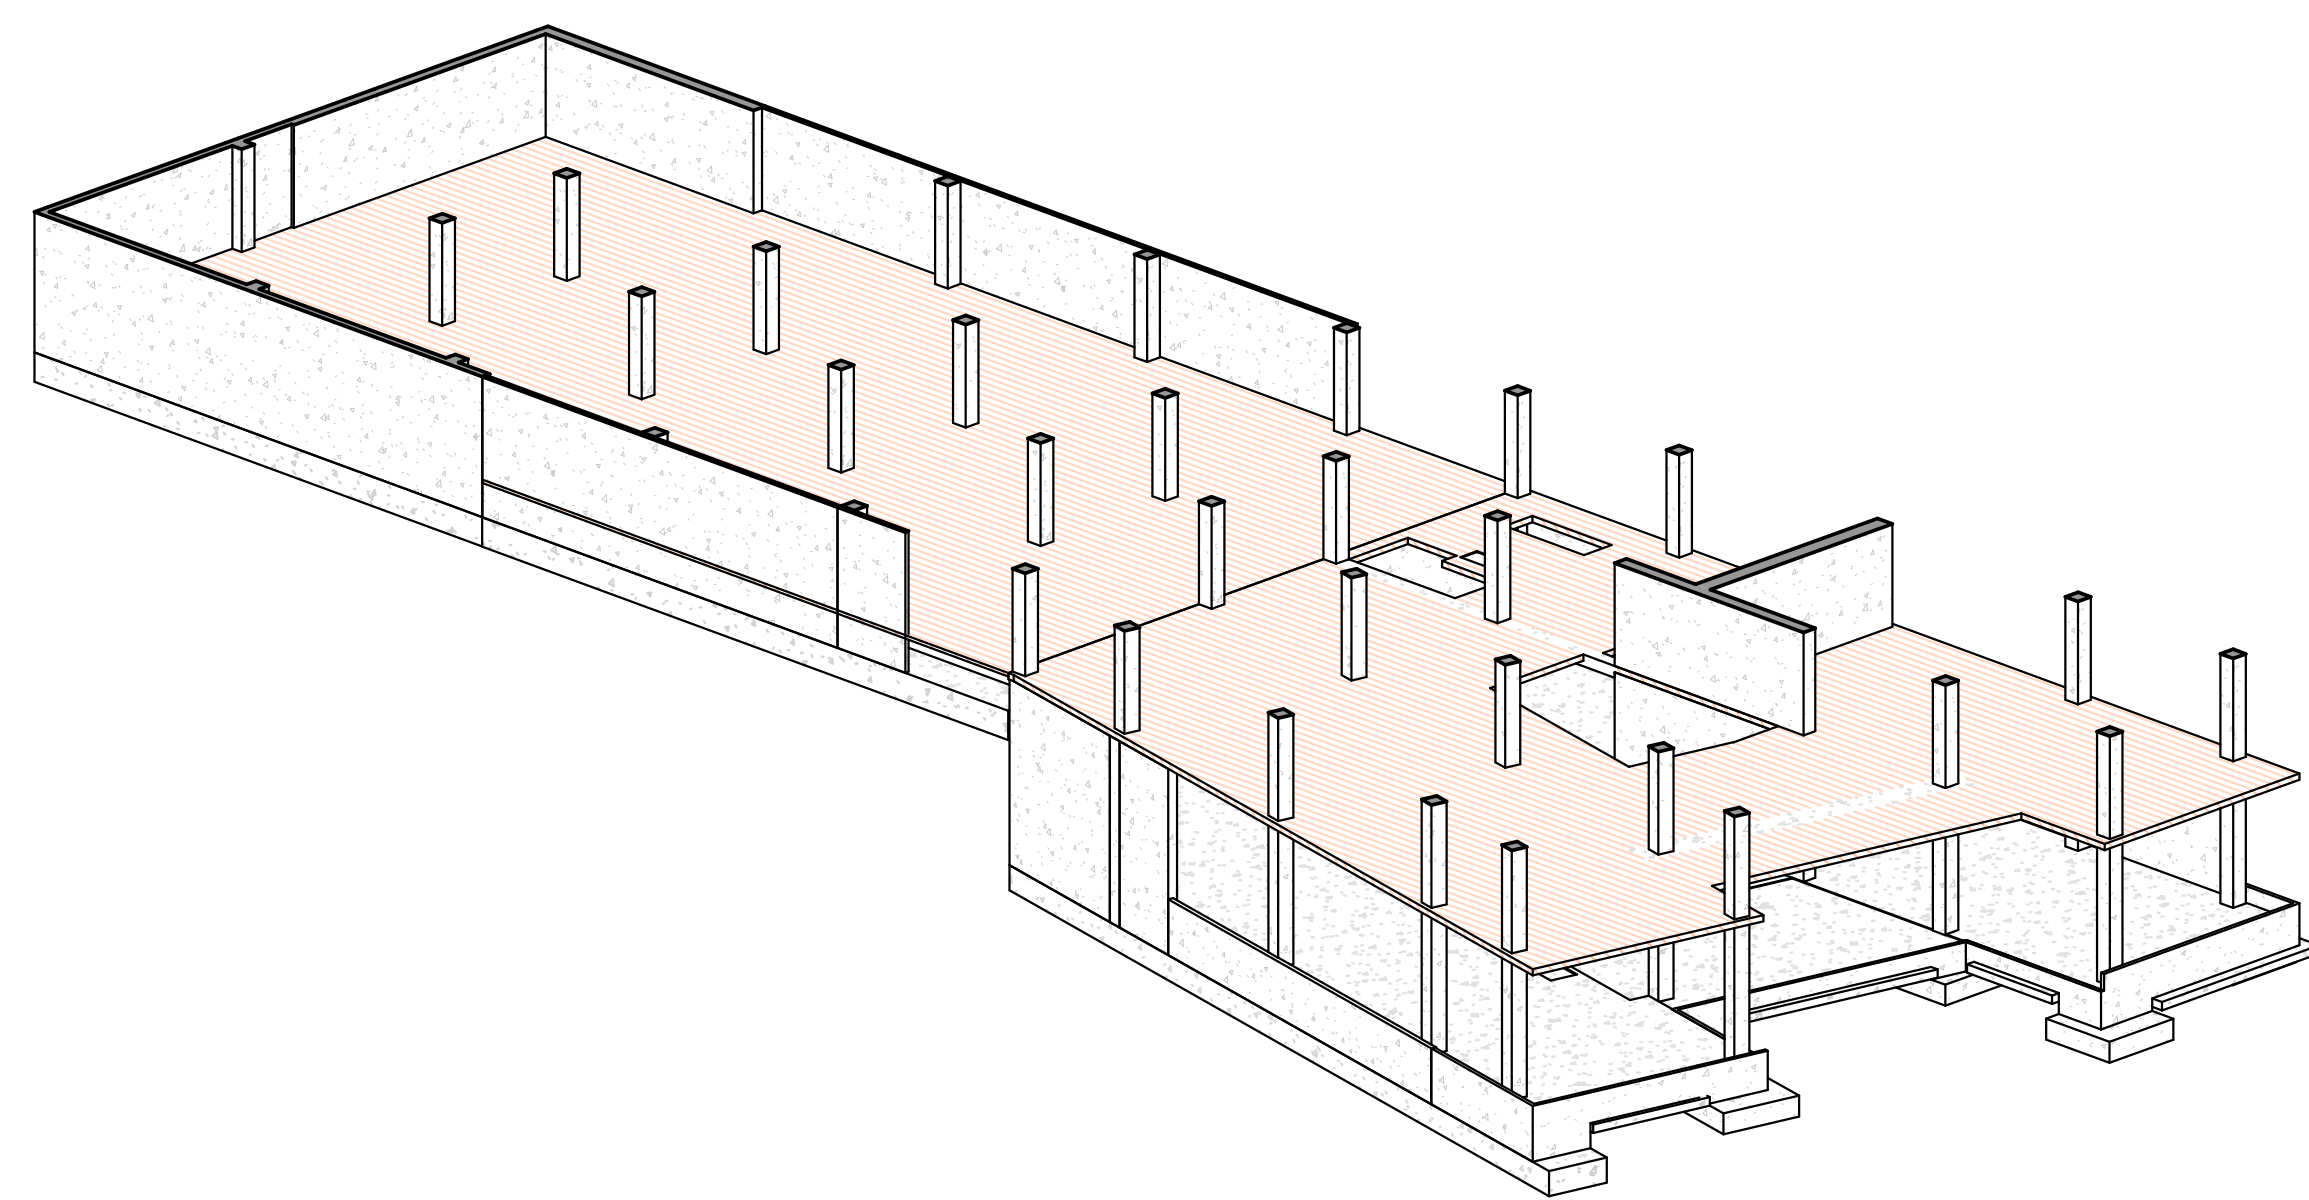

3 3D VIEW - LEVEL 01

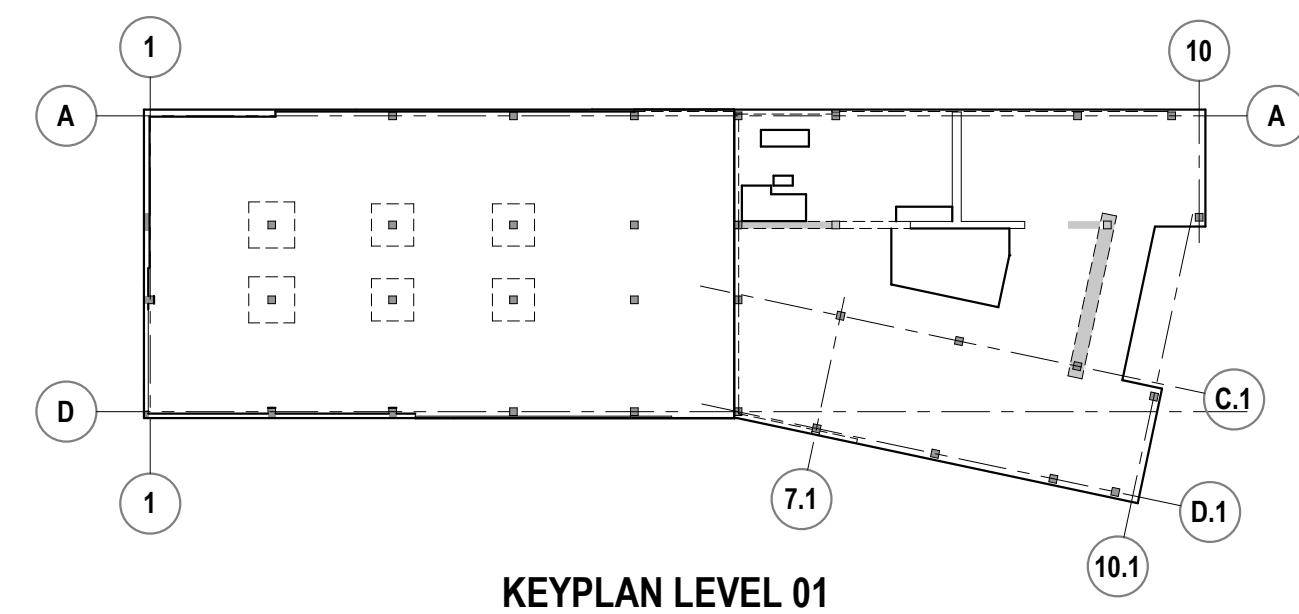


KEYPLAN LEVEL 01

NOTES:


- 3/4" CHAMFER ON ALL EXPOSED CONCRETE CORNERS TYP.
- ALL COLUMNS ARE CENTERED ON GRID LINES U.N.O.
- ALL BEAMS ARE CENTERED ON GRID LINES U.N.O.
- SLAB THICKNESS: 18" TYP. U.N.O.
- DO NOT SCALE THIS DRAWING. USE DIMENSIONS PROVIDED.

LEGEND

SYMBOLS		SHADE DESIGNATIONS	
1-BOX (ROUND-ENDS)	(TOP ELEV)	BEAM OR DROP CAP	
TOP OF CONCRETE ELEVATIONS	(BOT ELEV)	WALLS OR COLUMNS	
1-BOX (PLAN VIEWS)	(TOP ELEV)	CMU WALLS	
TOP & BOTTOM ELEVATIONS	(BOT ELEV)	DELAY STRIP OR CLOSURE POUR	
D = DEPTH OF CONC. MEMBER	(TOP ELEV)	GRADE OR SOIL	
3-BOX (SOFFIT PLANS)	(BOT ELEV)	12" SLAB DEPRESSION	
TOP & BOTTOM ELEVATIONS	(TOP ELEV)		
HEIGHT BELOW REFERENCE LEVEL	(BOT ELEV)		
D = DEPTH OF CONC. MEMBER			
SECTION VIEW		LINE DESIGNATIONS	
Ref.	DETAIL NUMBER	--- INDICATES TOP OF SLAB CHANGE OR EDGE OF SLAB	
SHEET NUMBER		--- INDICATES SOFFIT CHANGE	
ELEVATION VIEW	DETAIL NUMBER	--- INDICATES CONSTRUCTION JOINT	
SHEET NUMBER		--- INDICATES GRID LINE	

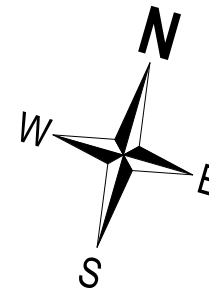


THIS DRAWING IS FOR THE EXCLUSIVE USE OF MCCLONE CONSTRUCTION COMPANY, ON THIS PROJECT ONLY. UTILIZATION OF THIS DRAWING BY OTHER PARTIES AND/OR OTHER PROJECTS WITHOUT THE EXPRESSED WRITTEN CONSENT OF MCCLONE CONSTRUCTION COMPANY IS STRICTLY PROHIBITED.

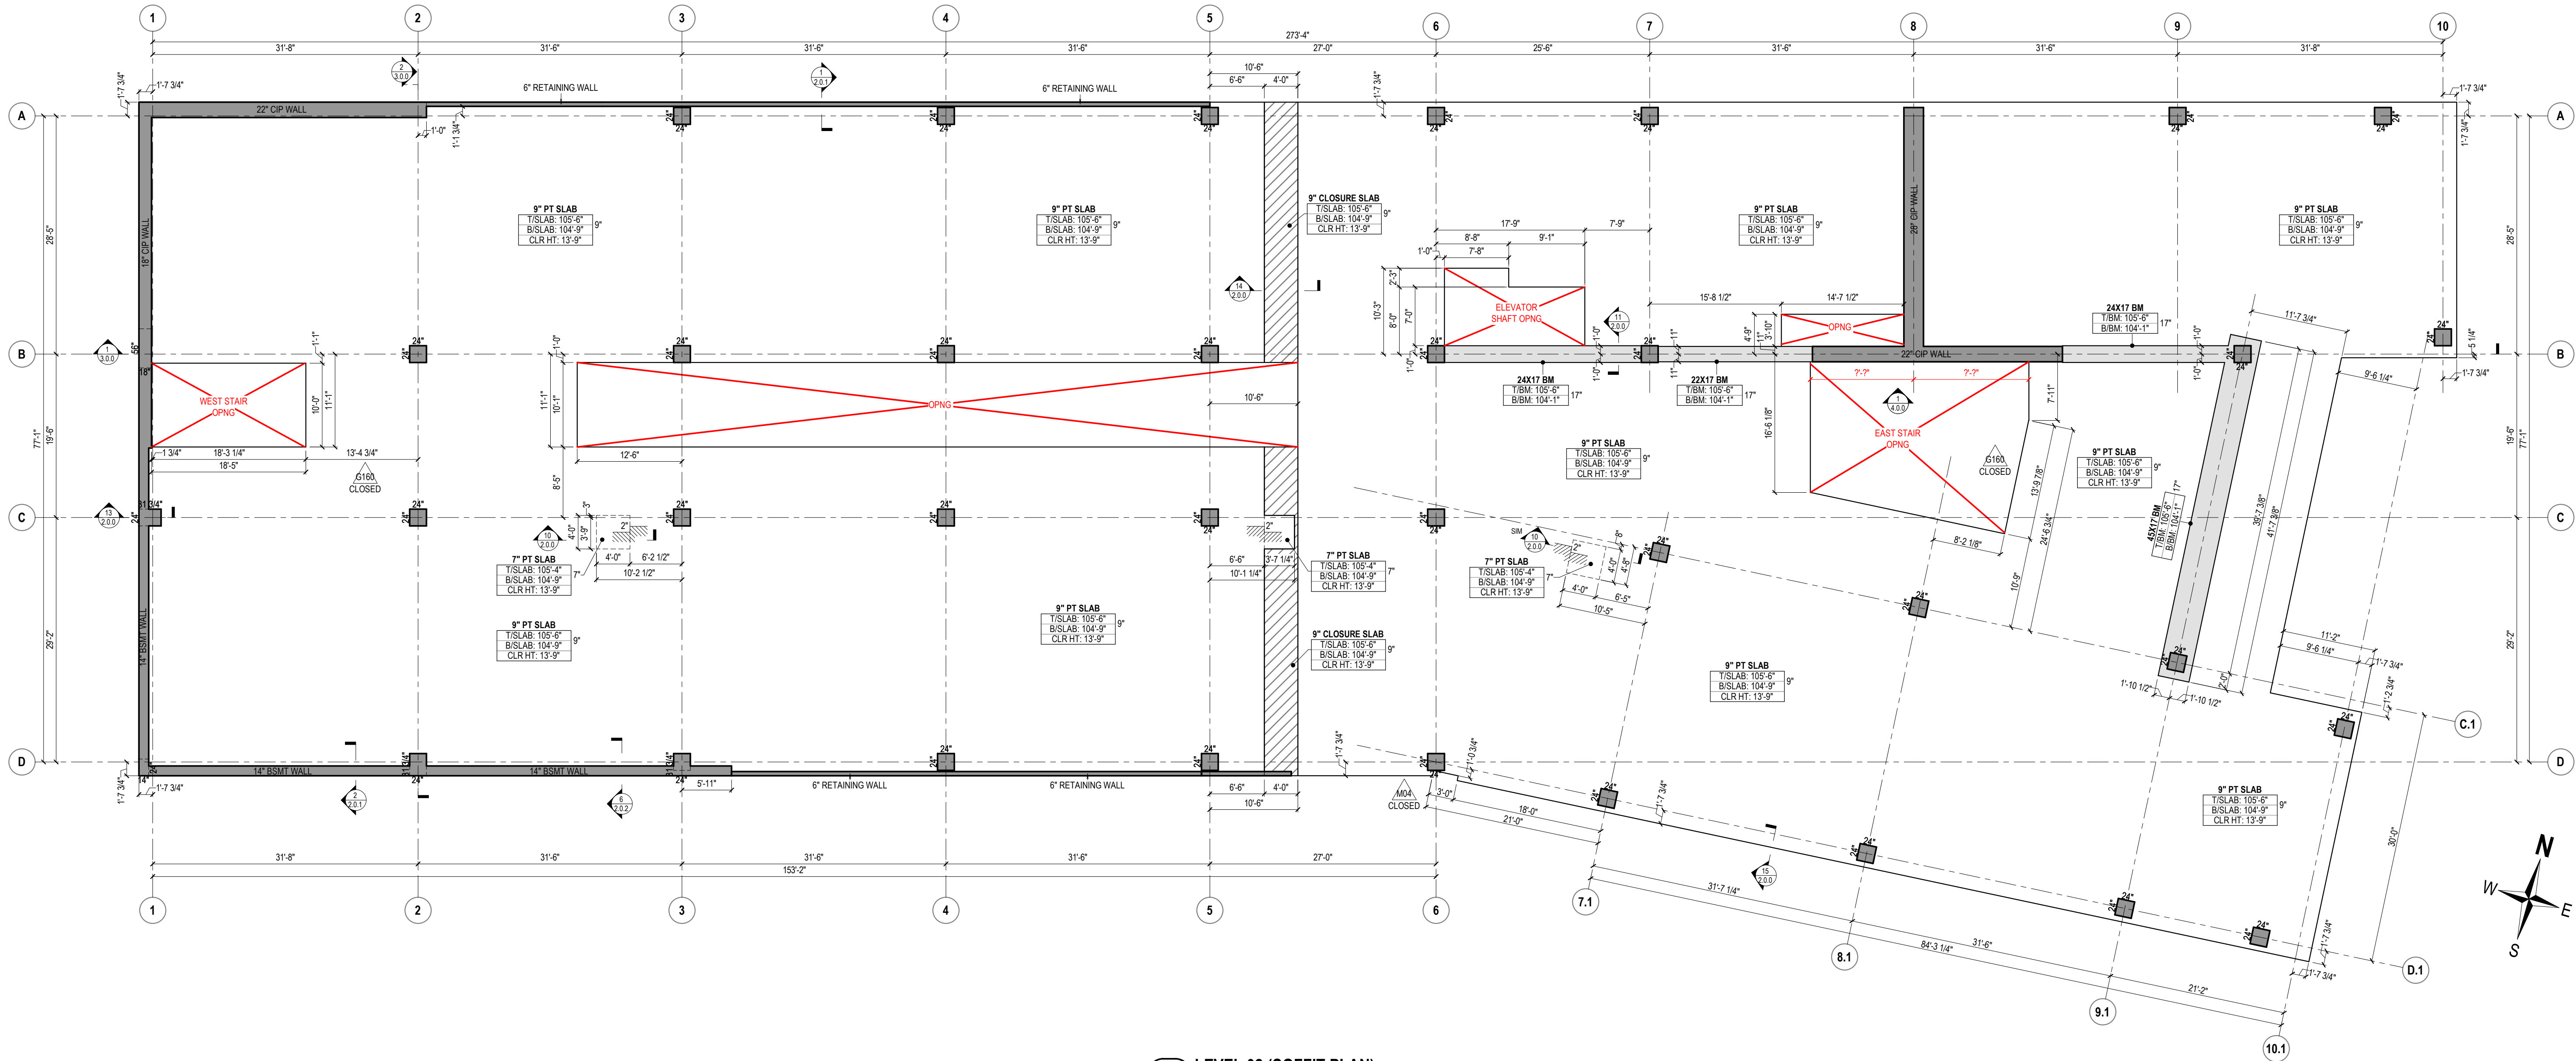


1 LEVEL 02 (SOFFIT PLAN)

1\"/>

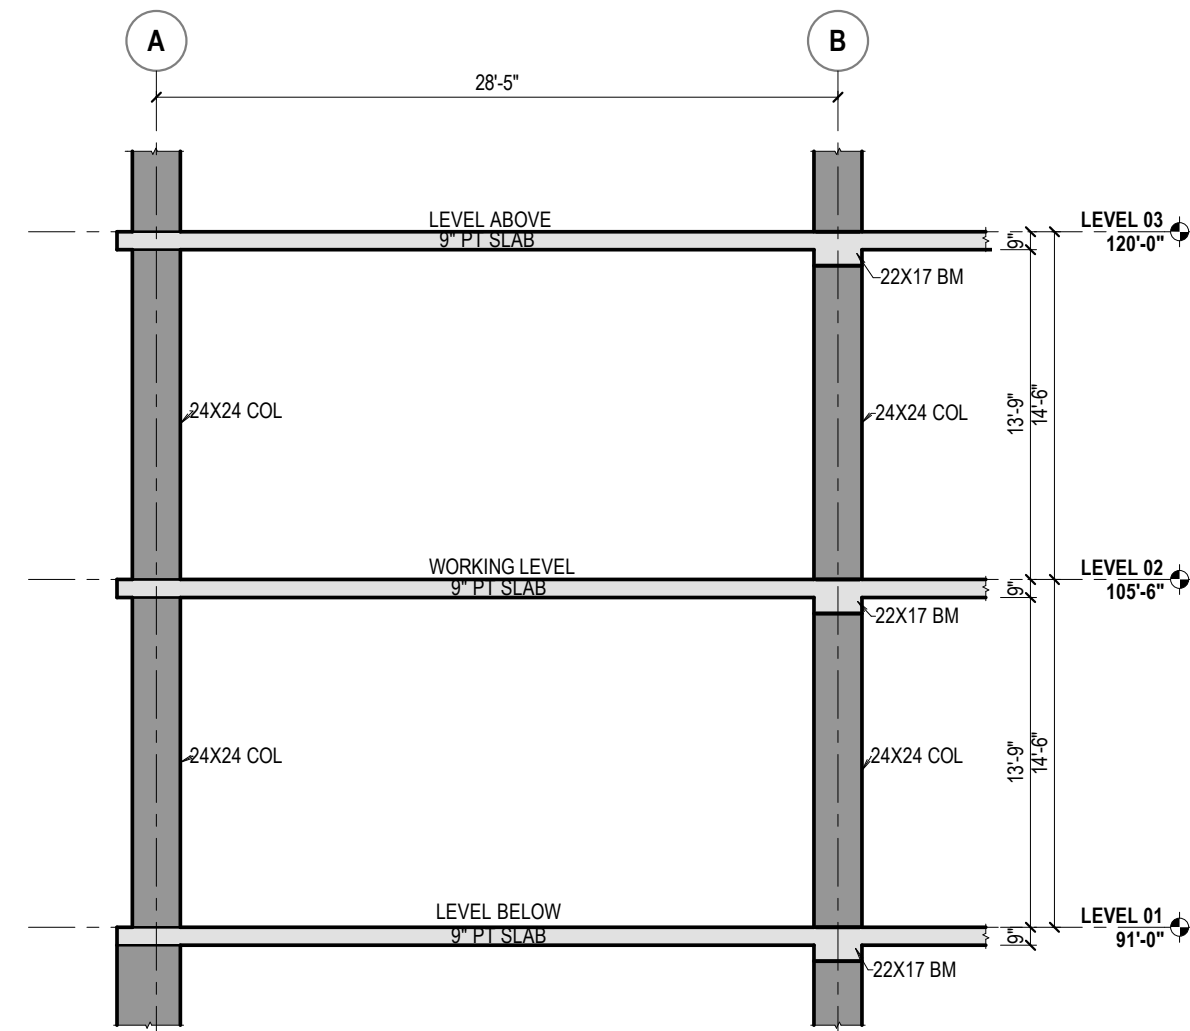


2 BUILDING ELEVATION - LEVEL 02

1/8\"/>

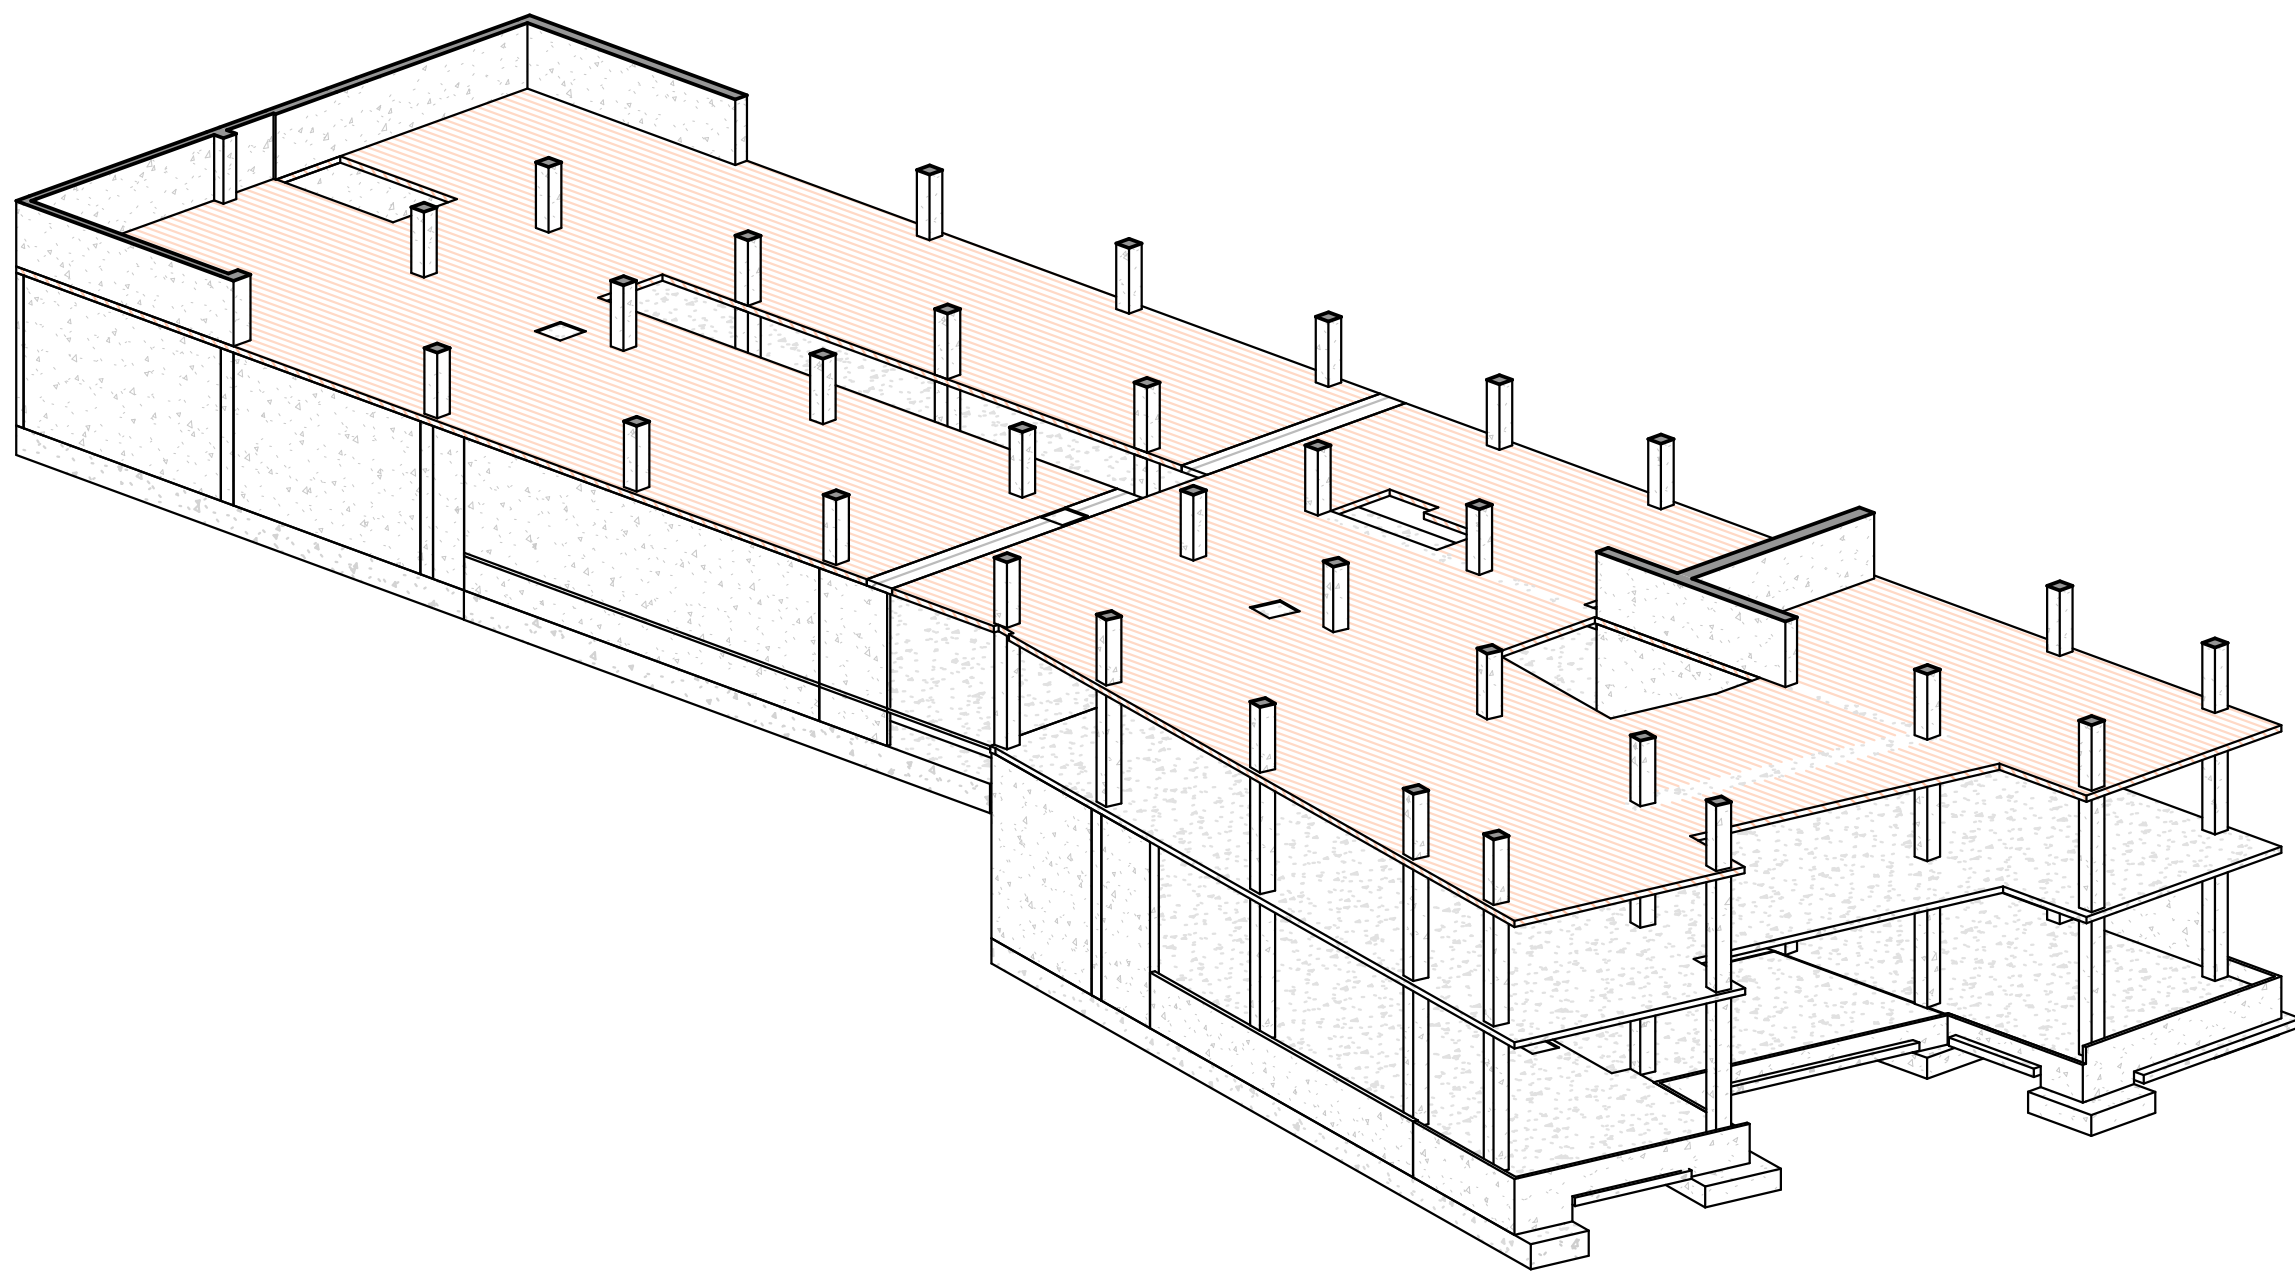

3 3D VIEW - LEVEL 02

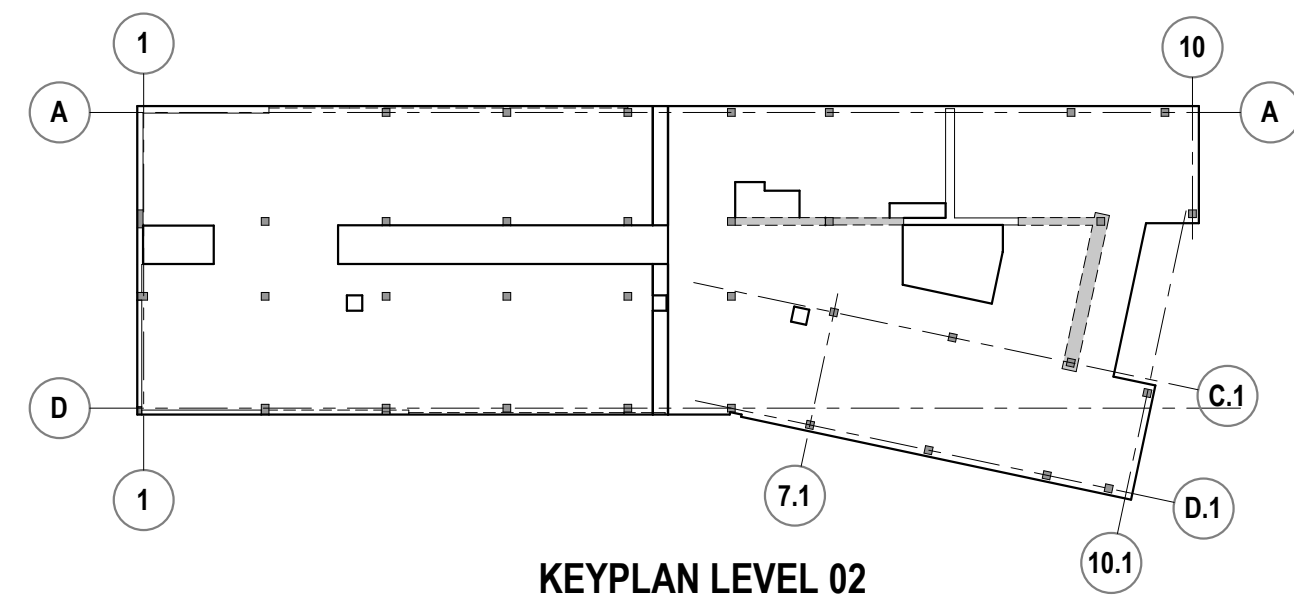

KEYPLAN LEVEL 02

NOTES:

- 3/4" CHAMFER ON ALL EXPOSED CONCRETE CORNERS TYP.
- ALL COLUMNS ARE CENTERED ON GRID LINES U.N.O.
- ALL BEAMS ARE CENTERED ON GRID LINES U.N.O.
- SLAB THICKNESS IS 9" TYP. U.N.O.
- DO NOT SCALE THIS DRAWING. USE DIMENSIONS PROVIDED.

LEGEND

SYMBOLS

- 1-BOX (ROUND-ENDS)
TOP OF CONCRETE ELEVATIONS
- 1-BOX
BOTTOM OF CONCRETE ELEVATIONS
- 2-BOX (PLAN VIEWS)
TOP & BOTTOM ELEVATIONS
D = DEPTH OF CONC. MEMBER
- 3-BOX (SOFFIT PLANS)
TOP & BOTTOM ELEVATIONS
HEIGHT BELOW REFERENCE LEVEL
D = DEPTH OF CONC. MEMBER

SECTION VIEW

SHEET NUMBER 1175

ELEVATION VIEW

SHEET NUMBER 1175


SHADE DESIGNATIONS

- BEAM OR DROP CAP
- WALLS OR COLUMNS
- CMU WALLS
- DELAY STRIP OR CLOSURE POUR
- GRADE OR SOIL
- 1/2" SLAB DEPRESSION

LINE DESIGNATIONS


- INDICATES TOP OF SLAB CHANGE OR EDGE OF SLAB
- INDICATES SOFFIT CHANGE
- INDICATES CONSTRUCTION JOINT
- INDICATES GRID LINE

THIS DRAWING IS FOR THE EXCLUSIVE USE OF MCCLONE CONSTRUCTION COMPANY, ON THIS PROJECT ONLY. UTILIZATION OF THIS DRAWING BY OTHER PARTIES AND/OR ON OTHER PROJECTS WITHOUT THE EXPRESSED WRITTEN CONSENT OF MCCLONE CONSTRUCTION COMPANY IS STRICTLY PROHIBITED.

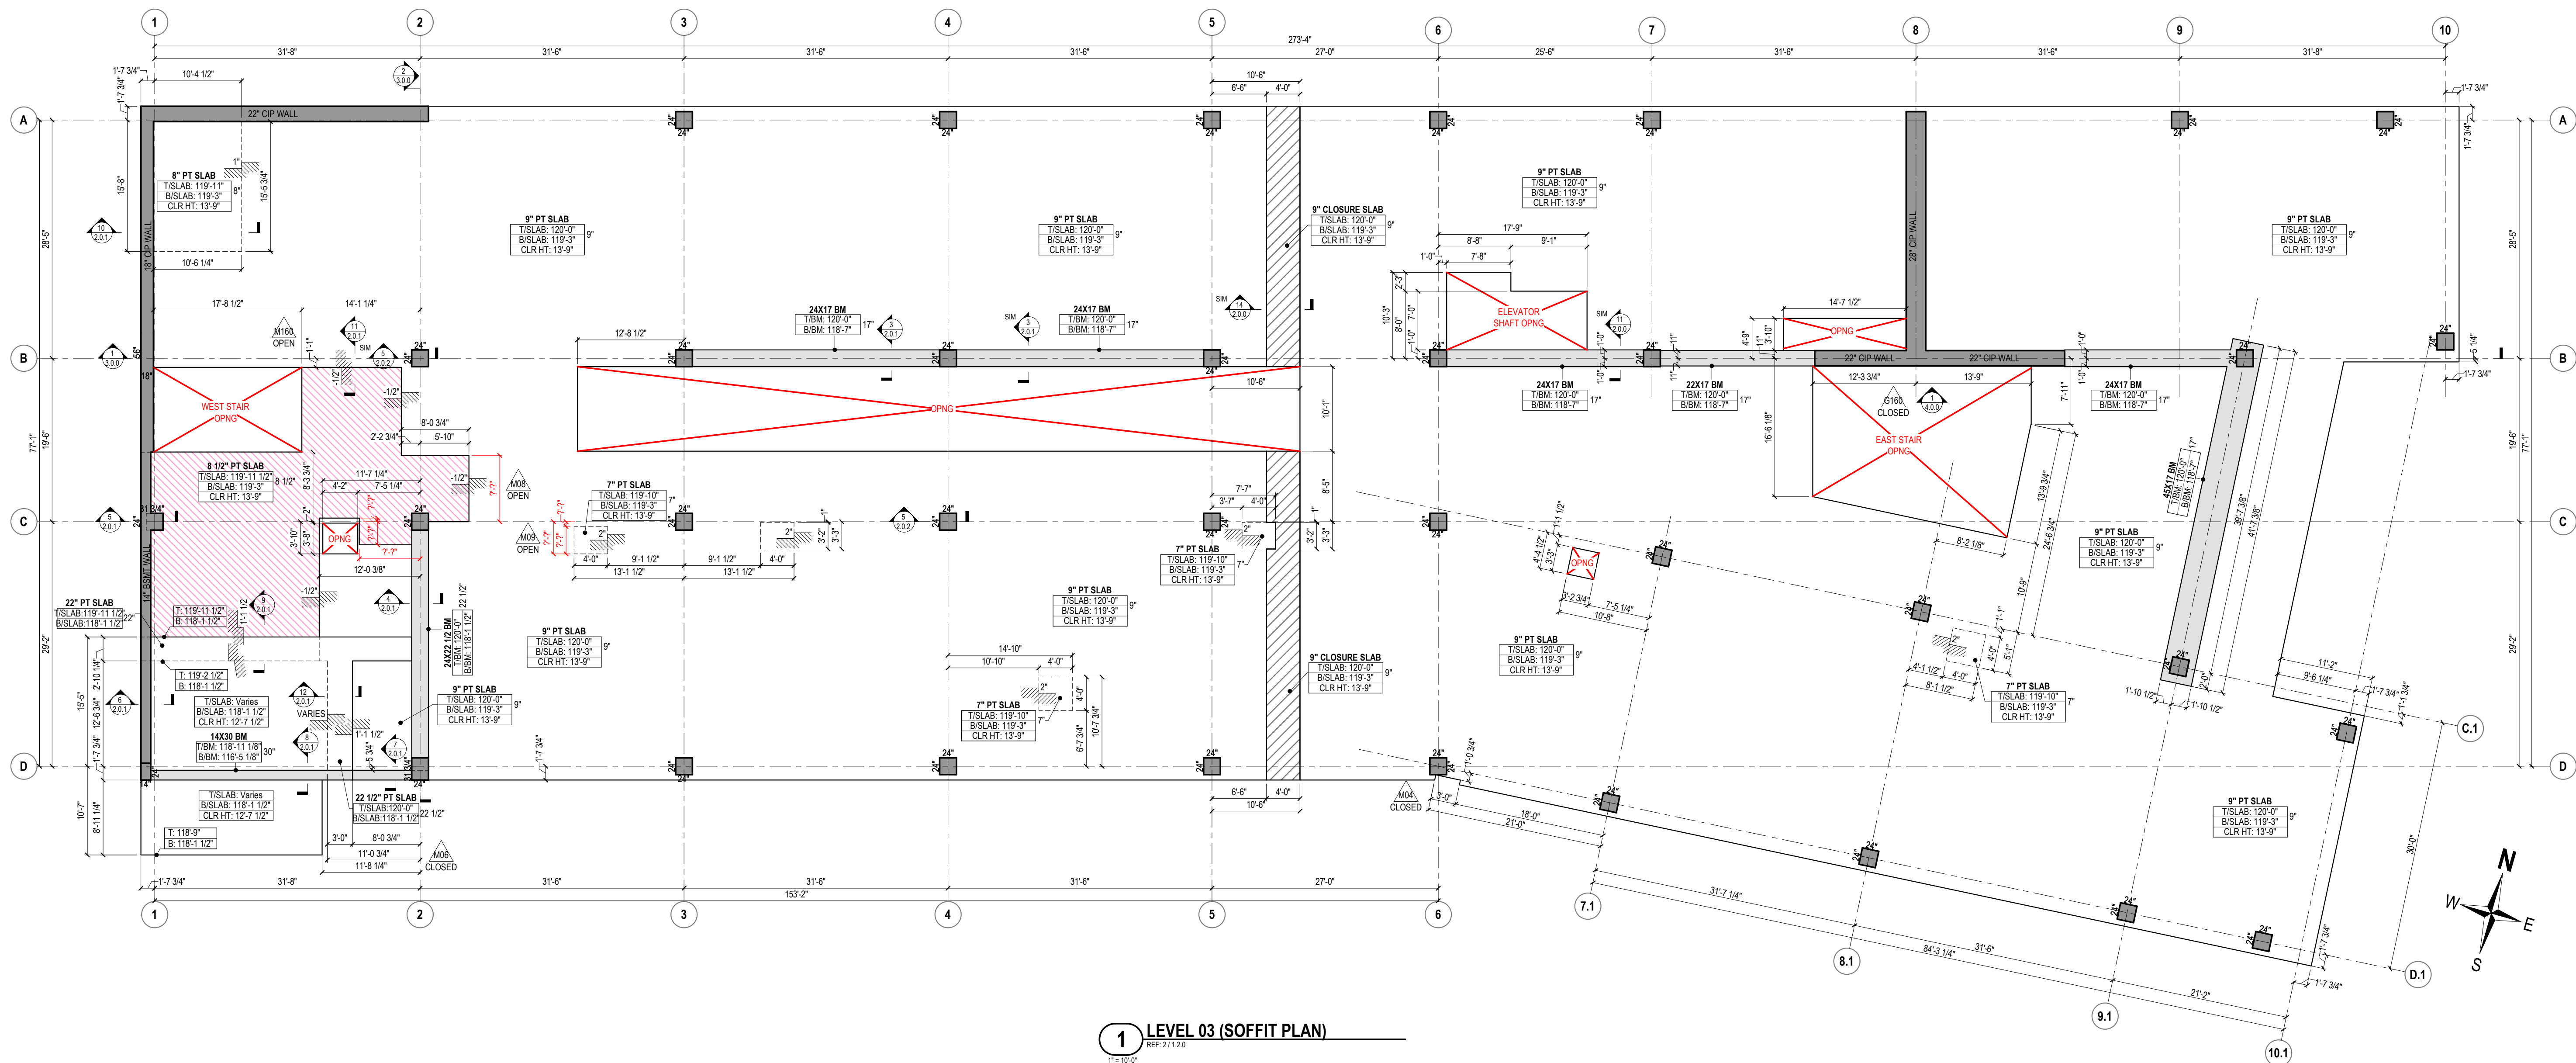


1 LEVEL 03 (SOFFIT PLAN)

1" = 10'-0"

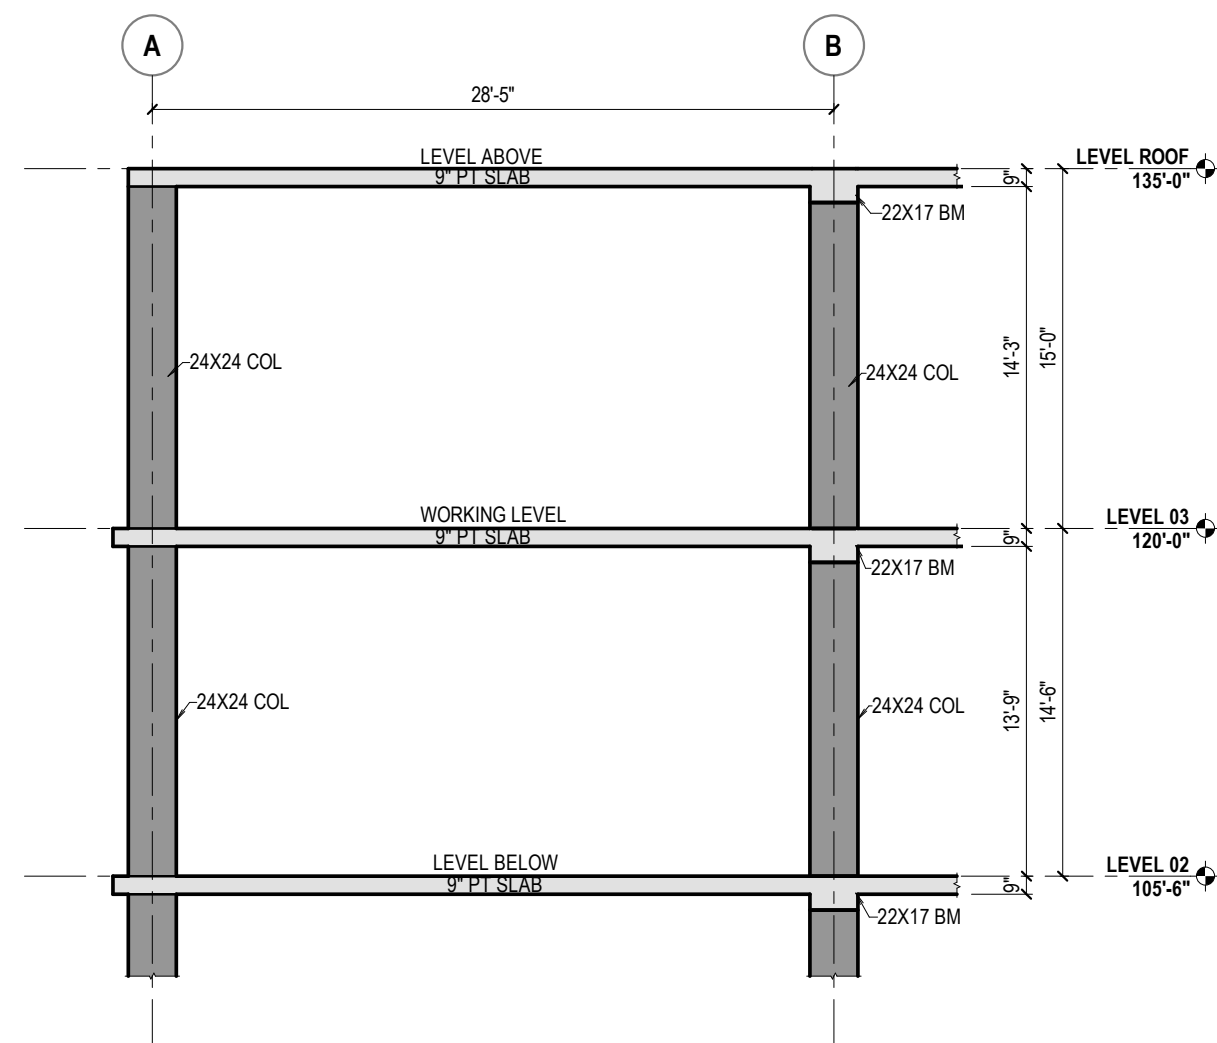


2 BUILDING ELEVATION - LEVEL 03

1/8" = 1'-0"

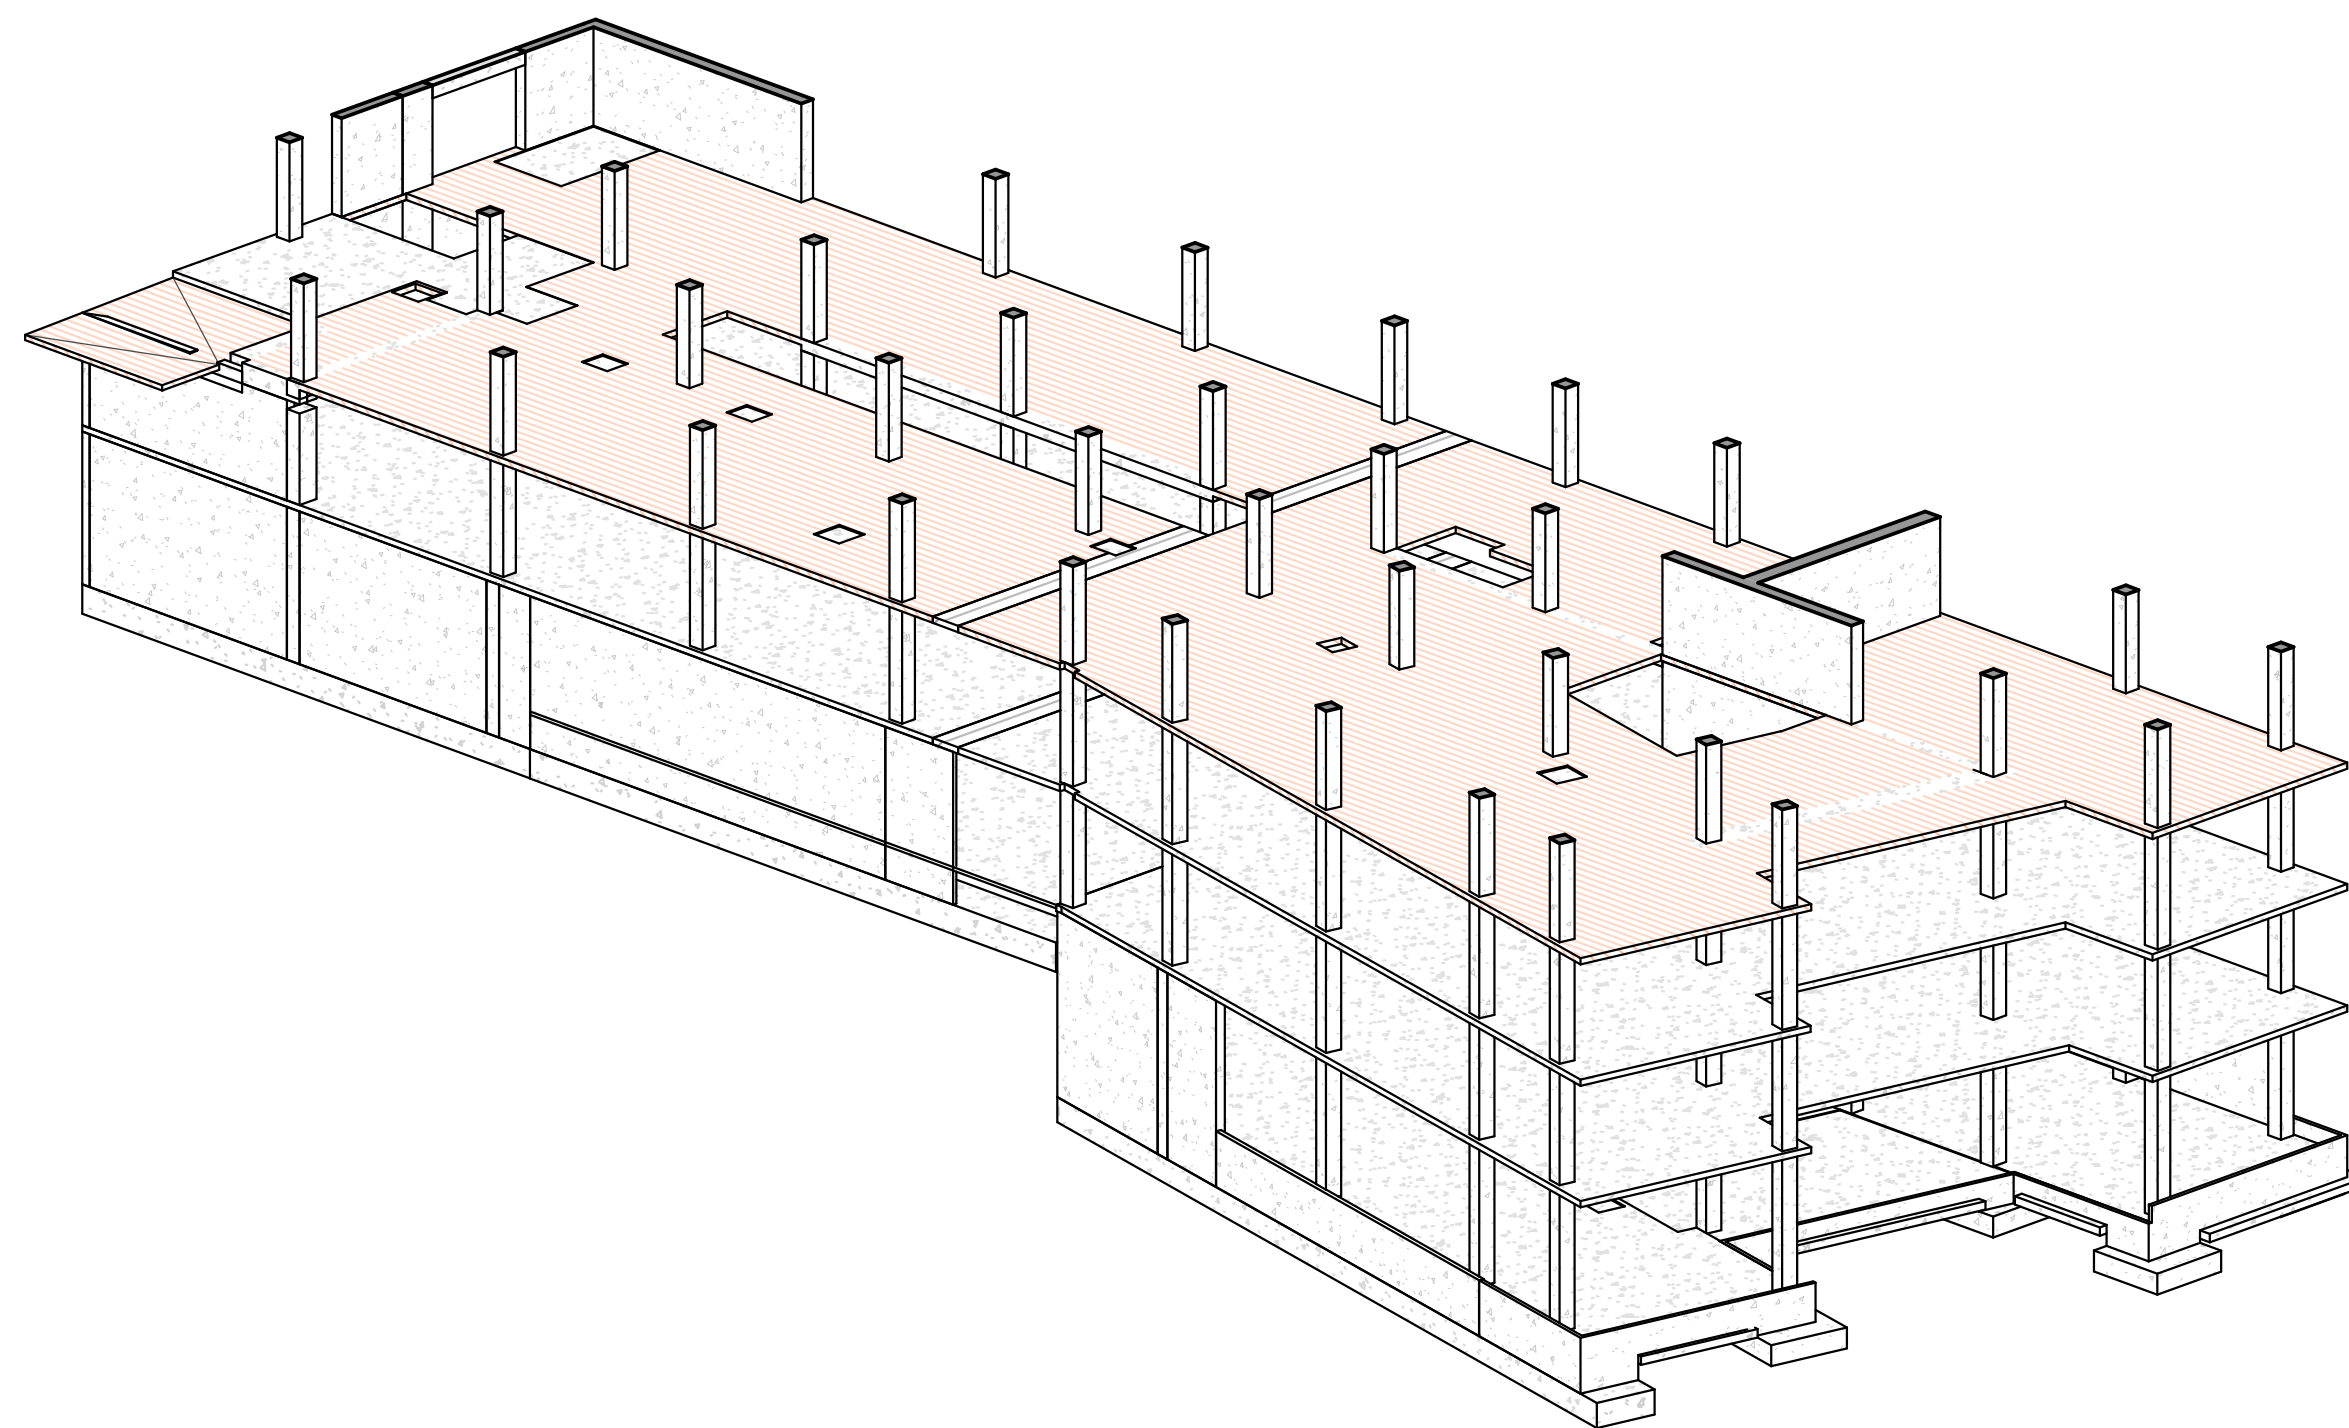

3 3D VIEW - LEVEL 03

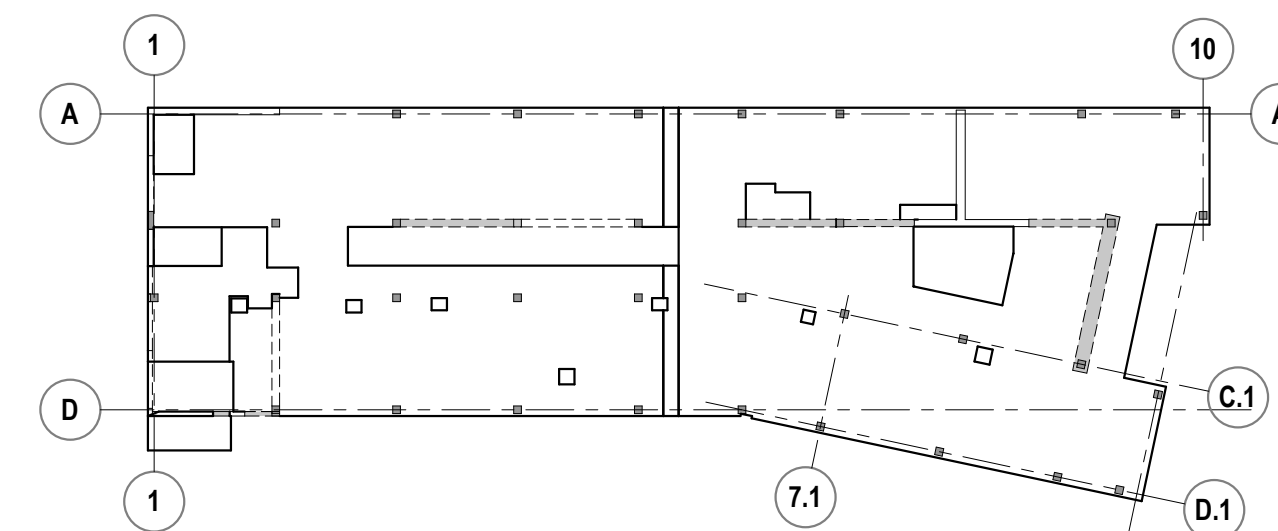

KEYPLAN LEVEL 03

NOTES:

- 3/4" CHAMFER ON ALL EXPOSED CONCRETE CORNERS TYP.
- ALL COLUMNS ARE CENTERED ON GRID LINES U.N.O.
- ALL BEAMS ARE CENTERED ON GRID LINES U.N.O.
- SLAB THICKNESS IS 9" TYP. U.N.O.
- DO NOT SCALE THIS DRAWING. USE DIMENSIONS PROVIDED.

LEGEND

SYMBOLS

- 1-BOX (ROUND-ENDS)
TOP OF CONCRETE ELEVATIONS
- 1-BOX
BOTTOM OF CONCRETE ELEVATIONS
- 2-BOX (PLAN VIEWS)
TOP & BOTTOM ELEVATIONS
D = DEPTH OF CONC. MEMBER
- 3-BOX (SOFFIT PLANS)
TOP & BOTTOM ELEVATIONS
HEIGHT BELOW REFERENCE LEVEL
D = DEPTH OF CONC. MEMBER

- SECTION VIEW
SHEET NUMBER
ELEVATION VIEW
SHEET NUMBER





SHADE DESIGNATIONS

- BEAM OR DROP CAP
- WALLS OR COLUMNS
- CMU WALLS
- DELAY STRIP OR CLOSURE POUR
- GRADE OR SOIL
- 1/2" SLAB DEPRESSION

LINE DESIGNATIONS

- INDICATES TOP OF SLAB CHANGE OR EDGE OF SLAB
- INDICATES SOFFIT CHANGE
- INDICATES CONSTRUCTION JOINT
- INDICATES GRID LINE

THIS DRAWING IS FOR THE EXCLUSIVE USE OF MCCLONE CONSTRUCTION COMPANY. ON THIS PROJECT ONLY. UTILIZATION OF THIS DRAWING BY OTHER PARTIES AND/OR ON OTHER PROJECTS WITHOUT THE EXPRESSED WRITTEN CONSENT OF MCCLONE CONSTRUCTION COMPANY IS STRICTLY PROHIBITED.

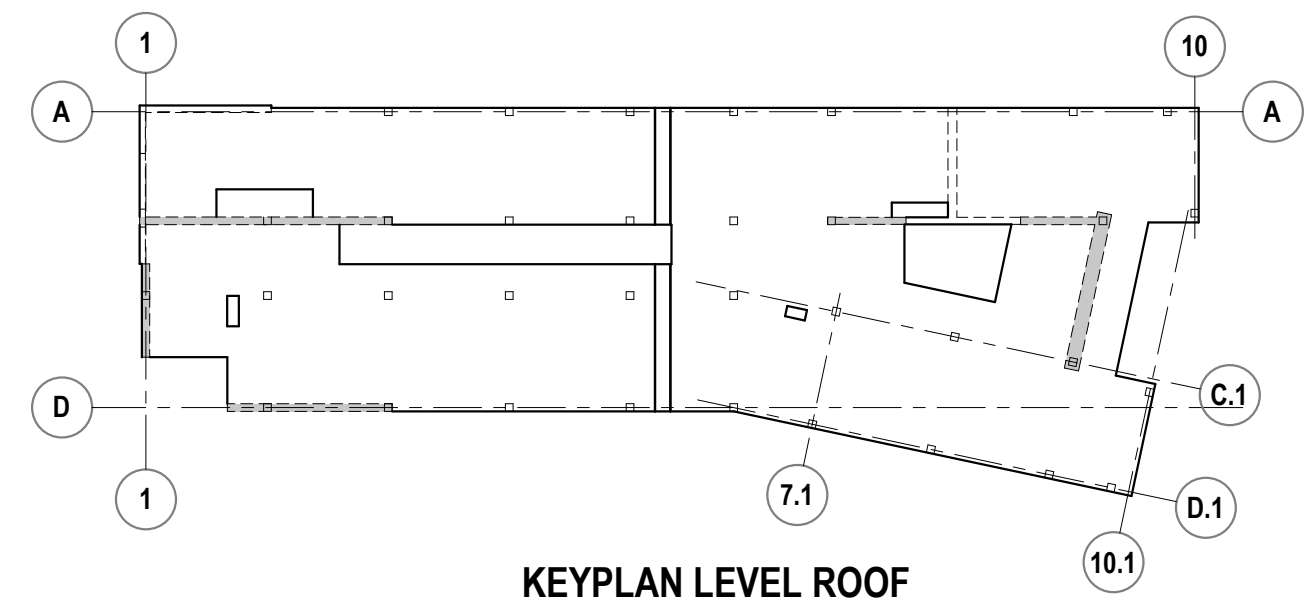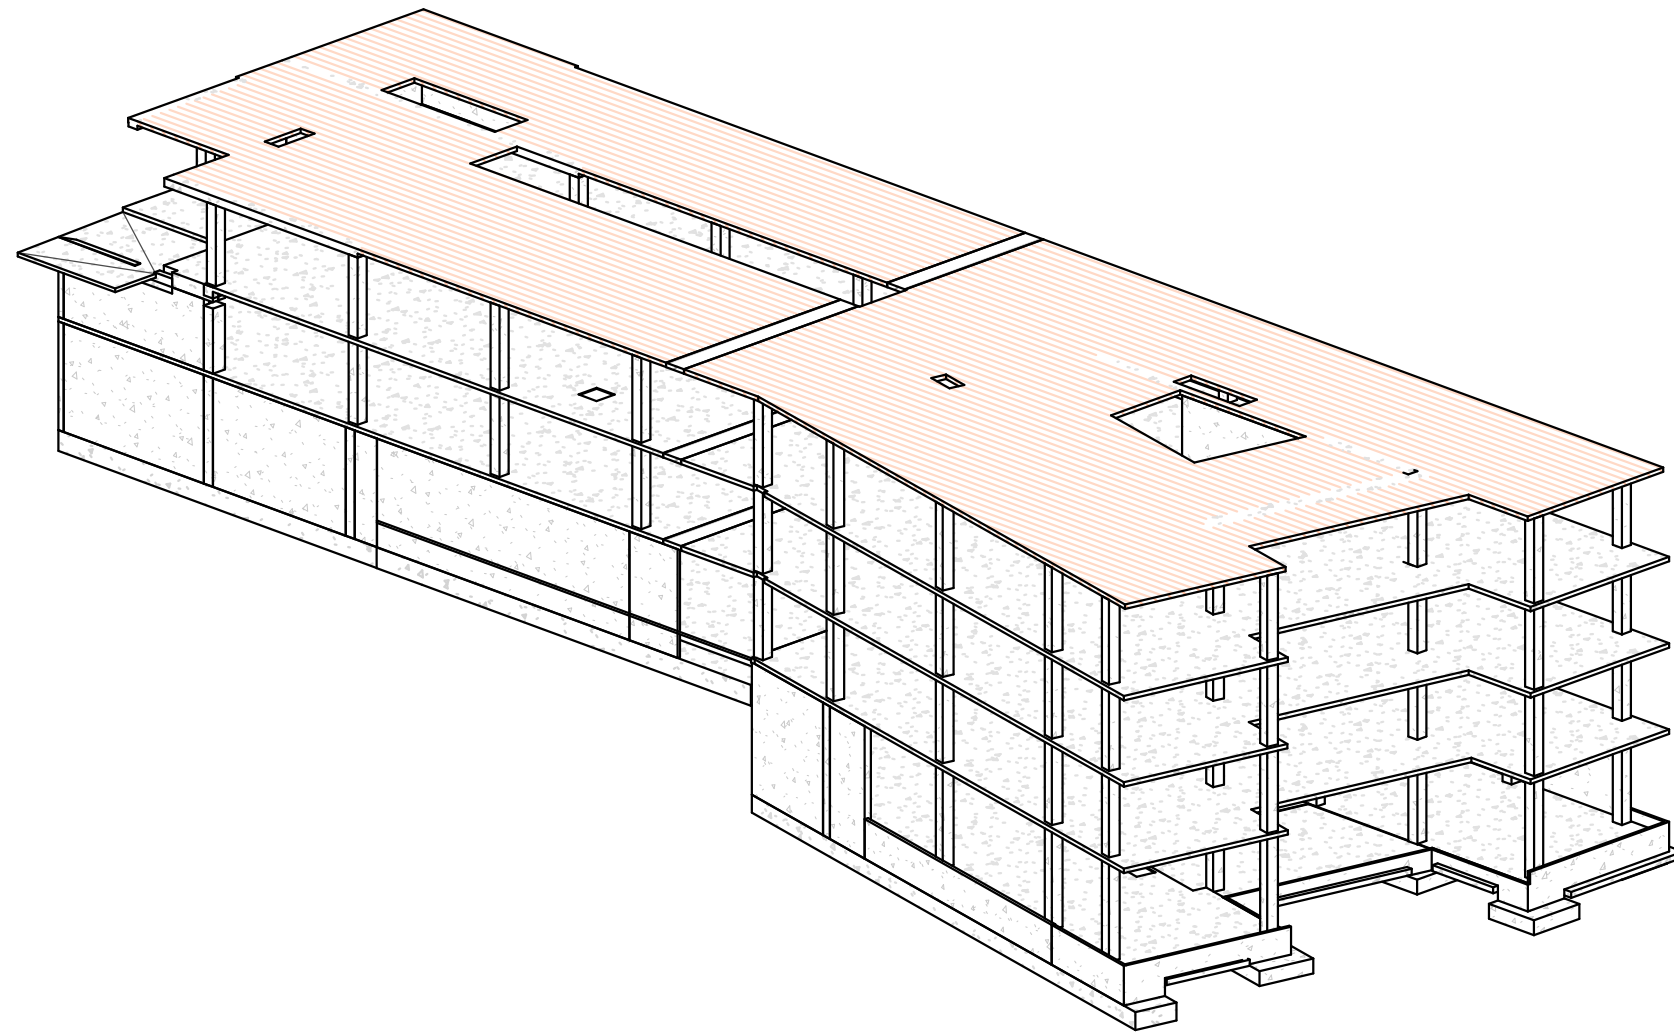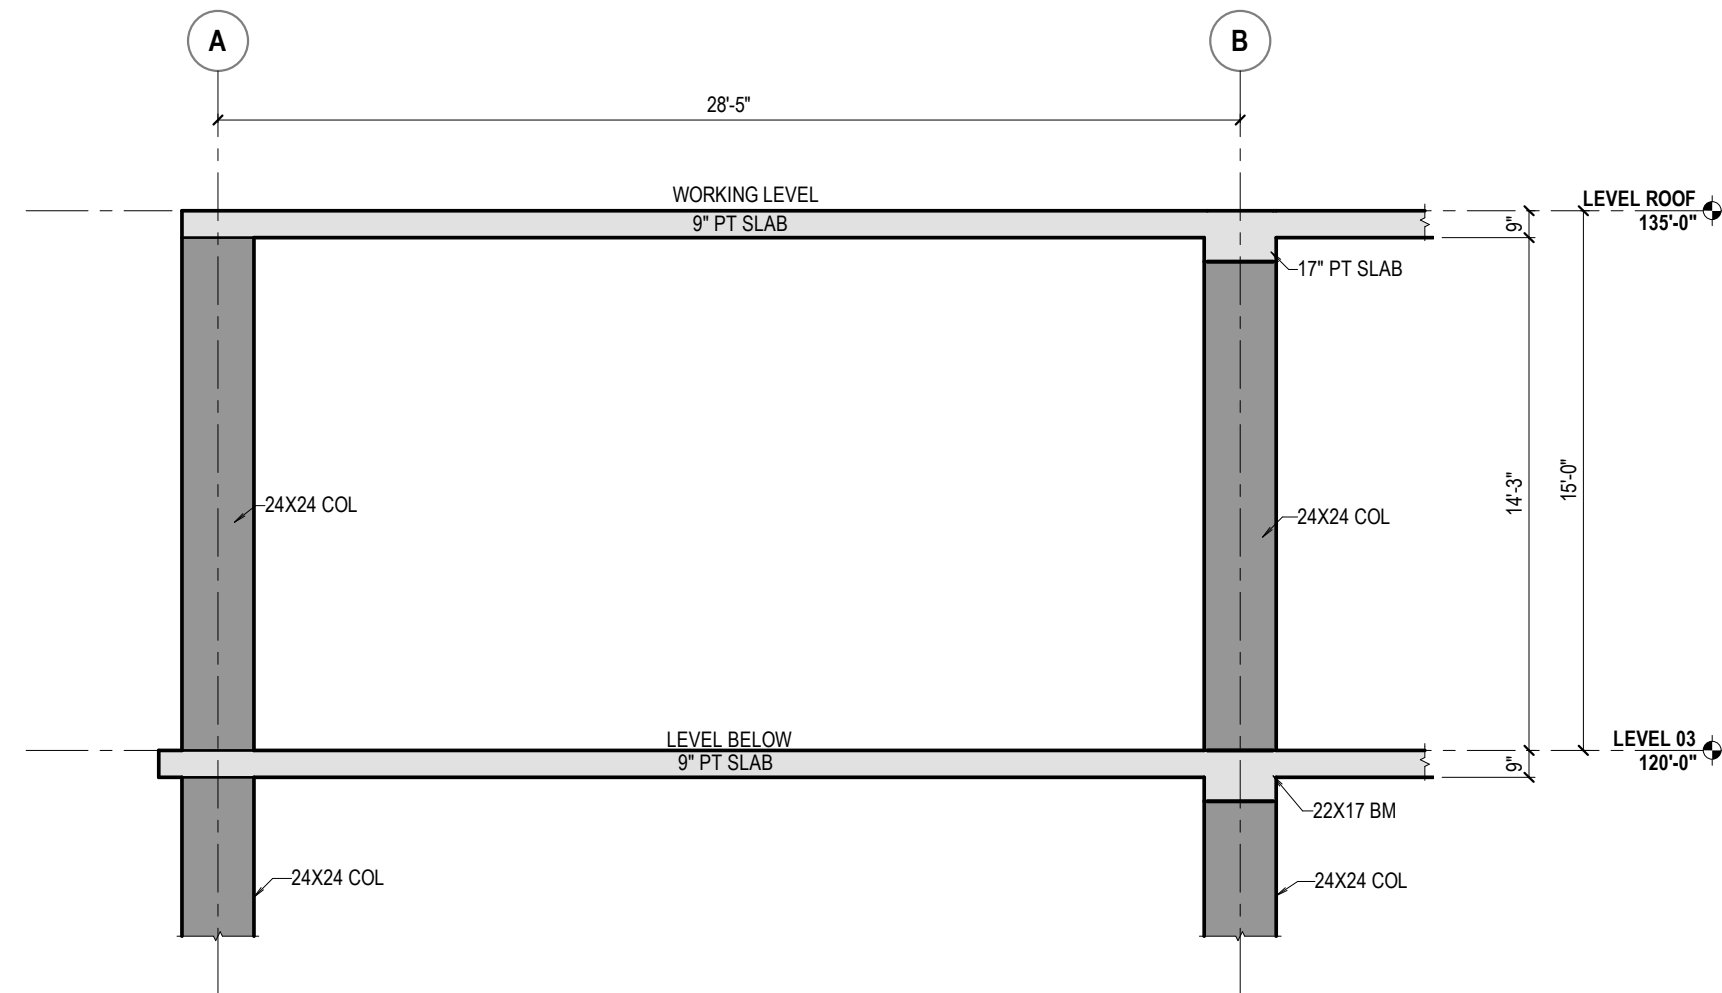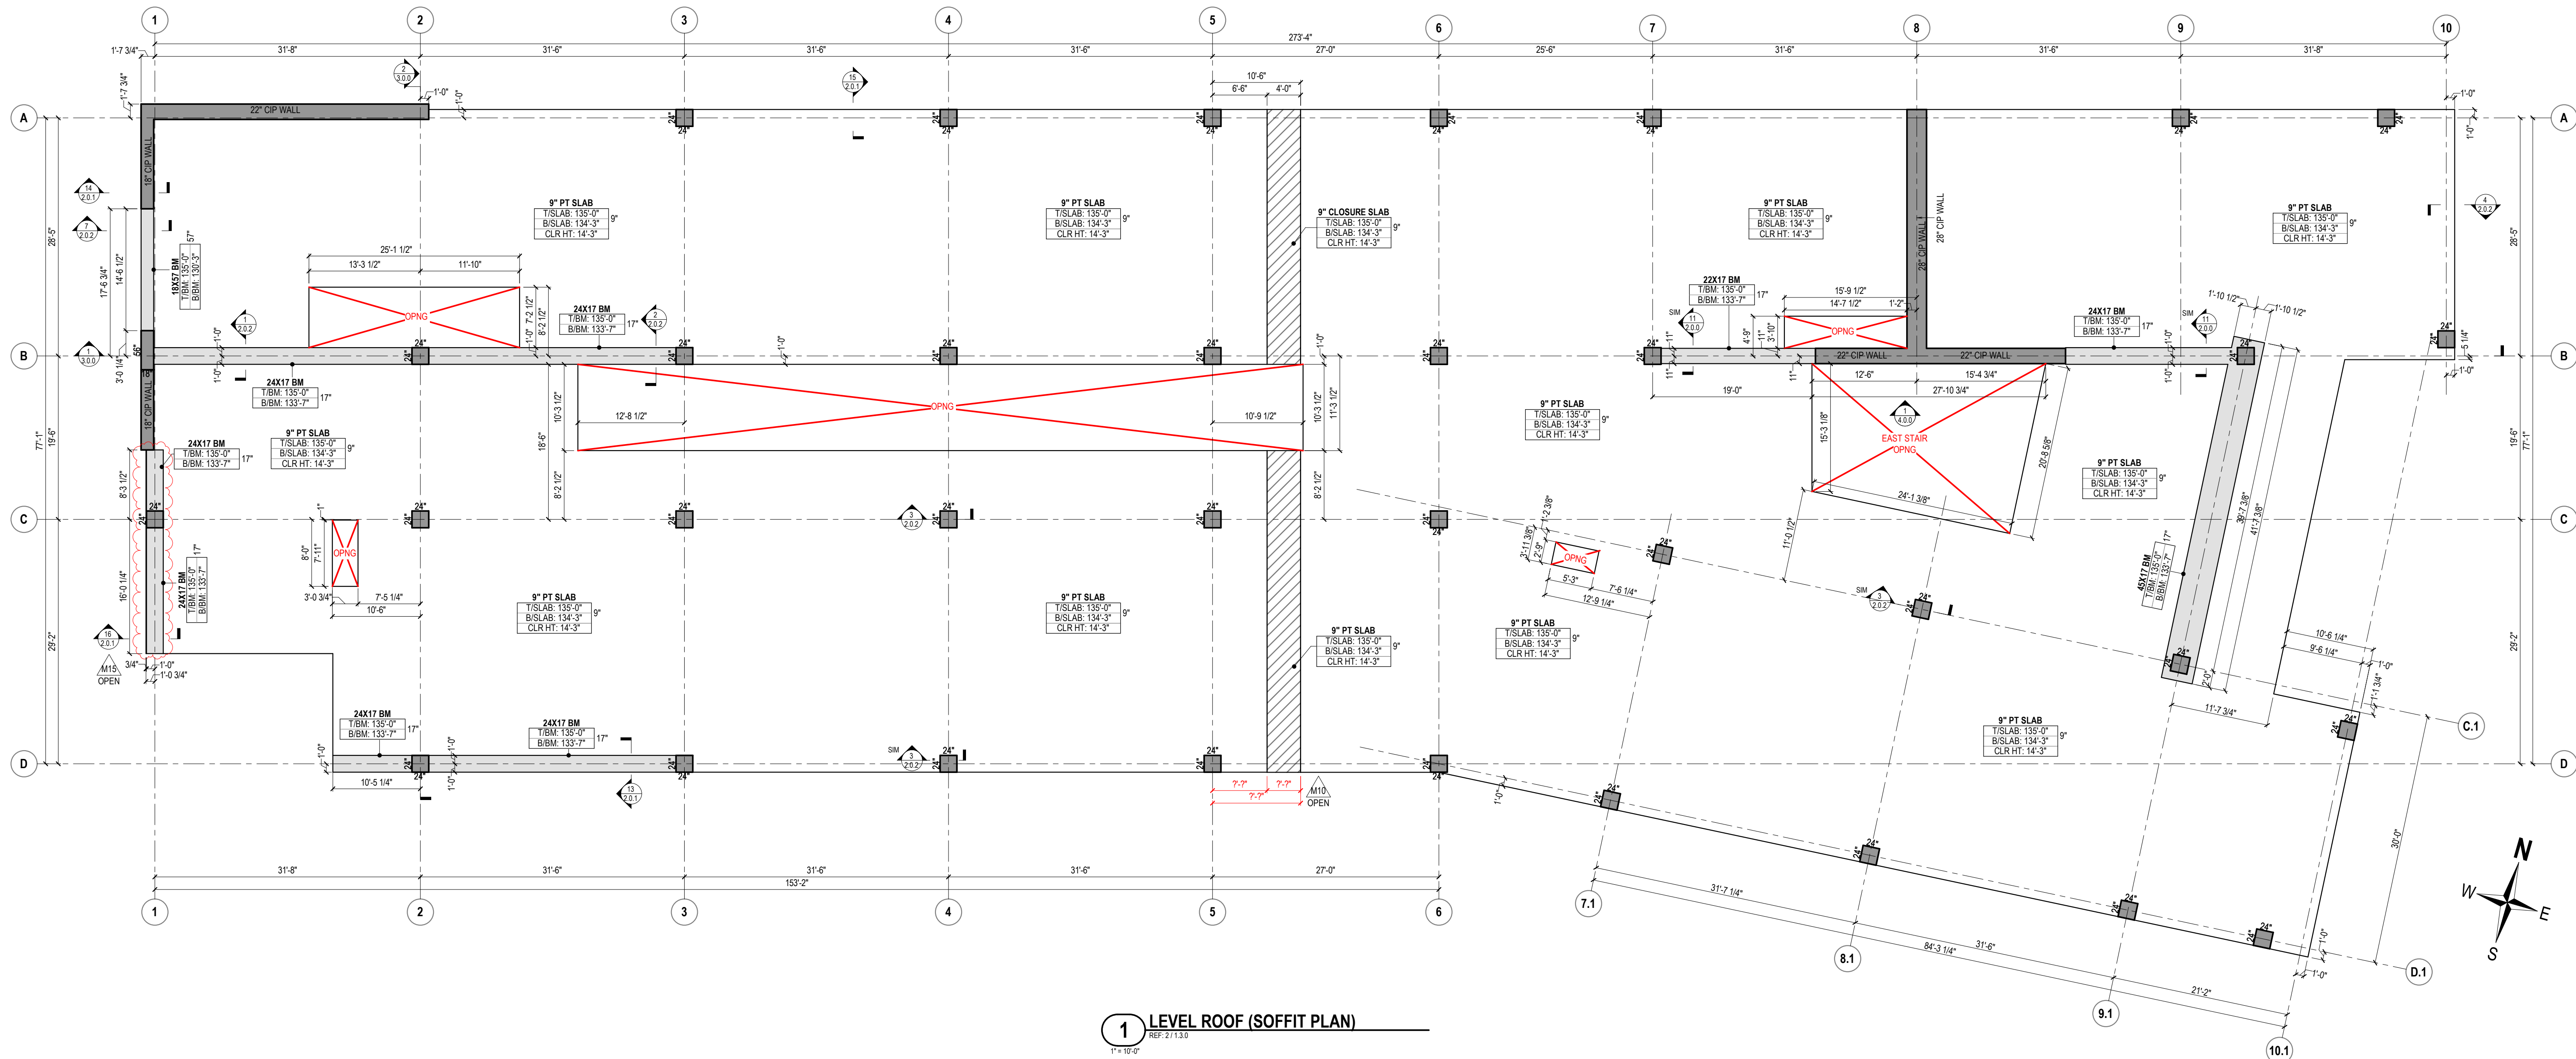

NOTES:

- 3/4\"/>
- ALL COLUMNS ARE CENTERED ON GRID LINES U.N.O.
- ALL BEAMS ARE CENTERED ON GRID LINES U.N.O.
- SLAB THICKNESS IS 9\"/>
- DO NOT SCALE THIS DRAWING. USE DIMENSIONS PROVIDED.

LEGEND

SYMBOLS

- 1-BOX (ROUND-ENDS)
TOP OF CONCRETE ELEVATIONS
- 1-BOX
BOTTOM OF CONCRETE ELEVATIONS
- 2-BOX (PLAN VIEWS)
TOP & BOTTOM ELEVATIONS
D = DEPTH OF CONC. MEMBER
- 3-BOX (SOFFIT PLANS)
TOP & BOTTOM ELEVATIONS
HEIGHT BELOW REFERENCE LEVEL
D = DEPTH OF CONC. MEMBER

SECTION VIEW

Ref. DETAIL NUMBER

SHEET NUMBER

ELEVATION VIEW

SHEET NUMBER

SHADE DESIGNATIONS

- BEAM OR DROP CAP
- WALLS OR COLUMNS
- CMU WALLS
- DELAY STRIP OR CLOSURE POUR
- GRADE OR SOIL
- 12\"/>

LINE DESIGNATIONS

- INDICATES TOP OF SLAB CHANGE OR EDGE OF SLAB
- INDICATES SOFFIT CHANGE
- INDICATES CONSTRUCTION JOINT
- INDICATES GRID LINE