

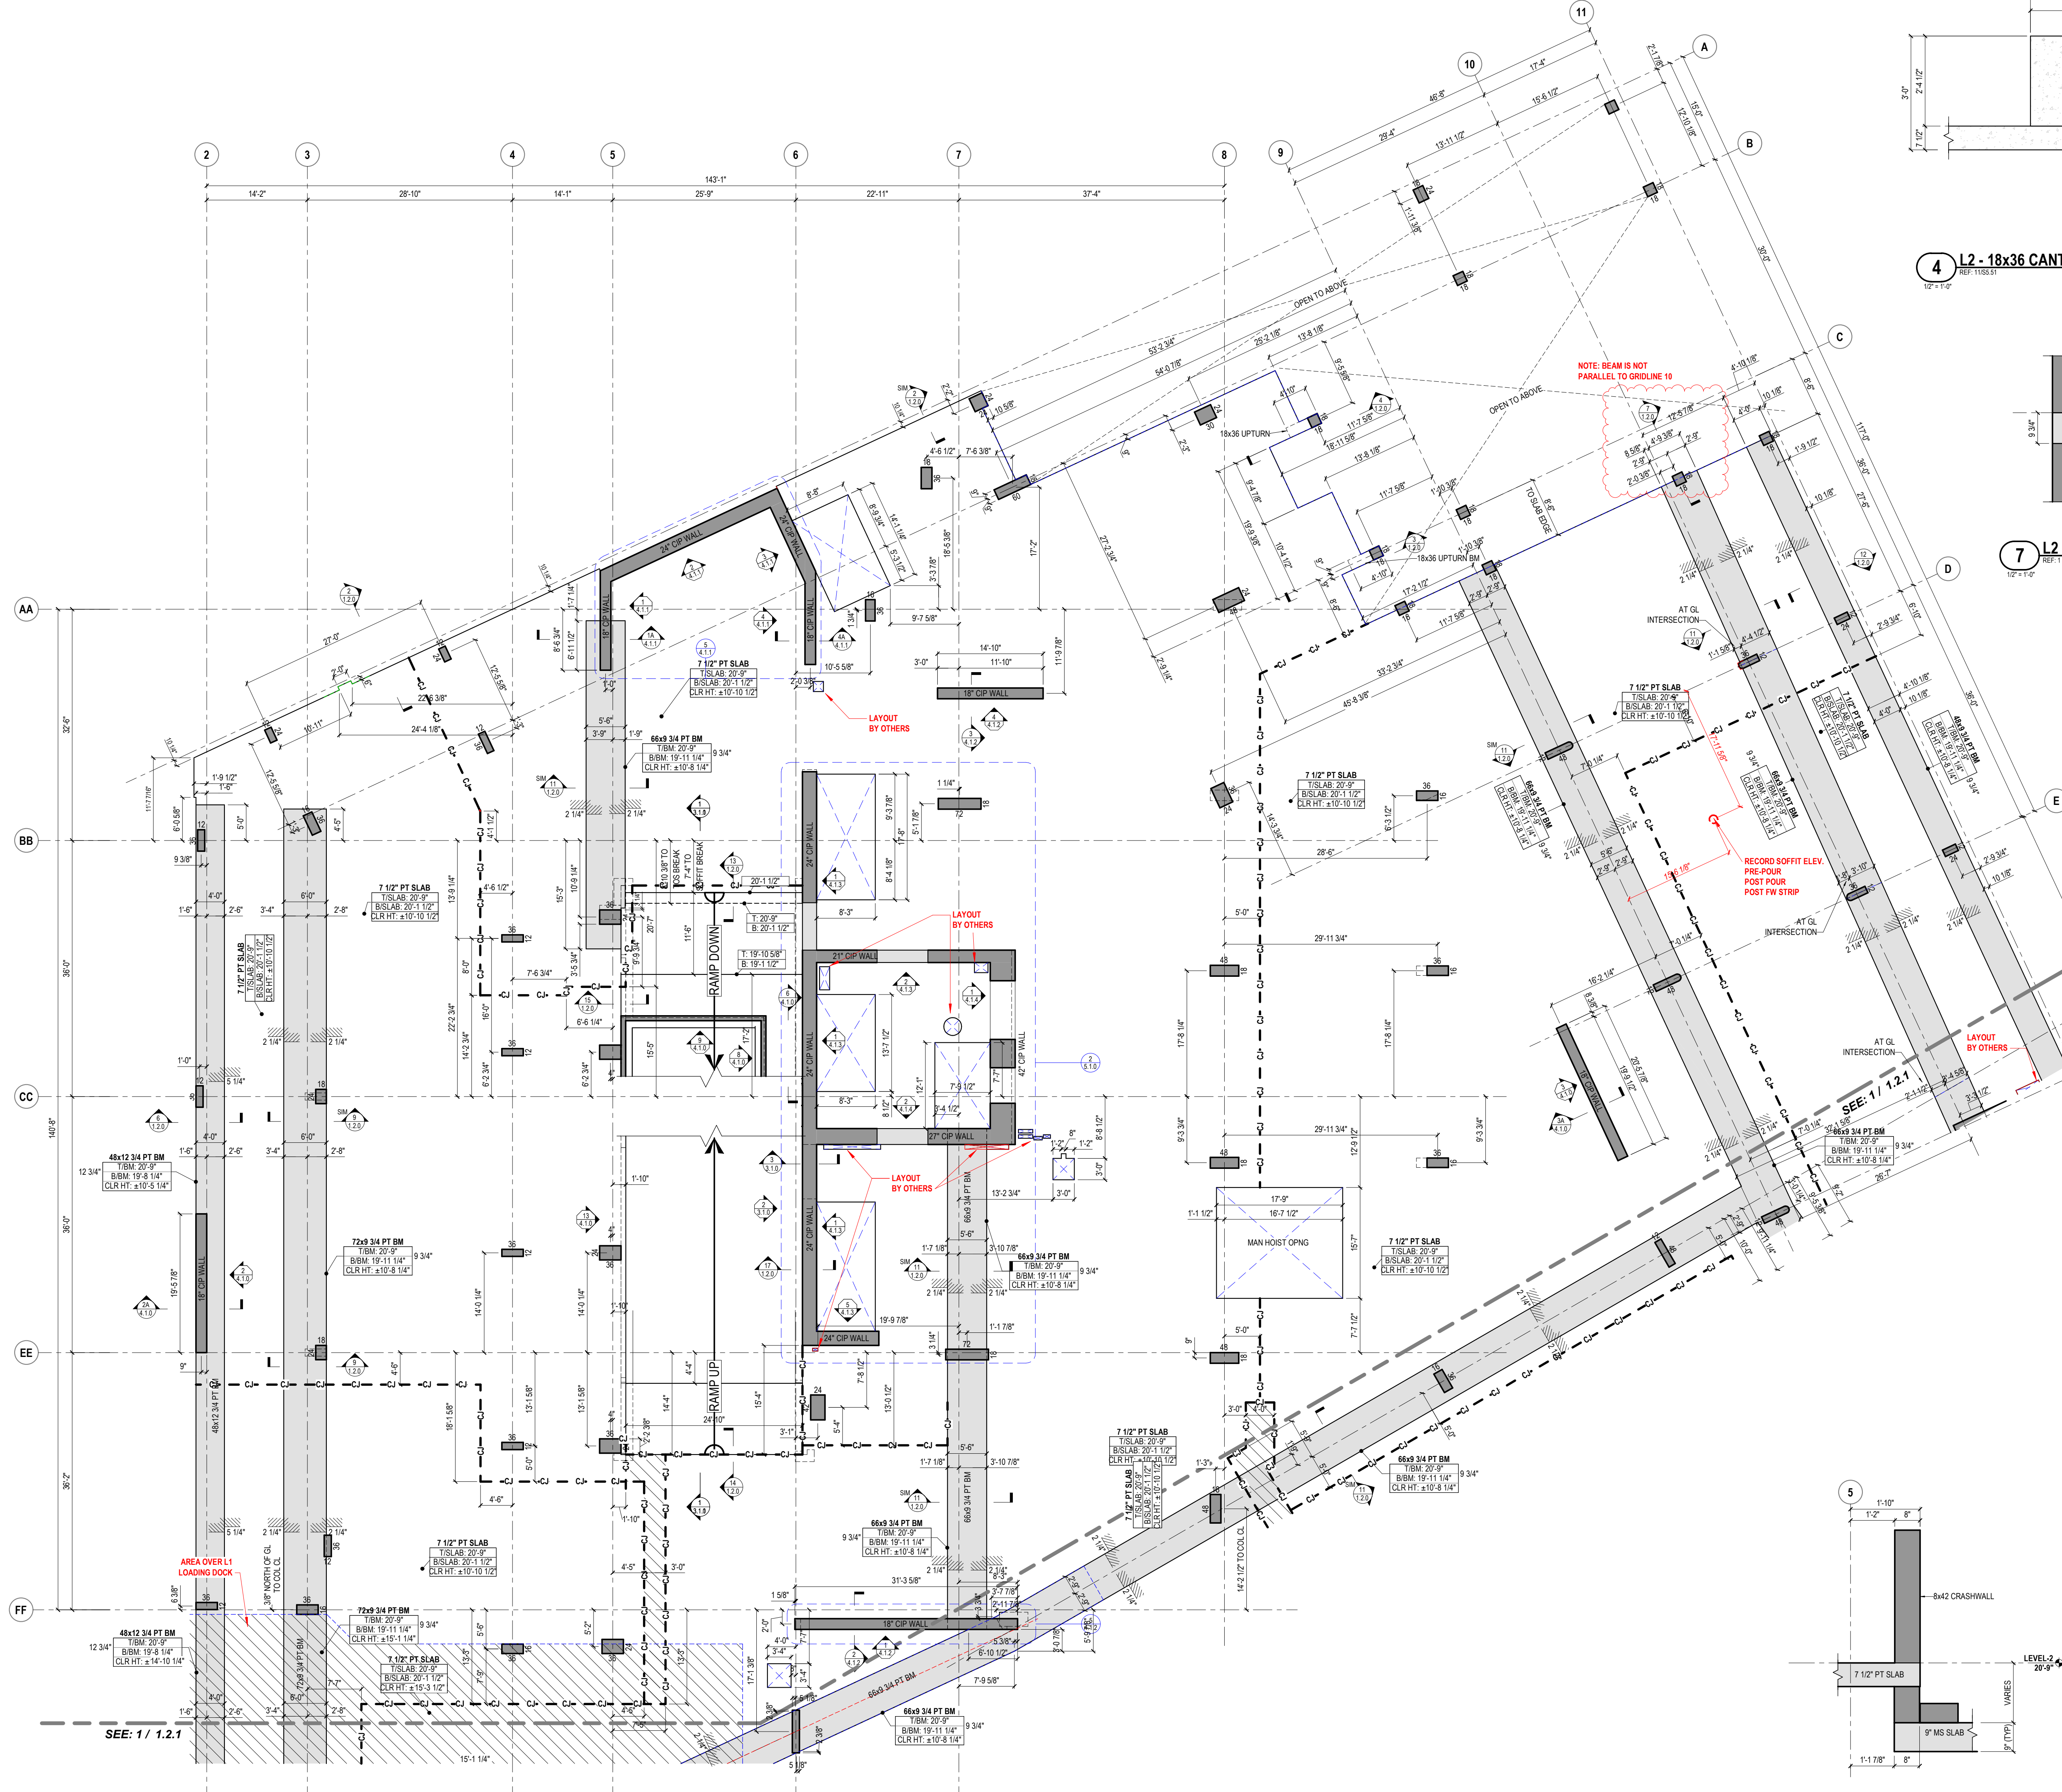


ALL DIMENSIONS SHOWN ARE IN FEET AND INCHES. DIMENSIONS IN PARENTHESES ARE IN METERS. DIMENSIONS IN PARENTHESES ARE IN METERS. DIMENSIONS IN PARENTHESES ARE IN METERS.

THIS DRAWING IS FOR THE EXCLUSIVE USE OF THE CLIENT. IT IS NOT TO BE REPRODUCED OR TRANSMITTED IN ANY FORM OR BY ANY MEANS, ELECTRONIC OR MECHANICAL, WITHOUT THE WRITTEN PERMISSION OF THE CLIENT.

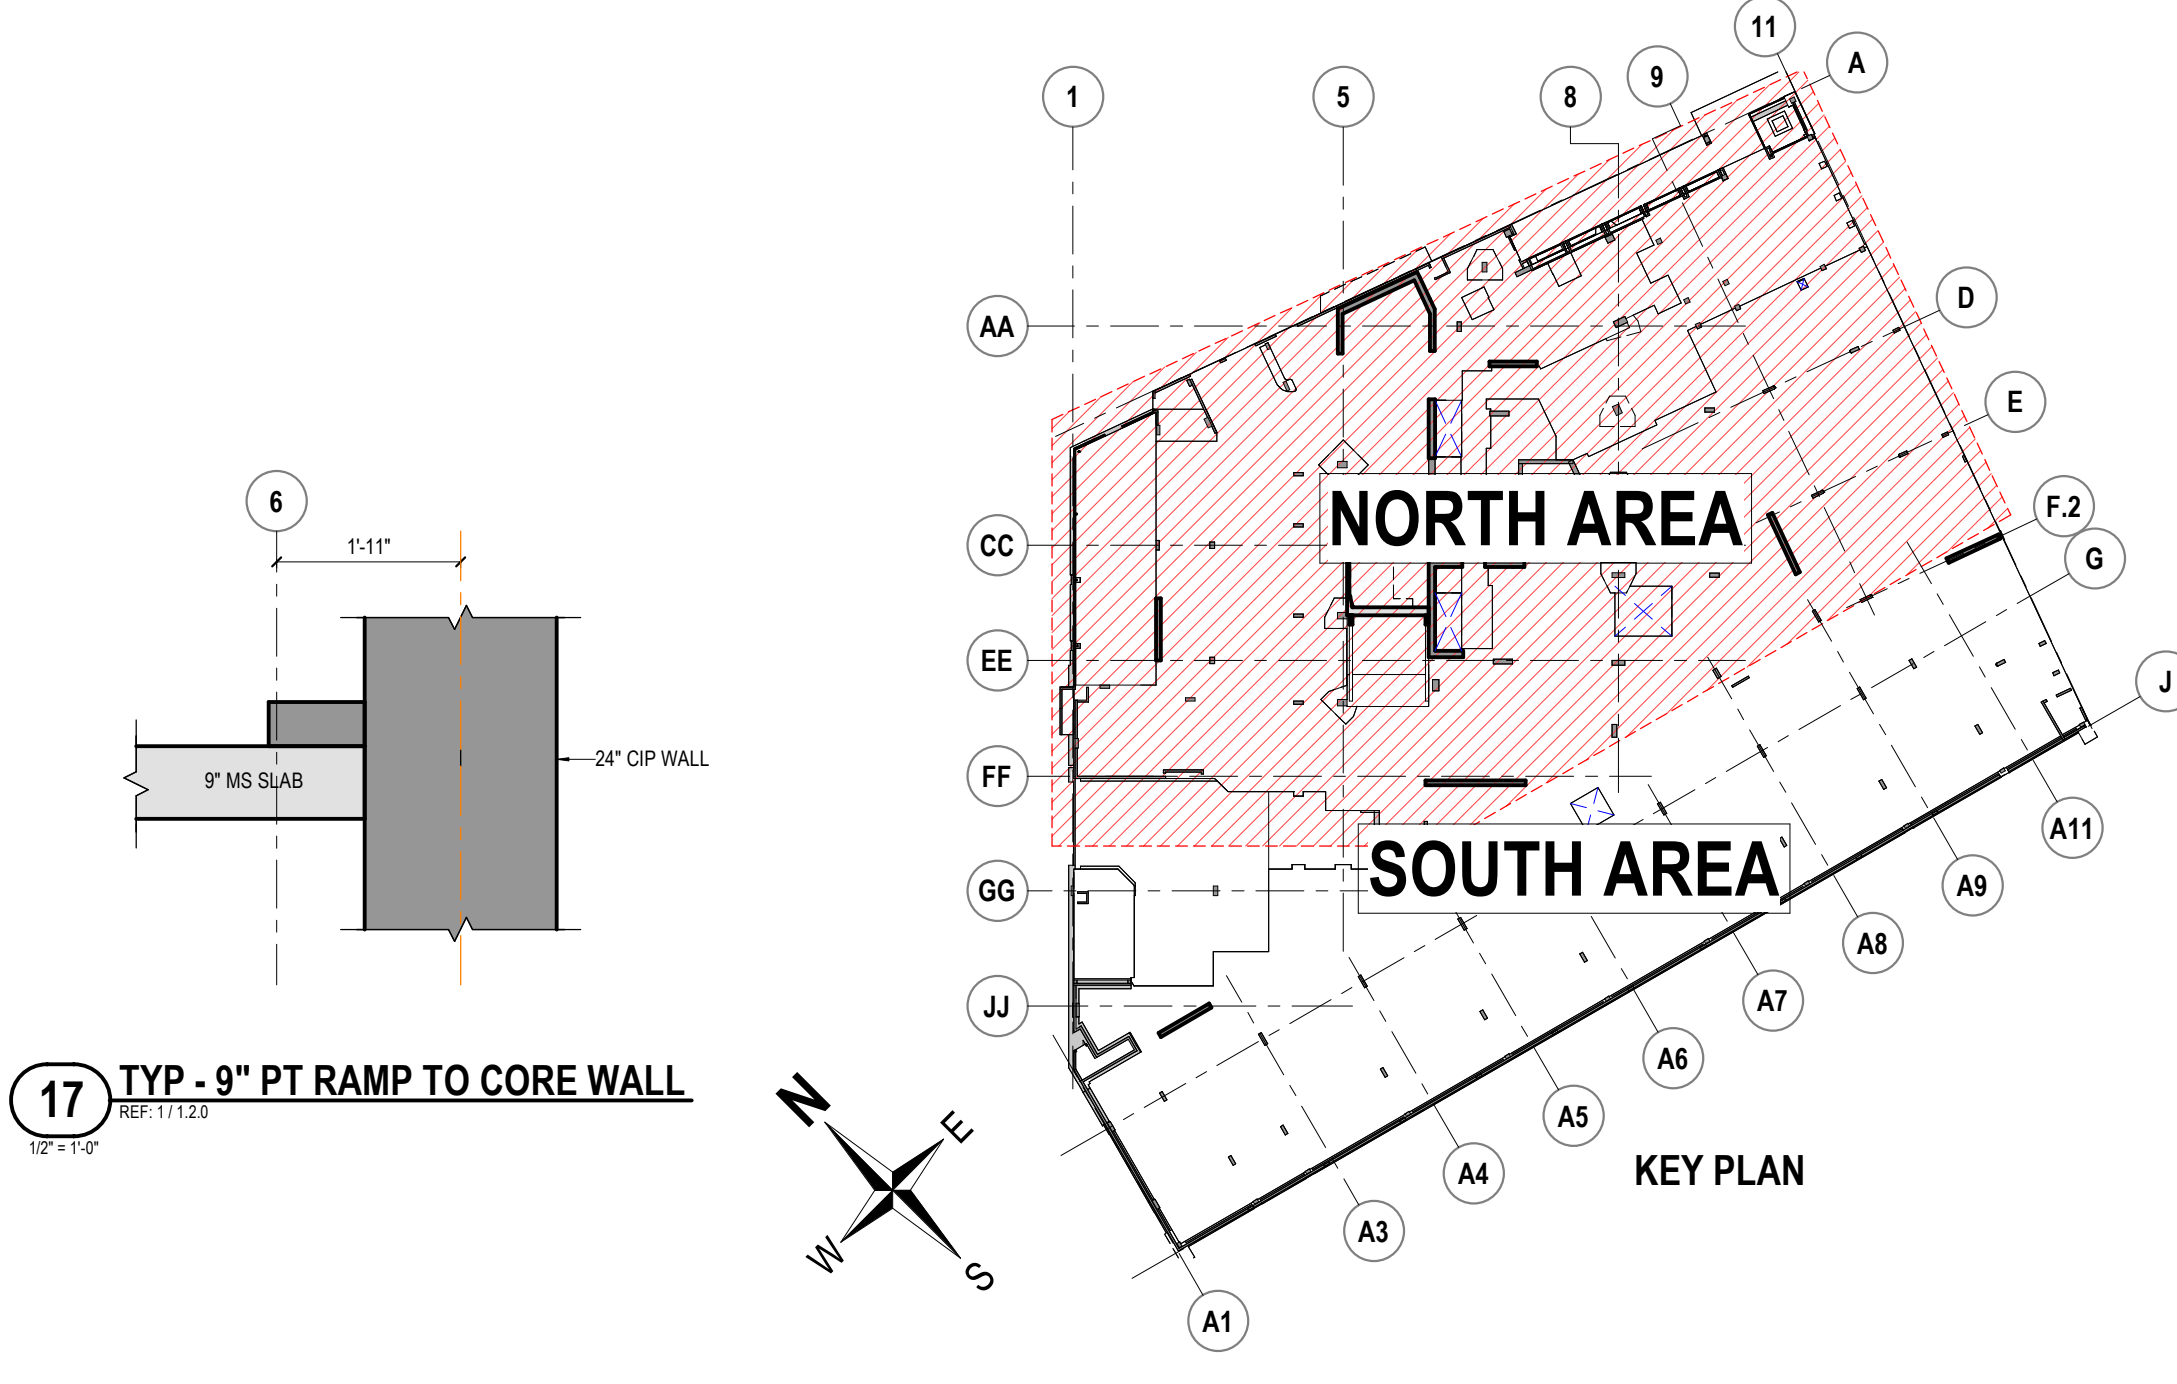

1 LEVEL 2 - NORTH AREA (SOFFIT PLAN)
REF: 1.1, 1.2, 1.3


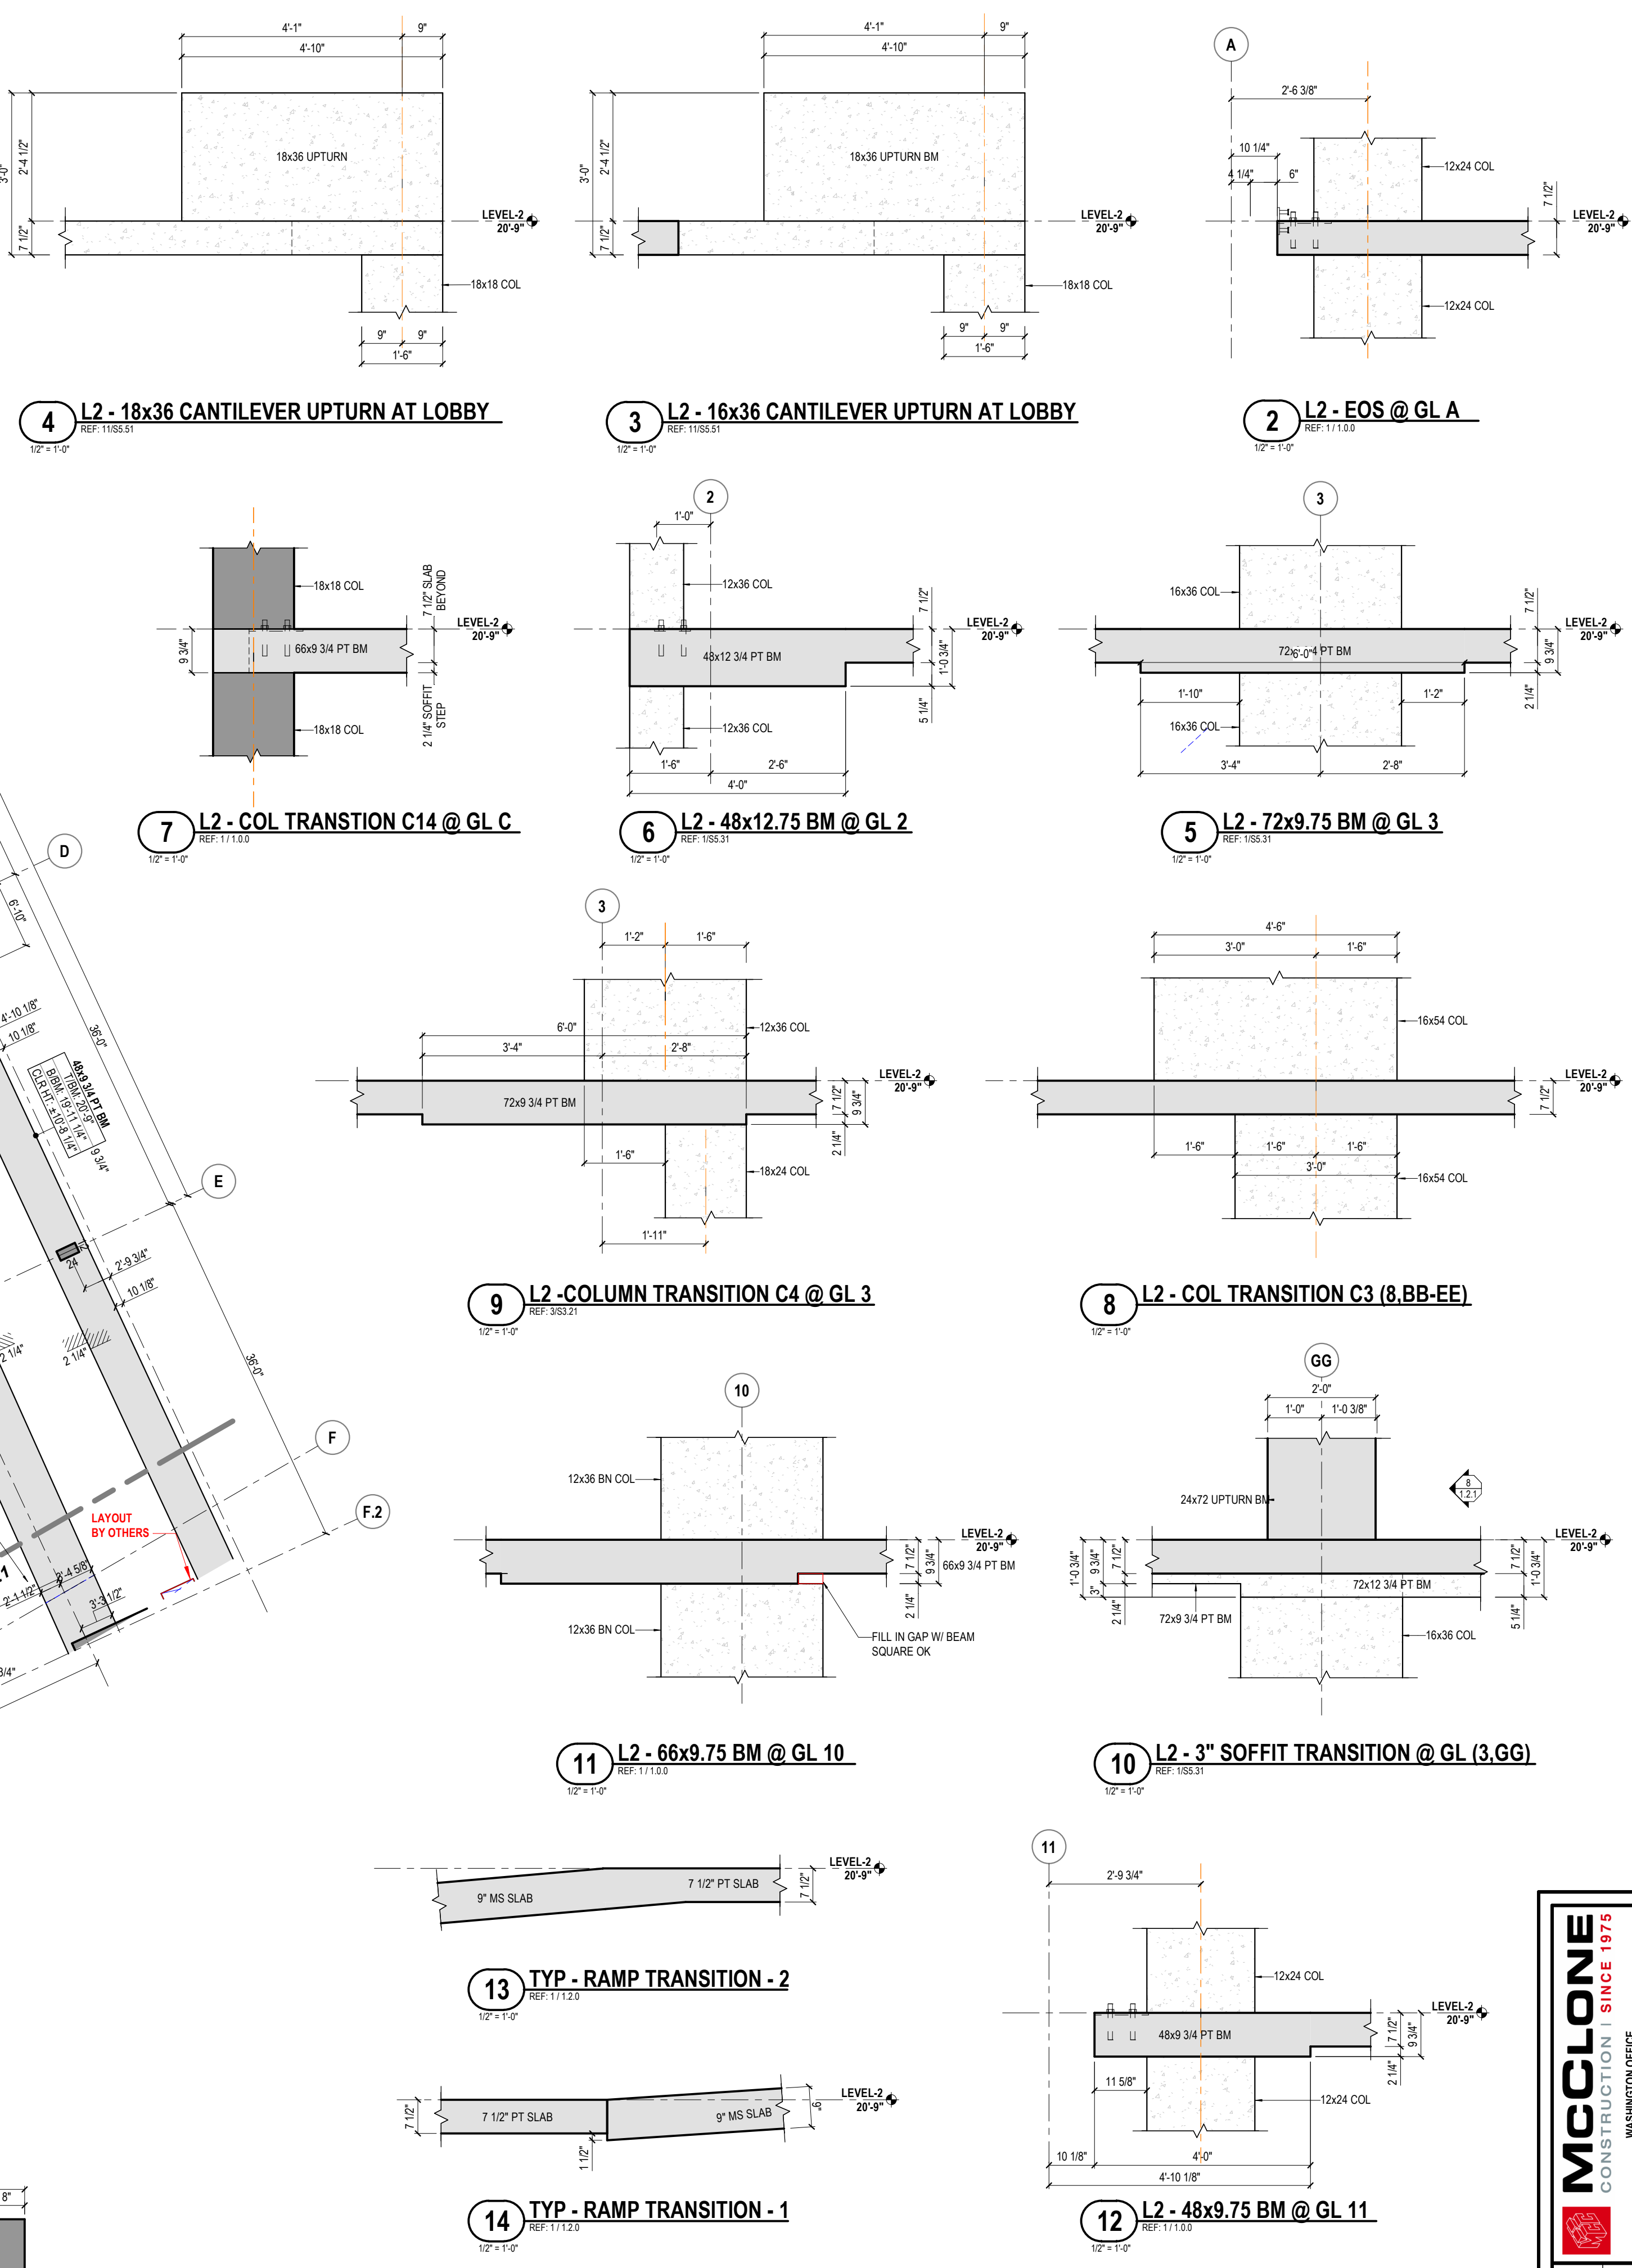


NORTH AREA

SOUTH AREA

KEY PLAN


THIS DRAWING IS FOR THE EXCLUSIVE USE OF MCCCLONE CONSTRUCTION COMPANY. ON THE PROJECT ONLY. UTILIZATION OF THIS DRAWING BY OTHER PARTIES WITHOUT THE EXPRESSED WRITTEN CONSENT OF MCCCLONE CONSTRUCTION COMPANY IS STRICTLY PROHIBITED.

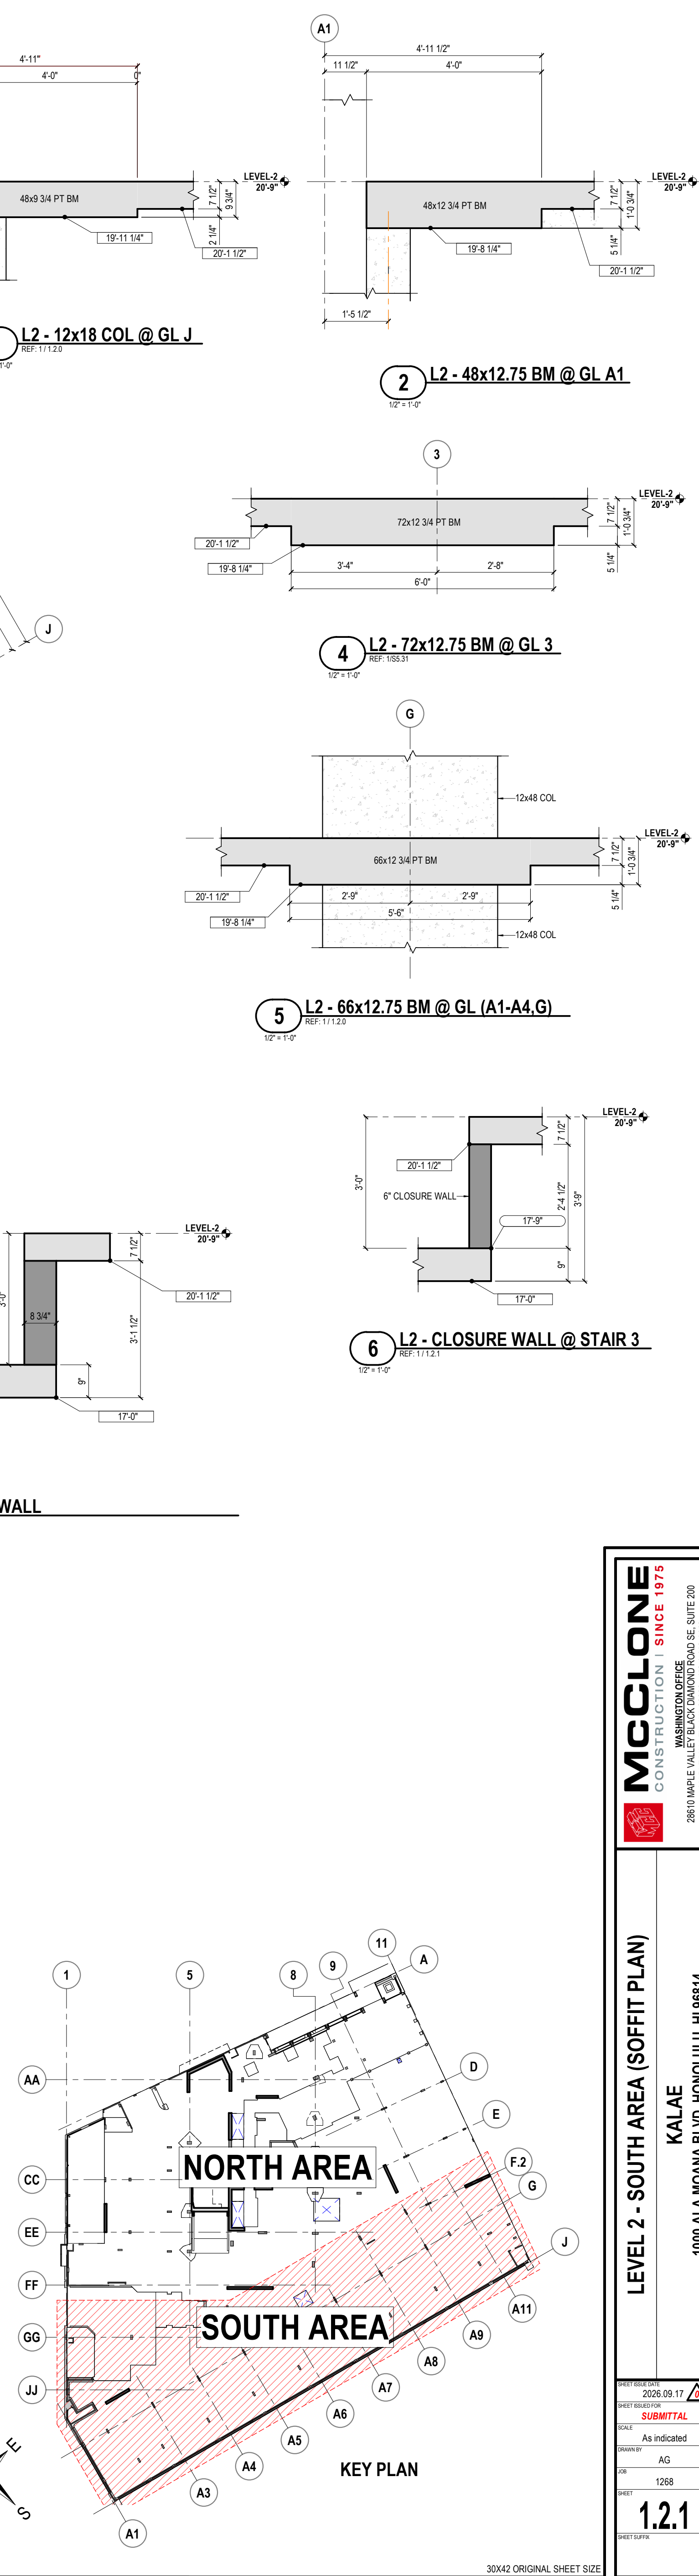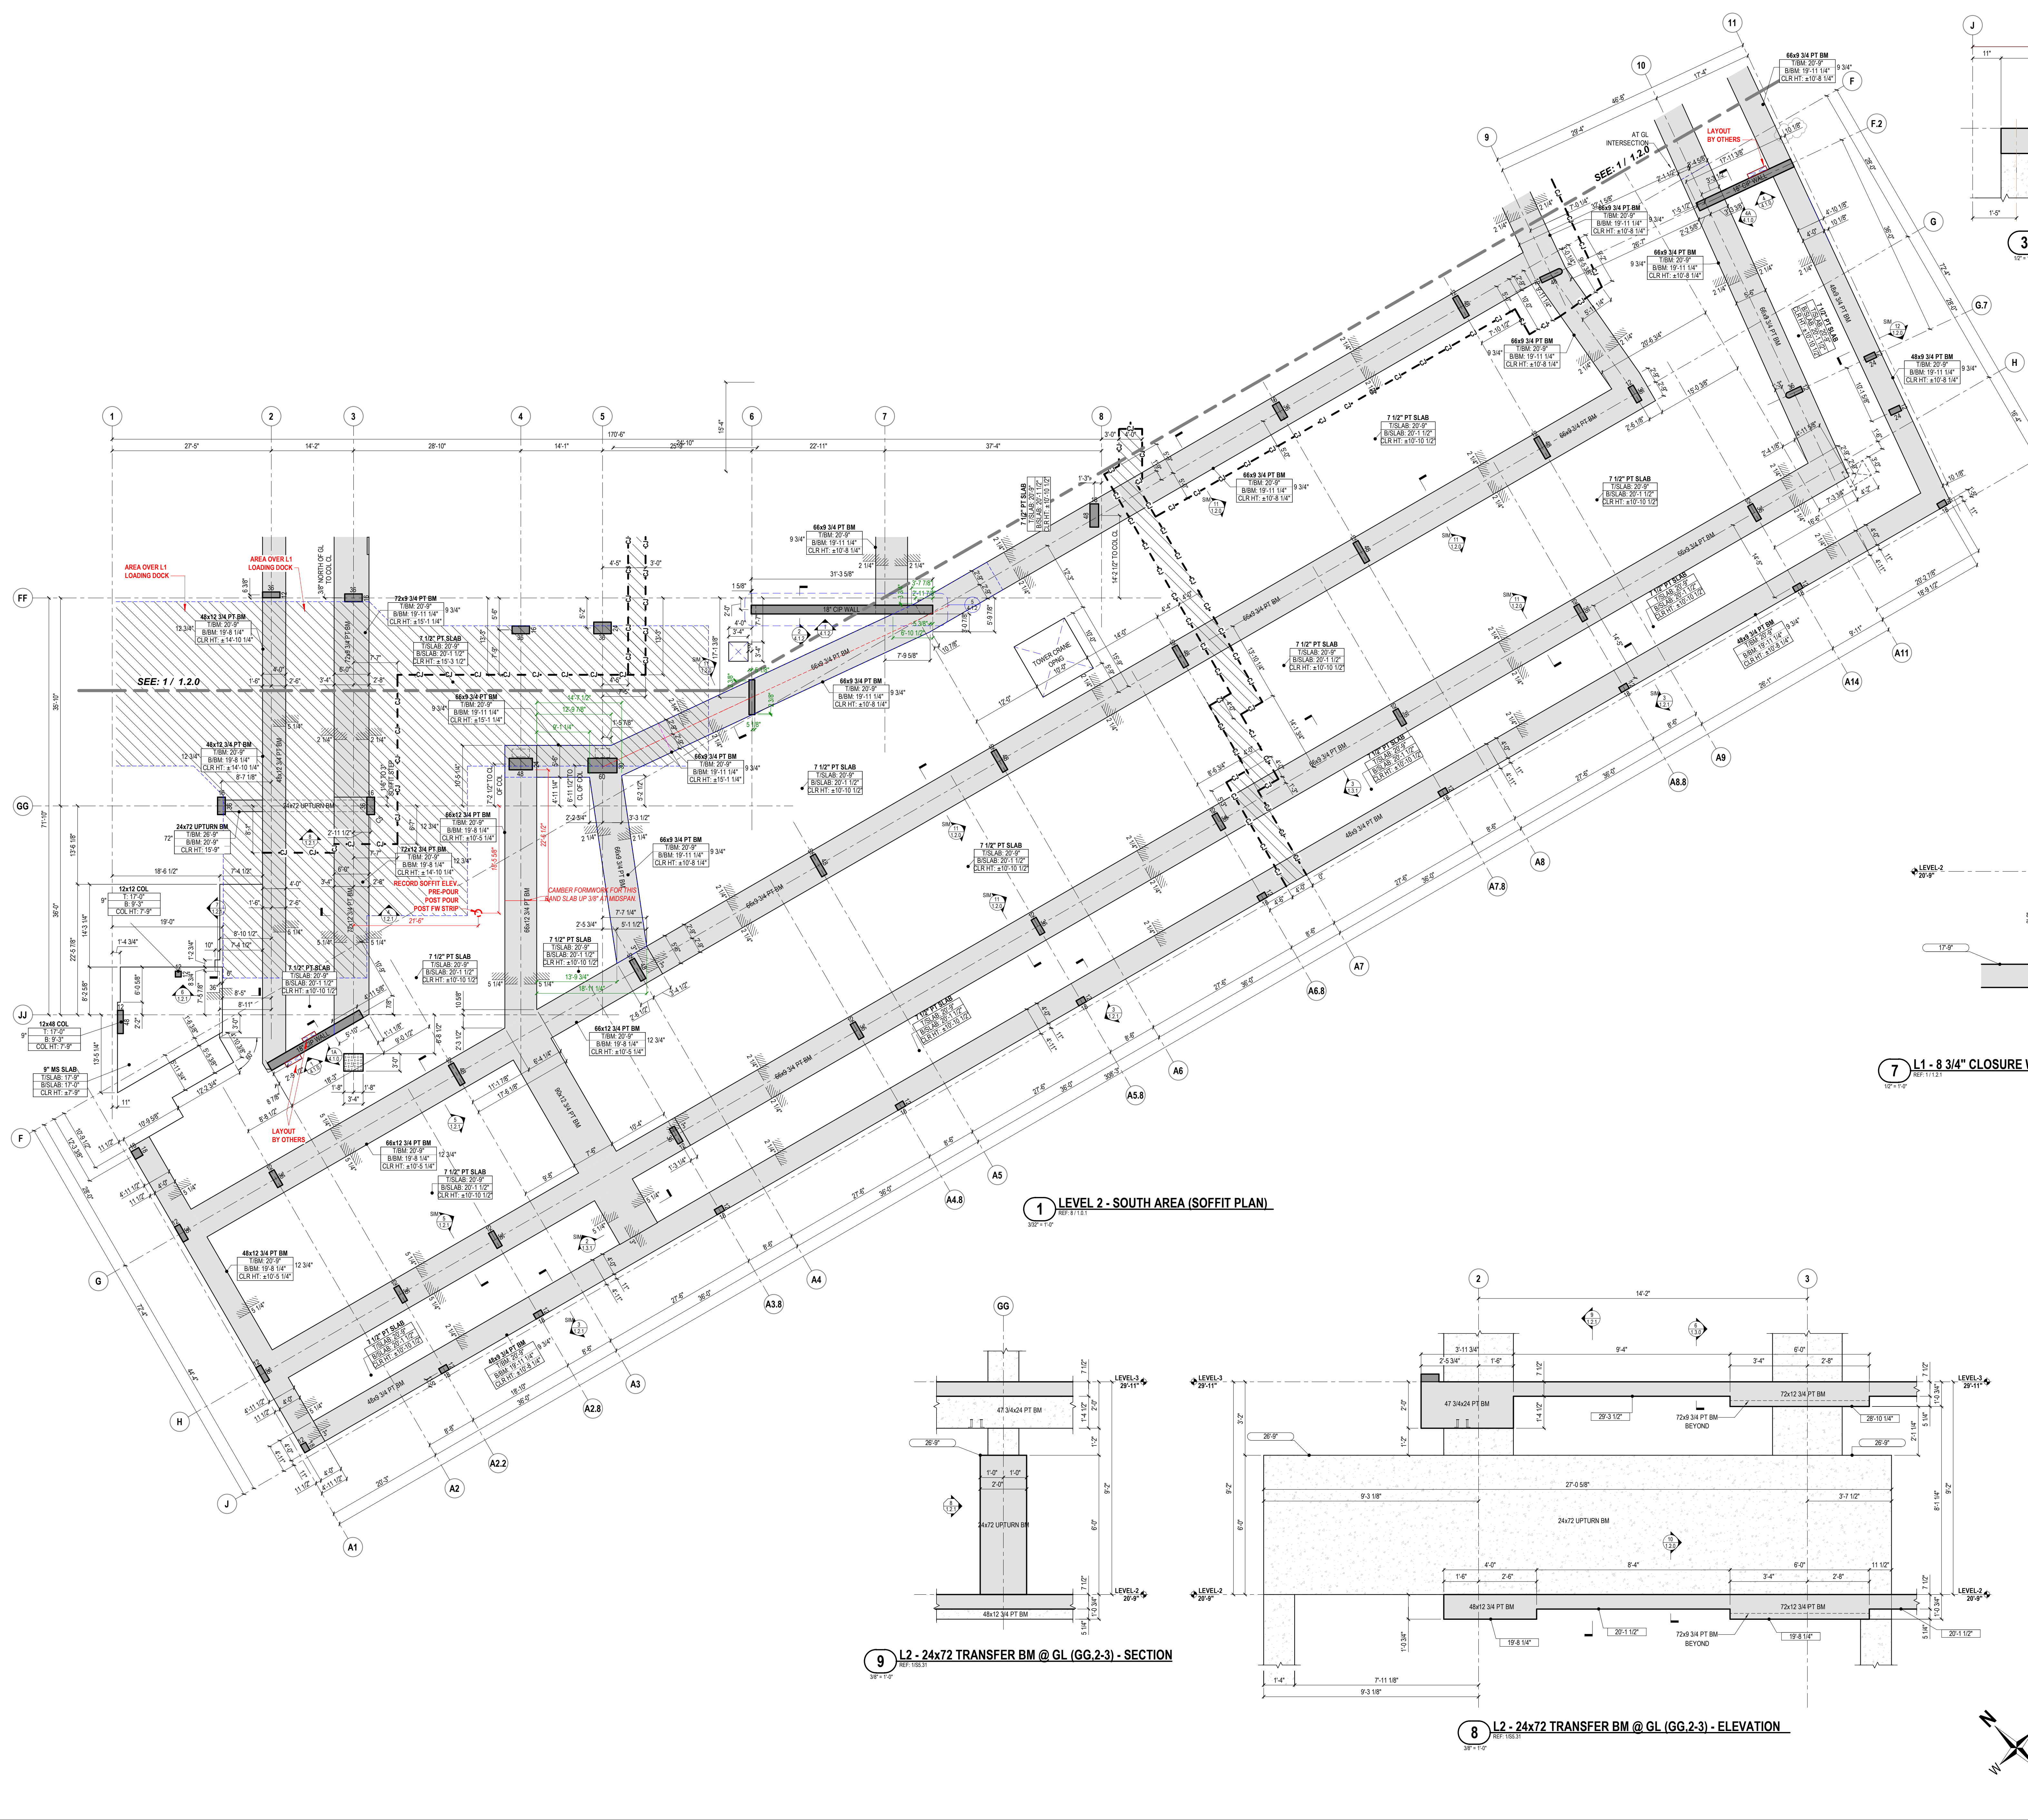


MCCCLONE
CONSTRUCTION
SINCE 1975
2863 MAPLE VALLEY BLVD. SUITE 200
MAPLE VALLEY, WA 98043-1460

LEVEL 2 - SOUTH AREA (SOFFIT PLAN)
KALAE
1000 ALA MOANA BLVD. HONOLULU, HI 96814


DATE: 2026.09.17
SUBMITTAL
As indicated
AG
1268
12.1

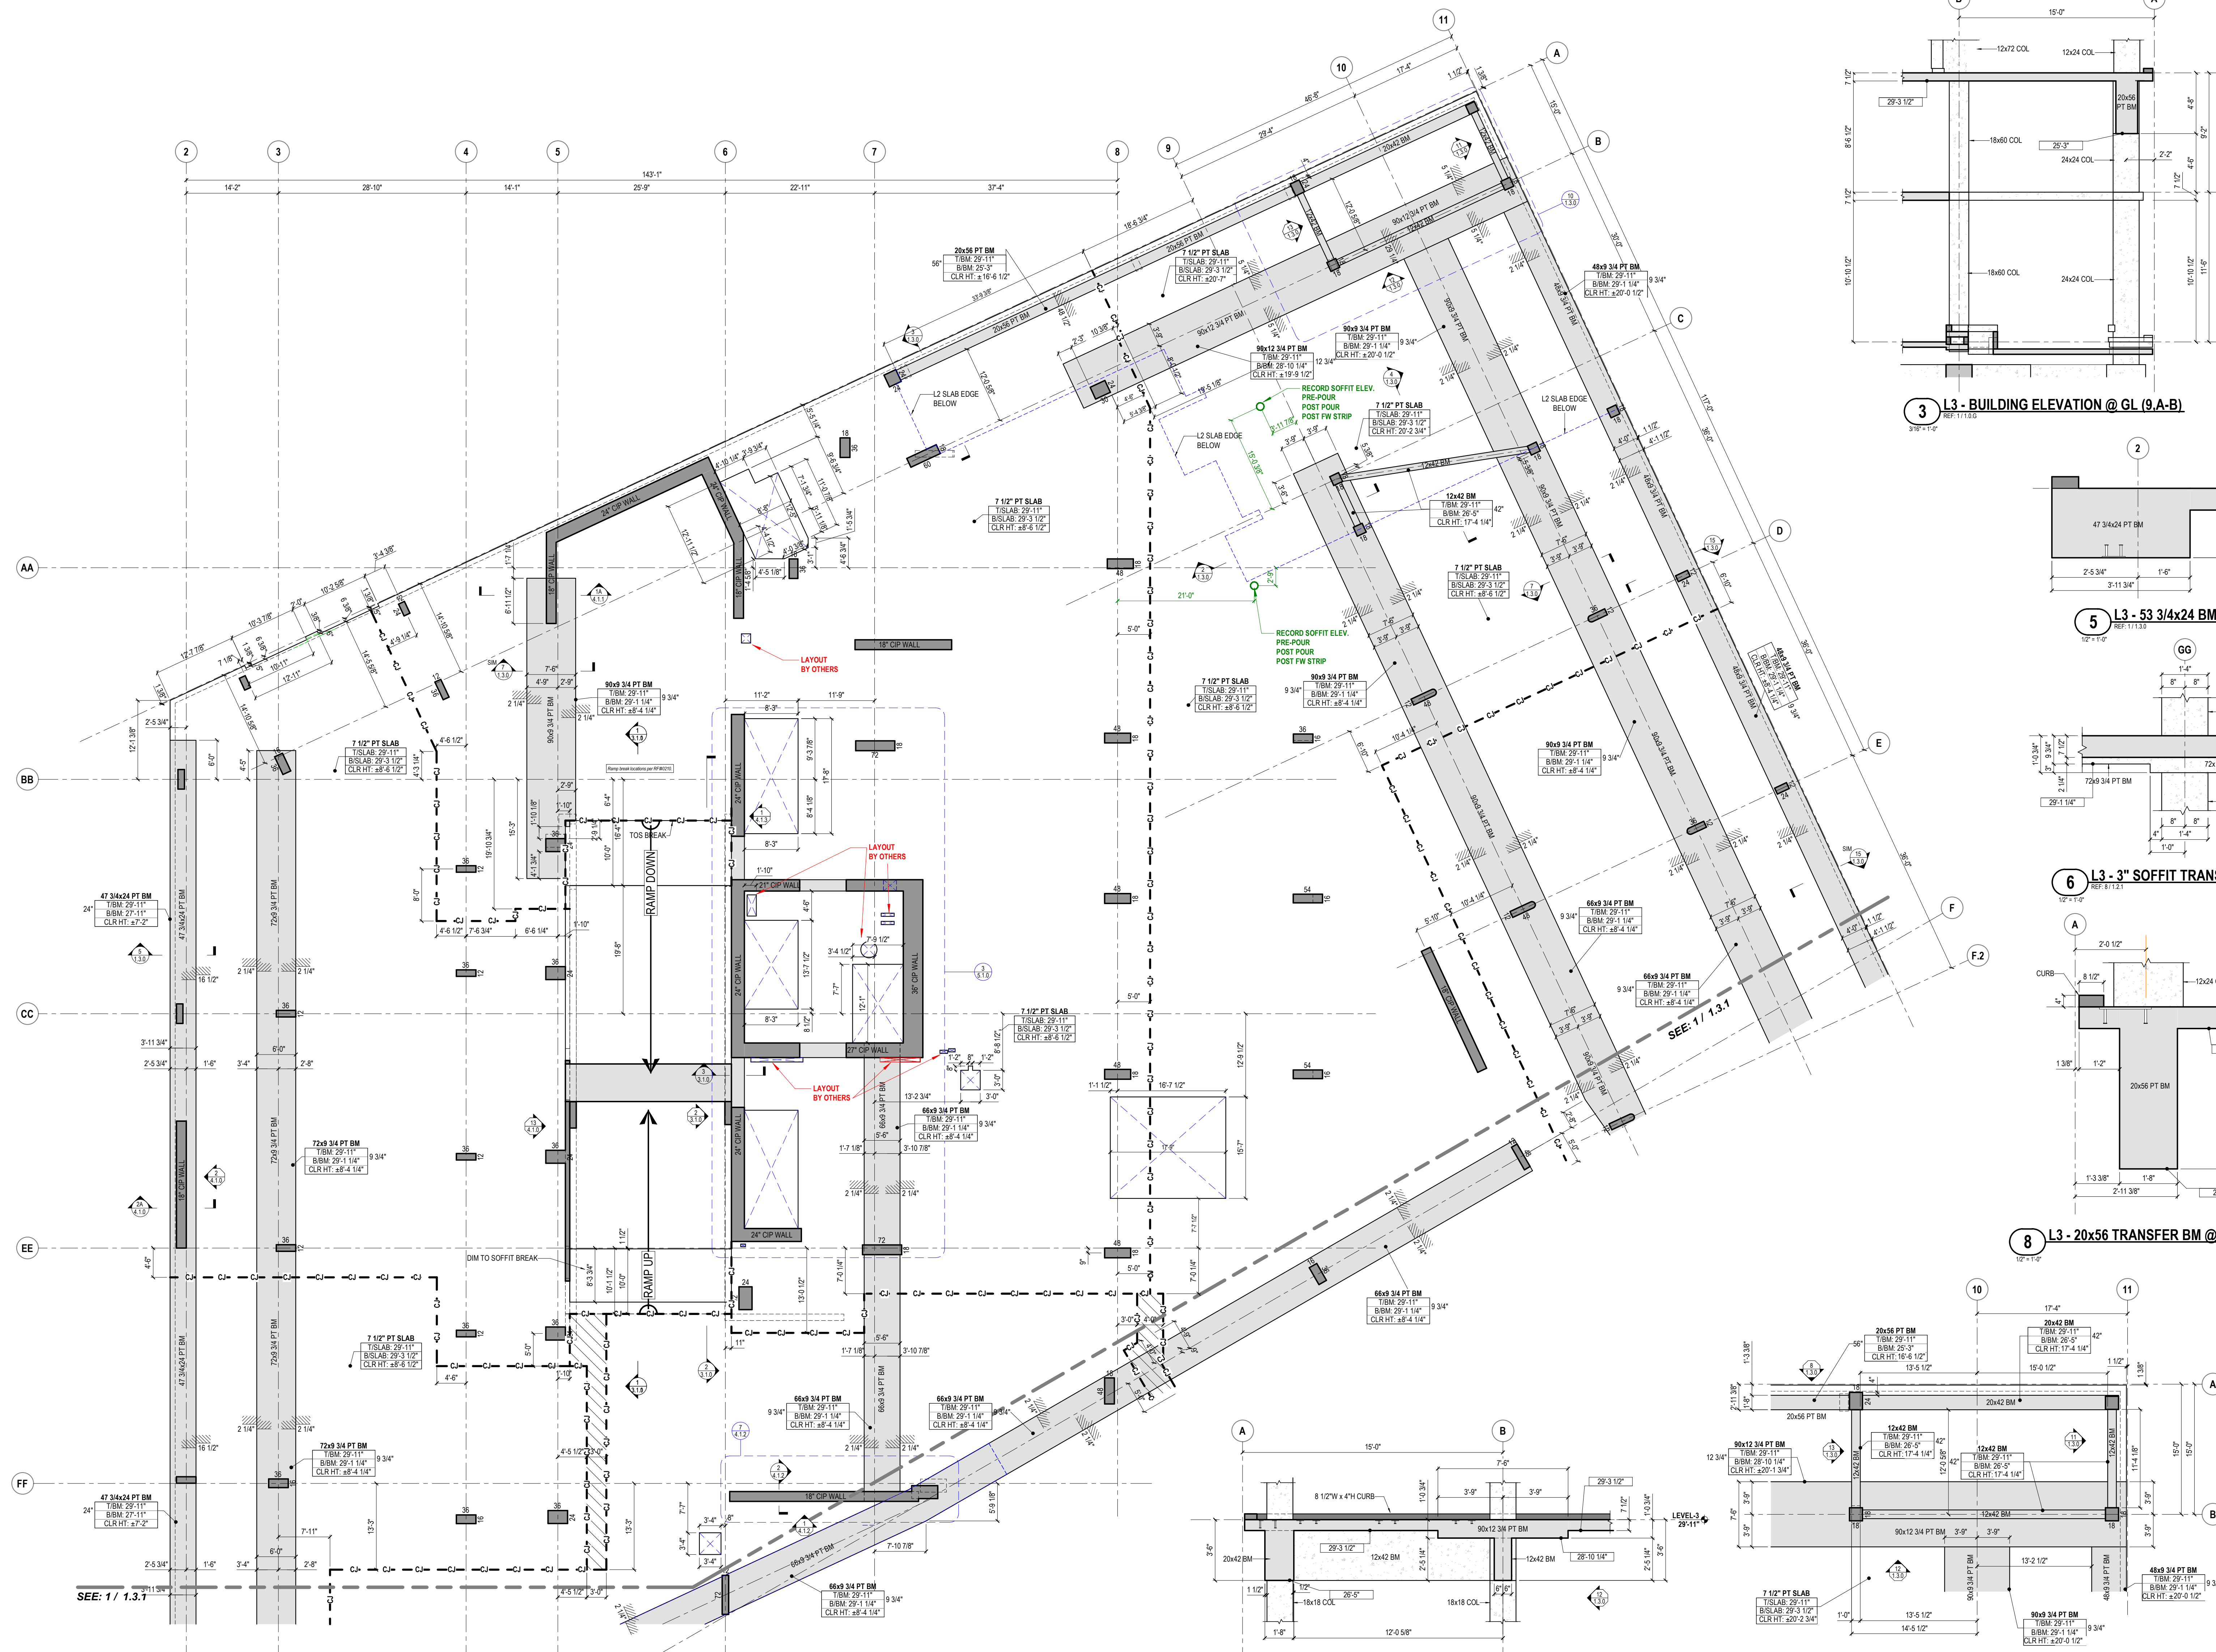

1 LEVEL 3 - NORTH AREA (SOFFIT PLAN)

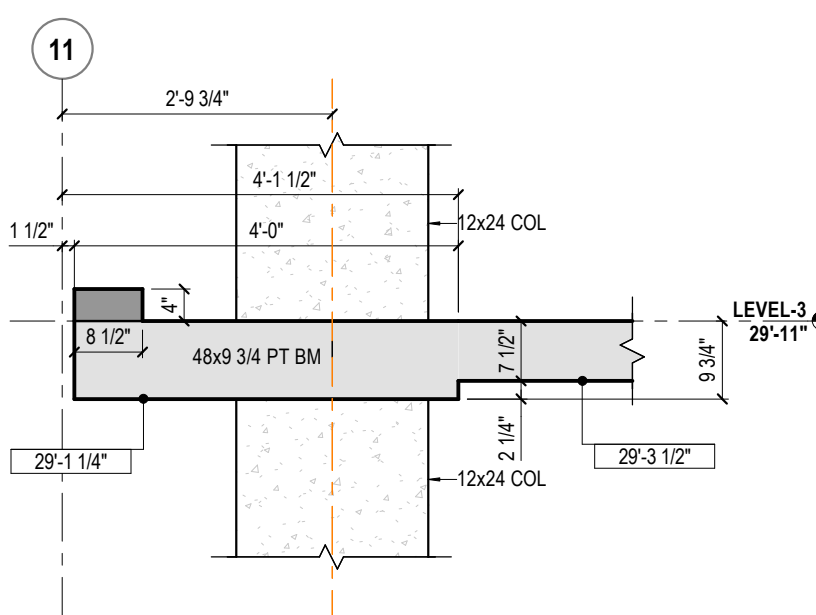


15 L3 - 48x9.75 BM @ GL 11

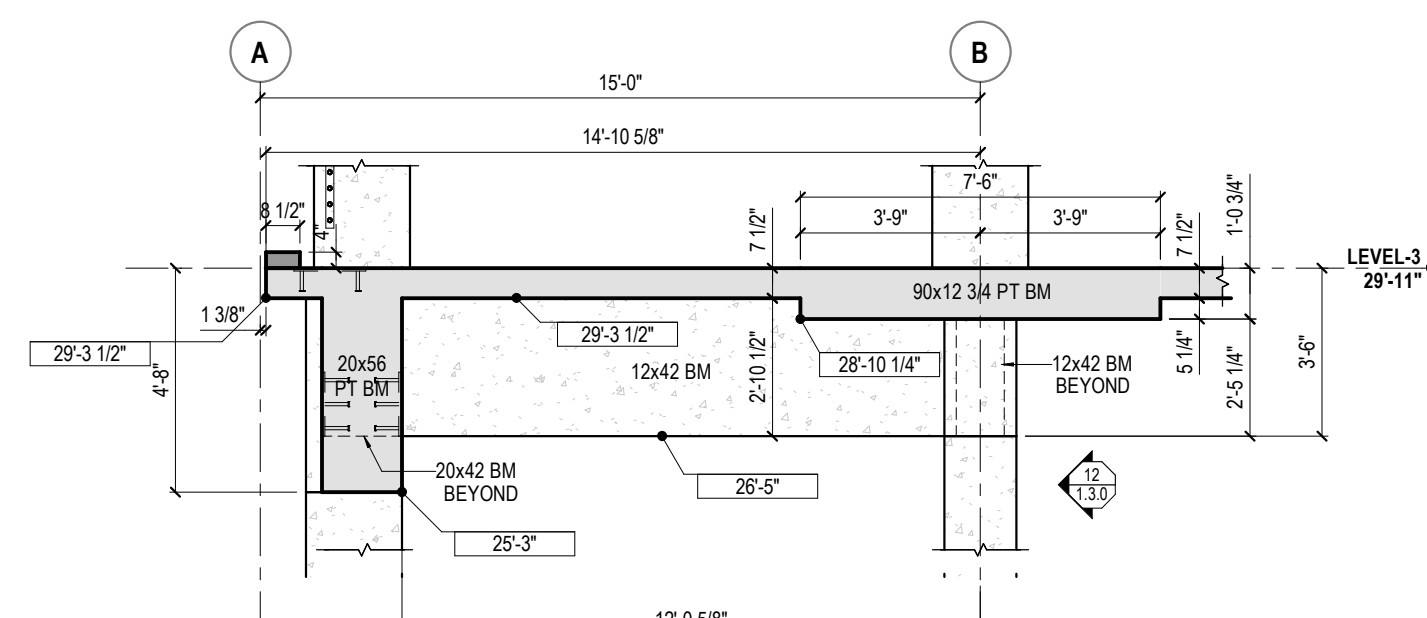


13 **L3 - BEAMS @ GL (10,A-B)**


11 L3 - BEAMS @ GL (11,A-E)

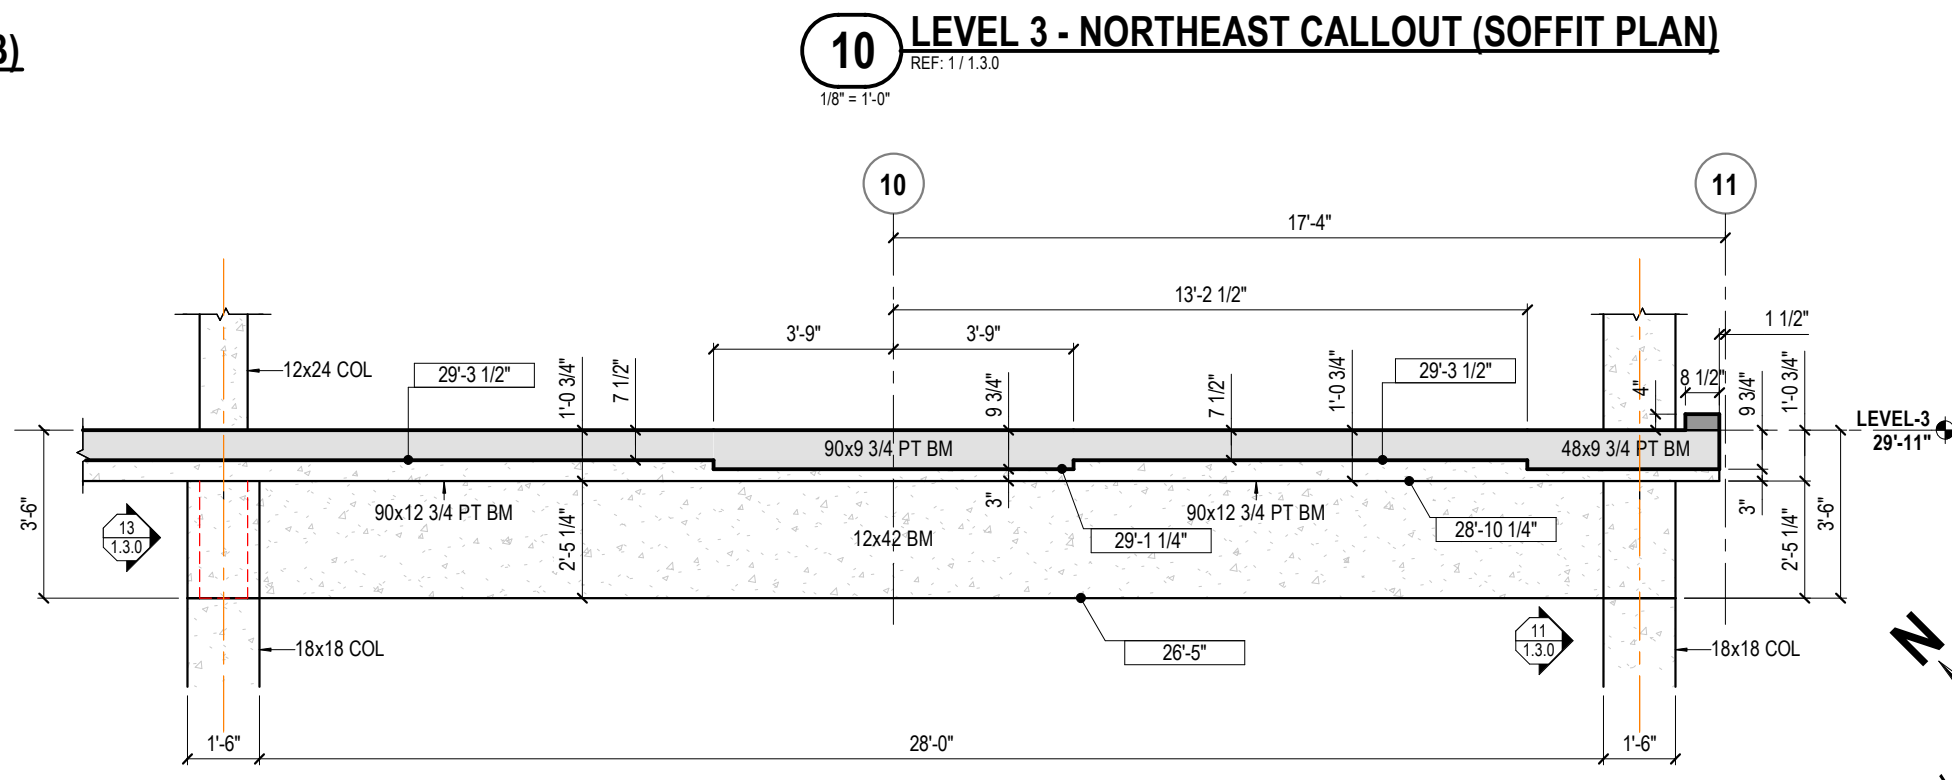


10 **LEVEL 3 - NORTHEAST CALLOUT (SOFFIT PLAN)**
REF: 1/13.0

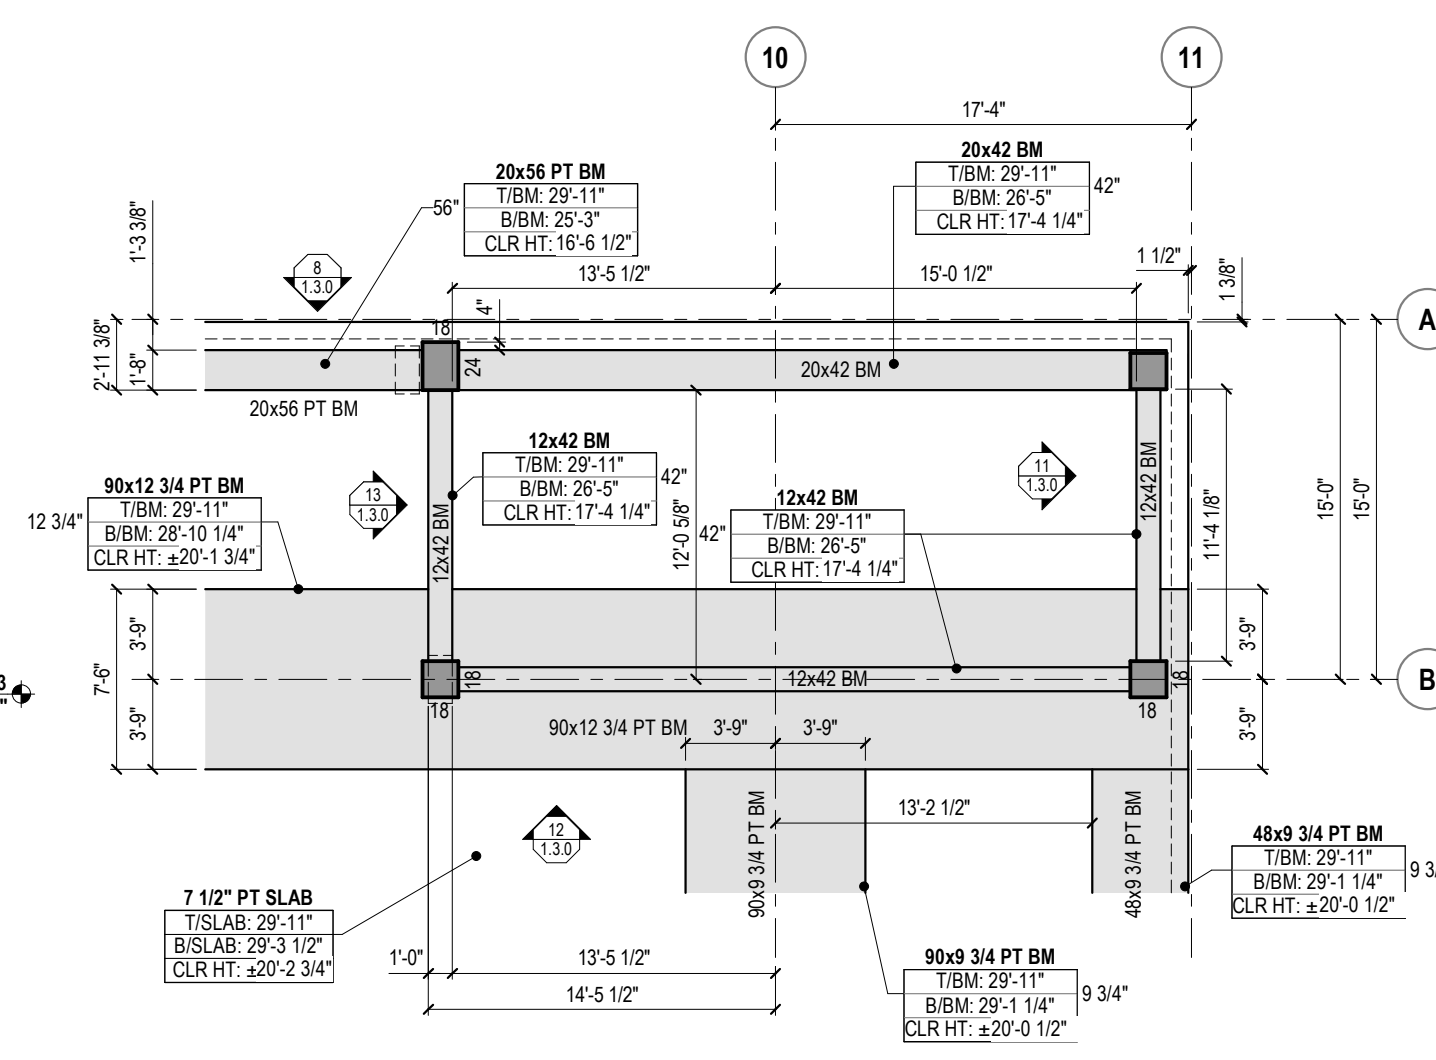


8 L3 - 20x56 TRANSFER BM @ GL (A.9) - SECTION

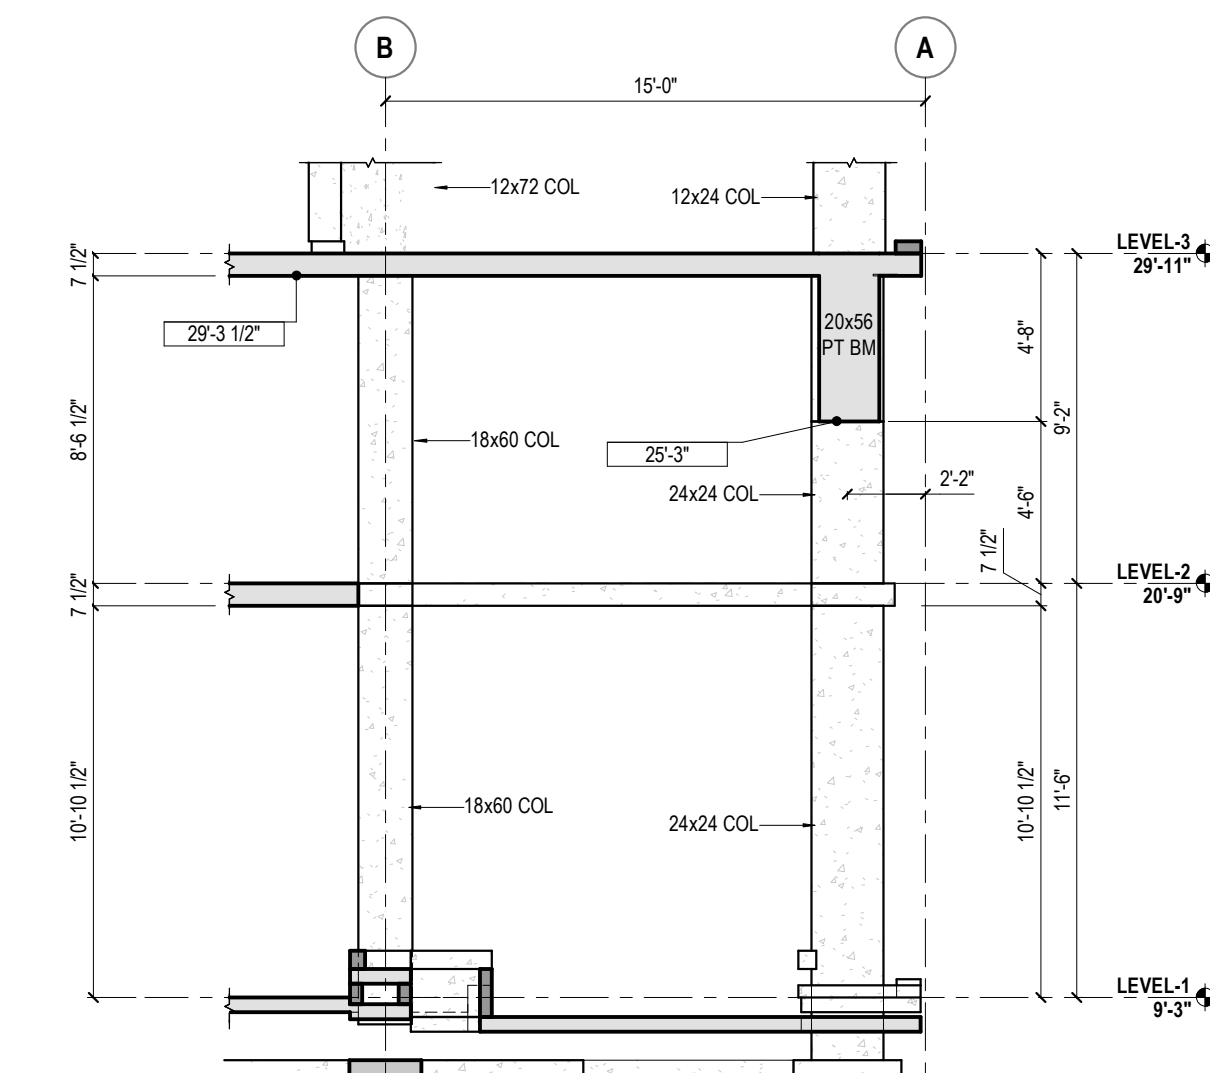


3 L3 - BUILDING ELEVATION @ GL (9,A-B)

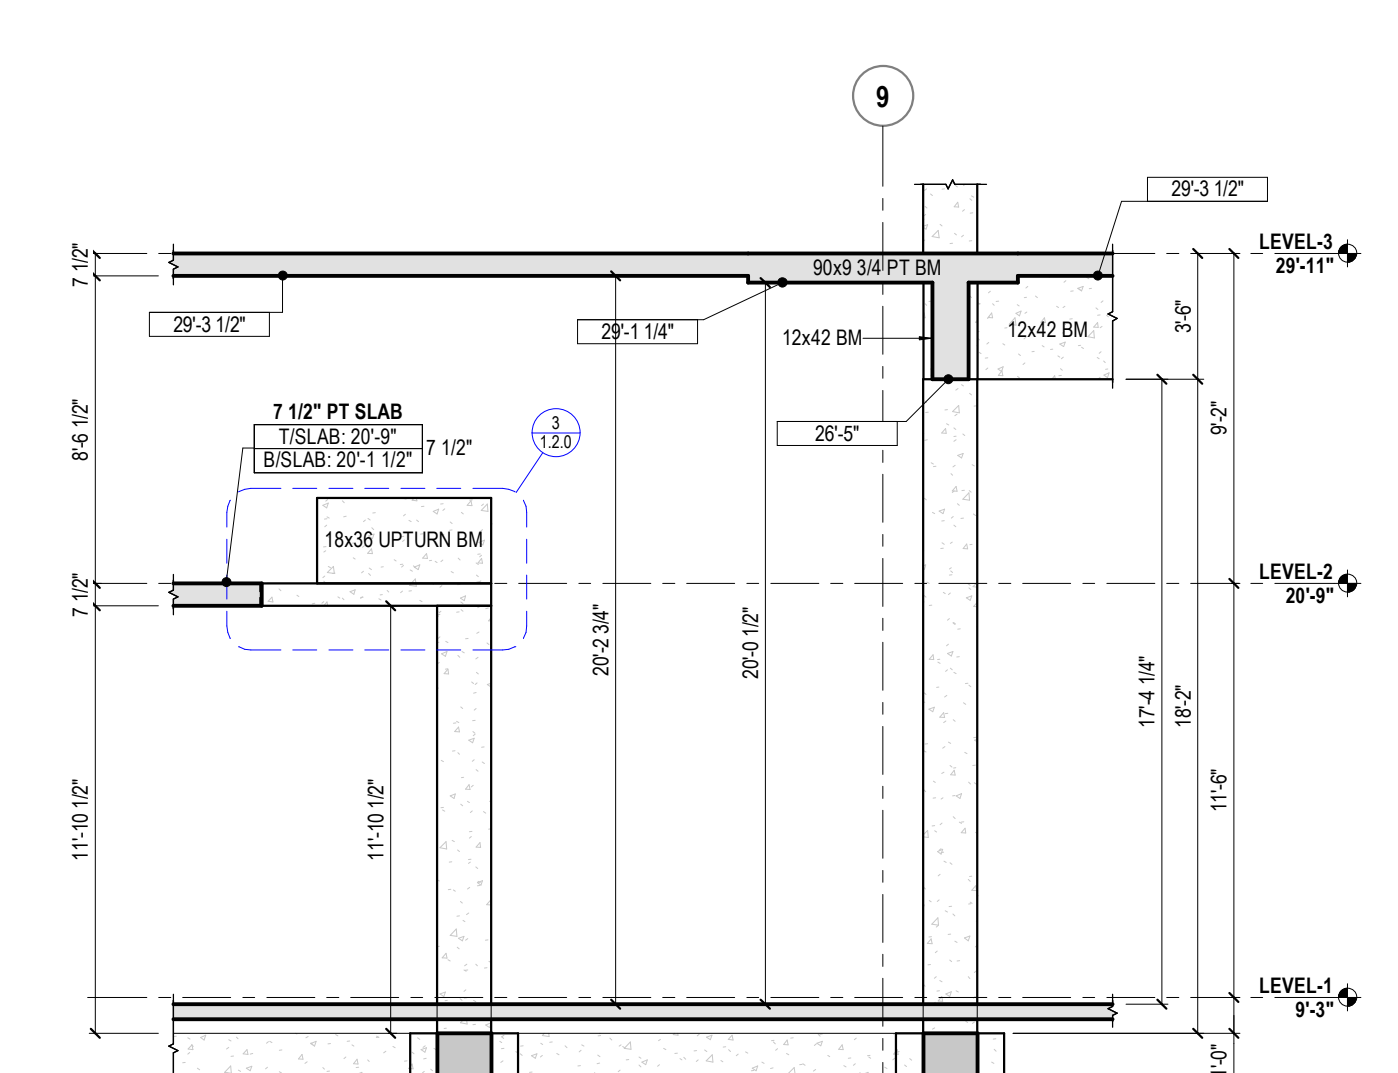


2 L3 - BUILDING ELEVATION @ GL (9,C)

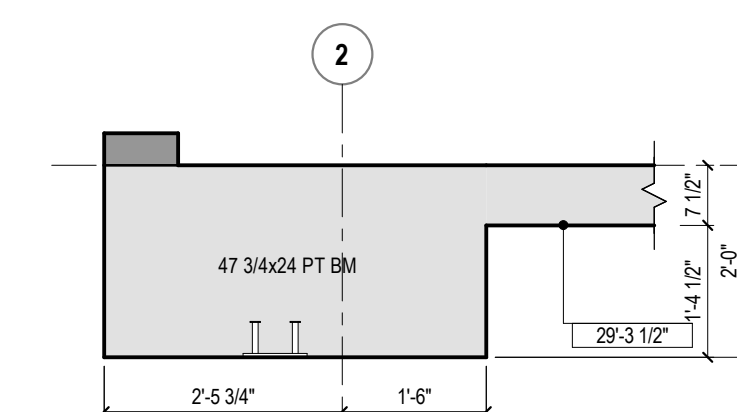


5 L3 - 53 3/4x24 BM ALONG GL 2

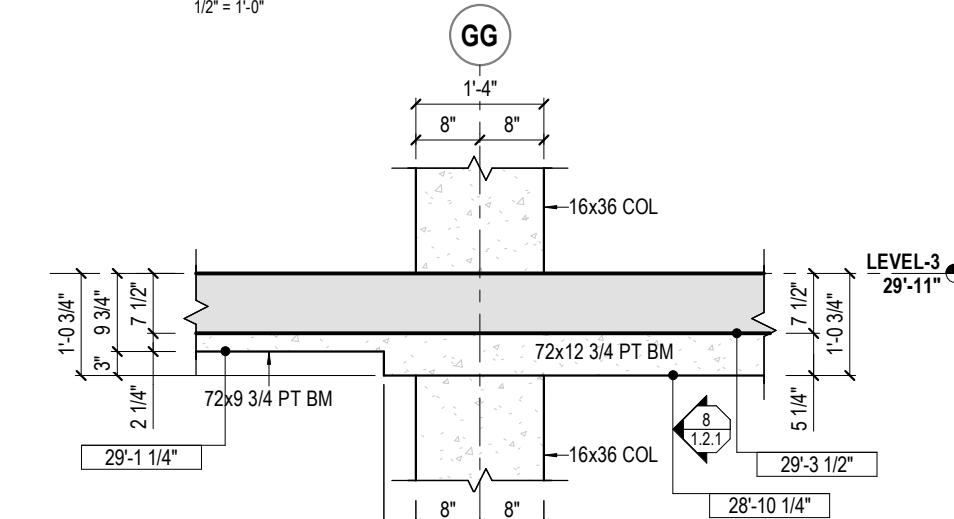


6 L3 - 3" SOFFIT TRANSITION @ GL (3,GG)

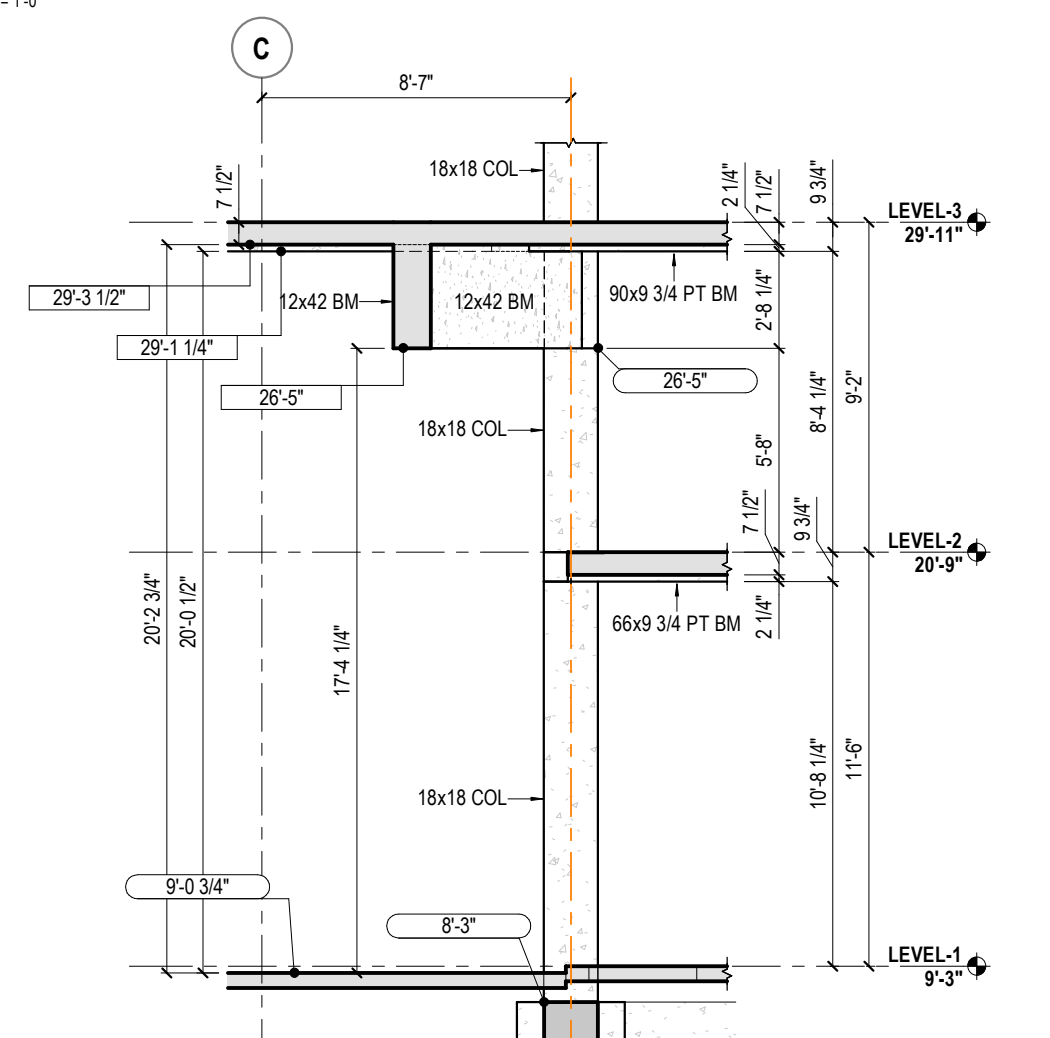


4 L3 - BUILDING ELEVATION @ GL (9-10,C)

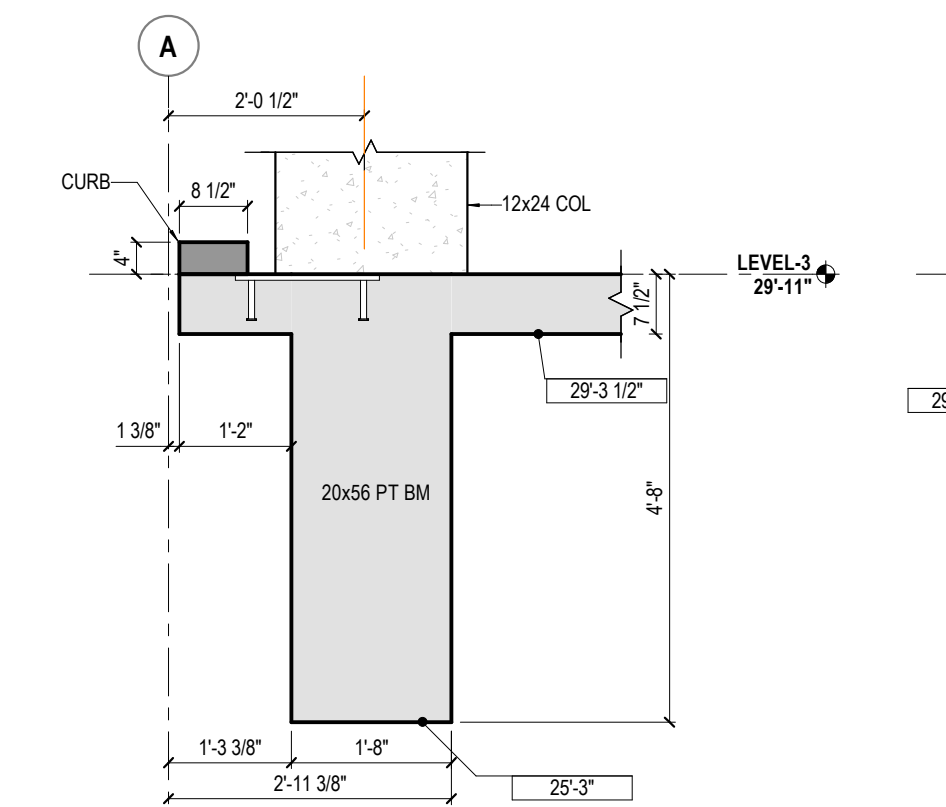

8 L3 - 20x56 TRANSFER BM @ GL (A.9) - SECTION

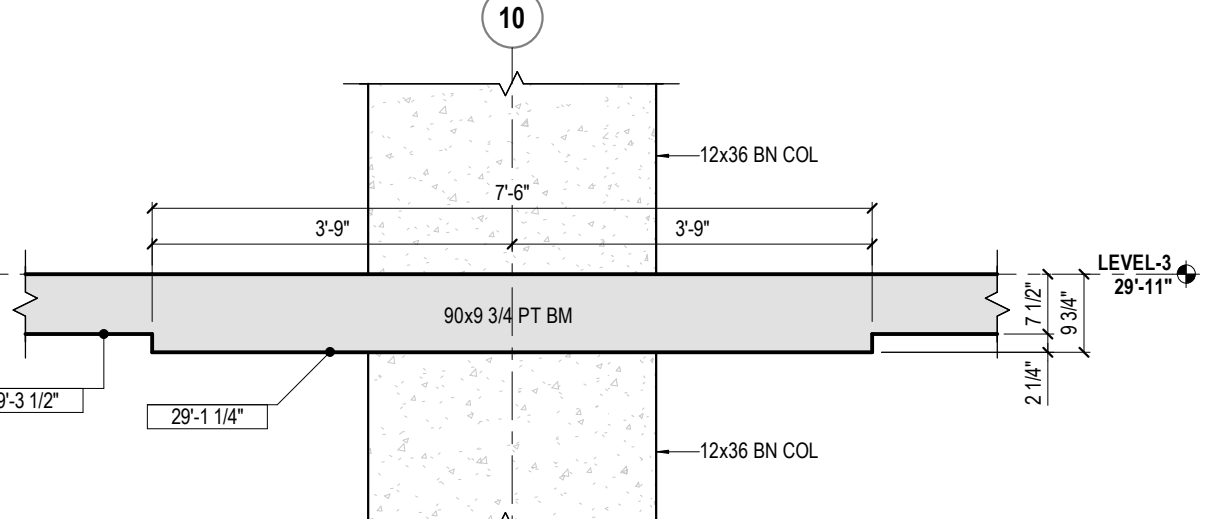


7 L3 - 90x9.75 BM @ GL 10

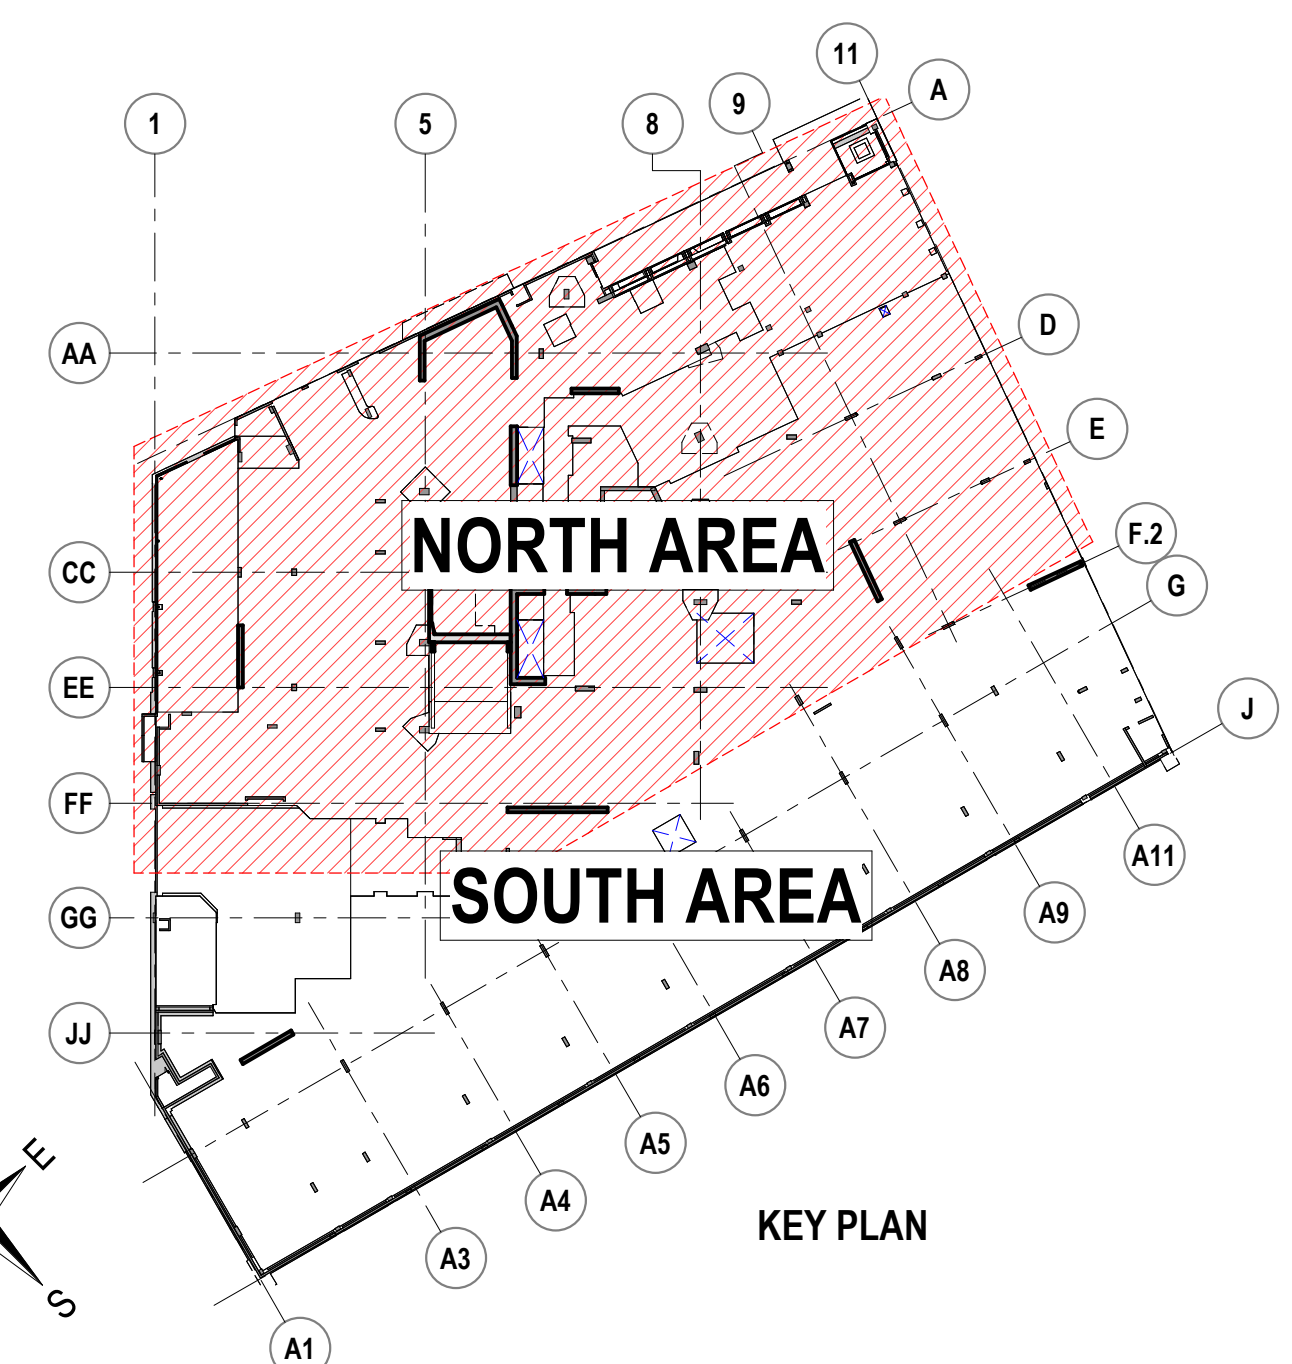





THIS DRAWING IS FOR THE EXCLUSIVE USE OF MCCLONE CONSTRUCTION COMPANY, INC. ON THE PROJECT ONLY. UTILIZATION OF THIS DRAWING BY OTHER PARTIES WITHOUT THE EXPRESSED WRITTEN CONSENT OF MCCLONE CONSTRUCTION COMPANY IS STRICTLY PROHIBITED.

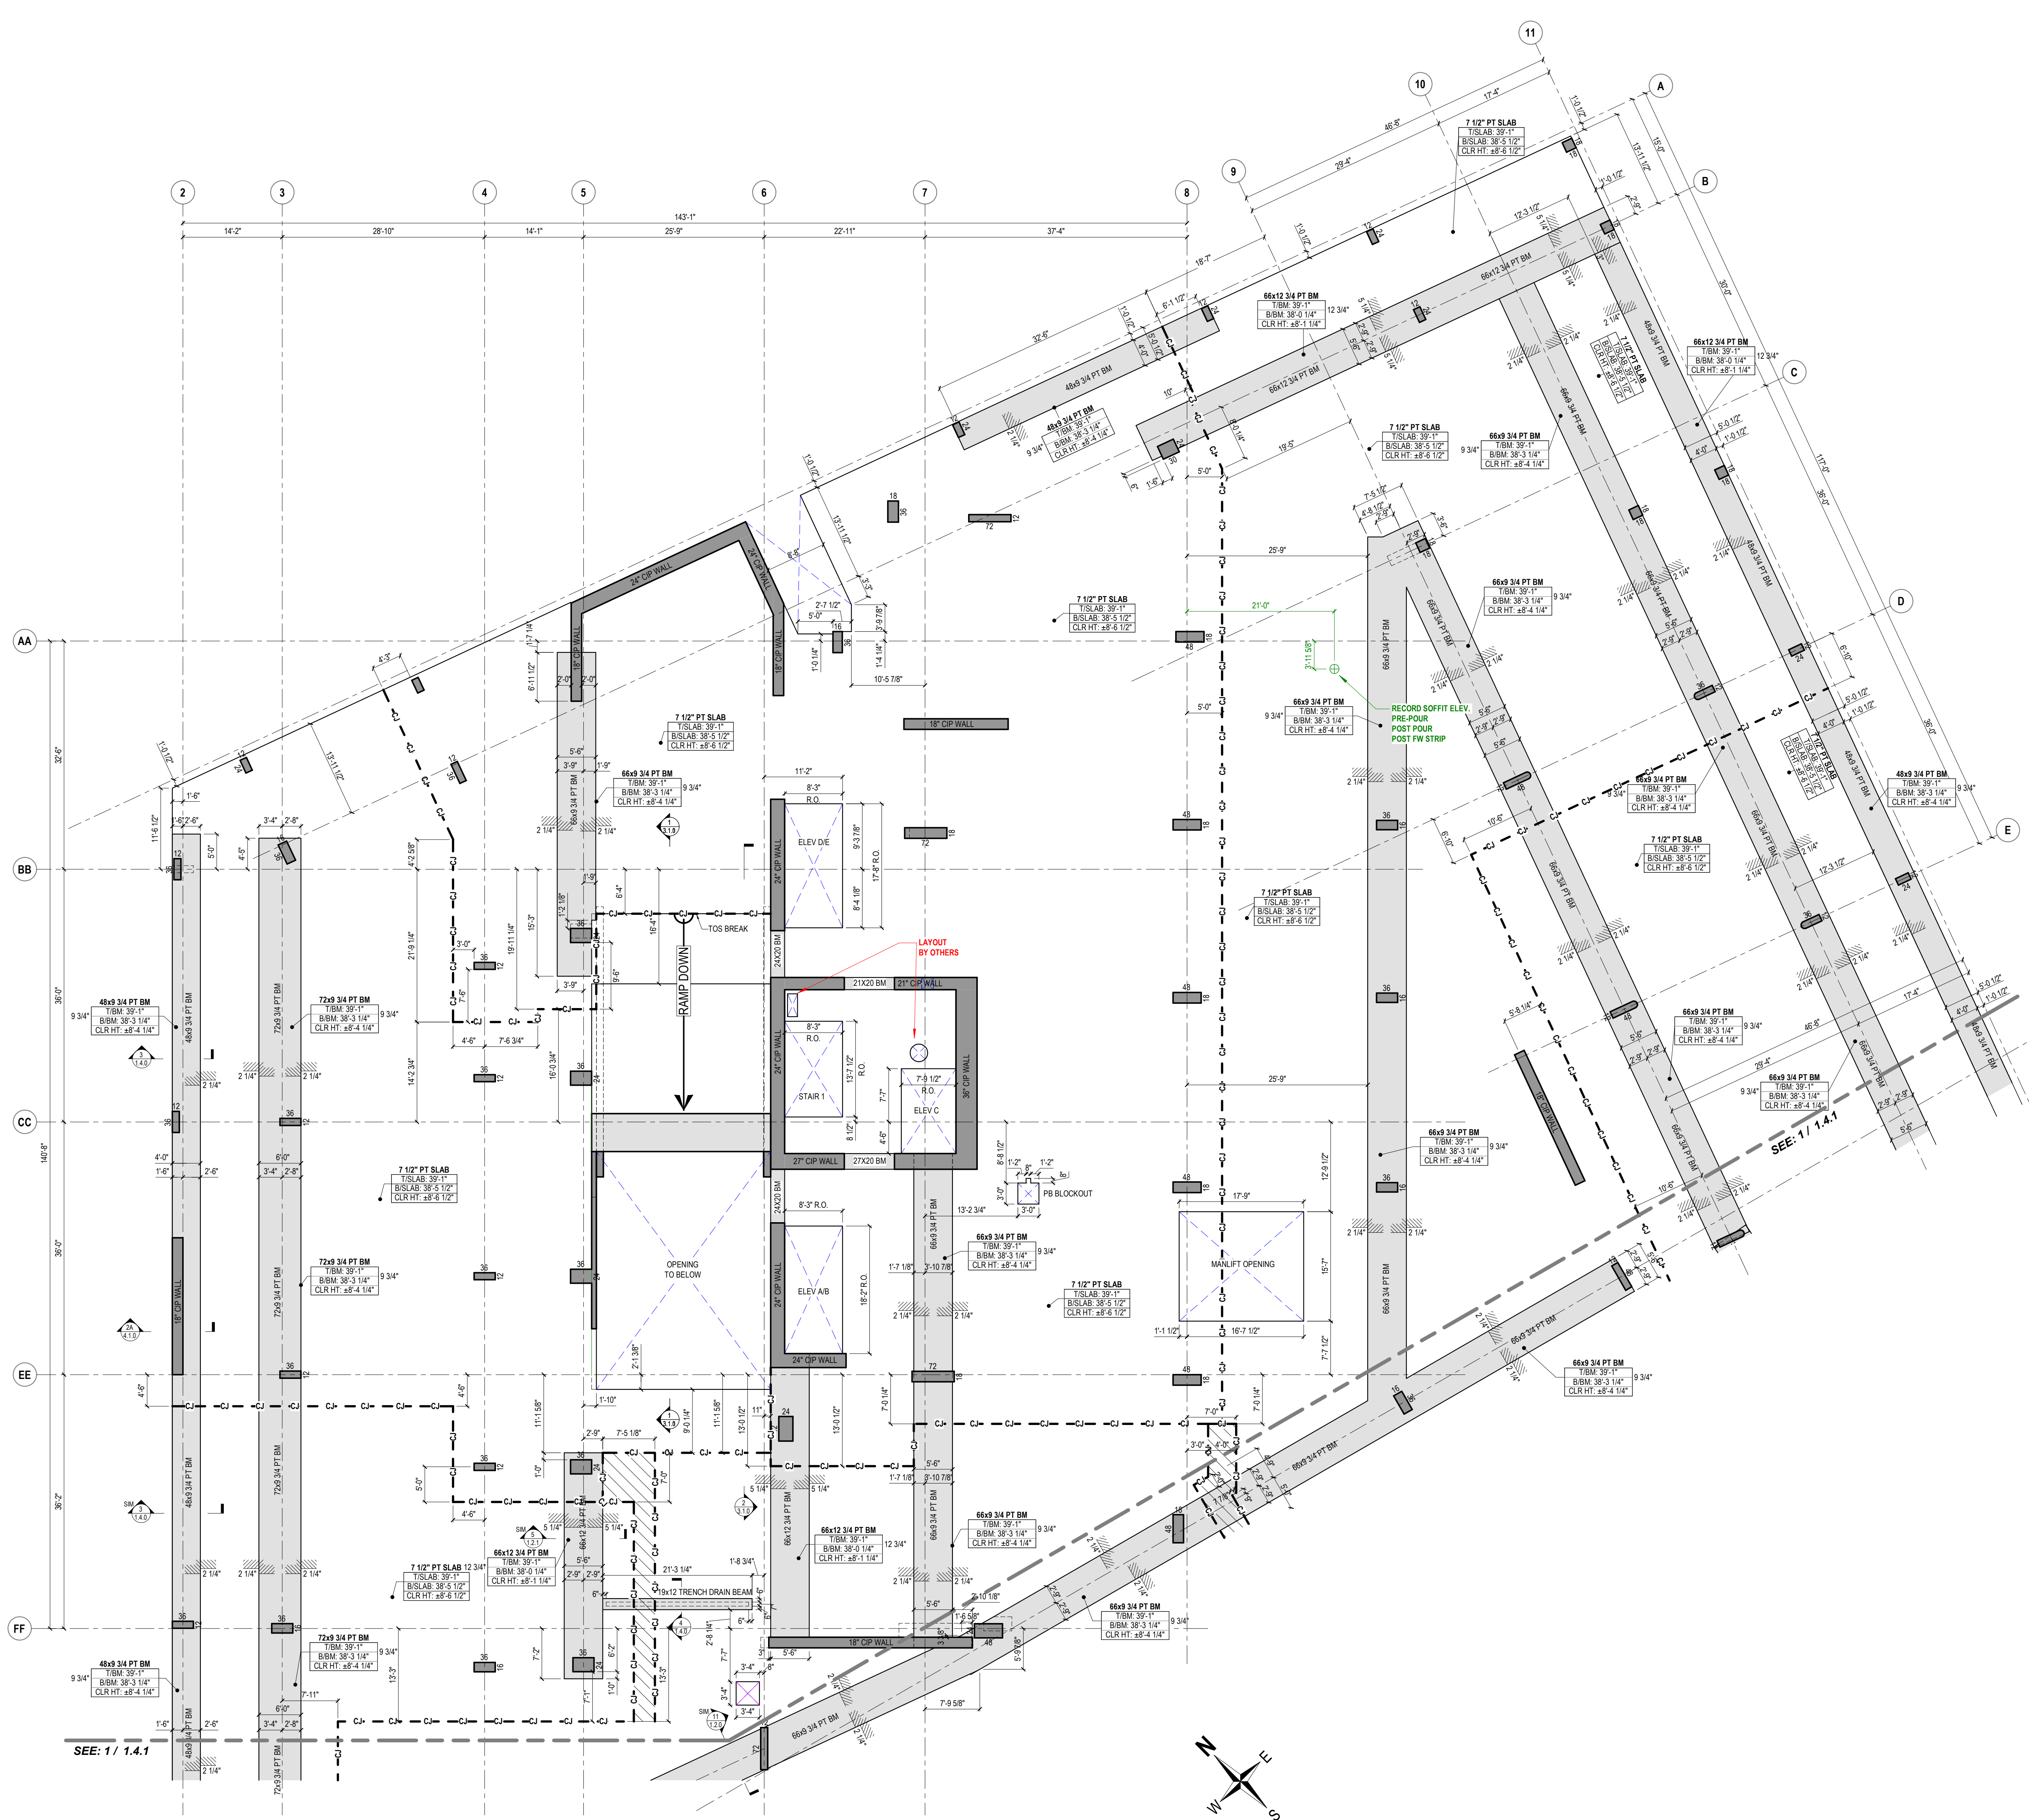


1 LEVEL 4 - NORTH AREA (SOFFIT PLAN)
REF: 21.135

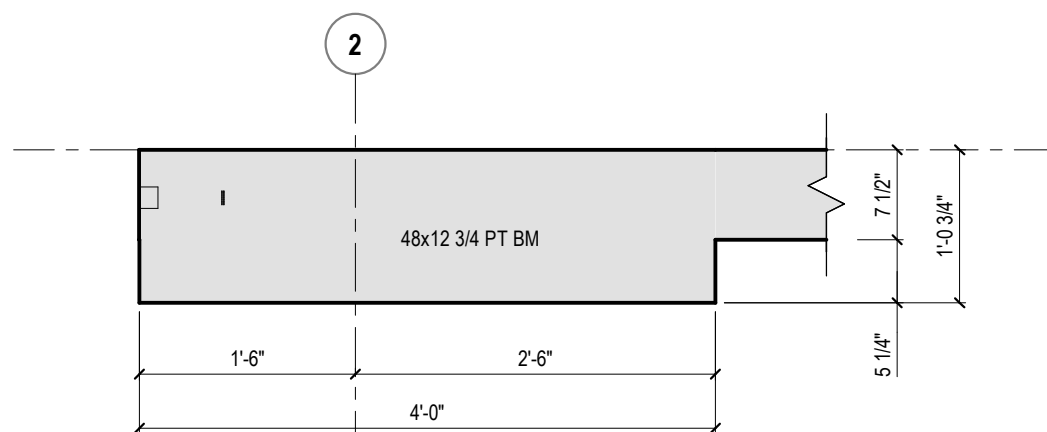


2 L4 - 48x12.75 BM ALONG GL 1
REF: 11.110

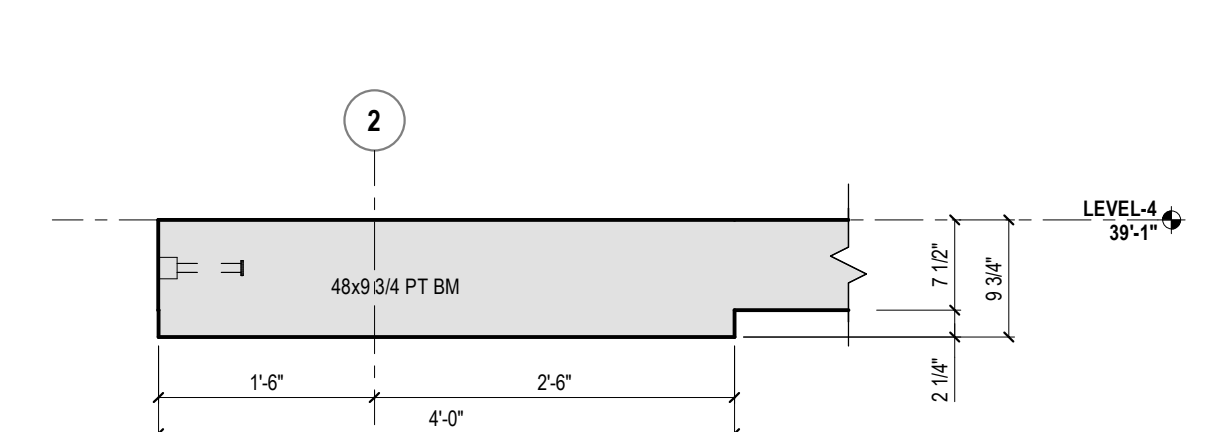

3 L4 - 48x9.75 BM ALONG GL 1
REF: 11.110

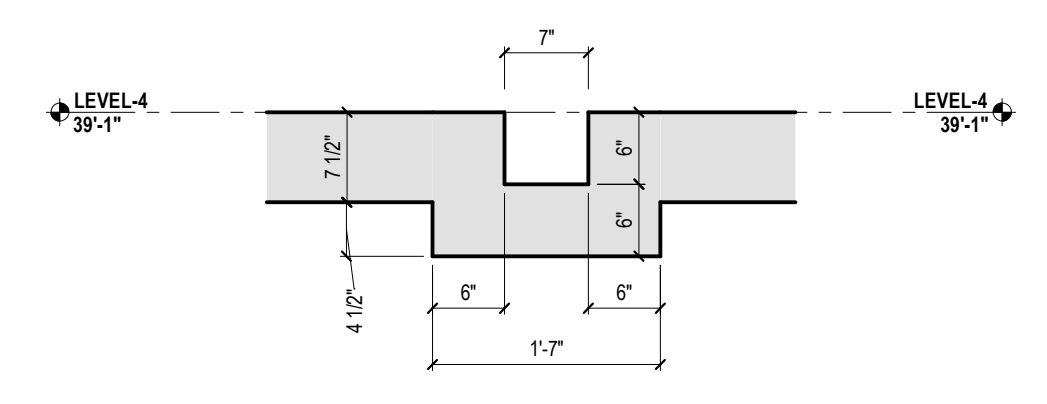

4 SECTION AT TRENCH DRAIN
REF: 11.110

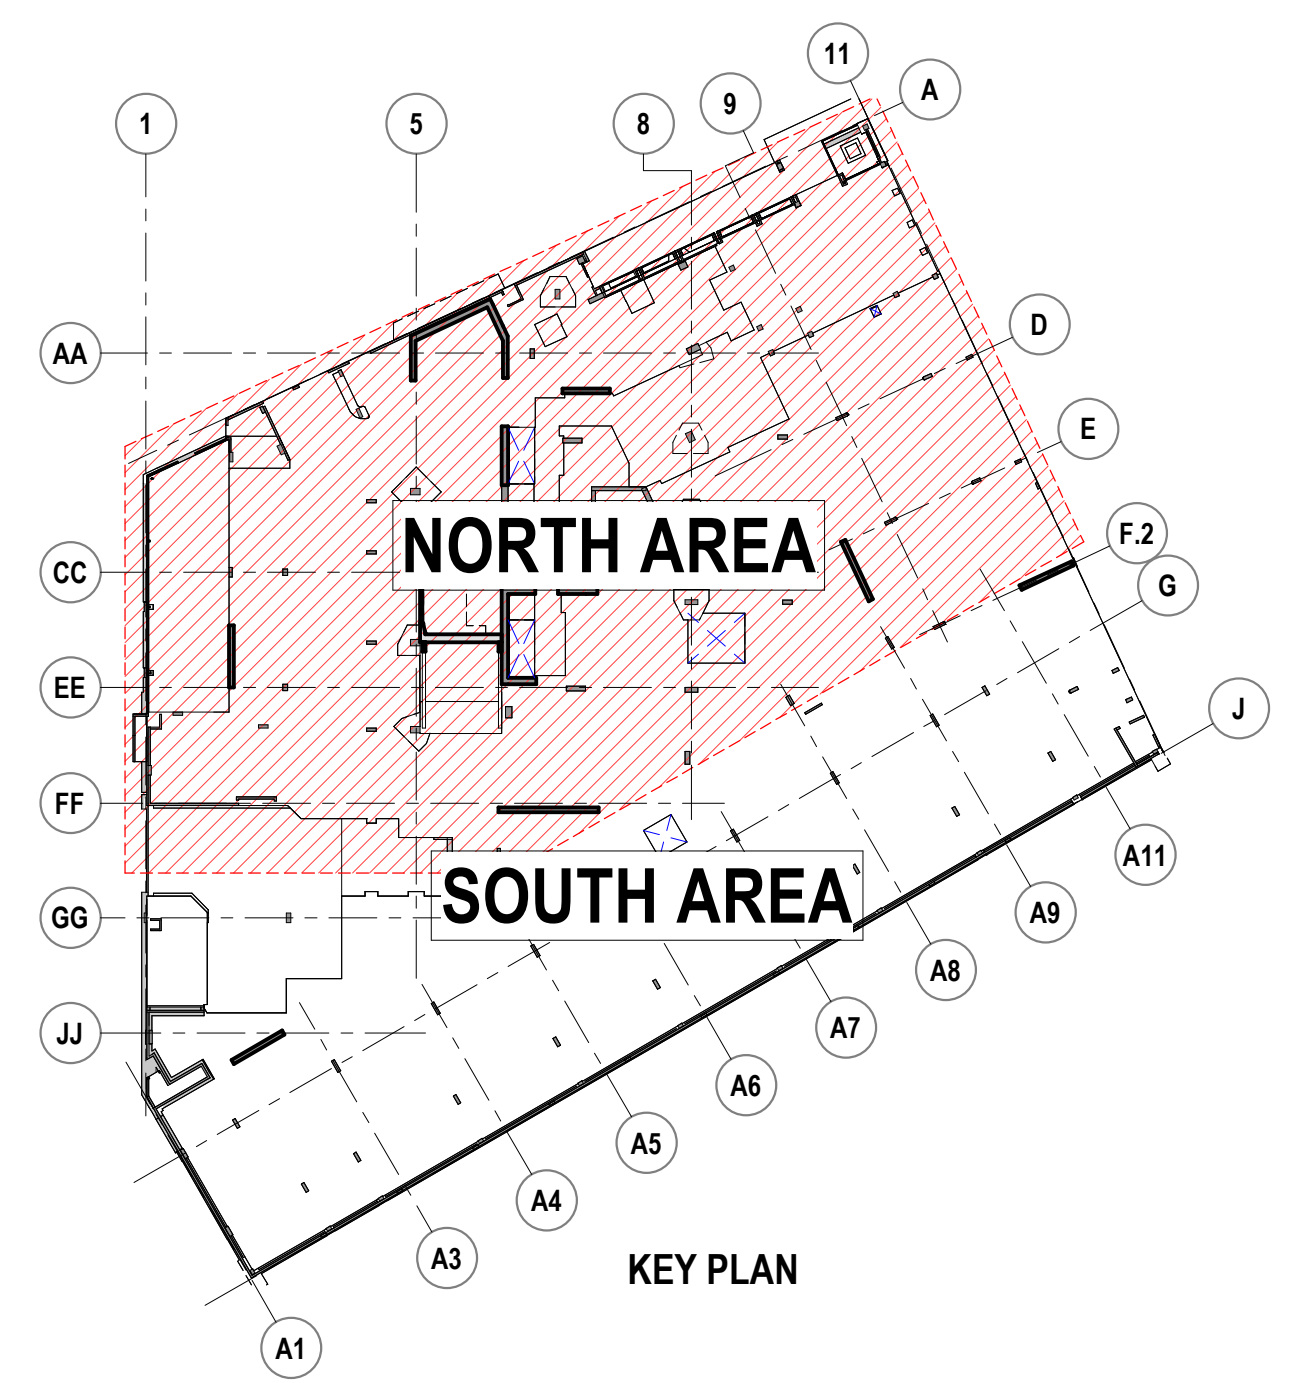

KEY PLAN

McCLONE
CONSTRUCTION
SINCE 1975

2865 MAPLE VALLEY BLVD. SUITE 200
MAPLE VALLEY, WA 98043 • (425) 413-1460

LEVEL 4 - NORTH AREA (SOFFIT PLAN)

KALAE

1000 ALA MOANA BLVD. HONOLULU, HI 96814

DATE: 2026.07.01

STATUS: SUBMITTAL


SCALE: As indicated

REVISION: AG

DATE: 12/28


REVISION: 1.4.0



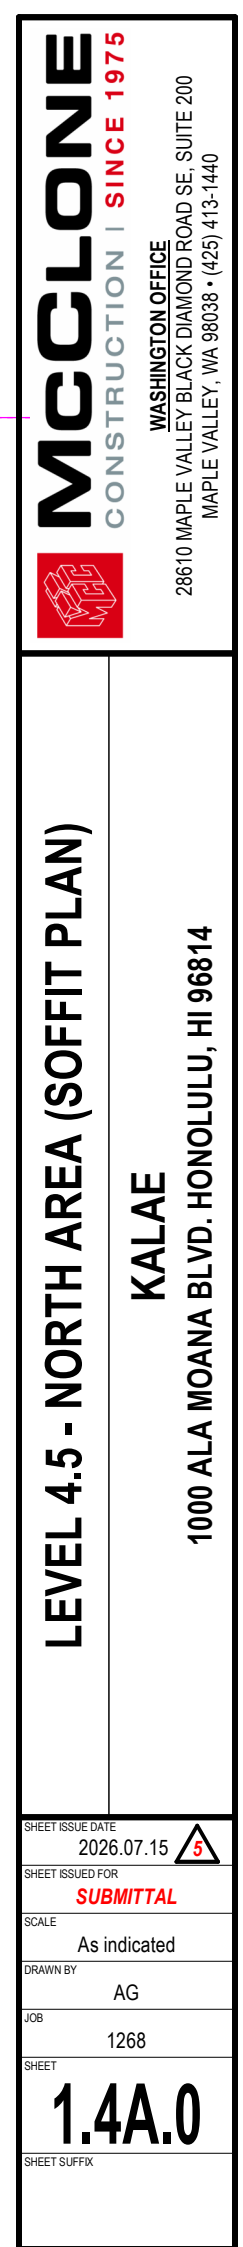

THIS DRAWING IS FOR THE EXCLUSIVE USE OF MCCLONE CONSTRUCTION COMPANY. ON THE PROJECT ONLY. UTILIZATION OF THIS DRAWING BY OTHER PARTIES WITHOUT THE EXPRESSED WRITTEN CONSENT OF MCCLONE CONSTRUCTION COMPANY IS STRICTLY PROHIBITED.


PLAT DATE TIME STAMP: 2026.07.01 10:46:27 AM
DRAWN BY: J. KALAE
CHECKED BY: J. KALAE
DATE: 2026.07.01
SCALE: AS SHOWN
SHEET: 14A.1
PROJECT: 30X42 ORIGINAL SHEET SIZE

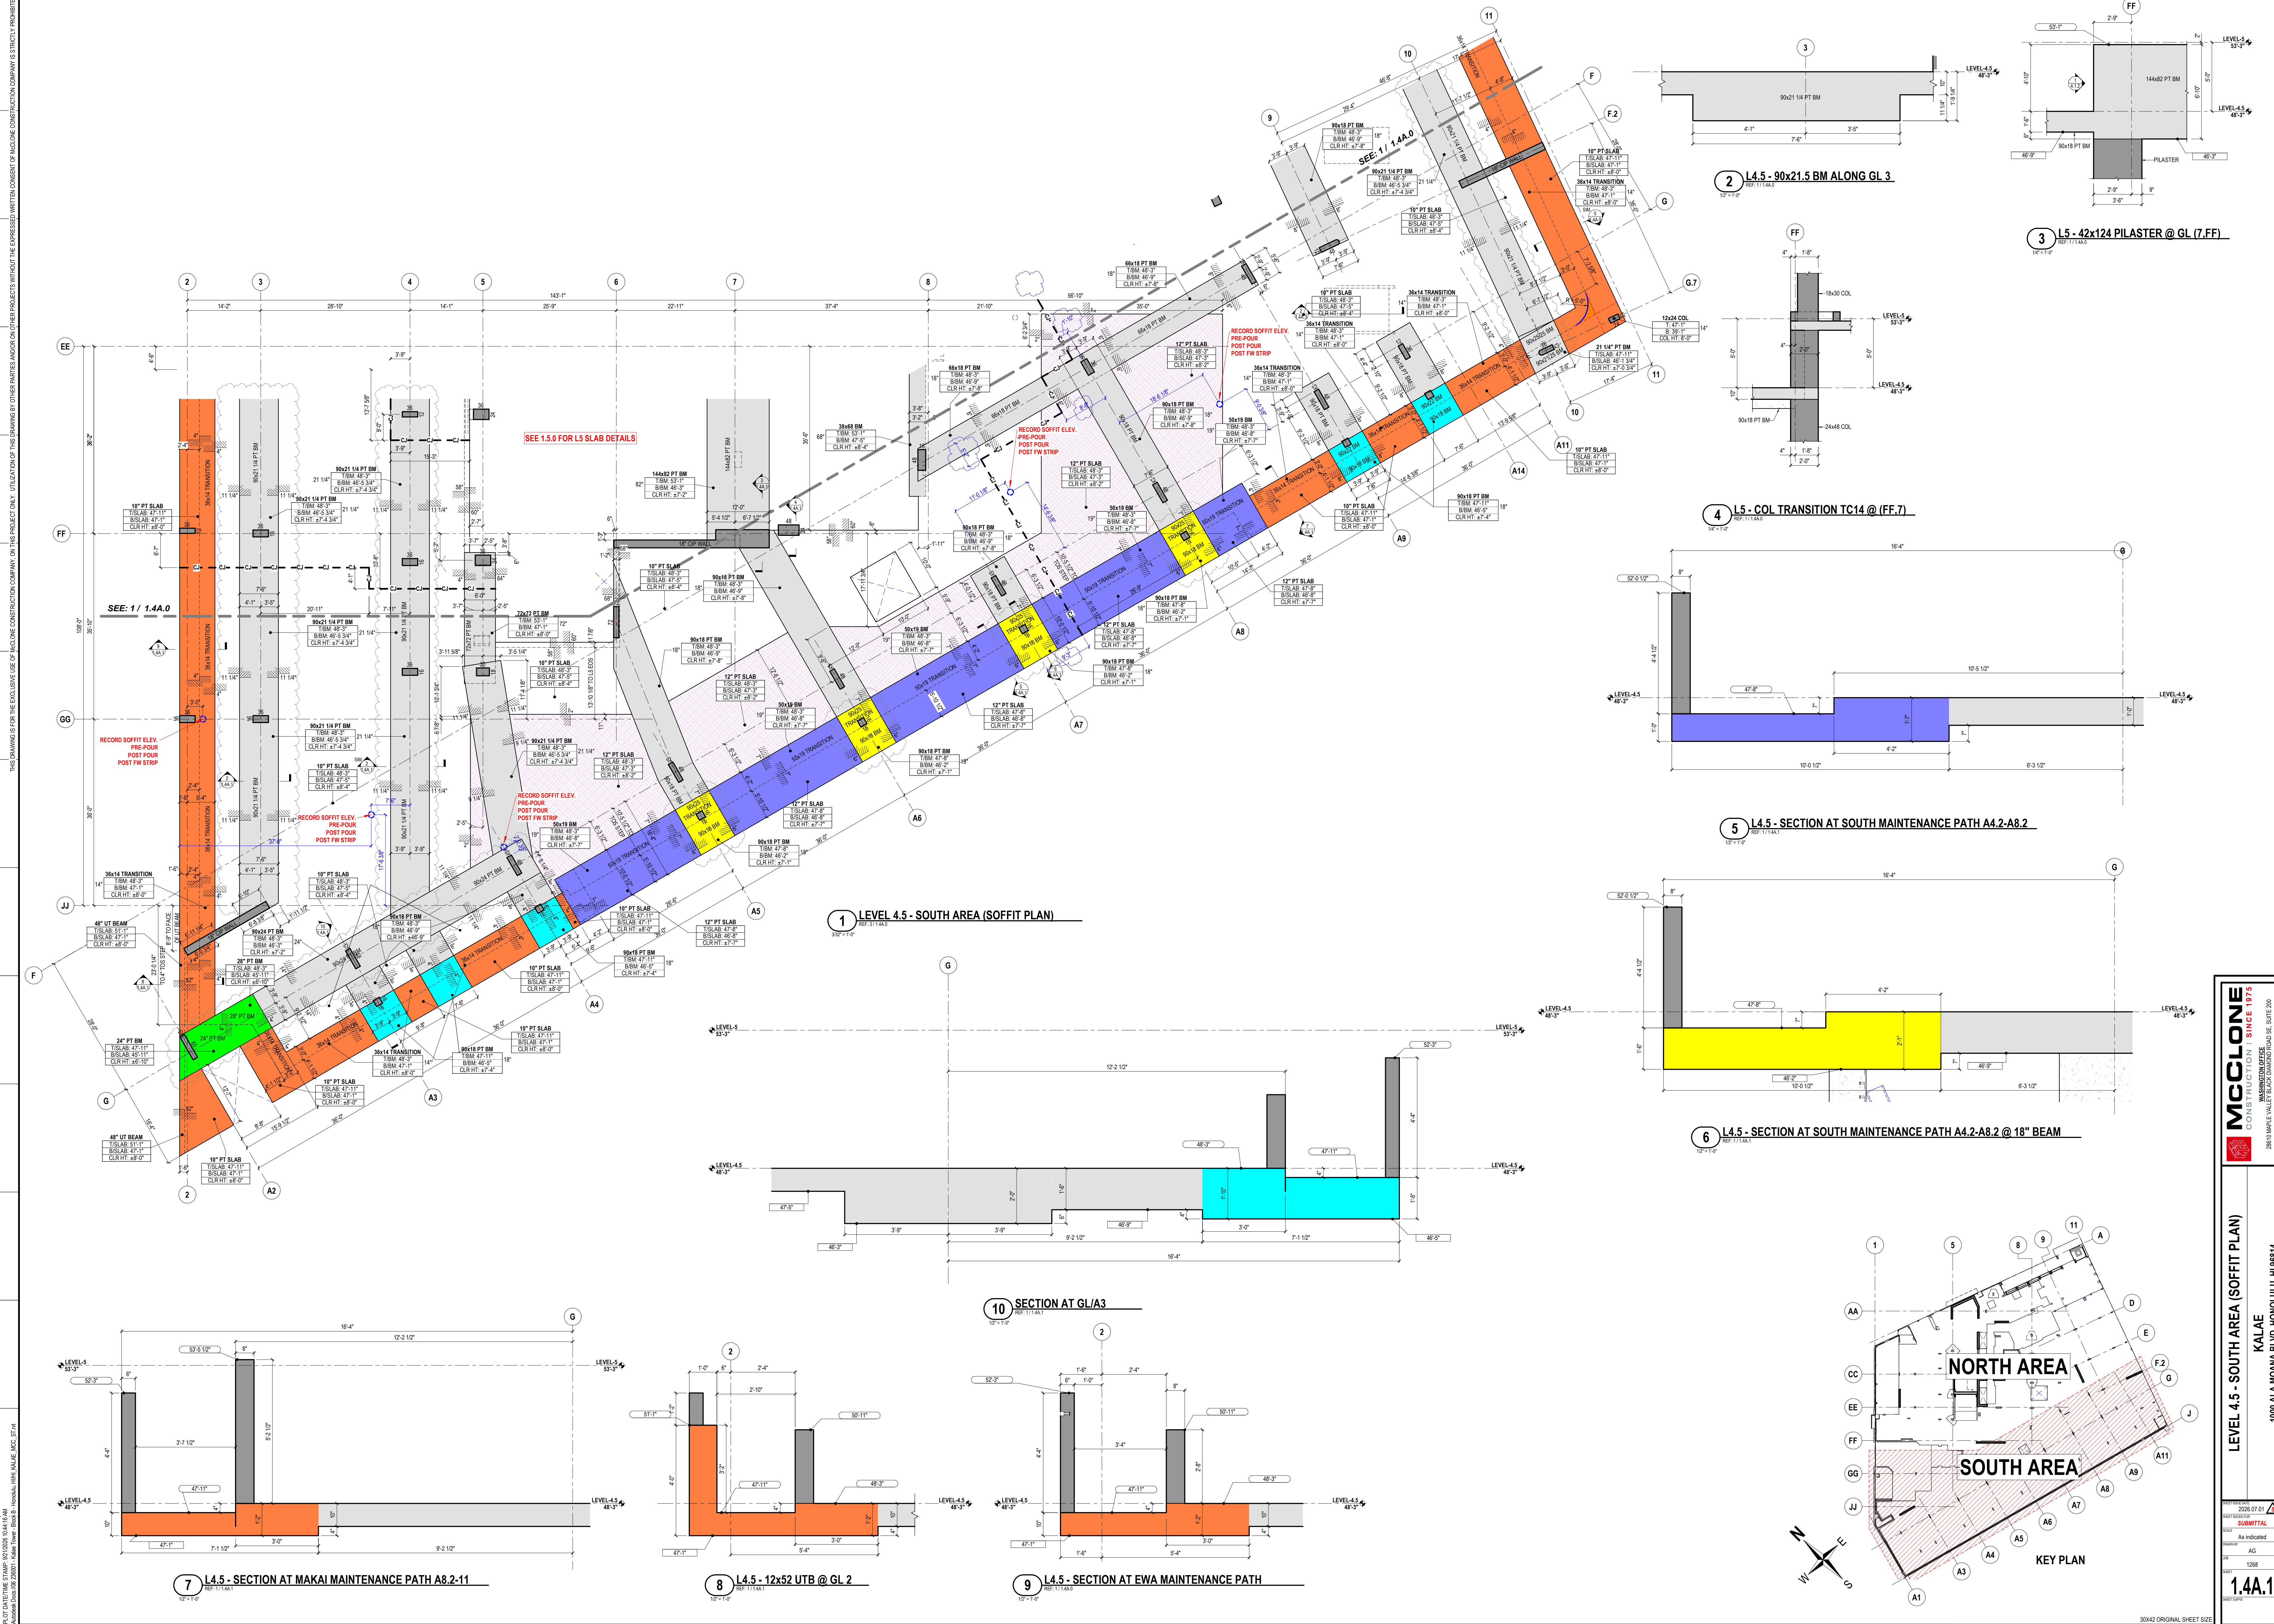


McCLONE
CONSTRUCTION
SINCE 1975
2865 MAPLE VALLEY BLVD. SUITE 200
MAPLE VALLEY, WA 98043-4258

LEVEL 4.5 - SOUTH AREA (SOFFIT PLAN)
KALAE
1000 ALA MOANA BLVD. HONOLULU, HI 96814


DATE: 2026.07.01
SUBMITTAL
As indicated
AG
1268
14A.1

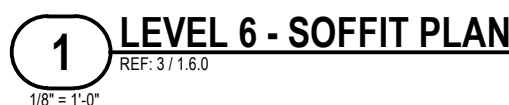


THIS DRAWING IS FOR THE EXCLUSIVE USE OF MCCCLONE CONSTRUCTION COMPANY, INC. ON THE PROJECT ONLY. UTILIZATION OF THIS DRAWING BY OTHER PARTIES AND/OR ON OTHER PROJECTS WITHOUT THE EXPRESSED WRITTEN CONSENT OF MCCCLONE CONSTRUCTION COMPANY IS STRICTLY PROHIBITED.

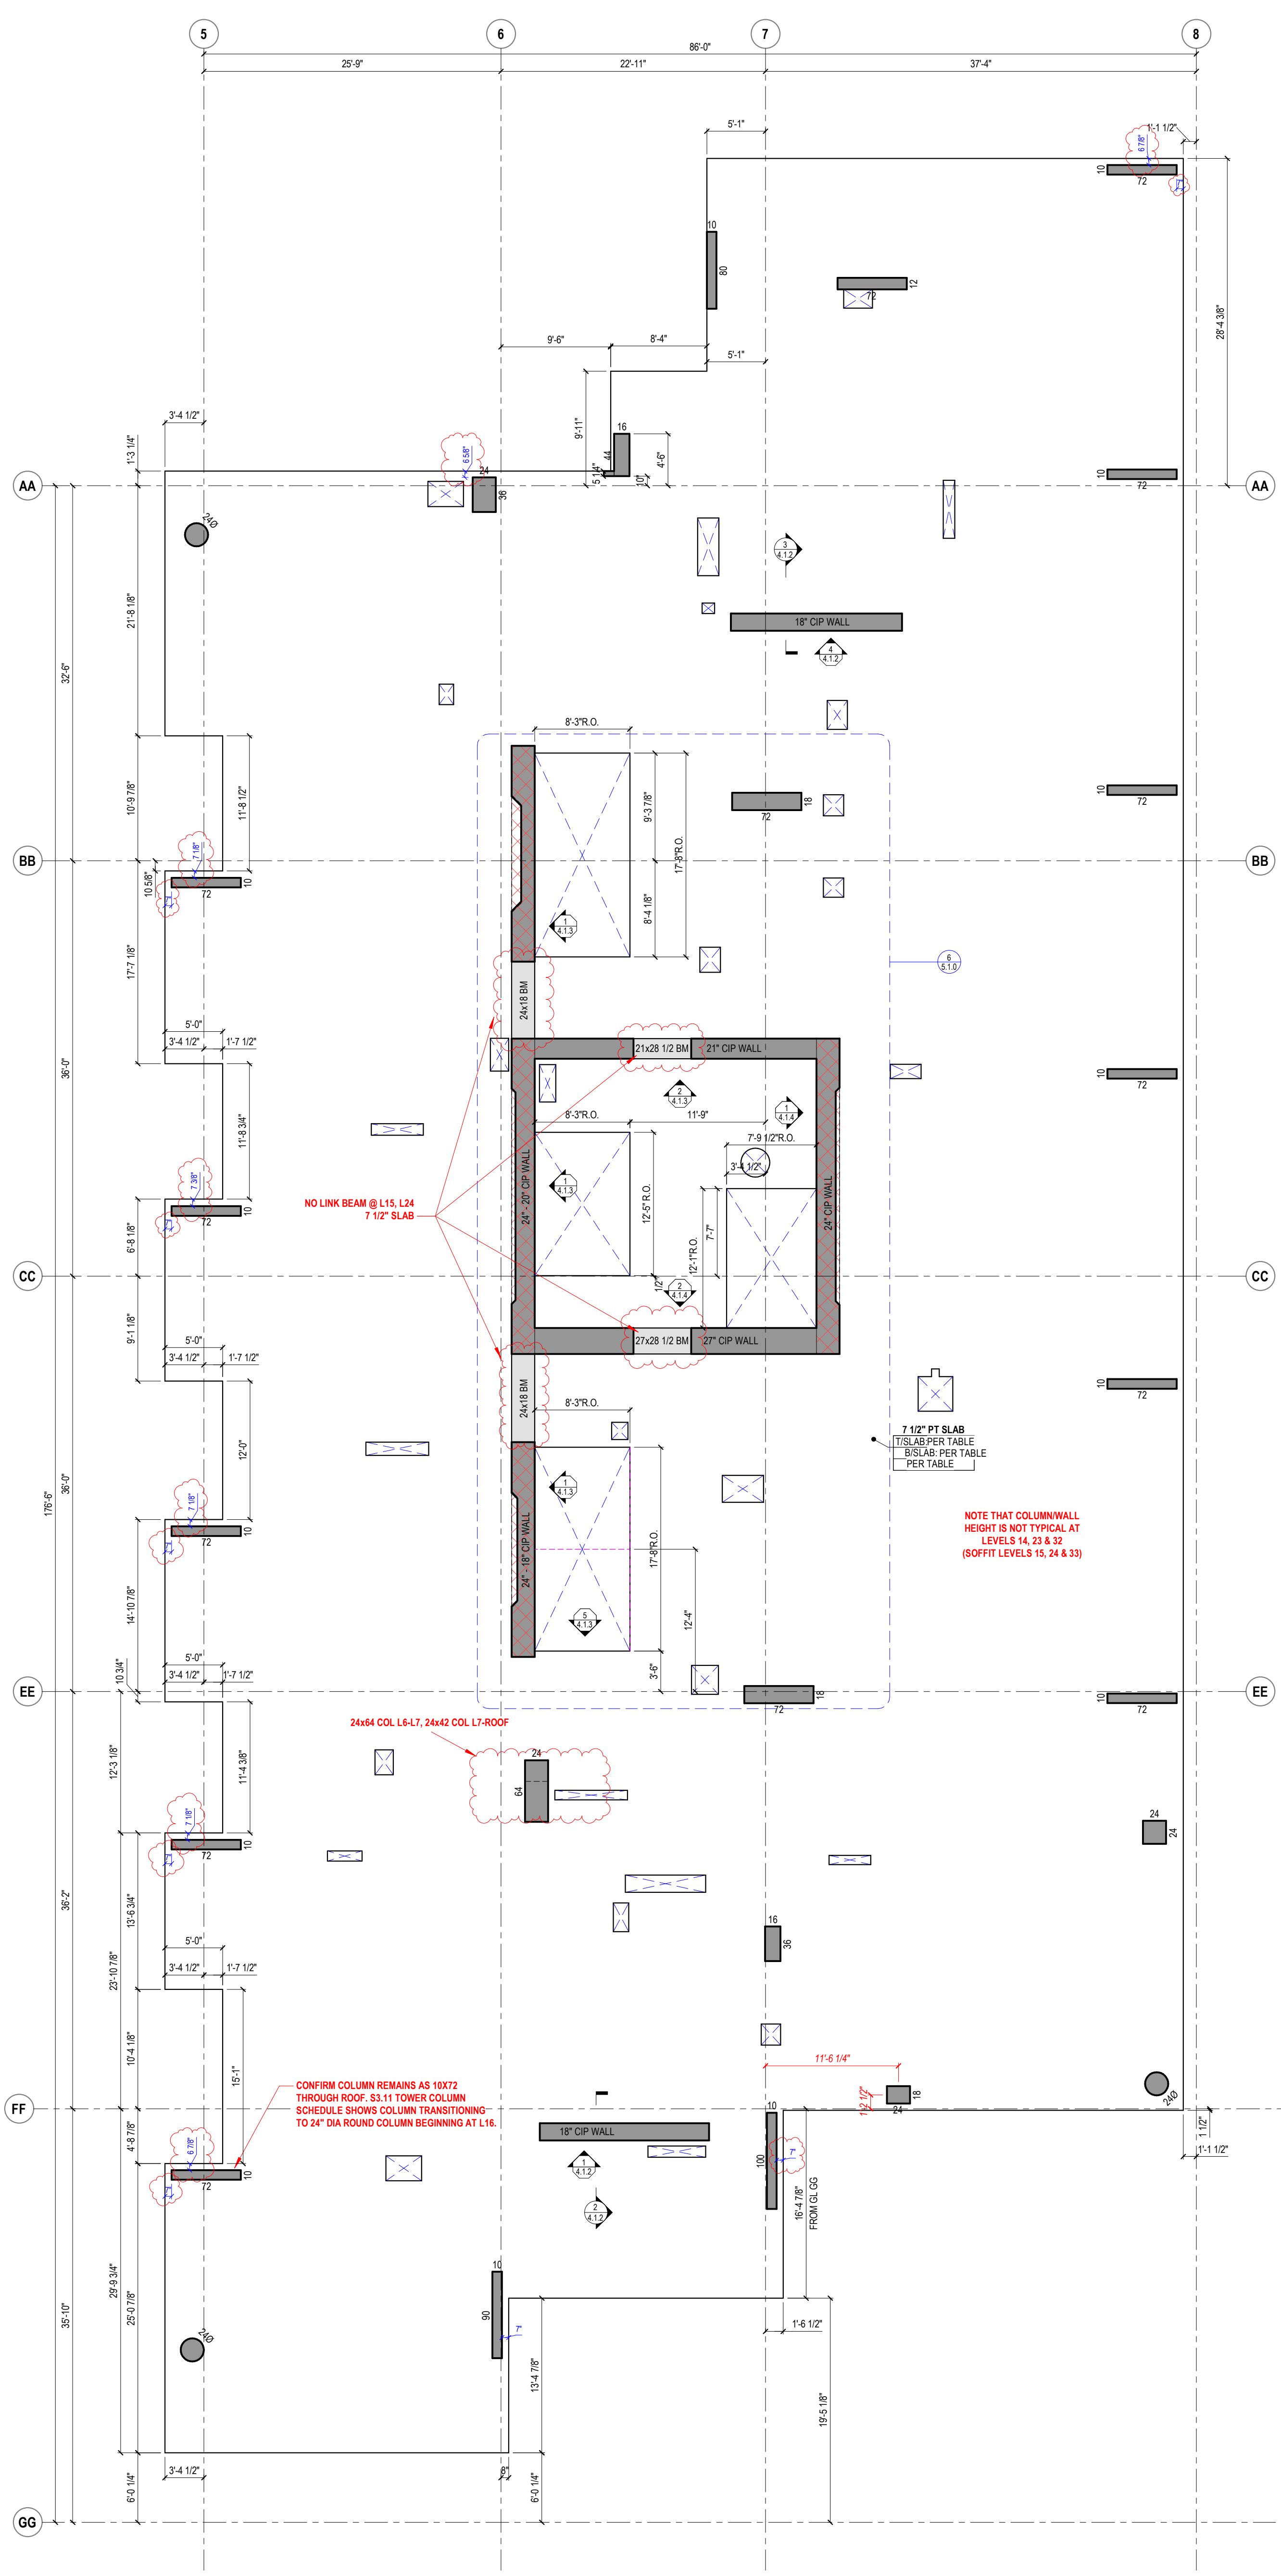

1 LEVEL 7 TO 25 - SOFFIT PLAN
REV: 11.14.12

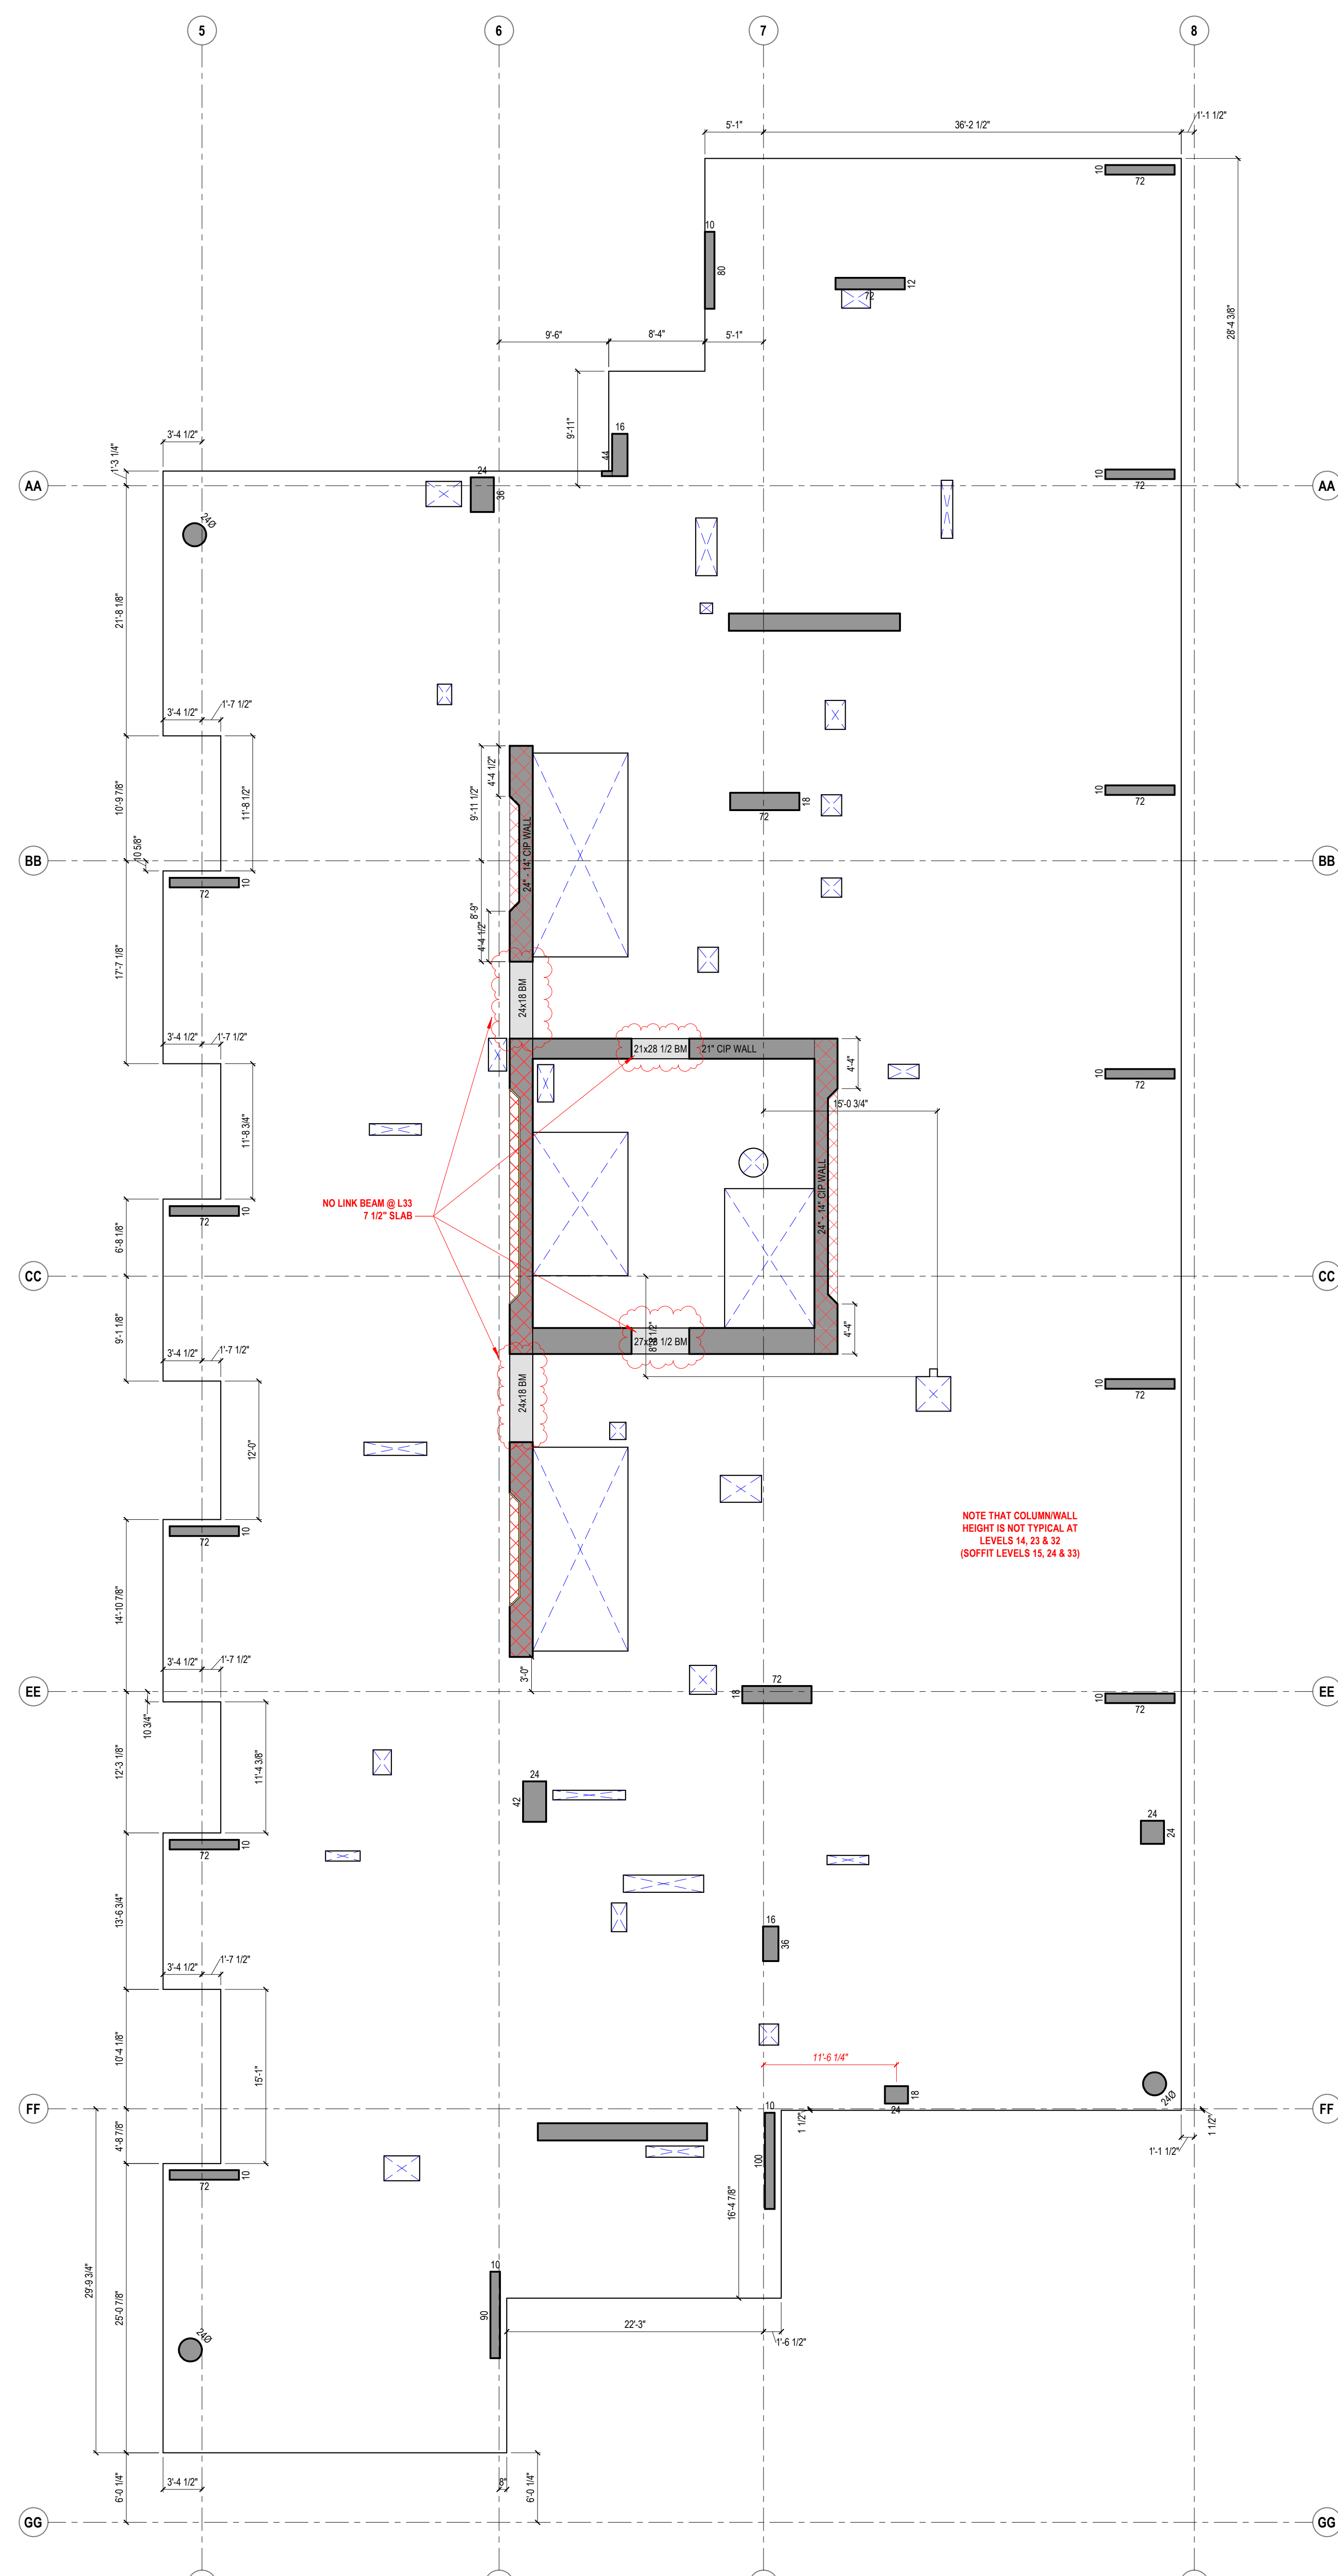

2 LEVEL 26-38 - SOFFIT PLAN
REV: 11.14.12

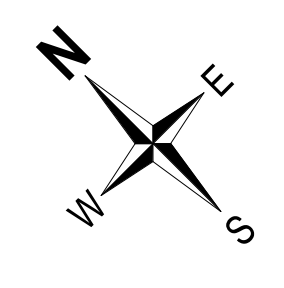

NOTE THAT COLUMN HEIGHT IS NOT TYPICAL AT LEVELS 14, 23 & 32 (SOFFIT LEVELS 15, 24 & 33)

NOTE THAT COLUMN/WALL HEIGHT IS NOT TYPICAL AT LEVELS 14, 23 & 32 (SOFFIT LEVELS 15, 24 & 33)

COL HEIGHT			
SOFFIT LEVEL	FLOOR BELOW	COL HT	QTY
MECH ROOF	ELEV MECH RM	8'-2 1/2"	2
ELEV MECH RM	ROOF	7'-10"	35
ROOF	ROOF	4'-8"	6
ROOF	LEVEL-38	11'-10 1/2"	23
LEVEL-38	LEVEL-37	10'-1"	26
LEVEL-37	LEVEL-36	9'-1"	26
LEVEL-36	LEVEL-35	9'-1"	26
LEVEL-35	LEVEL-34	9'-1"	26
LEVEL-34	LEVEL-33	9'-1"	26
LEVEL-33	LEVEL-32	9'-3"	26
LEVEL-32	LEVEL-31	9'-1"	26
LEVEL-31	LEVEL-30	9'-1"	26
LEVEL-30	LEVEL-29	9'-1"	26
LEVEL-29	LEVEL-28	9'-1"	26
LEVEL-28	LEVEL-27	9'-1"	26
LEVEL-27	LEVEL-26	9'-1"	26
LEVEL-26	LEVEL-25	9'-1"	26
LEVEL-25	LEVEL-24	9'-1"	26
LEVEL-24	LEVEL-23	9'-3"	26
LEVEL-23	LEVEL-22	9'-1"	26
LEVEL-22	LEVEL-21	9'-1"	26
LEVEL-21	LEVEL-20	9'-1"	26
LEVEL-20	LEVEL-19	9'-1"	26
LEVEL-19	LEVEL-18	9'-1"	26
LEVEL-18	LEVEL-17	9'-1"	26
LEVEL-17	LEVEL-16	9'-1"	26
LEVEL-16	LEVEL-15	9'-1"	26
LEVEL-15	LEVEL-14	9'-3"	26
LEVEL-14	LEVEL-13	9'-1"	26
LEVEL-13	LEVEL-12	9'-1"	26
LEVEL-12	LEVEL-11	9'-1"	26
LEVEL-11	LEVEL-10	9'-1"	26
LEVEL-10	LEVEL-9	9'-1"	26
LEVEL-9	LEVEL-8	9'-1"	26
LEVEL-8	LEVEL-7	9'-1"	26

TOS/SOFT ELEVATIONS		
LEVEL	TOP OF SLAB	SOFFIT
MECH ROOF	410'-11"	410'-3 1/2"
ELEV MECH RM	401'-7"	400'-11 1/2"
ROOF	392'-11"	392'-3 1/2"
LEVEL-38	380'-5"	379'-9 1/2"
LEVEL-37	369'-8 1/2"	369'-1"
LEVEL-36	360'-0"	359'-4 1/2"
LEVEL-35	350'-3 1/2"	349'-8"
LEVEL-34	340'-7"	339'-11 1/2"
LEVEL-33	330'-10 1/2"	330'-3"
LEVEL-32	321'-0"	320'-4 1/2"
LEVEL-31	311'-3 1/2"	310'-8"
LEVEL-30	301'-7"	300'-11 1/2"
LEVEL-29	291'-10 1/2"	291'-3"
LEVEL-28	282'-2"	281'-6 1/2"
LEVEL-27	272'-5 1/2"	271'-10"
LEVEL-26	262'-9"	262'-1 1/2"
LEVEL-25	253'-0 1/2"	252'-5"
LEVEL-24	243'-4"	242'-8 1/2"
LEVEL-23	233'-5 1/2"	232'-10"
LEVEL-22	223'-9"	223'-1 1/2"
LEVEL-21	214'-0 1/2"	213'-5"
LEVEL-20	204'-4"	203'-8 1/2"
LEVEL-19	194'-7 1/2"	194'-0"
LEVEL-18	184'-11"	184'-3 1/2"
LEVEL-17	175'-2 1/2"	174'-7"
LEVEL-16	165'-6"	164'-10 1/2"
LEVEL-15	155'-9 1/2"	155'-2"
LEVEL-14	145'-11"	145'-3 1/2"
LEVEL-13	136'-2 1/2"	135'-7"
LEVEL-12	126'-6"	125'-10 1/2"
LEVEL-11	116'-9 1/2"	116'-2"
LEVEL-10	107'-1"	106'-5 1/2"
LEVEL-9	97'-4 1/2"	96'-9"
LEVEL-8	87'-8"	87'-0 1/2"
LEVEL-7	77'-11 1/2"	77'-4"

MCCCLONE

CONSTRUCTION

SINCE 1975

2865 MARLE VALLEY PARKWAY SUITE 200

MARLE VALLEY, VA 22041-1253

1000 ALA MOANA BLVD. HONOLULU, HI 96814

KALAE

LEVEL 7 TO LEVEL 38 - TOWER FOOTPRINT (SOFFIT PLAN)

2026.07.01

2026.07.01

18" = 1'-0"

AG

1268

1.7.0

30X42 ORIGINAL SHEET SIZE