

PREPARED FOR
HORIZON HOUSE



DATE	ISSU
10.31.2023	100% DESIGN DEVELOPMENT
06.28.2024	PHASE 1 SHORING/EX/STRUCT PERMIT
04.04.2025	50% CONSTRUCTION DOCUMENTS
08.15.2025	GMP

MICHAEL BARNES

PROJECT MANAGER

PROJECT ARCHITECT

PROJECT DESIGNER


CHECK

TITLE

LOAD MAPS

PROJECT NO.
2131000
DATE
08/15/2025


SHEET NUMBER:
S-1.03
GMP SET
© 2024 MITHUN, INC.

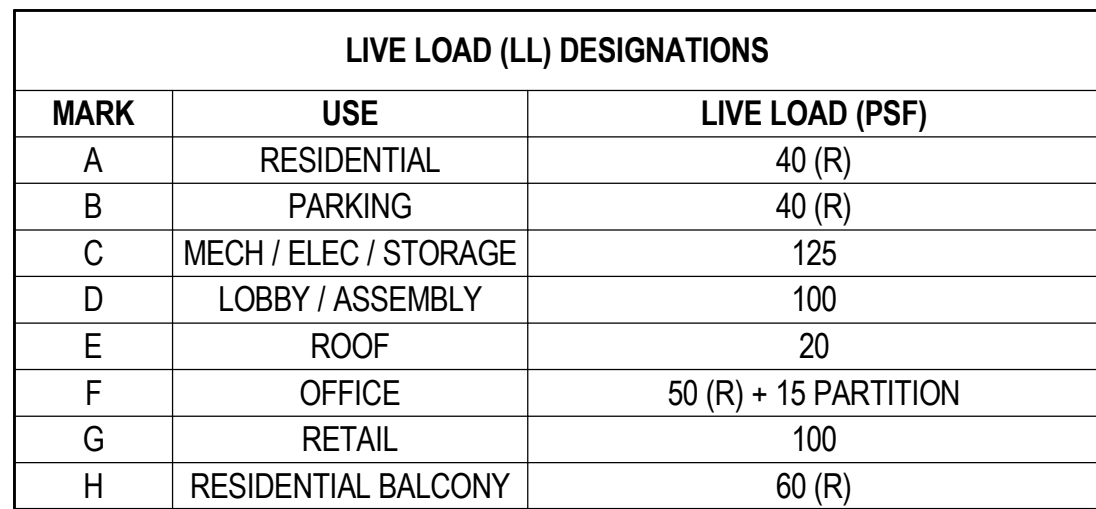

SUPERIMPOSED DEAD LOAD (SDL) DESIGNATIONS							
MARK	TYPE	TOTAL SDL (PSF)	CEILING/MEP LOAD (PSF)	FLOOR FINISH LOAD (PSF)	PARTITION LOAD (PSF)	SPECIAL LOAD (PSF)	SPECIAL LOAD DESCRIPTION
1	RESIDENTIAL	25	5	5	15	-	
2	CORRIDOR/ STAIR	10	5	5	-	-	
3	PARKING	5	5	-	-	-	
4	MECH / ELEC / STORAGE	10	10	-	-	-	
5	ROOF	20	5	-	-	15	ROOFING
6	HEAVY FINISH	35	5	15	15	-	
7	OFFICE	20	5	15	-	-	
8	TERRACE	80	5	75	-	-	
9	GREEN ROOF	120	-	-	-	120	
10	PAVERS	115	5	-	-	110	2" PAVERS + BU SLAB
11	PLANTERS	240	-	-	-	240	30" OF 95 PCF SOIL
12	BALCONY	10	5	5	-	-	

1. LIVE LOADS MARKED (R) ARE REDUCIBLE IN ACCORDANCE WITH THE BUILDING CODE
2. SUPERIMPOSED DEAD LOADS ARE IN ADDITION TO THE SELF-WEIGHT OF THE STRUCTURE.
3. SEE FRAMING PLANS FOR DESIGN LOAD OF SPECIFIC ITEMS SUCH AS ELEVATORS, ESCALATORS, AND MECHANICAL / ELECTRICAL EQUIPMENT.

1. REFER TO GENERAL NOTES, "EXTERIOR CLADDING" FOR ADDITIONAL INFORMATION
2. STRUCTURE IS DESIGNED FOR THE EQUIVALENT UNIFORM LOAD CORRESPONDING TO THE ANTICIPATED WEIGHT OF THE CLADDING SYSTEM. CLADDING ATTACHMENT WILL APPLY CONCENTRATED LOADS TO THE STRUCTURE. CONTRACTOR SHALL SUBMIT TYPICAL CLADDING ATTACHMENT DETAILS FOR REVIEW AND COMMENT PRIOR TO PREPARATION OF DETAILED CLADDING SUBMITTAL.

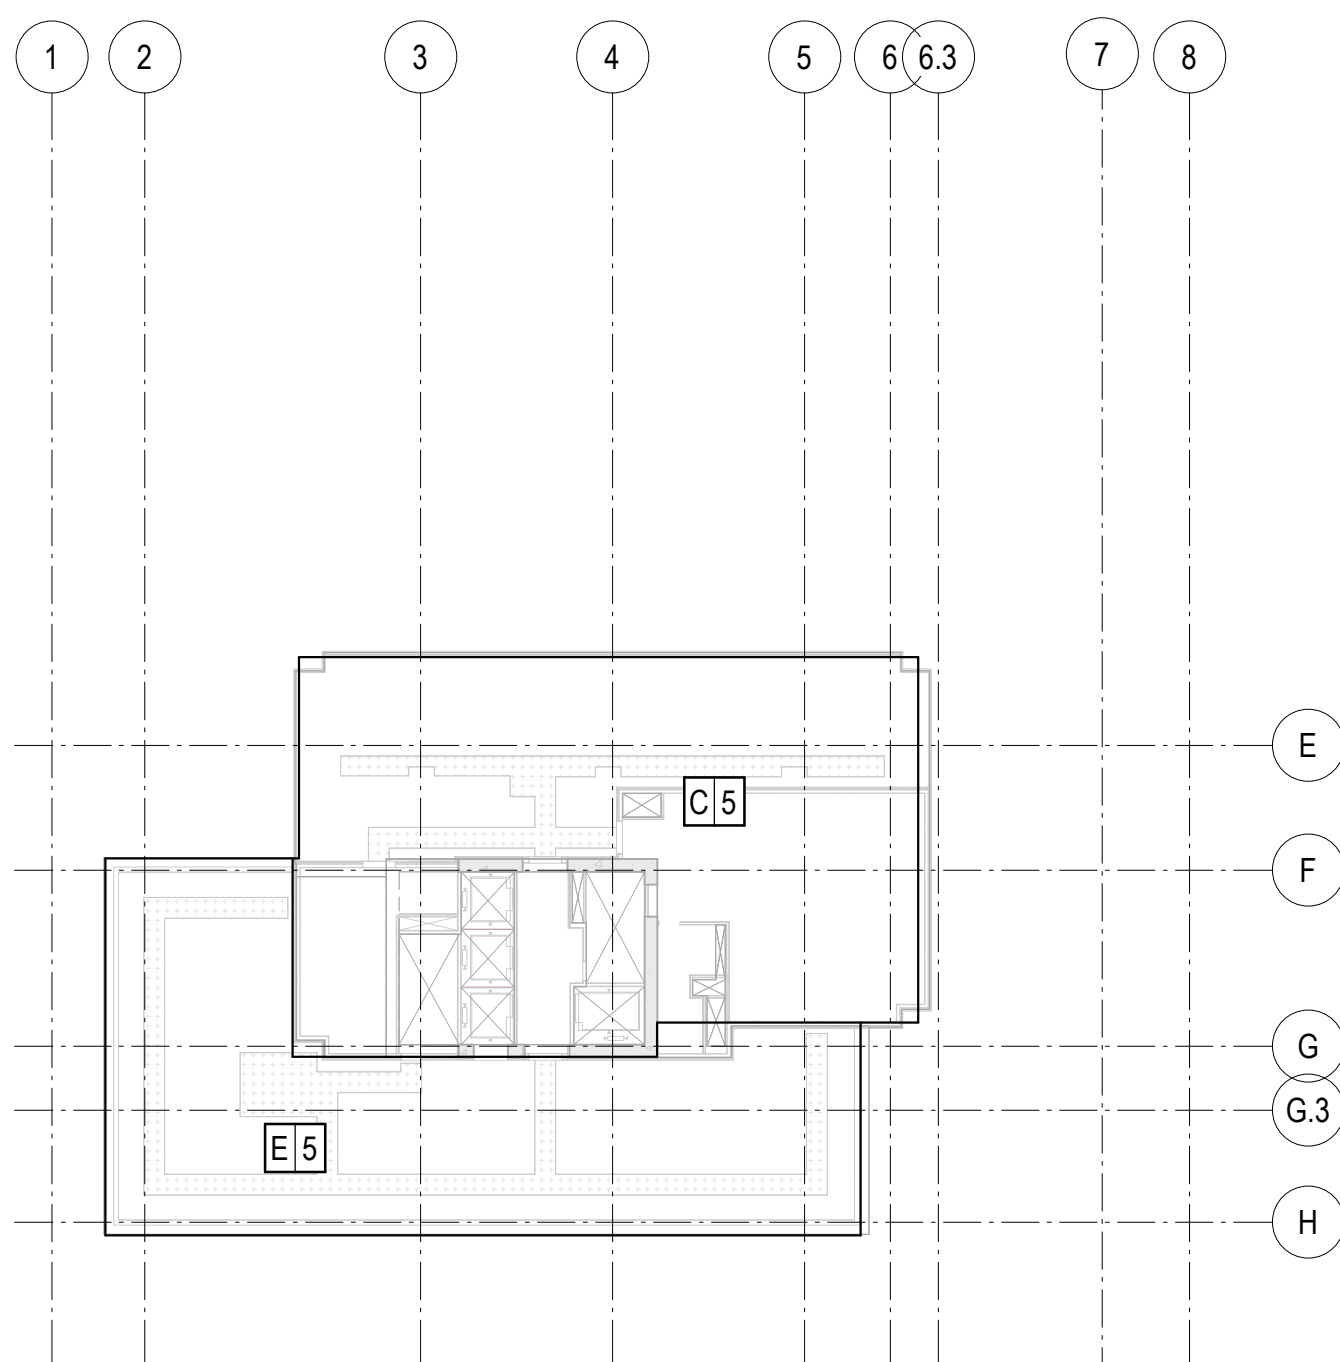

8 ROOF

19



20

THIS DRAWING IS FOR THE EXCLUSIVE USE OF MCCLONE CONSTRUCTION COMPANY. ON THE PROJECT ONLY. UTILIZATION OF THIS DRAWING BY OTHER PARTIES WITHOUT THE EXPRESSED WRITTEN CONSENT OF MCCLONE CONSTRUCTION COMPANY IS STRICTLY PROHIBITED.


PLT DATE/TIME STAMP: 9/20/2025 5:05:11 PM
DRAWING: 1.187.0 FOUNDATION PLAN
PROJECT: 1332 Maple - Final.dwg




1 LEVEL-B7 FOUNDATION PLAN

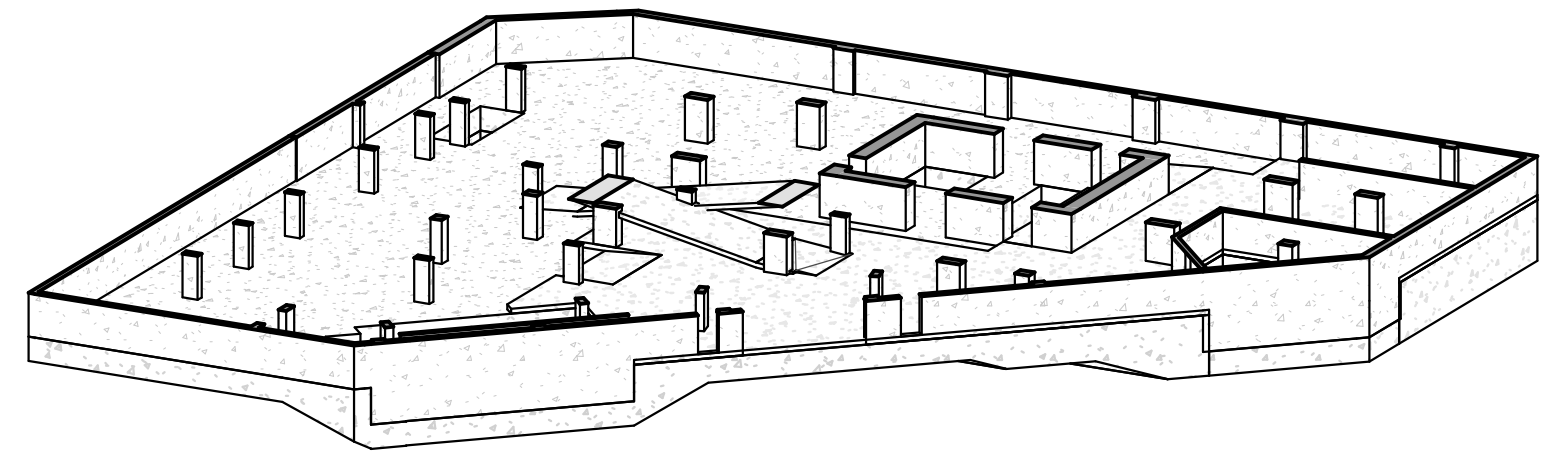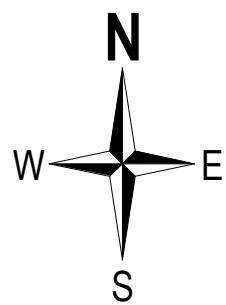

3D VIEW- LEVEL B7

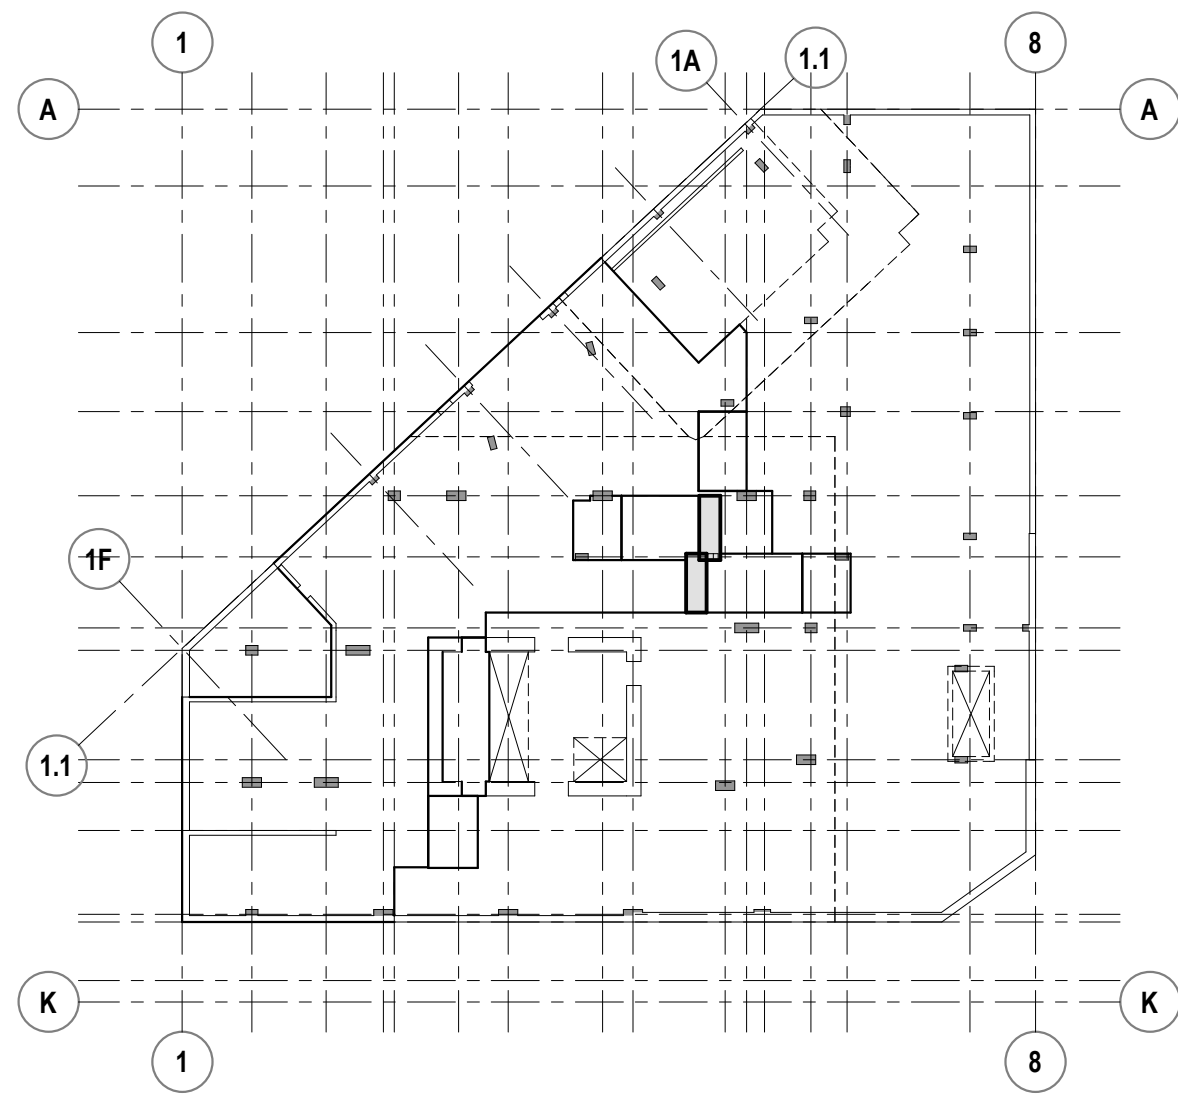

LEVEL-B7 KEY PLAN

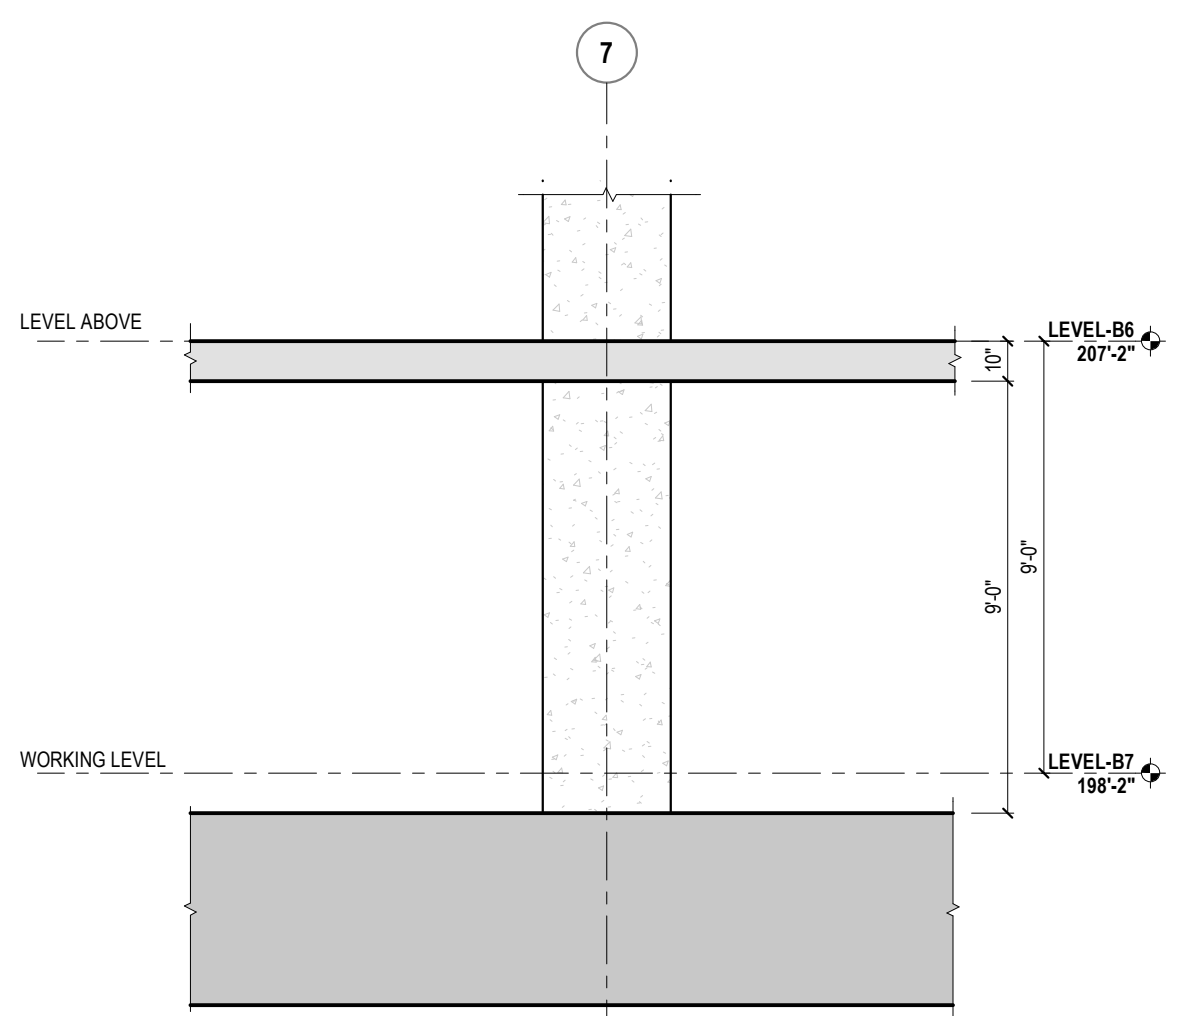

2 LEVEL-B7 BUILDING SECTION

NOTES:

- 3/4" CHAMFER ON ALL EXPOSED CONCRETE CORNERS TYP.
- ALL COLUMNS ARE CENTERED ON GRID LINES U.N.O.
- ALL BEAMS ARE CENTERED ON GRID LINES U.N.O.
- SLAB IS 4'-0" MAT FTG TYP. U.N.O.

SYMBOLS

- 1-BOX (ROUND ENDS)
TOP OF CONCRETE ELEVATIONS
- 1-BOX
BOTTOM OF CONCRETE ELEVATIONS
- 2-BOX (PLAN VIEWS)
TOP & BOTTOM ELEVATIONS
0'-1" DEPTH OF CONC MEMBER
- 3-BOX (FLOOR PLANS)
TOP & BOTTOM ELEVATIONS
COLUMN ELEVATION ABOVE REF. LEVEL
0'-1" DEPTH OF CONC MEMBER

SECTION VIEW

- Ref. DETAIL NUMBER
1-1
- SHEET NUMBER
1332
- ELEVATION VIEW
1332
- SHEET NUMBER
1332


LEGEND

SHAPE DESIGNATIONS

- FOOTINGS OR FOUNDATIONS
- WALLS OR COLUMNS
- CNU WALLS
- DELAY STRIP OR CLOSURE POUR
- GRADE OR SOIL


LINE DESIGNATIONS

- INDICATES TOP OF FTG CHANGE OR EDGE OF FTG
- INDICATES BOTTOM OF FTG CHANGE
- INDICATES CONSTRUCTION JOINT
- INDICATES GRID LINE

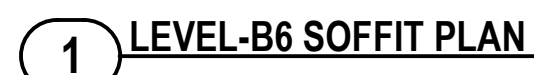

1. 3/4" CHAMFER ON ALL EXPOSED CONCRETE CORNERS TYP.
2. ALL COLUMNS ARE CENTERED ON GRID LINES U.N.O.
3. ALL BEAMS ARE CENTERED ON GRID LINES U.N.O.
4. SLAB THICKNESS IS 10" MILD-REINFORCED TYP. U.N.O.

McCLONE
CONSTRUCTION | SINCE 1975
WASHINGTON OFFICE
2885 10 MAPLE VALLEY BLACK DIAMOND ROAD SE, SUITE 200
BLACK DIAMOND, WA 98010
TEL: 206.451.0000 FAX: 206.451.0001

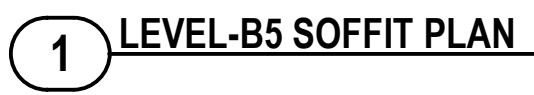

1. 3/4" CHAMFER ON ALL EXPOSED CONCRETE CORNERS TYP.
2. ALL COLUMNS ARE CENTERED ON GRID LINES U.N.O.
3. ALL BEAMS ARE CENTERED ON GRID LINES U.N.O.
4. SLAB THICKNESS IS 16" MILD-REINFORCED TYP. U.N.O.




McCLONE
CONSTRUCTION | SINCE 1975

LEVEL- B5 (SOFFIT PLAN)



SHEET ISSUE DATE	09/21/2026	
SHEET ISSUED FOR	PRELIMINARY	
SCALE	As indicated	
POINTS/SQ	YK	
DB	1332	
SHEET	1.B5.0	
SHEET SUFFIX		

THIS DRAWING IS FOR THE EXCLUSIVE USE OF MCCLONE CONSTRUCTION COMPANY. ON THE PROJECT ONLY. UTILIZATION OF THIS DRAWING BY OTHER PARTIES WITHOUT THE WRITTEN CONSENT OF MCCLONE CONSTRUCTION COMPANY IS STRICTLY PROHIBITED.


PLT DATE/TIME Stamp: 9/20/2025 8:05:11 AM
Drawing Path: C:\Users\jmcclone\OneDrive\Documents\1332 Maple - Final.dwg
User: jmcclone
Title: 1332 Maple - Final.dwg

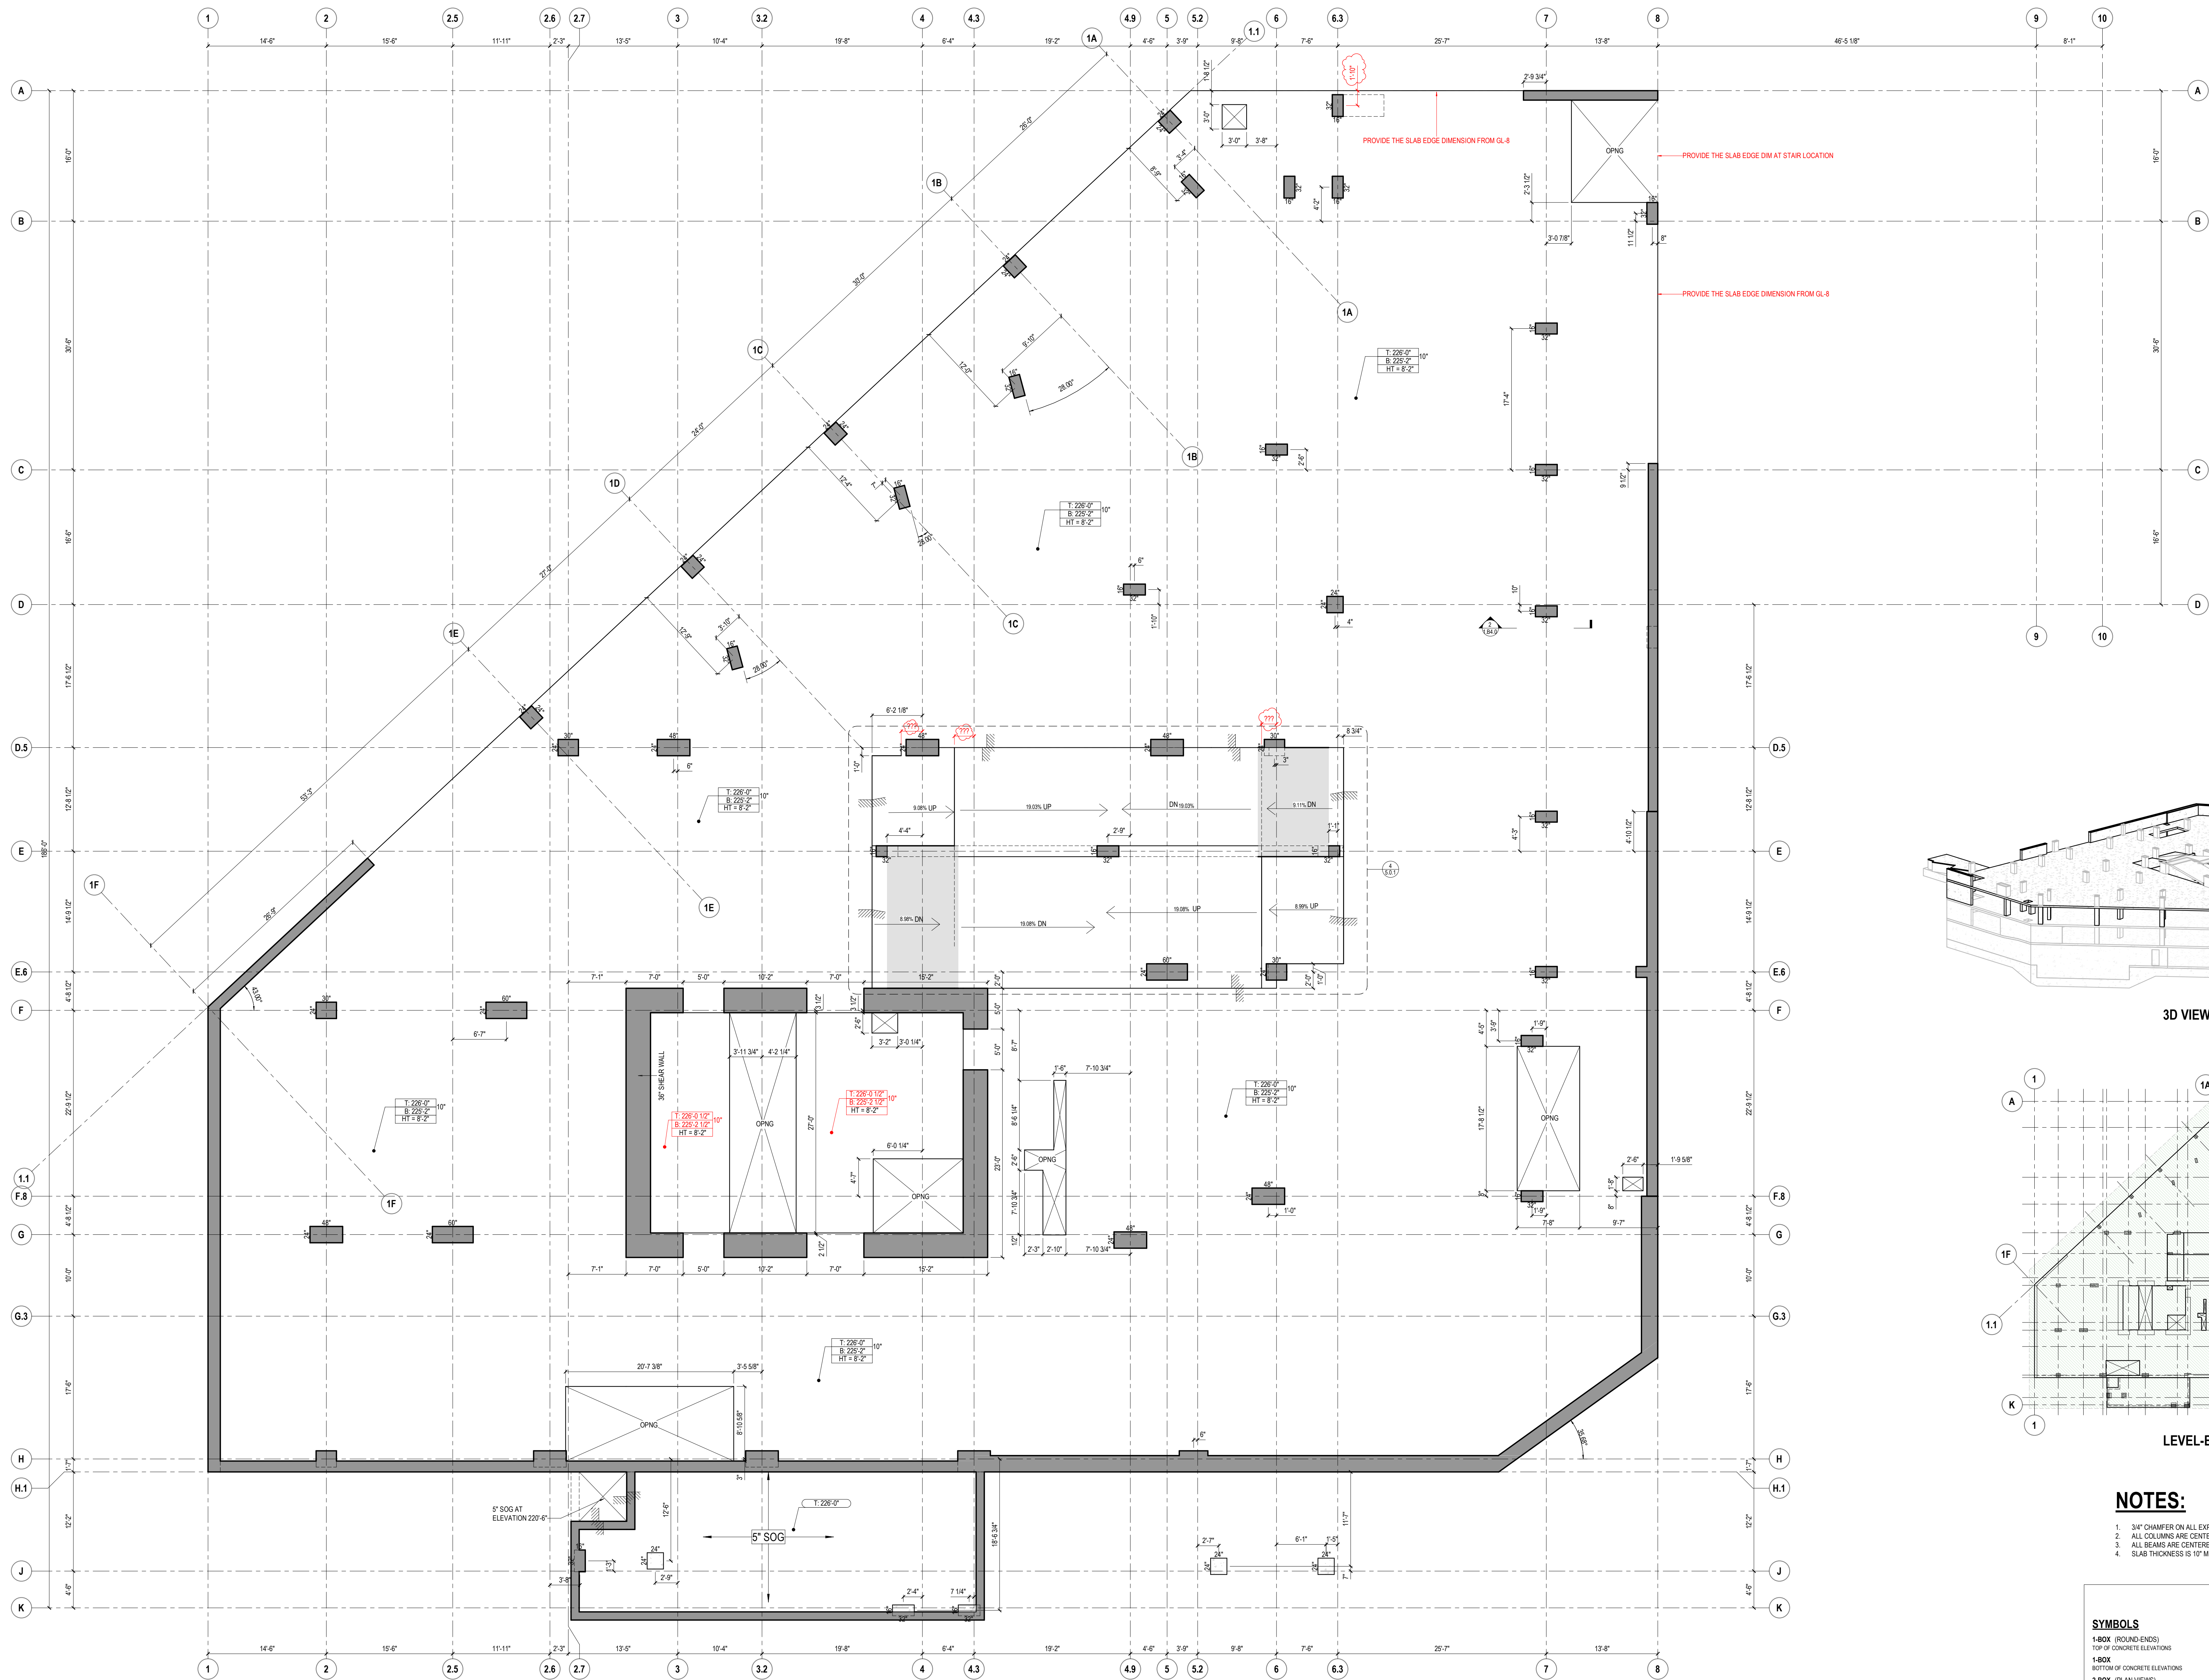


1 LEVEL-B4 (SOFFIT PLAN)

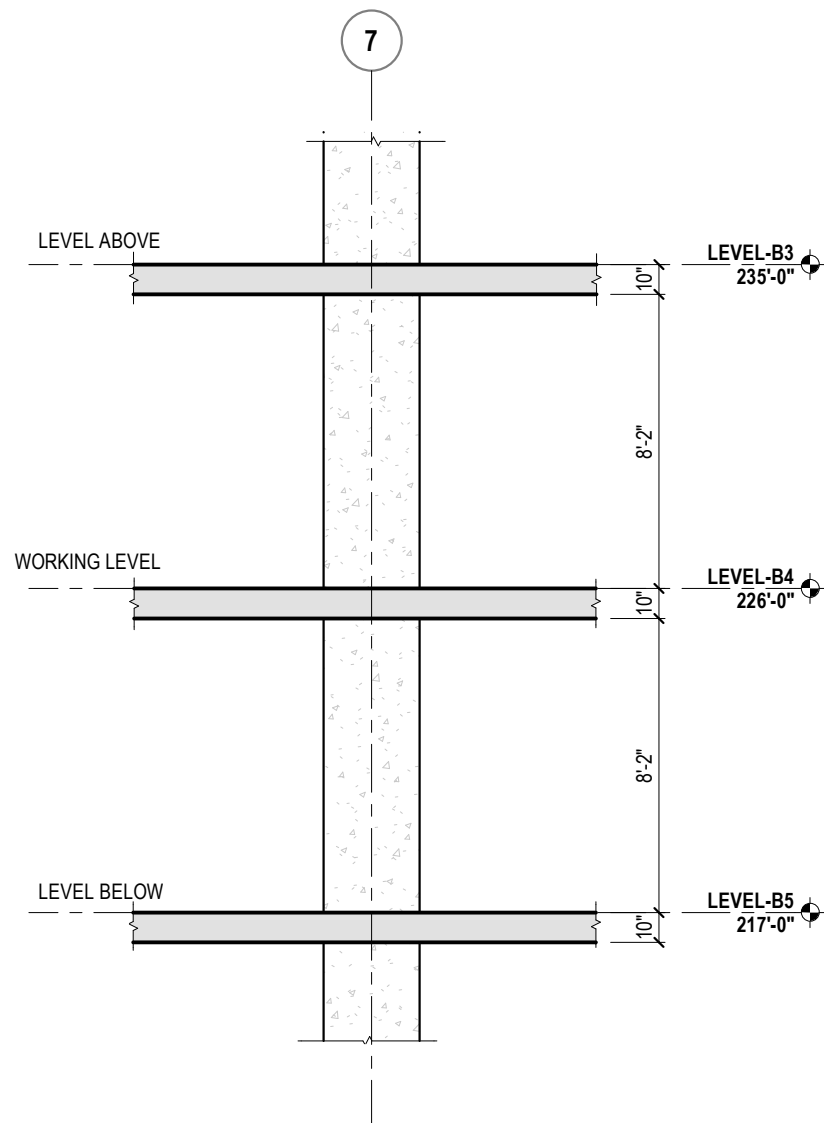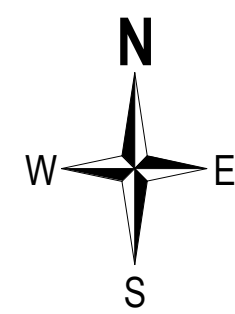

2 LEVEL-B4 BUILDING SECTION

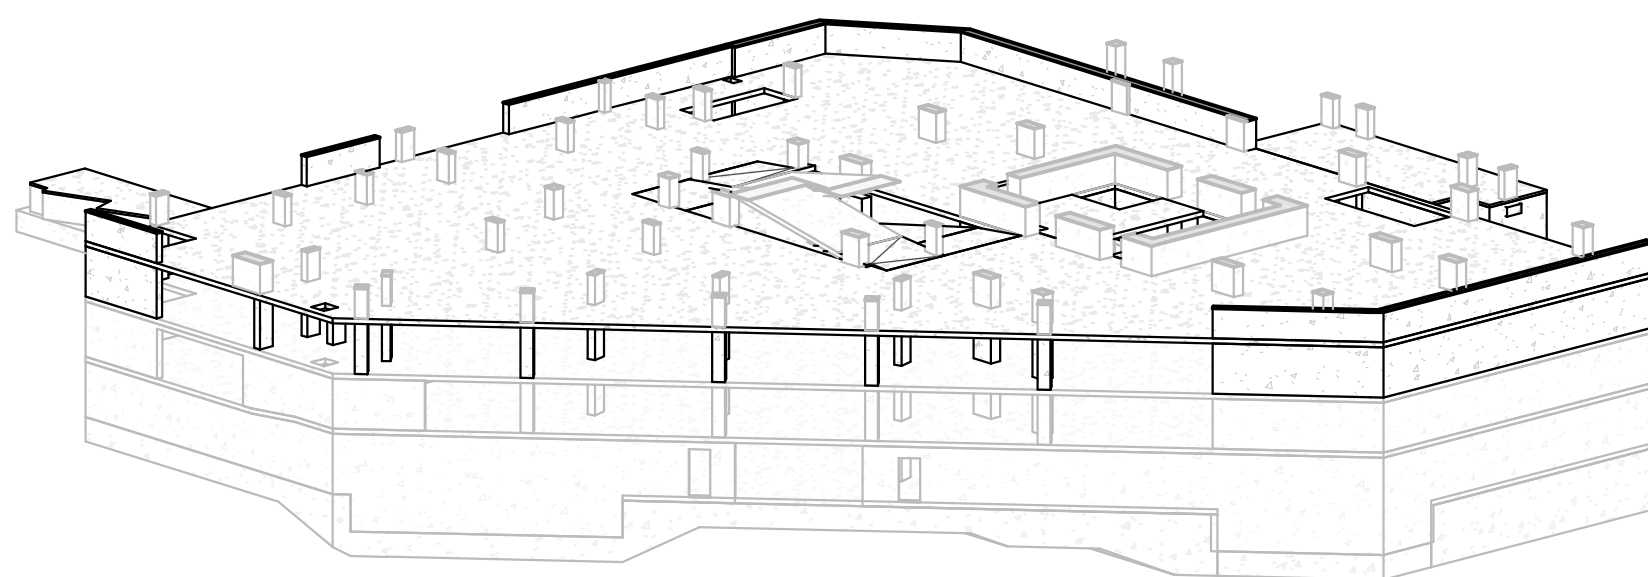

3D VIEW- LEVEL B4

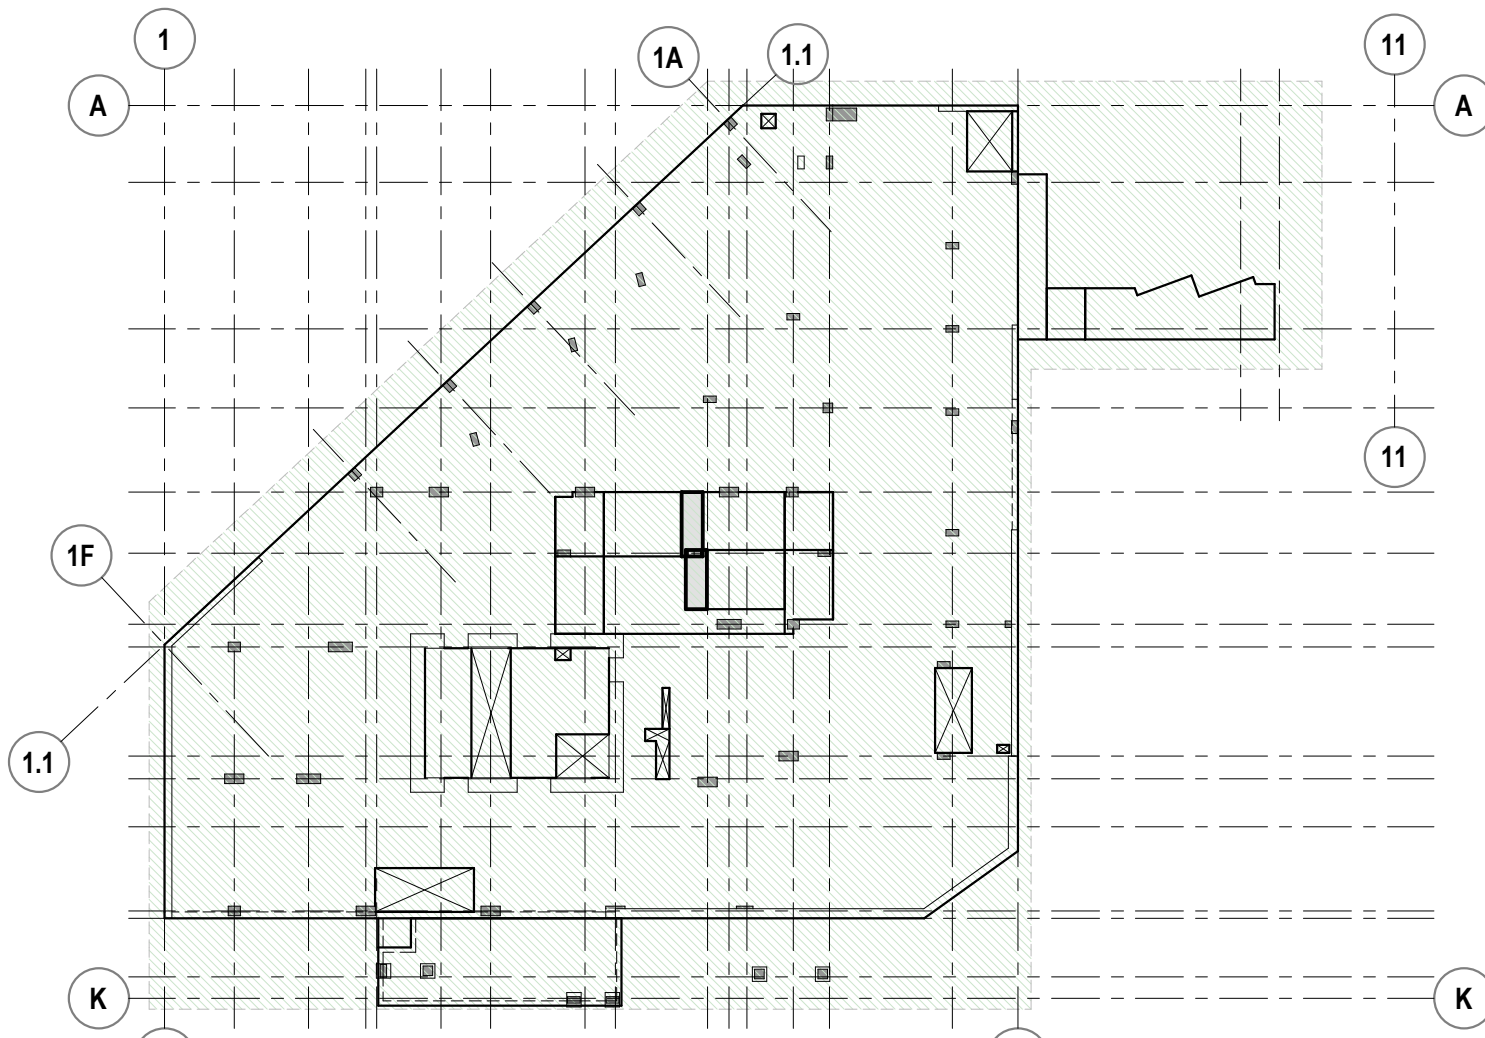

LEVEL-B4 KEY PLAN

NOTES:

- 3/4" CHAMFER ON ALL EXPOSED CONCRETE CORNERS TYP.
- ALL COLUMNS ARE CENTERED ON GRID LINES U.N.O.
- ALL BEAMS ARE CENTERED ON GRID LINES U.N.O.
- SLAB THICKNESS IS 10" MILD-REINFORCED TYP. U.N.O.


LEGEND

SYMBOLS		SHAPE DESIGNATIONS	
1-BOX (ROUND ENDS)		FOOTINGS OR FOUNDATIONS	
TOP OF CONCRETE ELEVATIONS		WALLS OR COLUMNS	
1-BOX		CNU WALLS	
BOTTOM OF CONCRETE ELEVATIONS		DELAY STRIP OR CLOSURE POUR	
2-BOX (PLAN VIEWS)		GRADE OR SOIL	
TOP & BOTTOM ELEVATIONS			
0'-DEPTH OF CONC MEMBER			
3-BOX (FLOOR PLANS)			
TOP & BOTTOM ELEVATIONS			
COLUMN ELEVATION ABOVE REF. LEVEL			
0'-DEPTH OF CONC MEMBER			
SECTION VIEW		LINE DESIGNATIONS	
Ref. DETAIL NUMBER		INDICATES TOP OF FTG CHANGE OR EDGE OF FTG	
SHEET NUMBER		INDICATES BOTTOM OF FTG CHANGE	
ELEVATION VIEW		---CJ---CJ--- INDICATES CONSTRUCTION JOINT	
SHEET NUMBER		--- INDICATES GRID LINE	


McCLONE
CONSTRUCTION
SINCE 1975
28610 MAPLE VALLEY BLVD SE SUITE 200
MAPLE VALLEY, WA 98043-4254

LEVEL-B4 (SOFFIT PLAN)
HORIZON HOUSE
900 UNIVERSITY ST, SEATTLE, WA 98101



DATE: 09/21/2025
DRAWN BY: YK
JOB: 1332
SHEET: 1.B4.0

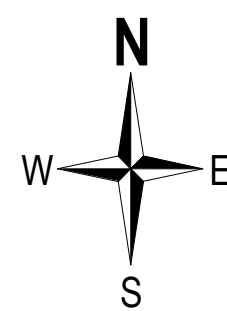


THIS DRAWING IS FOR THE EXCLUSIVE USE OF MCCLONE CONSTRUCTION COMPANY. ON THE PROJECT ONLY. UTILIZATION OF THIS DRAWING BY OTHER PARTIES WITHOUT THE WRITTEN CONSENT OF MCCLONE CONSTRUCTION COMPANY IS STRICTLY PROHIBITED.

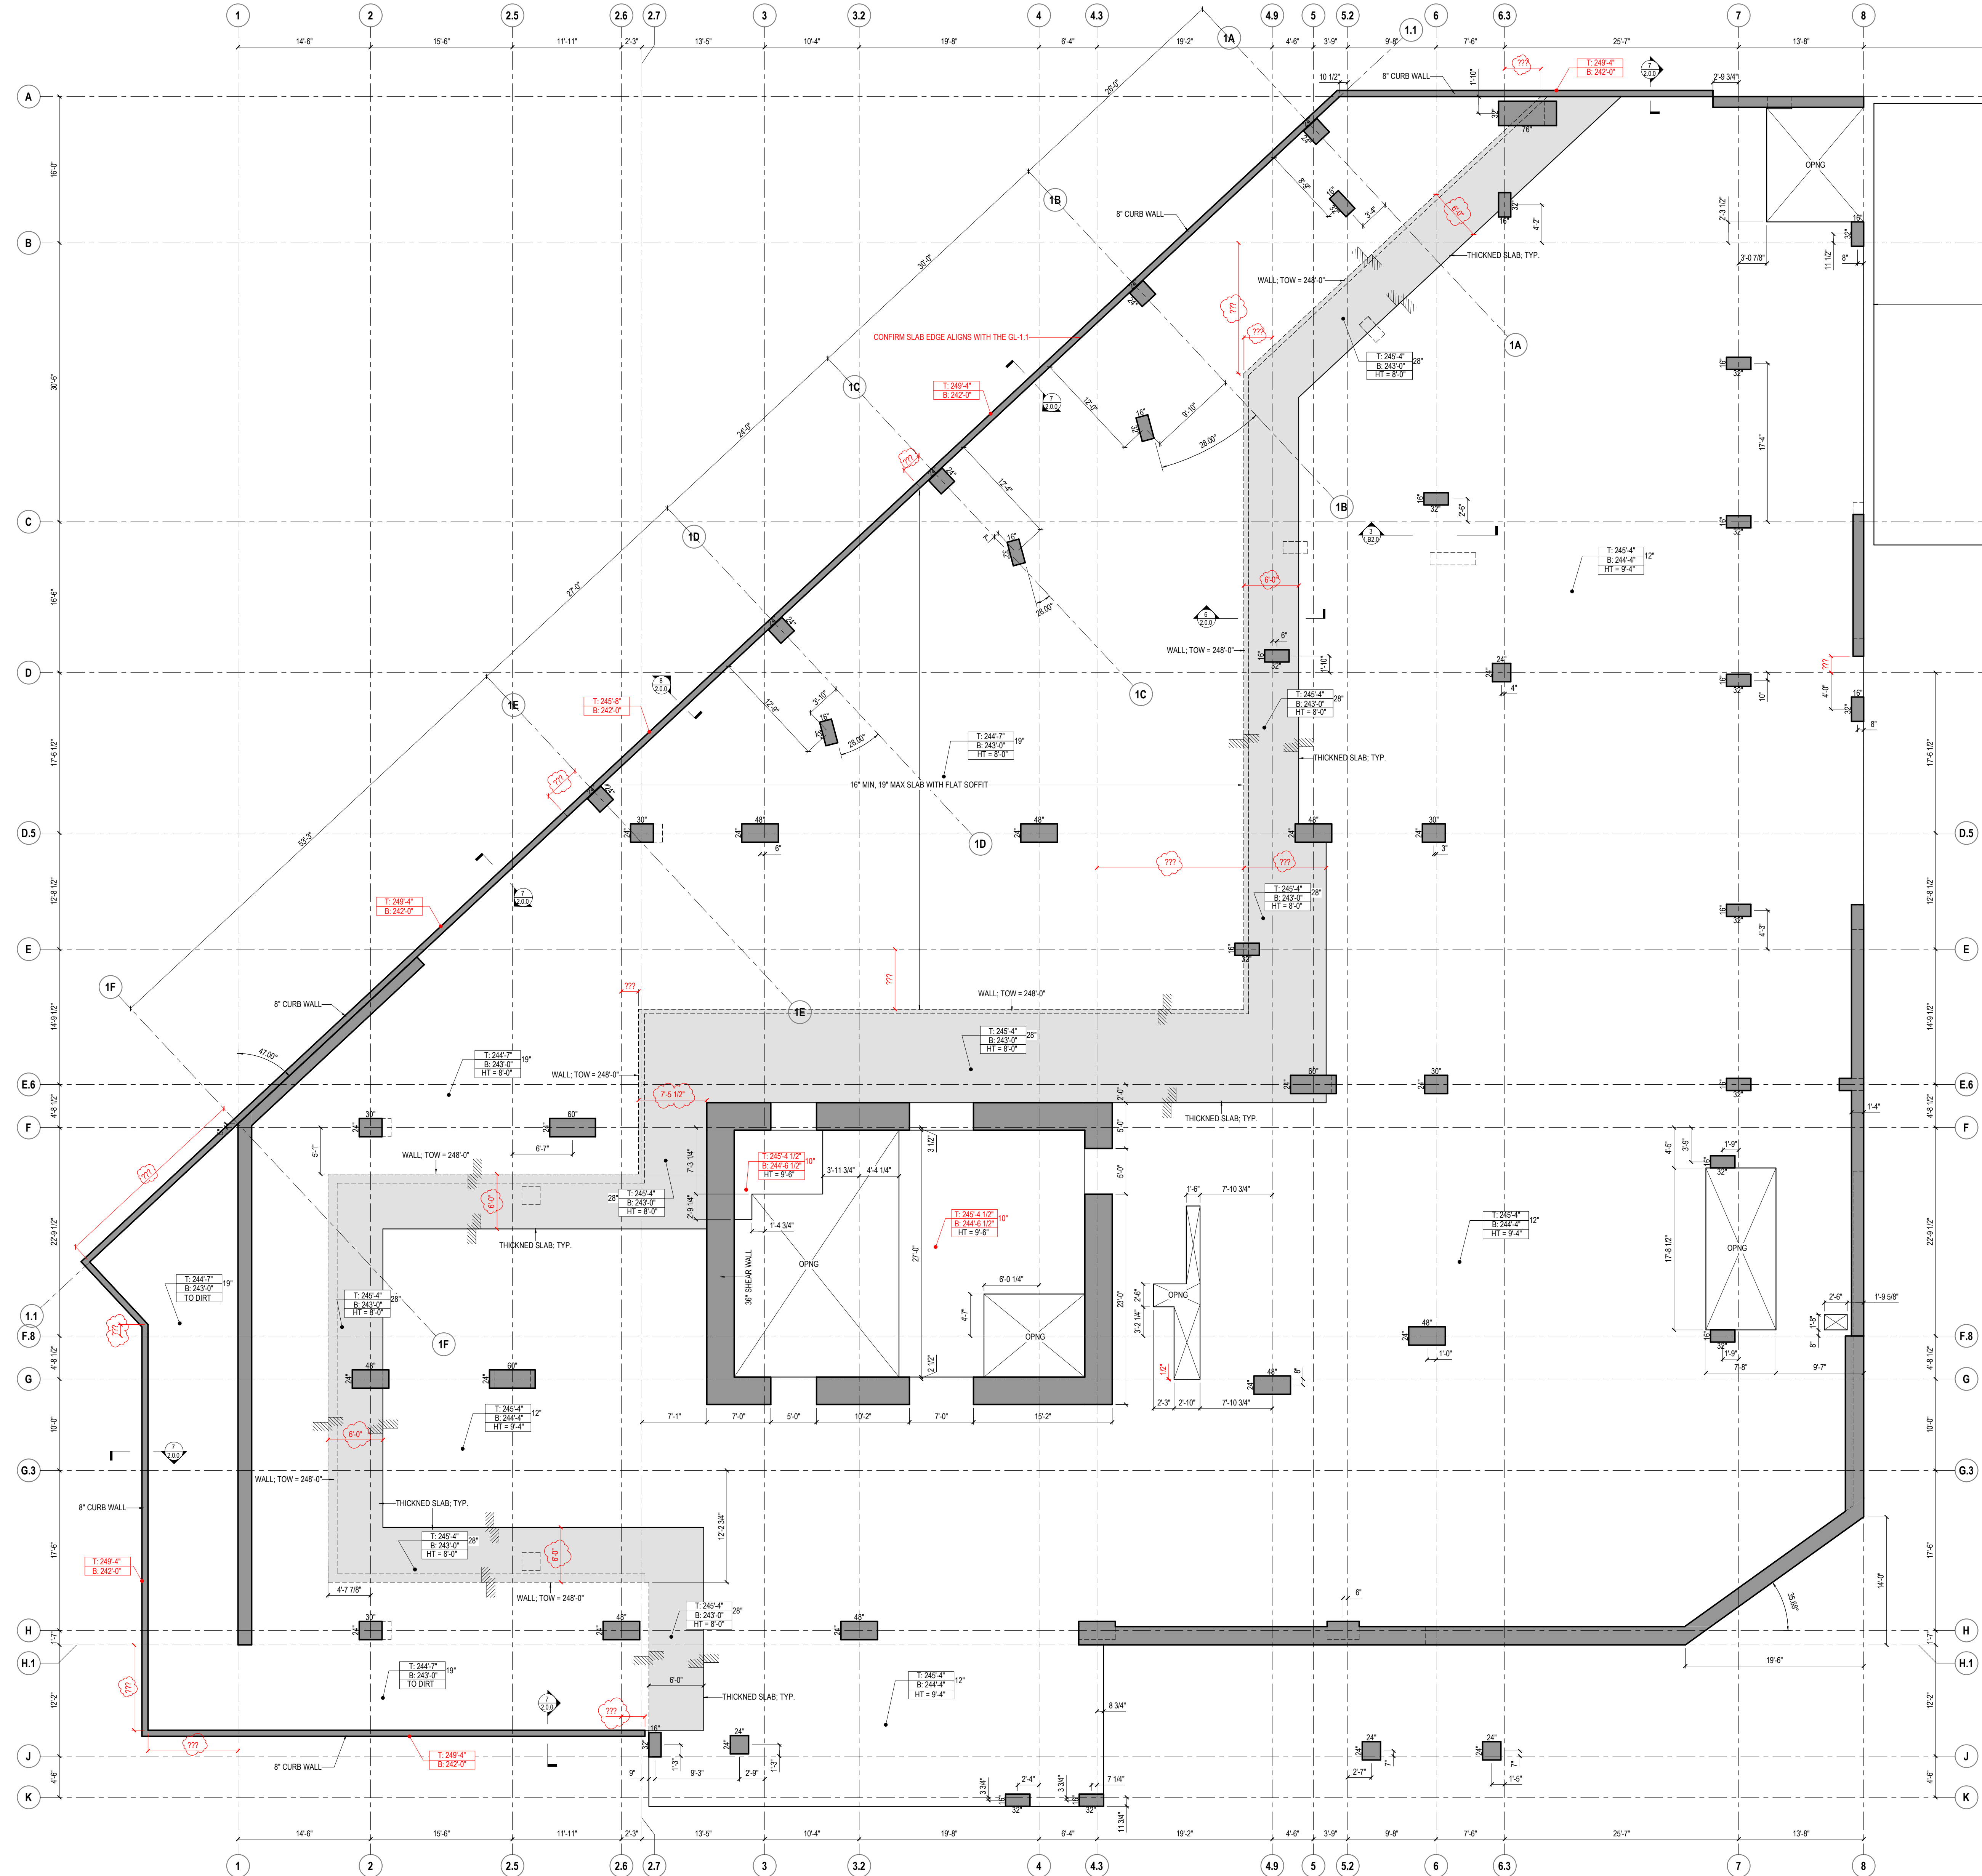

1 LEVEL-B2 (SOFFIT PLAN)

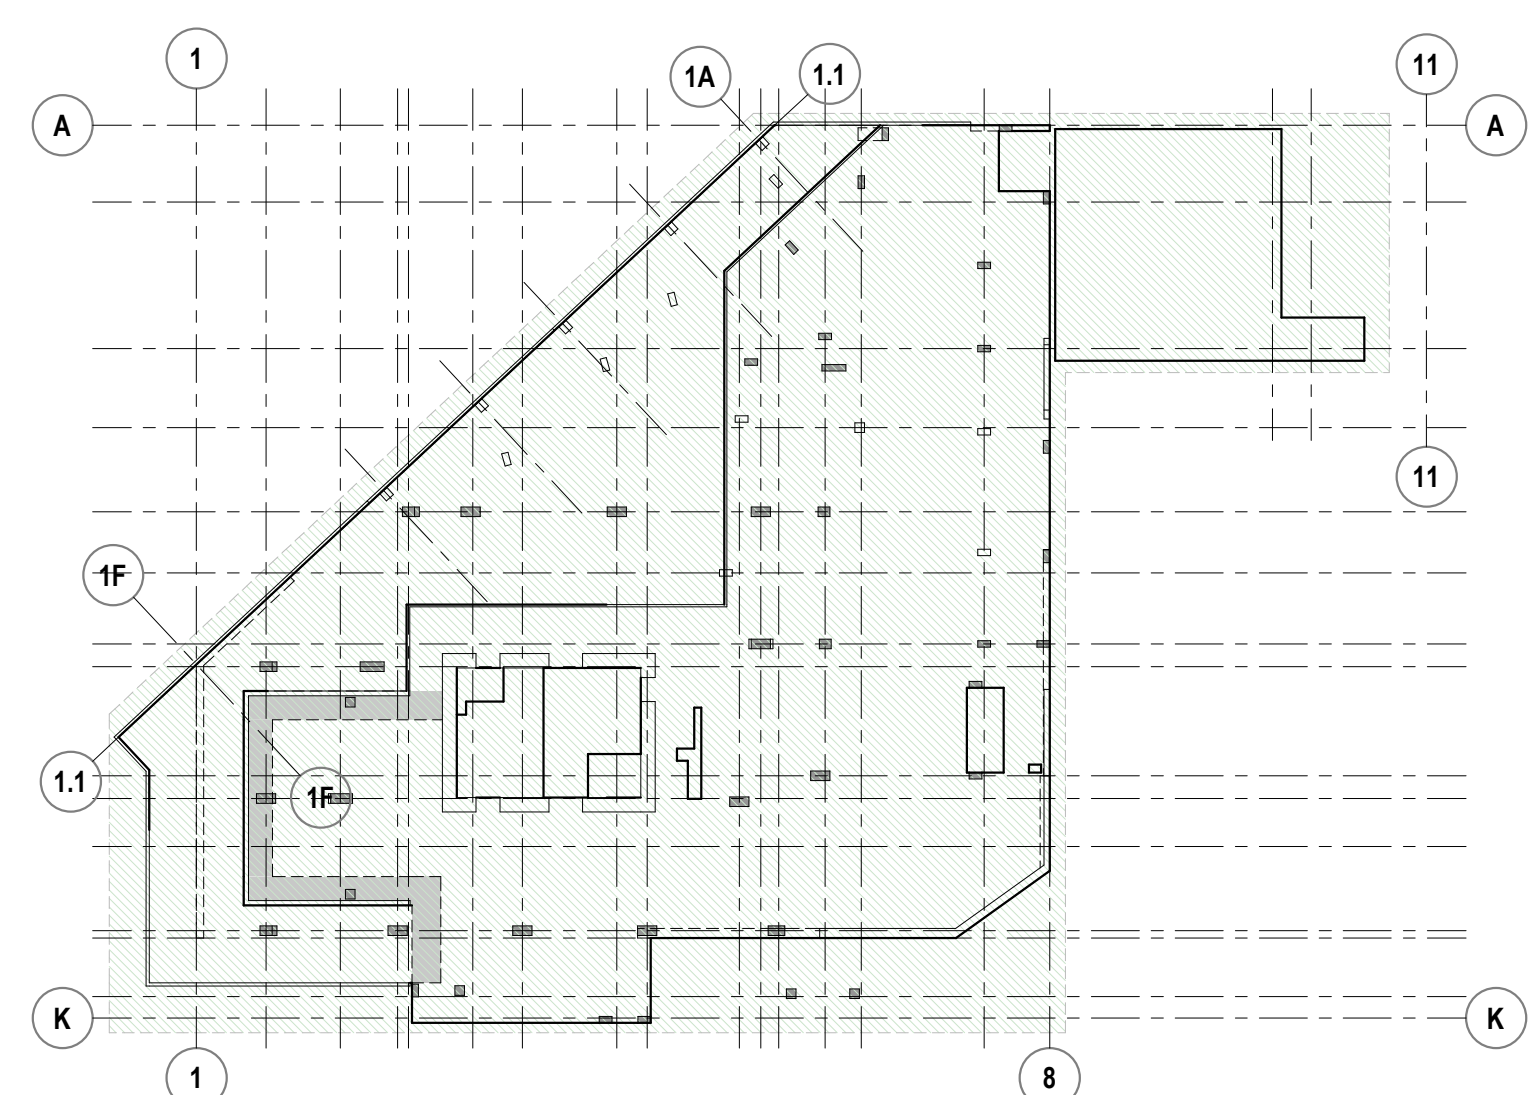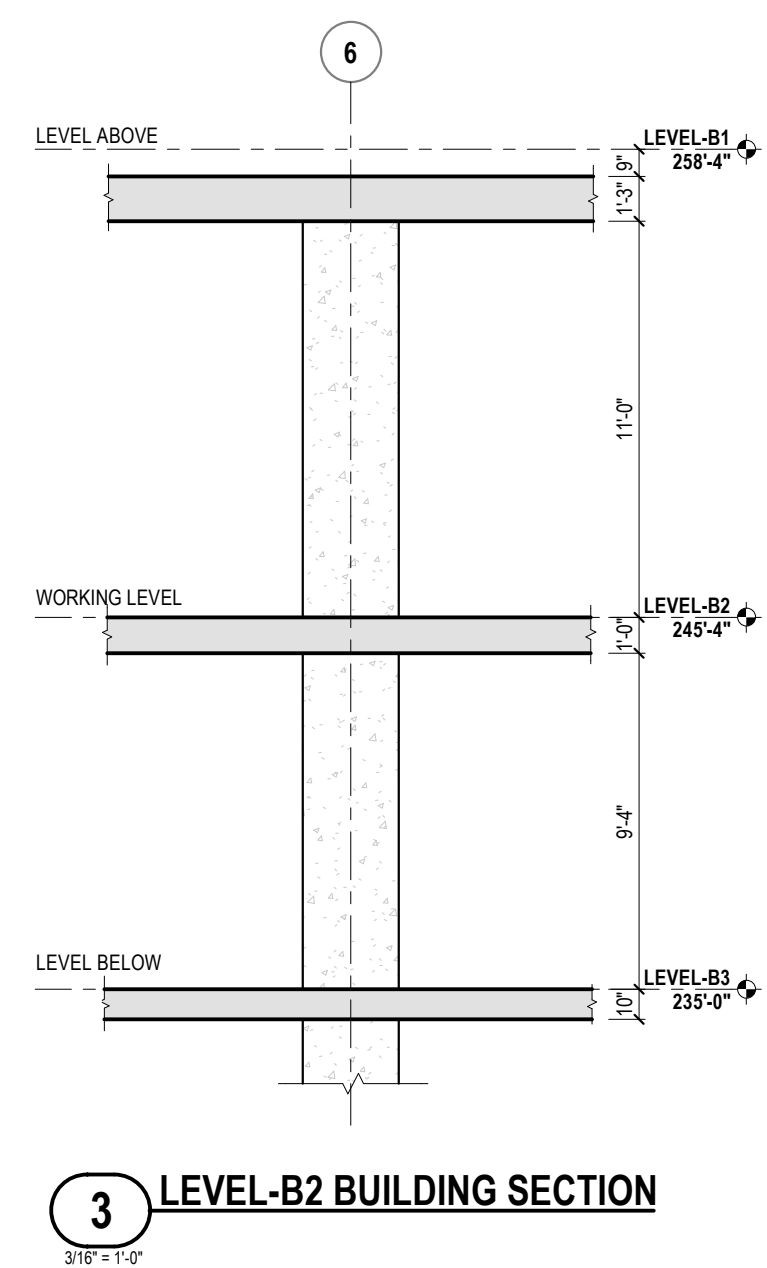

LEVEL-B2 KEY PLAN

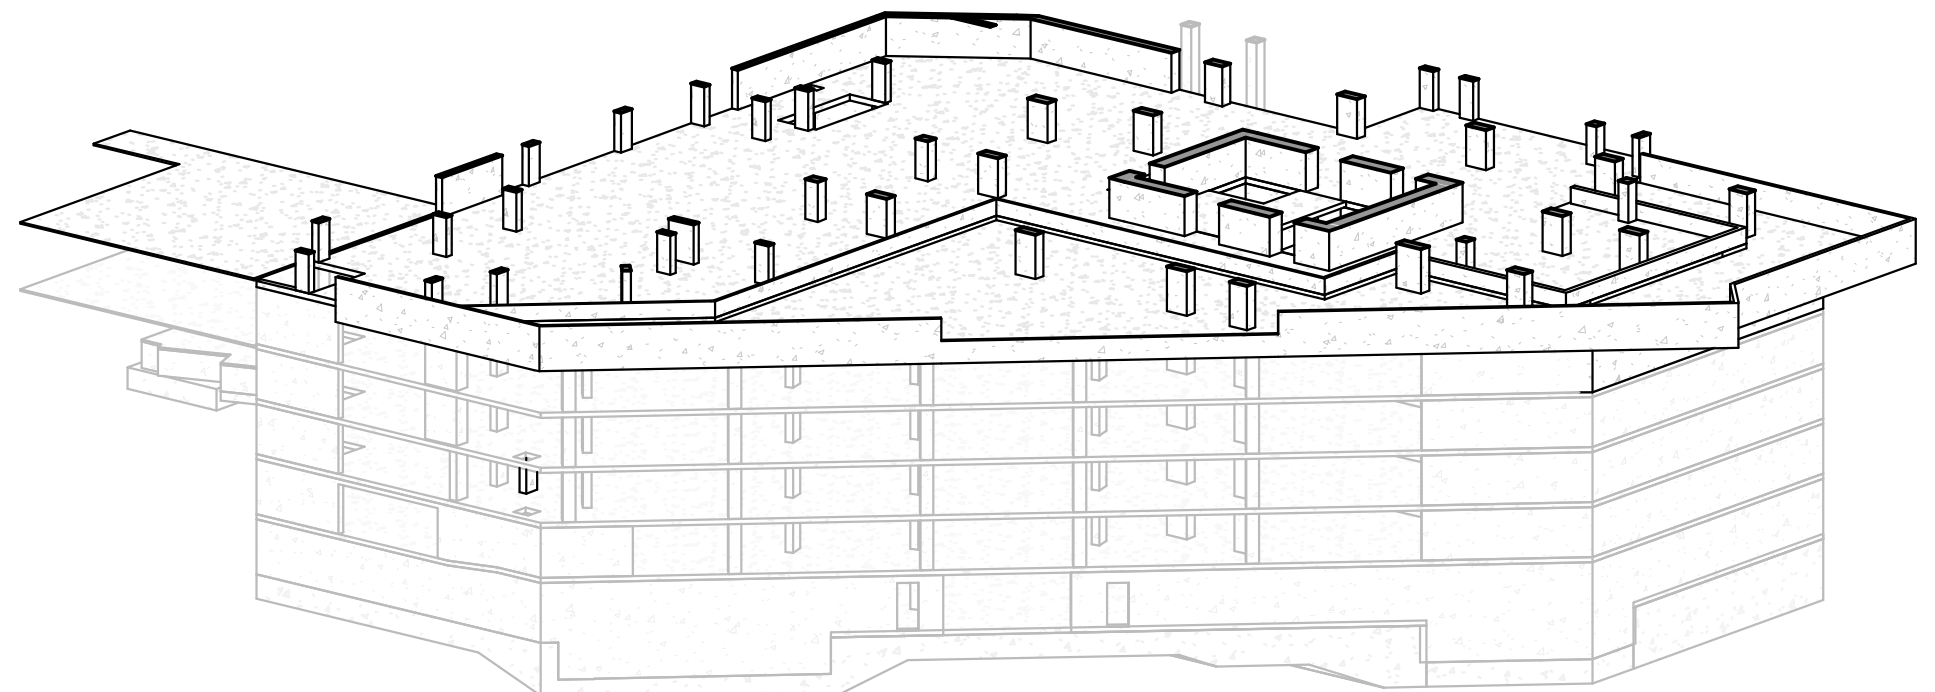



3D VIEW- LEVEL B2

NOTES:

1. 3/4" CHAMFER ON ALL EXPOSED CONCRETE CORNERS TYP.
2. ALL COLUMNS ARE CENTERED ON GRID LINES U.N.O.
3. ALL BEAMS ARE CENTERED ON GRID LINES U.N.O.
4. SLAB THICKNESS IS 12" MILD-REINFORCED TYP. U.N.O.

LEGEND

SYMBOLS		SHAPE DESIGNATIONS	
1-BOX (ROUND ENDS)		FOOTINGS OR FOUNDATIONS	
TOP OF CONCRETE ELEVATIONS		WALLS OR COLUMNS	
1-BOX (BOTTOM OF CONCRETE ELEVATIONS)		CNU WALLS	
2-BOX (PLAN VIEWS)		DELAY STRIP OR CLOSURE POUR	
TOP & BOTTOM ELEVATIONS		GRADE OR SOIL	
0-DEPTH OF CONC MEMBER			
3-BOX (FLOOR PLANS)			
TOP & BOTTOM ELEVATIONS			
COLUMN ELEVATIONS ABOVE & BELOW LEVEL			
0-DEPTH OF CONC MEMBER			
SECTION VIEW		LINE DESIGNATIONS	
Ref	DETAIL NUMBER	INDICATES TOP OF FTG CHANGE OR EDGE OF FTG	
Sheet Number	DETAIL NUMBER	INDICATES BOTTOM OF FTG CHANGE	
ELEVATION VIEW	DETAIL NUMBER	-CJ- INDICATES CONSTRUCTION JOINT	
Sheet Number	DETAIL NUMBER	INDICATES GRID LINE	

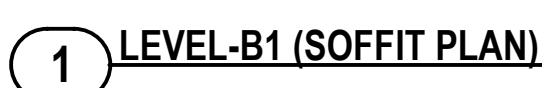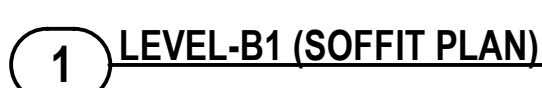

NOTES:

1. 3/4" CHAMFER ON ALL EXPOSED CONCRETE CORNERS TYP.
2. ALL COLUMNS ARE CENTERED ON GRID LINES U.N.O.
3. ALL BEAMS ARE CENTERED ON GRID LINES U.N.O.
4. SLAB THICKNESS IS 12" MILD-REINFORCED TYP. U.N.O.

LEGEND

SHADE DESIGNATIONS

	FOOTINGS OR FOUNDATIONS	
	WALLS OR COLUMNS	
	CMU WALLS	
	DELAY STRIP OR CLOSURE POUR	
	GRADE OR SOIL	

LINE DESIGNATIONS

_____ INDICATES TOP OF FTG CHANGE OR EDGE OF F
 - - - - - INDICATES BOTTOM OF FTG CHANGE
 --CJ--CJ-- INDICATES CONSTRUCTION JOINT
 _____ INDICATES GRID LINE

SYMBOLS

1-BOX (ROUND-ENDS)
TOP OF CONCRETE ELEVATIONS

1-BOX
BOTTOM OF CONCRETE ELEVATIONS

2-BOX (PLAN VIEWS)
TOP & BOTTOM ELEVATIONS
D = DEPTH OF CONC. MEMBER

3-BOX (FLOOR PLANS)
TOP & BOTTOM ELEVATIONS
COLUMN ELEVATION ABOVE REF. LEVEL
D = DEPTH OF CONC. MEMBER

SECTION VIEW

SHEET NUMBER _____ 

ELEVATION VIEW

SHEET NUMBER _____ 