


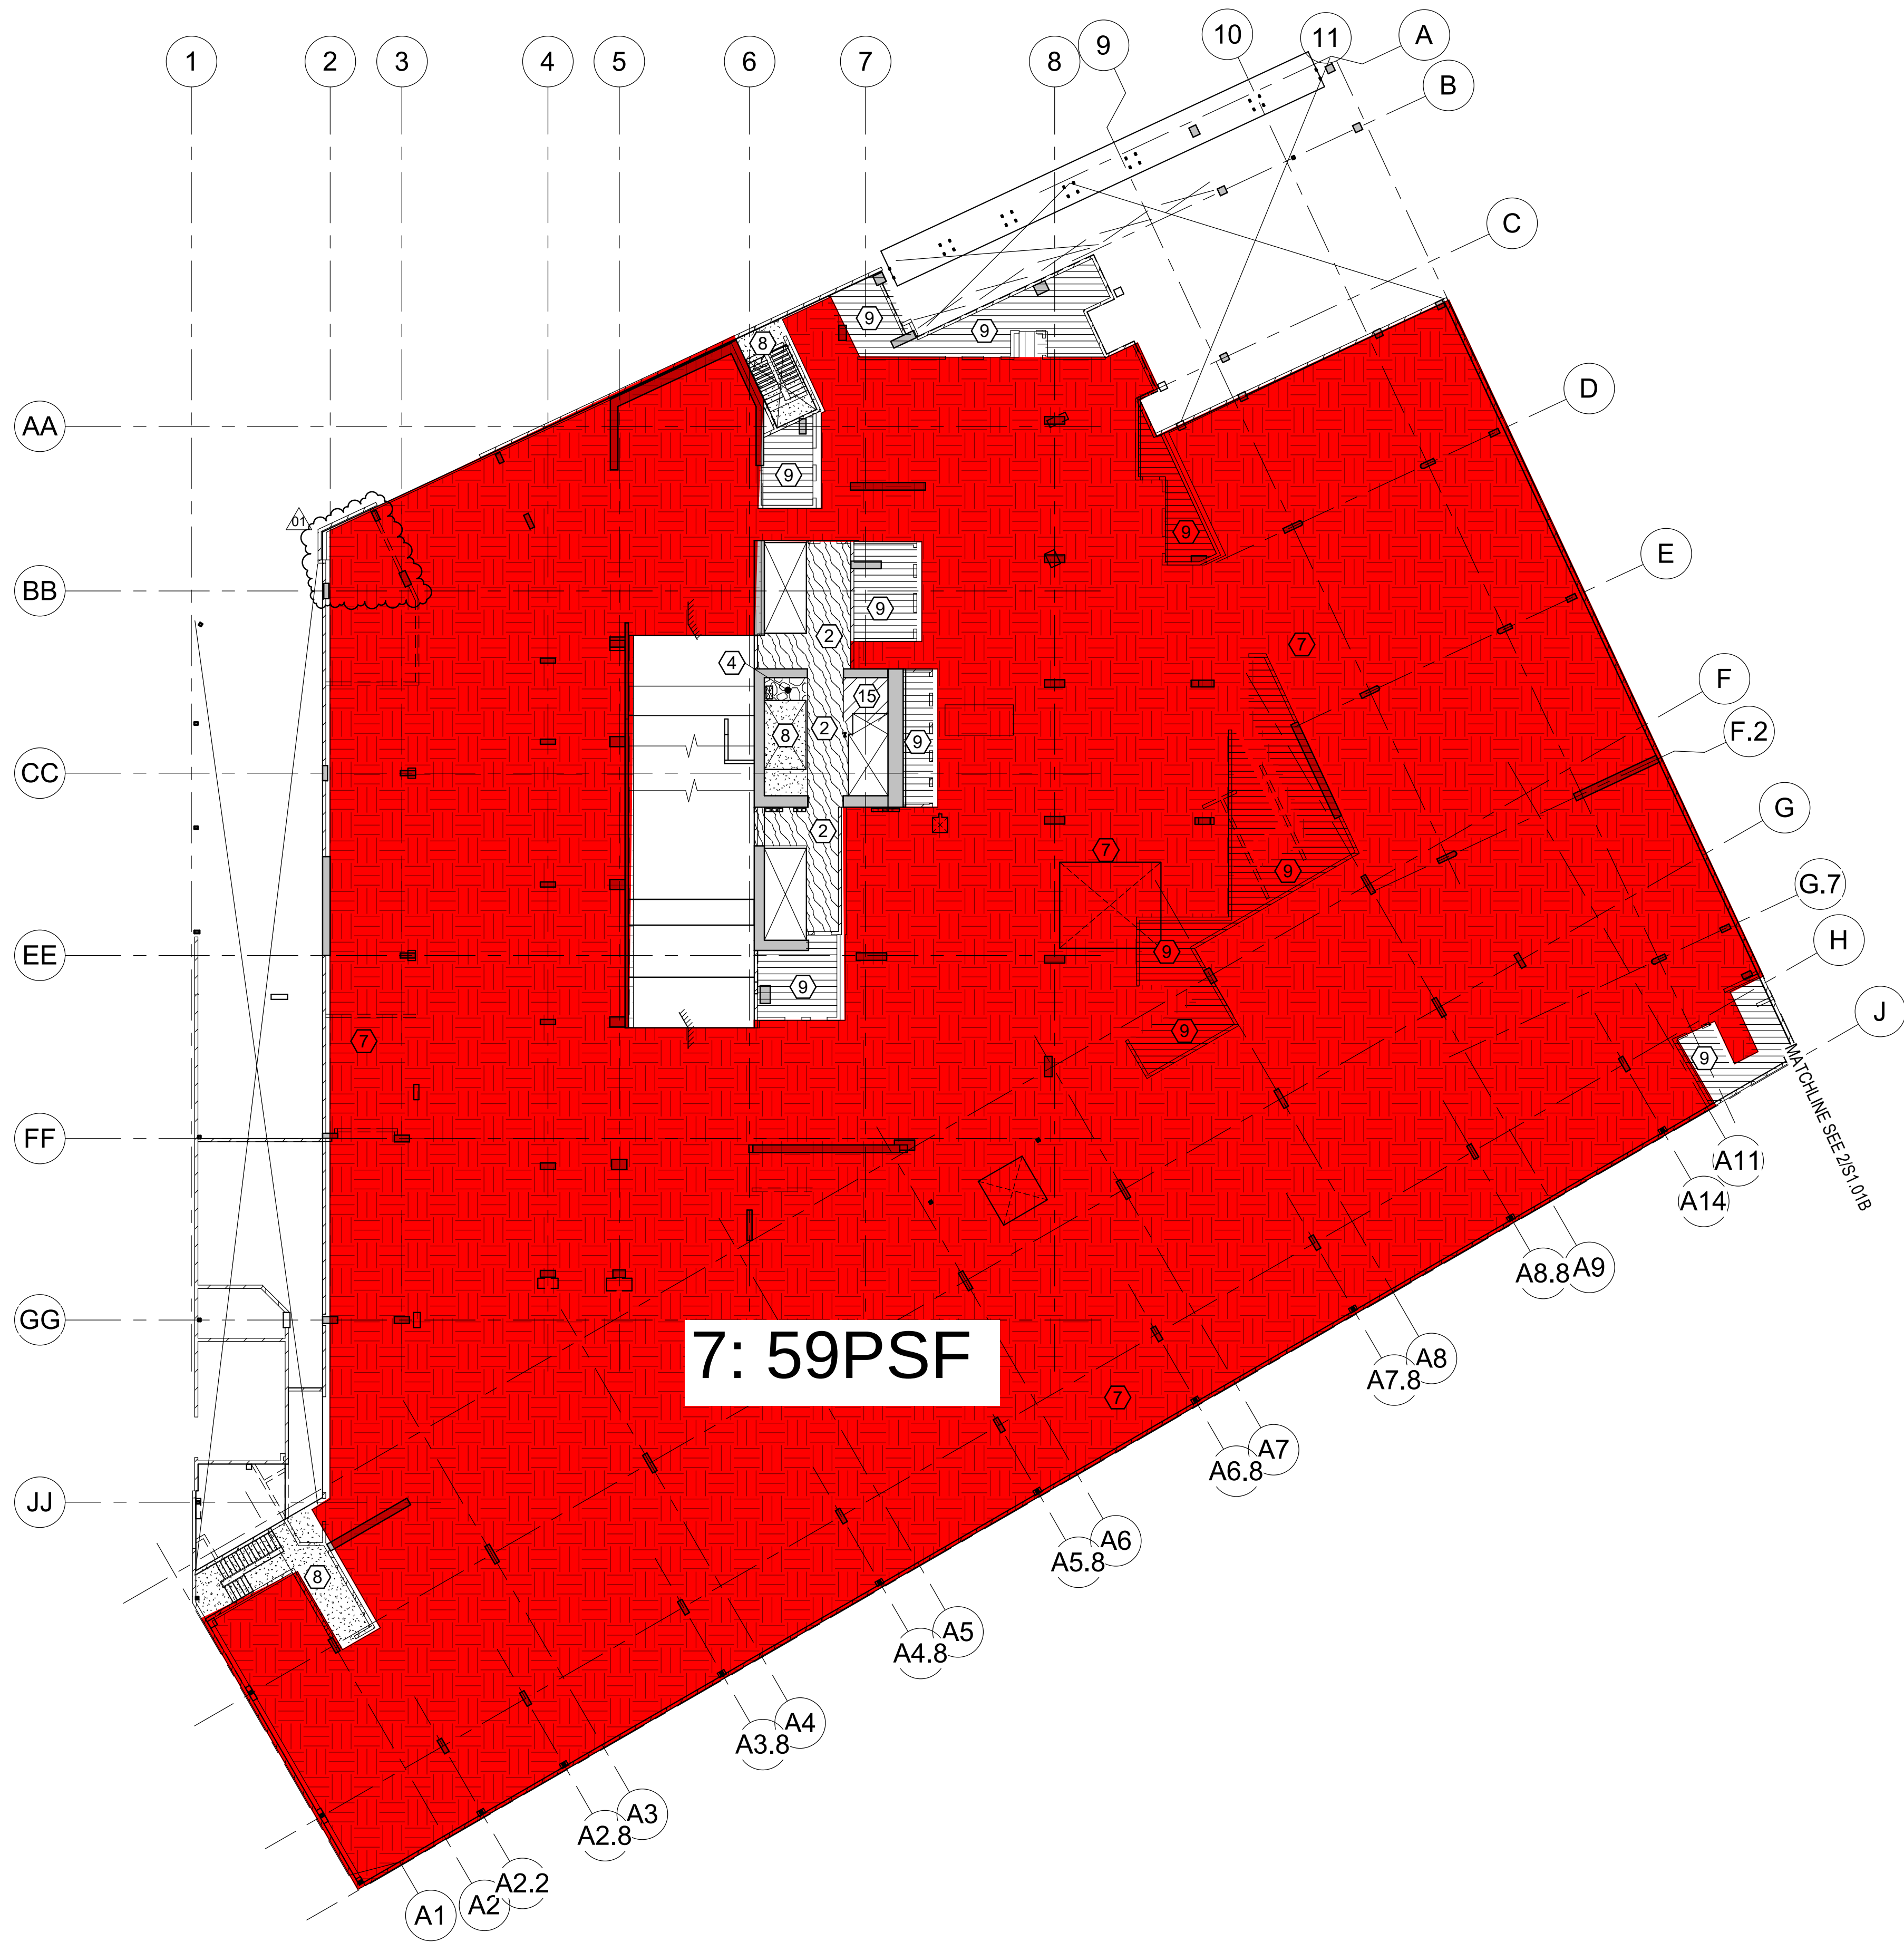

1 LEVEL 2 LOAD DIAGRAM
SCALE: 1" = 20'-0"



2 LEVEL 3 LOAD DIAGRAM
SCALE: 1" = 20'-0"

LOADING MAP											
MARK	DESCRIPTION	SDL (PSF)	LL (PSF)	CONCENTRATED LOAD (LBS)	MARK	DESCRIPTION	SDL (PSF)	LL (PSF)	CONCENTRATED LOAD (LBS)		
①	CORRIDOR (RESI)	25	40		⑩	INDOOR/OUTDOOR AMENITY	25	100			
②	LOBBY	15	100		⑪	ROOF	10	20			
③	PLANTER (NON-ACCESSIBLE)	150	20		⑫	OFFICE	15	50			
④	MECHANICAL	10	150		⑬	LOADING DOCK	5	150			
⑤	RESIDENTIAL	25	40		⑭	1' DEEP PLANTING SOIL	110	100			
⑥	TRASH	15	100		⑮	2' DEEP PLANTING SOIL	220	100			
⑦	PARKING	10	40		⑯	4' DEEP TREE/PALM PLANTING PIT	440	100			
⑧	STAIR	5	100	300	⑰	STONE PAVERS	130	100			
⑨	LIGHT STORAGE	10	125		⑱	SPA/TREATMENT ROOM	175	60			
⑩	FITNESS CENTER	25	100		⑲	SPA / FAMILY POOL	300	60			
⑪	POOL	340	60		⑳	TREE-TR1	-	-	2600		
⑫	ELEVATOR MACHINE RM	10	125		㉑	TREE-TR2	-	-	3000		
⑬	PUMP ROOM	15	100		㉒	TREE-TR3	-	-	3500		
⑭	ELECTRIC	10	100		㉓	TREE-TR4 - MISC	-	-	1000		
⑮					㉔	RETAIL	25	100			
⑯					㉕	BATHROOM	25	60			

- LOAD MAP NOTES:
- SUPERIMPOSED LOADS INDICATED ARE IN ADDITION TO SELF-WEIGHT OF STRUCTURE.
 - WHERE APPLICABLE, LIVE LOADS HAVE BEEN REDUCED BELOW THE TABULATED VALUES PER THE BUILDING CODE.
 - CLADDING LOADS:
15 PSF OVER WALL AREA (EXTERIOR GLAZING)
5 PSF FOR MECHANICAL SCREEN & LOUVERS

BALDRIDGE & ASSOCIATES
STRUCTURAL
ENGINEERING
1164 Bishop Street, Suite 1900
Honolulu, HI 96813
Phone: 808.534.1300 | Email: info@baseeng.com

HALEKANA PERMITS
THIRD PARTY CERTIFICATION
☐ BUILDING CODE ☐ ELECTRICAL CODE
☐ MECHANICAL CODE ☐ RESIDENTIAL CODE
☐ STRUCTURAL (NON-SHALED STORY OVERLAYS)



Digitally signed by Steven M. Baldrige
Date: 2024.06.22 22:43:07-1000
April 30, 2026

FOR BALDRIDGE & ASSOCIATES STRUCTURAL ENGINEERING, INC.
THIS WORK WAS PREPARED BY ME OR UNDER MY SUPERVISION AND CONSTRUCTION OF THIS PROJECT WILL BE UNDER MY OBSERVATION

S1	11.17.2023	SUPERSTRUCTURE PERMIT R1
B1	11.17.2023	BUILDING PERMIT R1
F1	11.17.2023	FOUNDATION PERMIT R1
3	08.30.2024	ADDENDUM 03
F5	05.31.2024	FOUNDATION PERMIT R5
F2	02.29.2024	FOUNDATION PERMIT R2
S2	02.27.2024	SUPERSTRUCTURE PERMIT R2
1	11.17.2023	ADDENDUM 01
F1	11.17.2023	FOUNDATION PERMIT R1
B1	11.17.2023	BUILDING PERMIT R1
S1	11.17.2023	SUPERSTRUCTURE PERMIT R1
NO.	DATE	DESCRIPTION

SCB
Solomon Cordwell Buenz
Chicago
T 312.896.1100
San Francisco
T 415.216.2450
www.scb.com


KALAE BUILDING PERMIT


TMK: (1) 2-3-001: 133
1000 ALA MOANA BLVD.
HONOLULU, HI 96814

© 2023 Solomon Cordwell Buenz

LOADING DIAGRAMS

SCALE: As indicated
Drawn By: DJ
Checked By: MH
Project Number: 2018032
Sheet Number: S0.06

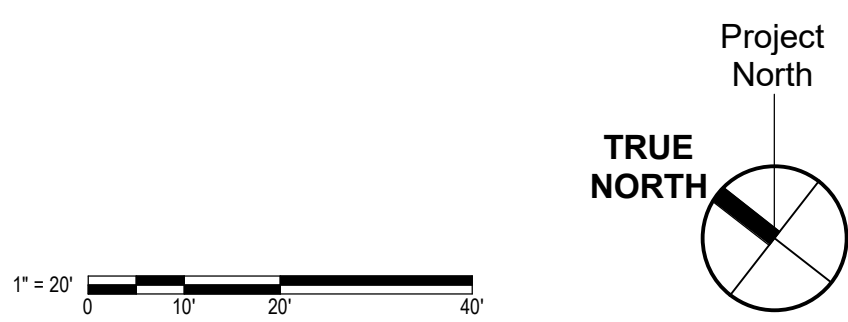

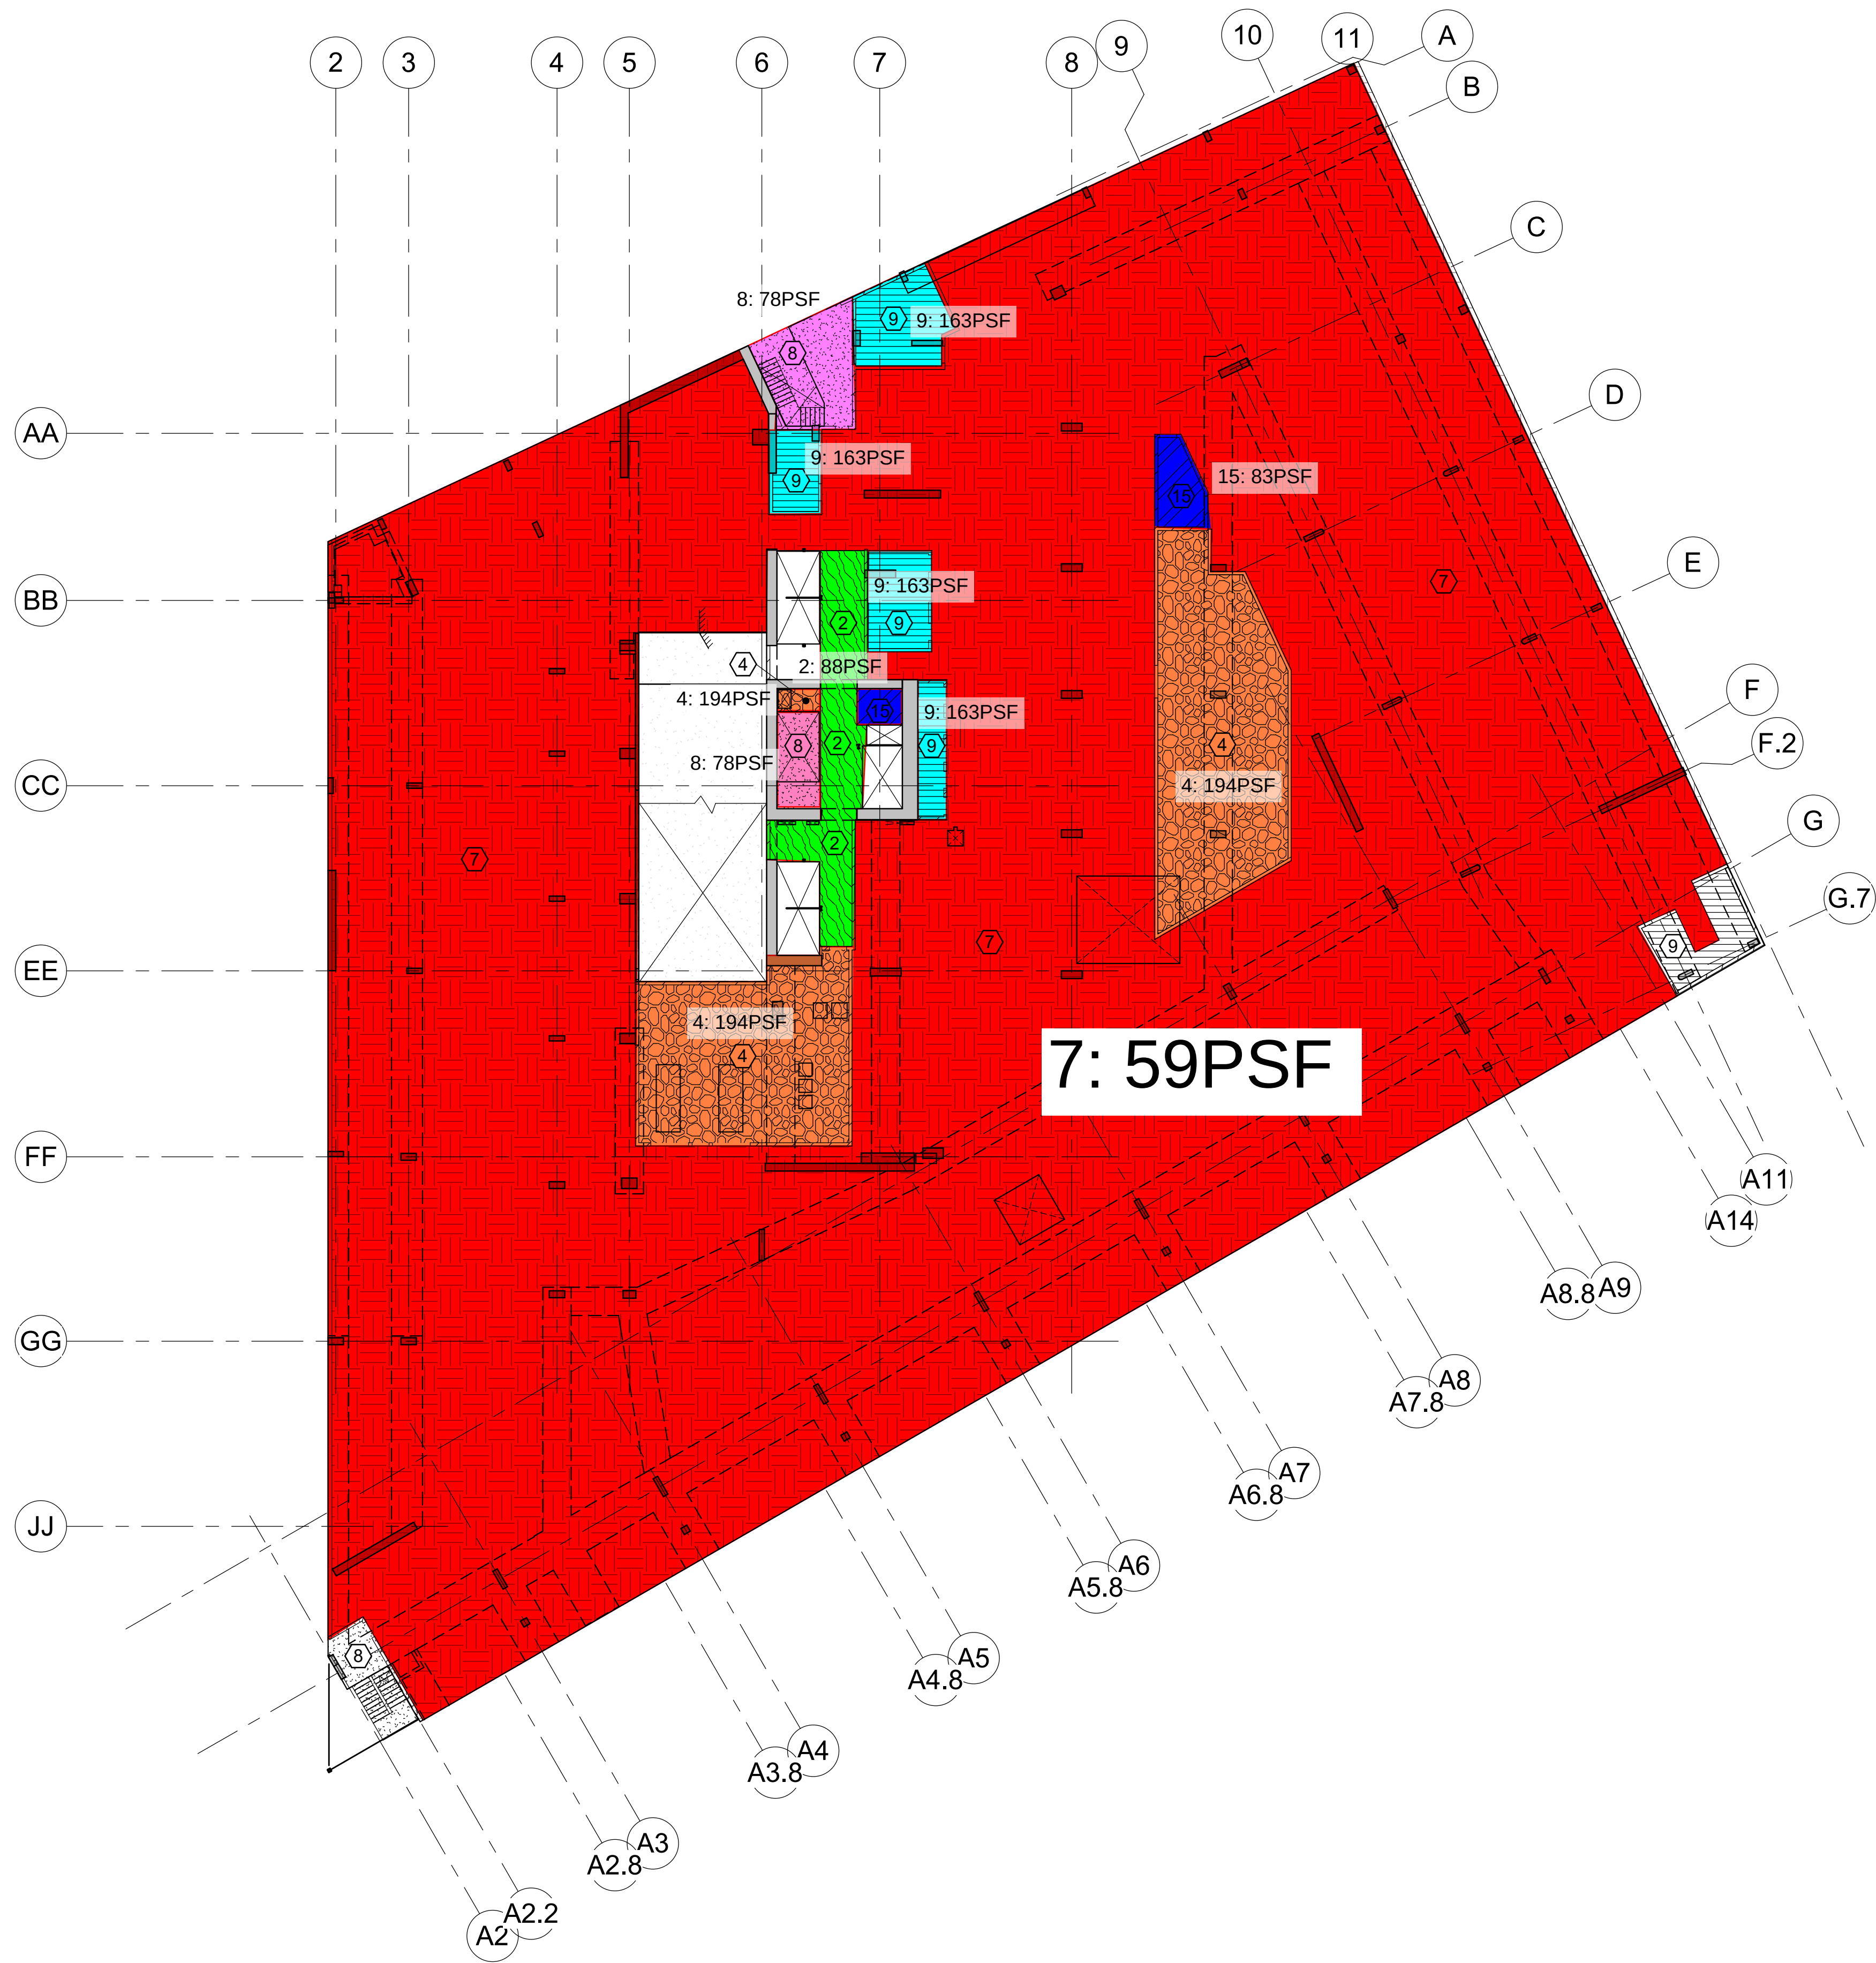

1 LEVEL 4 LOAD DIAGRAM
SCALE: 1" = 20'-0"



2 LEVEL 5 LOAD DIAGRAM
SCALE: 1" = 20'-0"

LOADING MAP											
MARK	DESCRIPTION	SDL (PSF)	LL (PSF)	CONCENTRATED LOAD (LBS)	MARK	DESCRIPTION	SDL (PSF)	LL (PSF)	CONCENTRATED LOAD (LBS)		
1	CORRIDOR (RESI)	25	40		16	INDOOR/OUTDOOR AMENITY	25	100			
2	LOBBY	15	100		17	ROOF	10	20			
3	PLANTER (NON-ACCESSIBLE)	150	20		18	OFFICE	15	50			
4	MECHANICAL	10	150		19	LOADING DOCK	5	150			
5	RESIDENTIAL	25	40		20	1' DEEP PLANTING SOIL	110	100			
6	TRASH	15	100		21	2' DEEP PLANTING SOIL	220	100			
7	PARKING	10	40		22	4' DEEP TREE/PALM PLANTING PIT	440	100			
8	STAIR	5	100	300	23	STONE PAVERS	130	100			
9	LIGHT STORAGE	10	125		24	SPA/TREATMENT ROOM	175	60			
10	FITNESS CENTER	25	100		25	SPA / FAMILY POOL	300	60			
11	WATER STORAGE TANK	15	1700		26						
12	POOL	340	50		27	TREE-TR1	-	-	2600		
13	ELEVATOR MACHINE RM	10	125		28	TREE-TR2	-	-	3000		
14	PUMP ROOM	15	100		29	TREE-TR3	-	-	3500		
15	ELECTRIC	10	100		30	TREE-TR4 - MISC	-	-	1000		
					31	RETAIL	25	100			
					32	BATHROOM	25	60			

- LOAD MAP NOTES:
- SUPERIMPOSED LOADS INDICATED ARE IN ADDITION TO SELF-WEIGHT OF STRUCTURE.
 - WHERE APPLICABLE, LIVE LOADS HAVE BEEN REDUCED BELOW THE TABULATED VALUES PER THE BUILDING CODE.
 - CLADDING LOADS:
15 PSF OVER WALL AREA (EXTERIOR GLAZING)
5 PSF FOR MECHANICAL SCREEN & LOUVERS

BALDRIDGE & ASSOCIATES
STRUCTURAL
ENGINEERING
1164 Bishop Street, Suite 1600
Honolulu, HI 96813
Phone: 808.534.1300 | Email: info@baseeng.com

PALEKANA PERMITS
THIRD PARTY CERTIFICATION
☐ BUILDING CODE ☐ ELECTRICAL CODE
☐ MECHANICAL CODE ☐ RESIDENTIAL CODE
☐ STRUCTURAL NON-SHALED STORY OVERLAP(S)

STEVEN M. BALDRIDGE
LICENSED PROFESSIONAL ENGINEER
No. 7874-S
HAWAII, U.S.A.
Digitally signed by Steven M. Baldridge
Date: 2024.06.22 22:43:07 -0500
April 30, 2026

FOR BALDRIDGE & ASSOCIATES STRUCTURAL ENGINEERING, INC.
THIS WORK WAS PREPARED BY ME OR UNDER MY SUPERVISION AND CONSTRUCTION OF THIS PROJECT WILL BE UNDER MY OBSERVATION

NO.	DATE	DESCRIPTION
3	08.30.2024	ADDENDUM 03
F5	05.31.2024	FOUNDATION PERMIT R5
F2	02.29.2024	FOUNDATION PERMIT R2
S2	02.27.2024	SUPERSTRUCTURE PERMIT R2
1	11.17.2023	ADDENDUM 01
F1	11.17.2023	FOUNDATION PERMIT R1
B1	11.17.2023	BUILDING PERMIT R1
S1	11.17.2023	SUPERSTRUCTURE PERMIT R1

SCB
Solomon Cordwell Buenz
Chicago
T 312.896.1100
San Francisco
T 415.216.2450
www.scb.com


KALAE BUILDING PERMIT


TMK: (1) 2-3-001: 133
1000 ALA MOANA BLVD.
HONOLULU, HI 96814

© 2023 Solomon Cordwell Buenz


LOADING DIAGRAMS

SCALE: As indicated
Drawn By: DJ
Checked By: MH
Project Number: 2018032
Sheet Number: S0.07

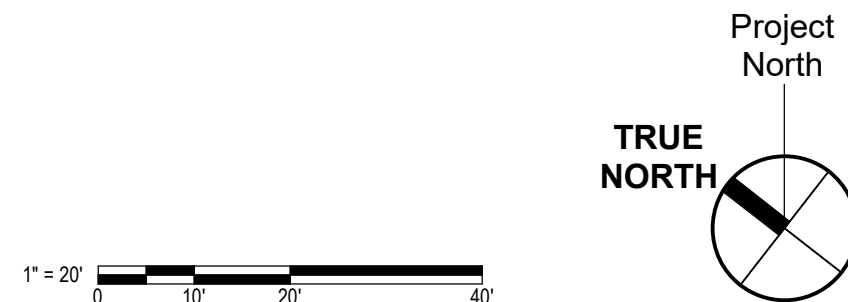


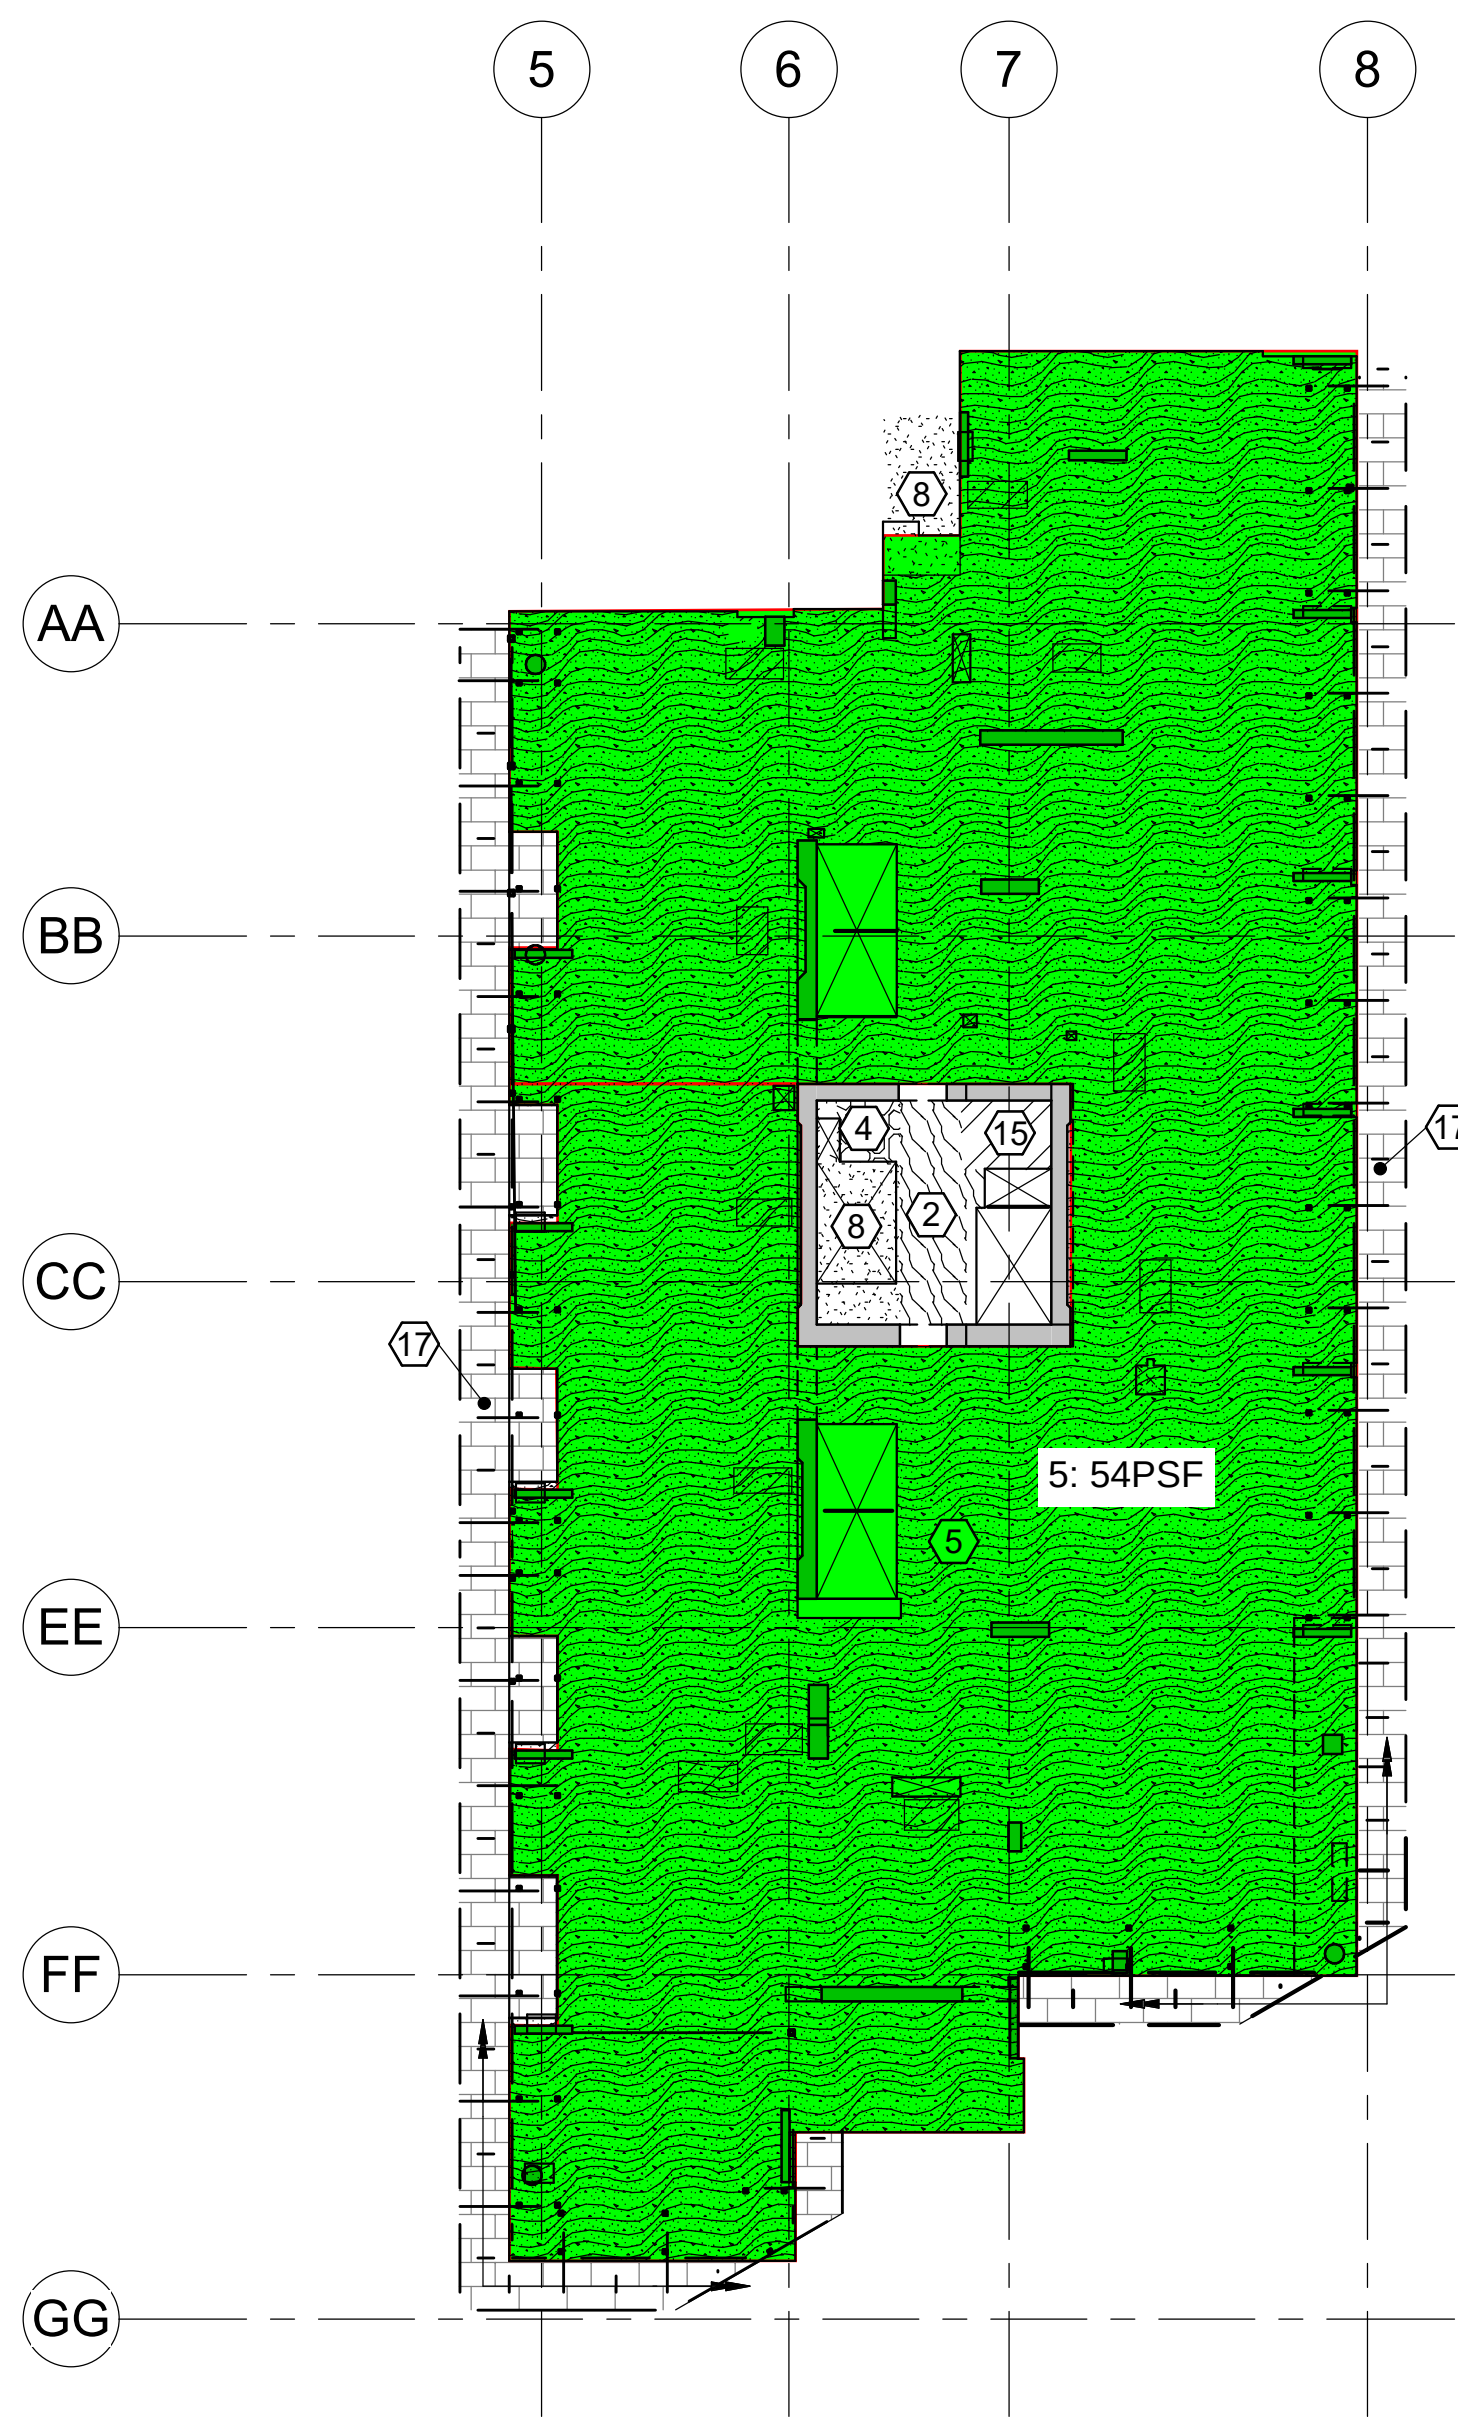


1 LEVEL 6 LOAD DIAGRAM
SCALE: 1" = 20'-0"

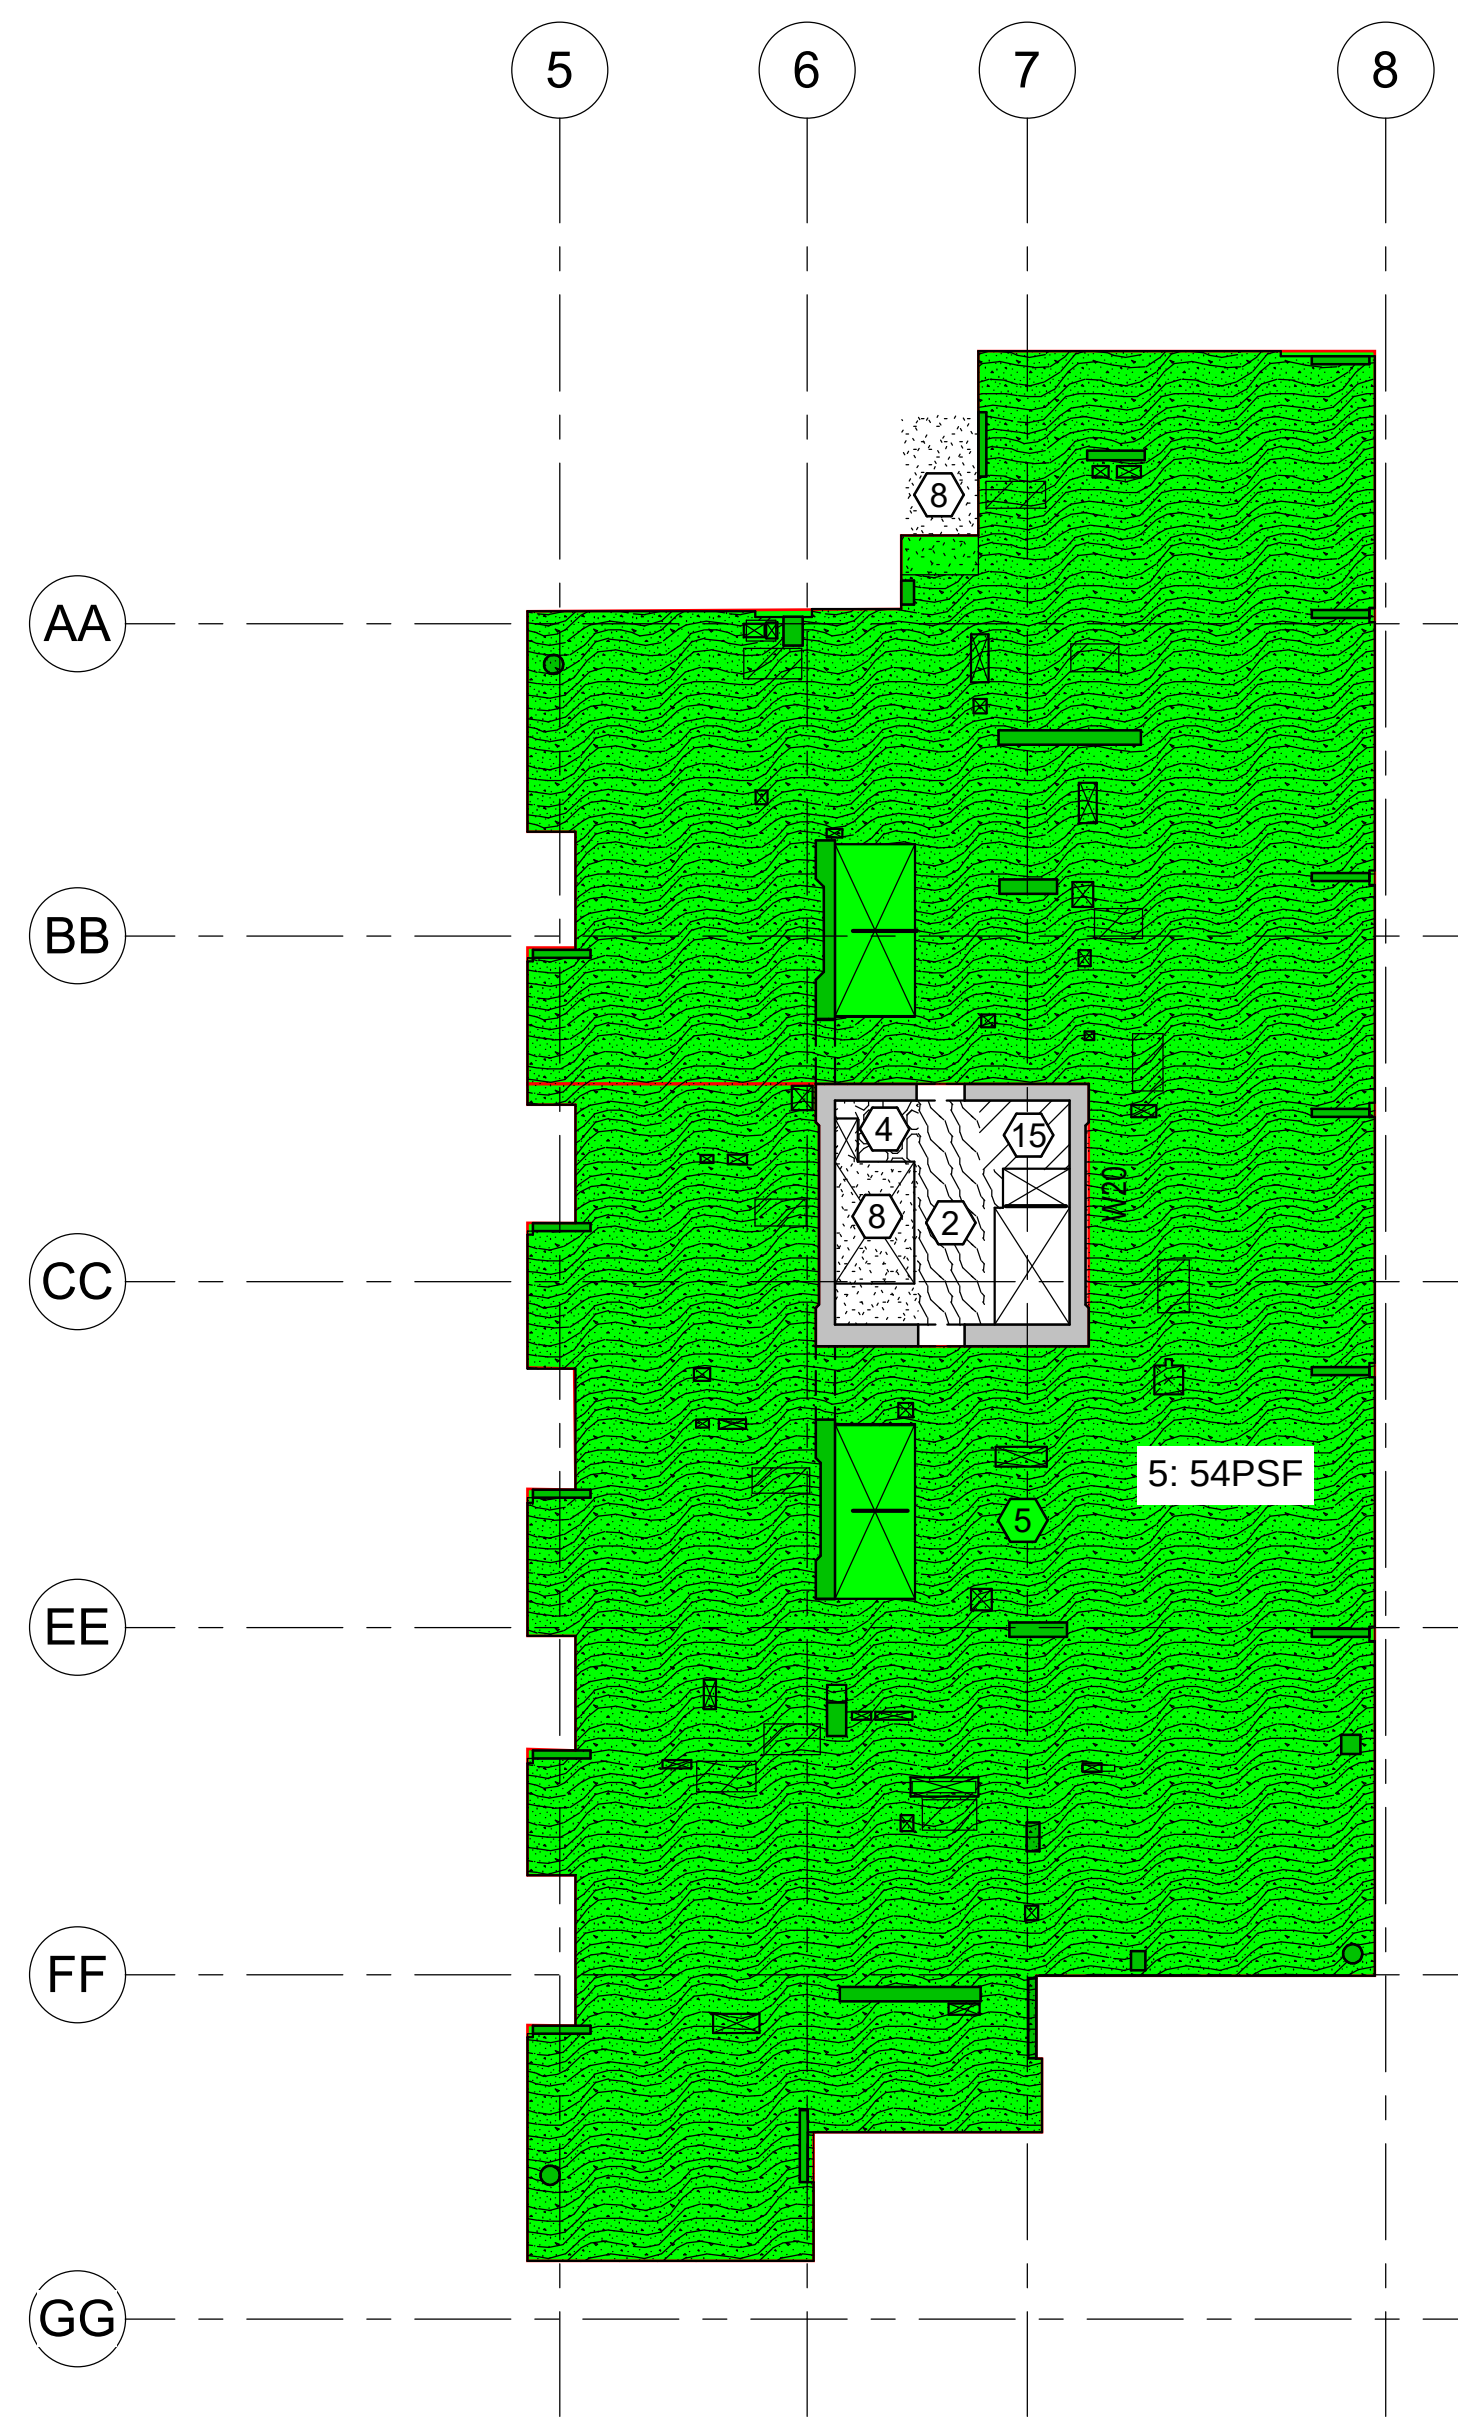


2 LEVEL 7-38 LOAD DIAGRAM
SCALE: 1" = 20'-0"

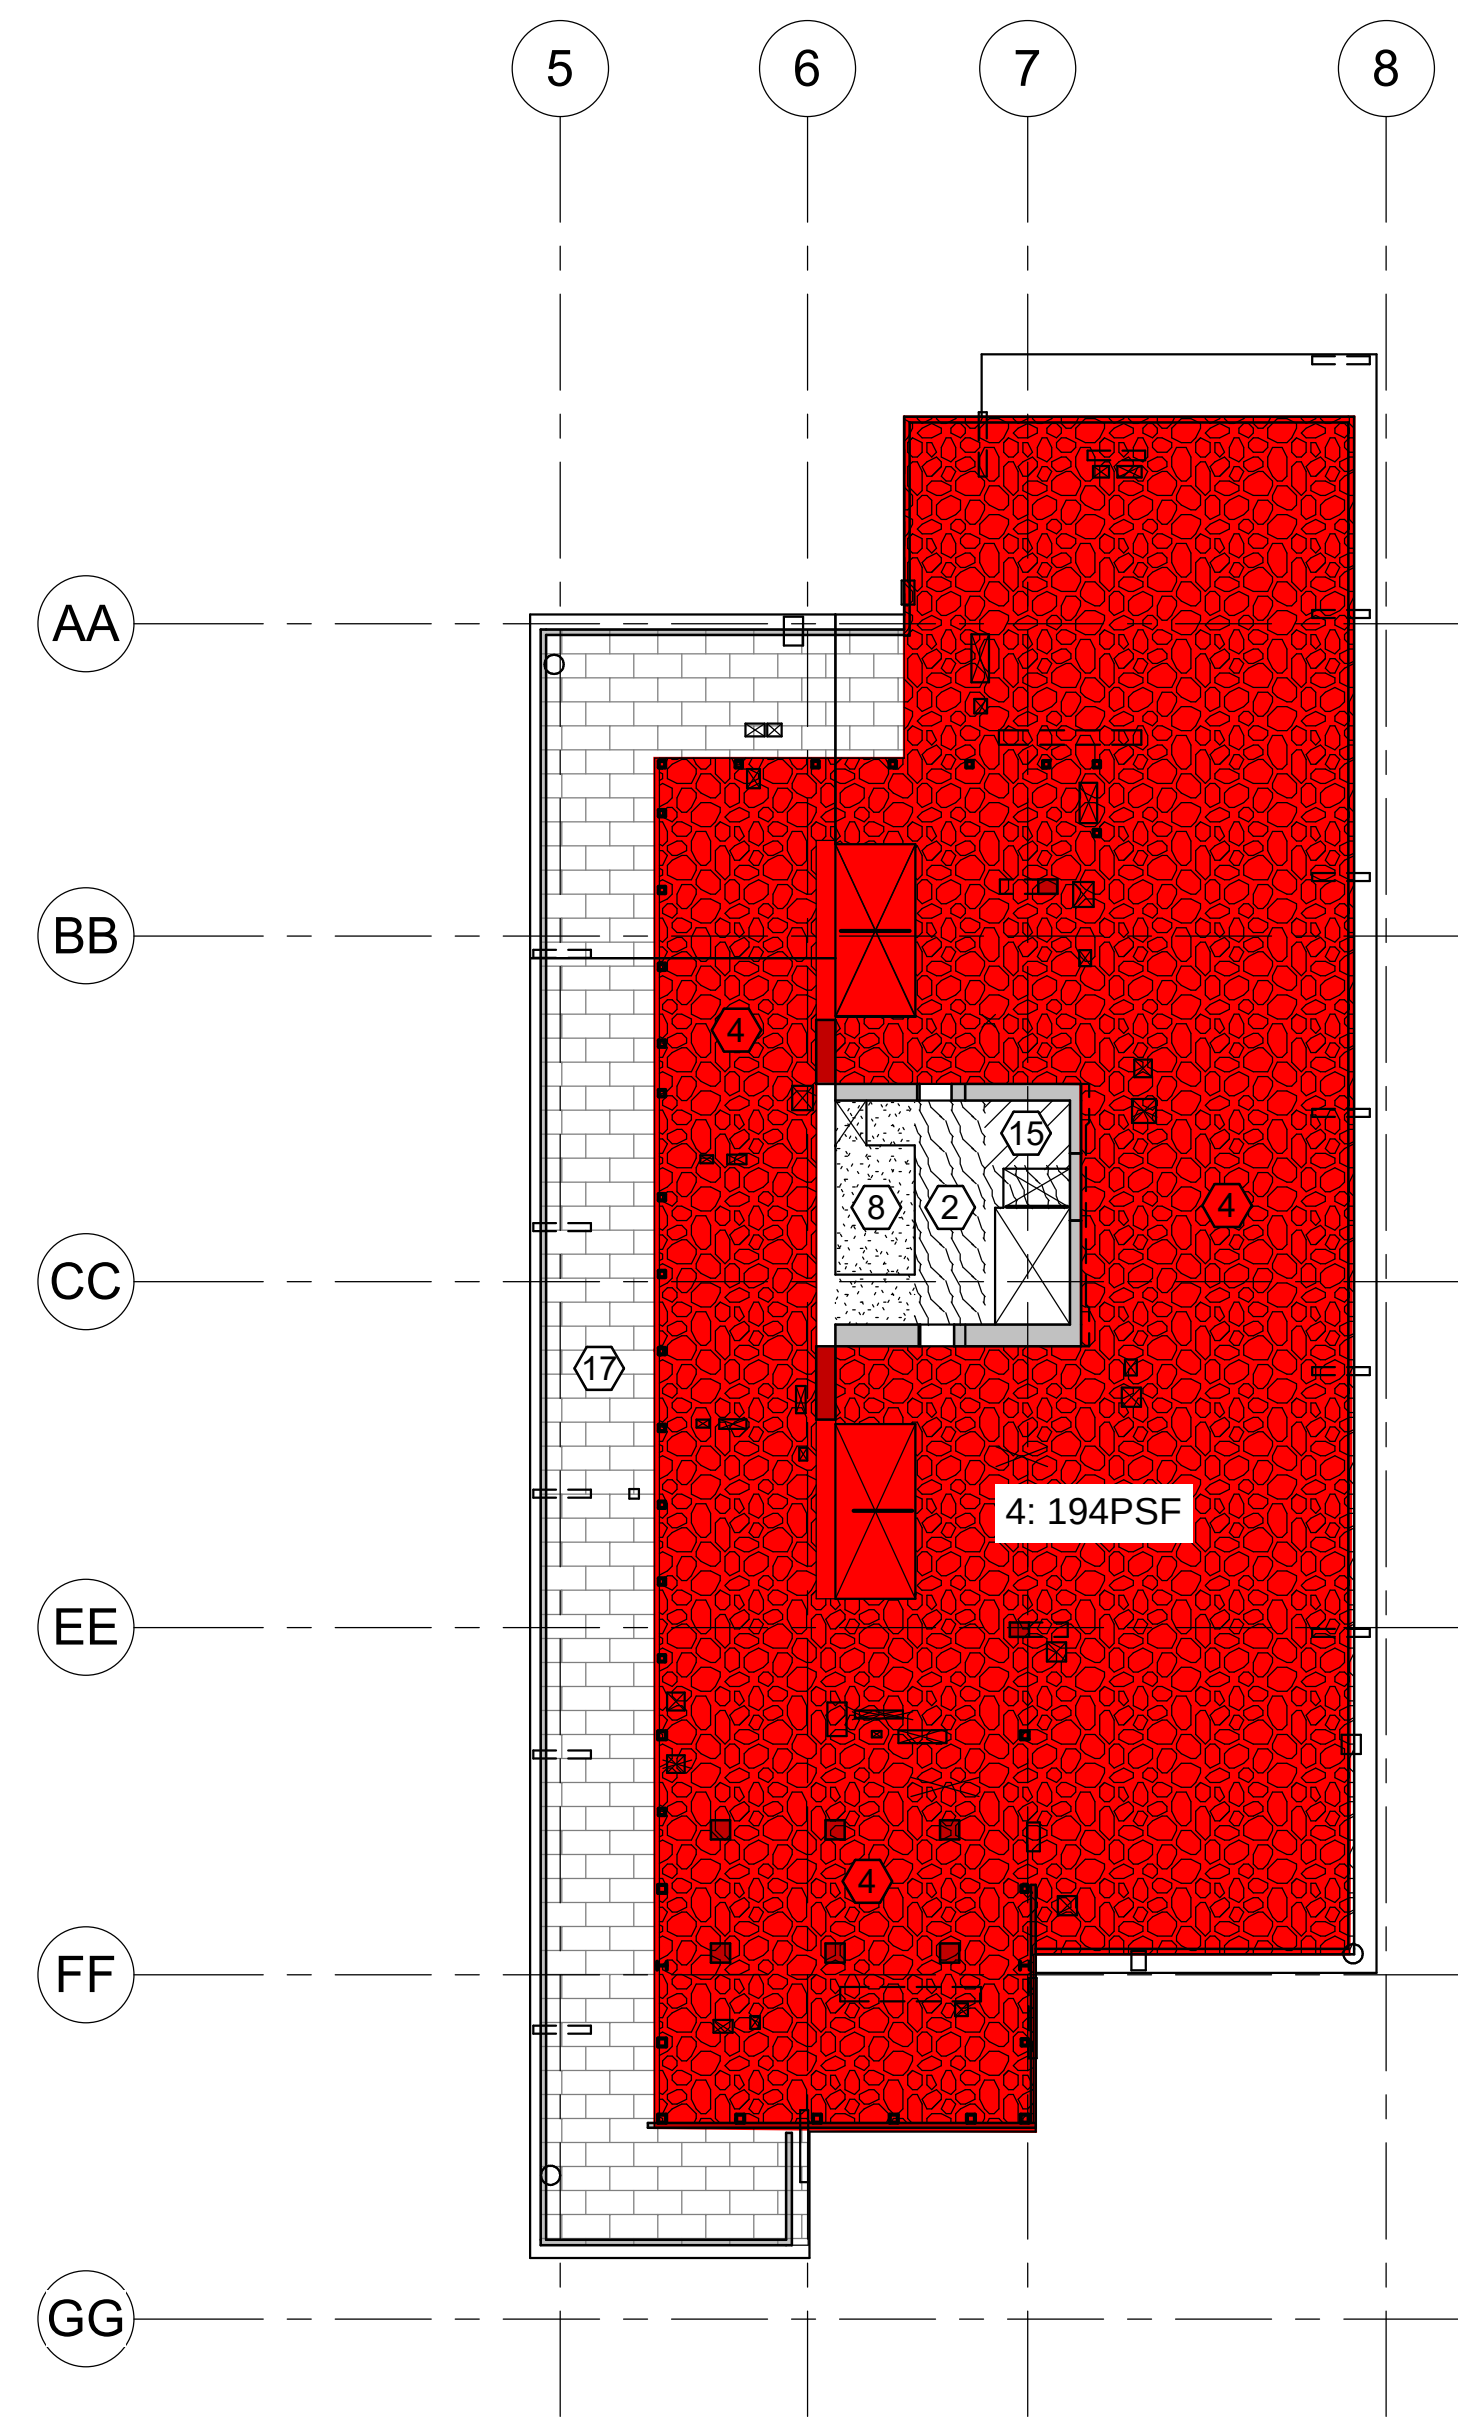

3 ROOF LOAD DIAGRAM
SCALE: 1" = 20'-0"

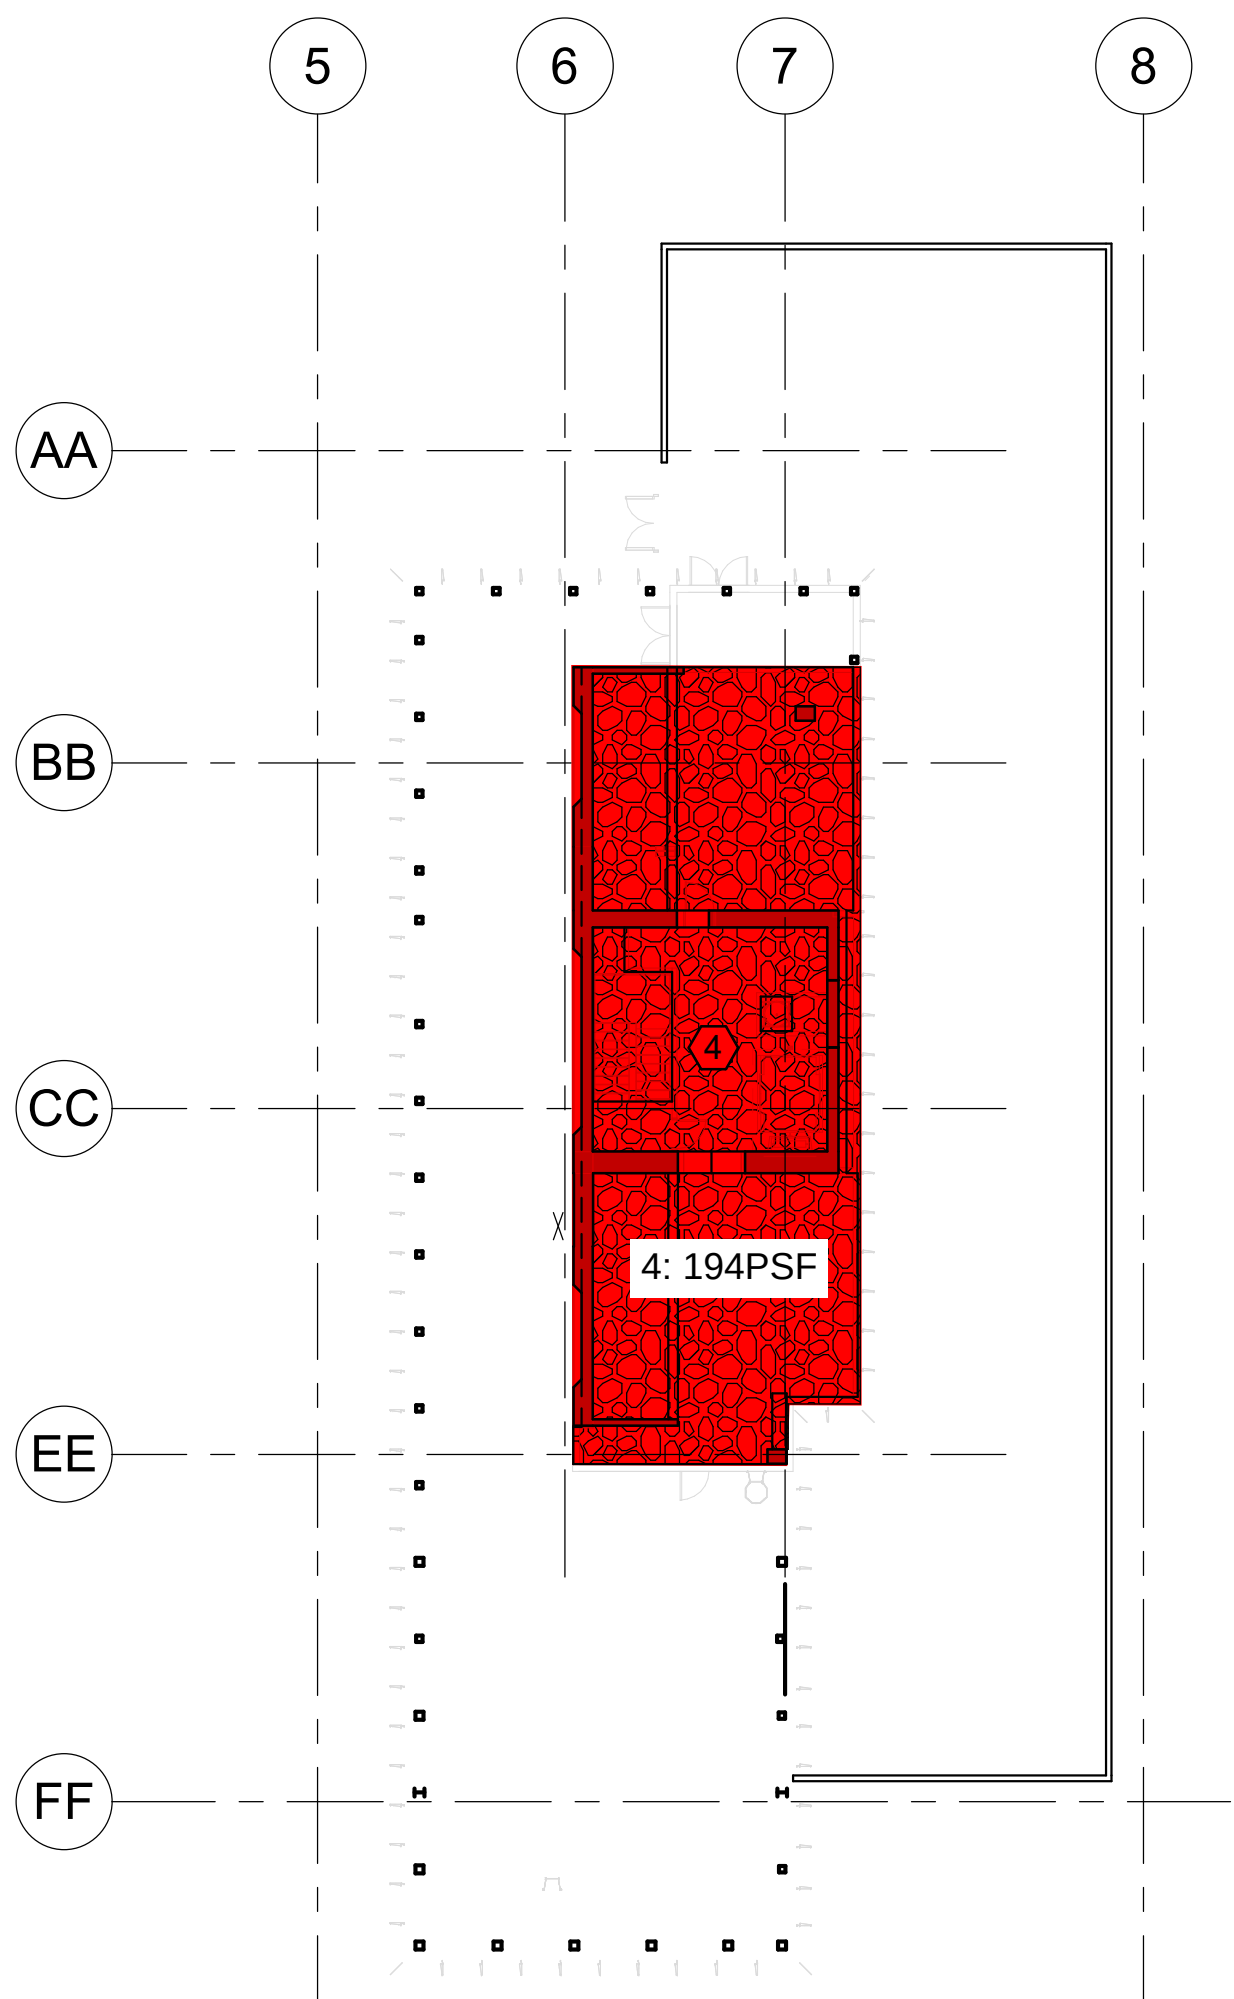

4 ELEV. MACH RM LOAD DIAGRAM
SCALE: 1" = 20'-0"

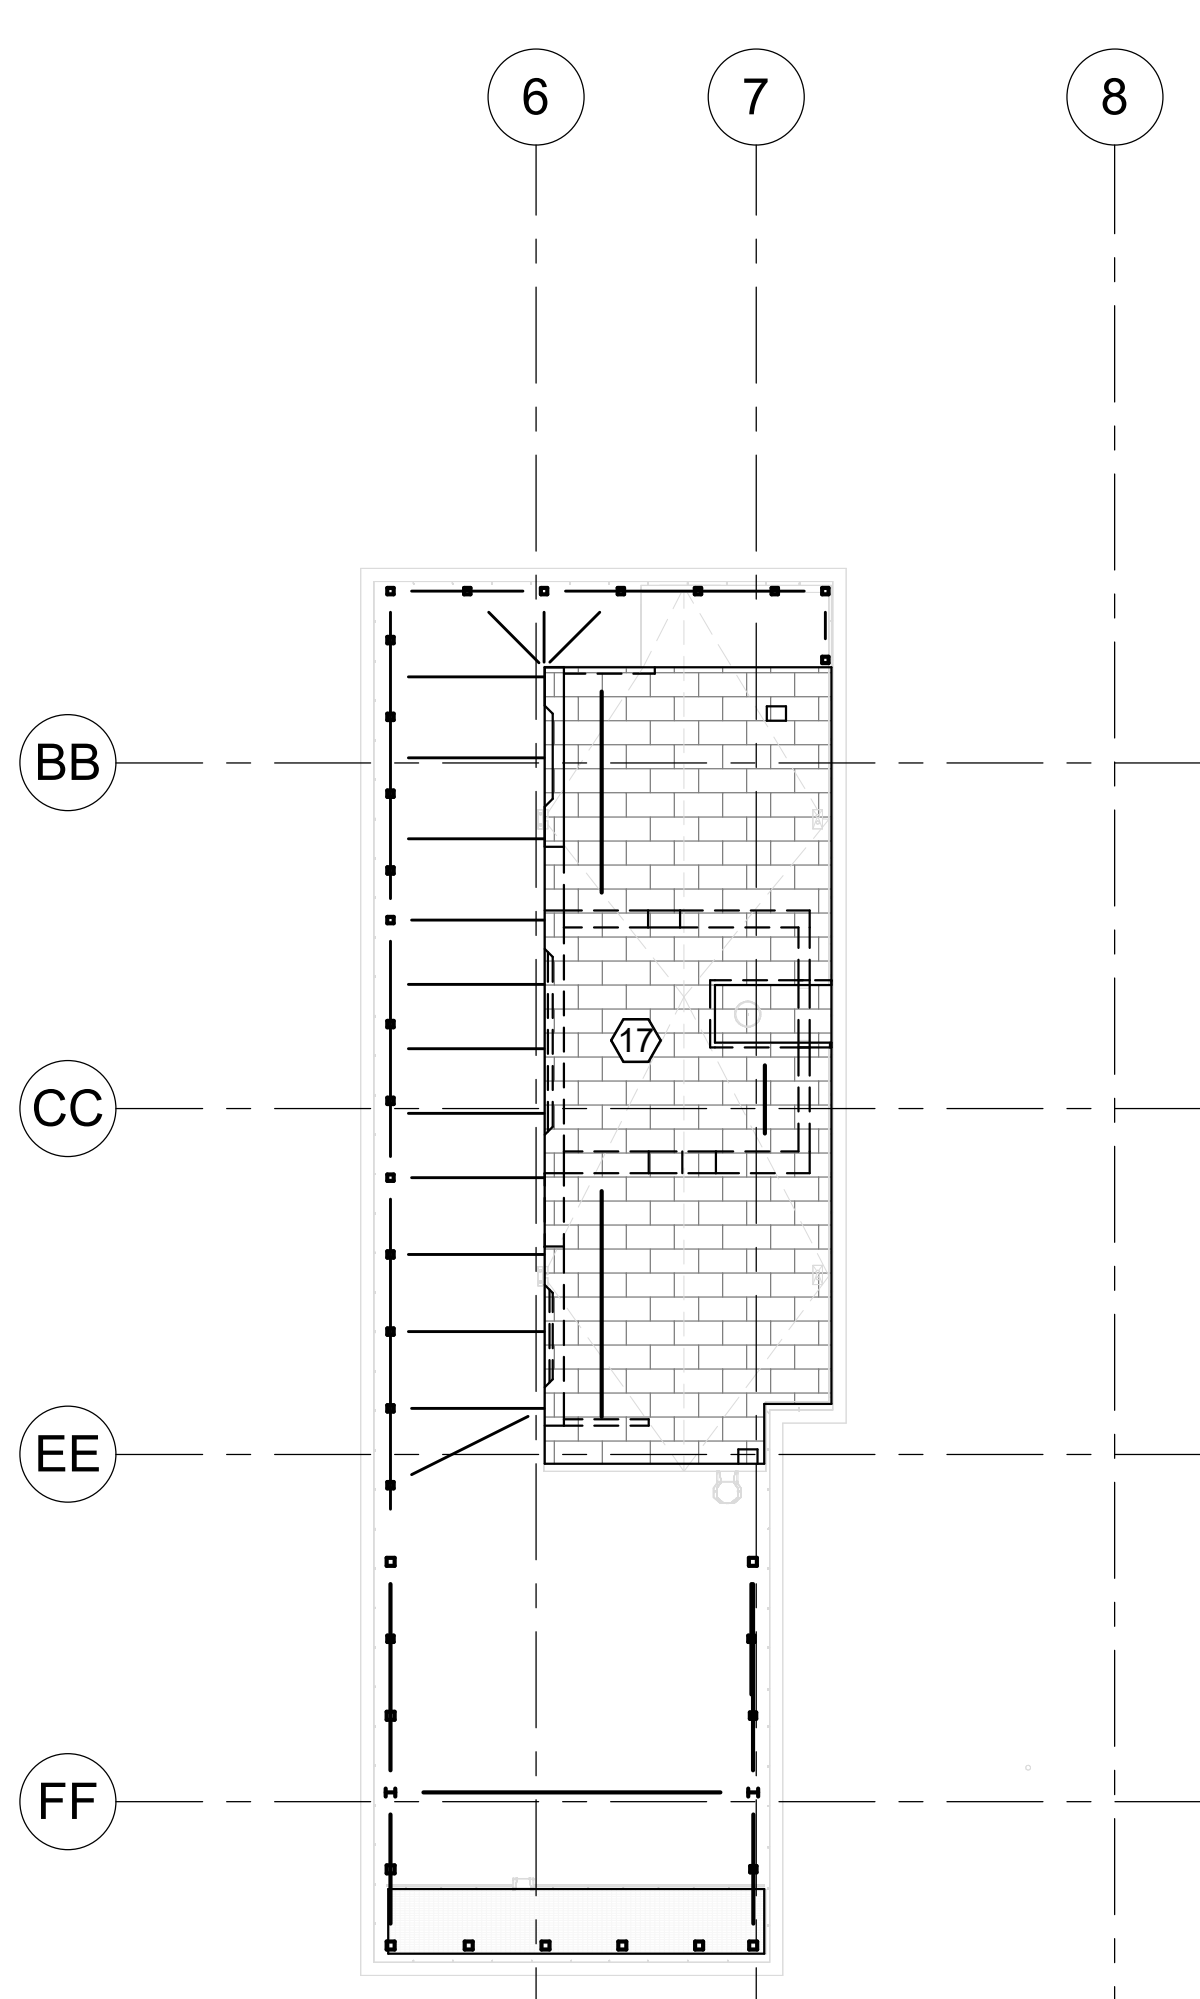

5 ELEV MACH RM ROOF LOAD DIAGRAM
SCALE: 1" = 20'-0"

LOADING MAP									
MARK	DESCRIPTION	SDL (PSF)	LL (PSF)	CONCENTRATED LOAD (LBS)	MARK	DESCRIPTION	SDL (PSF)	LL (PSF)	CONCENTRATED LOAD (LBS)
①	CORRIDOR (RESI)	25	40		⑩	INDOOR/OUTDOOR AMENITY	25	100	
②	LOBBY	15	100		⑪	ROOF	10	20	
③	PLANTER (NON-ACCESSIBLE)	150	20		⑫	OFFICE	15	50	
④	MECHANICAL	10	150		⑬	LOADING DOCK	5	150	
⑤	RESIDENTIAL	25	40		⑭	1' DEEP PLANTING SOIL	110	100	
⑥	TRASH	15	100		⑮	2' DEEP PLANTING SOIL	220	100	
⑦	PARKING	10	40		⑯	4' DEEP TREE/PALM PLANTING PIT	440	100	
⑧	STAIR	5	100	300	⑰	STONE PAVERS	130	100	
⑨	LIGHT STORAGE	10	125		⑱	SPA/TREATMENT ROOM	175	60	
⑩	FITNESS CENTER	25	100		⑲	SPA / FAMILY POOL	300	60	
⑪	WATER STORAGE TANK	15	1700		⑳	TREE-TR1	-	-	2600
⑫	POOL	340	50		㉑	TREE-TR2	-	-	3000
⑬	ELEVATOR MACHINE RM	10	125		㉒	TREE-TR3	-	-	3500
⑭	PUMP ROOM	15	100		㉓	TREE-TR4 - MISC	-	-	1000
⑮	ELECTRIC	10	100		㉔	RETAIL	25	100	
					㉕	BATHROOM	25	60	

- LOAD MAP NOTES:
- SUPERIMPOSED LOADS INDICATED ARE IN ADDITION TO SELF-WEIGHT OF STRUCTURE.
 - WHERE APPLICABLE, LIVE LOADS HAVE BEEN REDUCED BELOW THE TABULATED VALUES PER THE BUILDING CODE.
 - CLADDING LOADS:
15 PSF OVER WALL AREA (EXTERIOR GLAZING)
5 PSF FOR MECHANICAL SCREEN & LOUVERS

BALDRIDGE & ASSOCIATES
STRUCTURAL
ENGINEERING
1164 Balape Street, Suite 1600
Honolulu, HI 96813
Phone: 808.534.1300 | Email: info@baseeng.com

PALEKANA PERMITS
THIRD PARTY CERTIFICATION
☐ BUILDING CODE ☐ ELECTRICAL CODE
☐ MECHANICAL CODE ☐ RESIDENTIAL CODE
☐ STRUCTURAL (NON-SHALED STORY OVERLAP)



Digitally signed by Steven M. Baldrige
Date: 2024.08.22 22:43:07-0500 April 30, 2026

FOR BALDRIDGE & ASSOCIATES STRUCTURAL ENGINEERING, INC.
THIS WORK WAS PREPARED BY ME OR UNDER MY SUPERVISION AND CONSTRUCTION OF THIS PROJECT WILL BE UNDER MY OBSERVATION

NO.	DATE	DESCRIPTION
3	08.30.2024	ADDENDUM 03
F5	05.31.2024	FOUNDATION PERMIT R5
F2	02.29.2024	FOUNDATION PERMIT R2
S2	02.27.2024	SUPERSTRUCTURE PERMIT R2
1	11.17.2023	ADDENDUM 01
F1	11.17.2023	FOUNDATION PERMIT R1
B1	11.17.2023	BUILDING PERMIT R1
S1	11.17.2023	SUPERSTRUCTURE PERMIT R1

SCB
Solomon Cordwell Buenz
Chicago
T 312.896.1100
San Francisco
T 415.216.2450
www.scb.com

KALAE BUILDING PERMIT

TMK: (1) 2-3-001: 133
1000 ALA MOANA BLVD.
HONOLULU, HI 96814

LOADING DIAGRAMS

SCALE: As indicated
Drawn By: DJ
Checked By: MH
Project Number: 2018032
Sheet Number: S0.08