


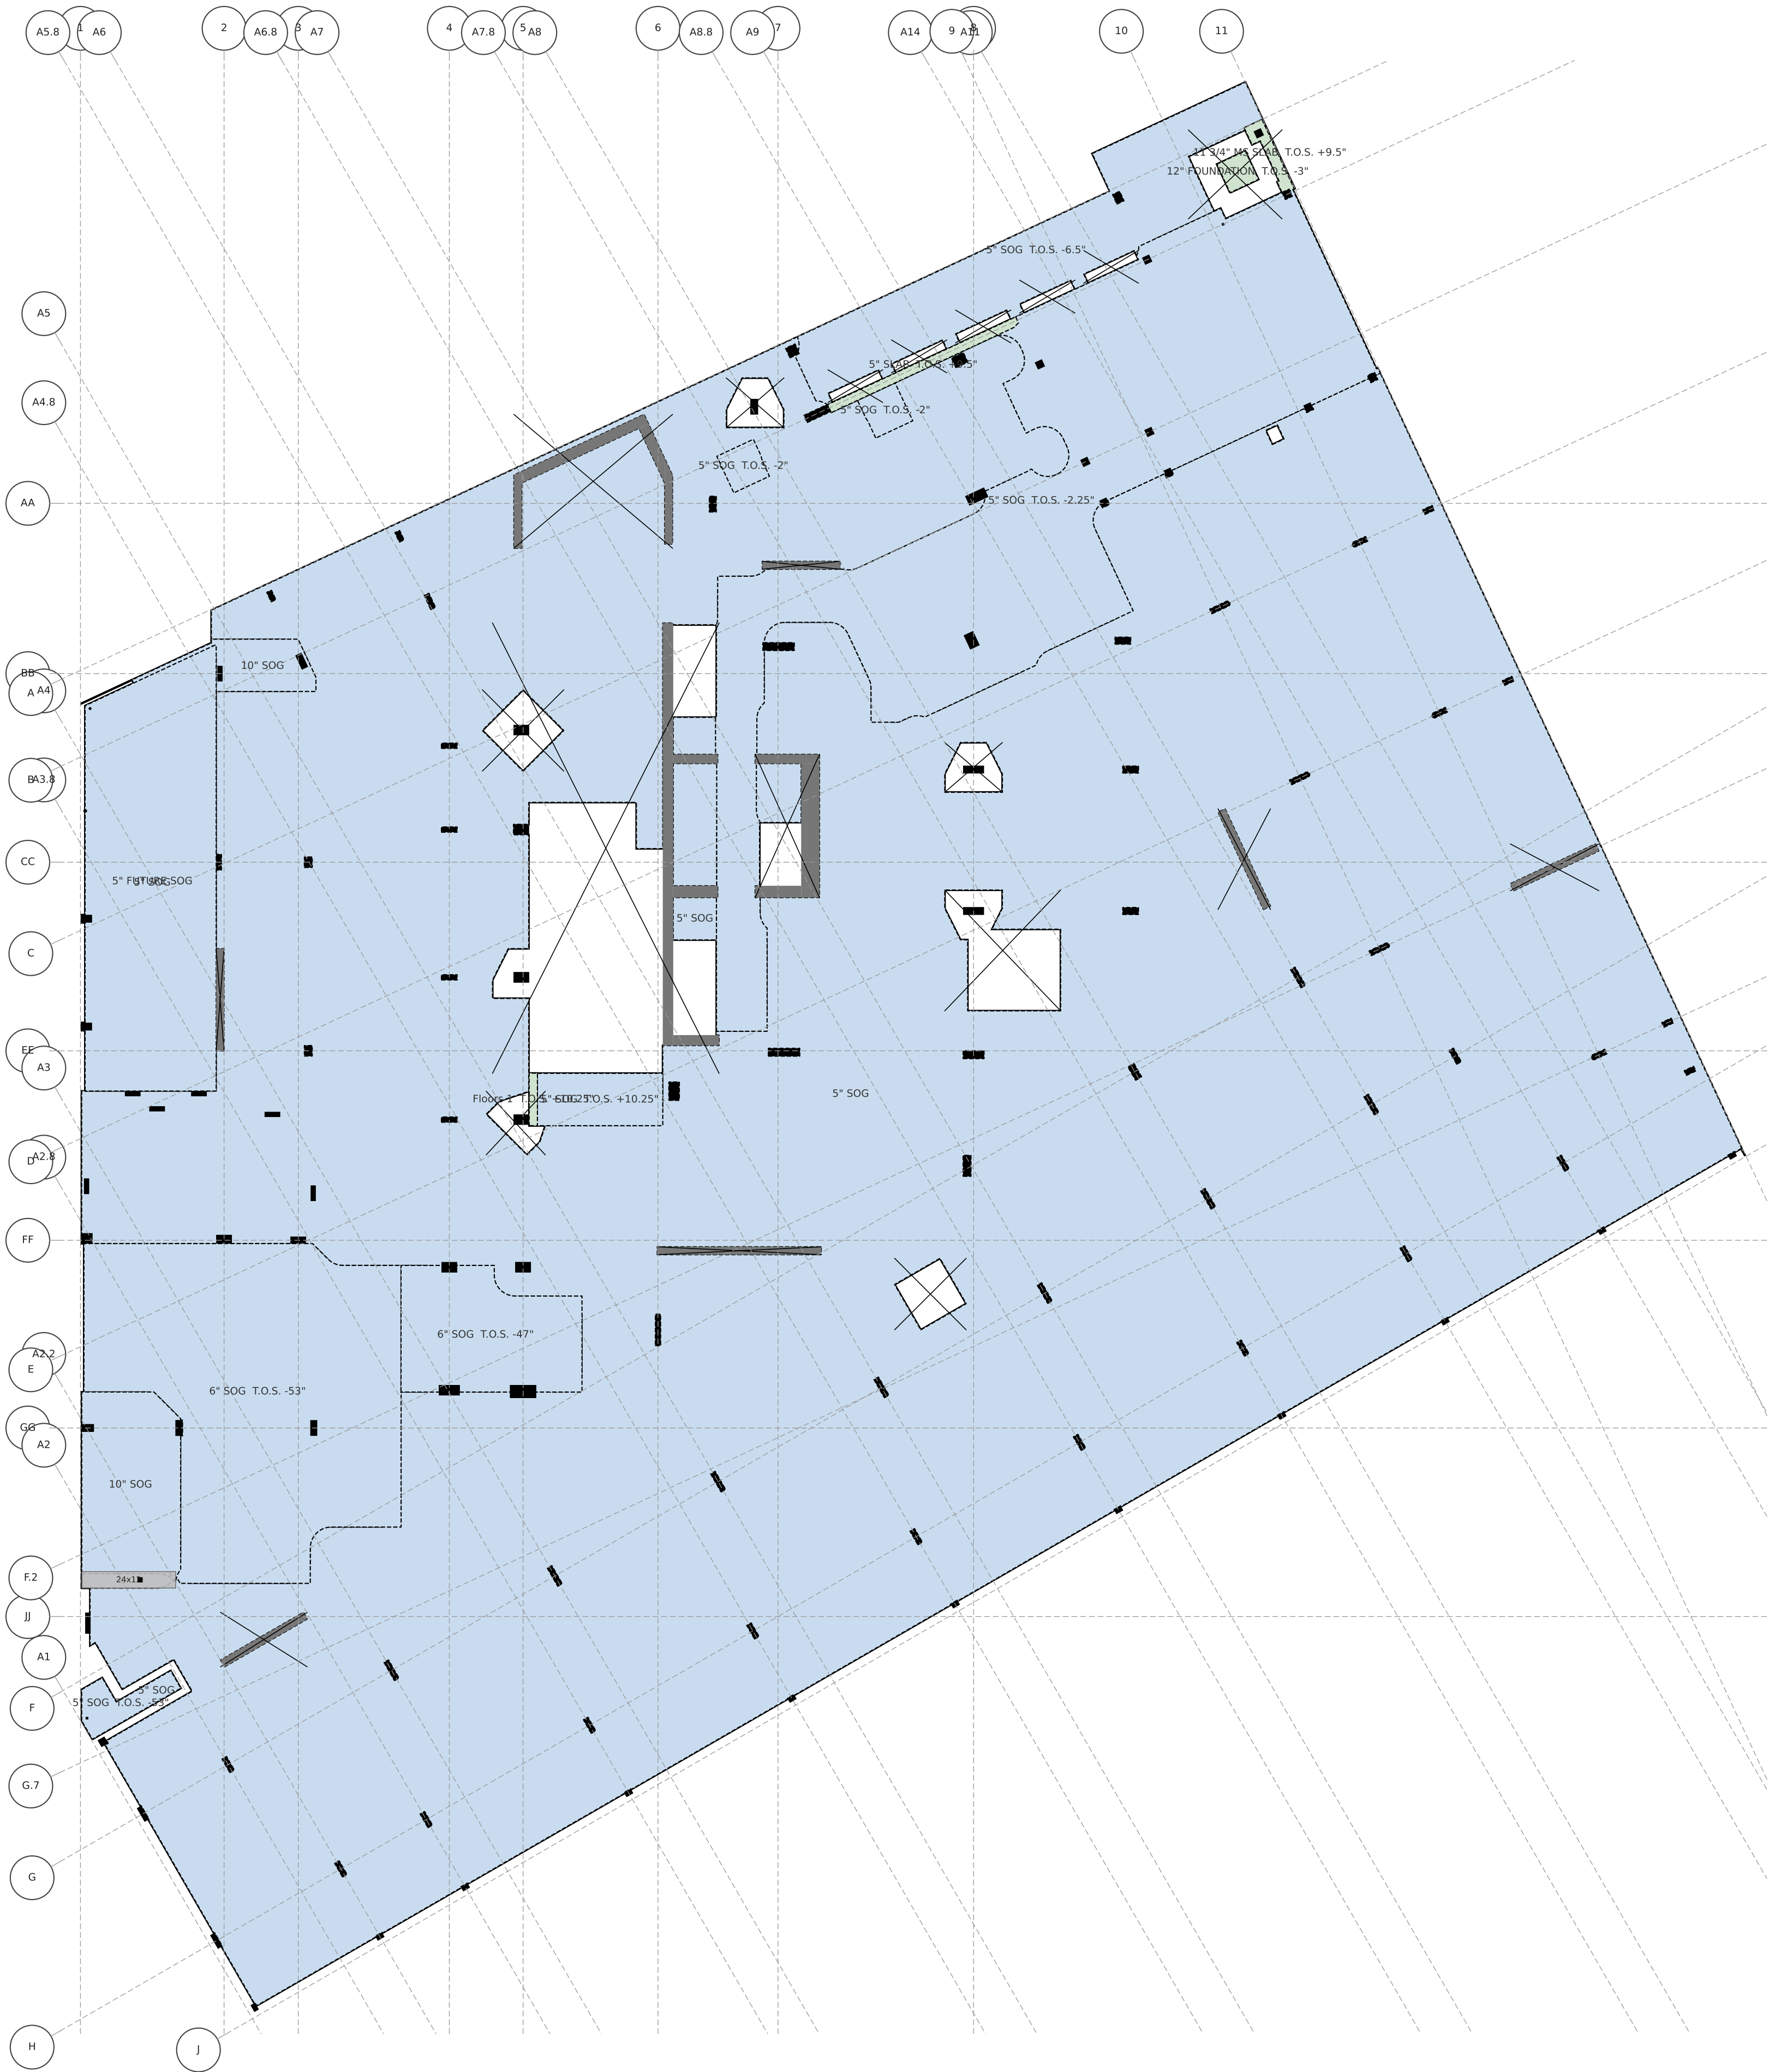


1268 KALAE

LEVEL 1 FLOOR PLAN

T.O.S. 100'-0" · typical slab 5" · scale 1" = 20' · SLAB ON GRADE

Generated from 92743ac6-HI_KALAE_MCC_ST.ifc (Revit scope model) for the McClone Reshore Calculator — geometry only; loading marks are drawn in the calculator.

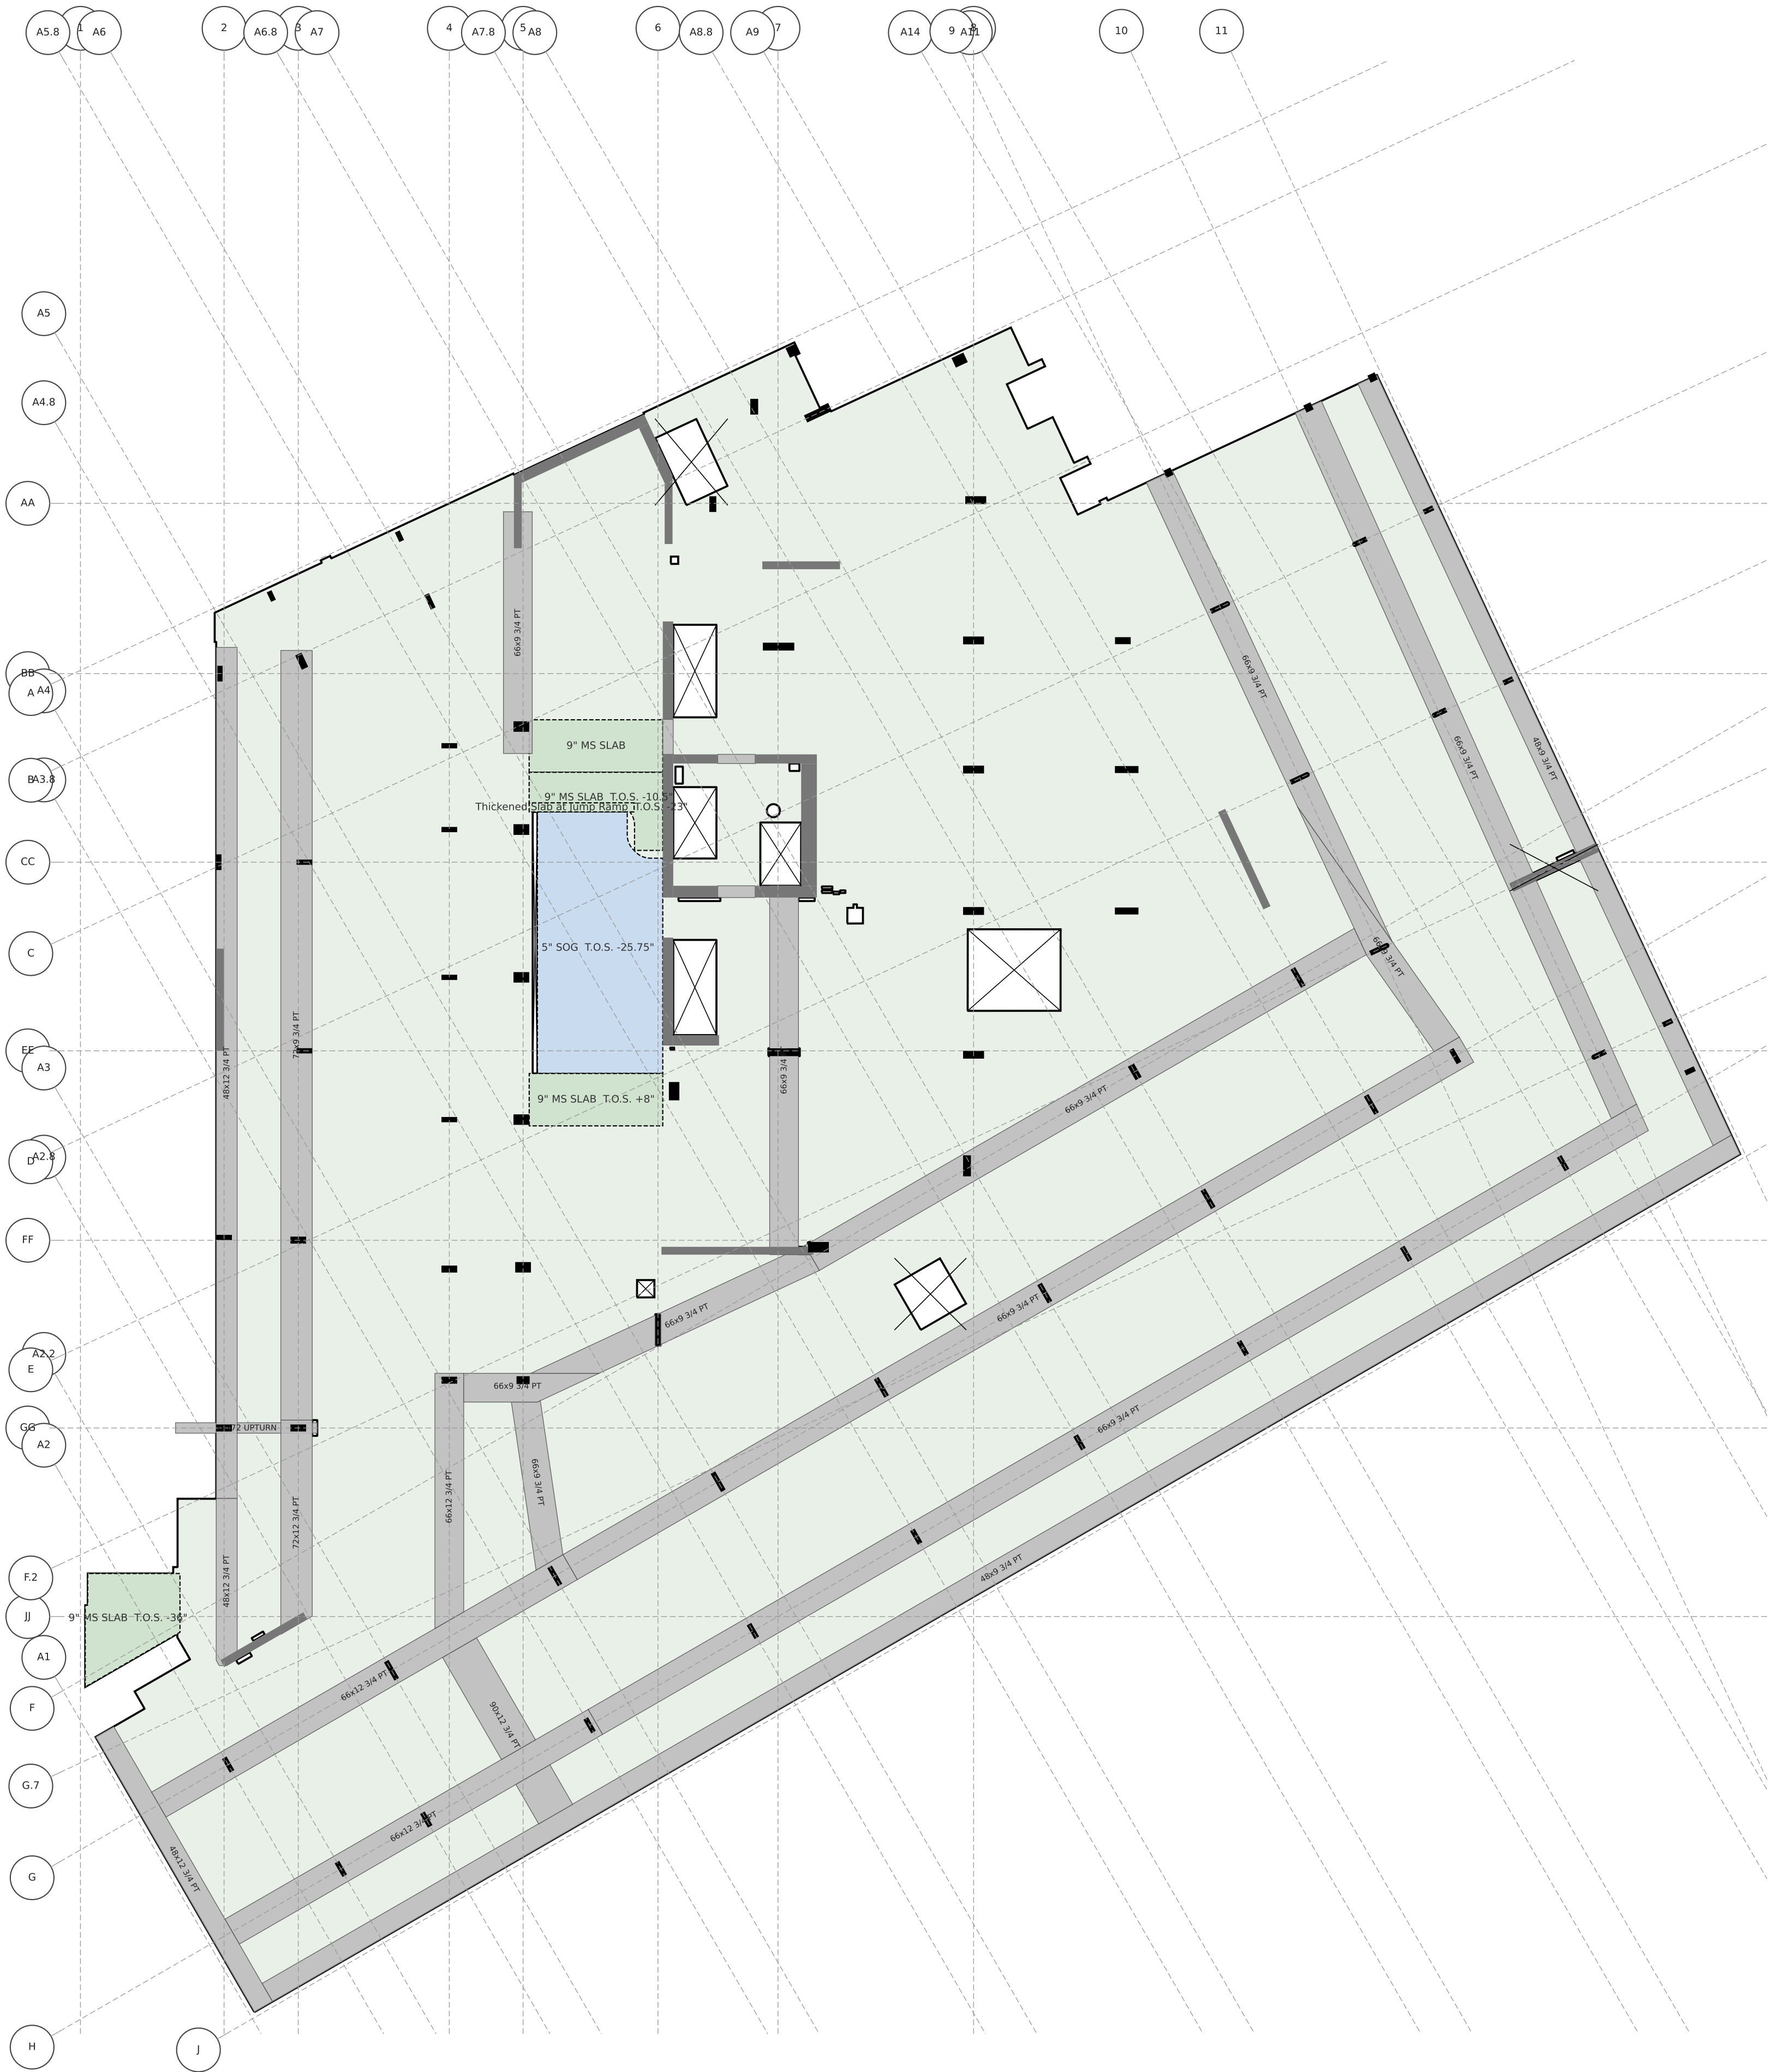


1268 KALAE

LEVEL 2 FLOOR PLAN

T.O.S. 111'-6" · typical slab 7.5" · scale 1" = 20'

Generated from 92743ac6-HI_KALAE_MCC_ST.ifc (Revit scope model) for the McClone Reshore Calculator — geometry only; loading marks are drawn in the calculator.

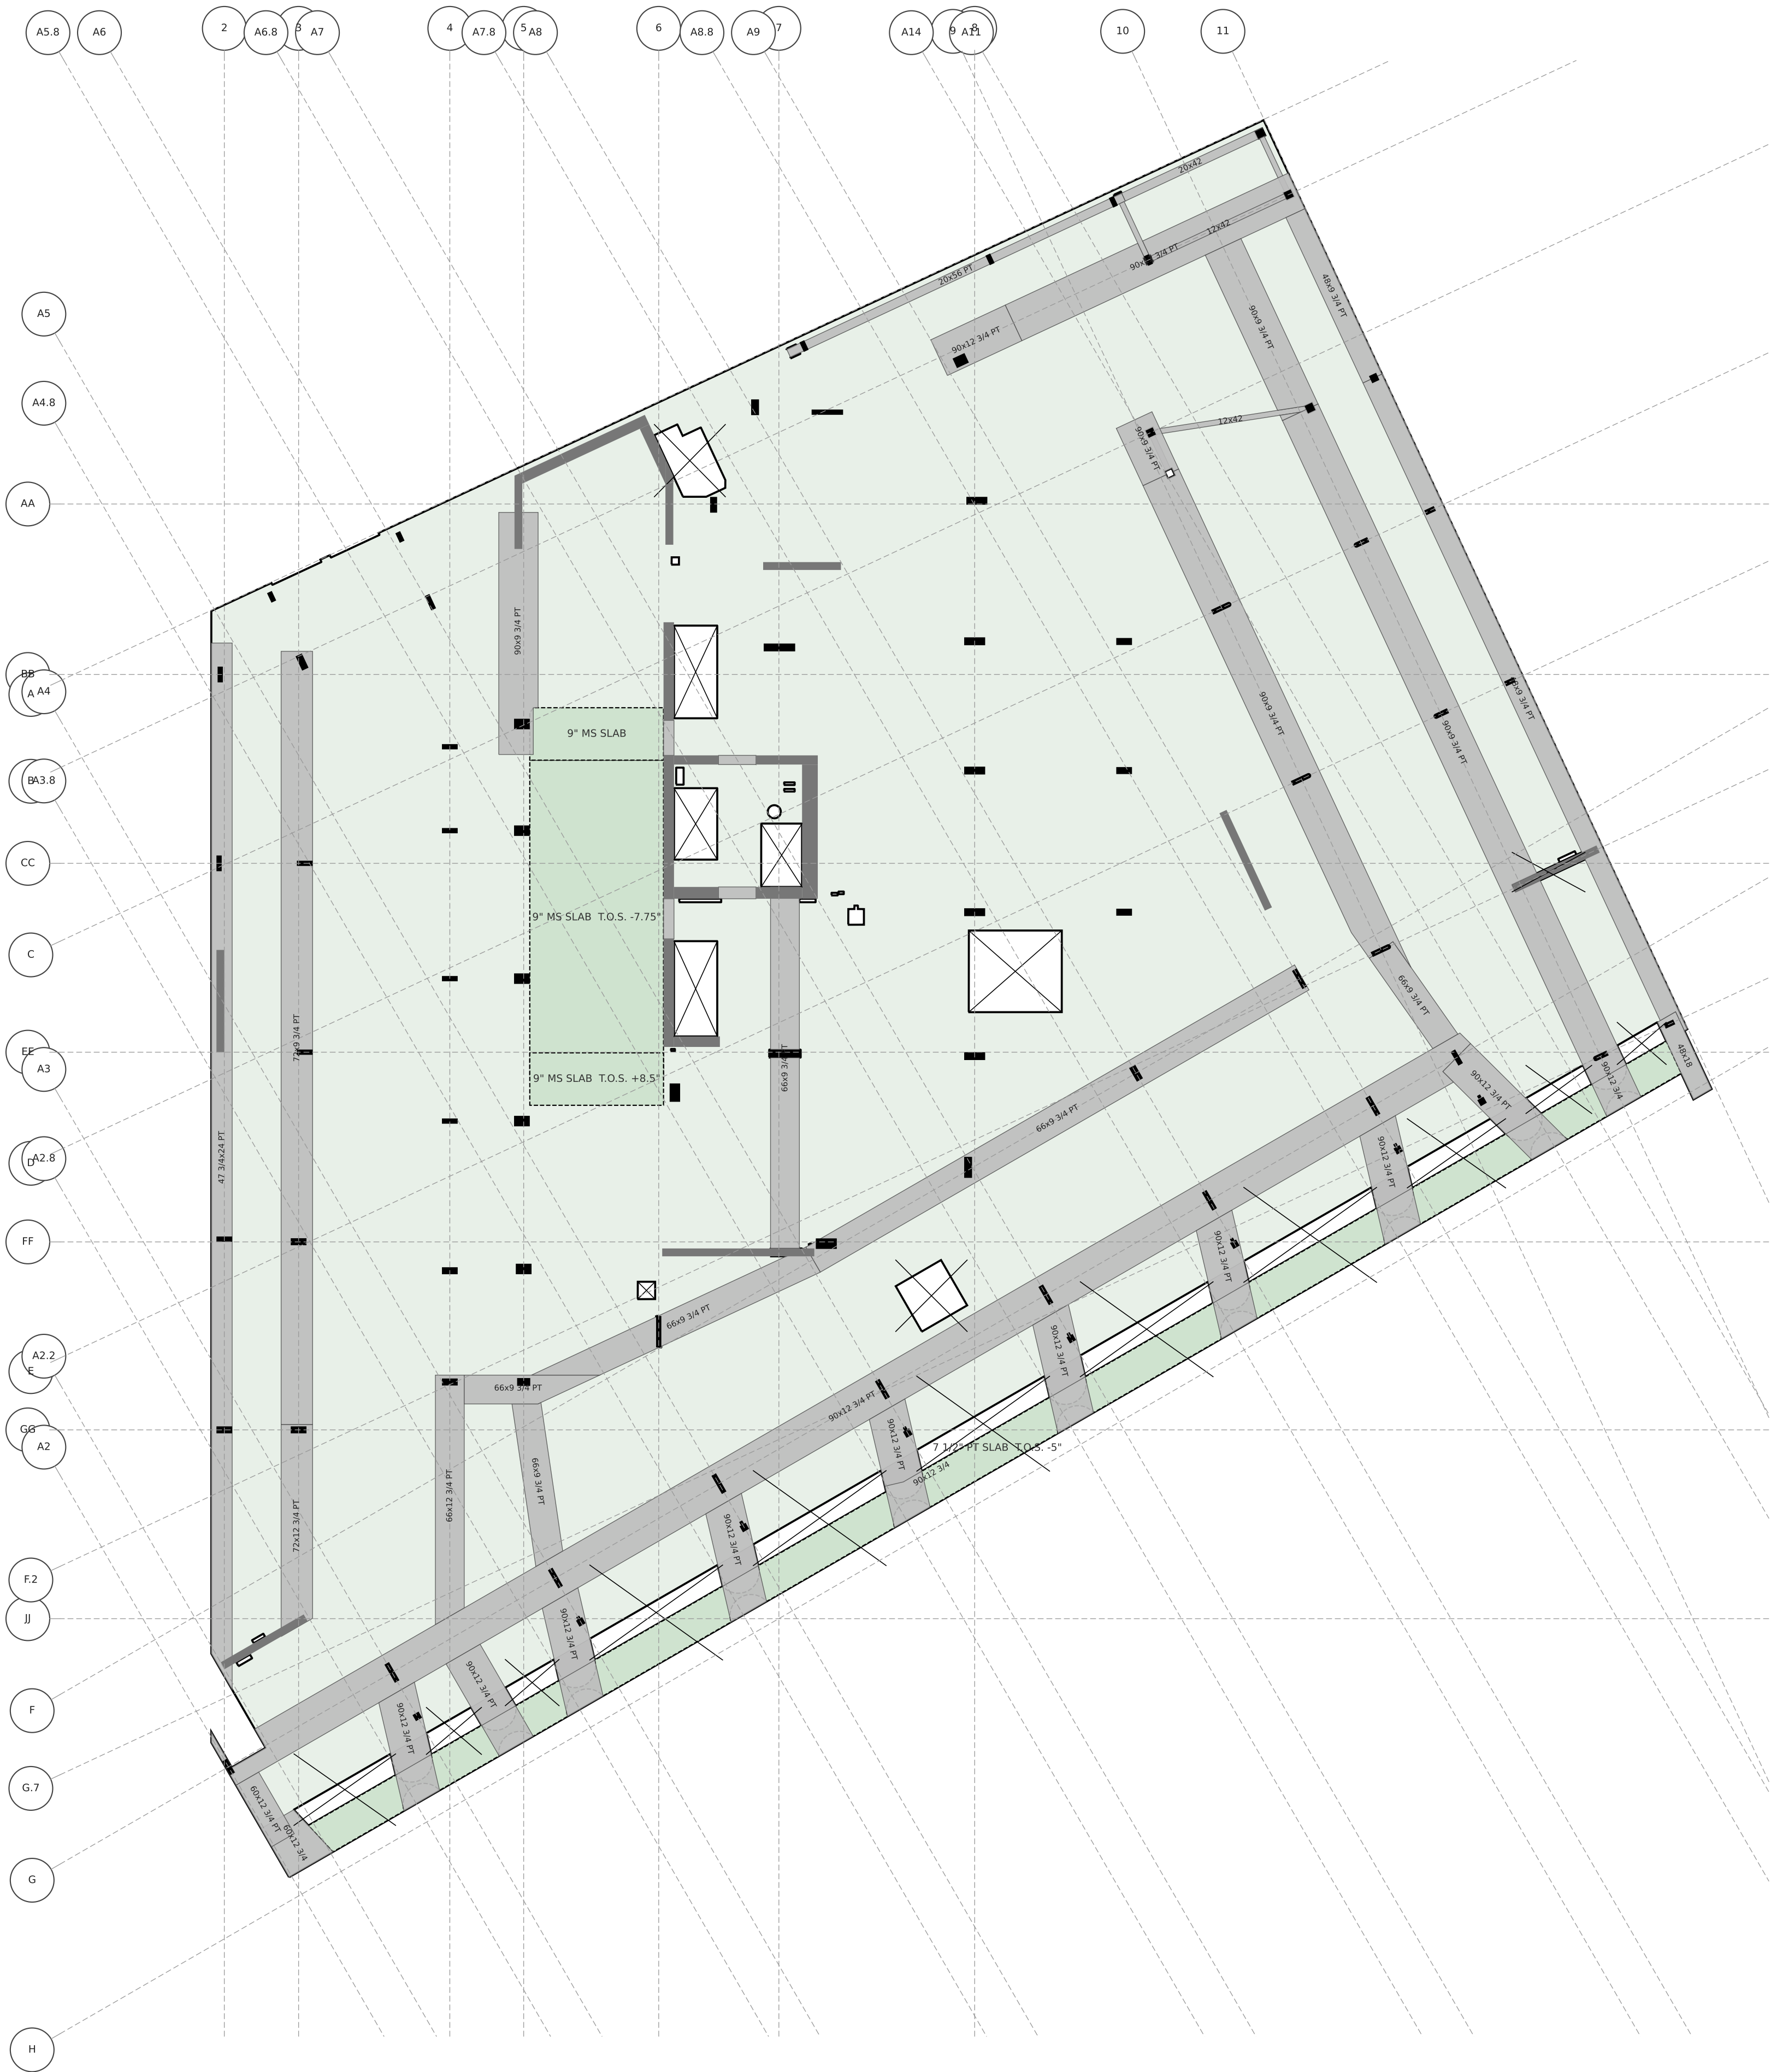


1268 KALAE

LEVEL 3 FLOOR PLAN

T.O.S. 120'-8" · typical slab 7.5" · scale 1" = 20'

Generated from 92743ac6-HI_KALAE_MCC_ST.ifc (Revit scope model) for the McClone Reshore Calculator — geometry only; loading marks are drawn in the calculator.

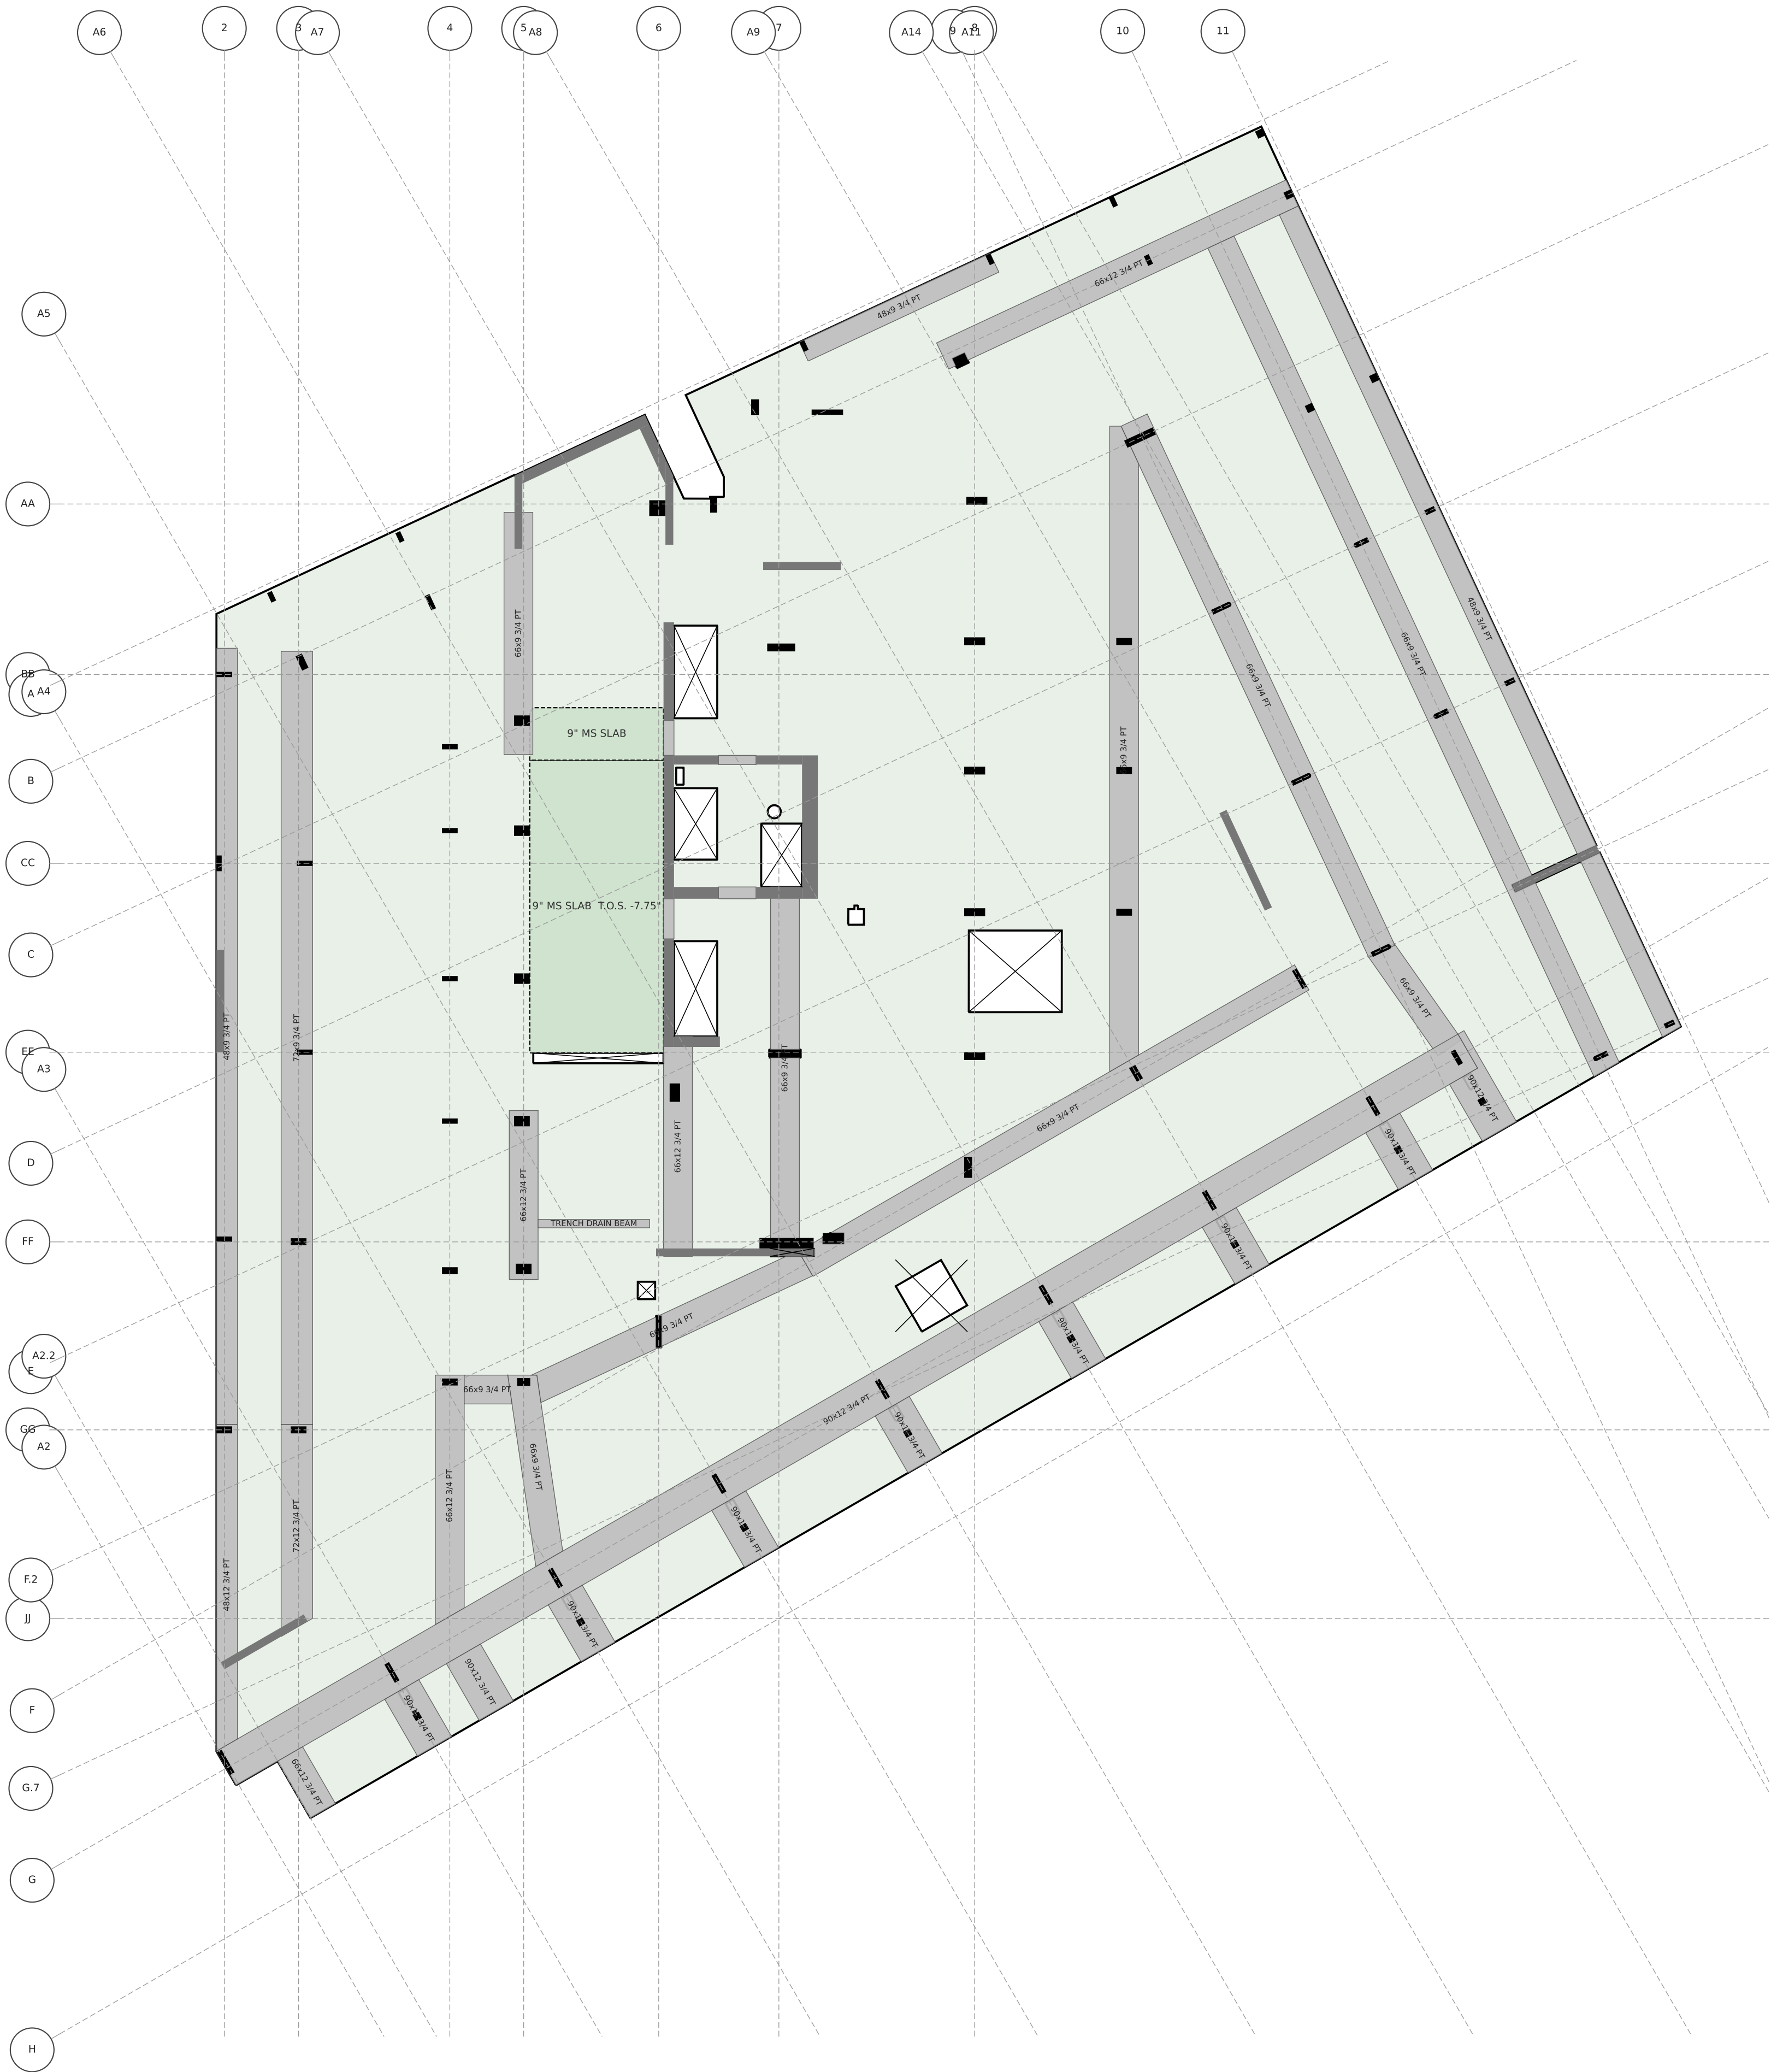


1268 KALAE

LEVEL 4 FLOOR PLAN

T.O.S. 129'-10" · typical slab 7.5" · scale 1" = 20'

Generated from 92743ac6-HI_KALAE_MCC_ST.ifc (Revit scope model) for the McClone Reshore Calculator — geometry only; loading marks are drawn in the calculator.

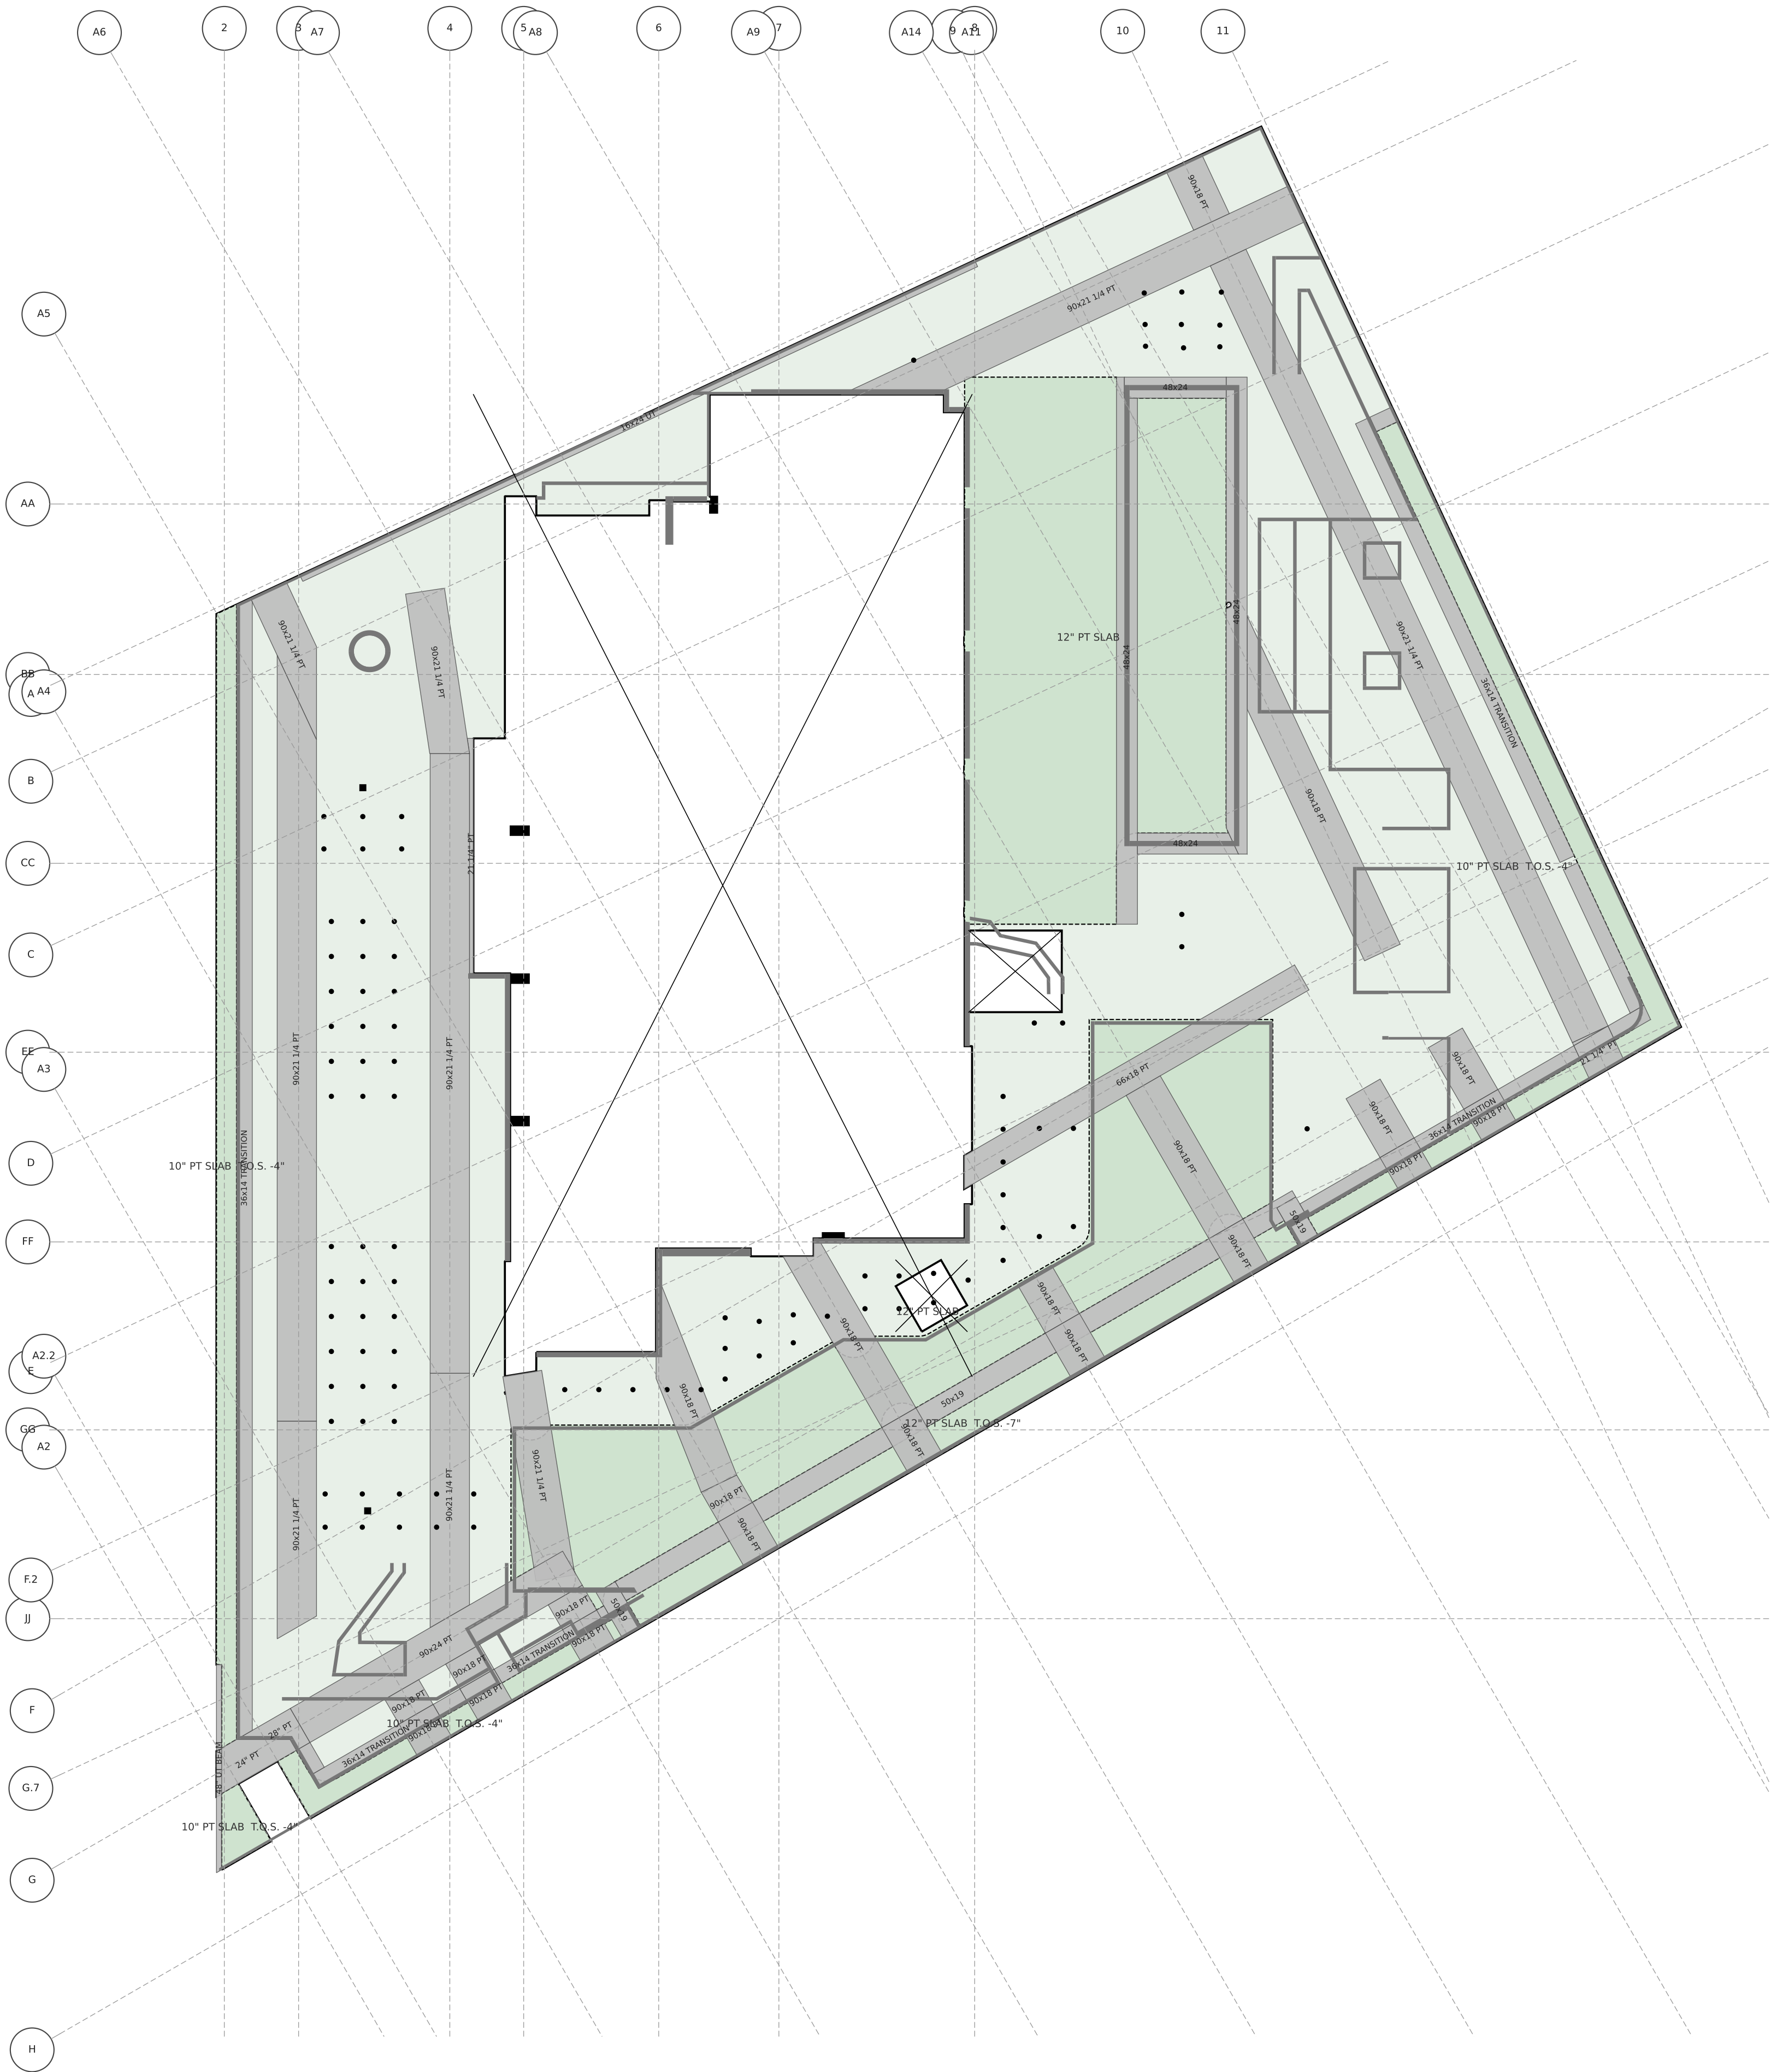


1268 KALAE

LEVEL 4.5 FLOOR PLAN

T.O.S. 139'-0" · typical slab 10" · scale 1" = 20'

Generated from 92743ac6-HI_KALAE_MCC_ST.ifc (Revit scope model) for the McClone Reshore Calculator — geometry only; loading marks are drawn in the calculator.

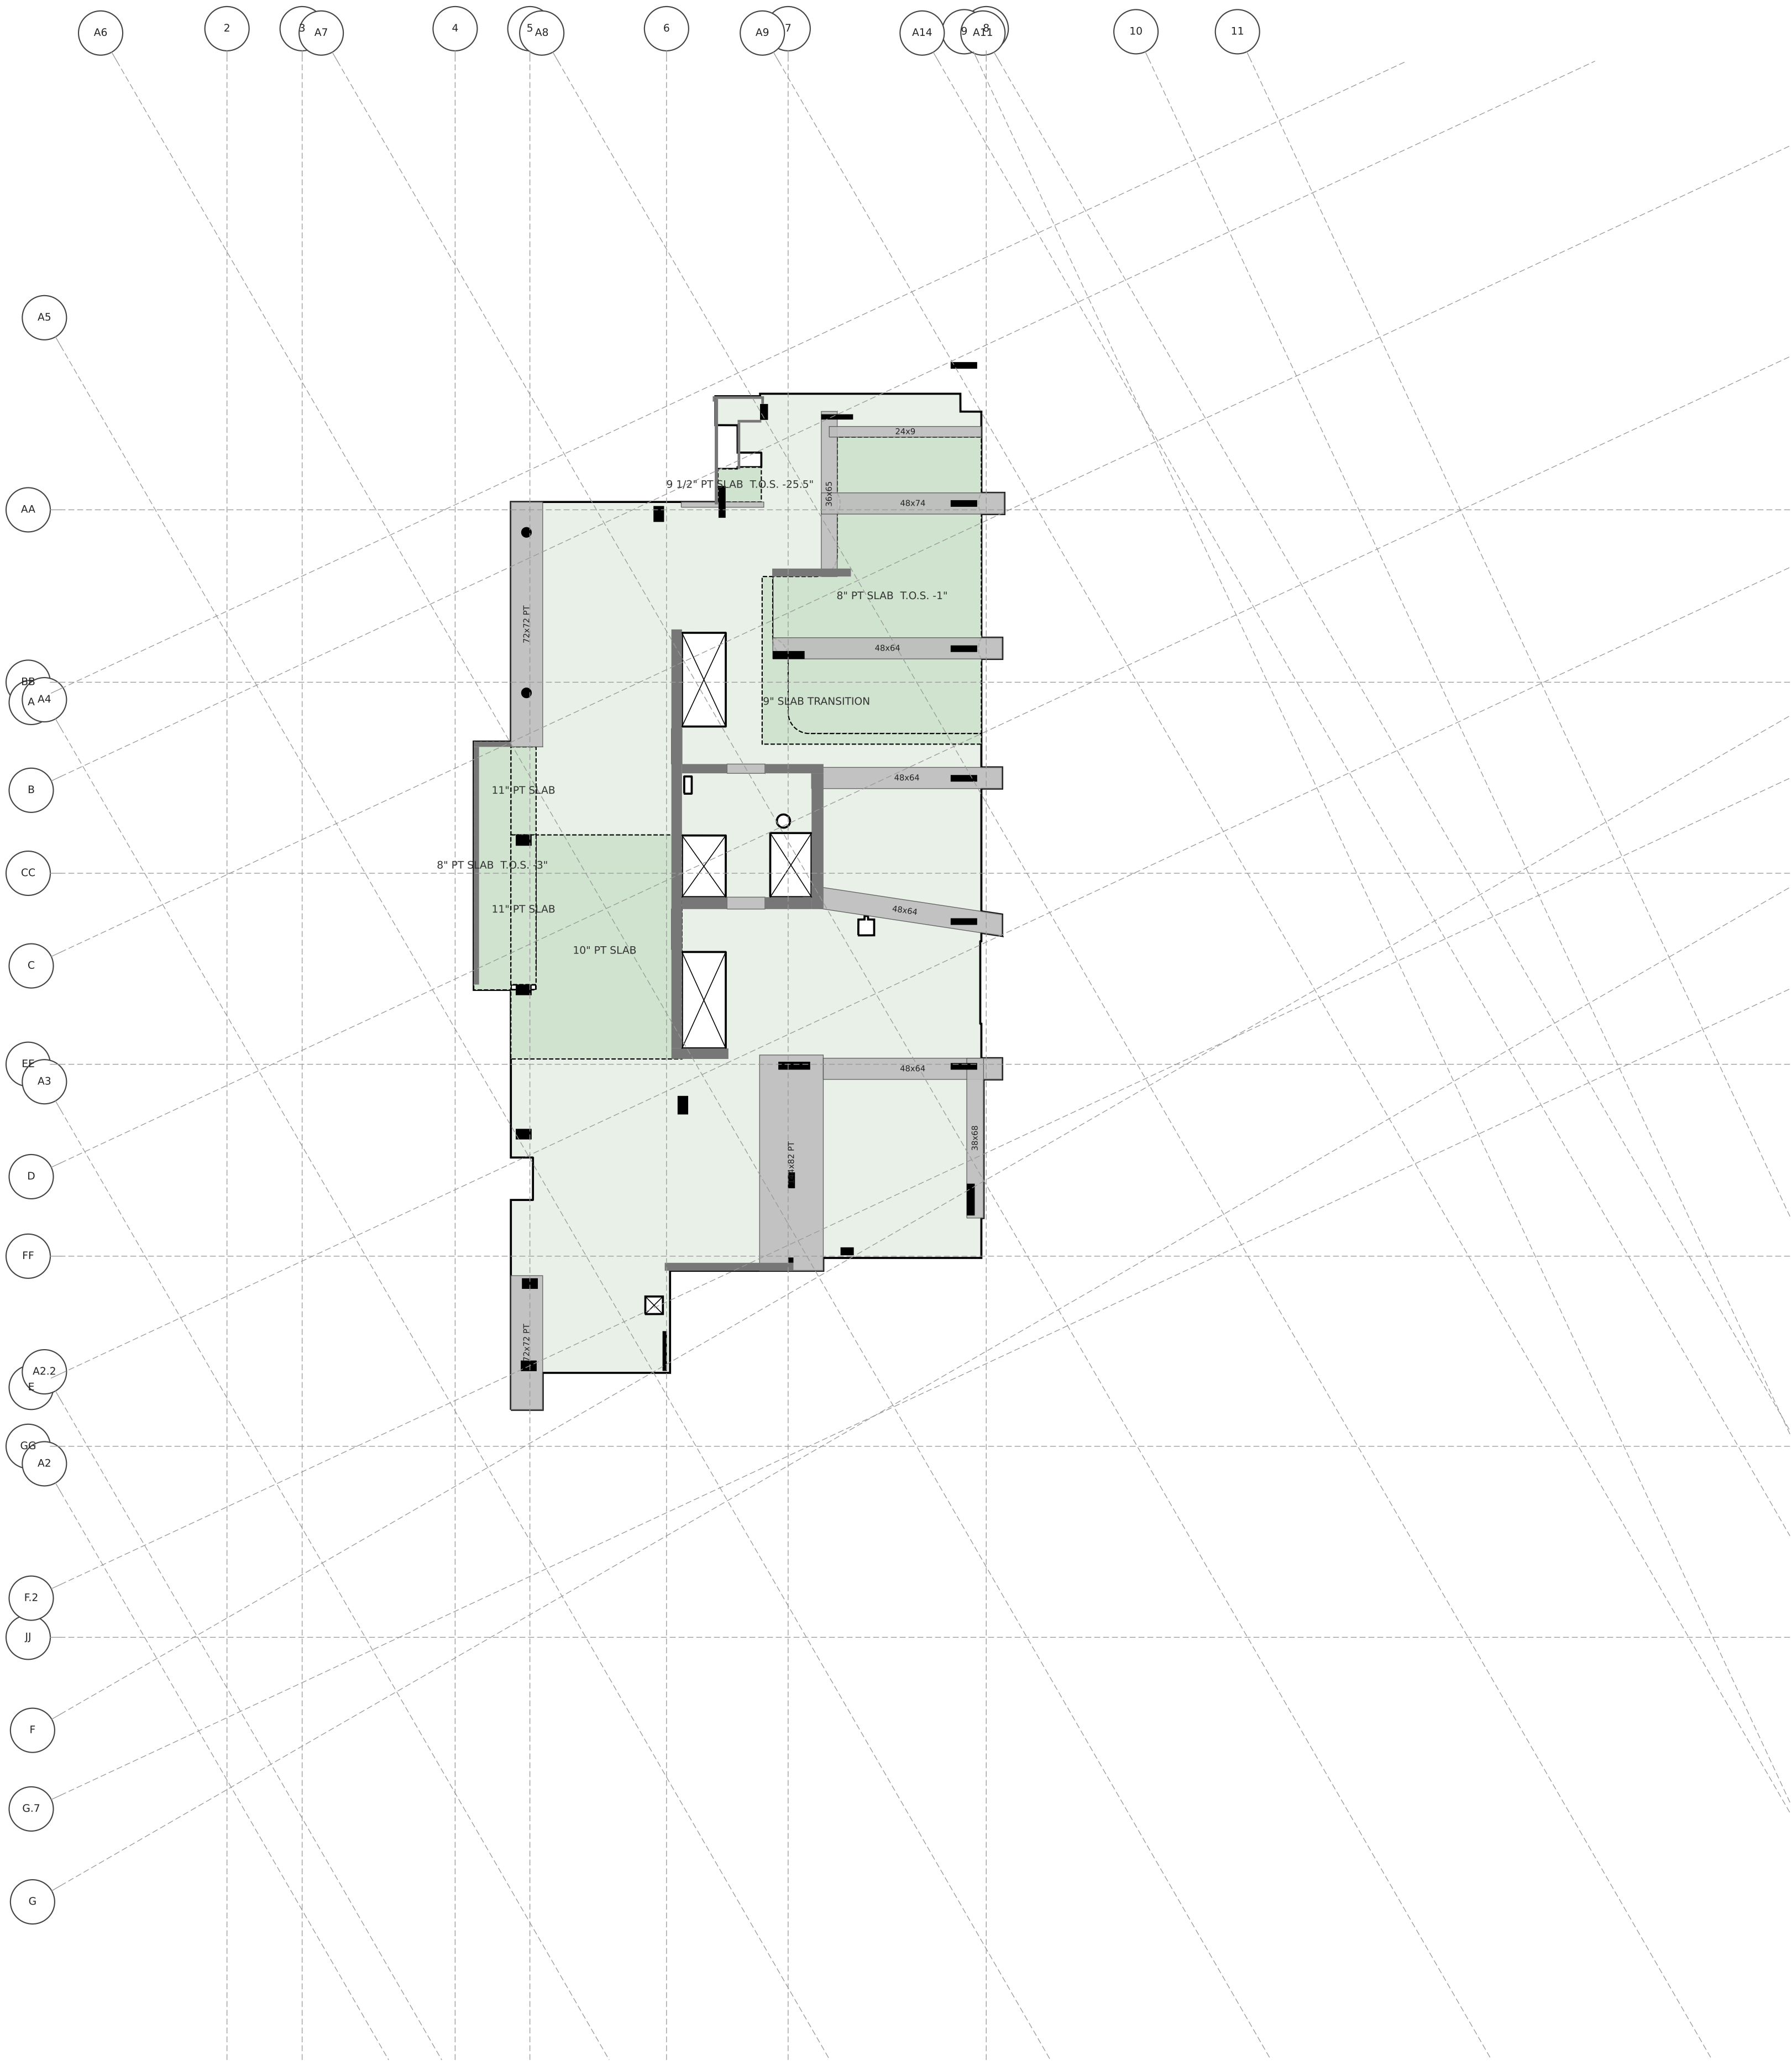


1268 KALAE

LEVEL 5 FLOOR PLAN

T.O.S. 143'-10" · typical slab 8" · scale 1" = 20'

Generated from 92743ac6-HI_KALAE_MCC_ST.ifc (Revit scope model) for the McClone Reshore Calculator — geometry only; loading marks are drawn in the calculator.

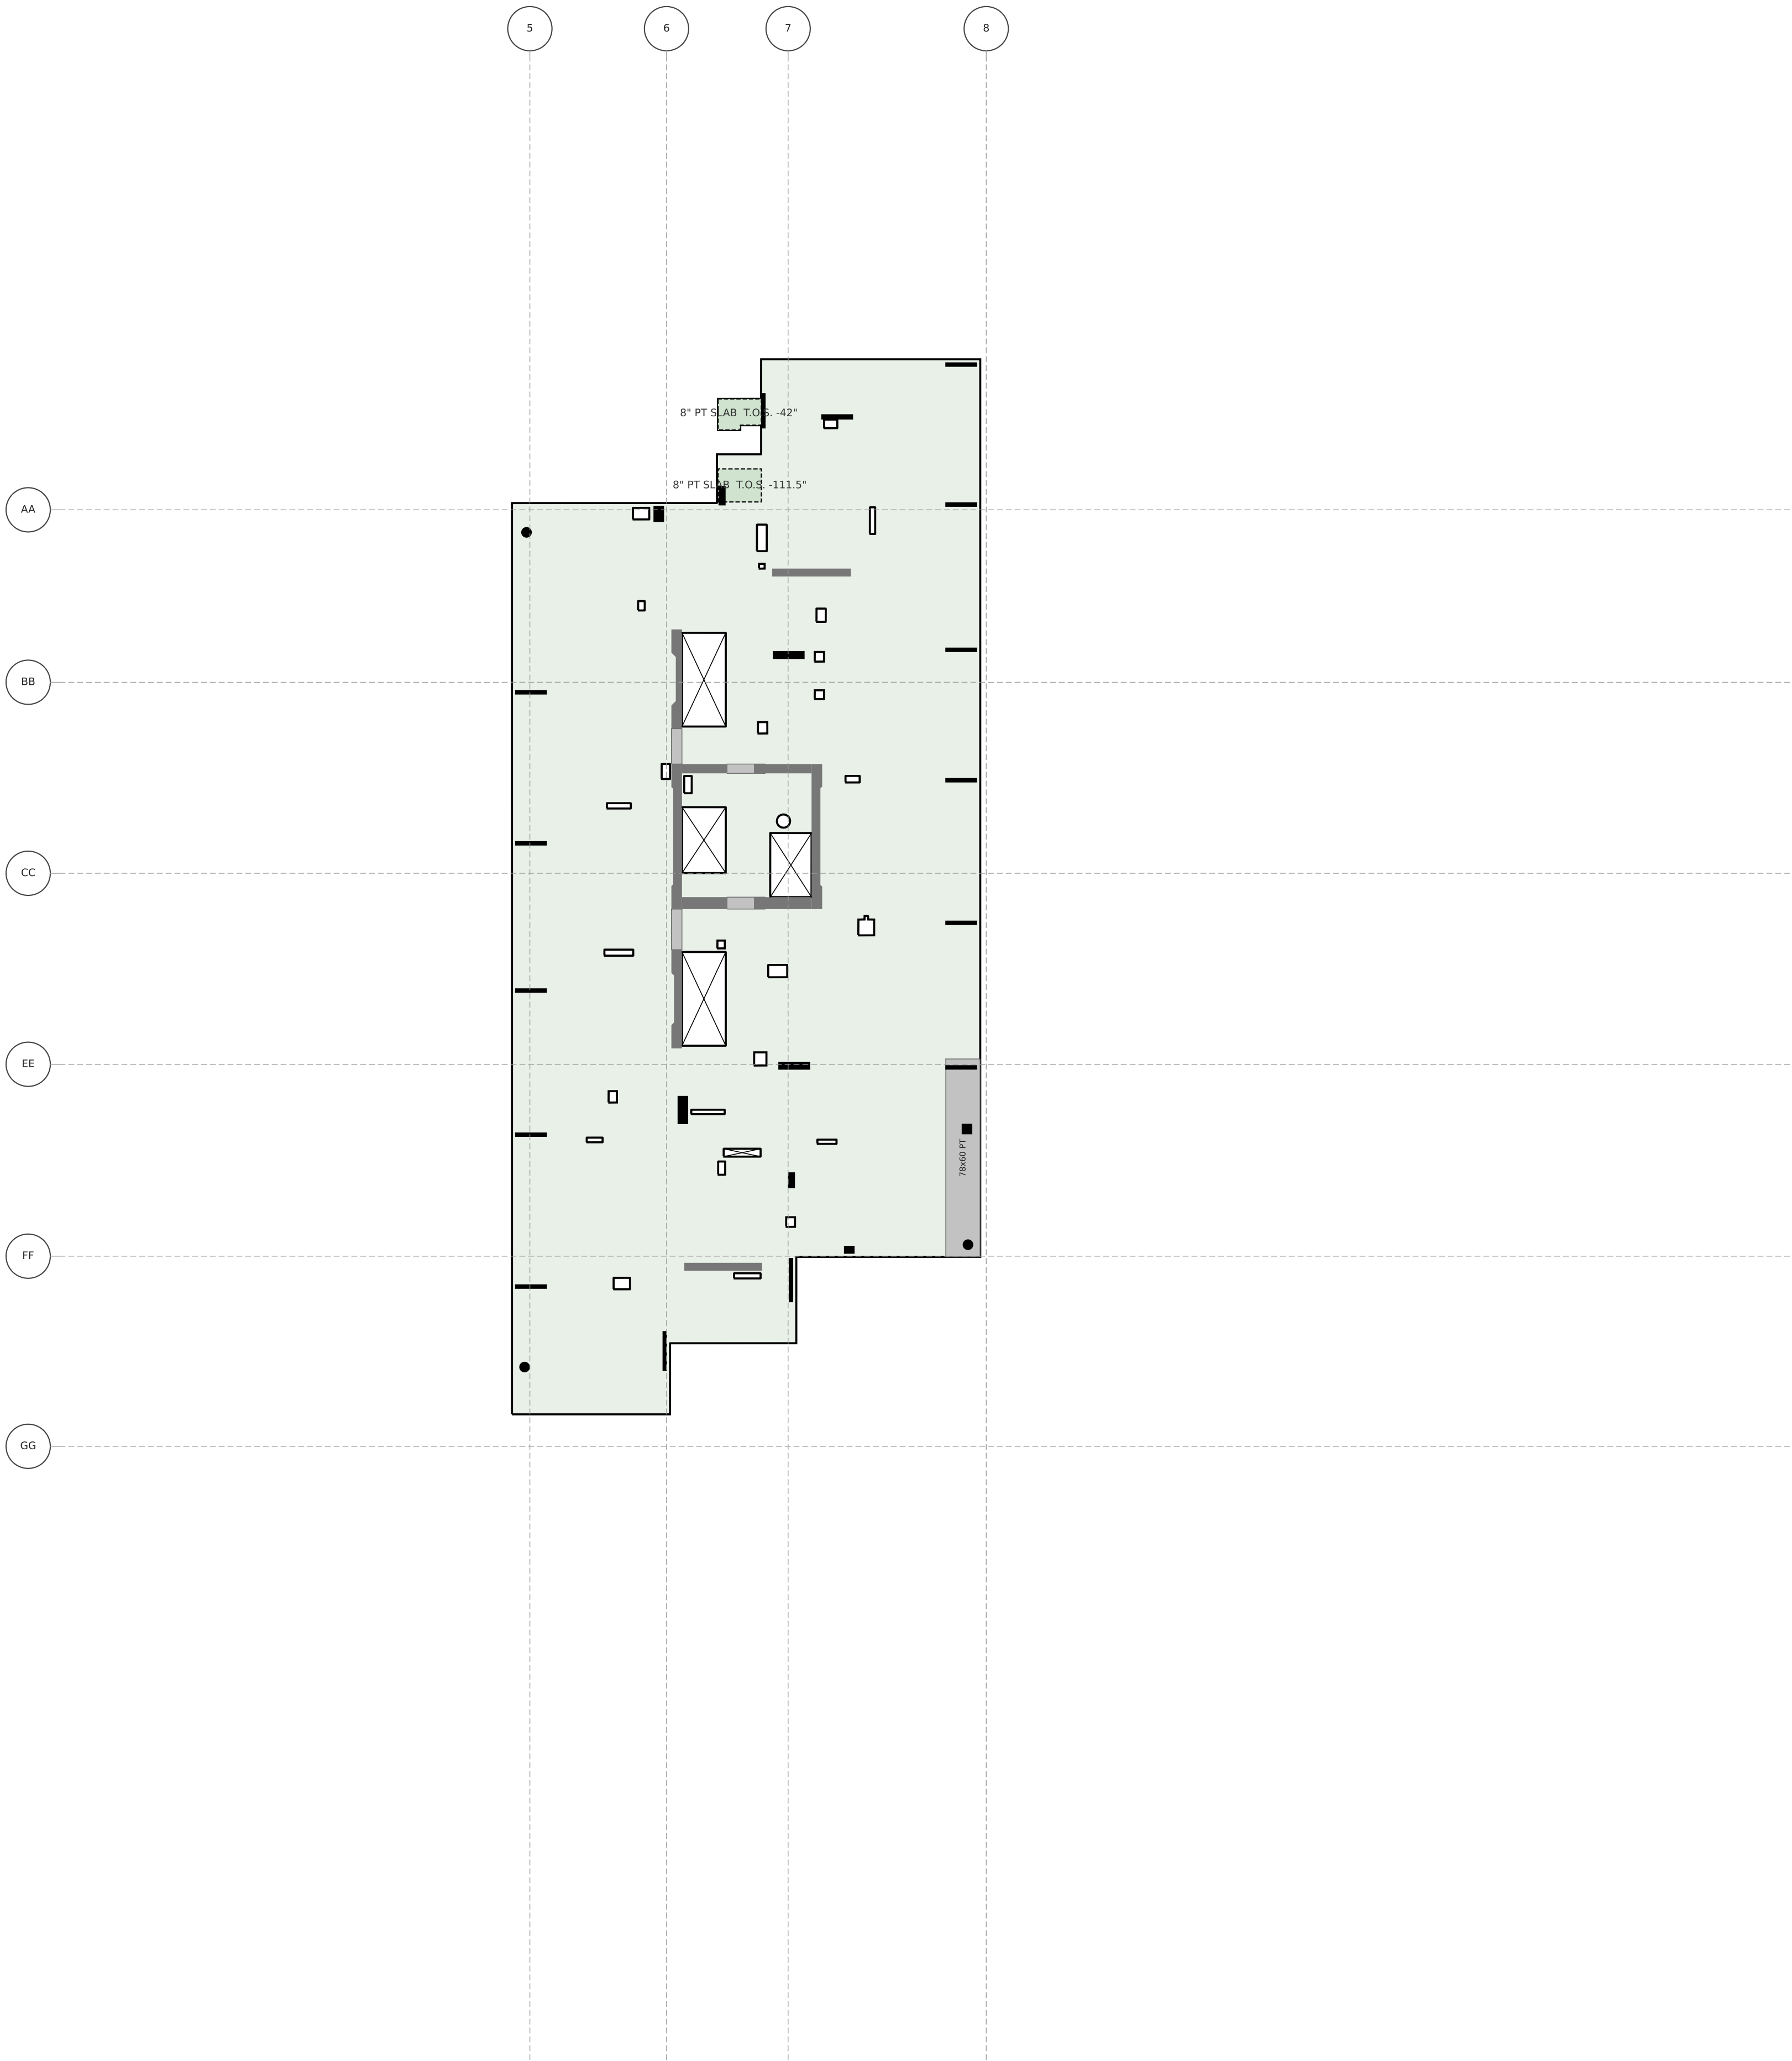


1268 KALAE

LEVEL 6 FLOOR PLAN

T.O.S. 159'-0" · typical slab 7.5" · scale 1" = 20'

Generated from 92743ac6-HI_KALAE_MCC_ST.ifc (Revit scope model) for the McClone Reshore Calculator — geometry only; loading marks are drawn in the calculator.

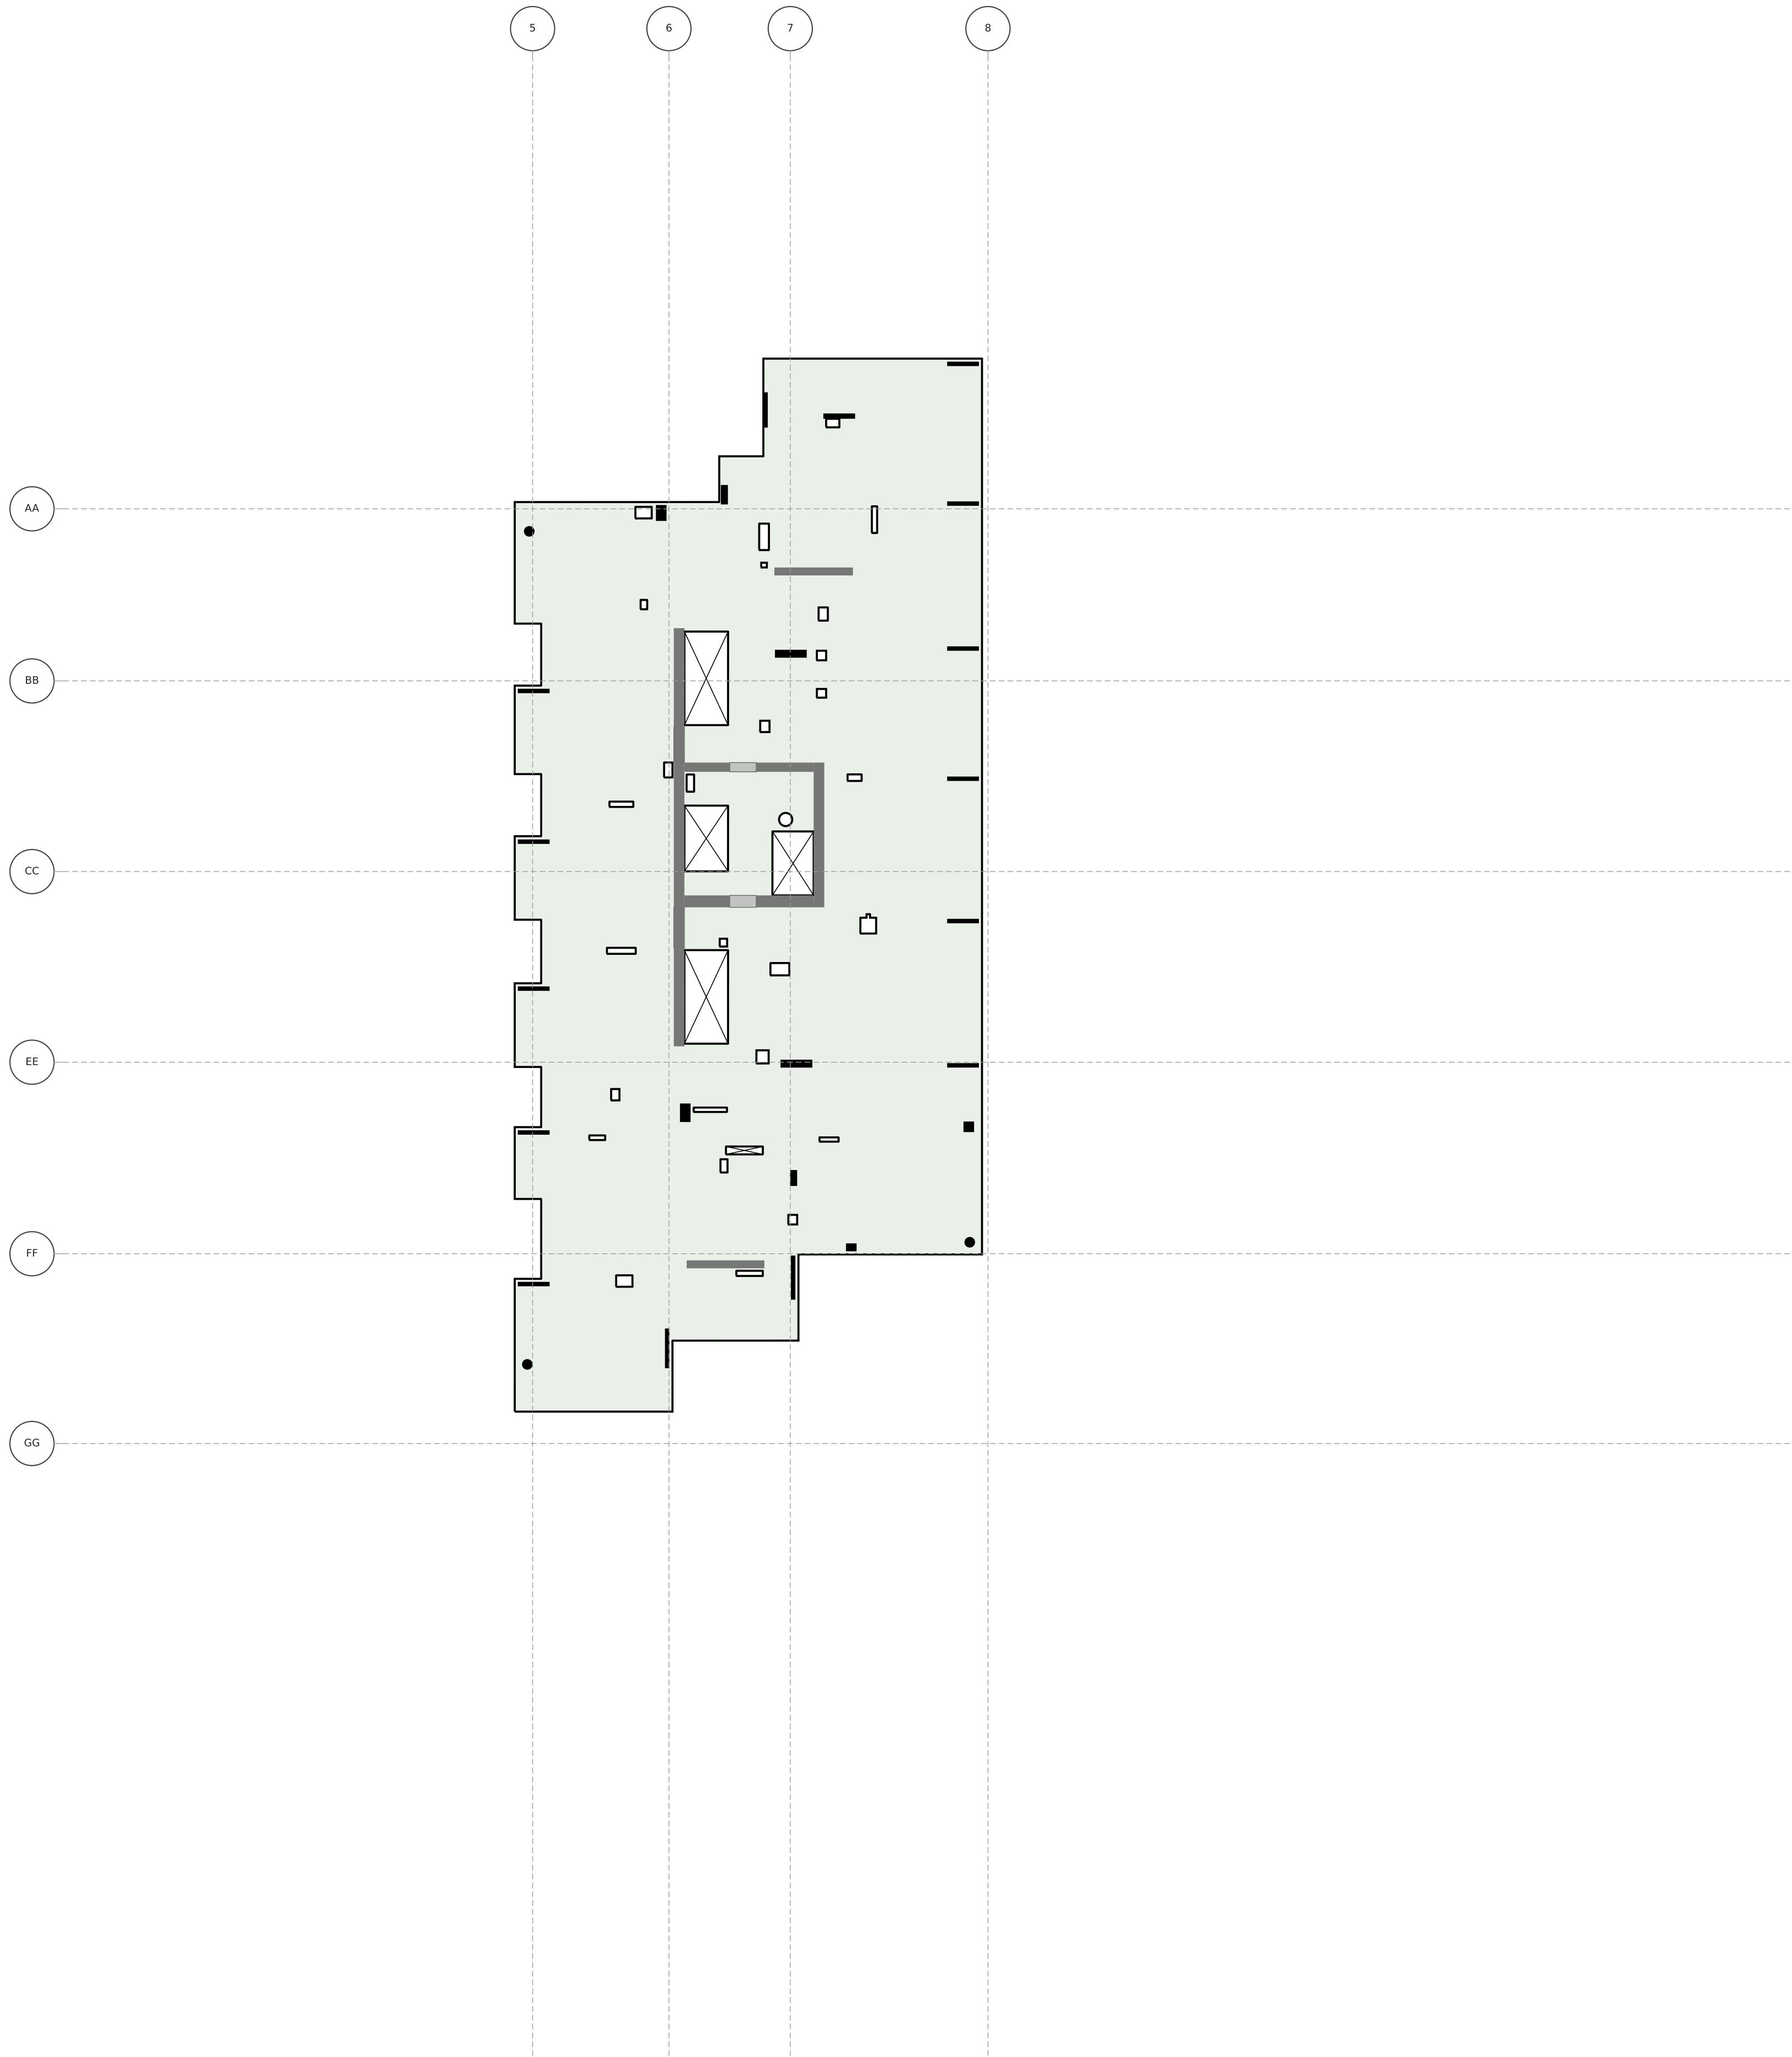


1268 KALAE

LEVEL 7 FLOOR PLAN

T.O.S. 168'-8.5" · typical slab 7.5" · scale 1" = 20'

Generated from 92743ac6-HI_KALAE_MCC_ST.ifc (Revit scope model) for the McClone Reshore Calculator — geometry only; loading marks are drawn in the calculator.

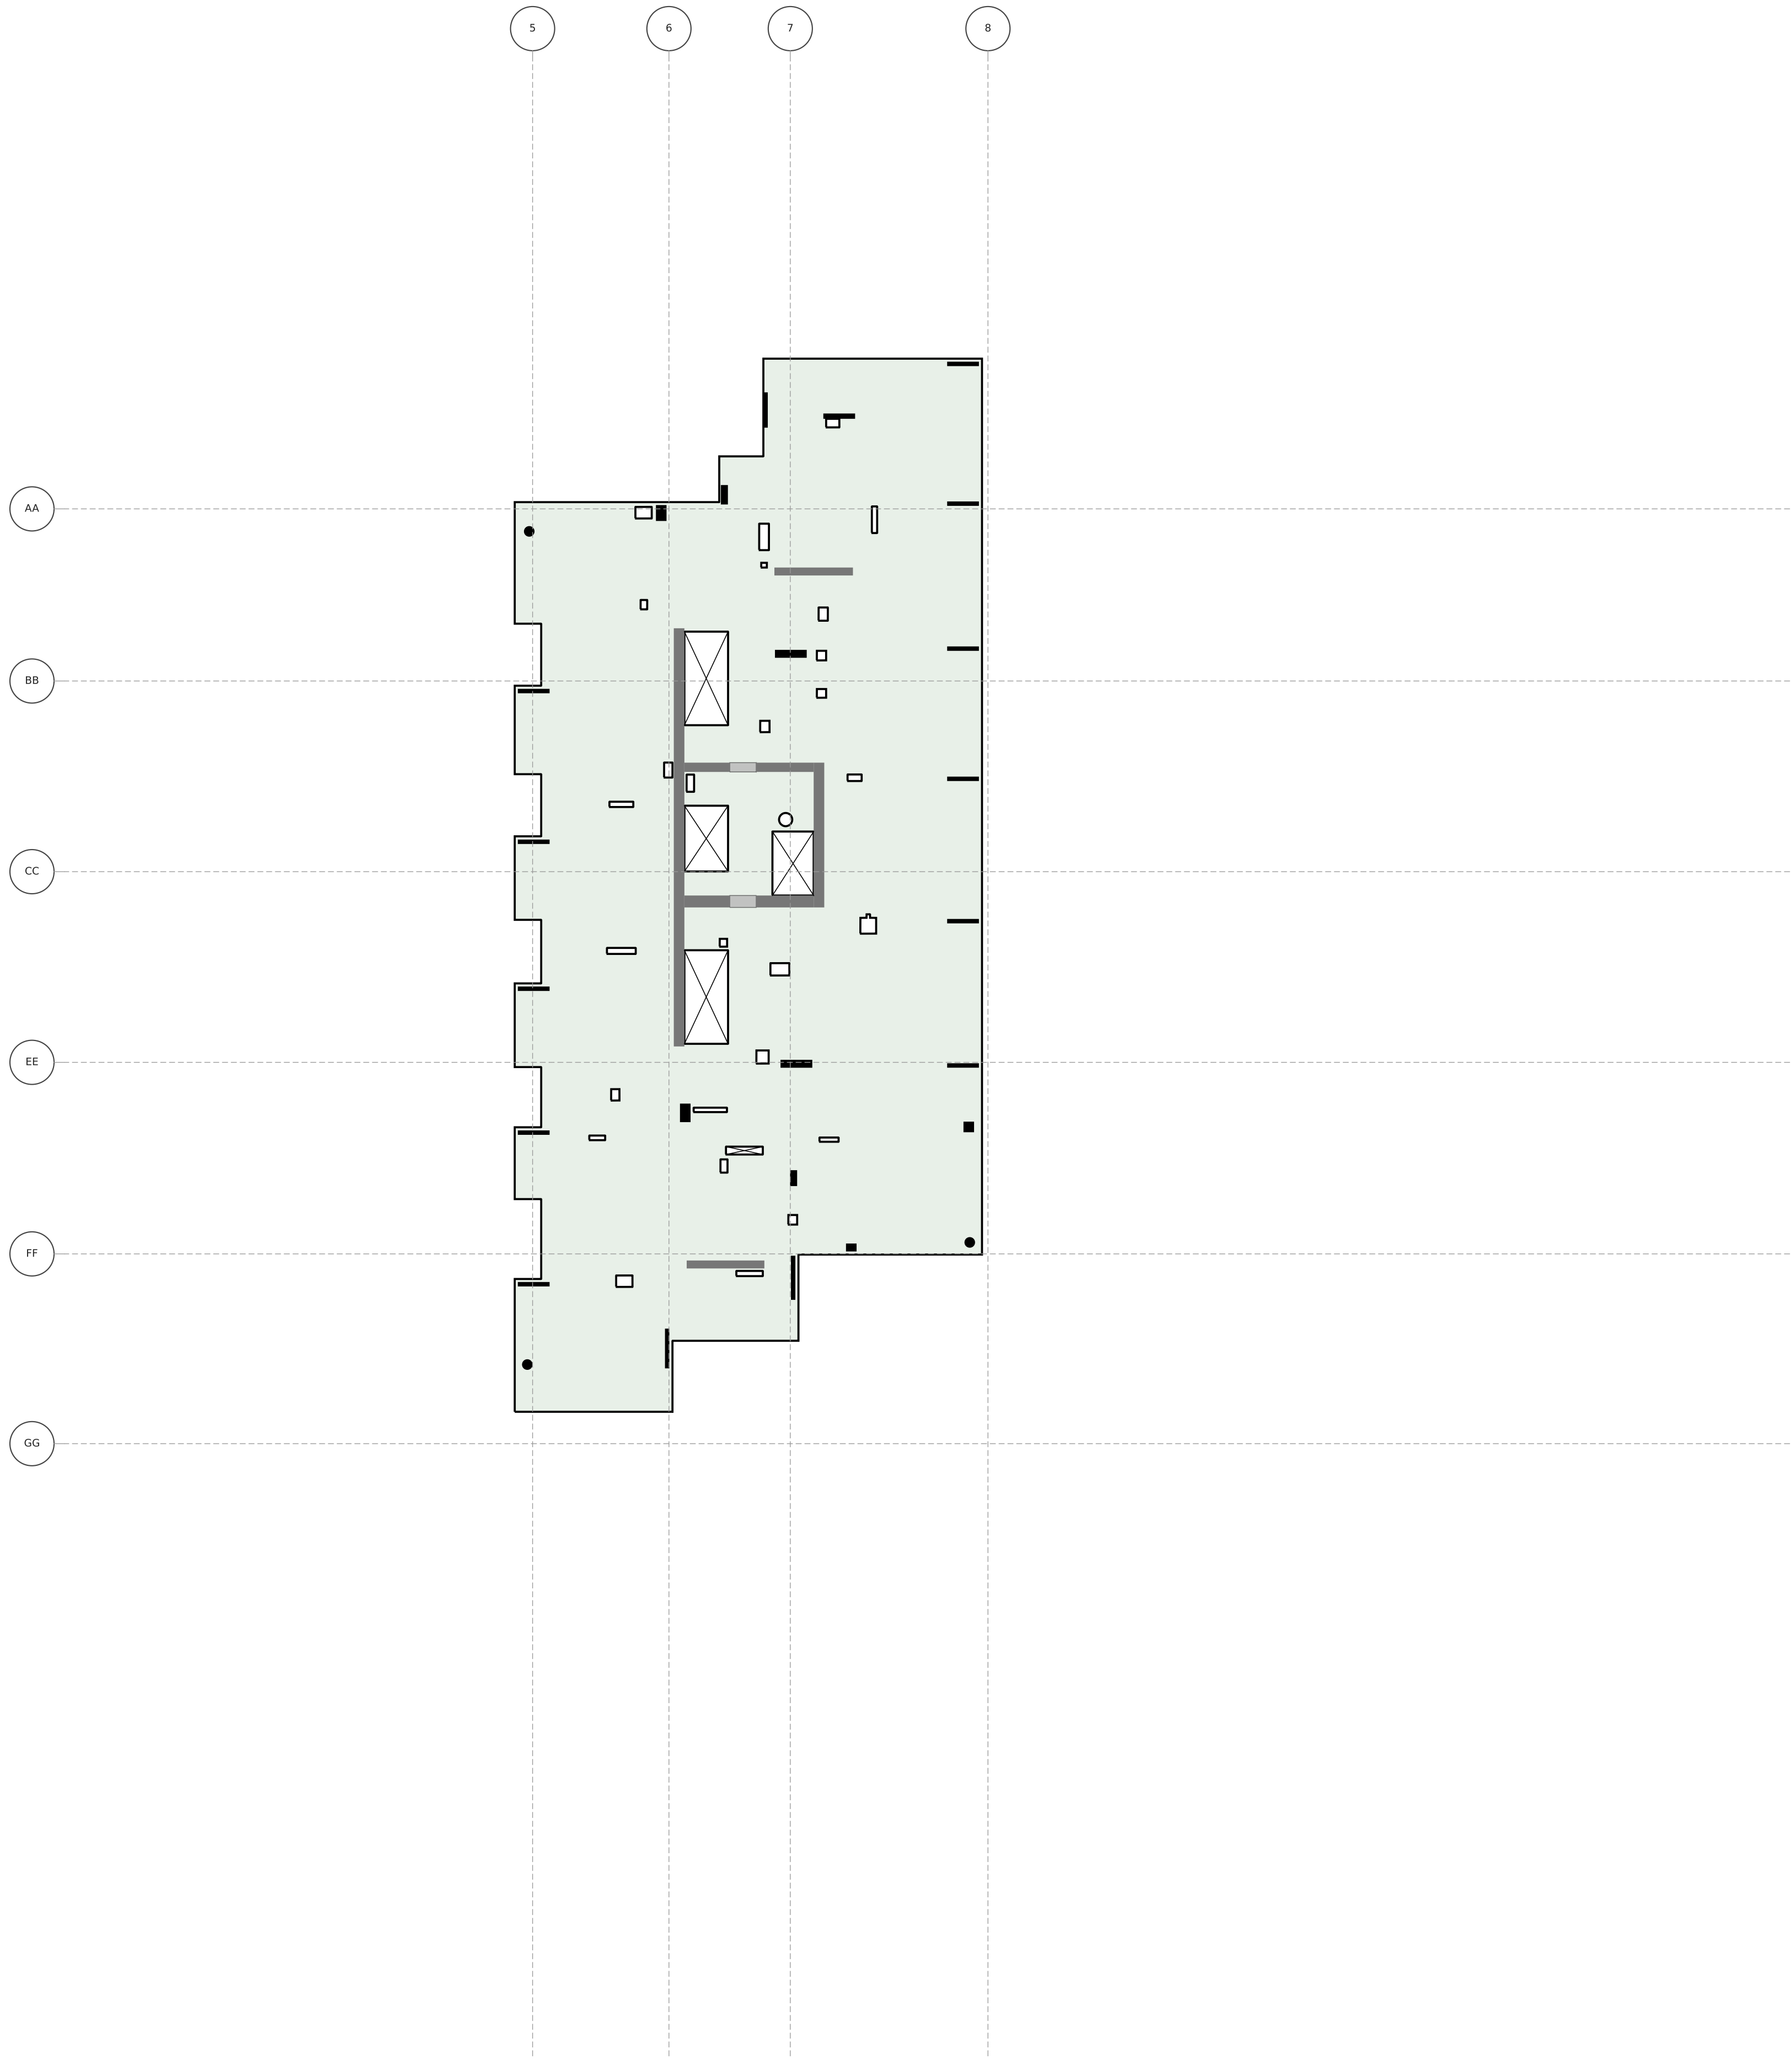


1268 KALAE

LEVEL 8 FLOOR PLAN

T.O.S. 178'-5" · typical slab 7.5" · scale 1" = 20'

Generated from 92743ac6-HI_KALAE_MCC_ST.ifc (Revit scope model) for the McClone Reshore Calculator — geometry only; loading marks are drawn in the calculator.

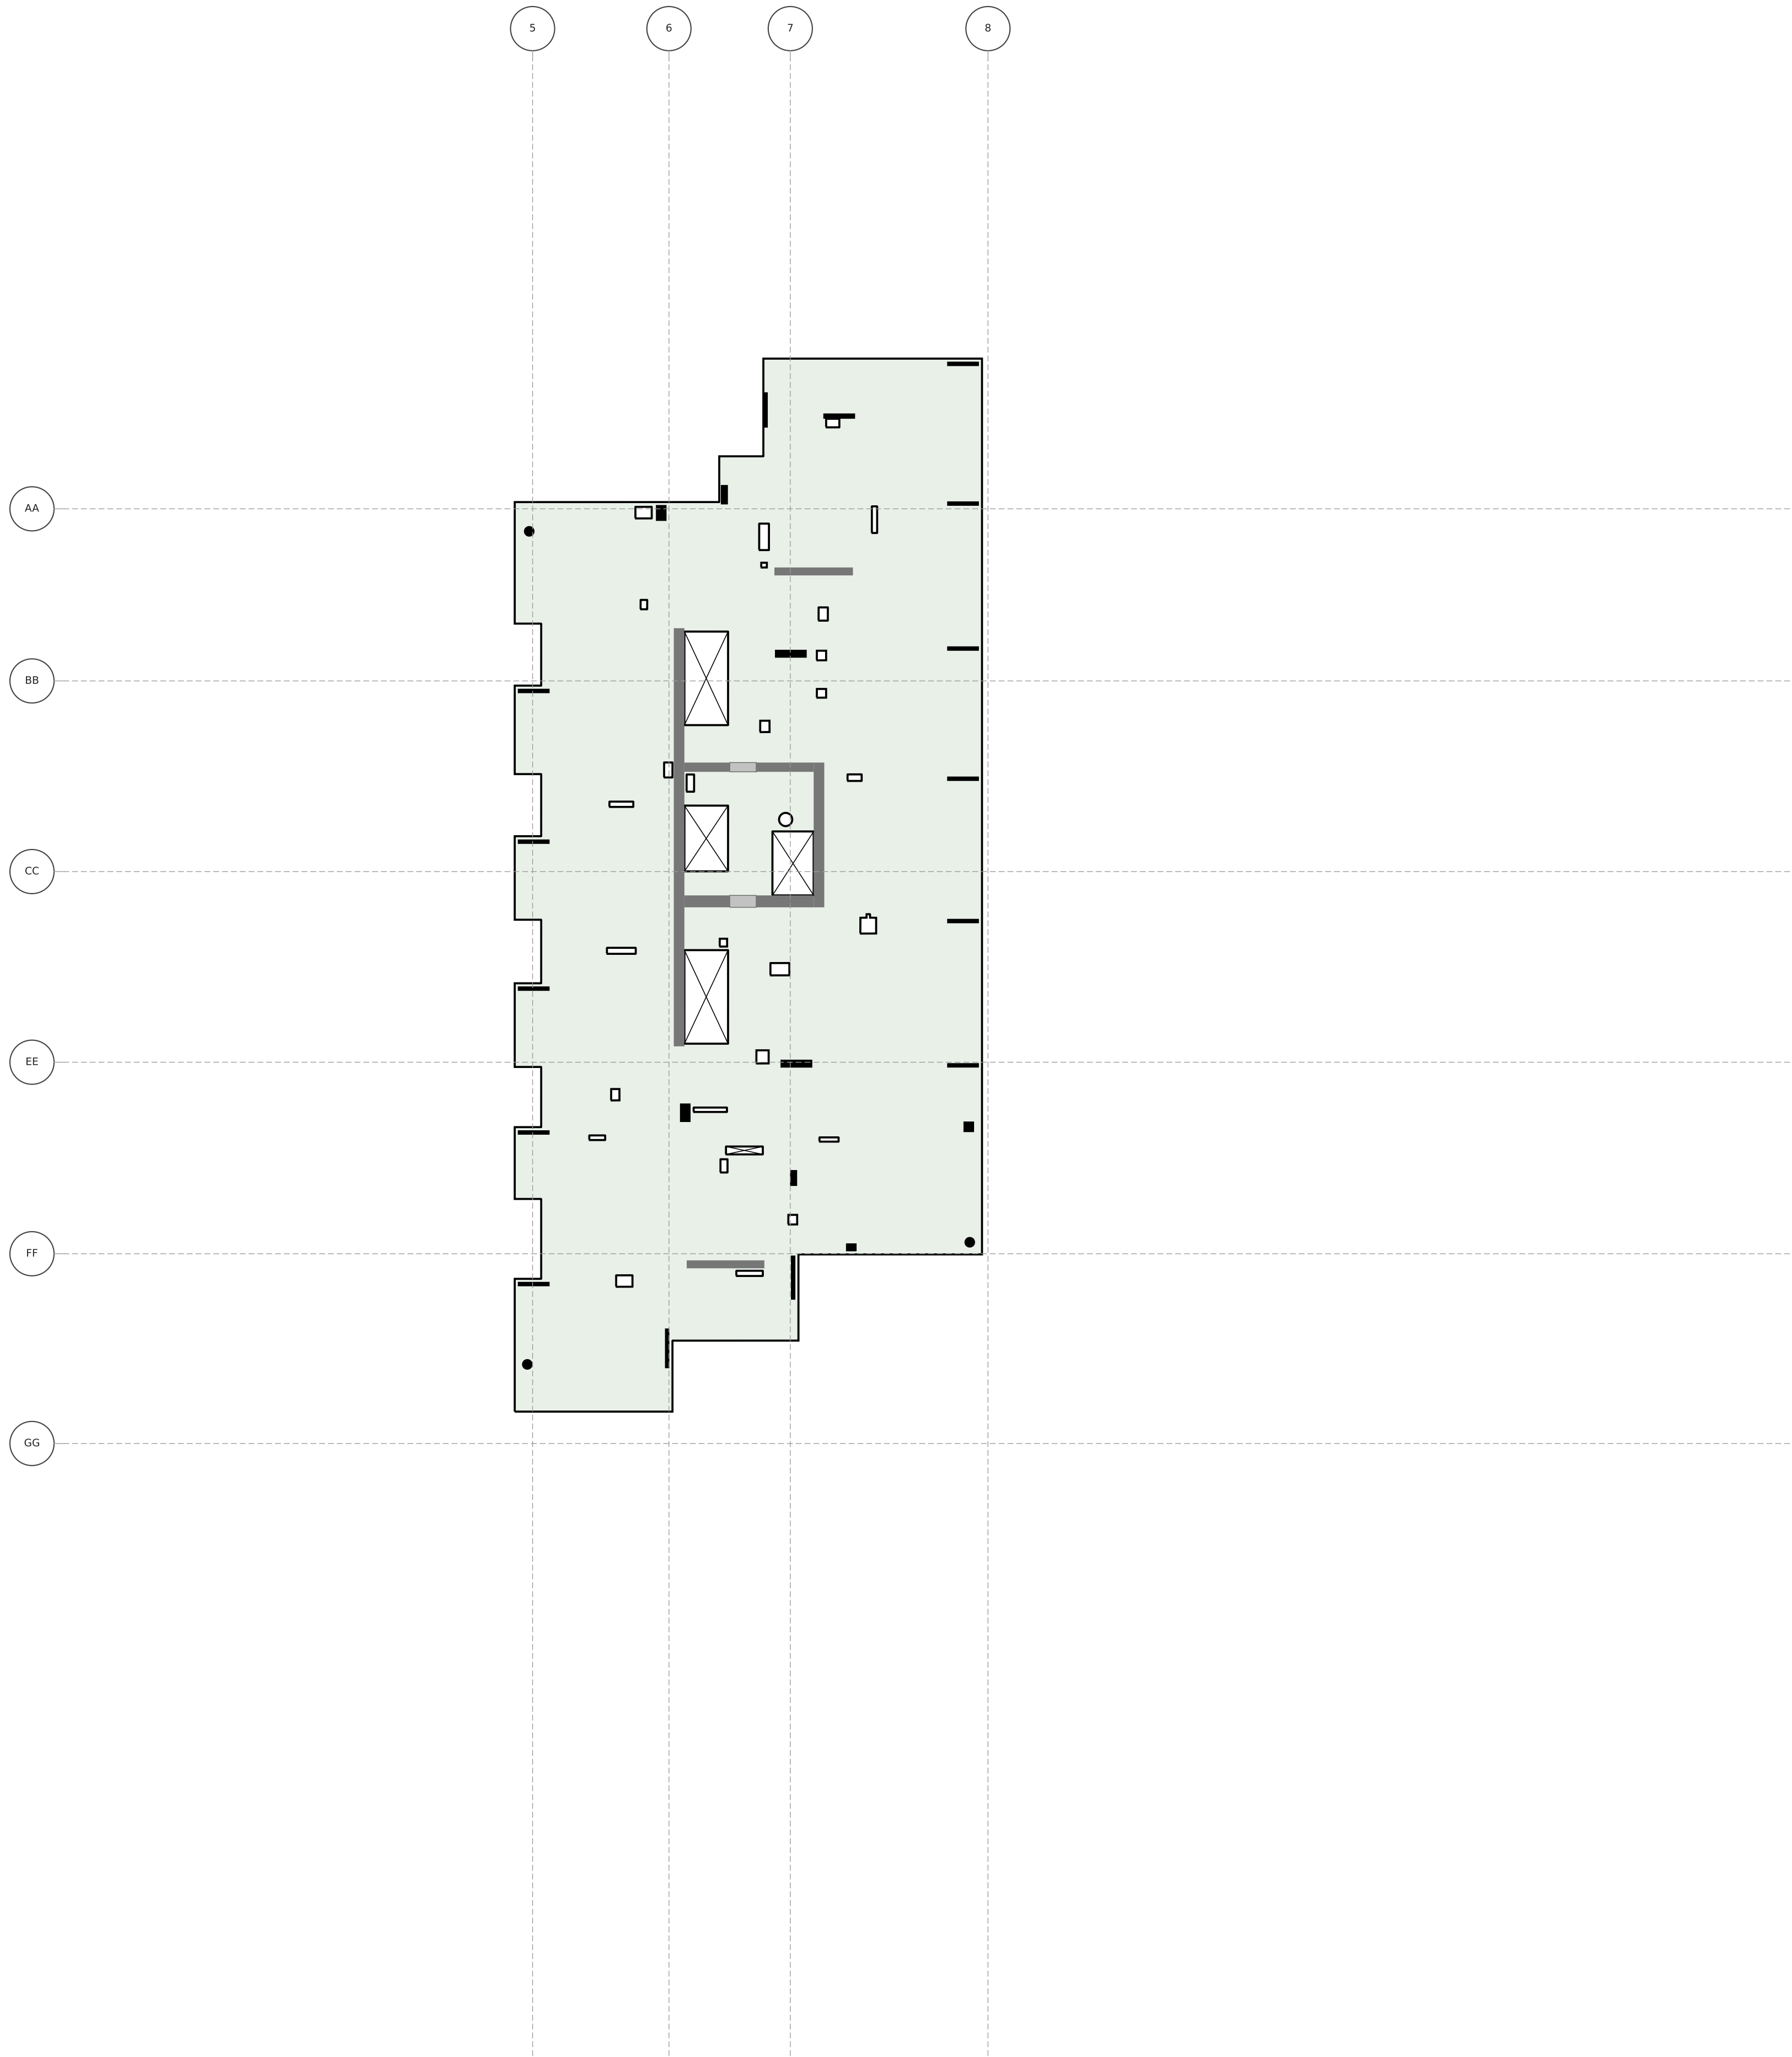


1268 KALAE

LEVEL 9 FLOOR PLAN

T.O.S. 188'-1.5" · typical slab 7.5" · scale 1" = 20'

Generated from 92743ac6-HI_KALAE_MCC_ST.ifc (Revit scope model) for the McClone Reshore Calculator — geometry only; loading marks are drawn in the calculator.

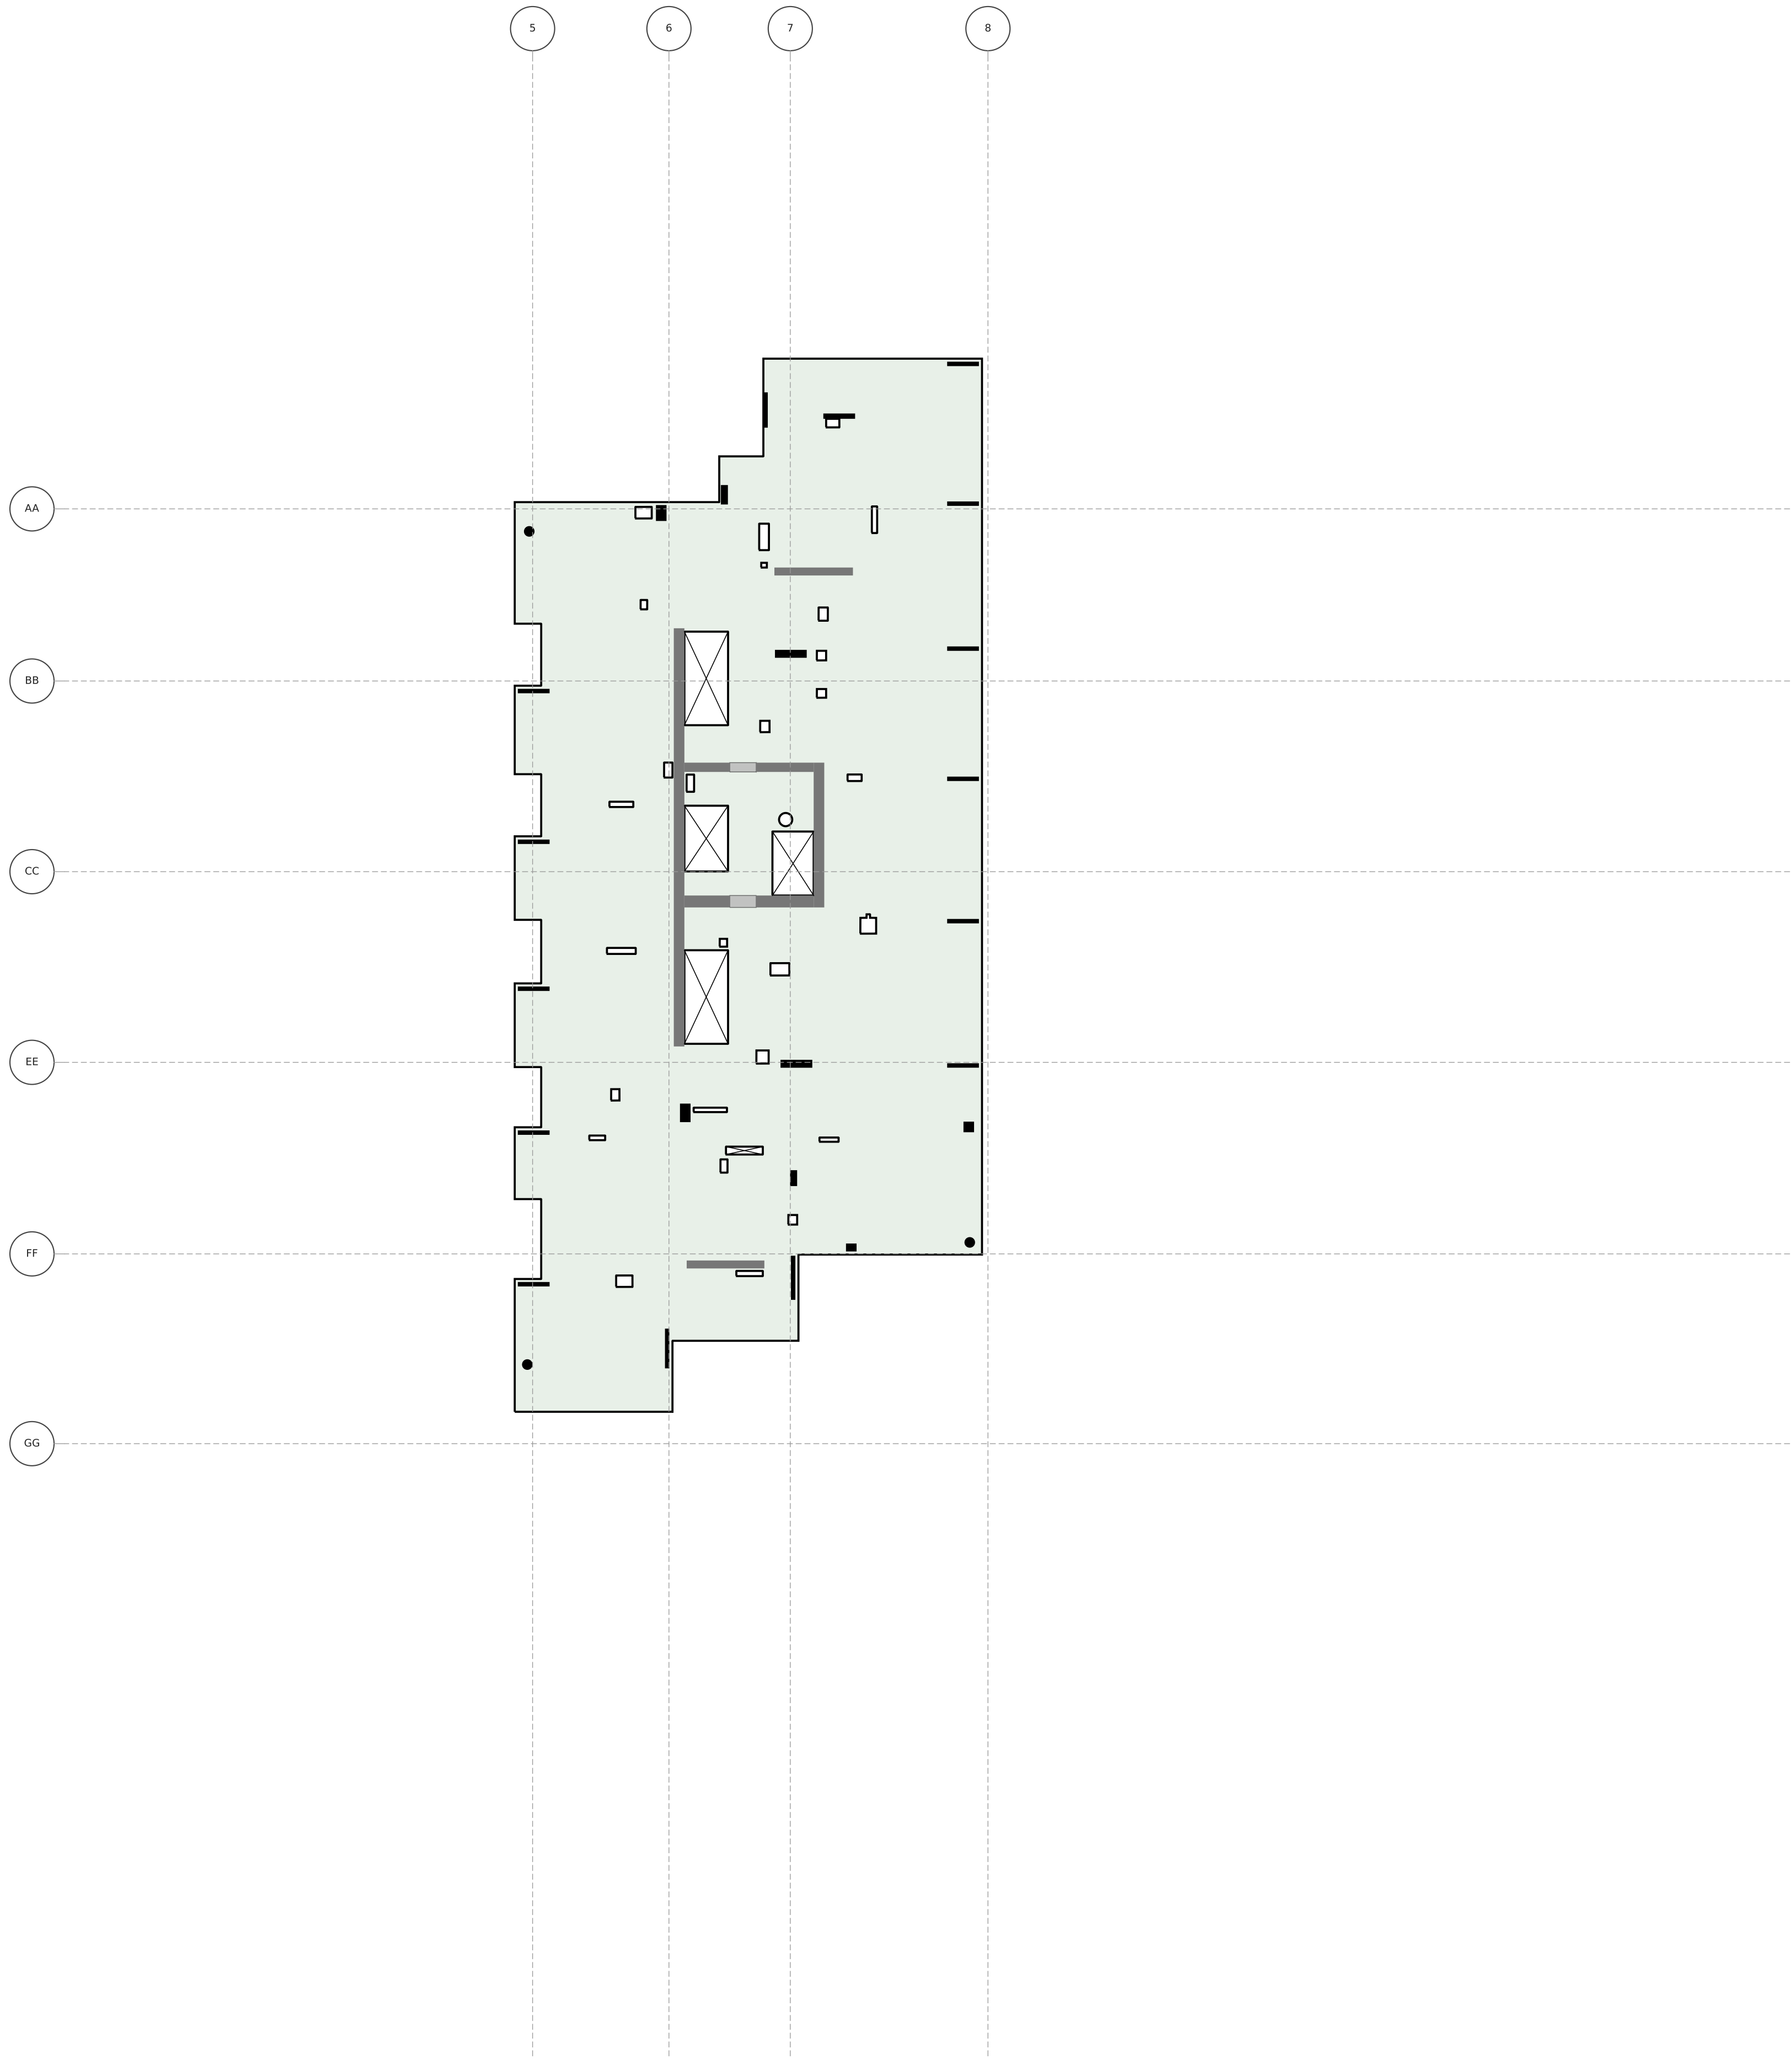


1268 KALAE

LEVEL 10 FLOOR PLAN

T.O.S. 197'-10" · typical slab 7.5" · scale 1" = 20'

Generated from 92743ac6-HI_KALAE_MCC_ST.ifc (Revit scope model) for the McClone Reshore Calculator — geometry only; loading marks are drawn in the calculator.

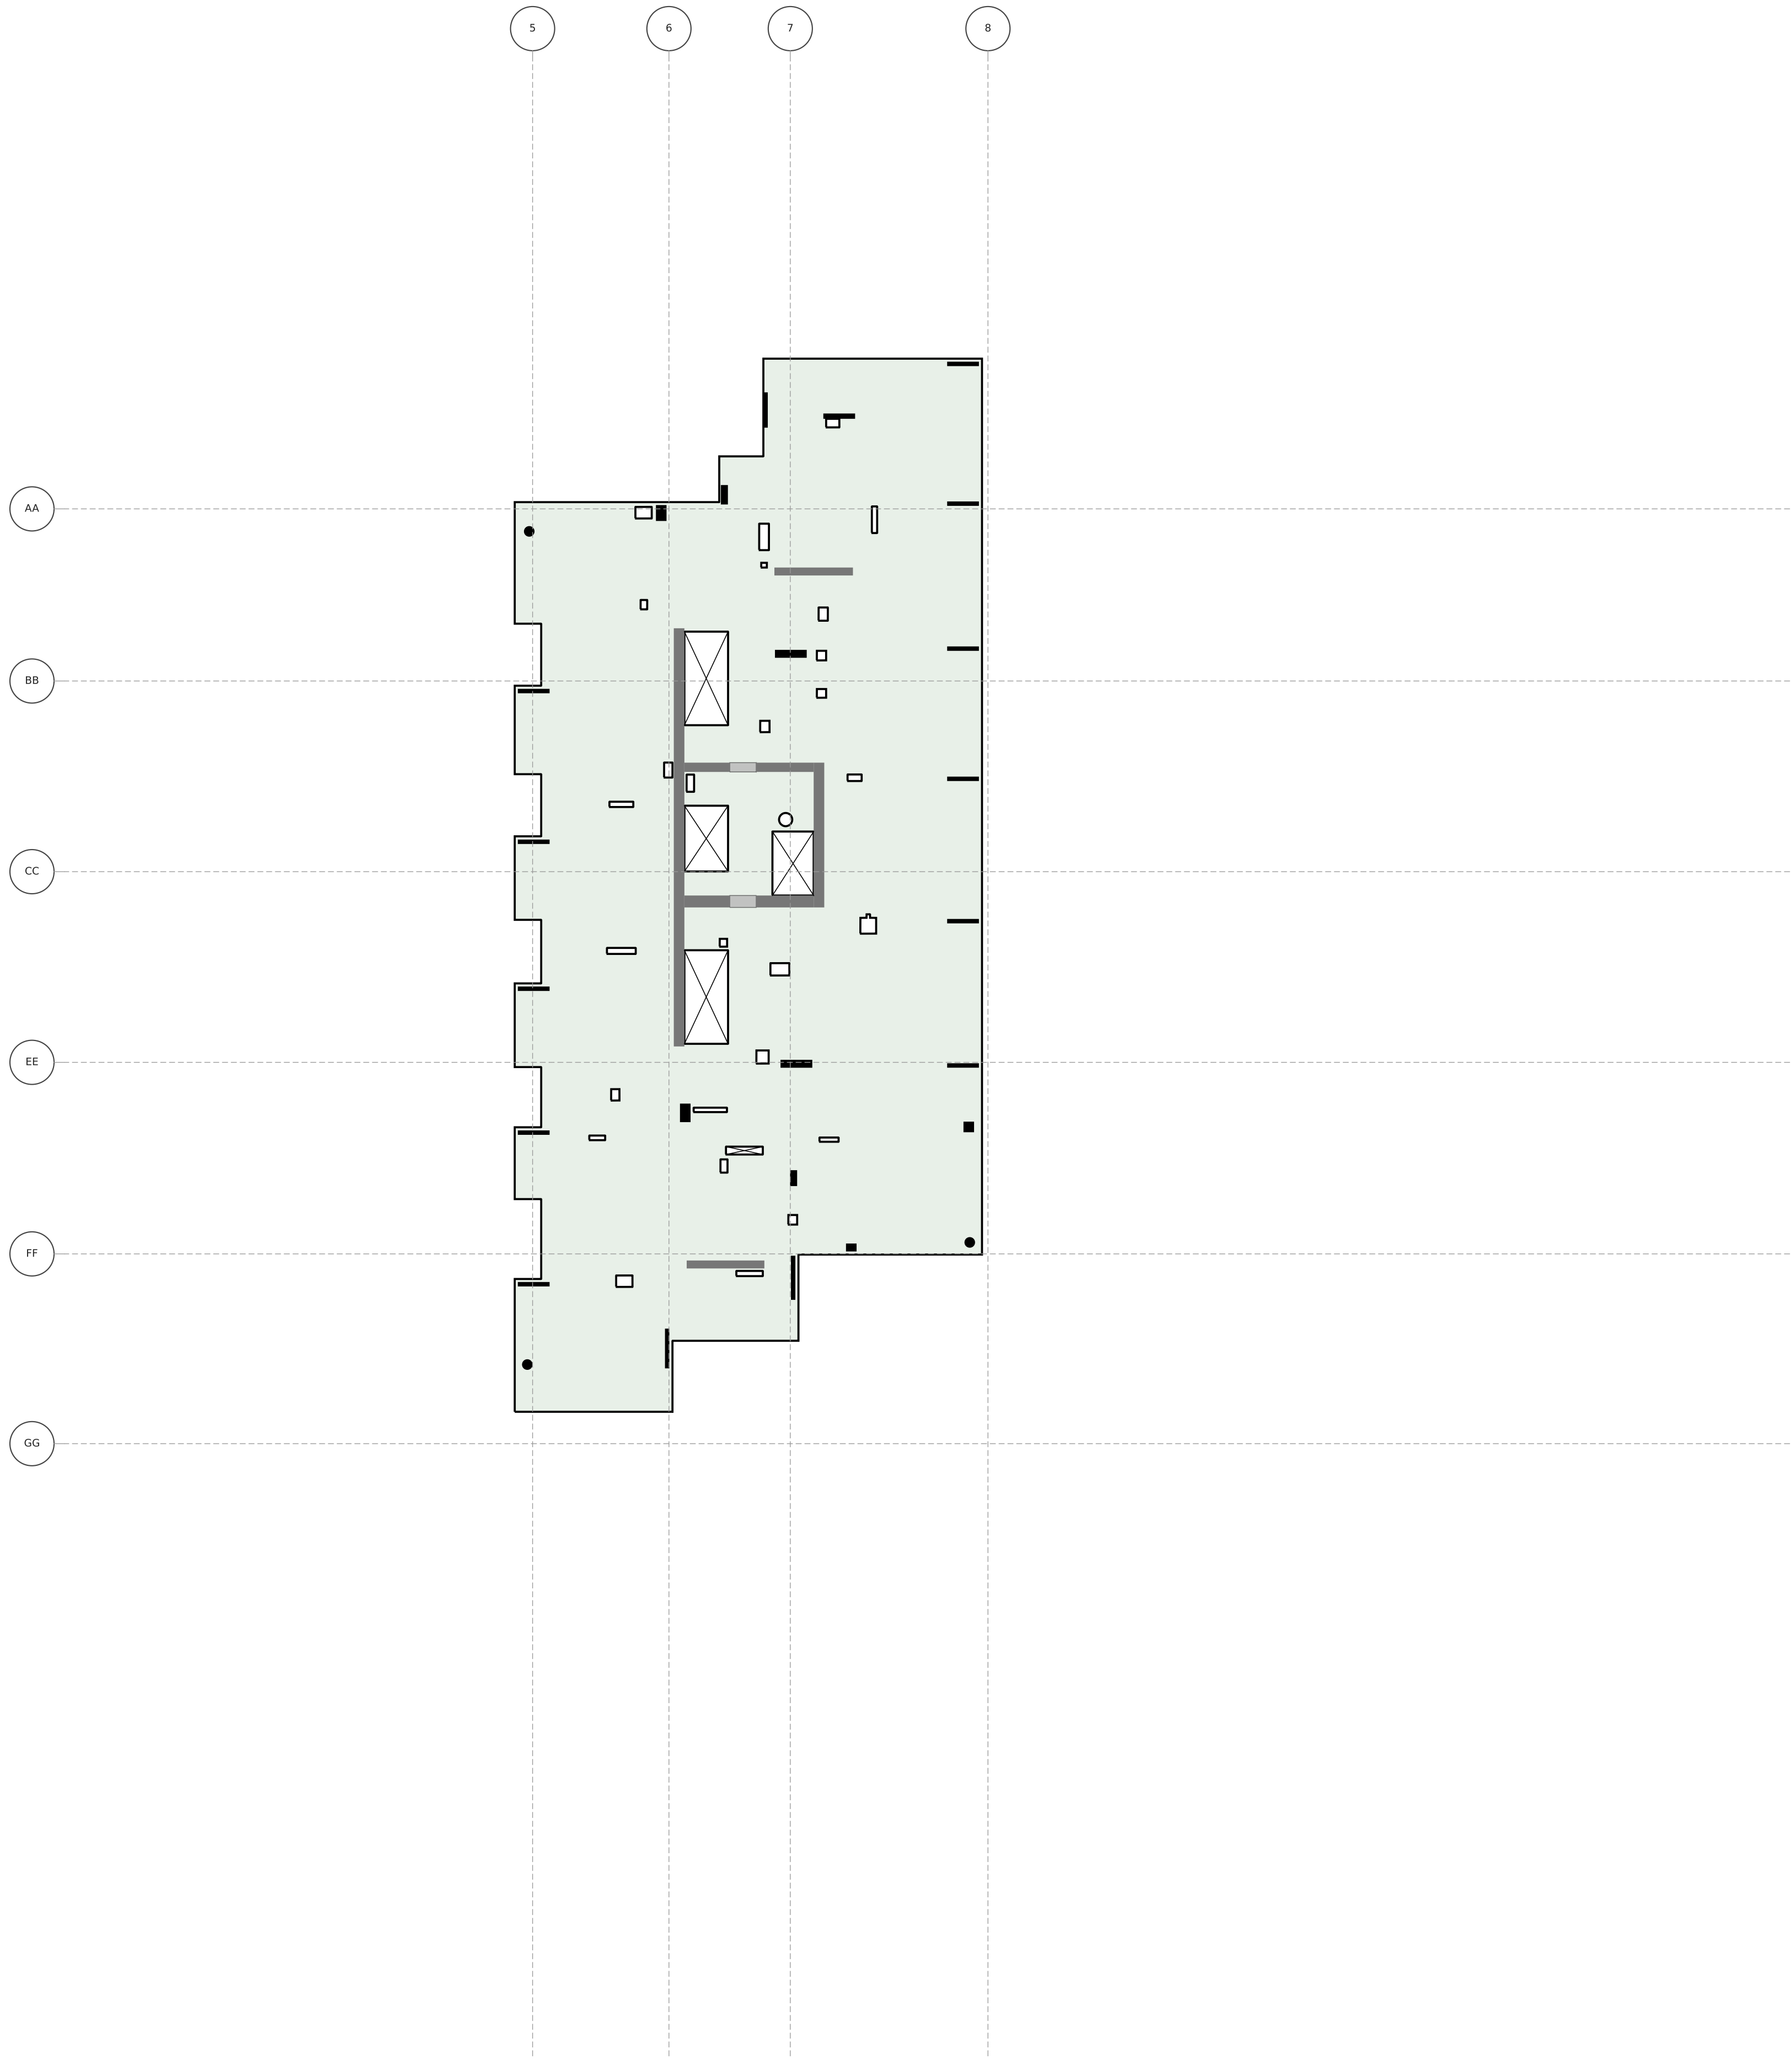


1268 KALAE

LEVEL 11 FLOOR PLAN

T.O.S. 207'-6.5" · typical slab 7.5" · scale 1" = 20'

Generated from 92743ac6-HI_KALAE_MCC_ST.ifc (Revit scope model) for the McClone Reshore Calculator — geometry only; loading marks are drawn in the calculator.

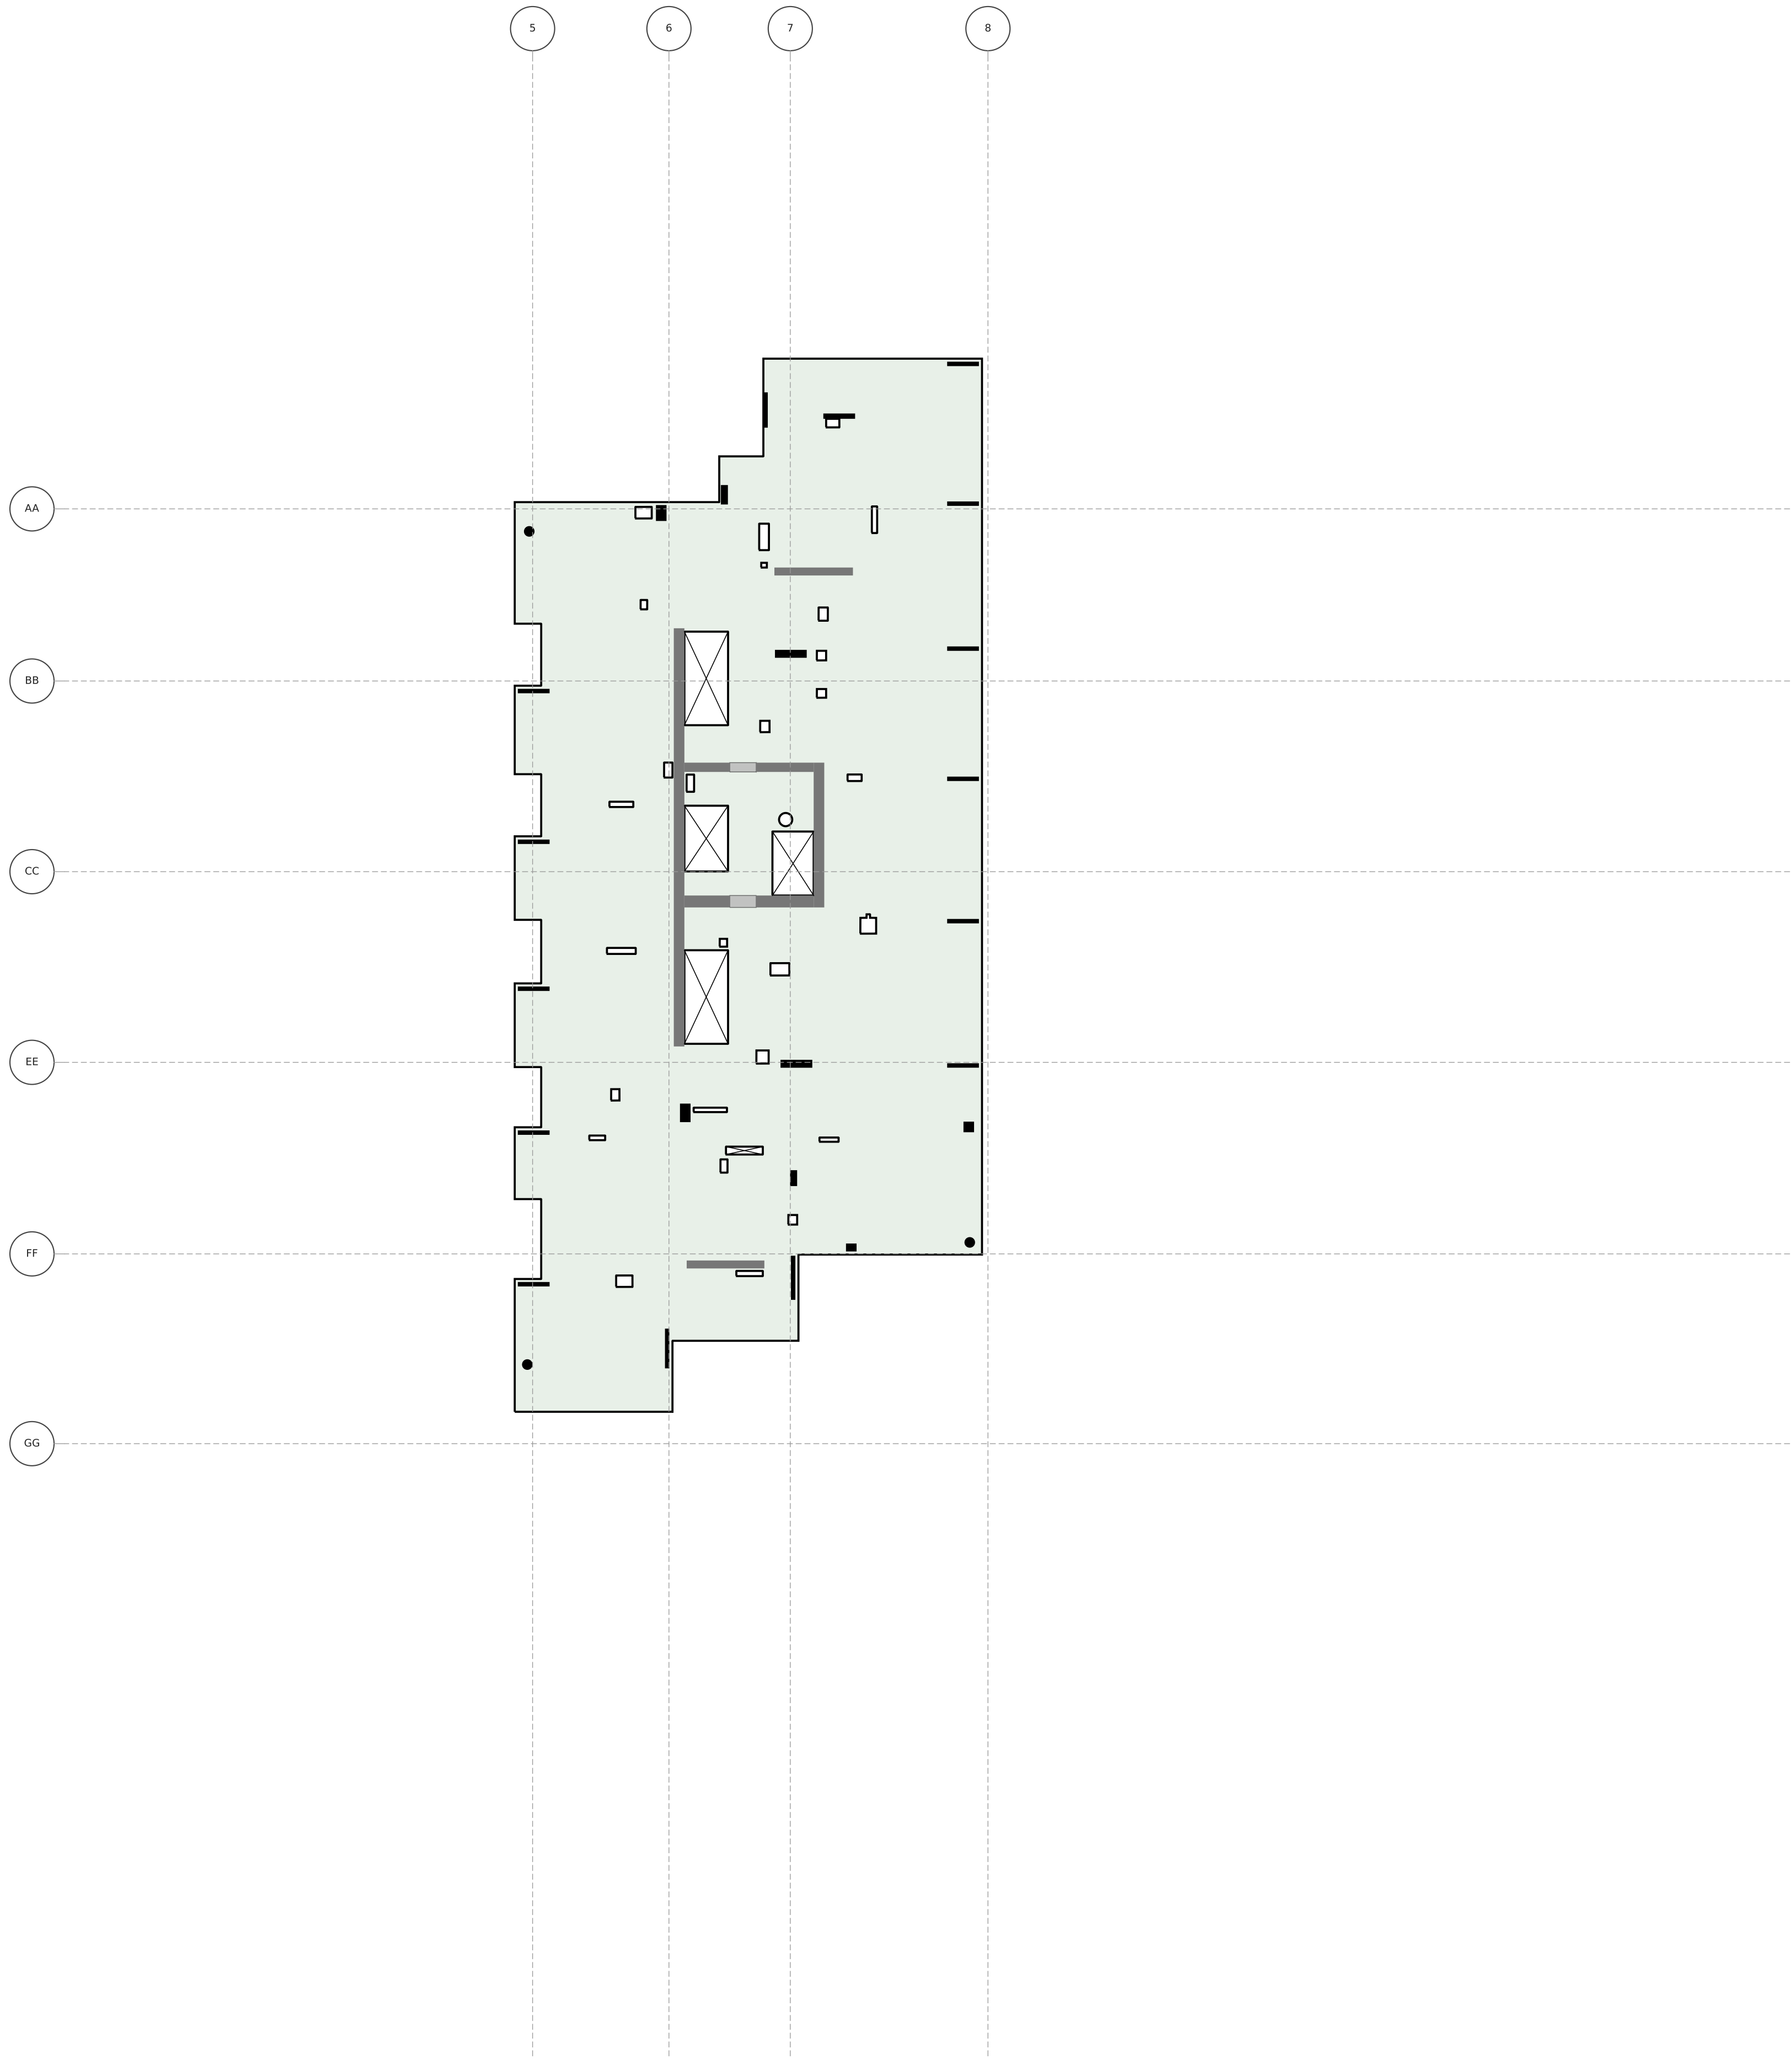


1268 KALAE

LEVEL 12 FLOOR PLAN

T.O.S. 217'-3" · typical slab 7.5" · scale 1" = 20'

Generated from 92743ac6-HI_KALAE_MCC_ST.ifc (Revit scope model) for the McClone Reshore Calculator — geometry only; loading marks are drawn in the calculator.

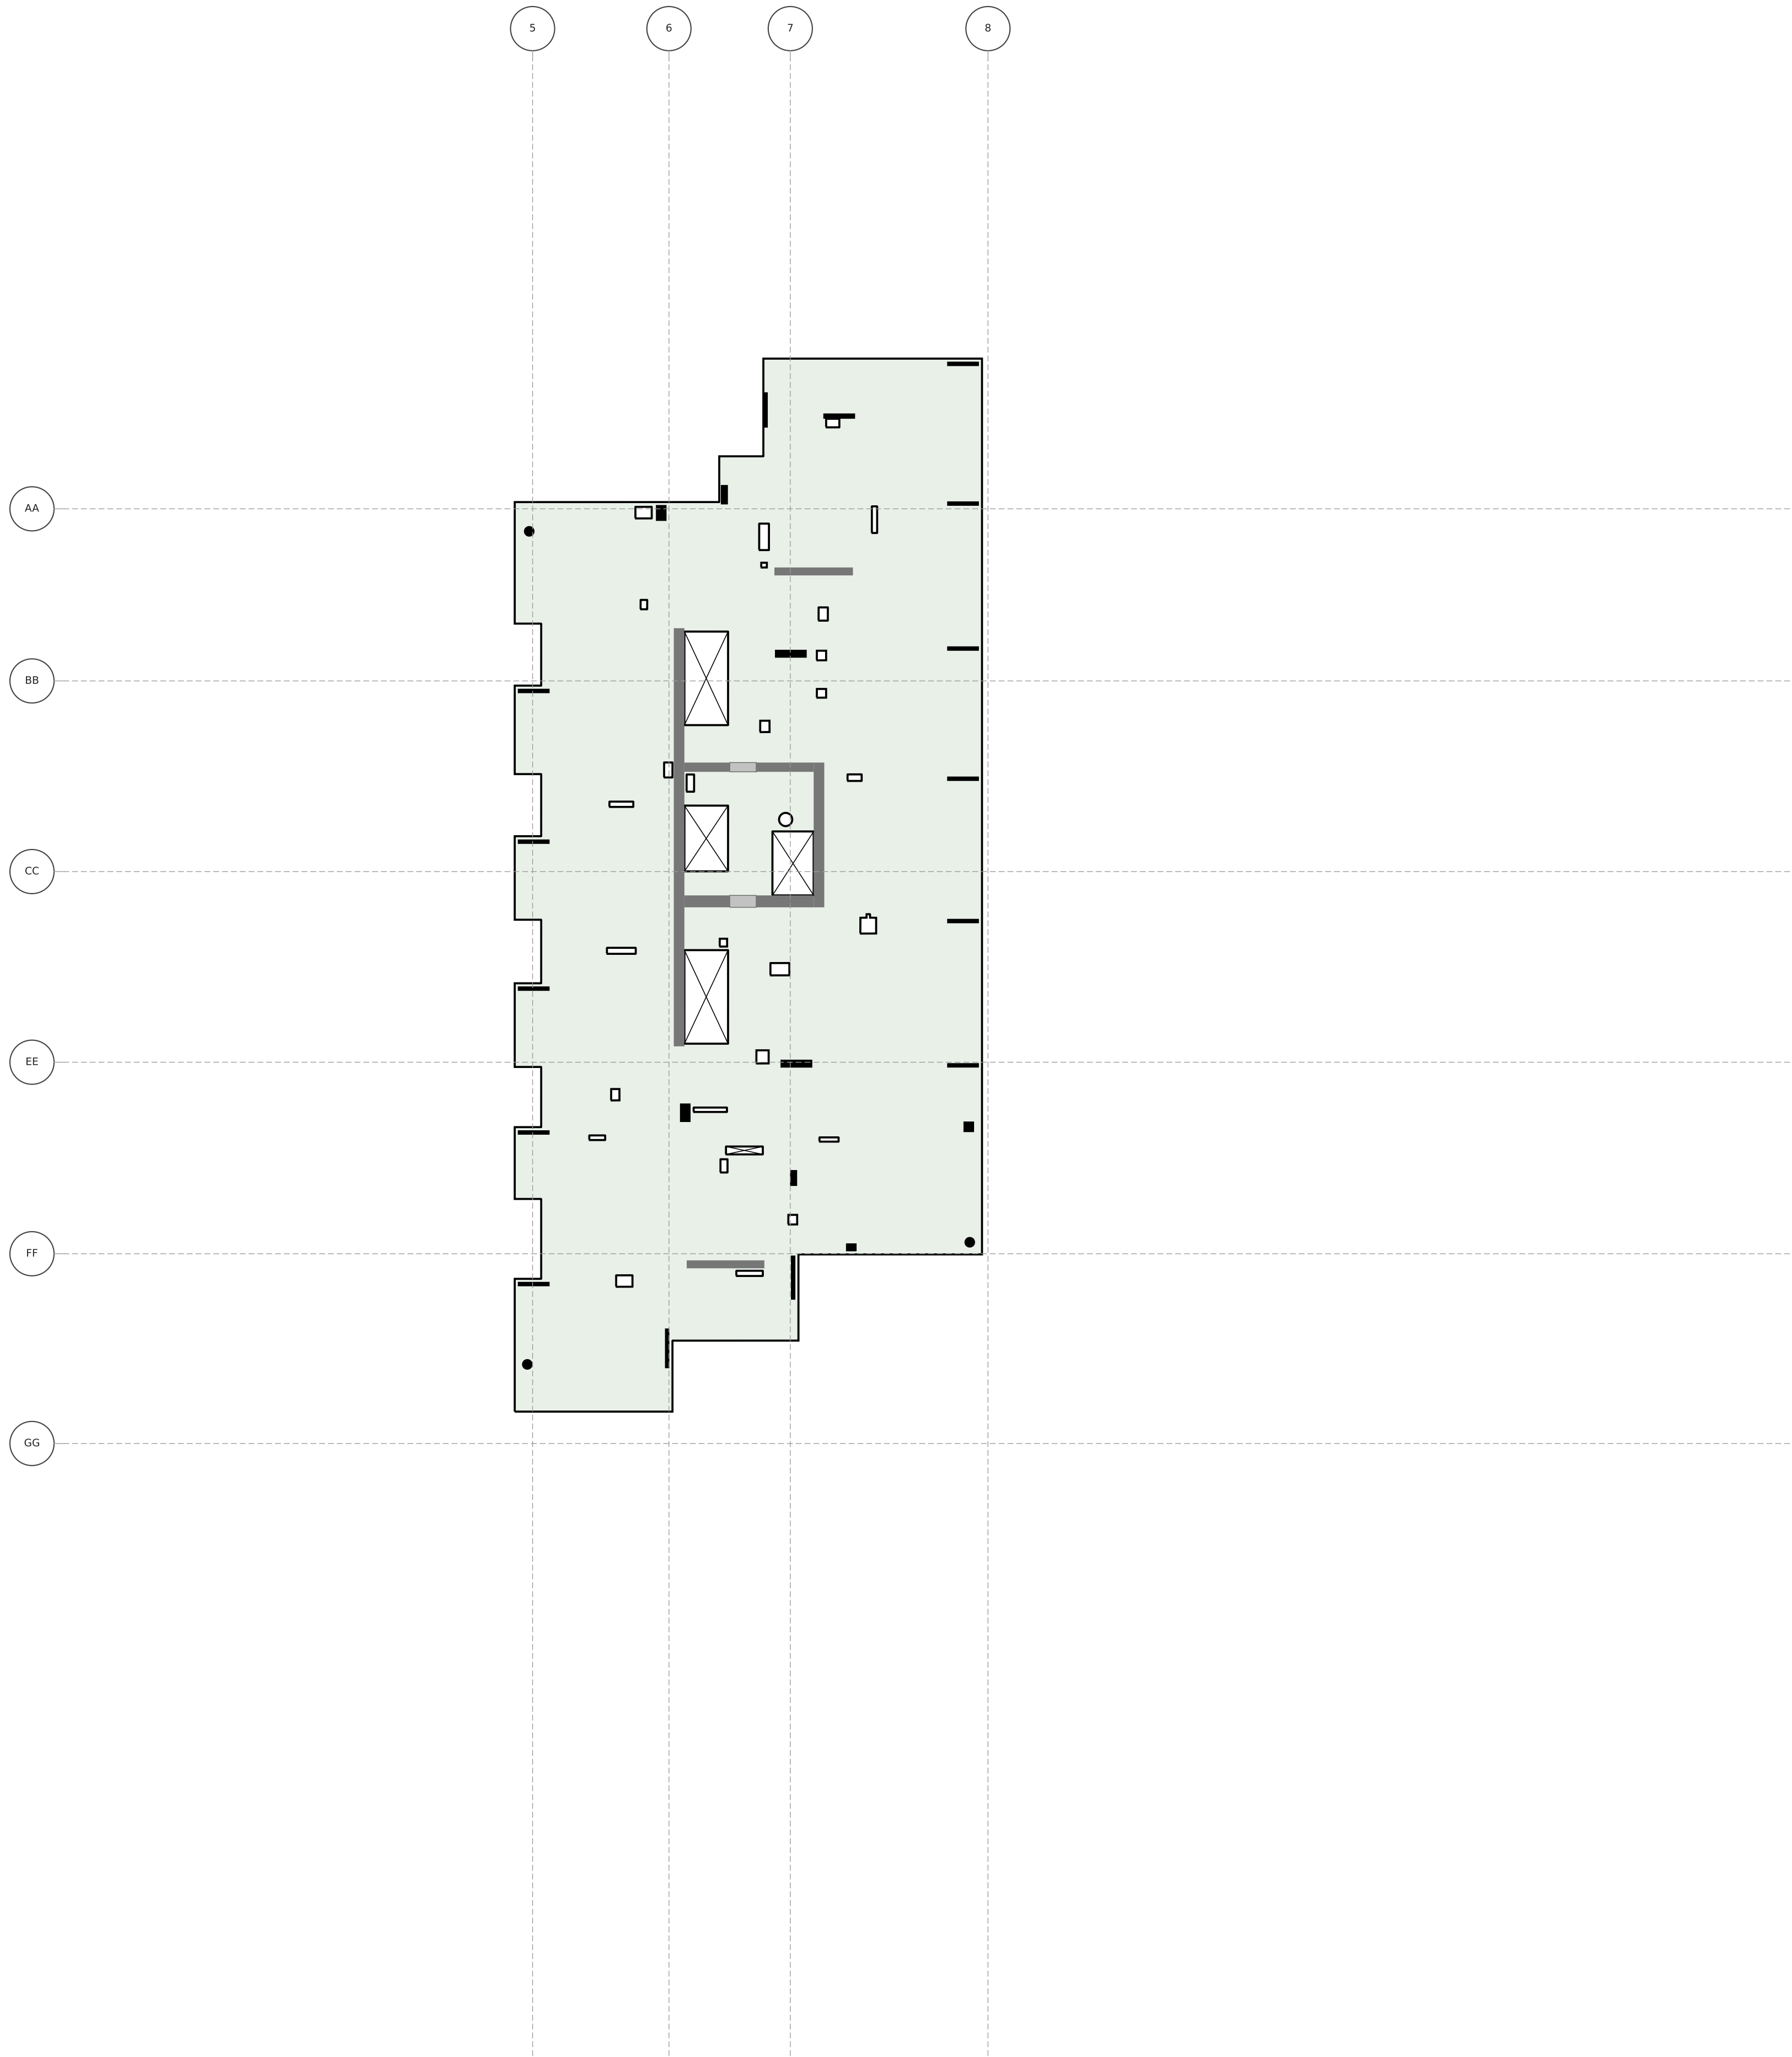


1268 KALAE

LEVEL 13 FLOOR PLAN

T.O.S. 226'-11.5" · typical slab 7.5" · scale 1" = 20'

Generated from 92743ac6-HI_KALAE_MCC_ST.ifc (Revit scope model) for the McClone Reshore Calculator — geometry only; loading marks are drawn in the calculator.

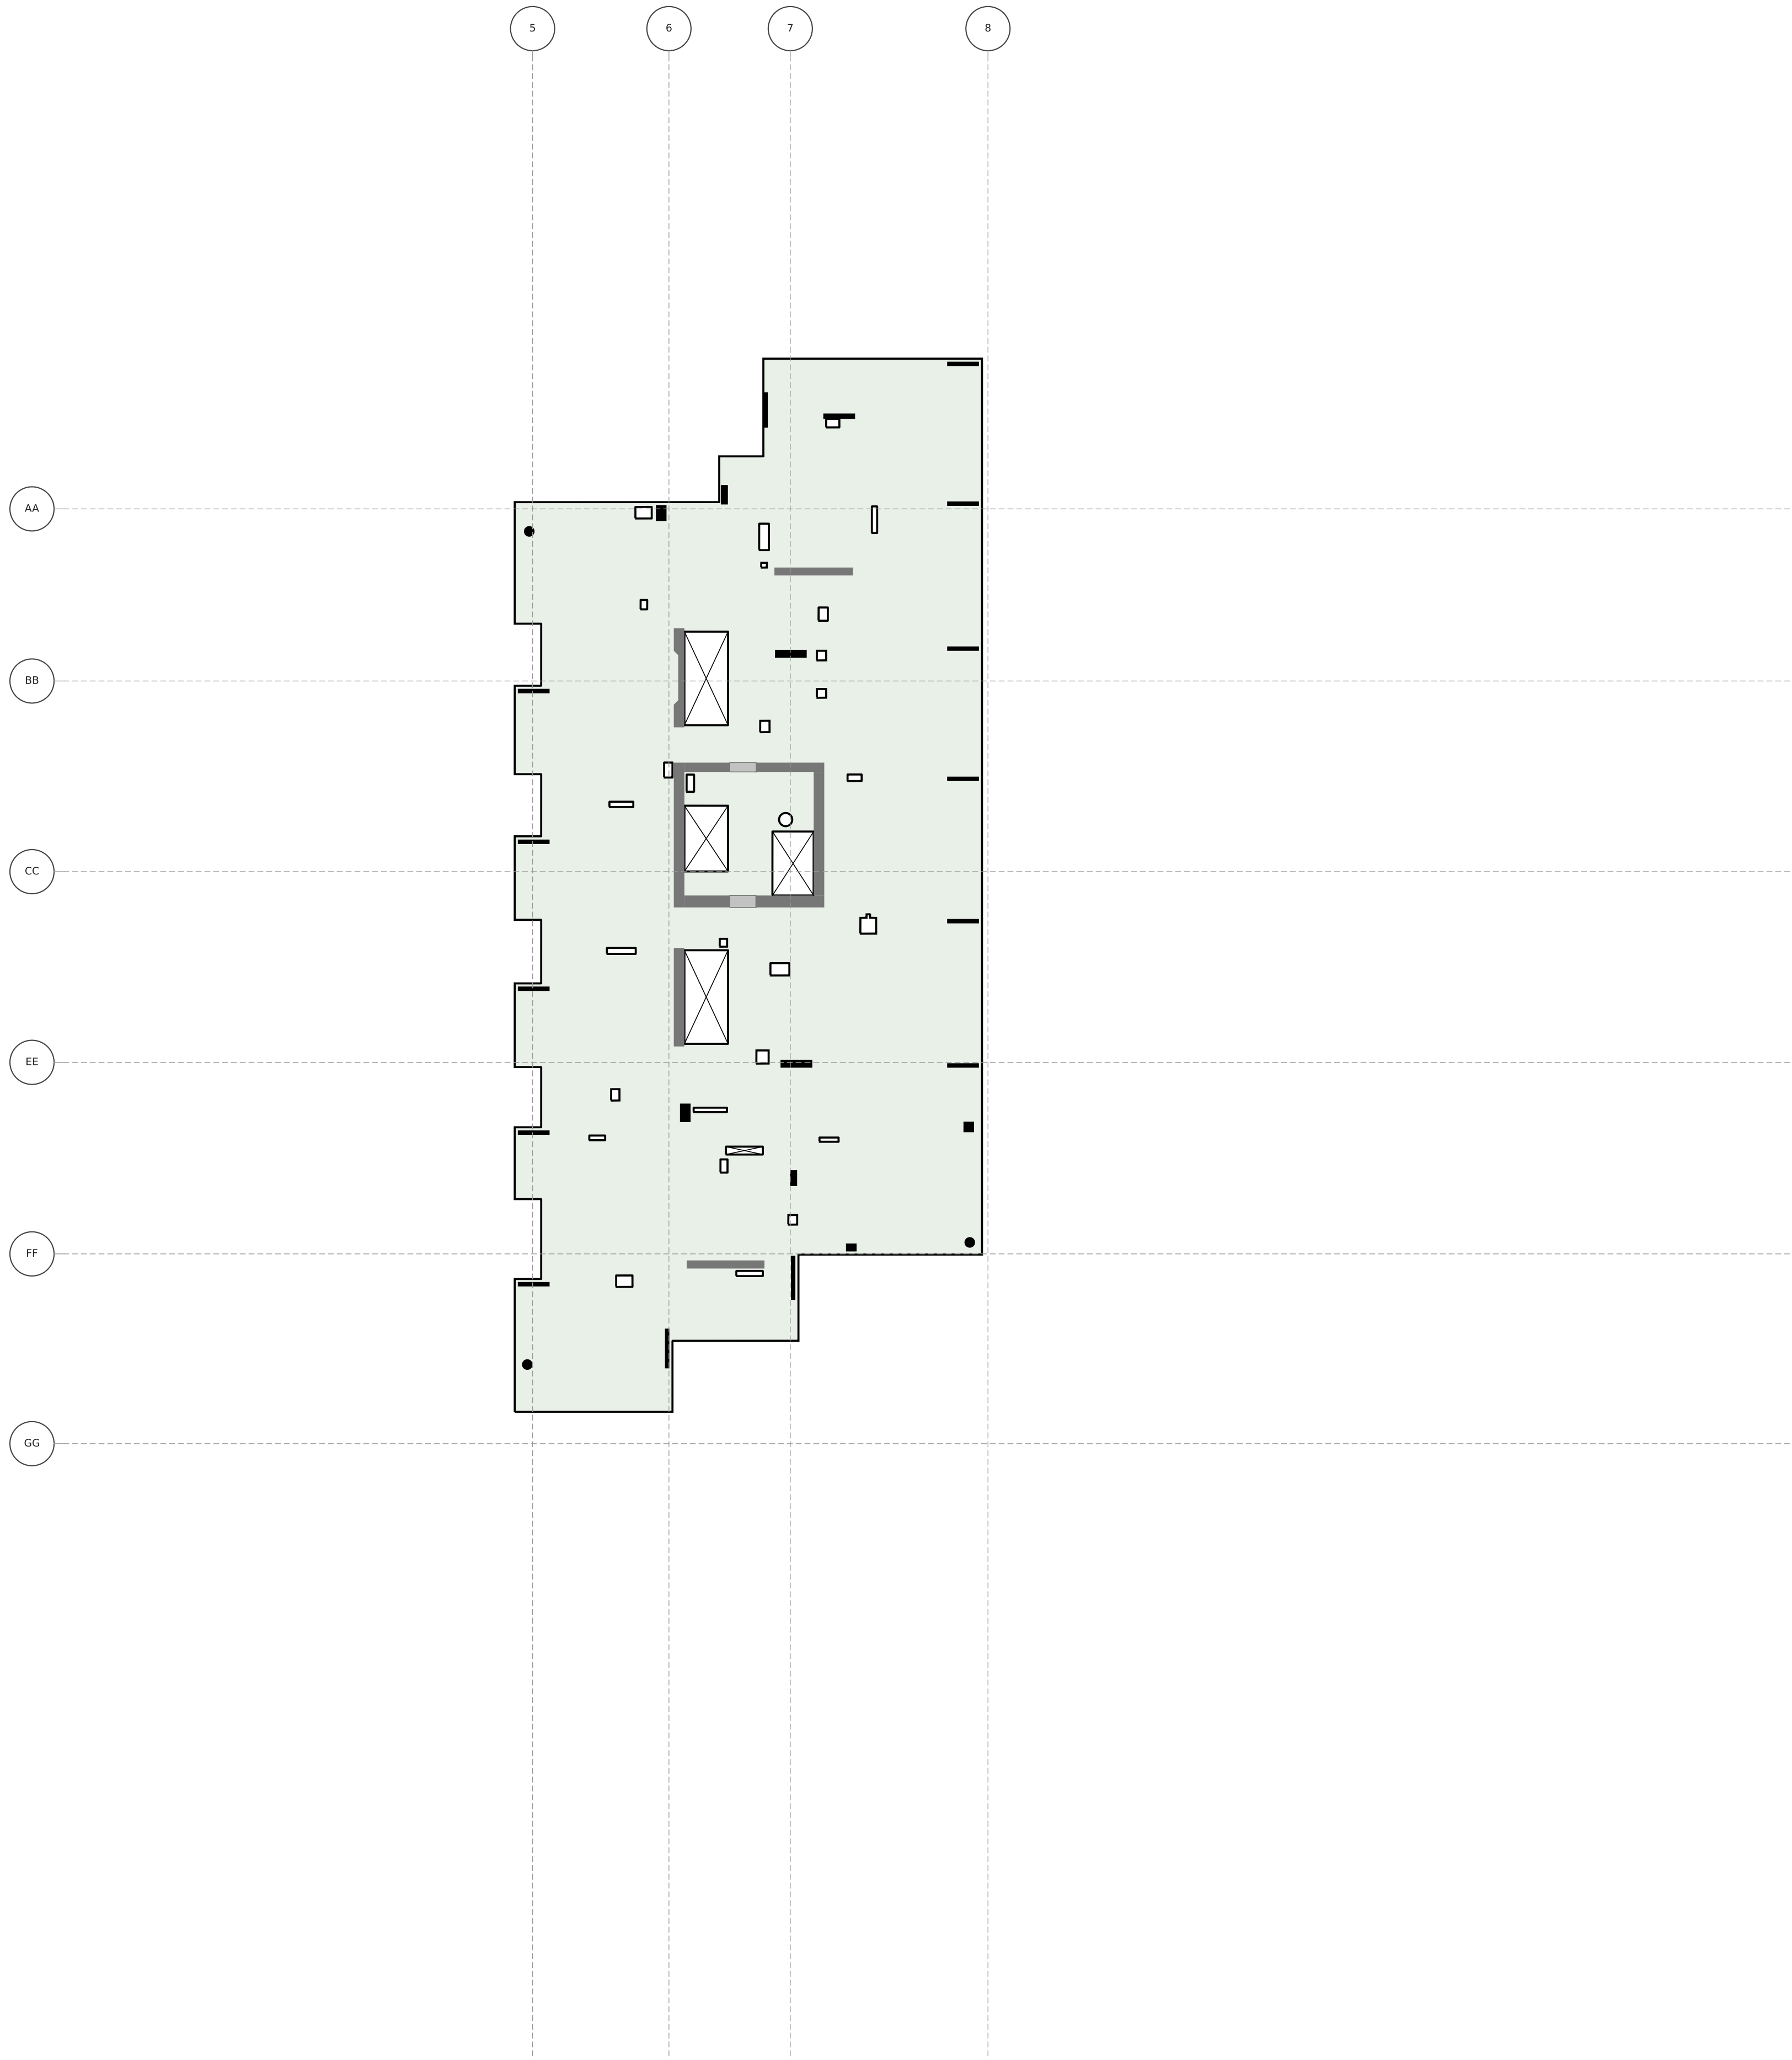


1268 KALAE

LEVEL 14 FLOOR PLAN

T.O.S. 236'-8" · typical slab 7.5" · scale 1" = 20'

Generated from 92743ac6-HI_KALAE_MCC_ST.ifc (Revit scope model) for the McClone Reshore Calculator — geometry only; loading marks are drawn in the calculator.

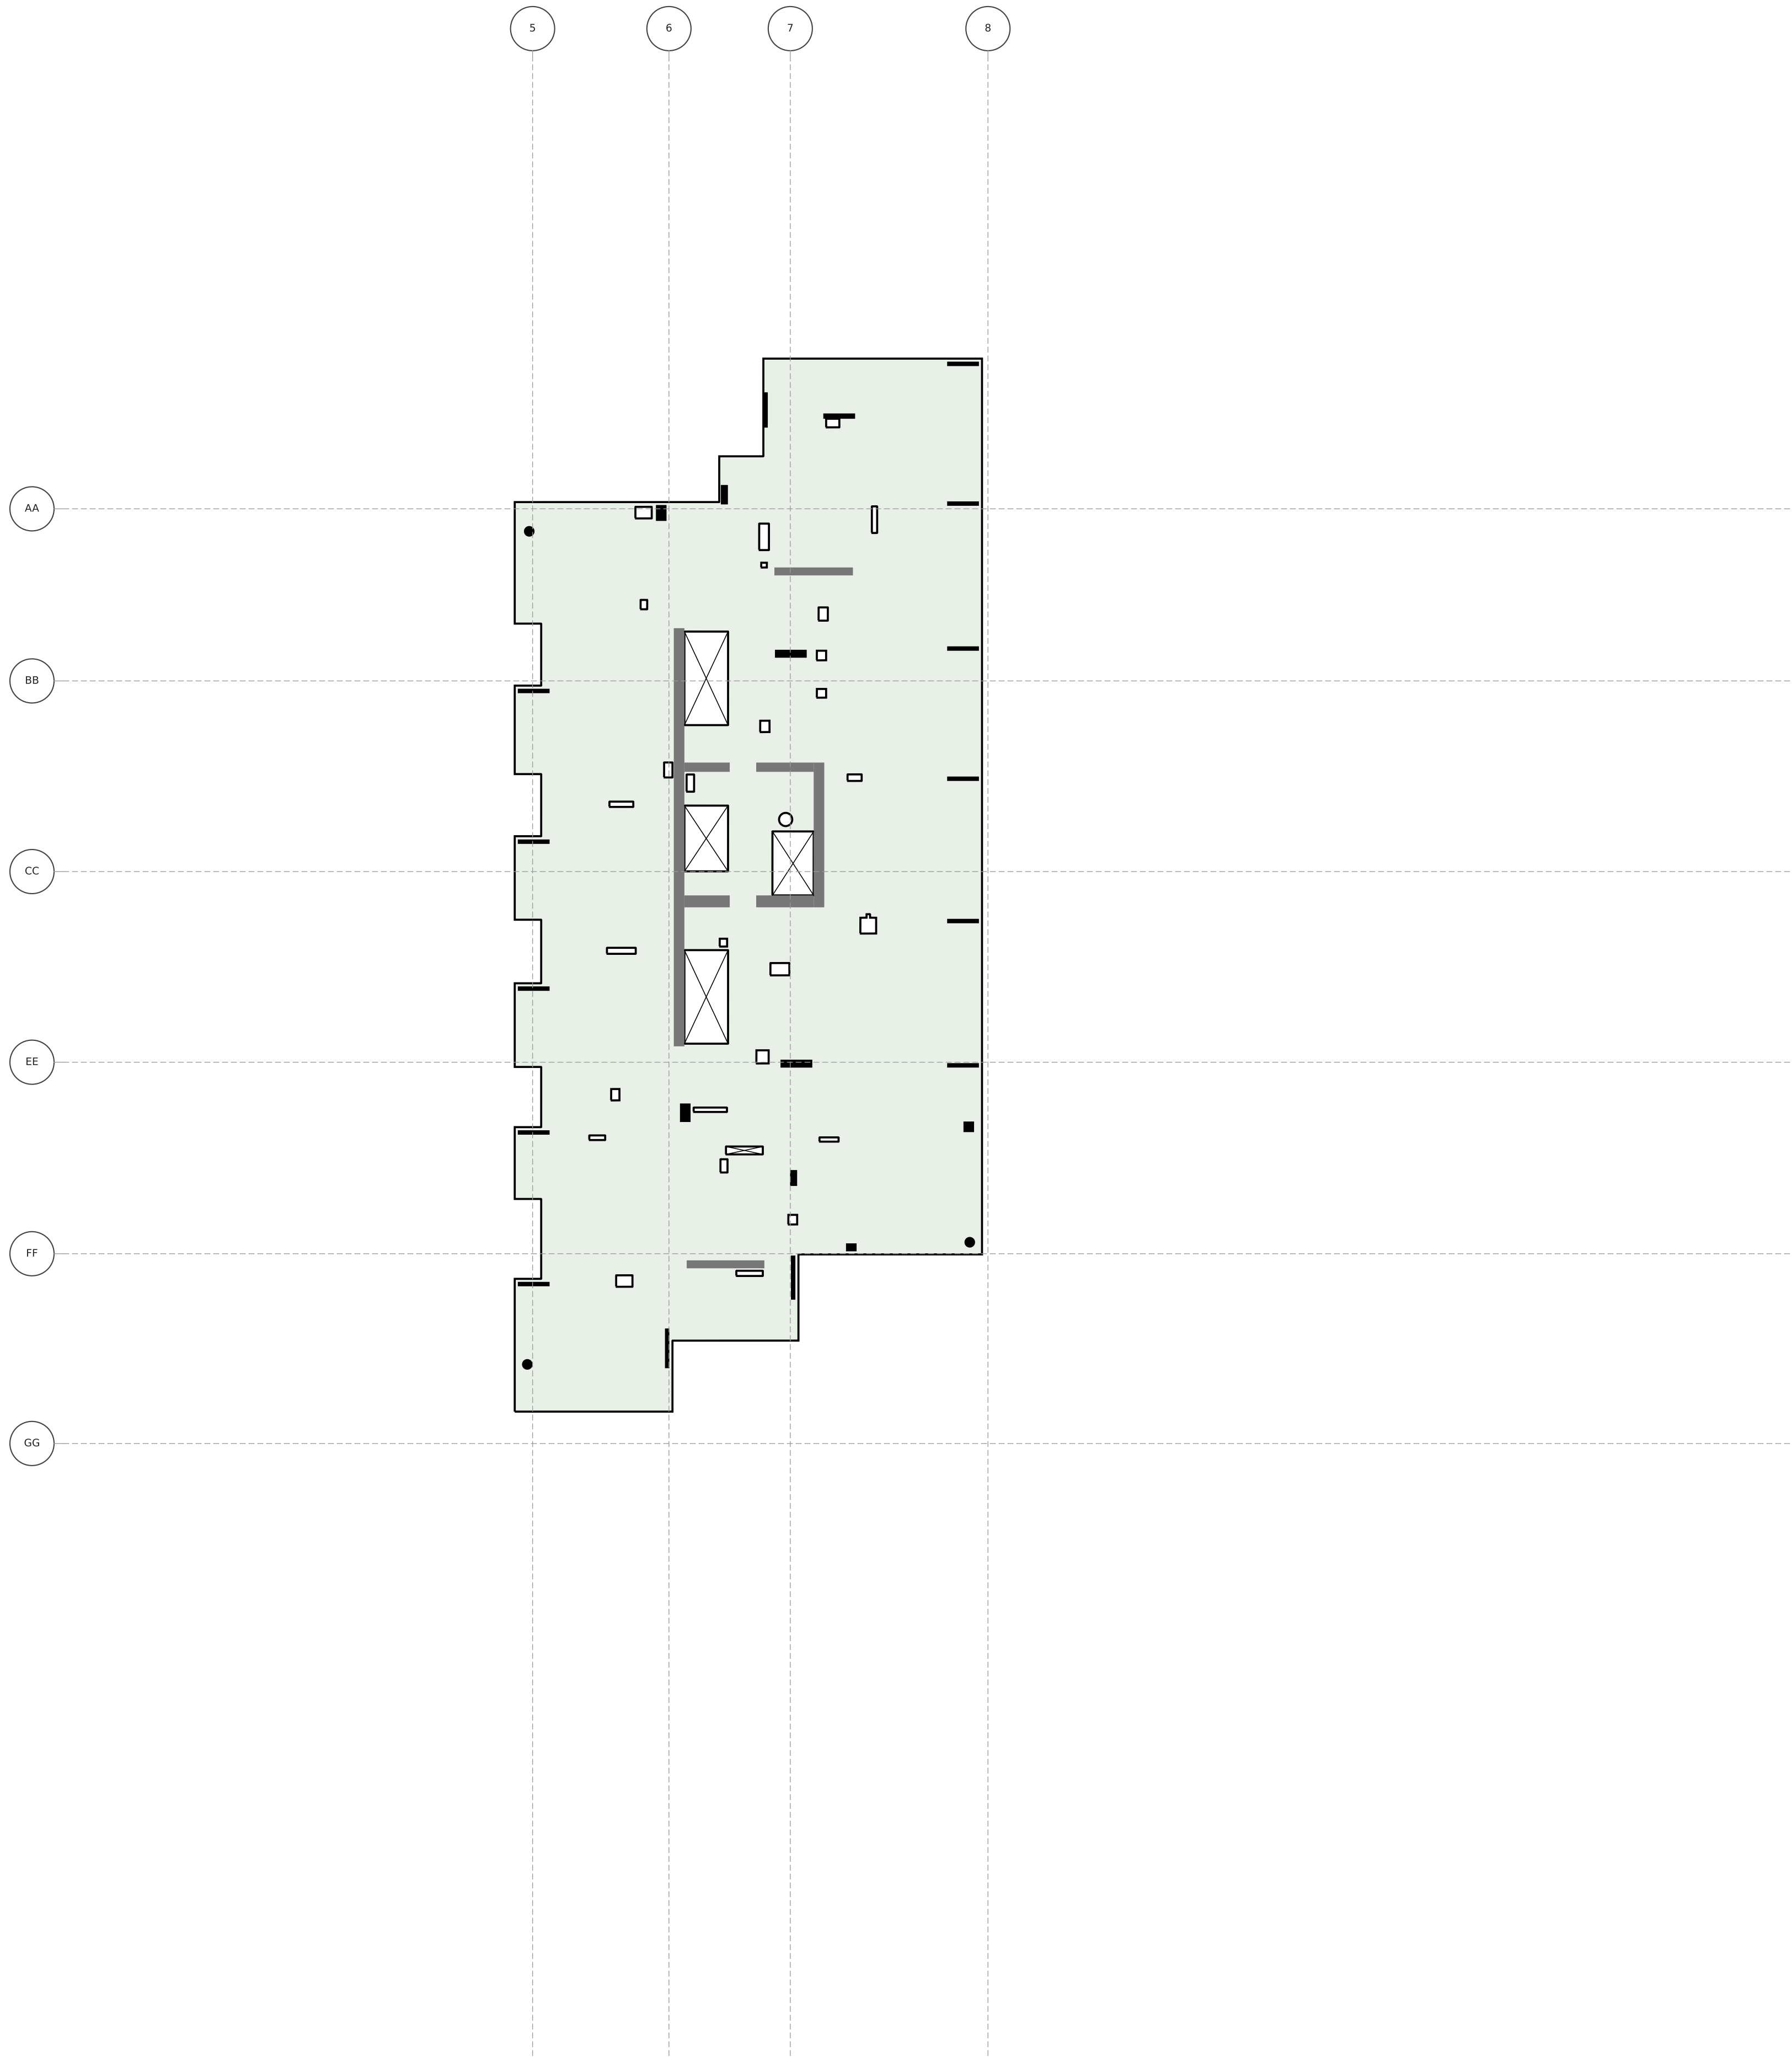


1268 KALAE

LEVEL 15 FLOOR PLAN

T.O.S. 246'-6.5" · typical slab 7.5" · scale 1" = 20'

Generated from 92743ac6-HI_KALAE_MCC_ST.ifc (Revit scope model) for the McClone Reshore Calculator — geometry only; loading marks are drawn in the calculator.

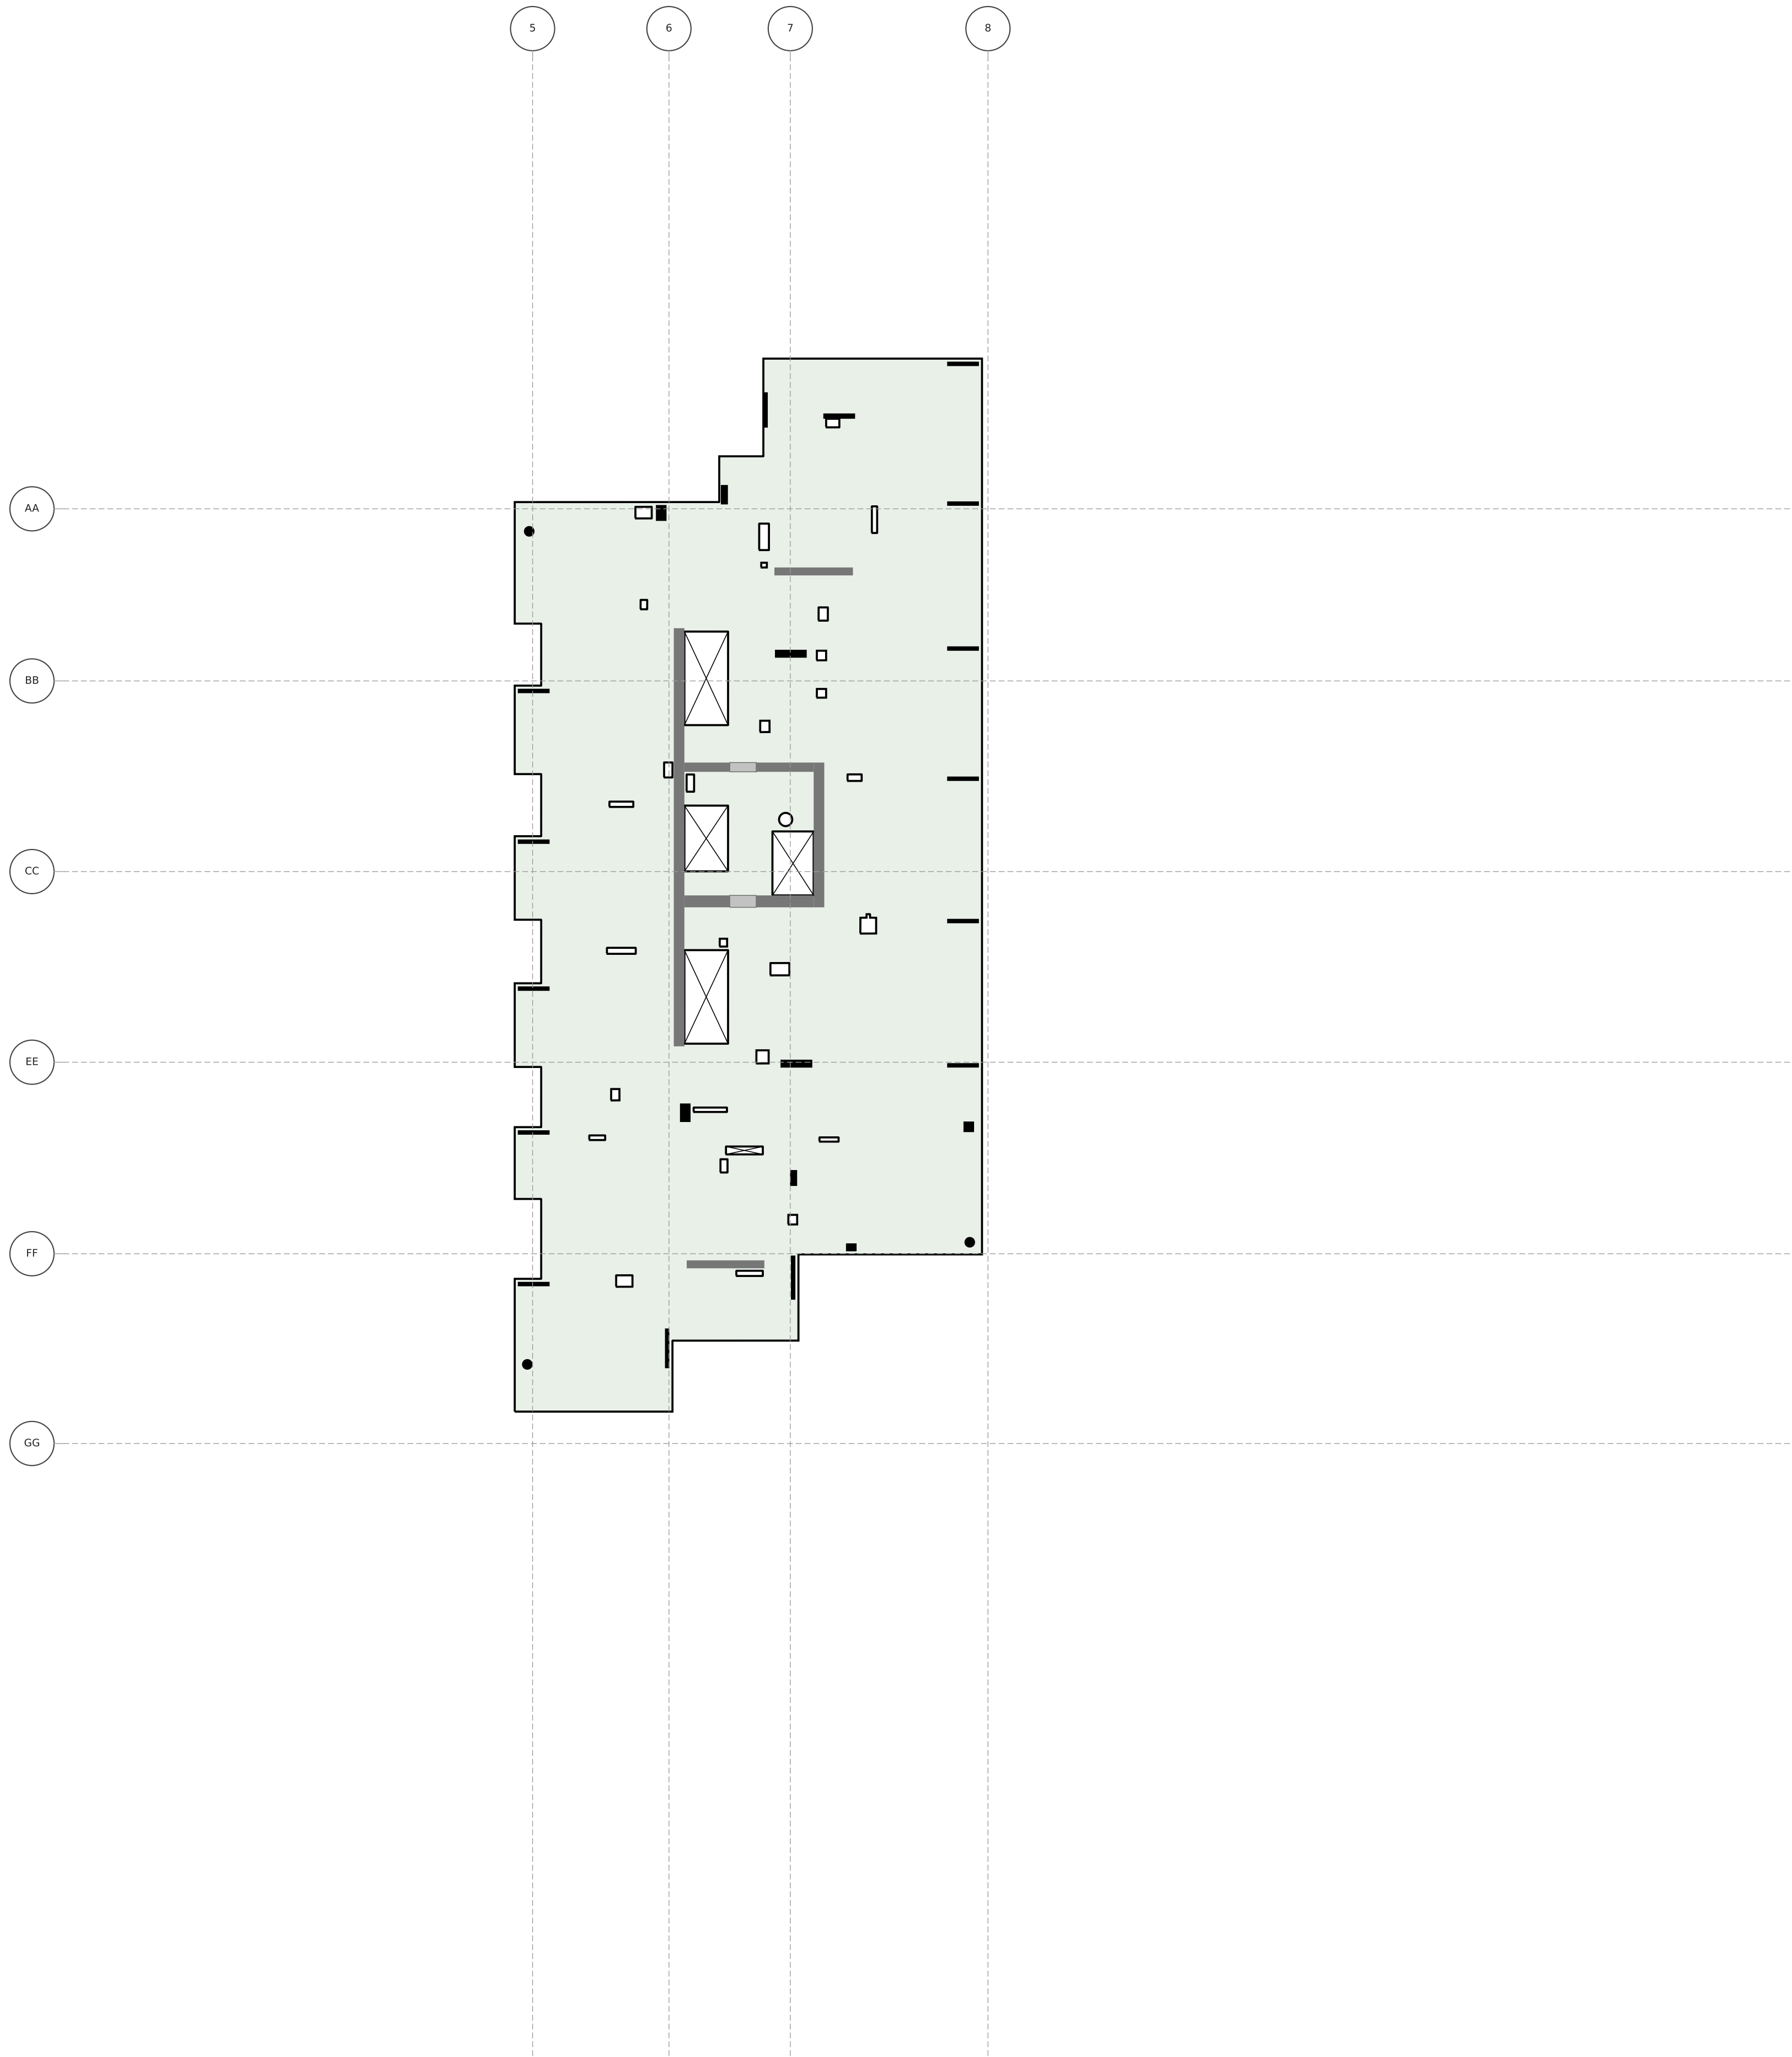


1268 KALAE

LEVEL 16 FLOOR PLAN

T.O.S. 256'-3" · typical slab 7.5" · scale 1" = 20'

Generated from 92743ac6-HI_KALAE_MCC_ST.ifc (Revit scope model) for the McClone Reshore Calculator — geometry only; loading marks are drawn in the calculator.

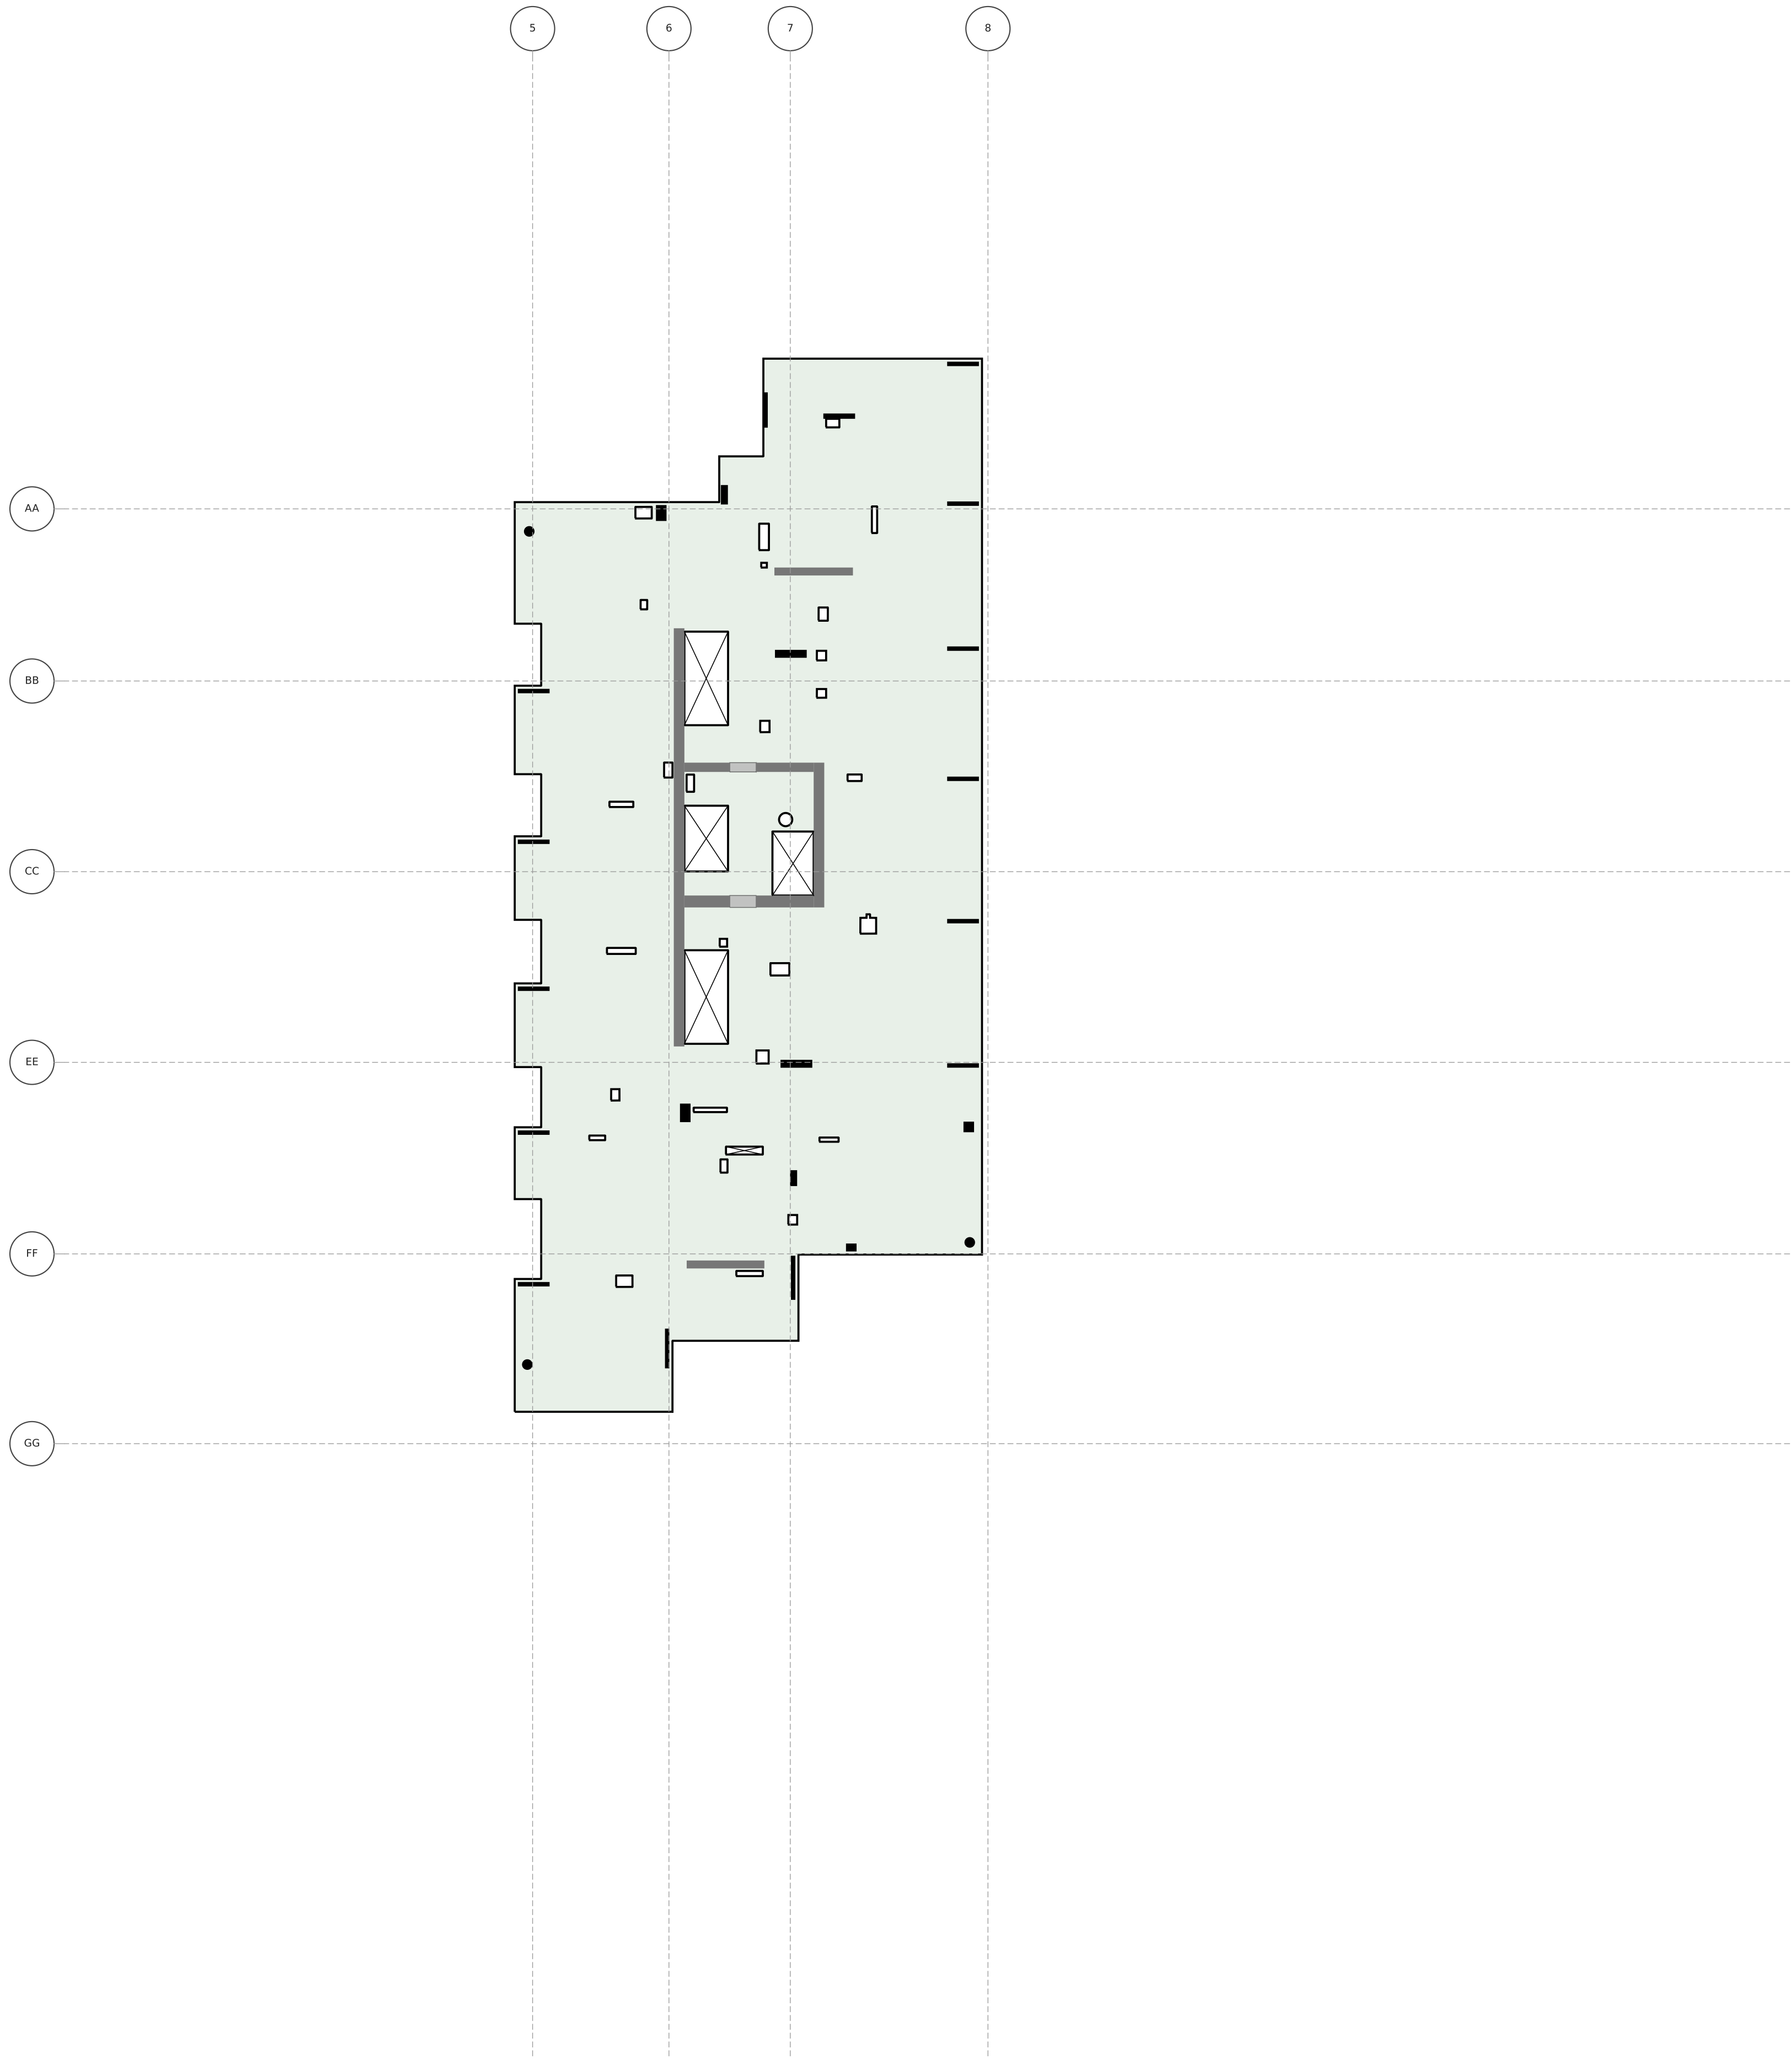


1268 KALAE

LEVEL 17 FLOOR PLAN

T.O.S. 265'-11.5" · typical slab 7.5" · scale 1" = 20'

Generated from 92743ac6-HI_KALAE_MCC_ST.ifc (Revit scope model) for the McClone Reshore Calculator — geometry only; loading marks are drawn in the calculator.

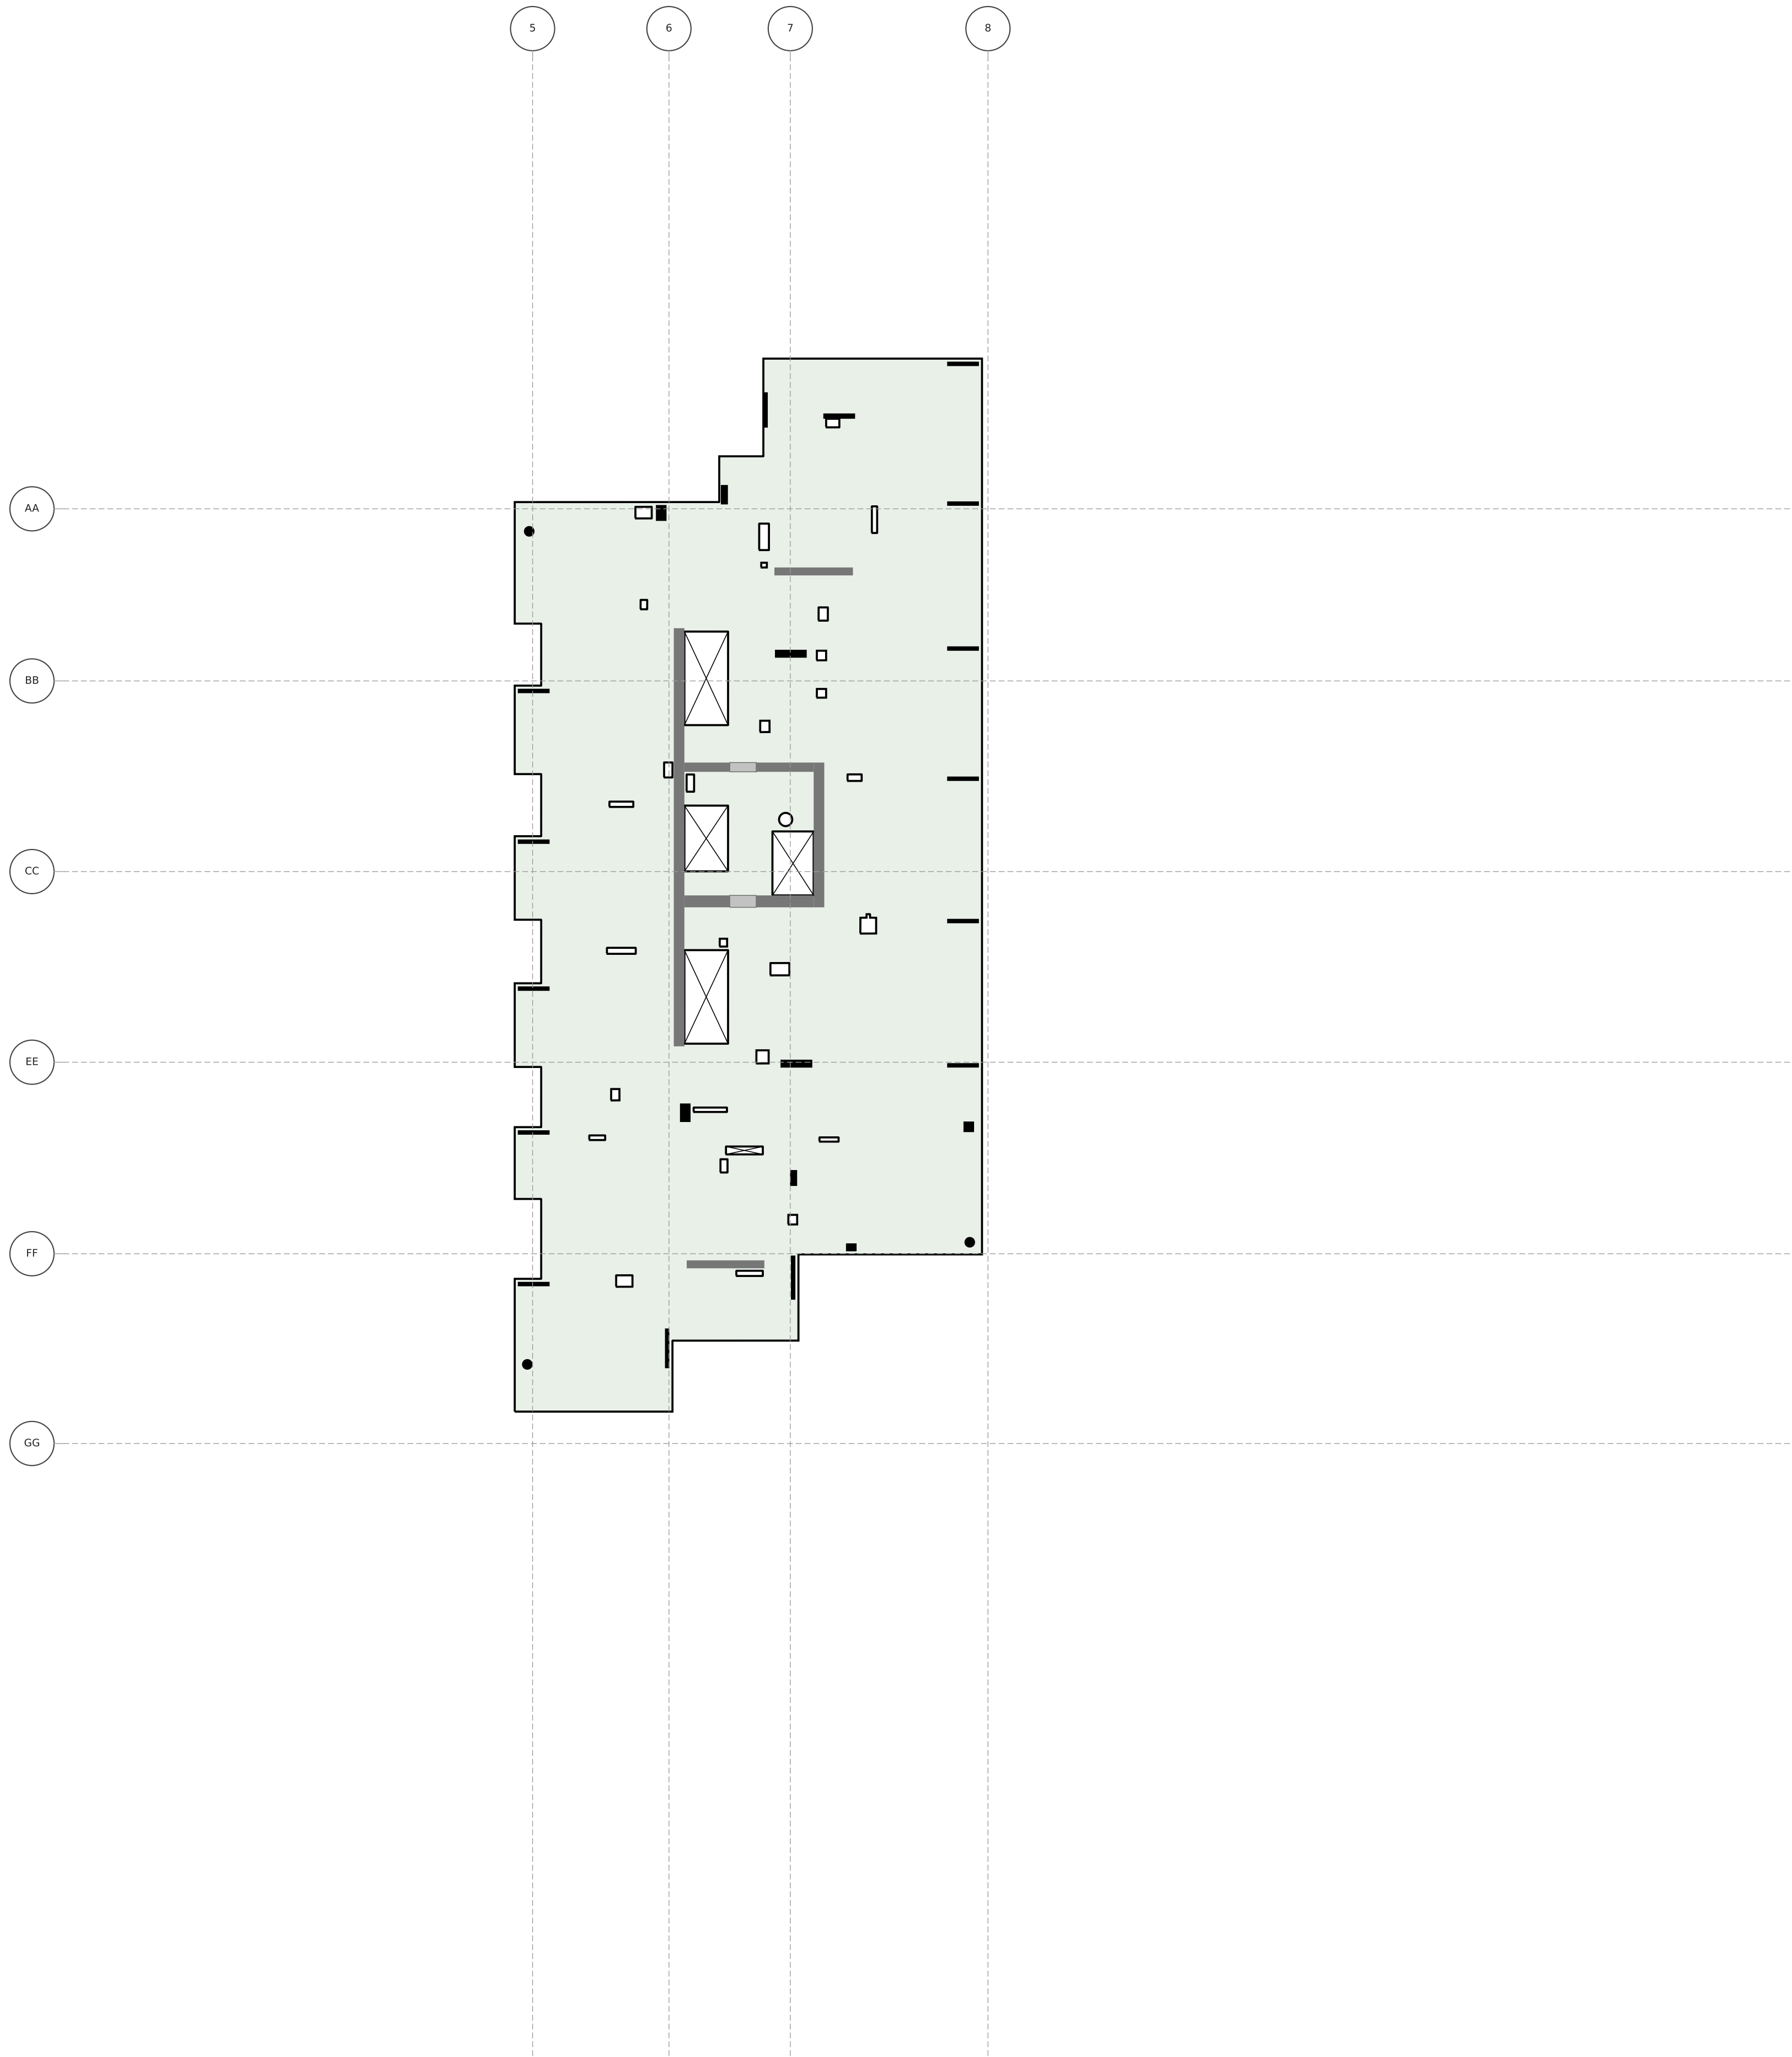


1268 KALAE

LEVEL 18 FLOOR PLAN

T.O.S. 275'-8" · typical slab 7.5" · scale 1" = 20'

Generated from 92743ac6-HI_KALAE_MCC_ST.ifc (Revit scope model) for the McClone Reshore Calculator — geometry only; loading marks are drawn in the calculator.

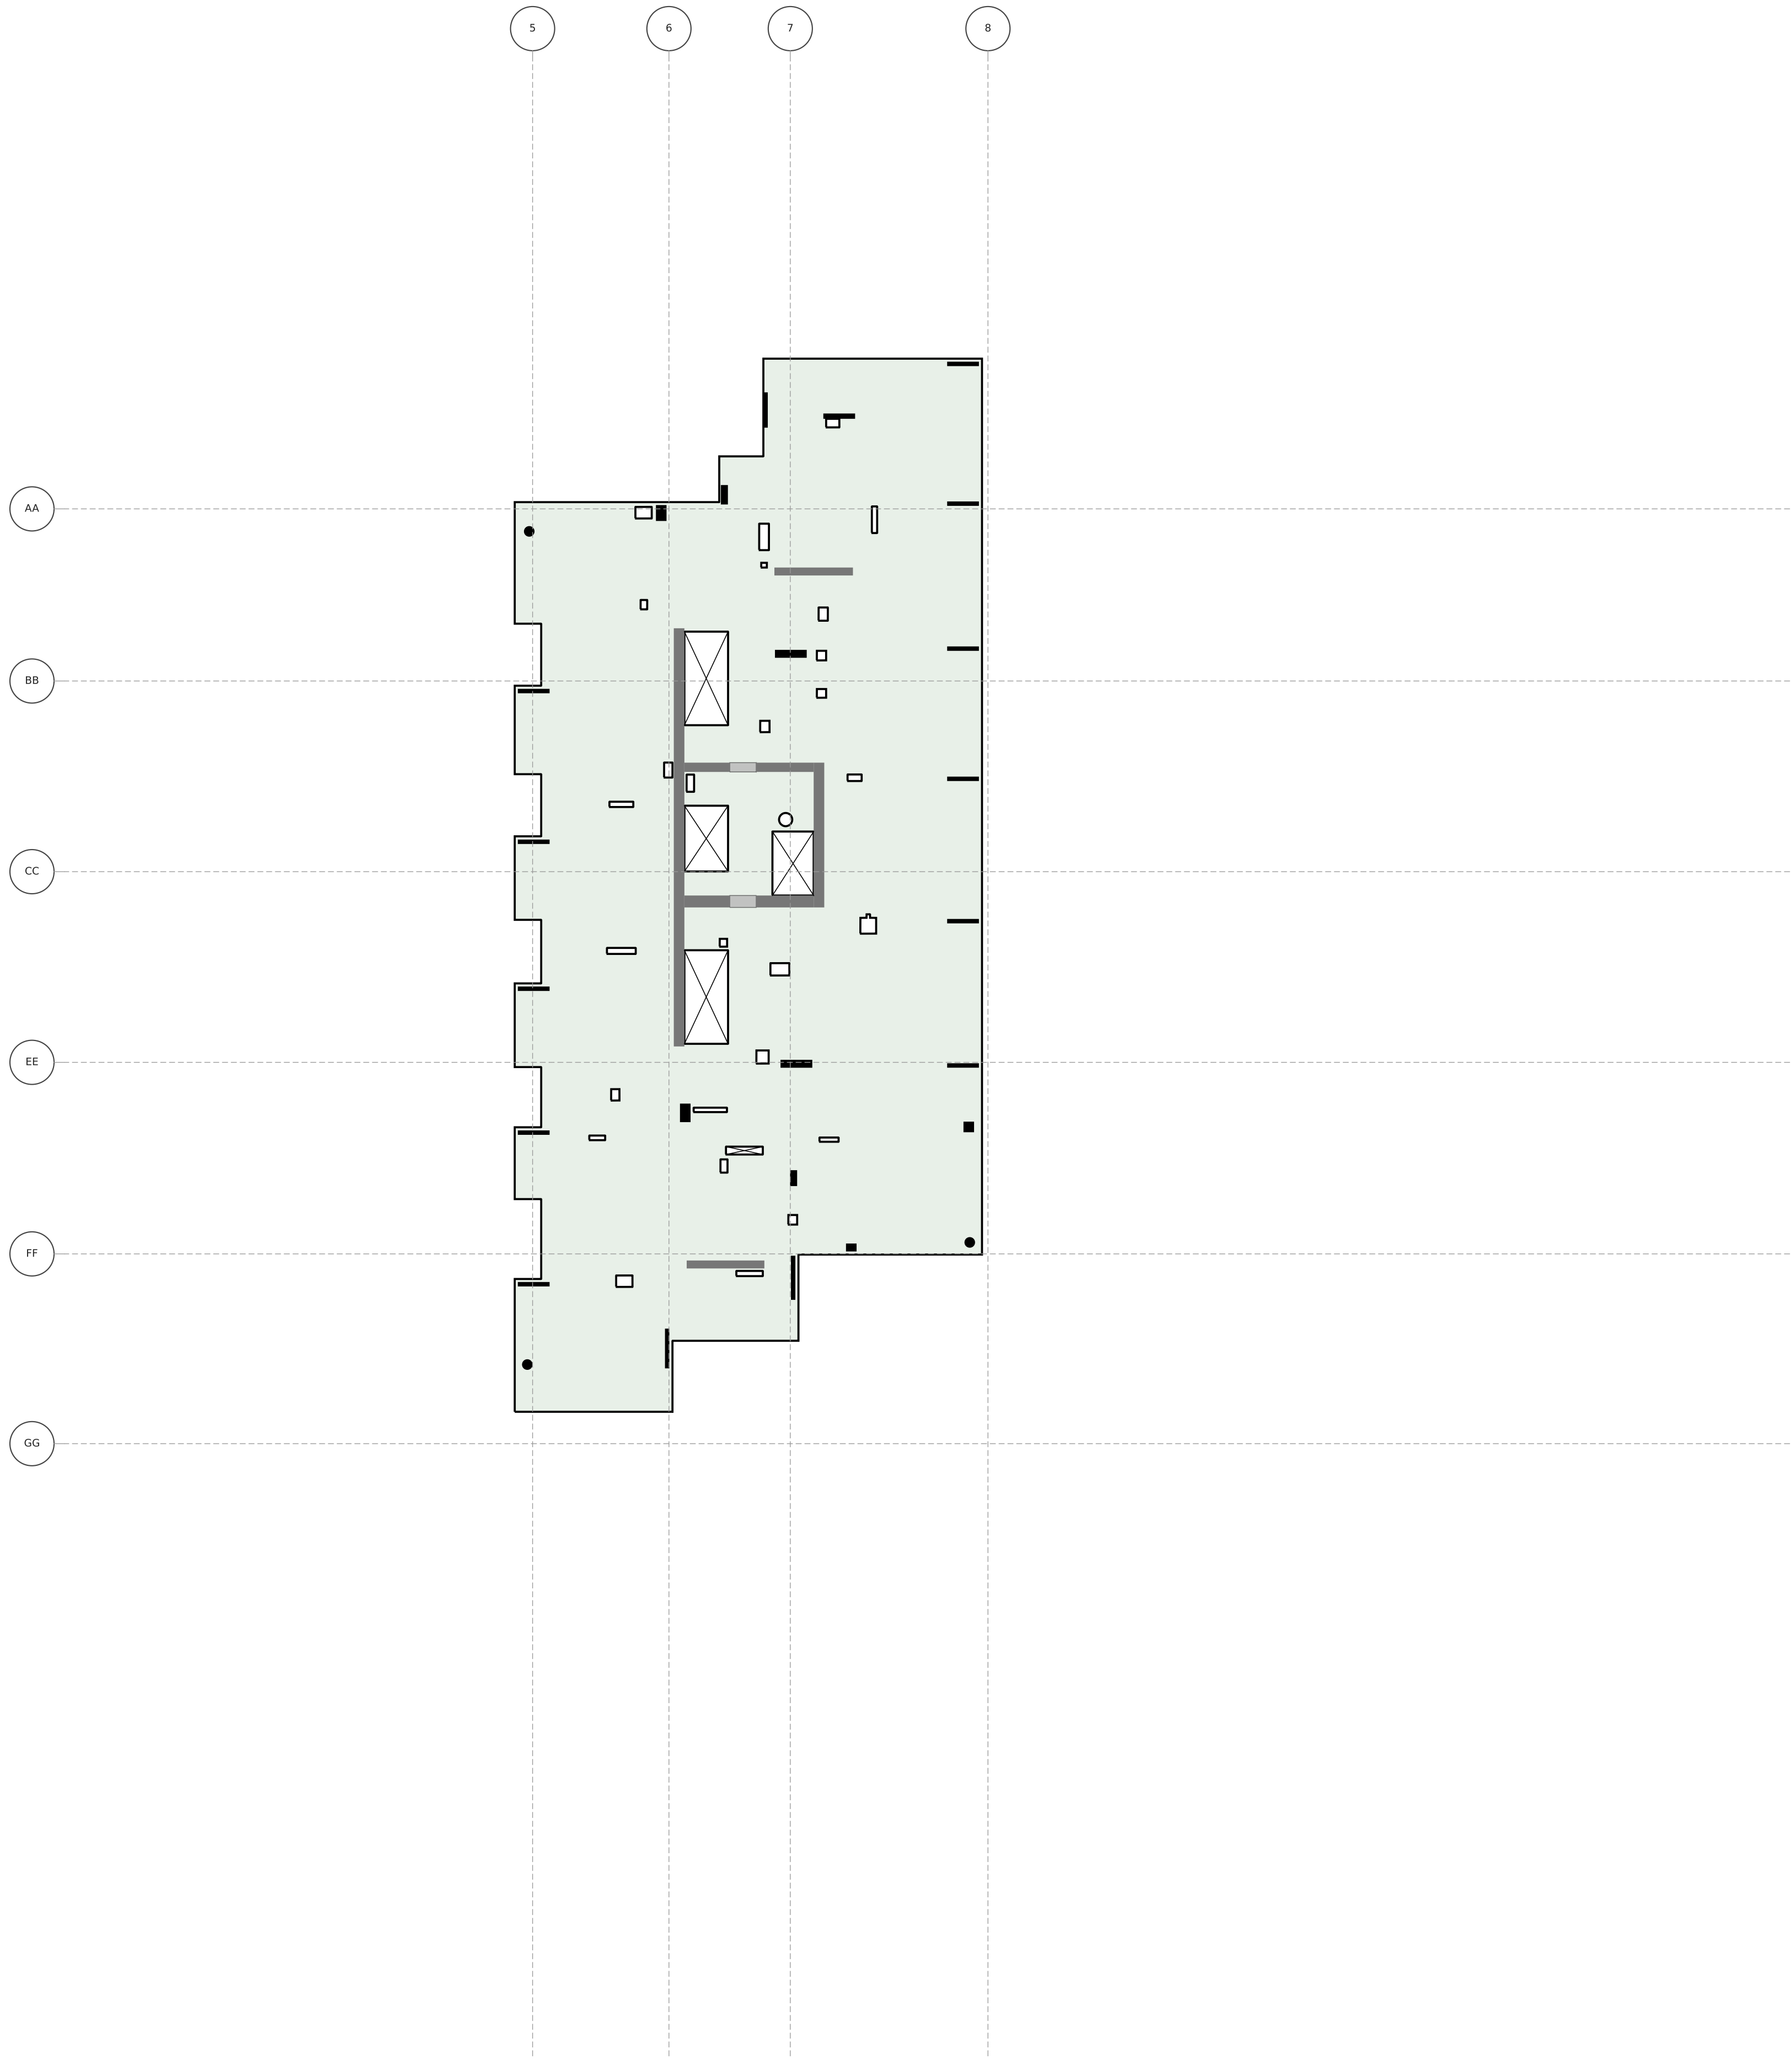


1268 KALAE

LEVEL 19 FLOOR PLAN

T.O.S. 285'-4.5" · typical slab 7.5" · scale 1" = 20'

Generated from 92743ac6-HI_KALAE_MCC_ST.ifc (Revit scope model) for the McClone Reshore Calculator — geometry only; loading marks are drawn in the calculator.

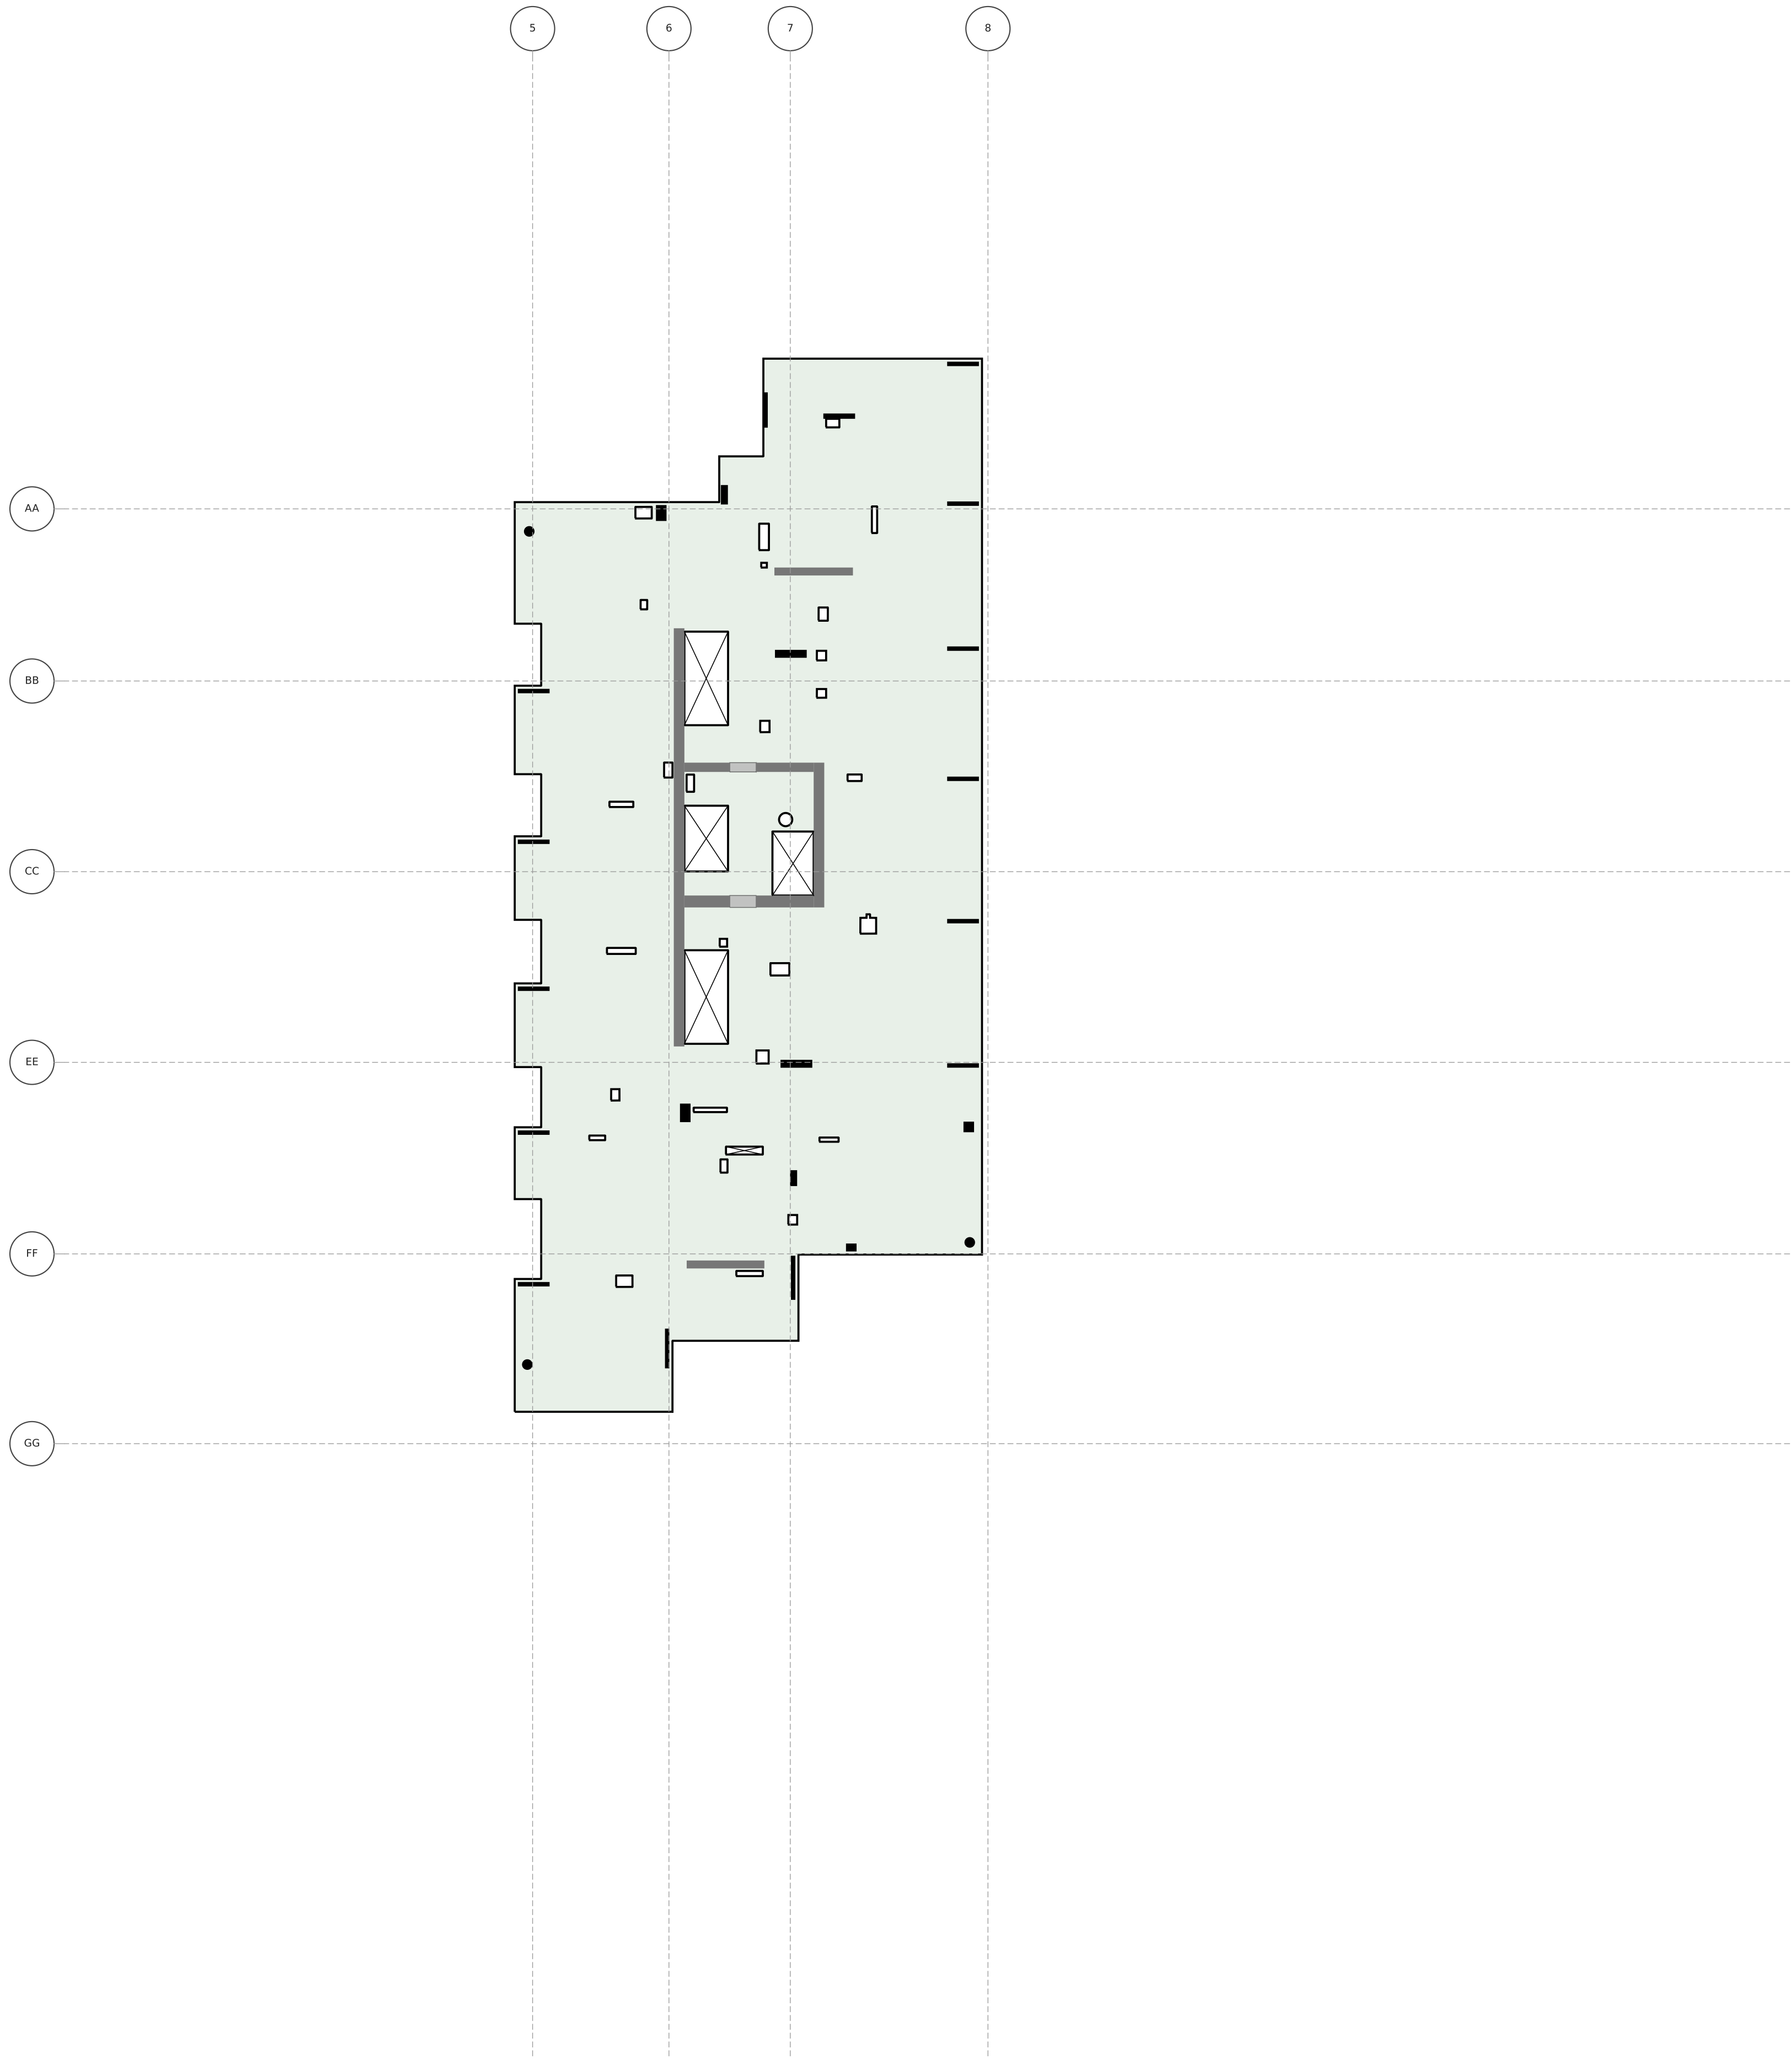


1268 KALAE

LEVEL 20 FLOOR PLAN


T.O.S. 295'-1" · typical slab 7.5" · scale 1" = 20'

Generated from 92743ac6-HI_KALAE_MCC_ST.ifc (Revit scope model) for the McClone Reshore Calculator — geometry only; loading marks are drawn in the calculator.

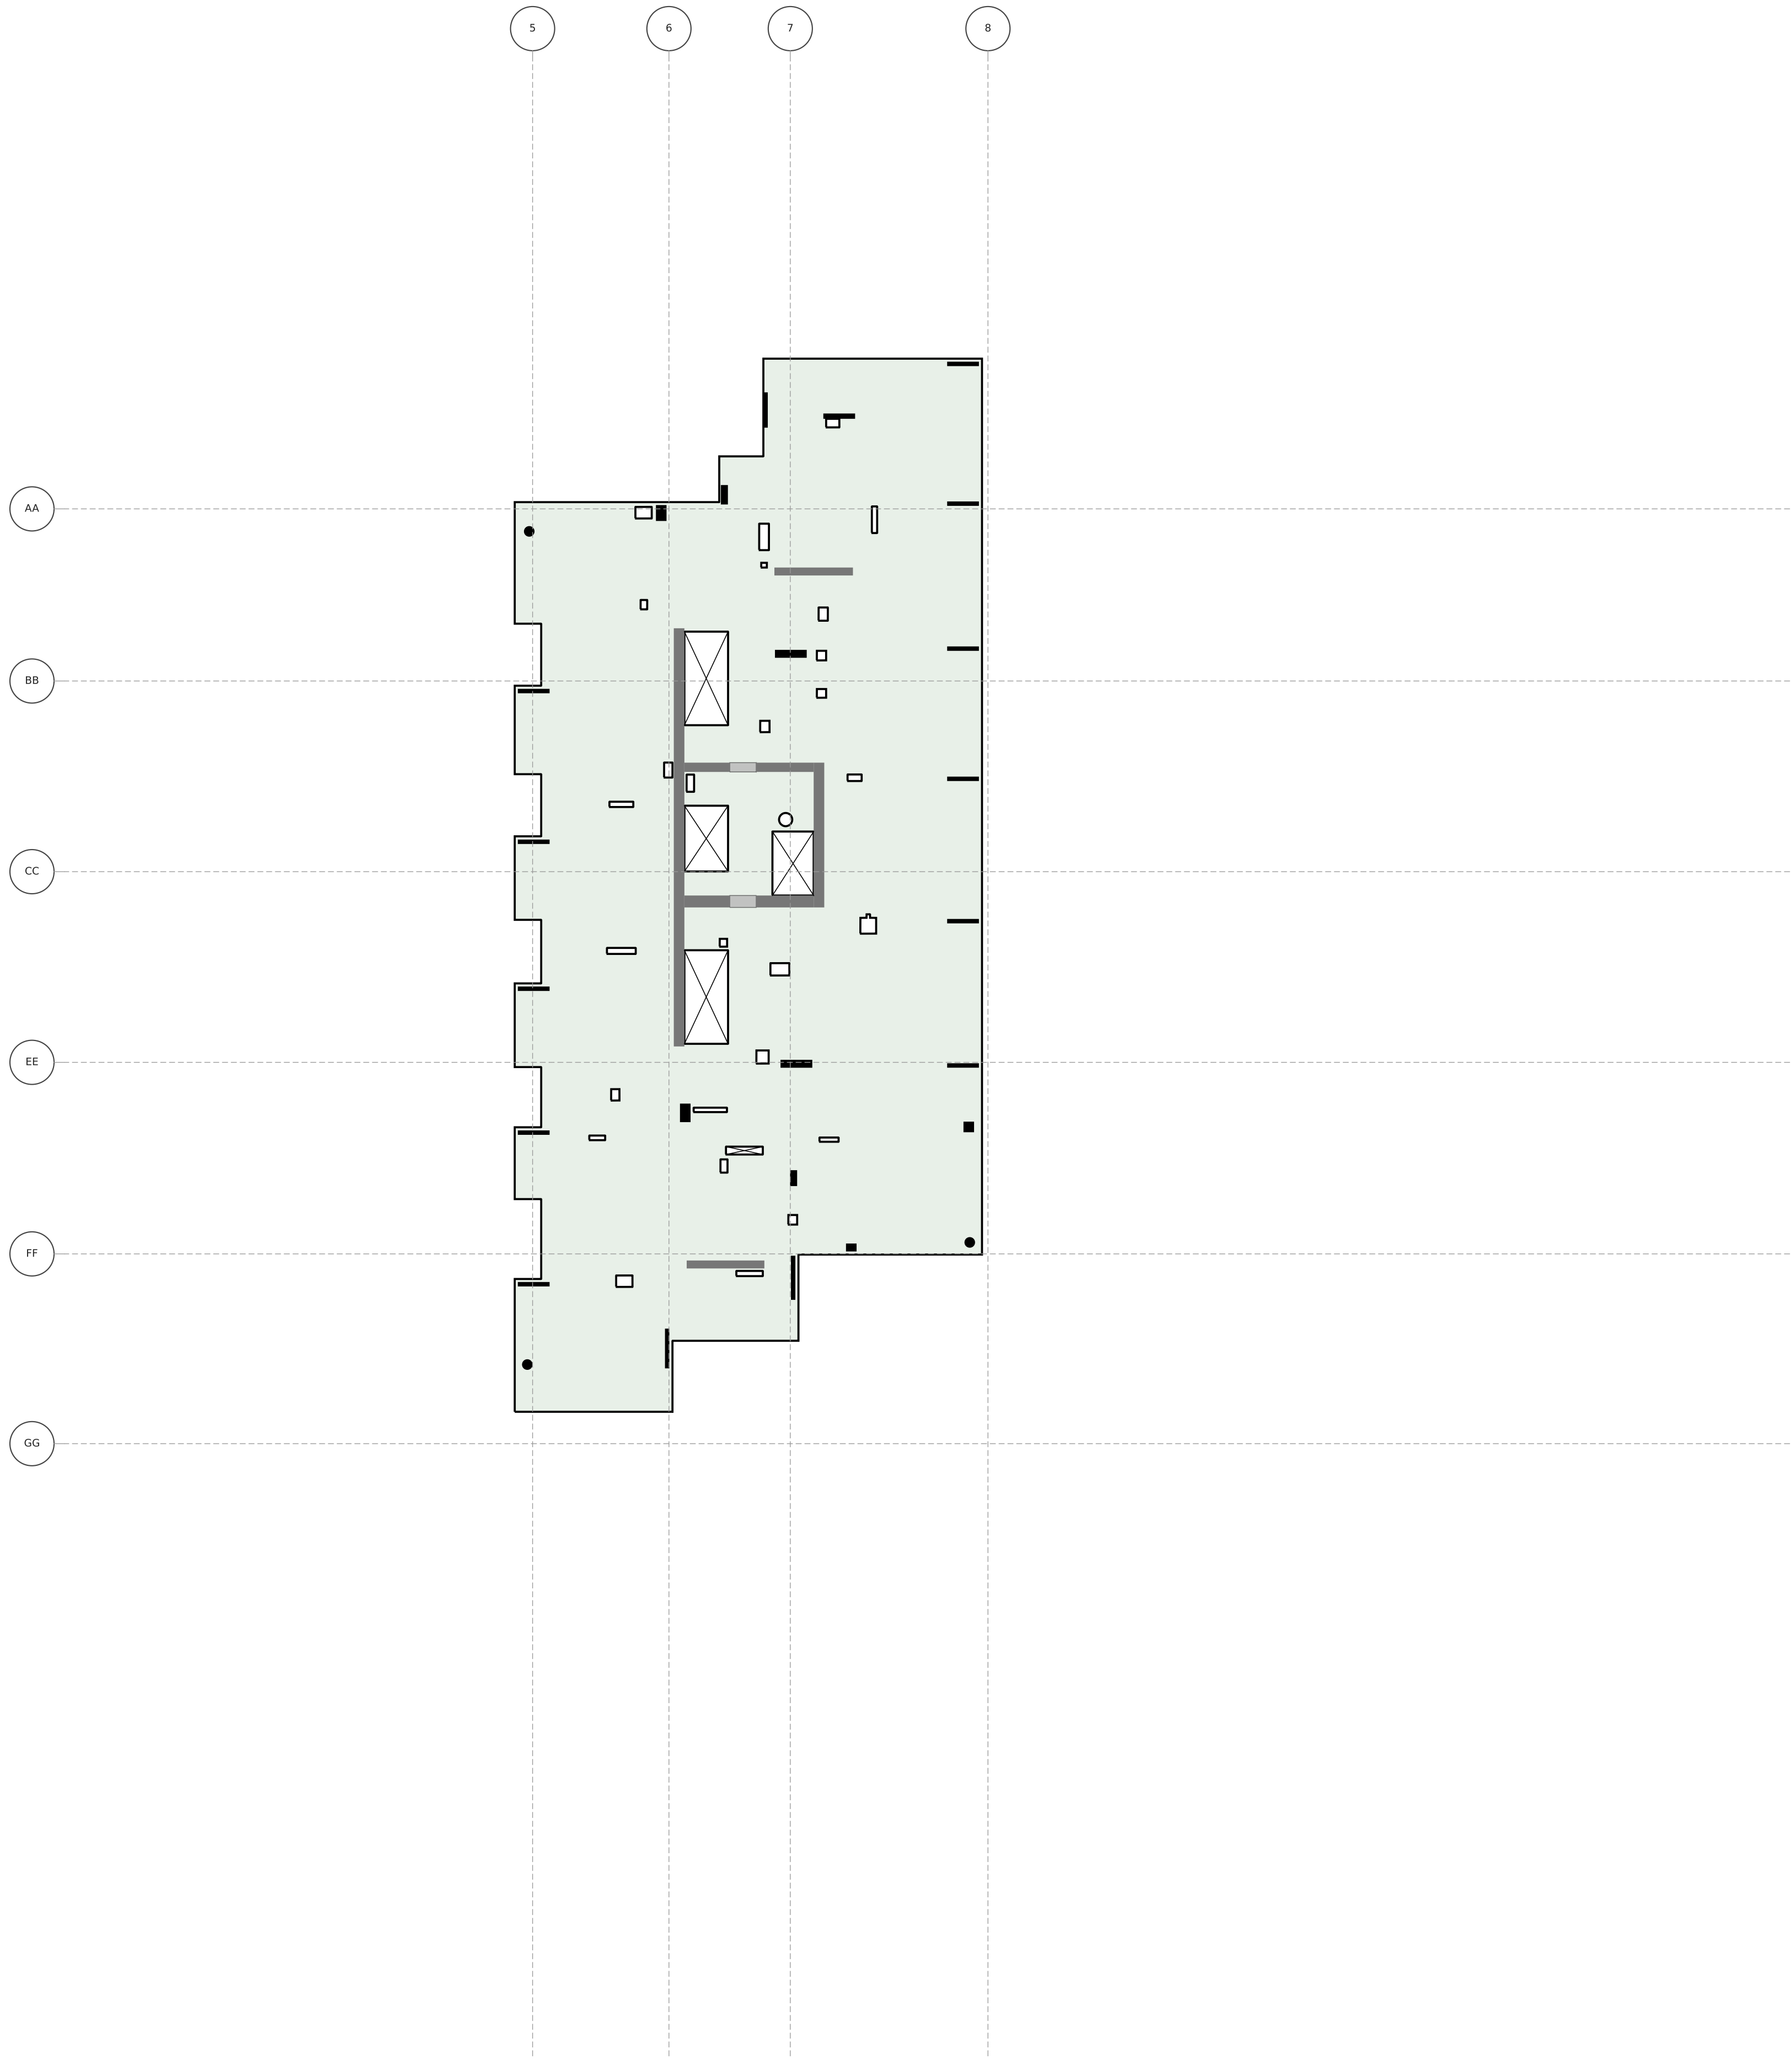

1268 KALAE
LEVEL 21 FLOOR PLAN

T.O.S. 304'-9.5" · typical slab 7.5" · scale 1" = 20'
Generated from 92743ac6-HI_KALAE_MCC_ST.ifc (Revit scope model) for the McClone Reshore Calculator — geometry only; loading marks are drawn in the calculator.

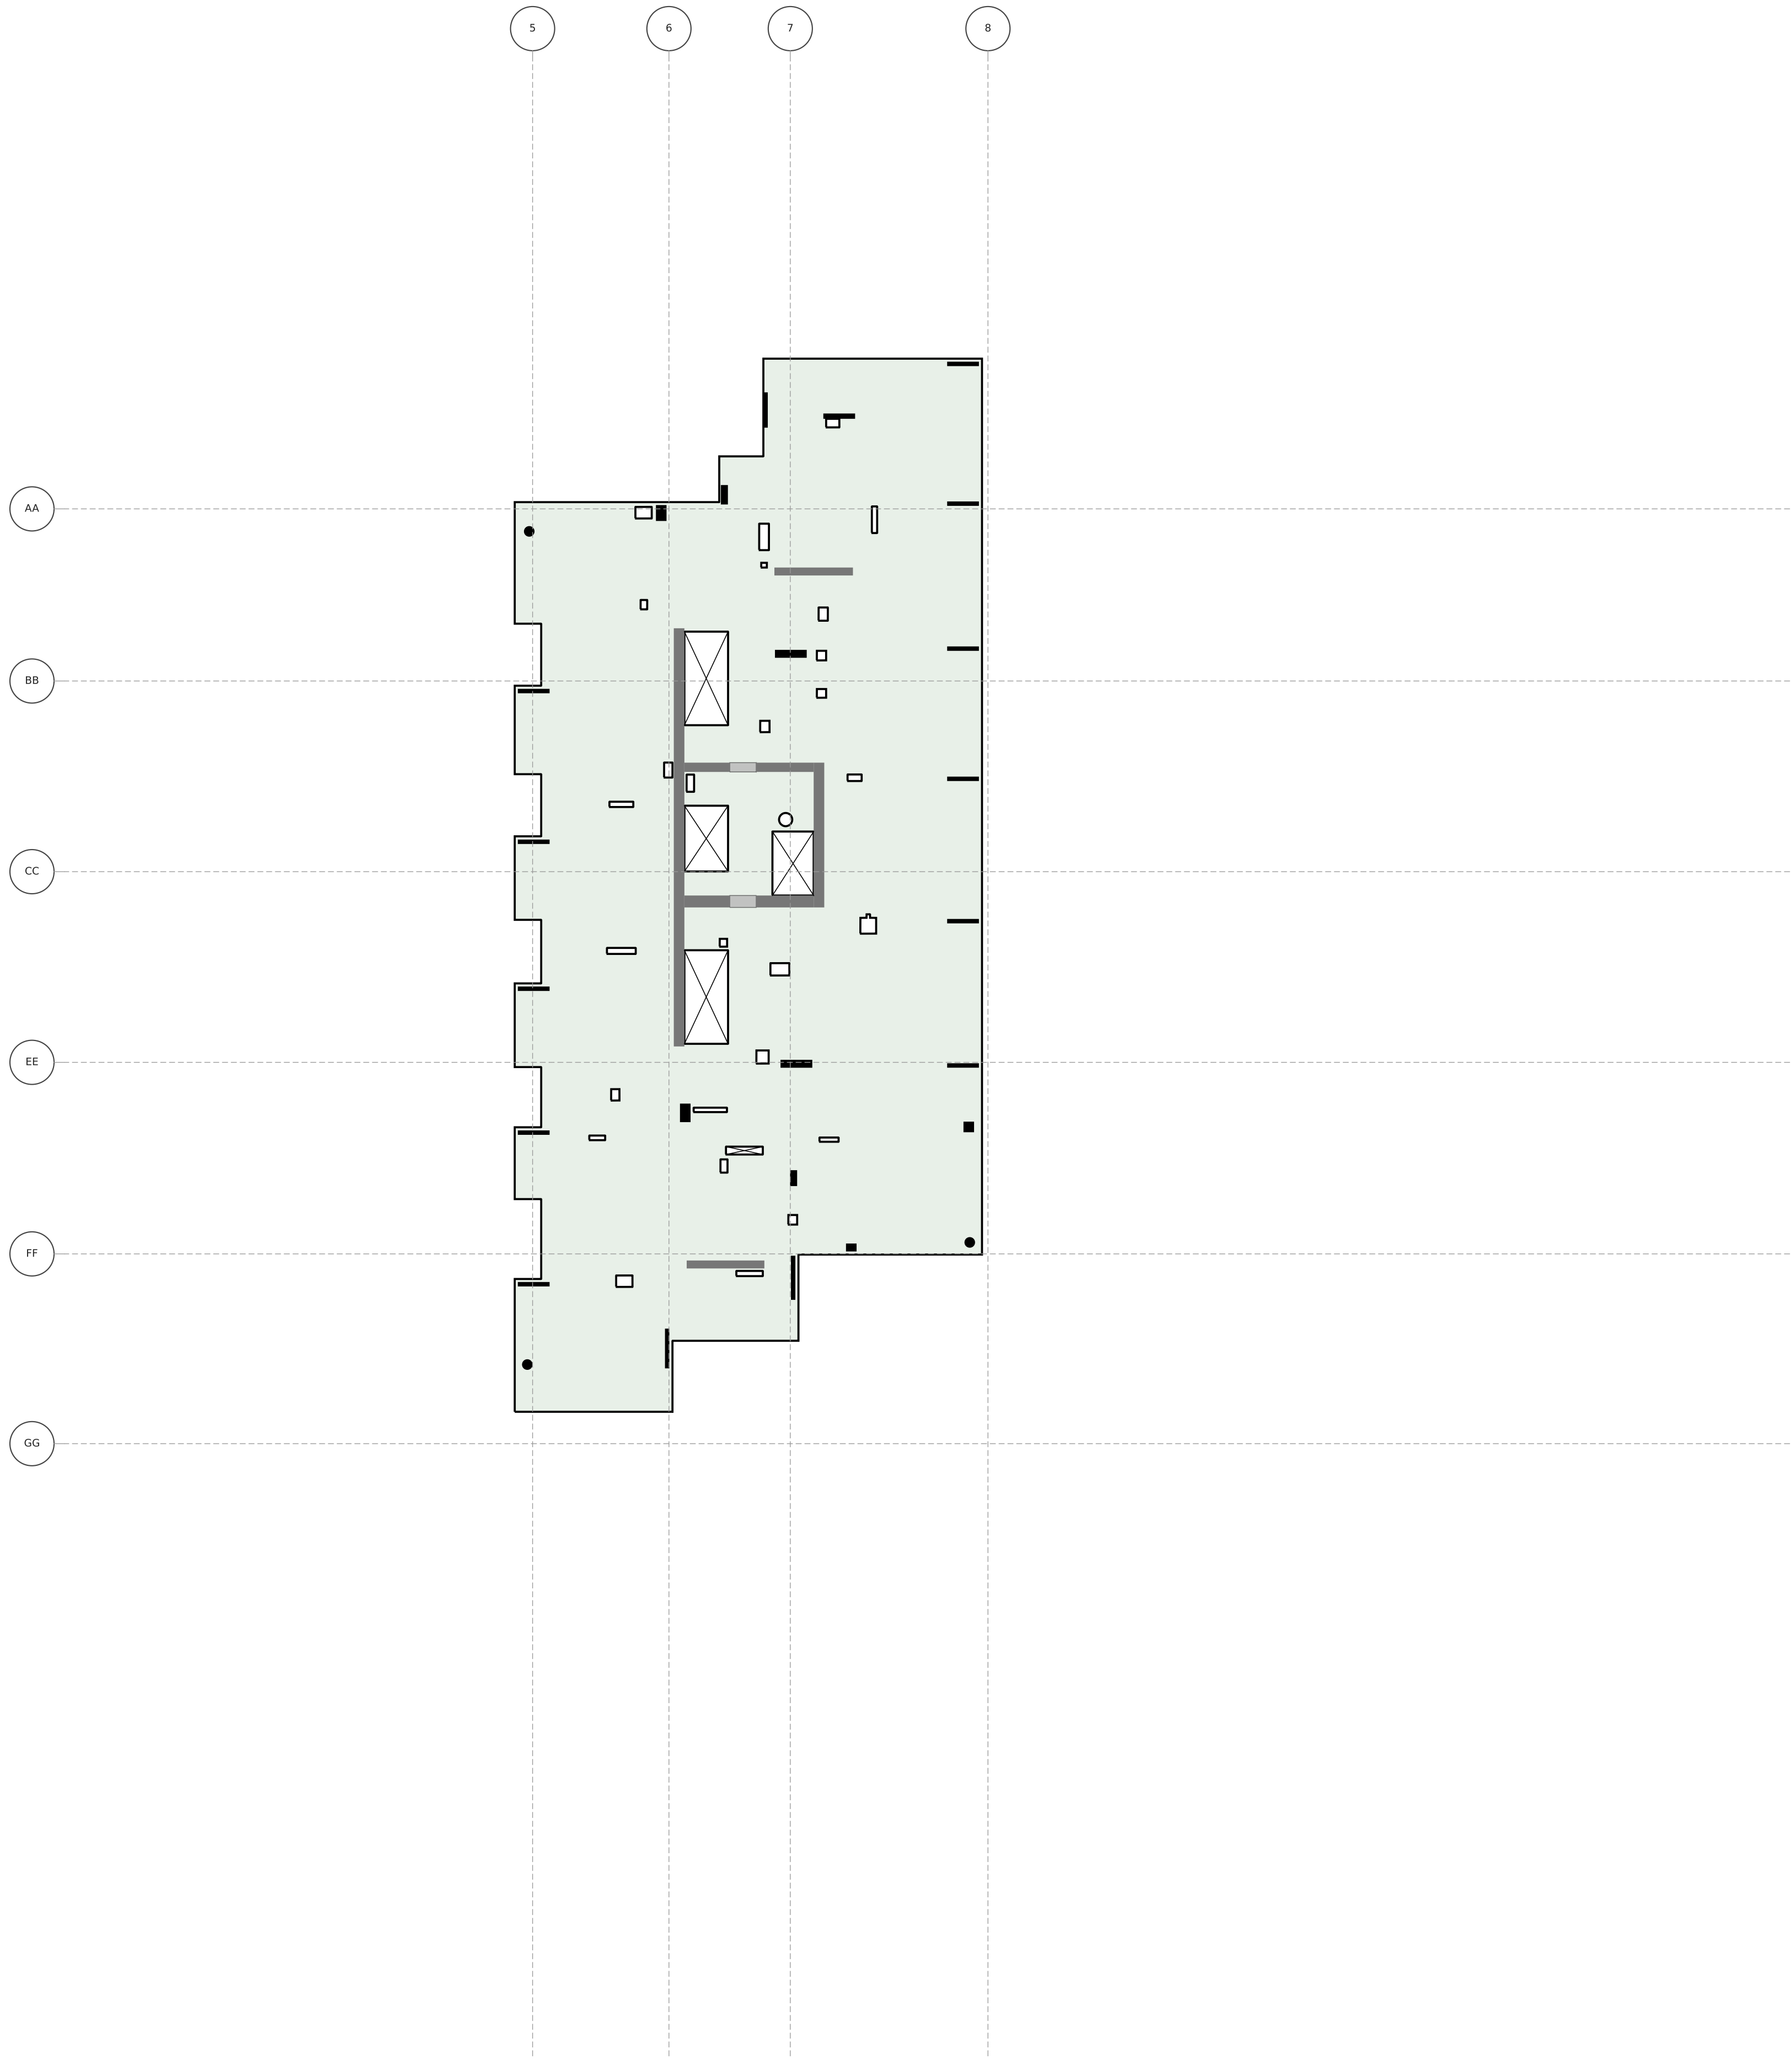


1268 KALAE

LEVEL 22 FLOOR PLAN

T.O.S. 314'-6" · typical slab 7.5" · scale 1" = 20'

Generated from 92743ac6-HI_KALAE_MCC_ST.ifc (Revit scope model) for the McClone Reshore Calculator — geometry only; loading marks are drawn in the calculator.

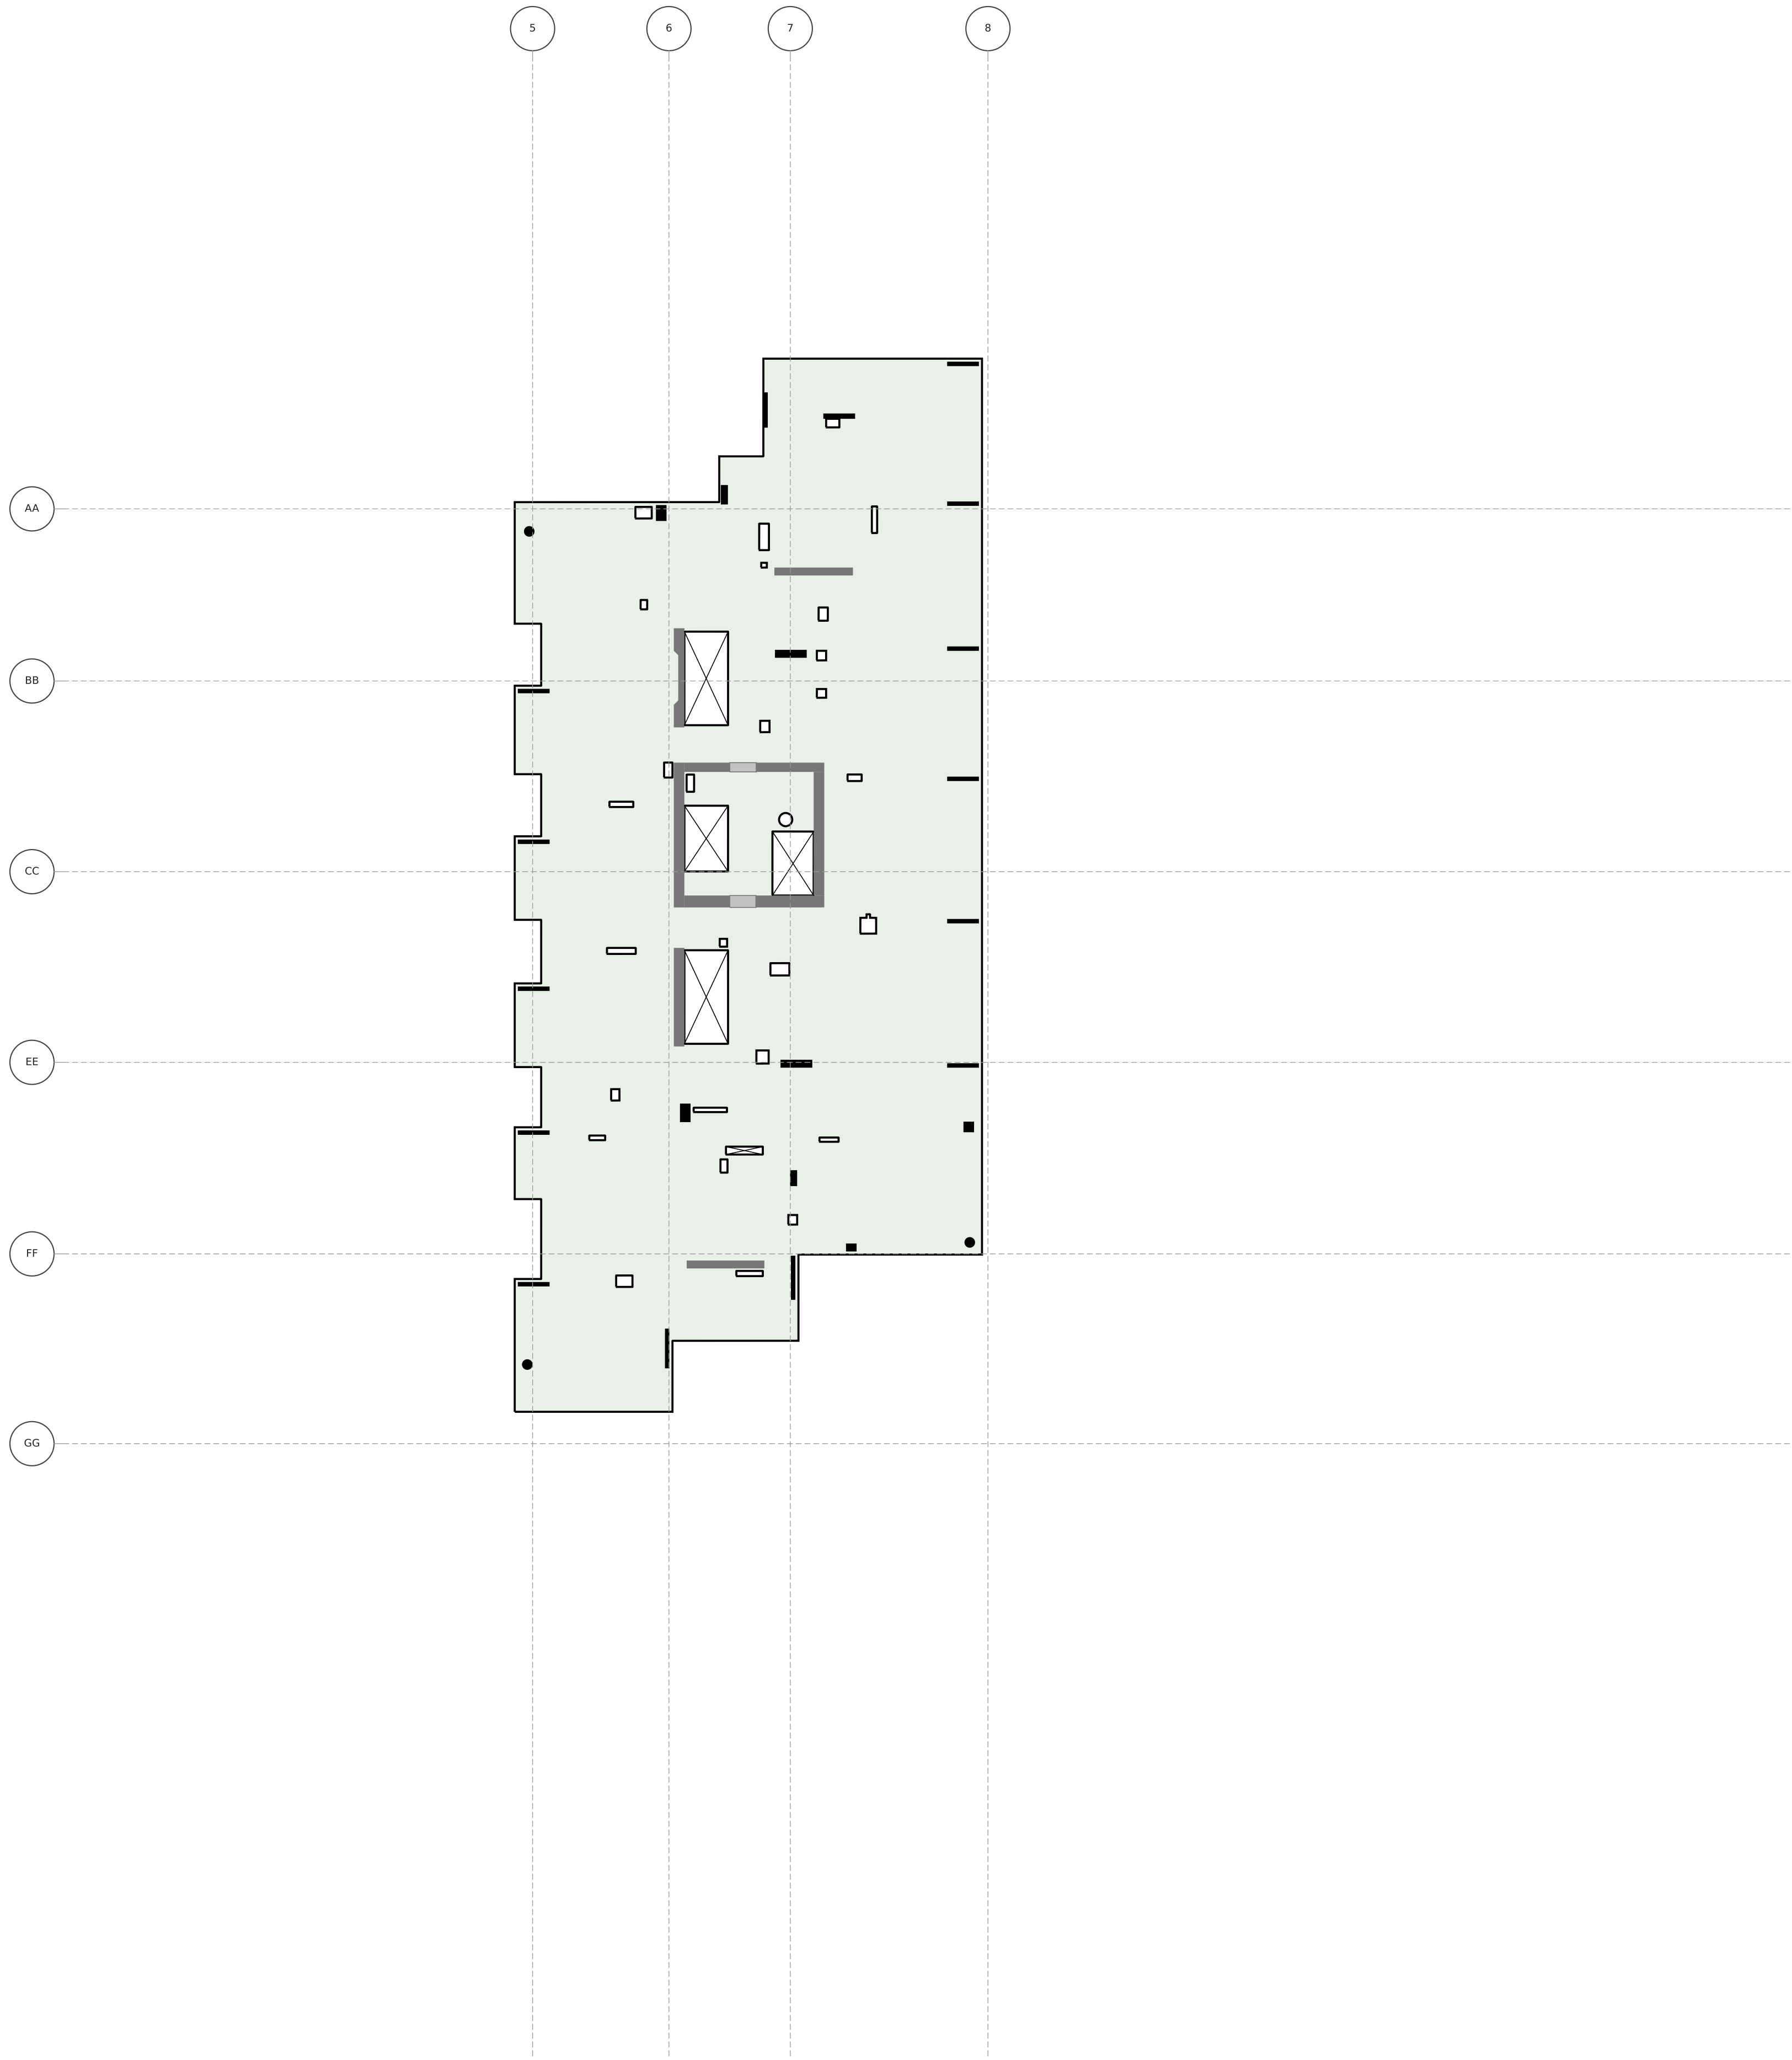


1268 KALAE

LEVEL 23 FLOOR PLAN

T.O.S. 324'-2.5" · typical slab 7.5" · scale 1" = 20'

Generated from 92743ac6-HI_KALAE_MCC_ST.ifc (Revit scope model) for the McClone Reshore Calculator — geometry only; loading marks are drawn in the calculator.

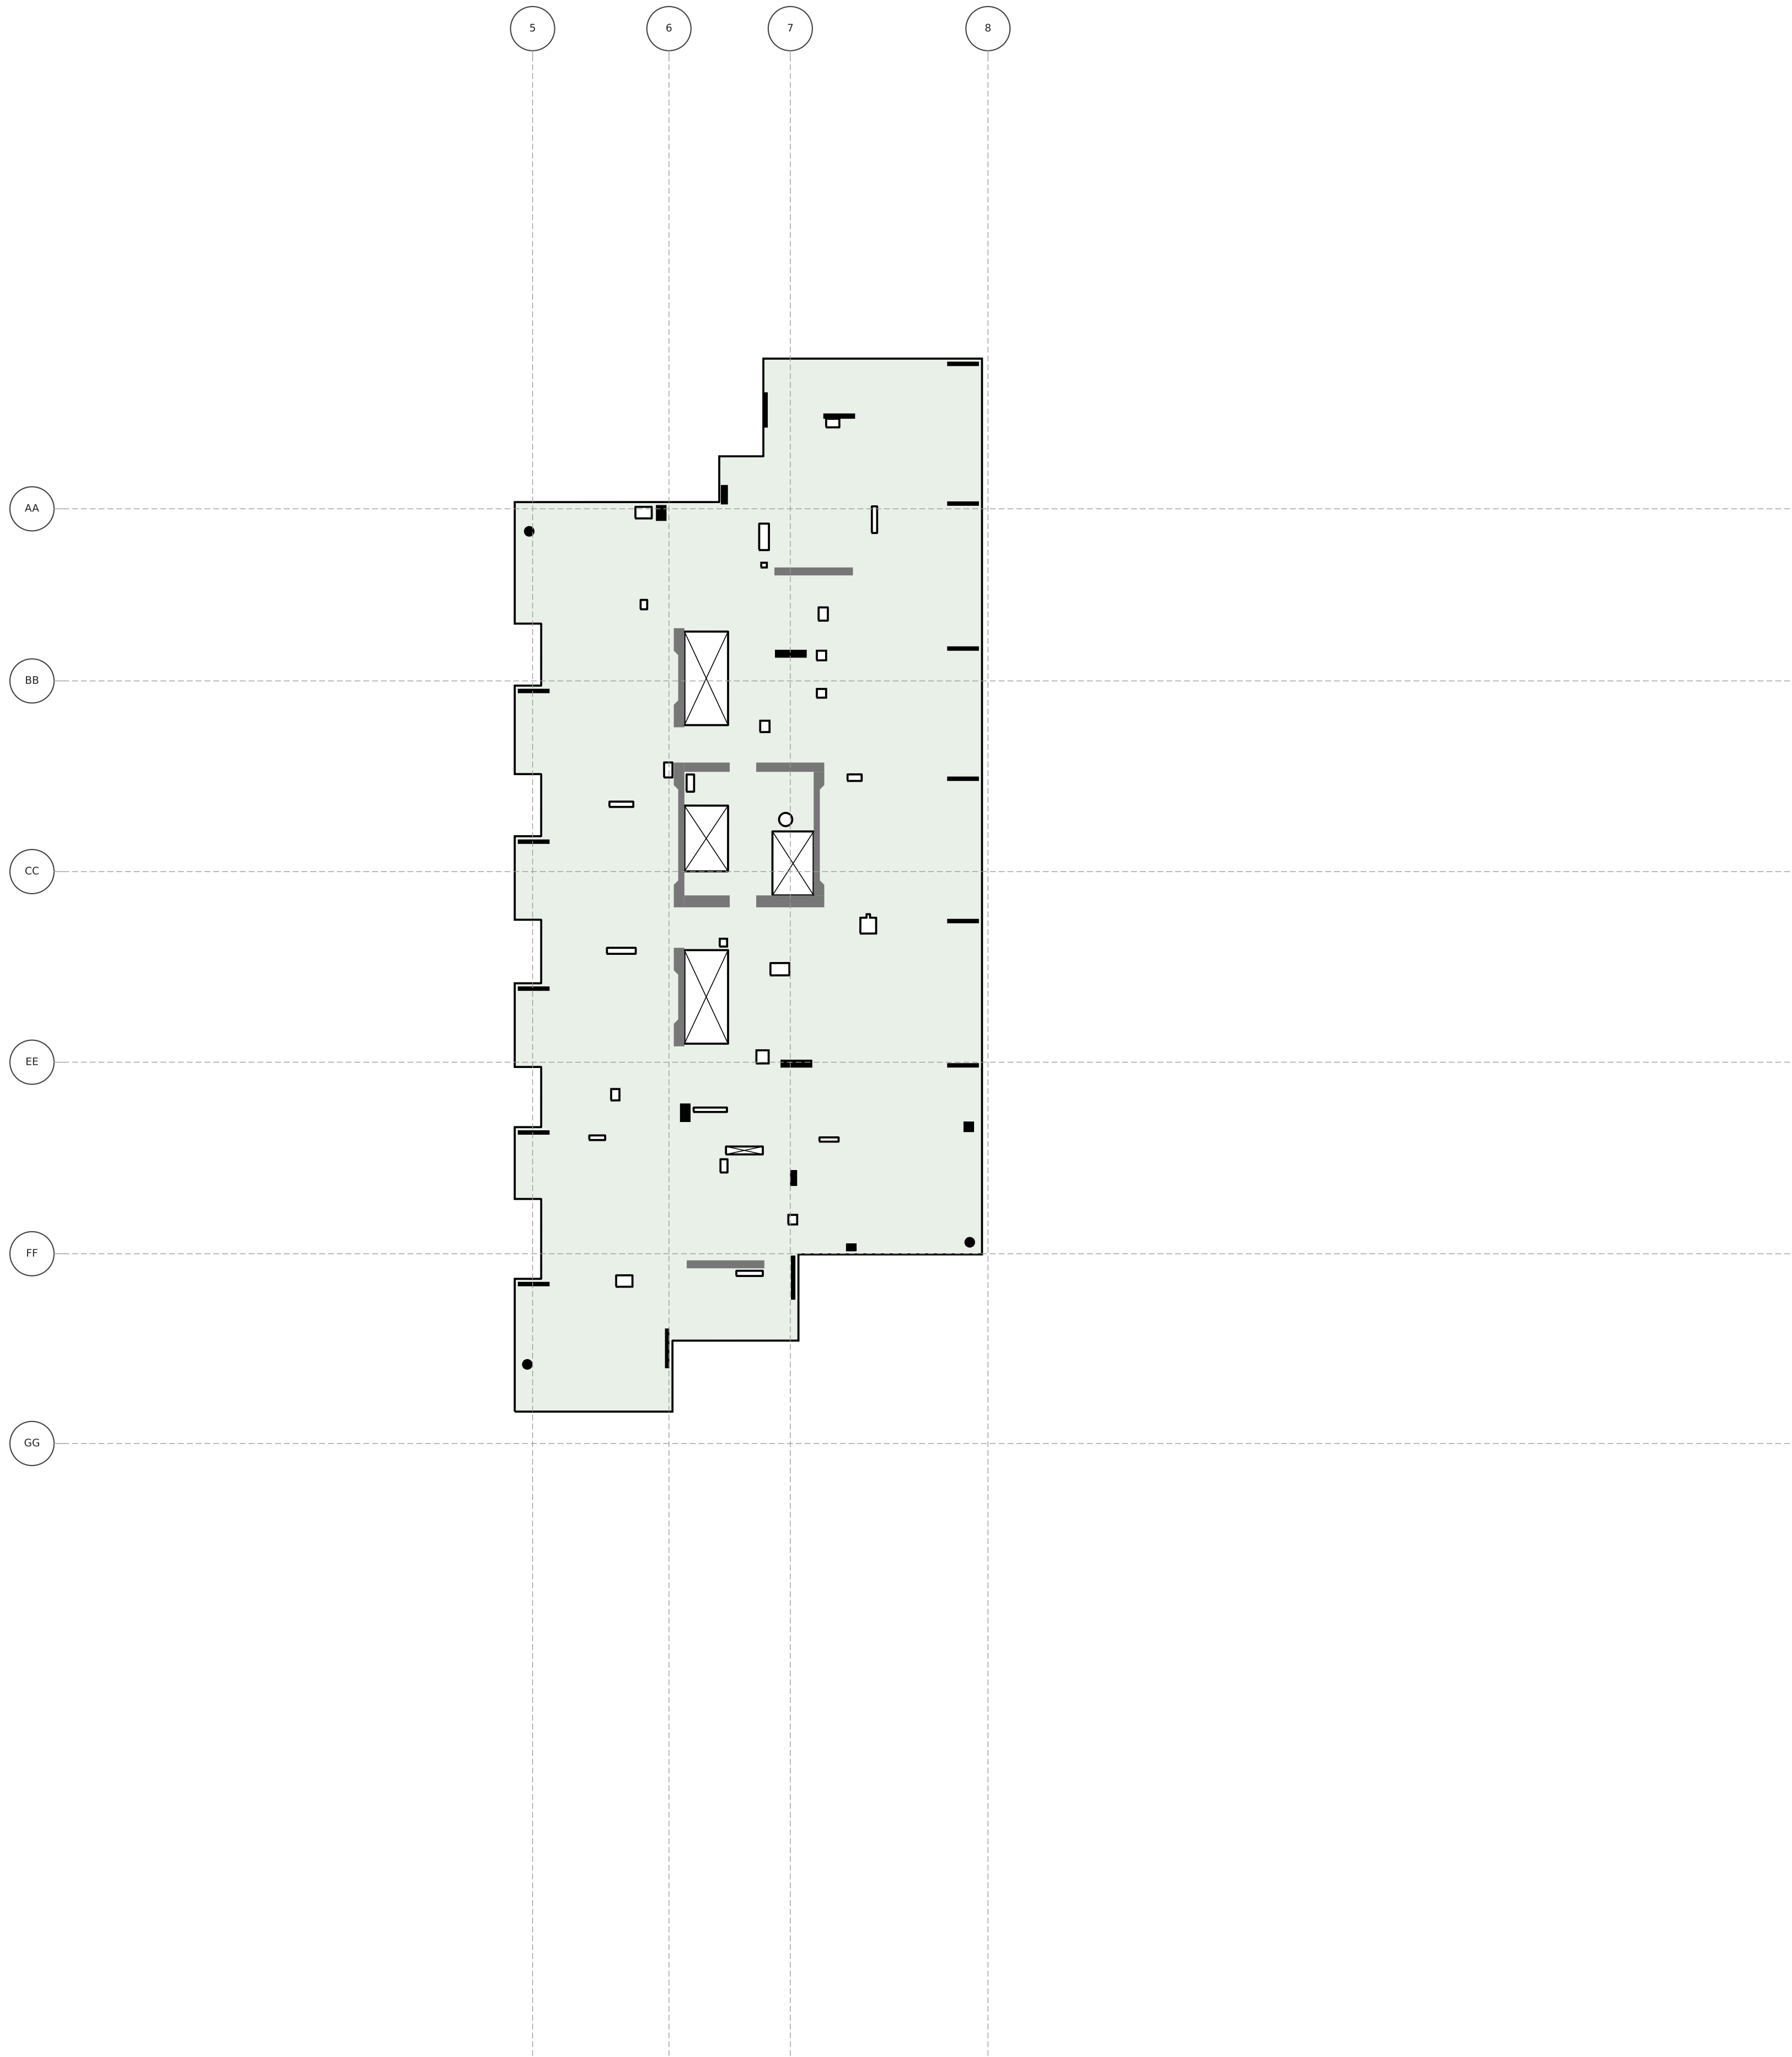


1268 KALAE

LEVEL 24 FLOOR PLAN

T.O.S. 334'-1" · typical slab 7.5" · scale 1" = 20'

Generated from 92743ac6-HI_KALAE_MCC_ST.ifc (Revit scope model) for the McClone Reshore Calculator — geometry only; loading marks are drawn in the calculator.

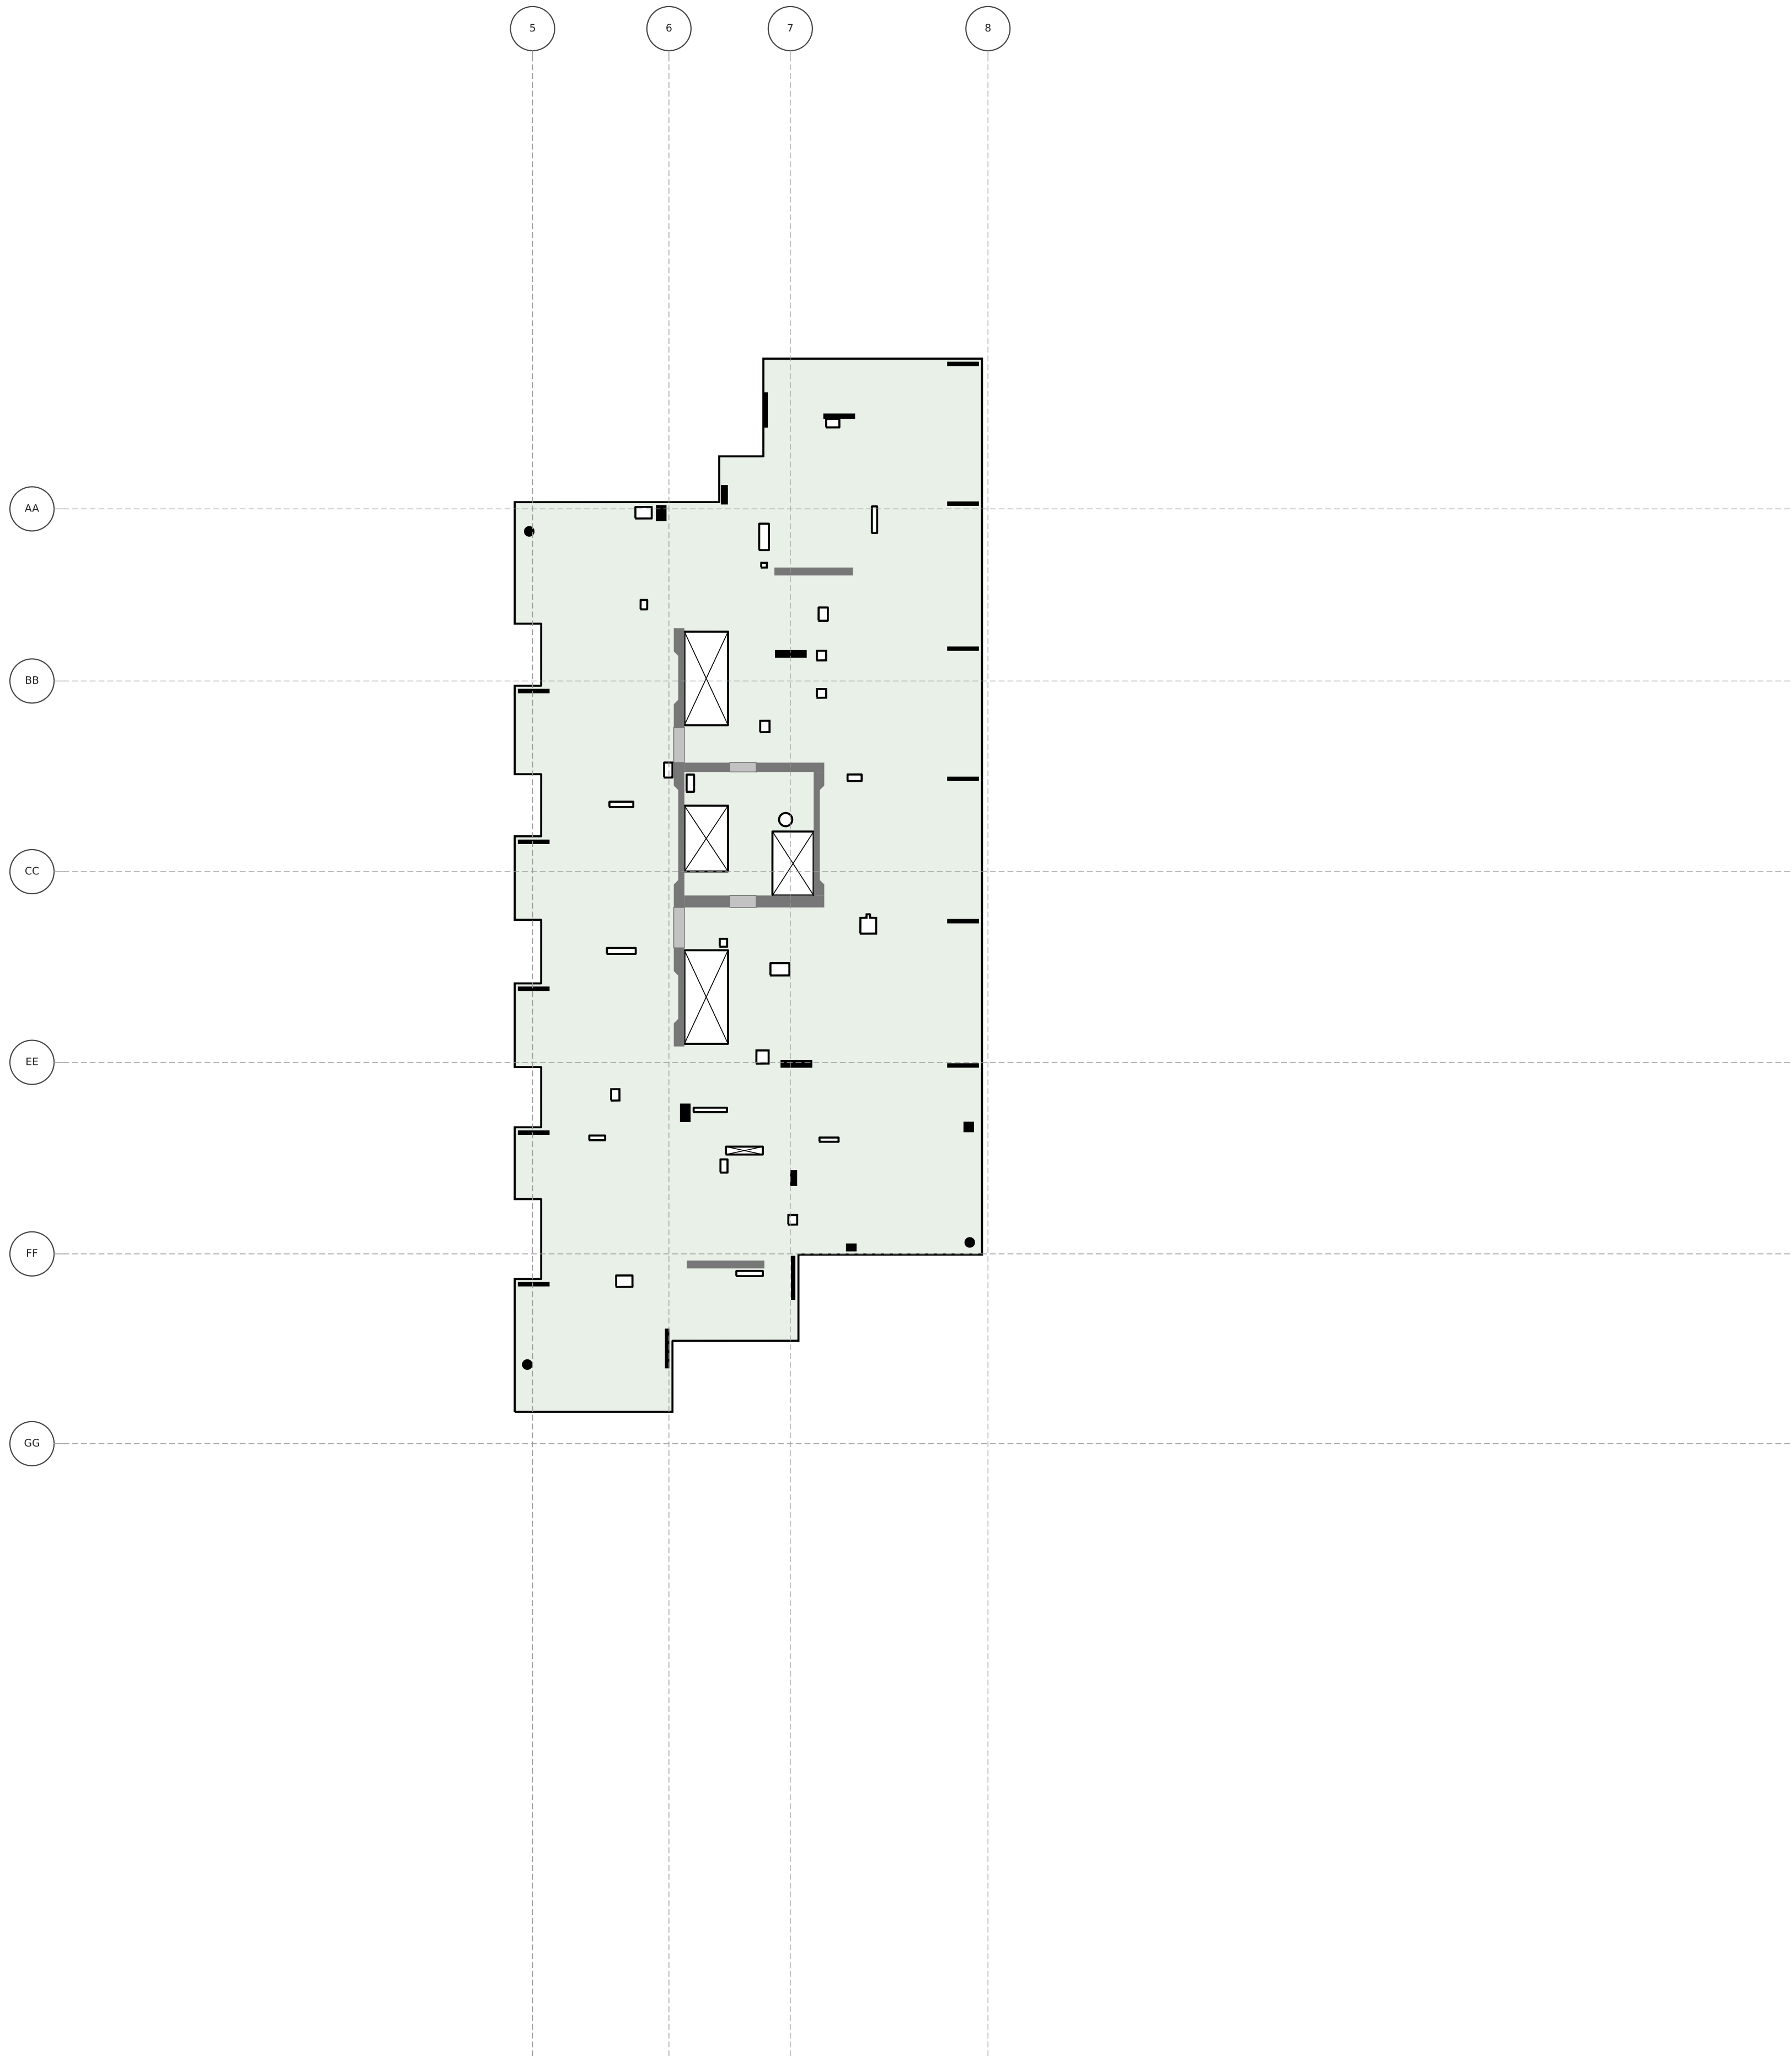


1268 KALAE

LEVEL 25 FLOOR PLAN

T.O.S. 343'-9.5" · typical slab 7.5" · scale 1" = 20'

Generated from 92743ac6-HI_KALAE_MCC_ST.ifc (Revit scope model) for the McClone Reshore Calculator — geometry only; loading marks are drawn in the calculator.

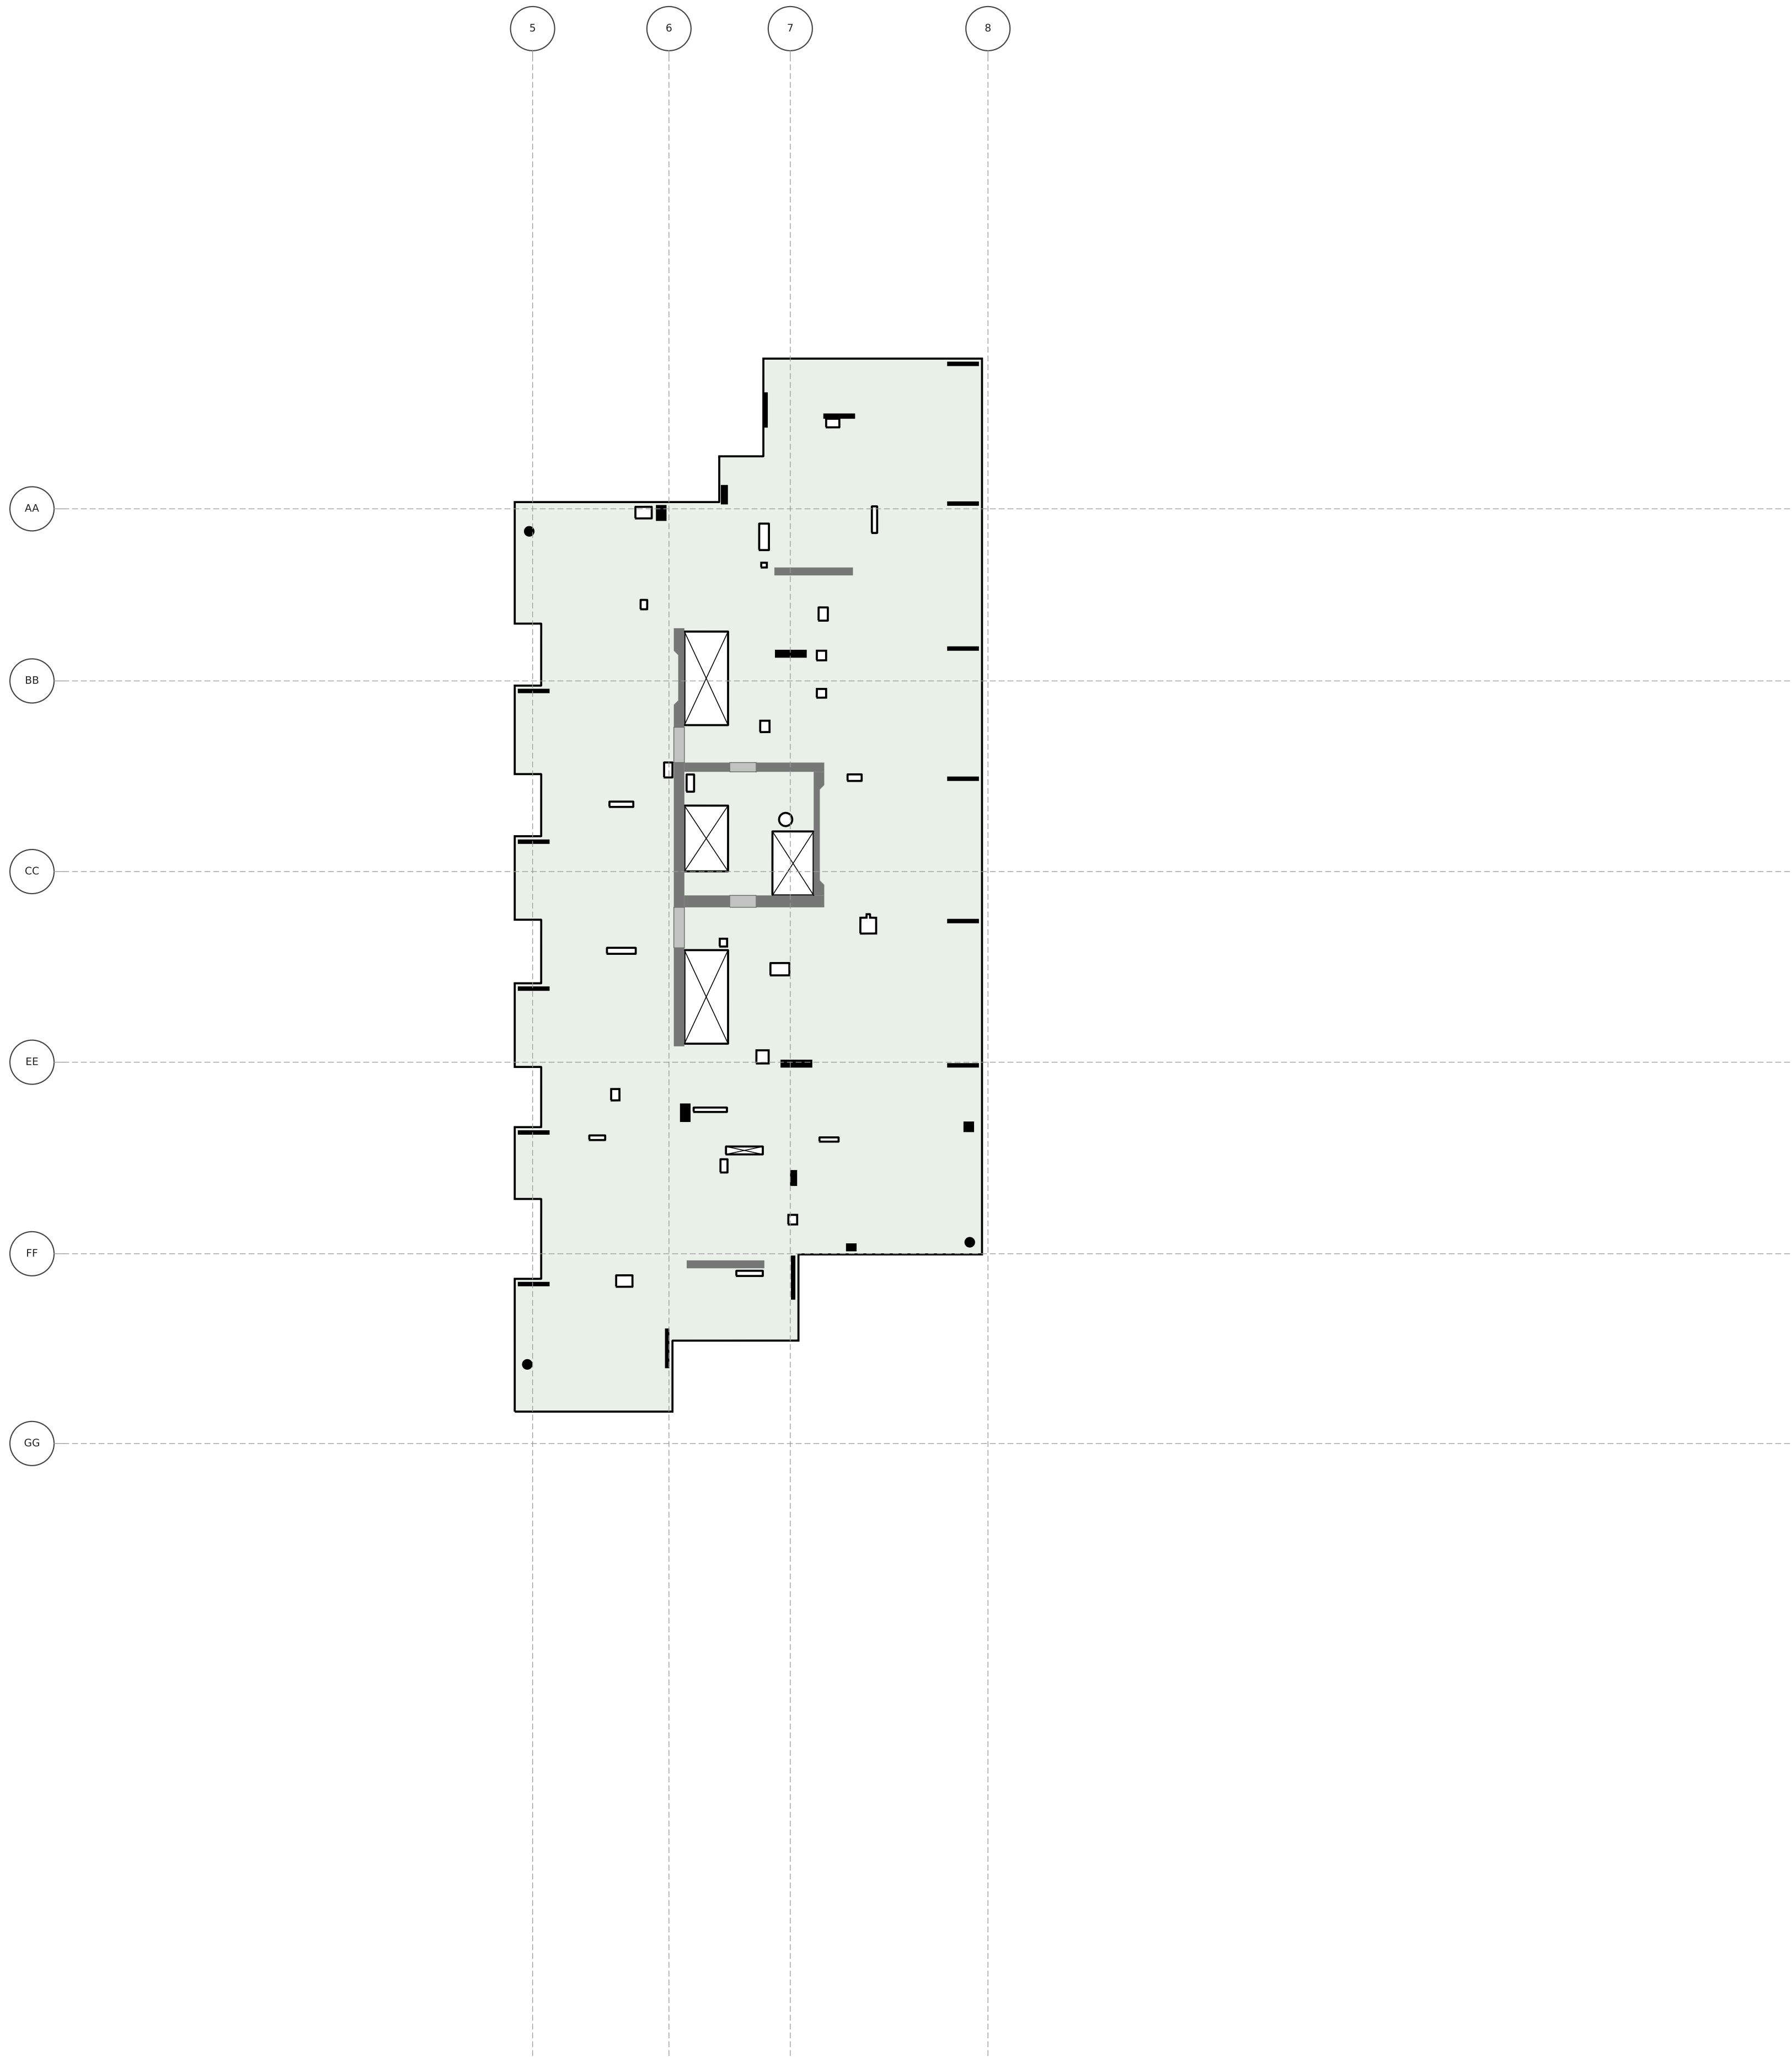


1268 KALAE

LEVEL 26 FLOOR PLAN

T.O.S. 353'-6" · typical slab 7.5" · scale 1" = 20'

Generated from 92743ac6-HI_KALAE_MCC_ST.ifc (Revit scope model) for the McClone Reshore Calculator — geometry only; loading marks are drawn in the calculator.

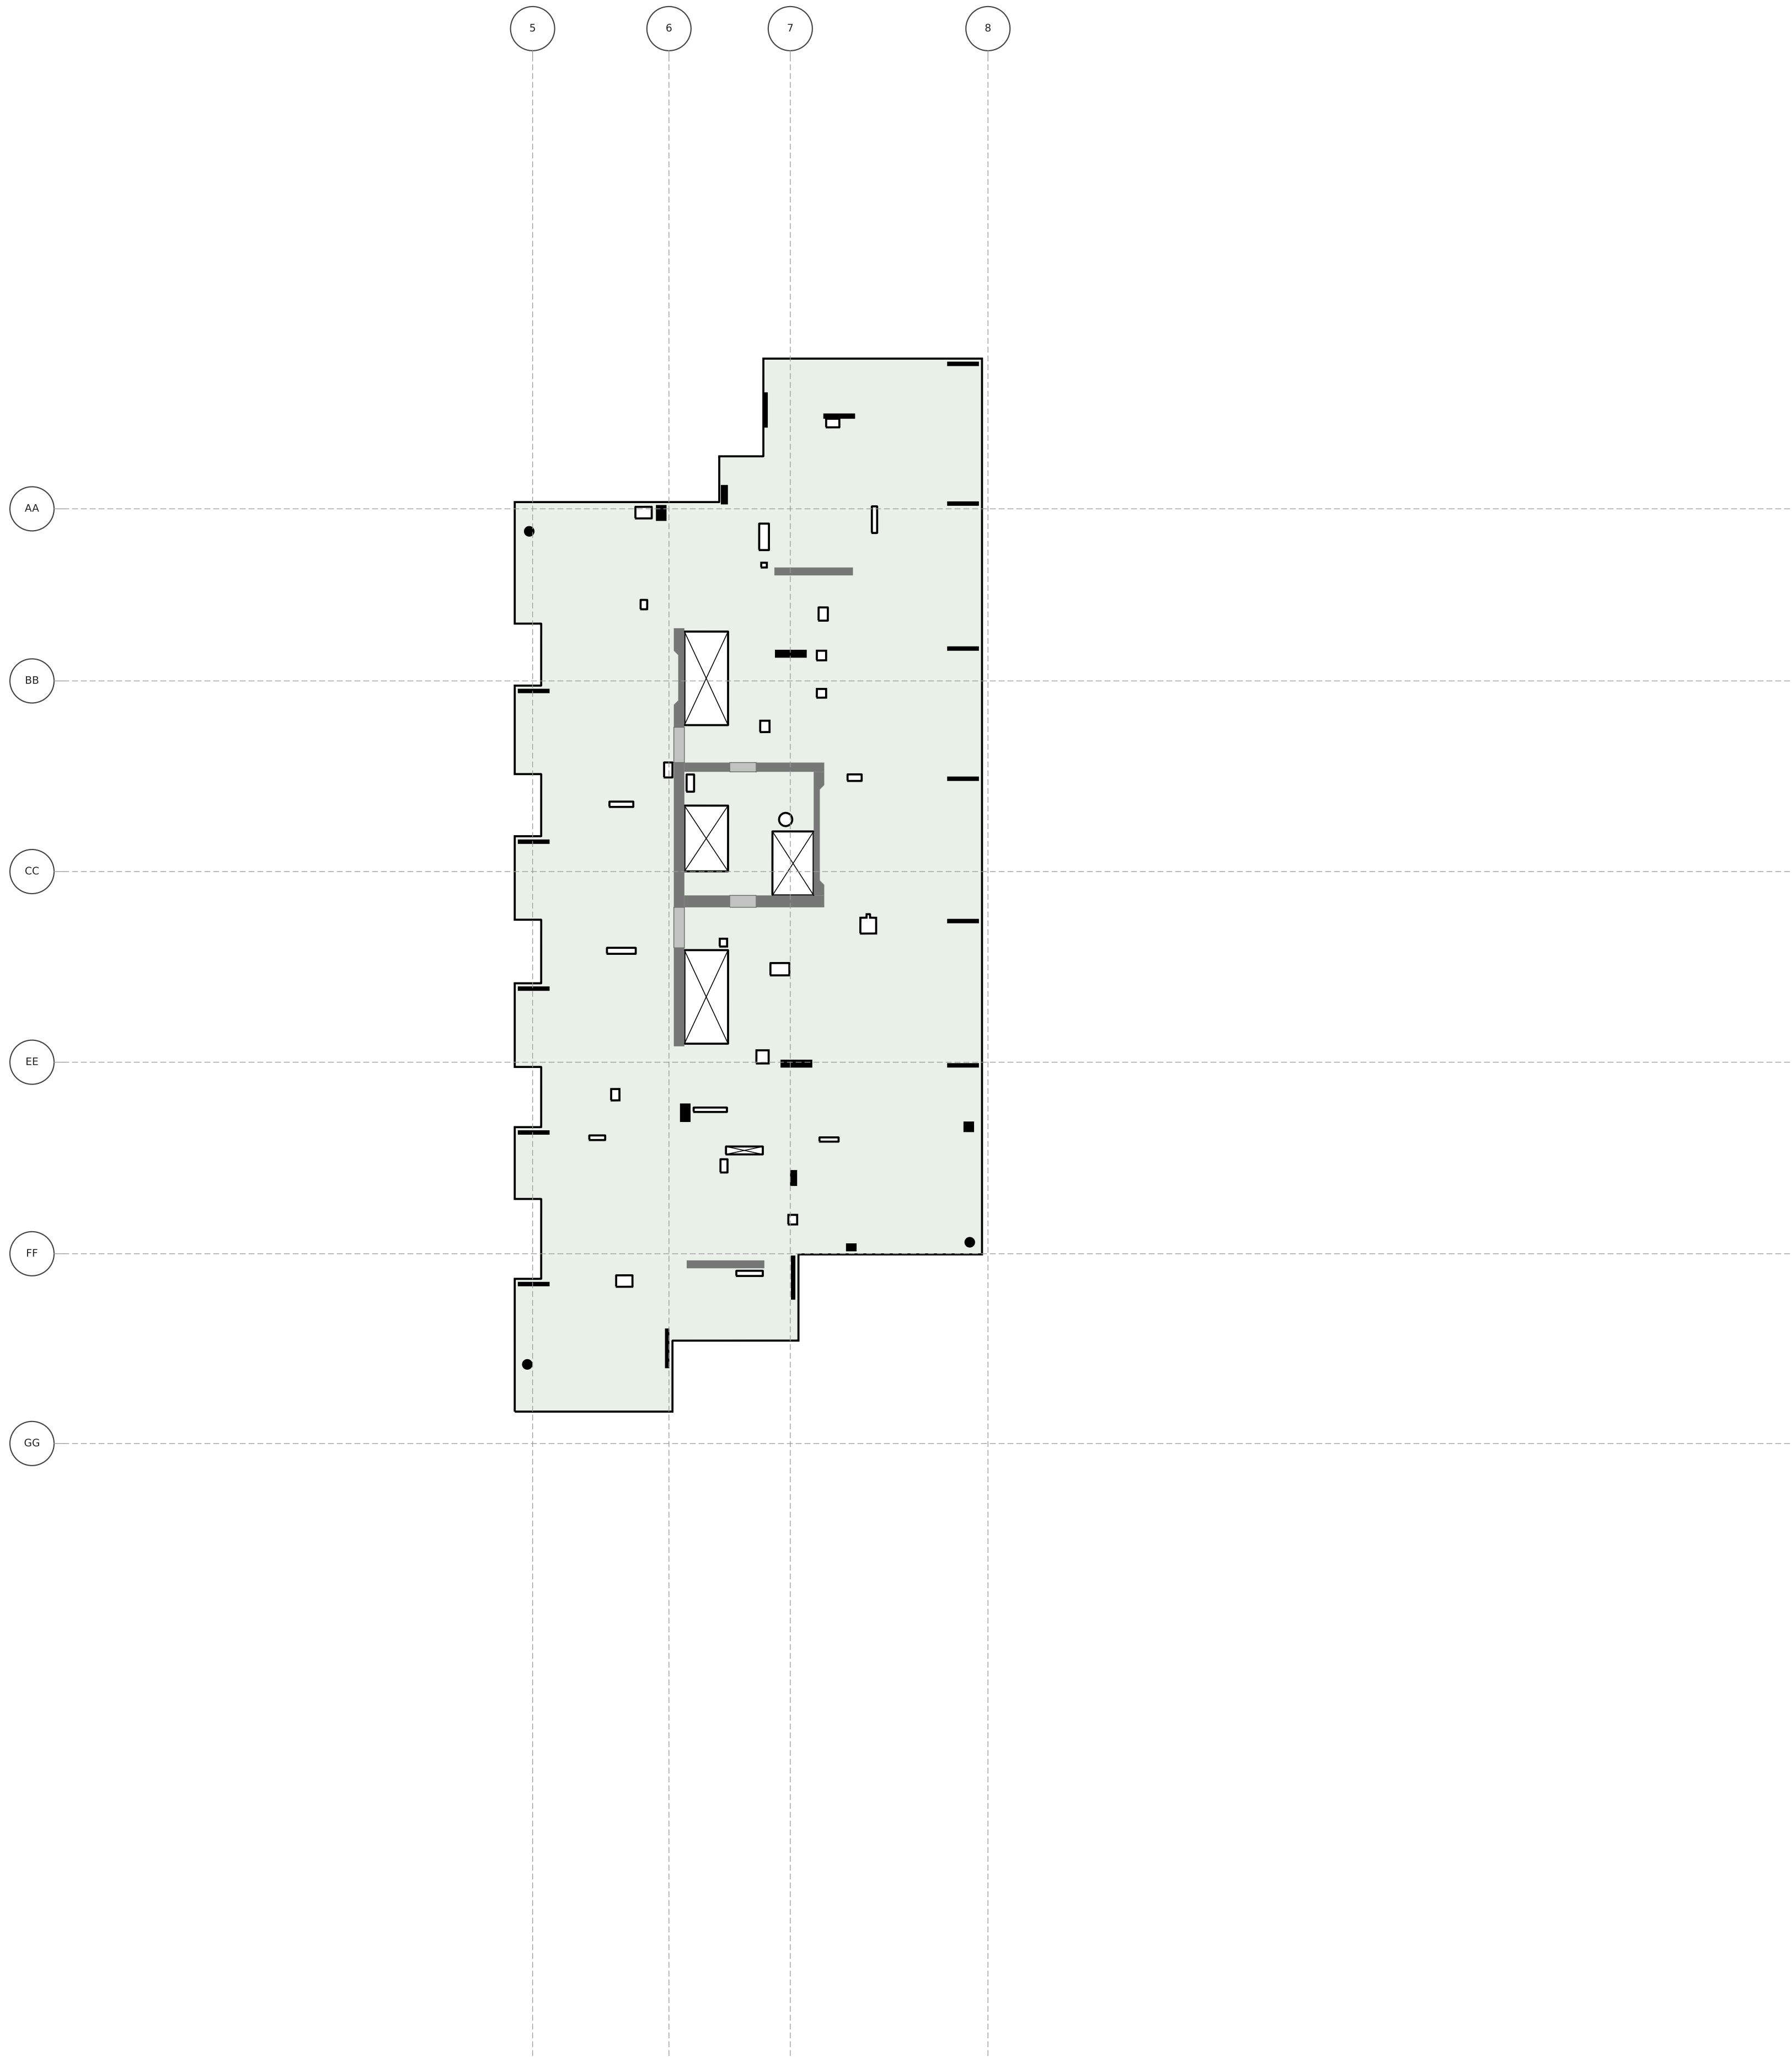


1268 KALAE

LEVEL 27 FLOOR PLAN

T.O.S. 363'-2.5" · typical slab 7.5" · scale 1" = 20'

Generated from 92743ac6-HI_KALAE_MCC_ST.ifc (Revit scope model) for the McClone Reshore Calculator — geometry only; loading marks are drawn in the calculator.

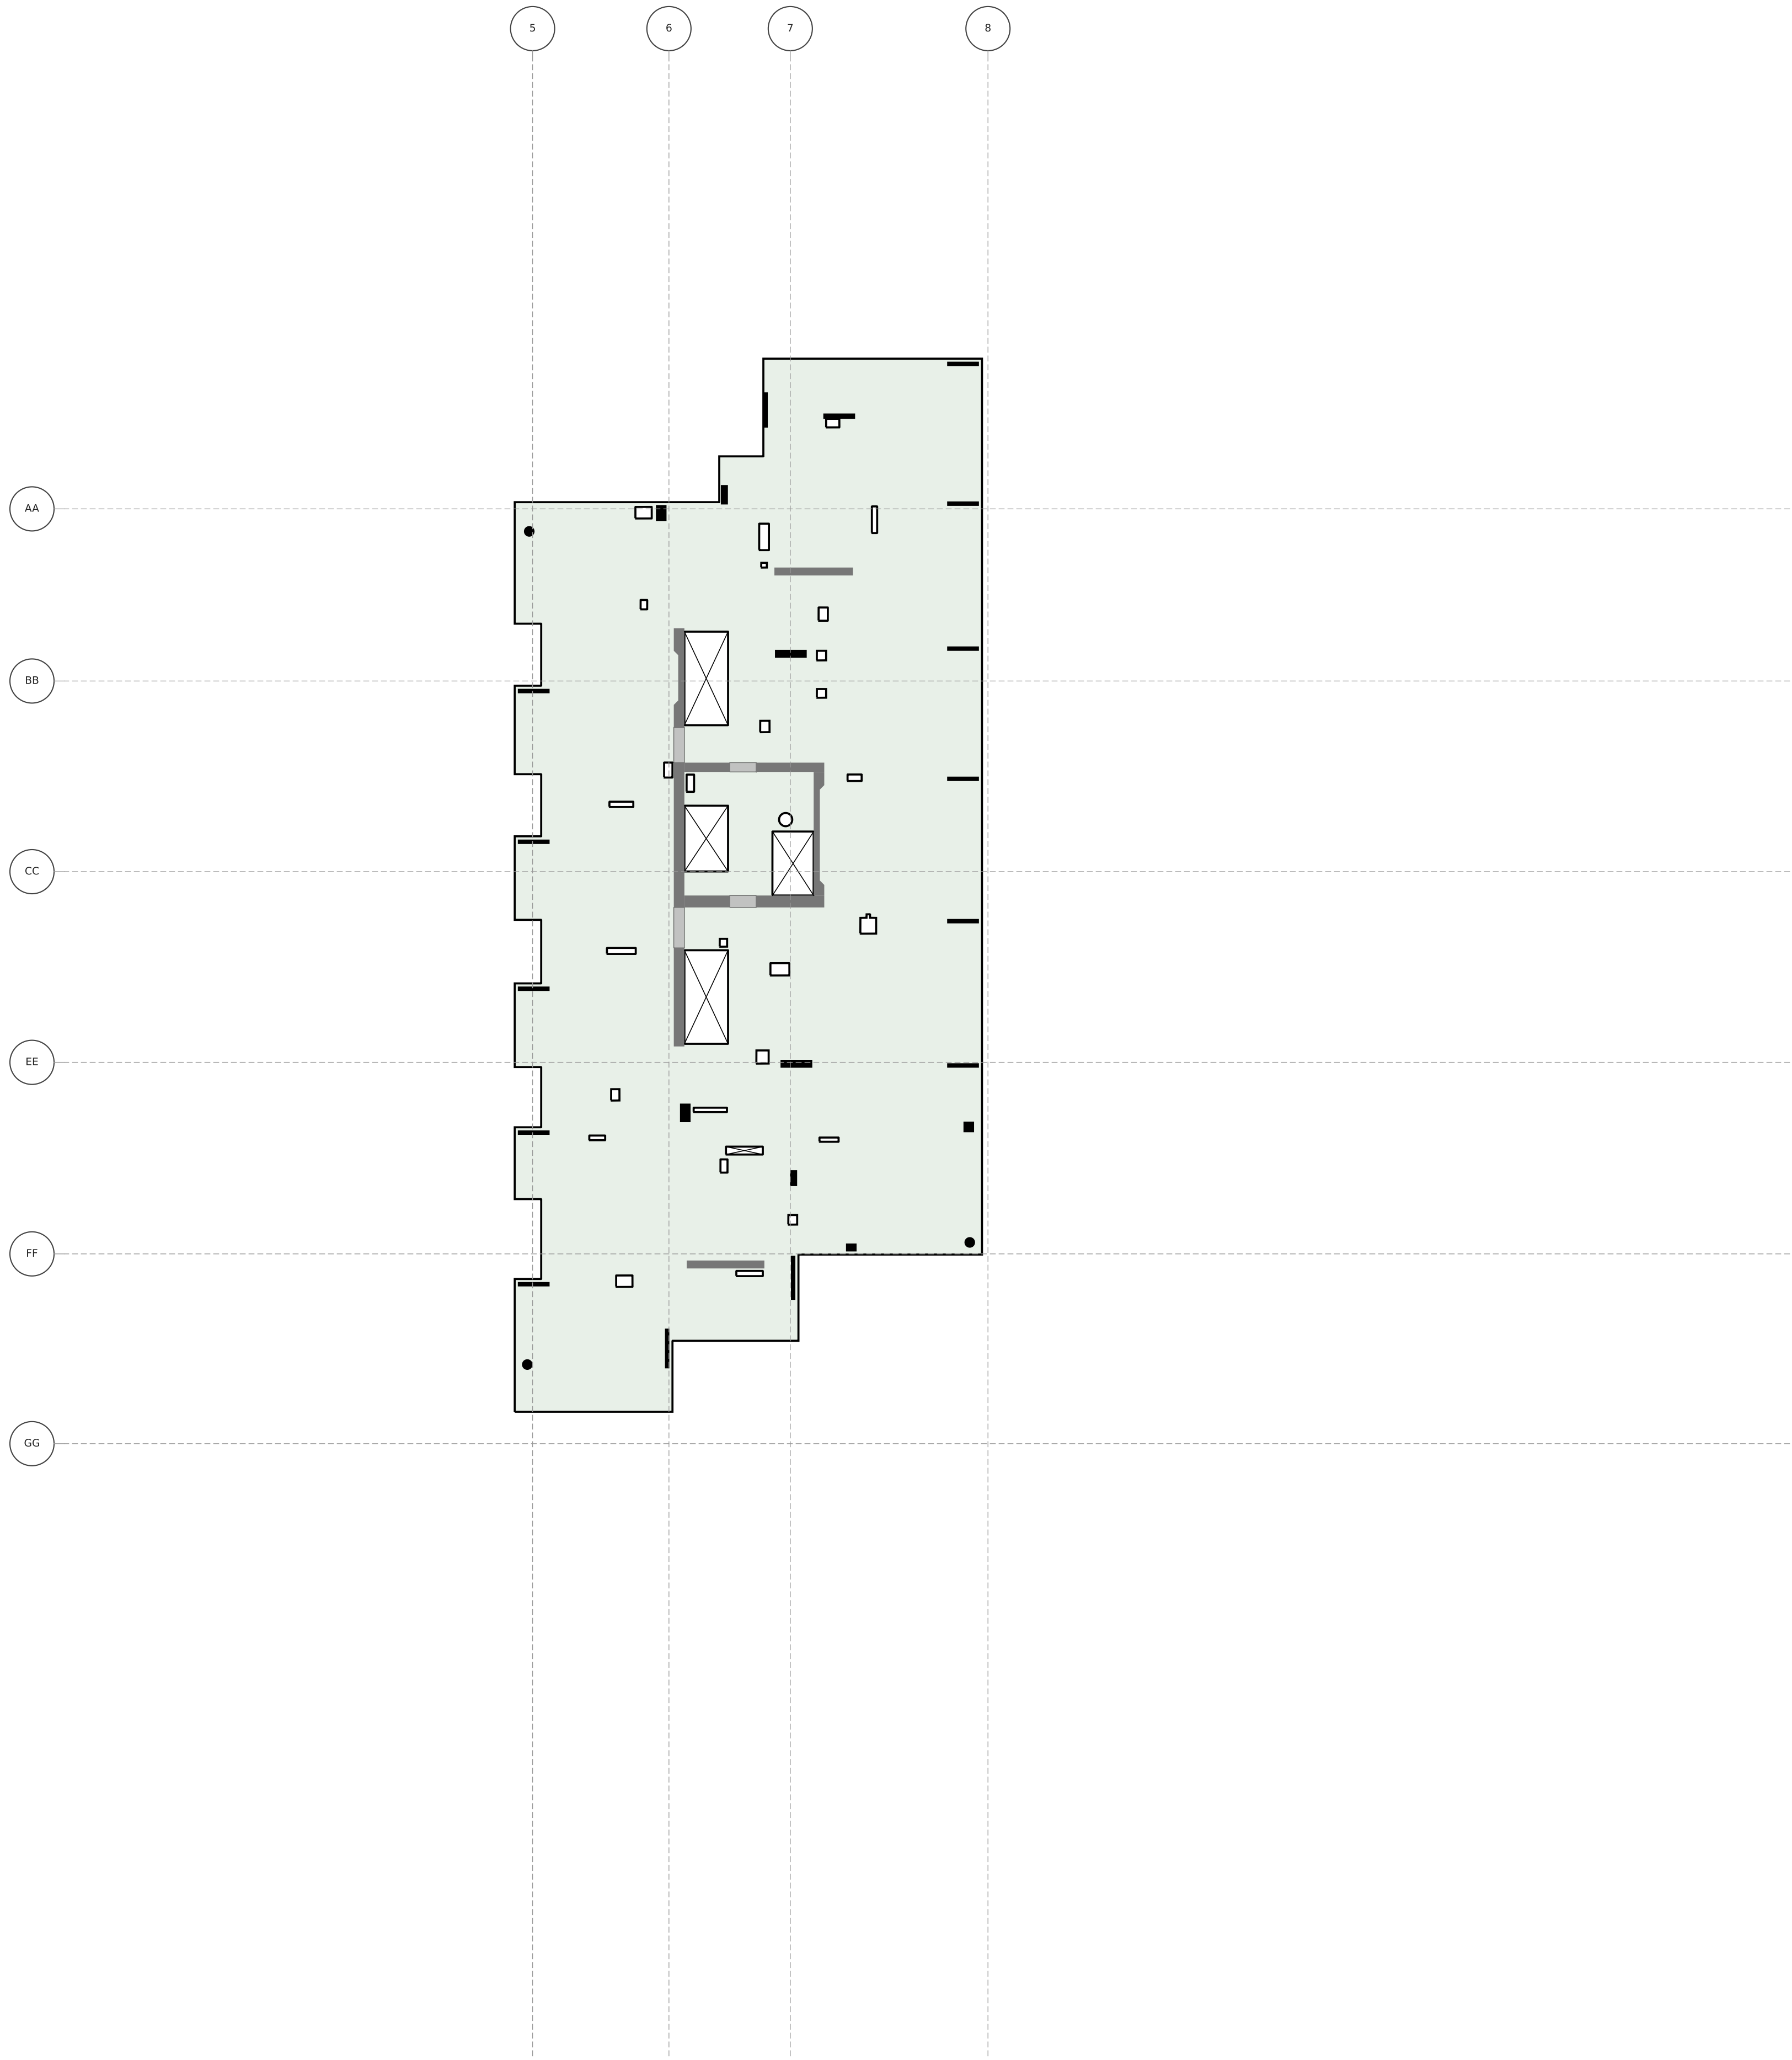


1268 KALAE

LEVEL 28 FLOOR PLAN

T.O.S. 372'-11" · typical slab 7.5" · scale 1" = 20'

Generated from 92743ac6-HI_KALAE_MCC_ST.ifc (Revit scope model) for the McClone Reshore Calculator — geometry only; loading marks are drawn in the calculator.

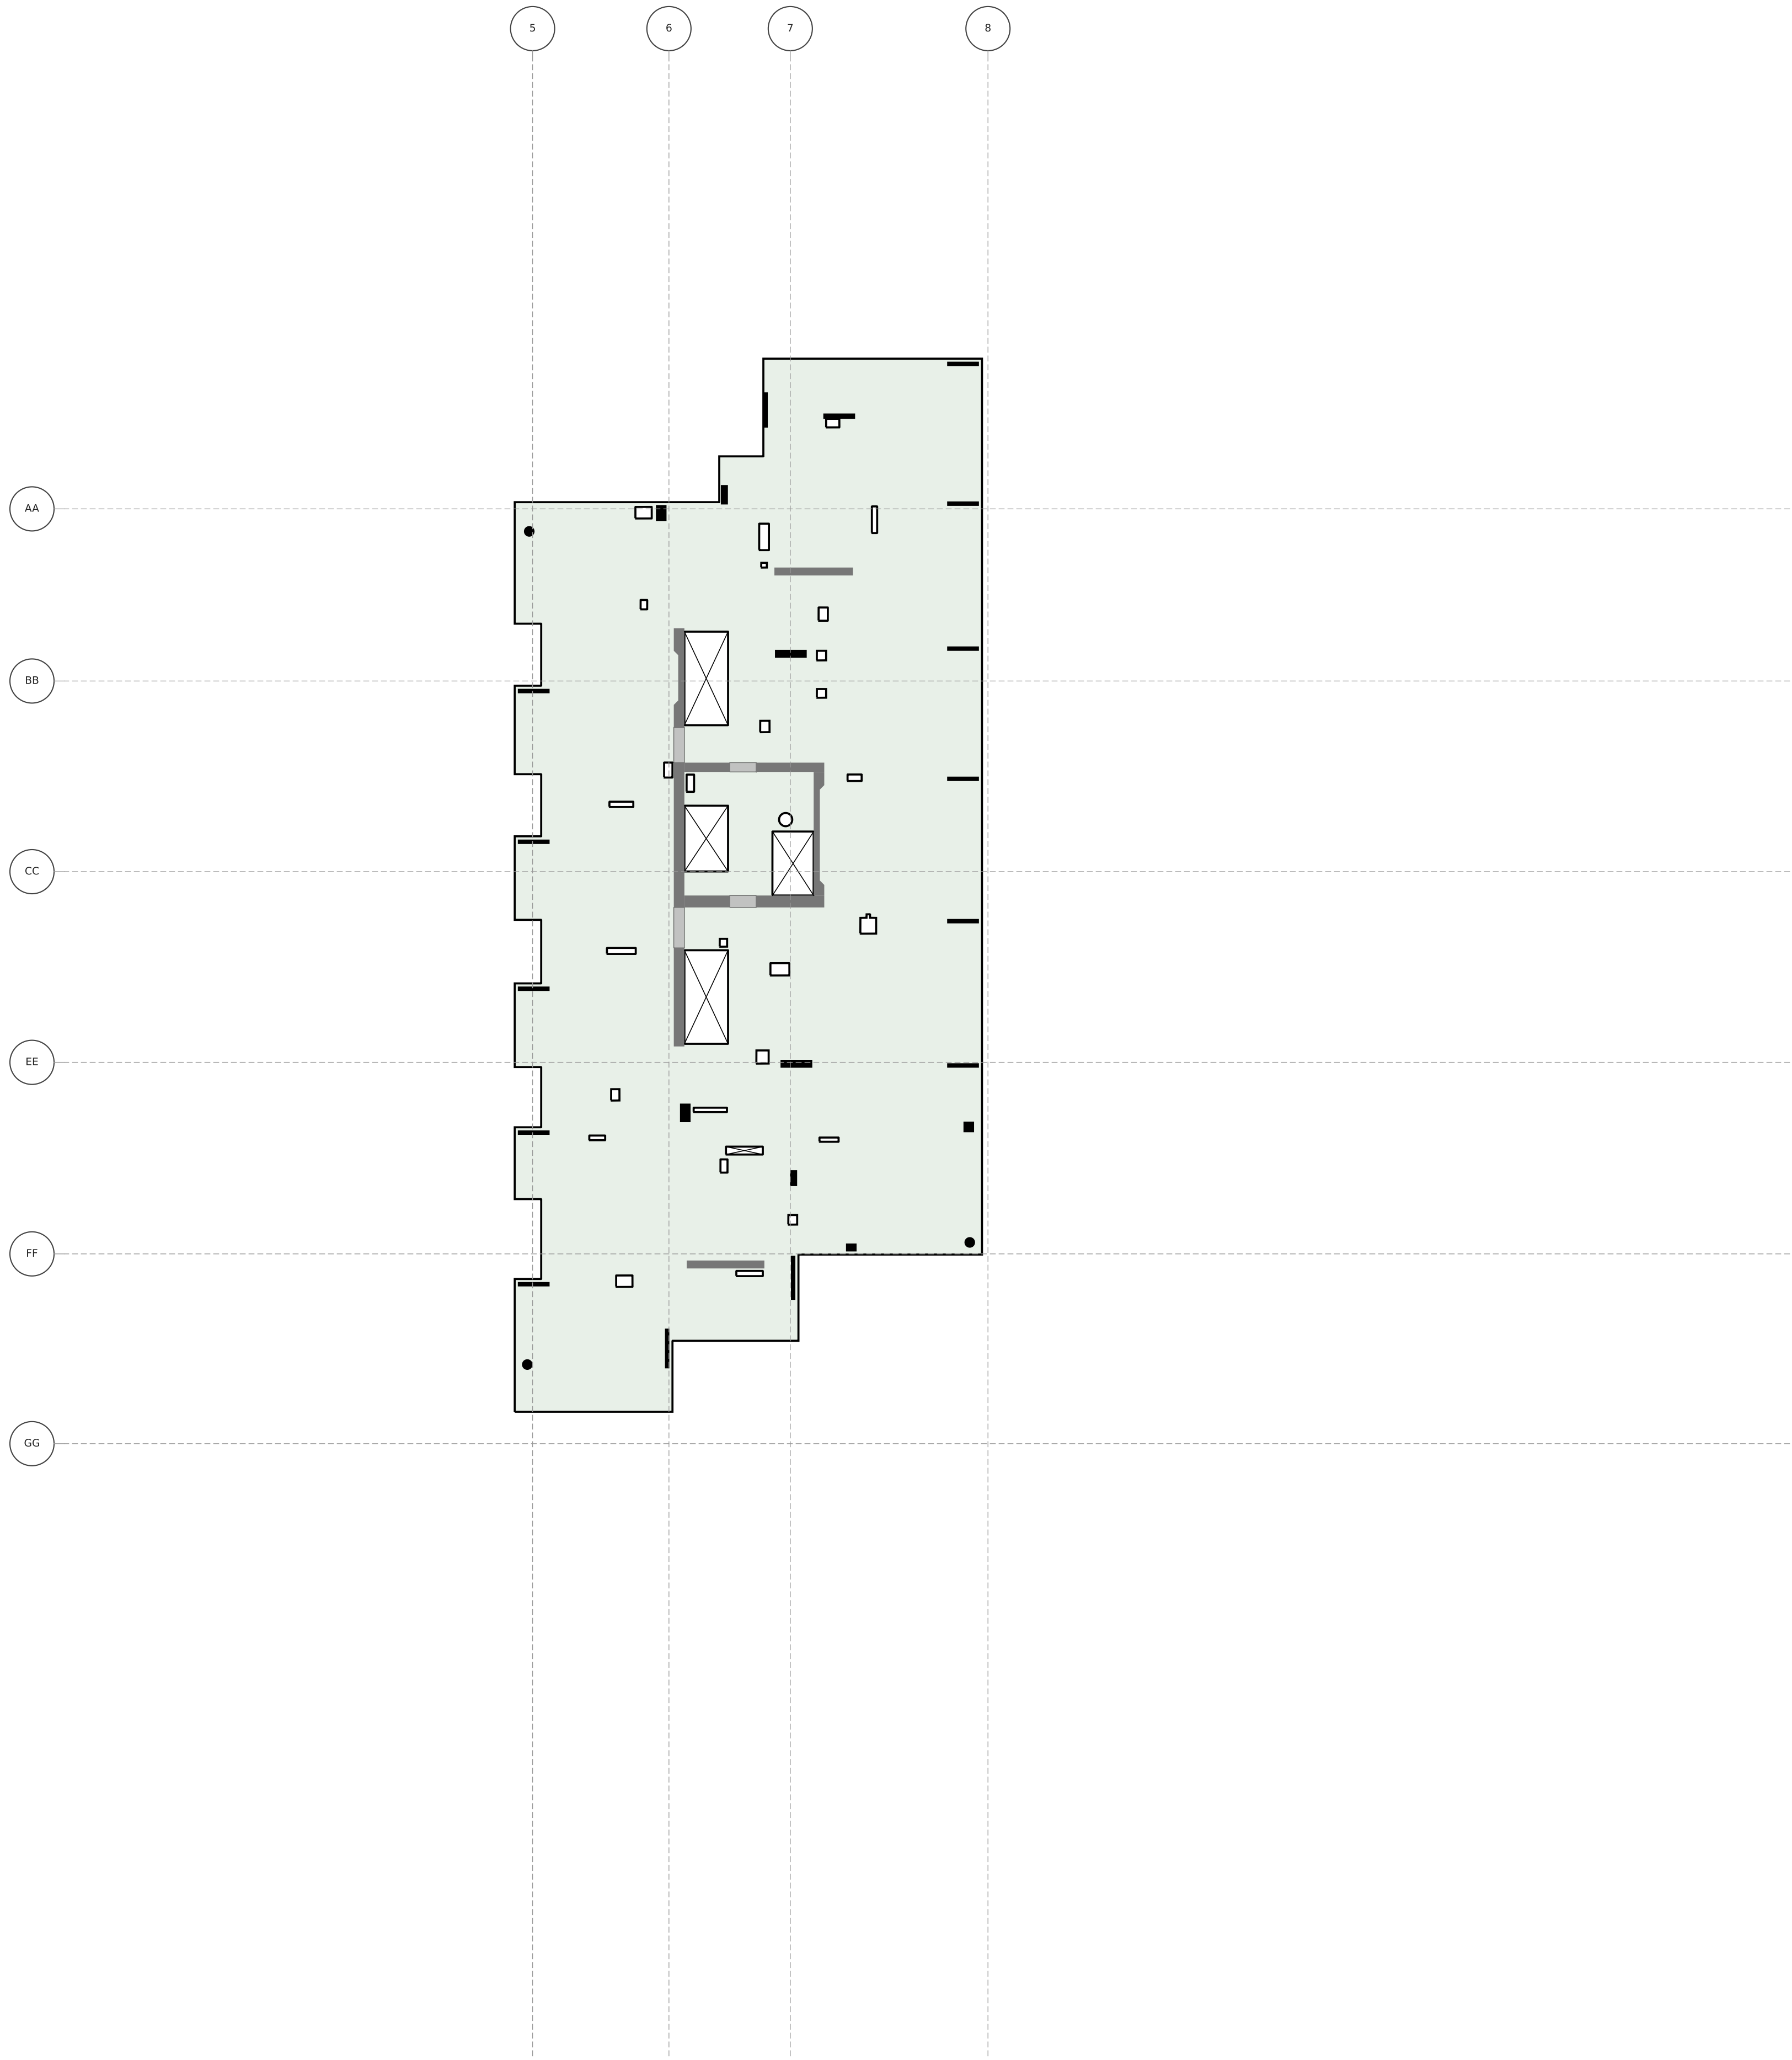


1268 KALAE

LEVEL 29 FLOOR PLAN

T.O.S. 382'-7.5" · typical slab 7.5" · scale 1" = 20'

Generated from 92743ac6-HI_KALAE_MCC_ST.ifc (Revit scope model) for the McClone Reshore Calculator — geometry only; loading marks are drawn in the calculator.

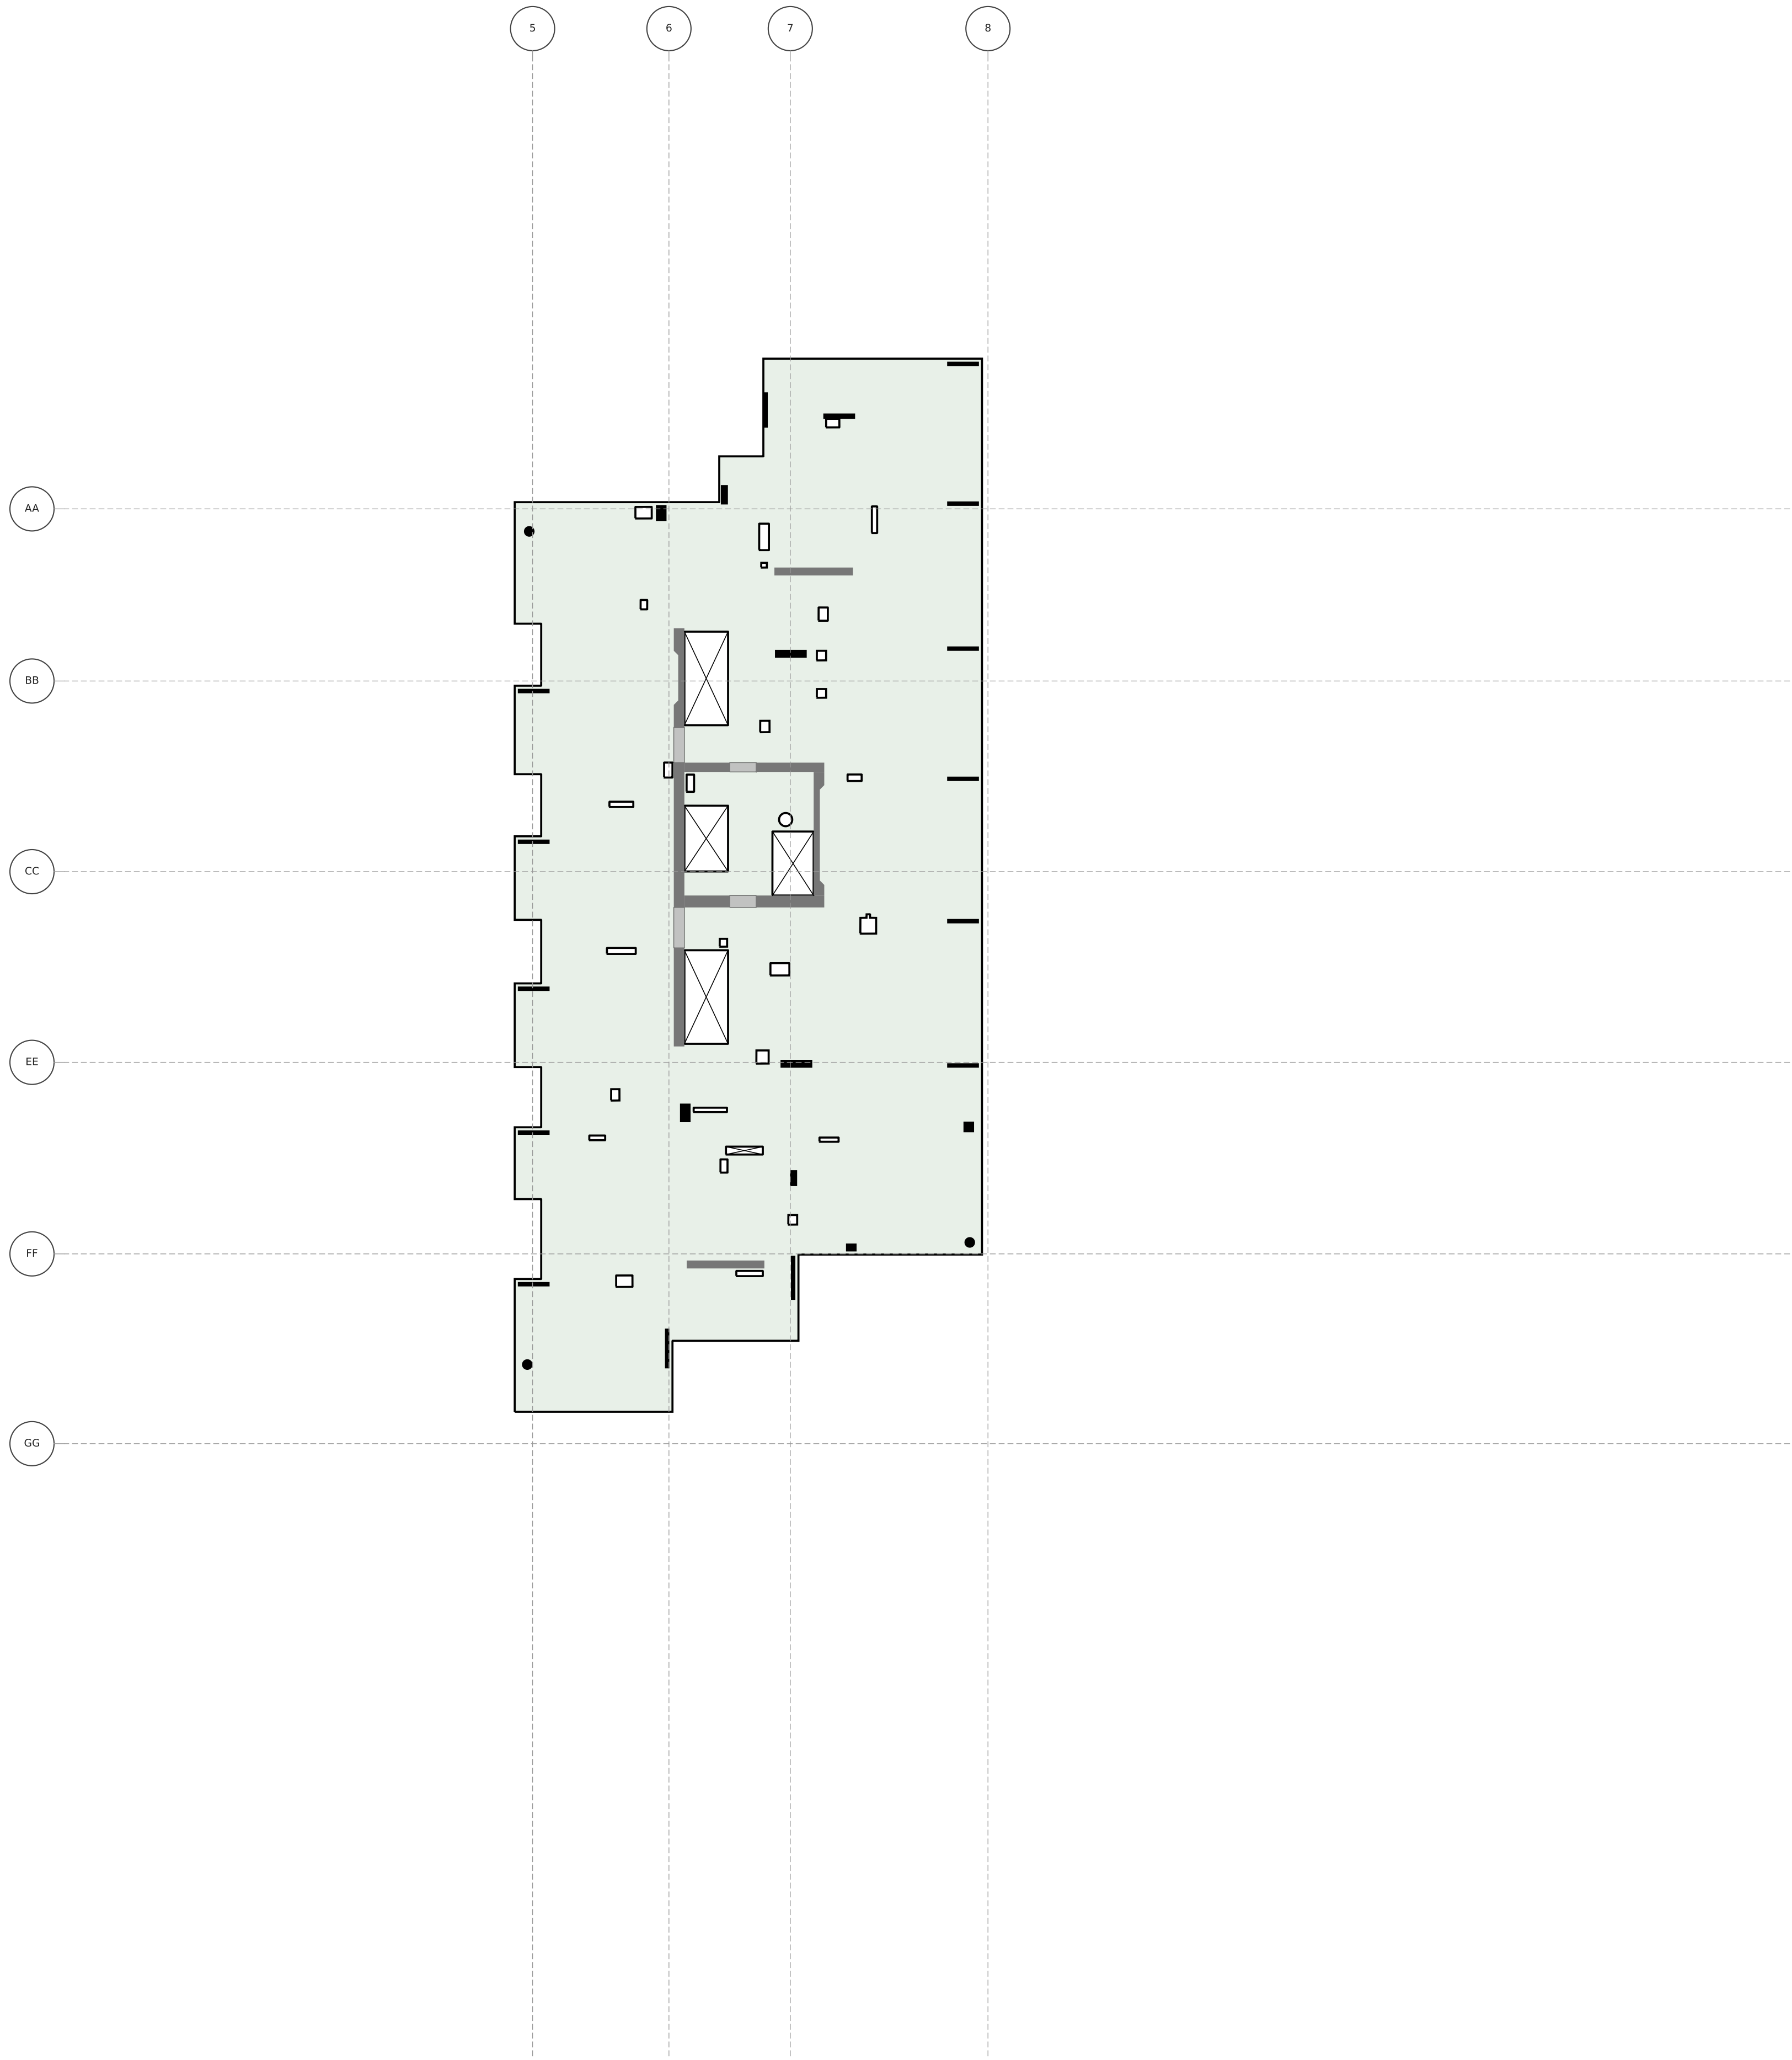


1268 KALAE

LEVEL 30 FLOOR PLAN

T.O.S. 392'-4" · typical slab 7.5" · scale 1" = 20'

Generated from 92743ac6-HI_KALAE_MCC_ST.ifc (Revit scope model) for the McClone Reshore Calculator — geometry only; loading marks are drawn in the calculator.

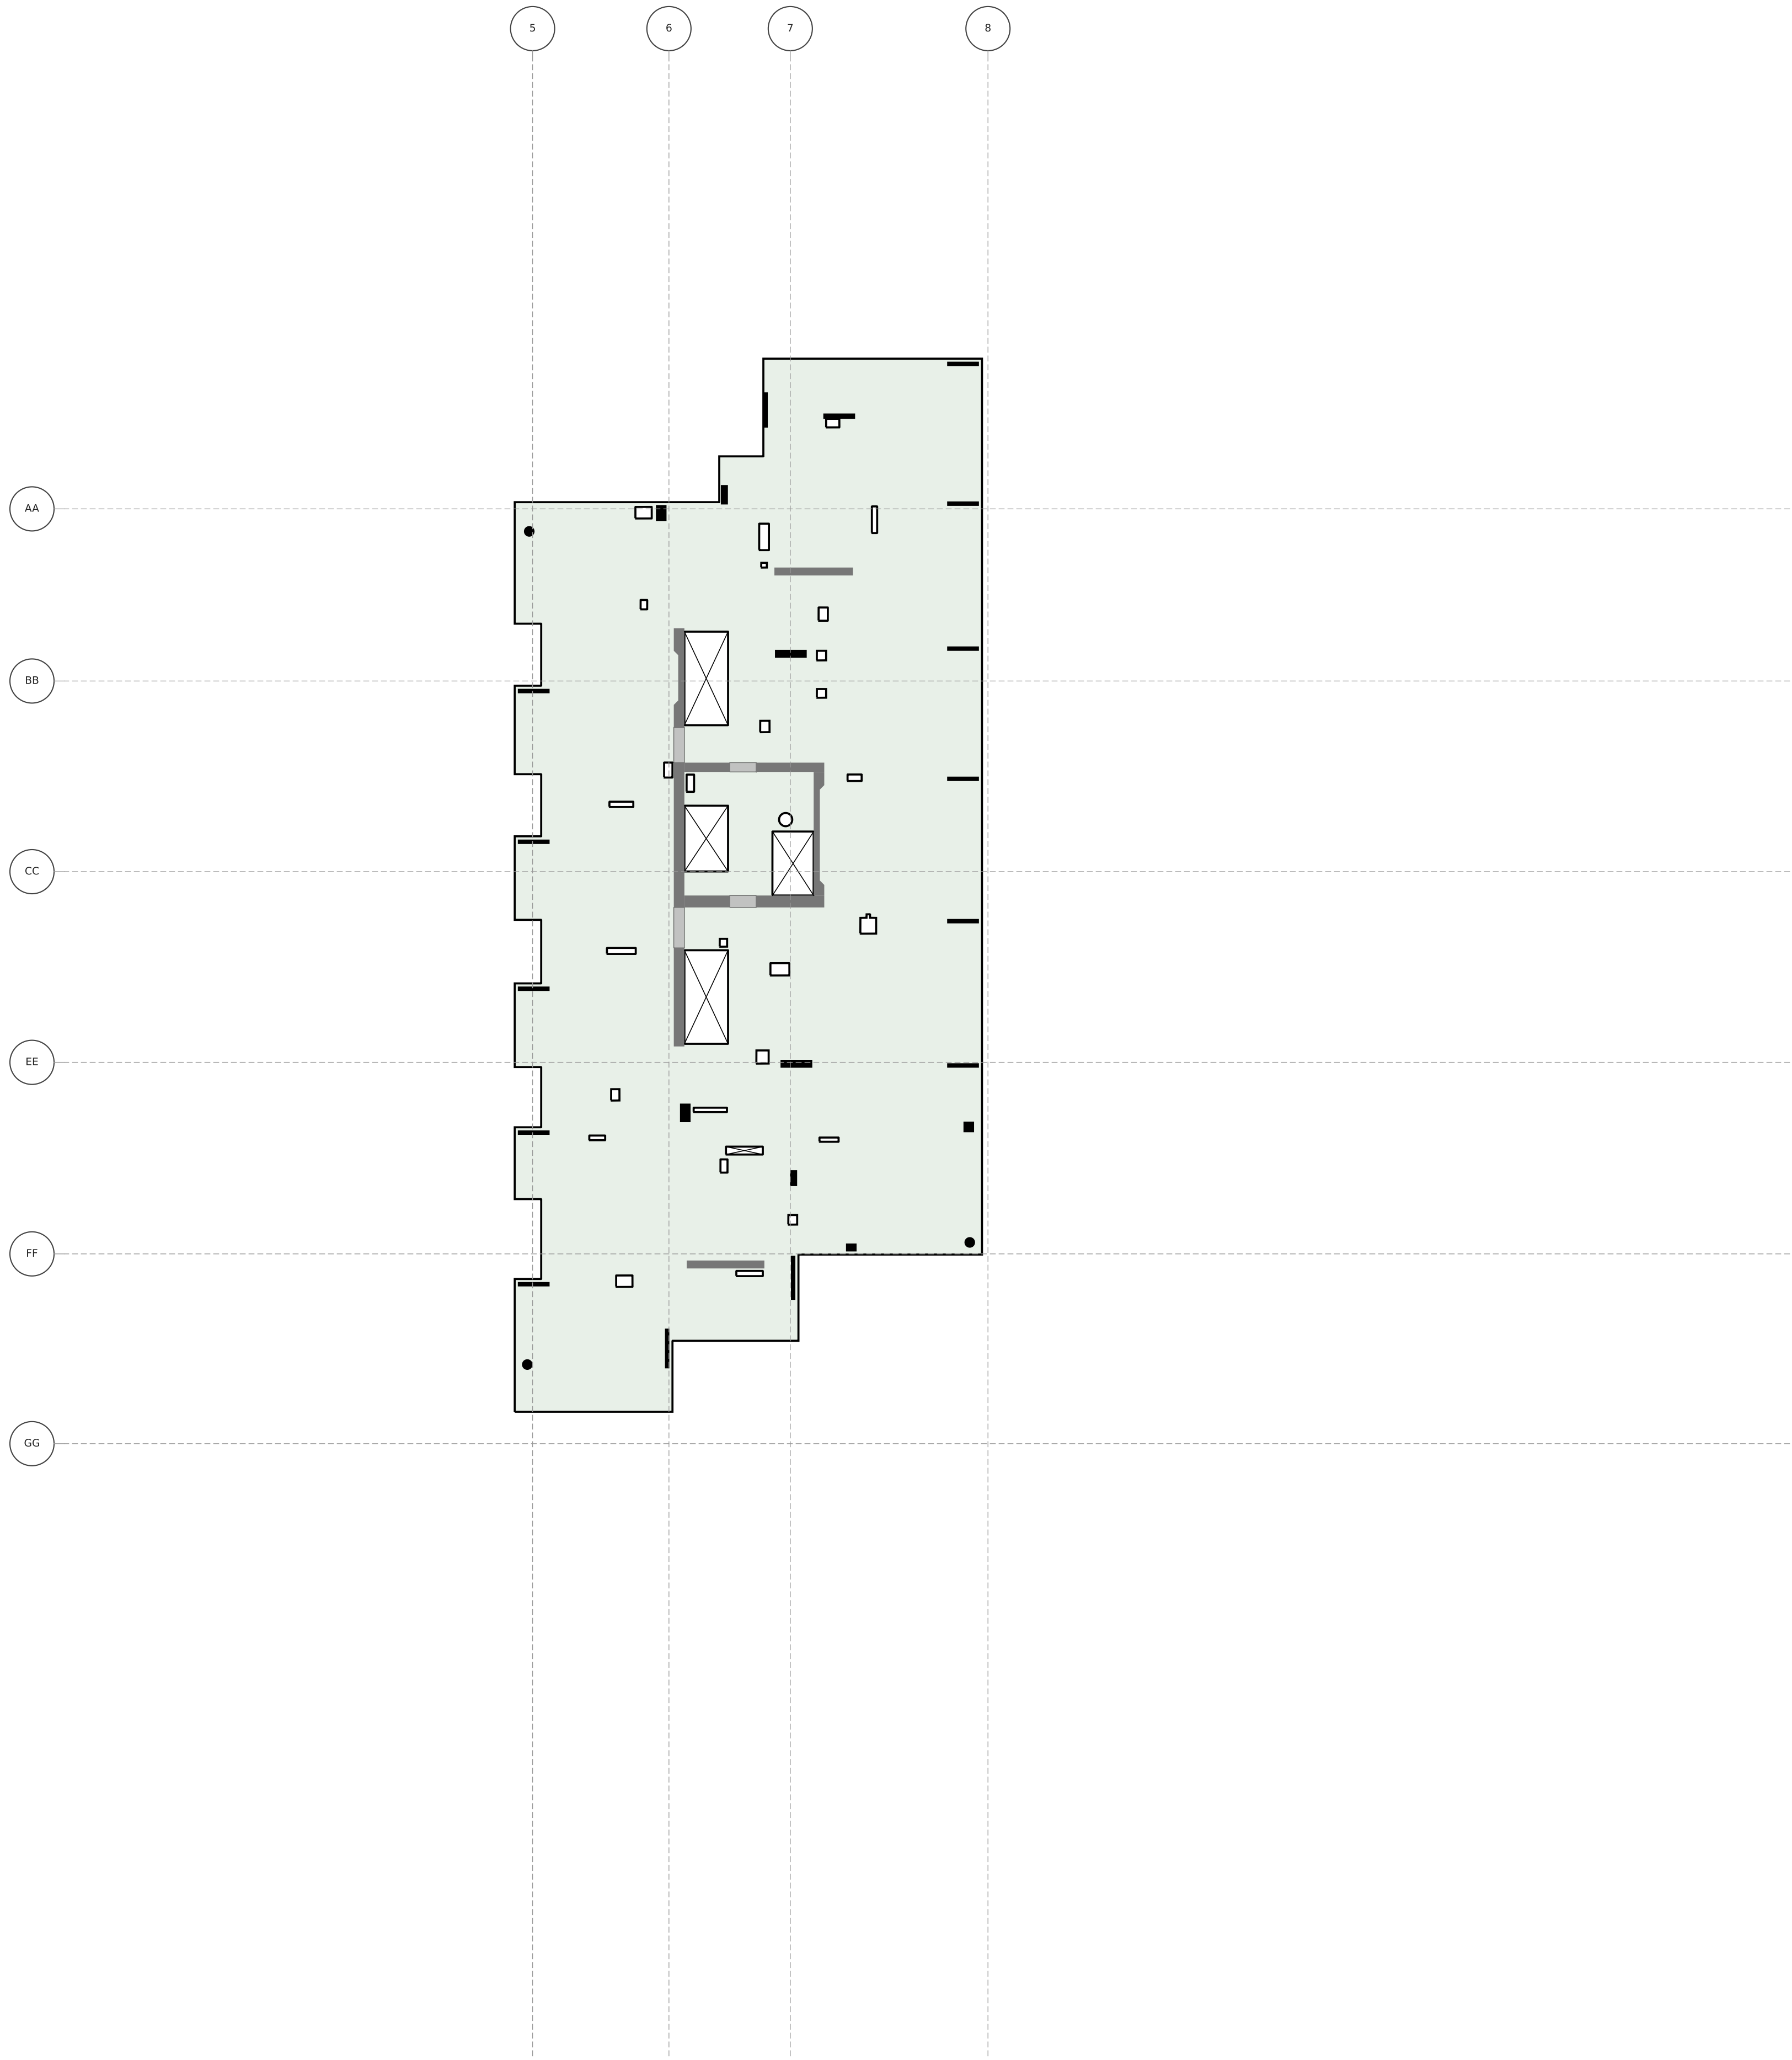


1268 KALAE

LEVEL 31 FLOOR PLAN

T.O.S. 402'-0.5" · typical slab 7.5" · scale 1" = 20'

Generated from 92743ac6-HI_KALAE_MCC_ST.ifc (Revit scope model) for the McClone Reshore Calculator — geometry only; loading marks are drawn in the calculator.

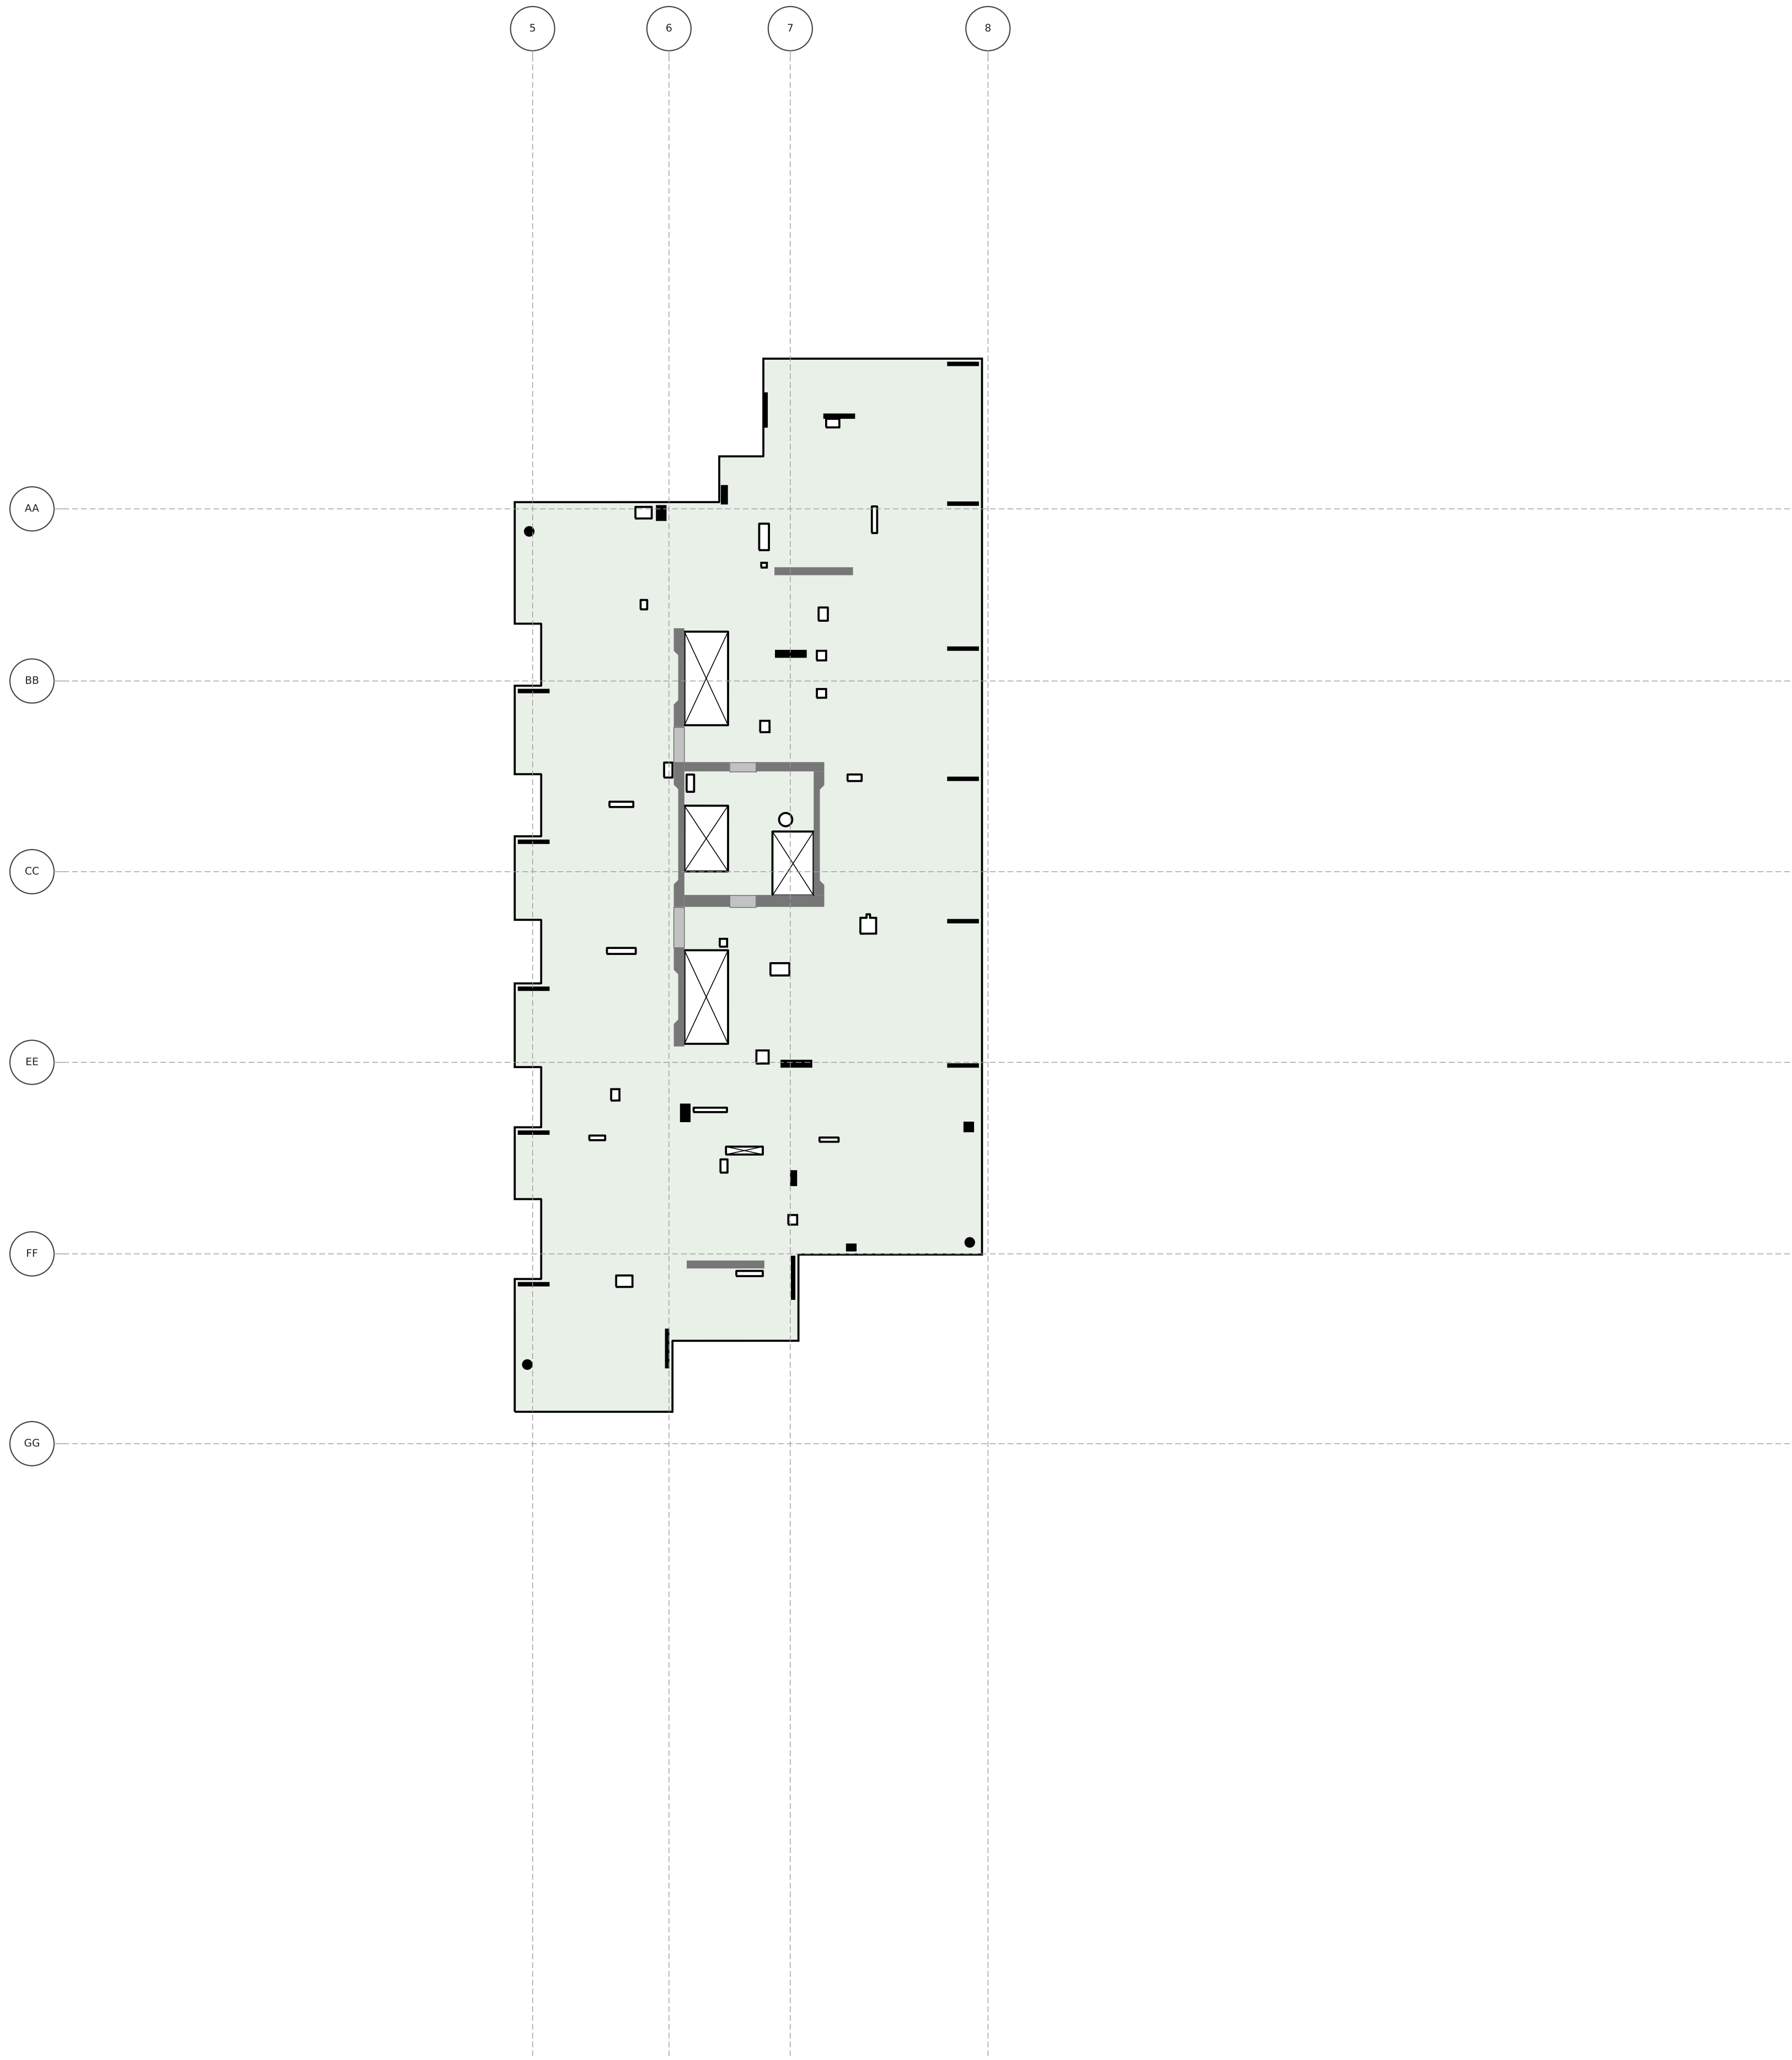


1268 KALAE

LEVEL 32 FLOOR PLAN

T.O.S. 411'-9" · typical slab 7.5" · scale 1" = 20'

Generated from 92743ac6-HI_KALAE_MCC_ST.ifc (Revit scope model) for the McClone Reshore Calculator — geometry only; loading marks are drawn in the calculator.

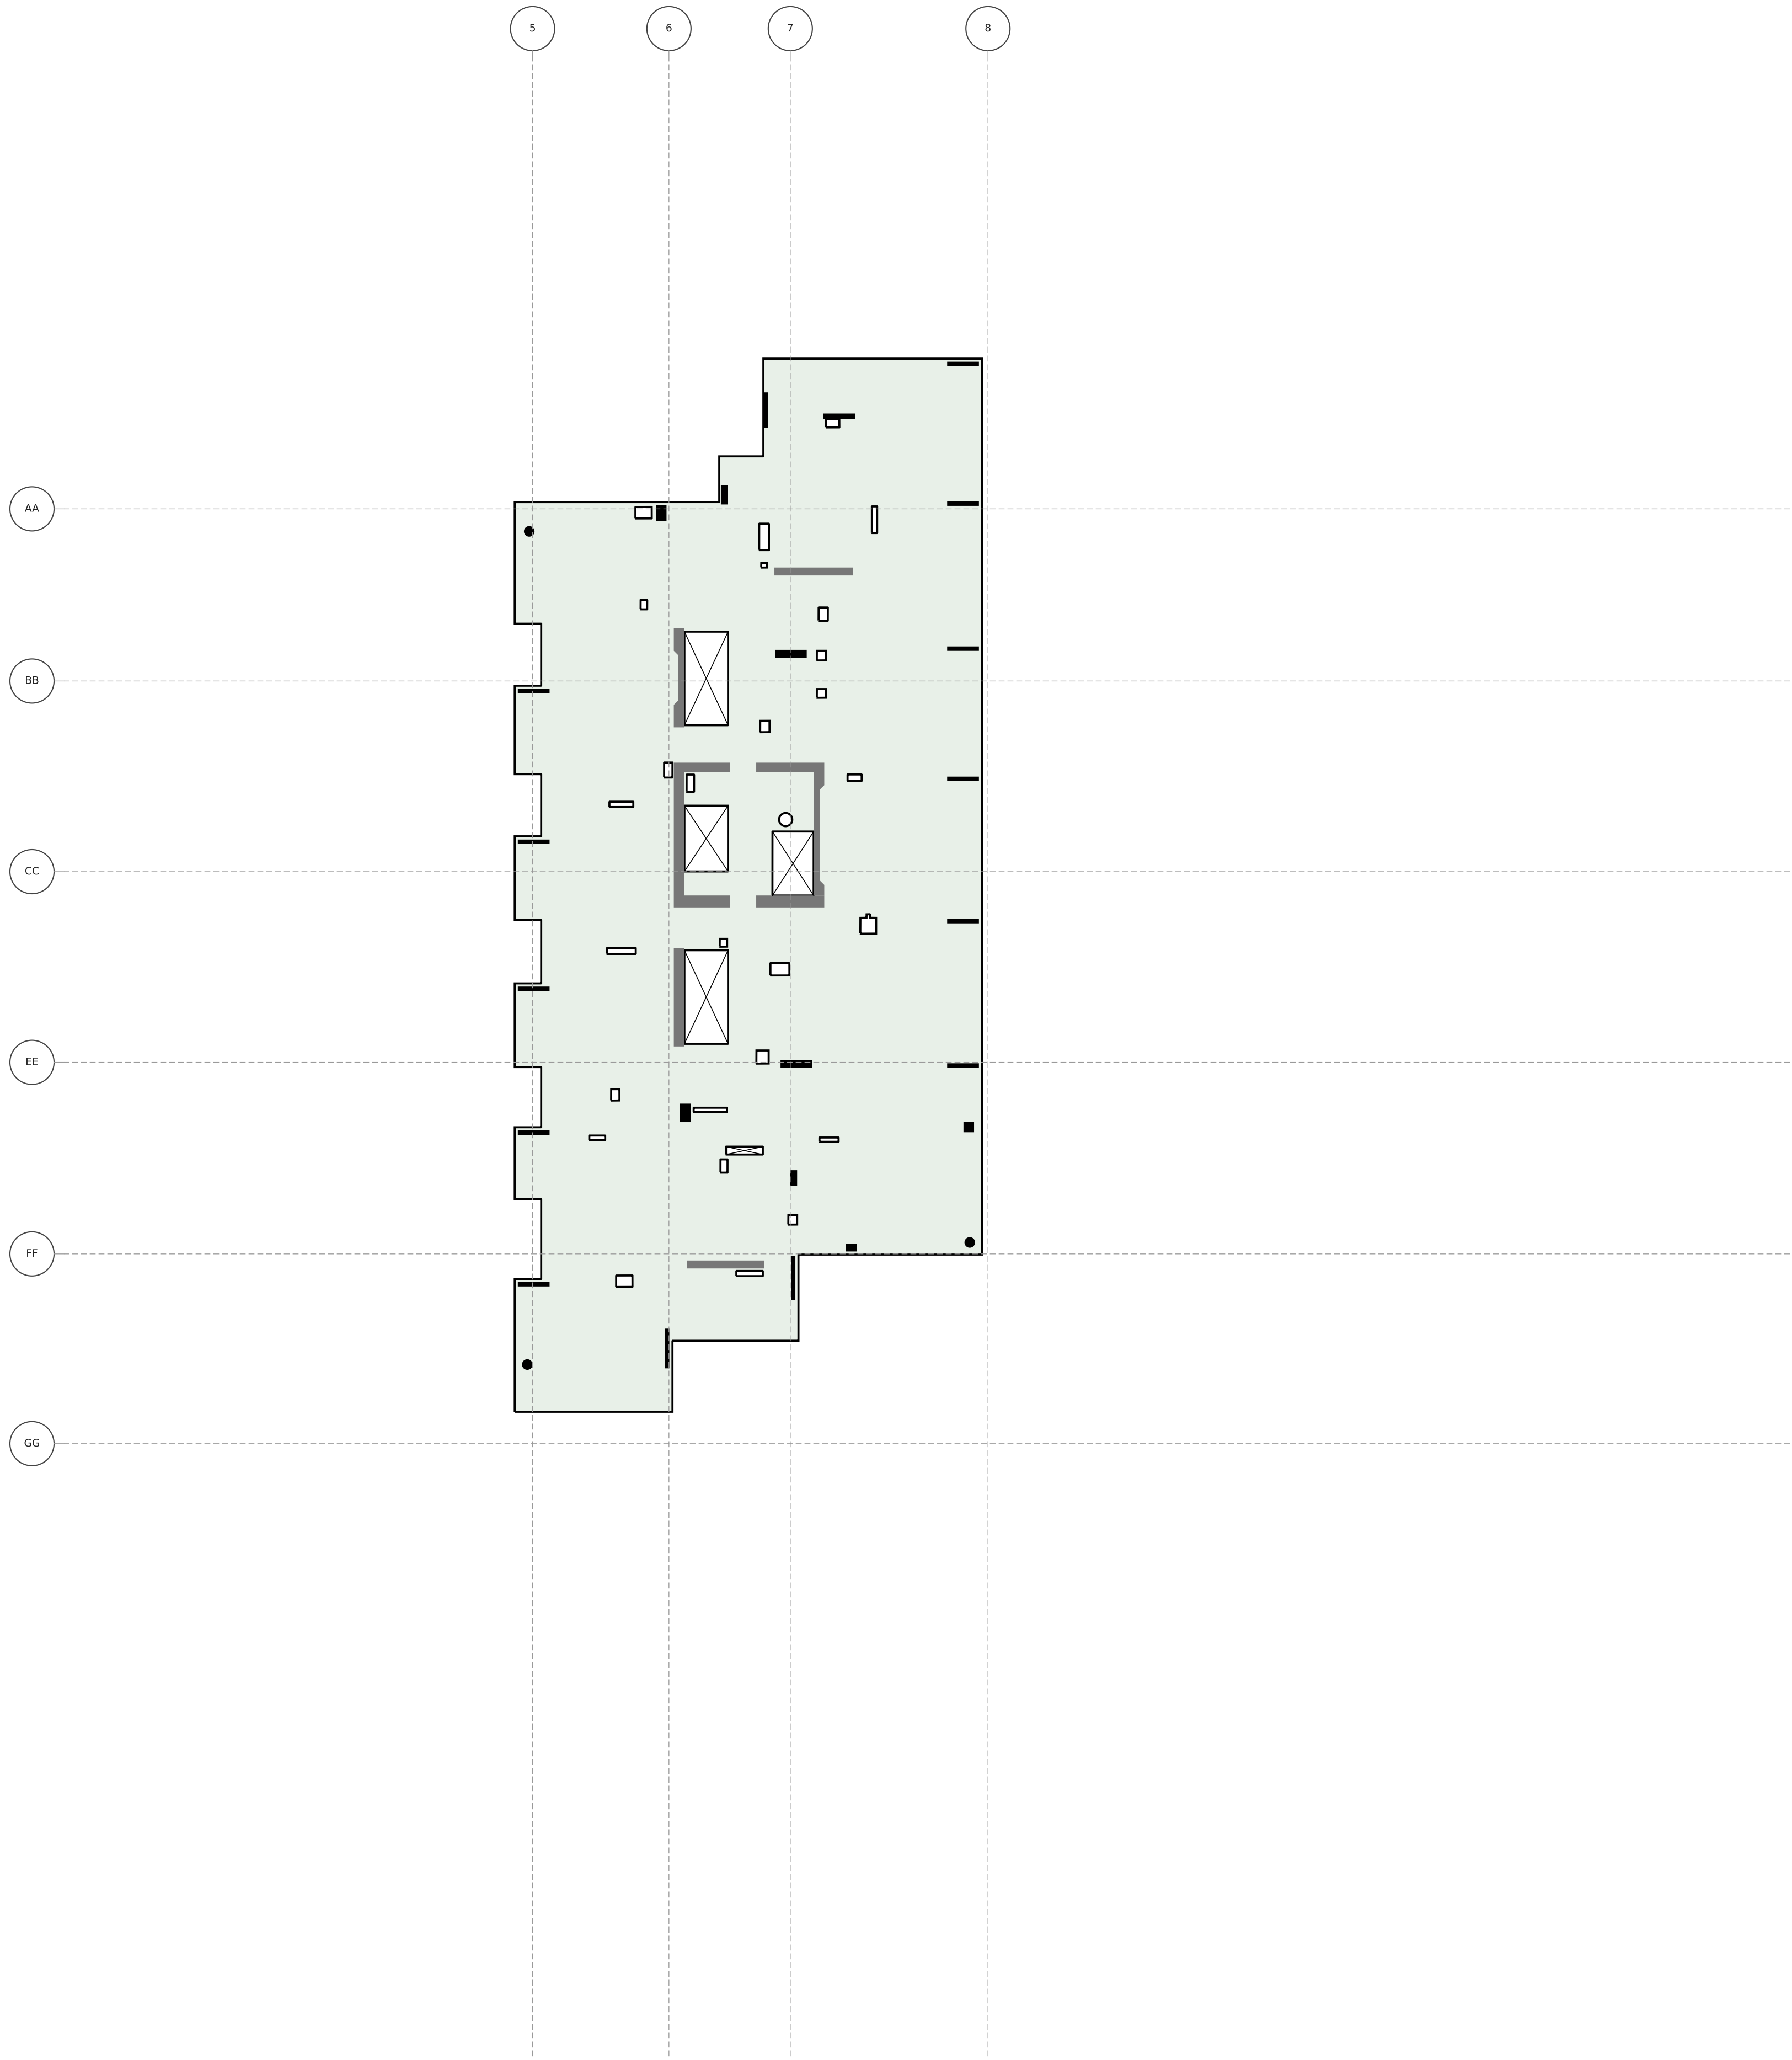


1268 KALAE

LEVEL 33 FLOOR PLAN

T.O.S. 421'-7.5" · typical slab 7.5" · scale 1" = 20'

Generated from 92743ac6-HI_KALAE_MCC_ST.ifc (Revit scope model) for the McClone Reshore Calculator — geometry only; loading marks are drawn in the calculator.

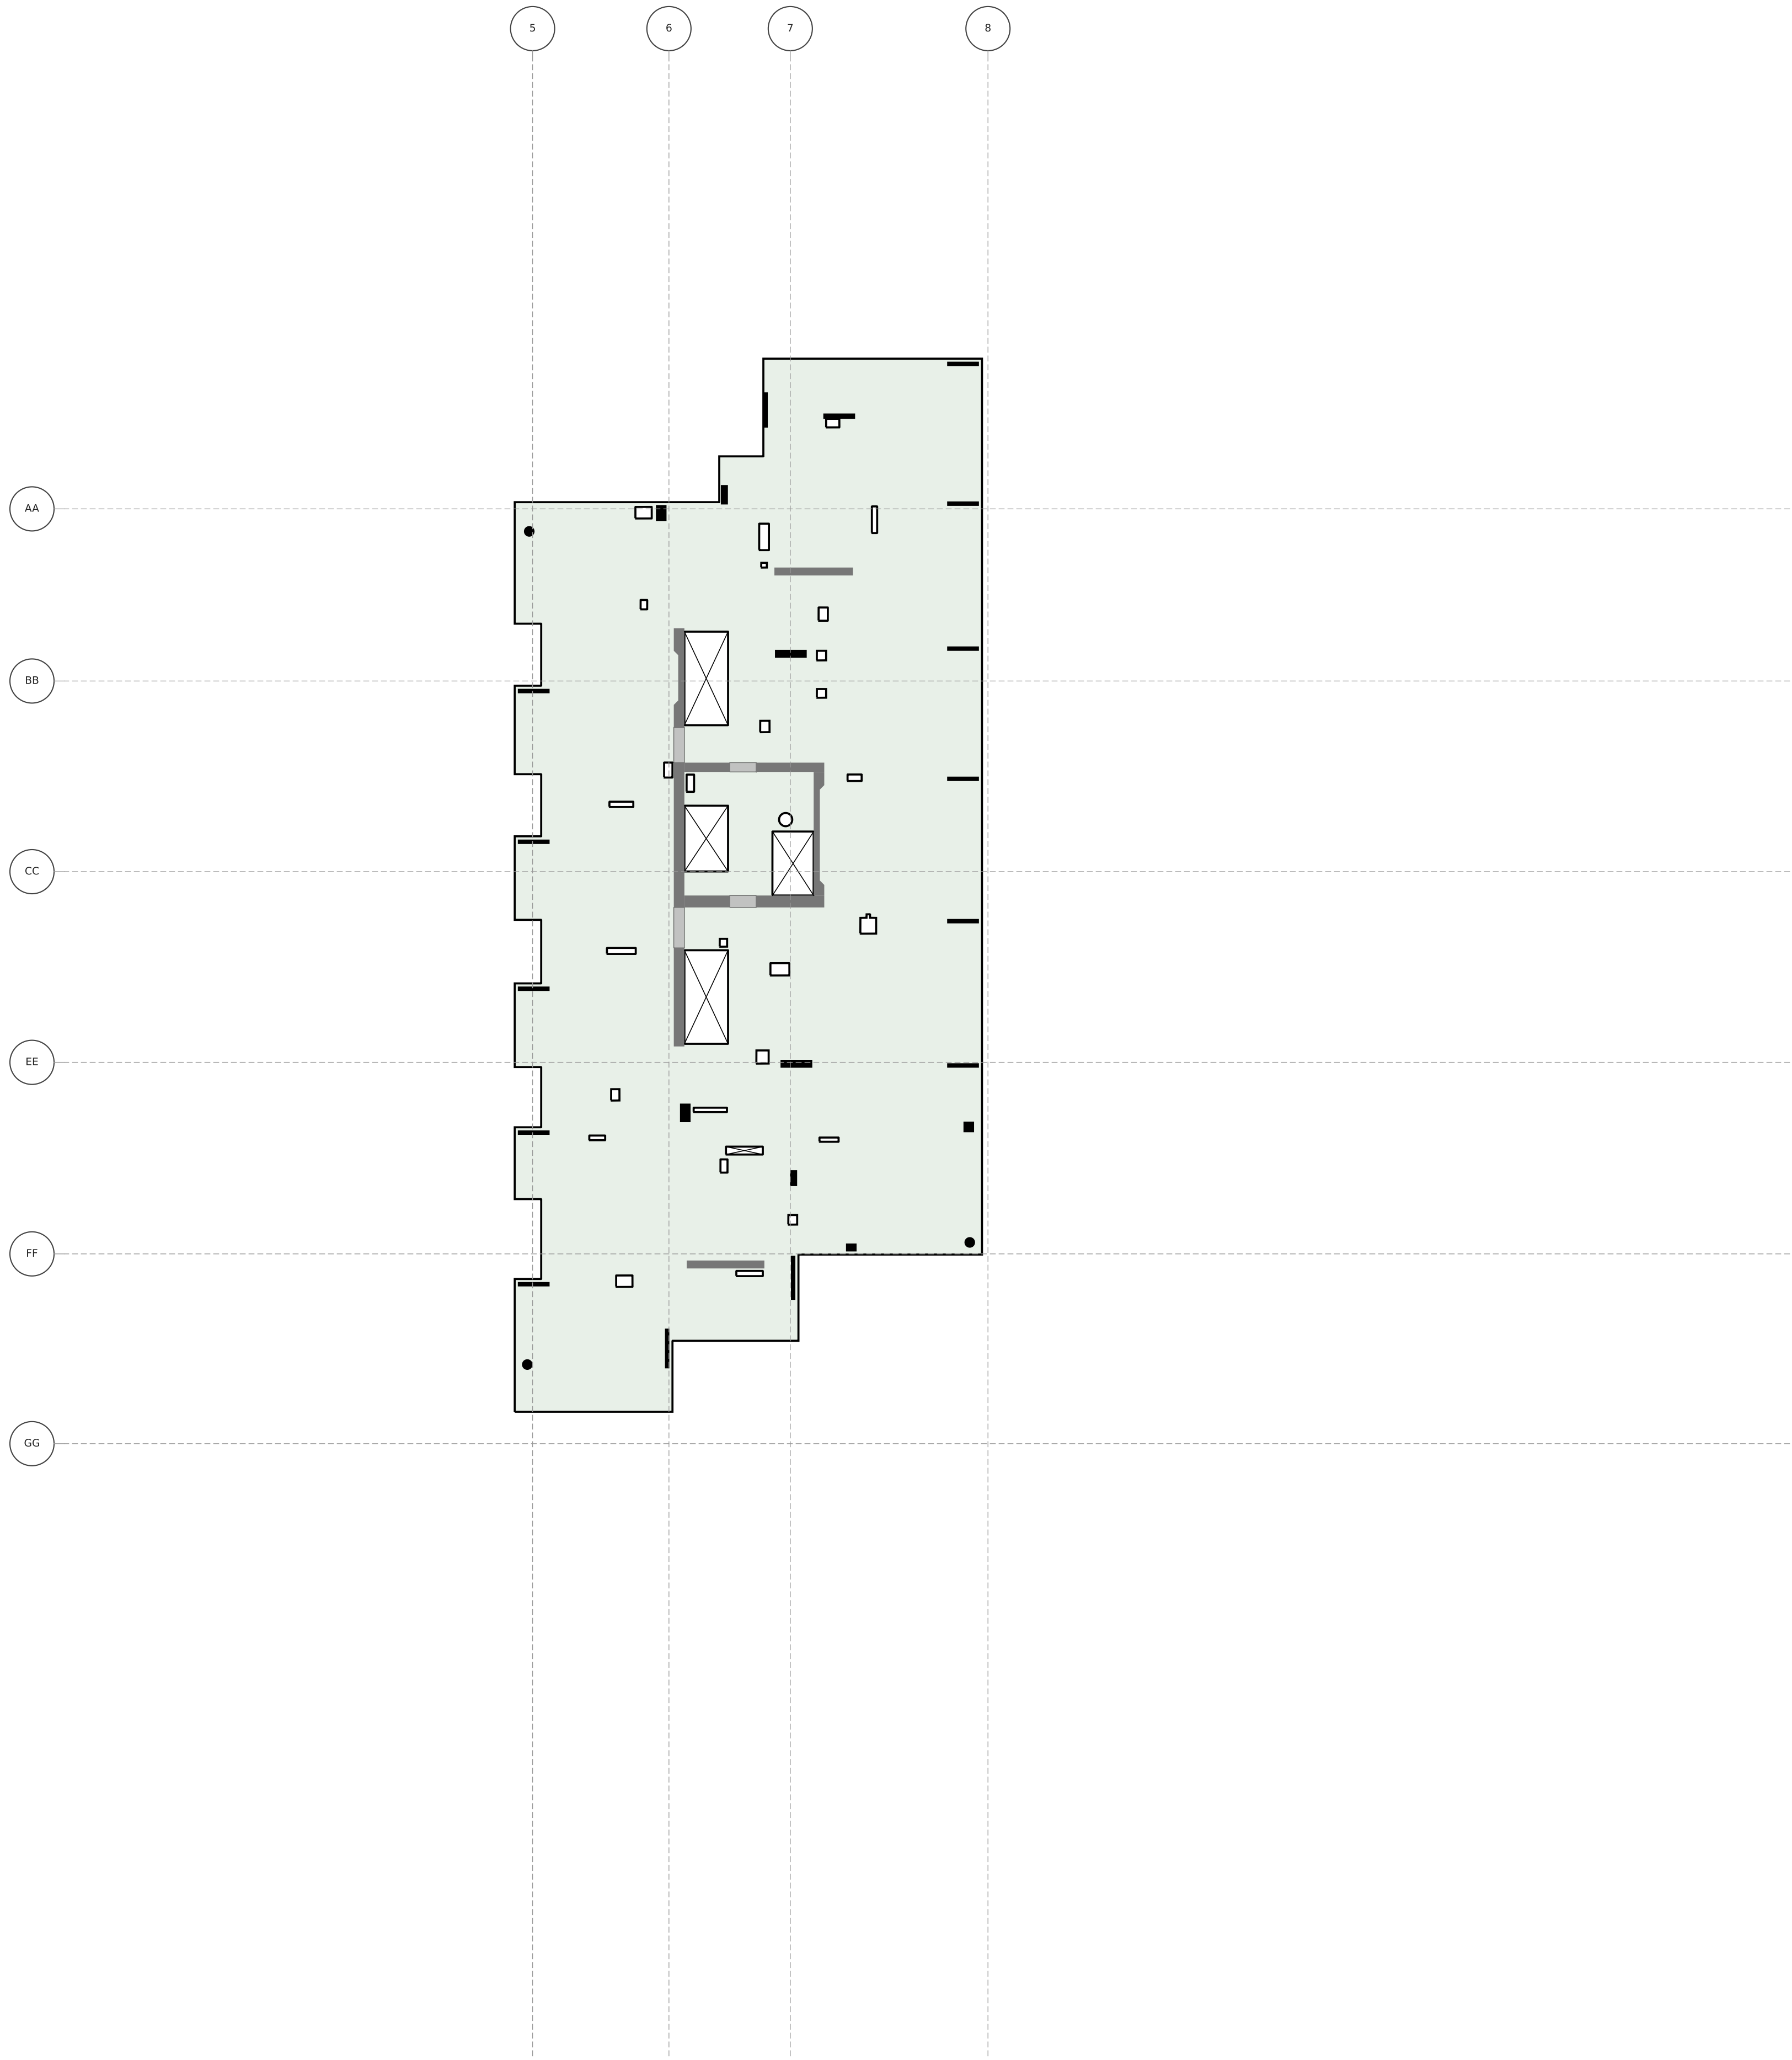


1268 KALAE

LEVEL 34 FLOOR PLAN

T.O.S. 431'-4" · typical slab 7.5" · scale 1" = 20'

Generated from 92743ac6-HI_KALAE_MCC_ST.ifc (Revit scope model) for the McClone Reshore Calculator — geometry only; loading marks are drawn in the calculator.

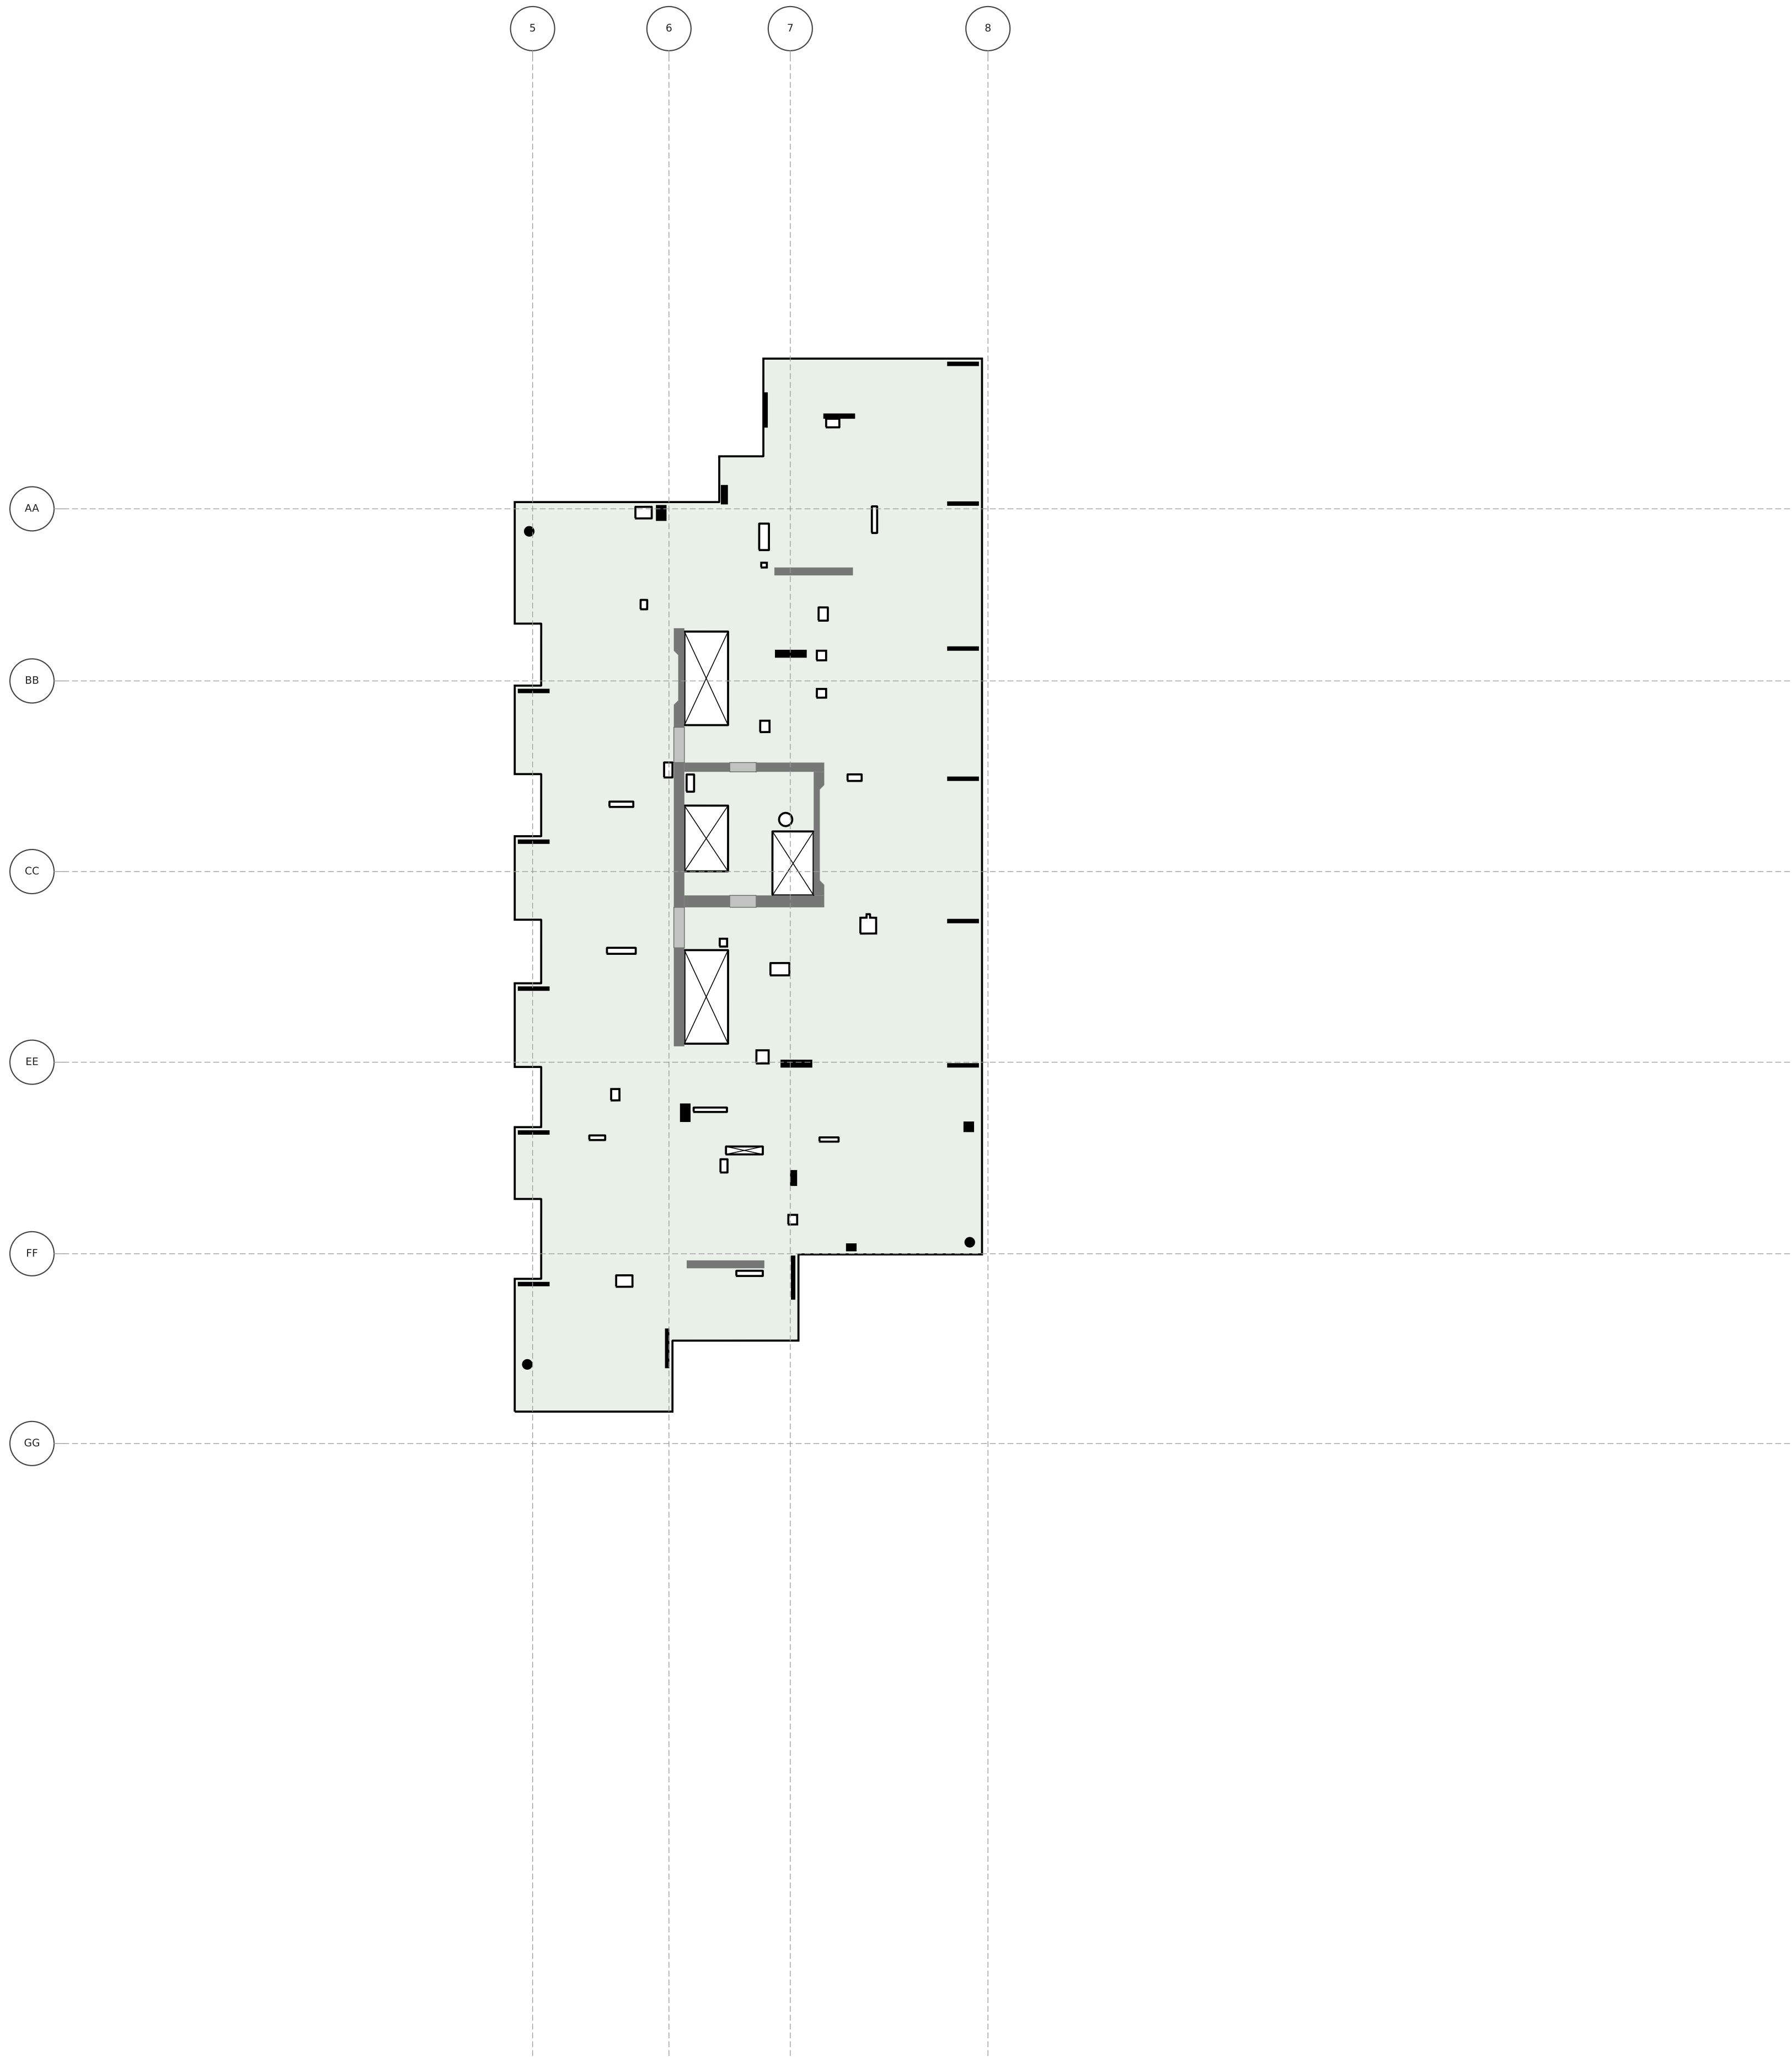


1268 KALAE

LEVEL 35 FLOOR PLAN

T.O.S. 441'-0.5" · typical slab 7.5" · scale 1" = 20'

Generated from 92743ac6-HI_KALAE_MCC_ST.ifc (Revit scope model) for the McClone Reshore Calculator — geometry only; loading marks are drawn in the calculator.

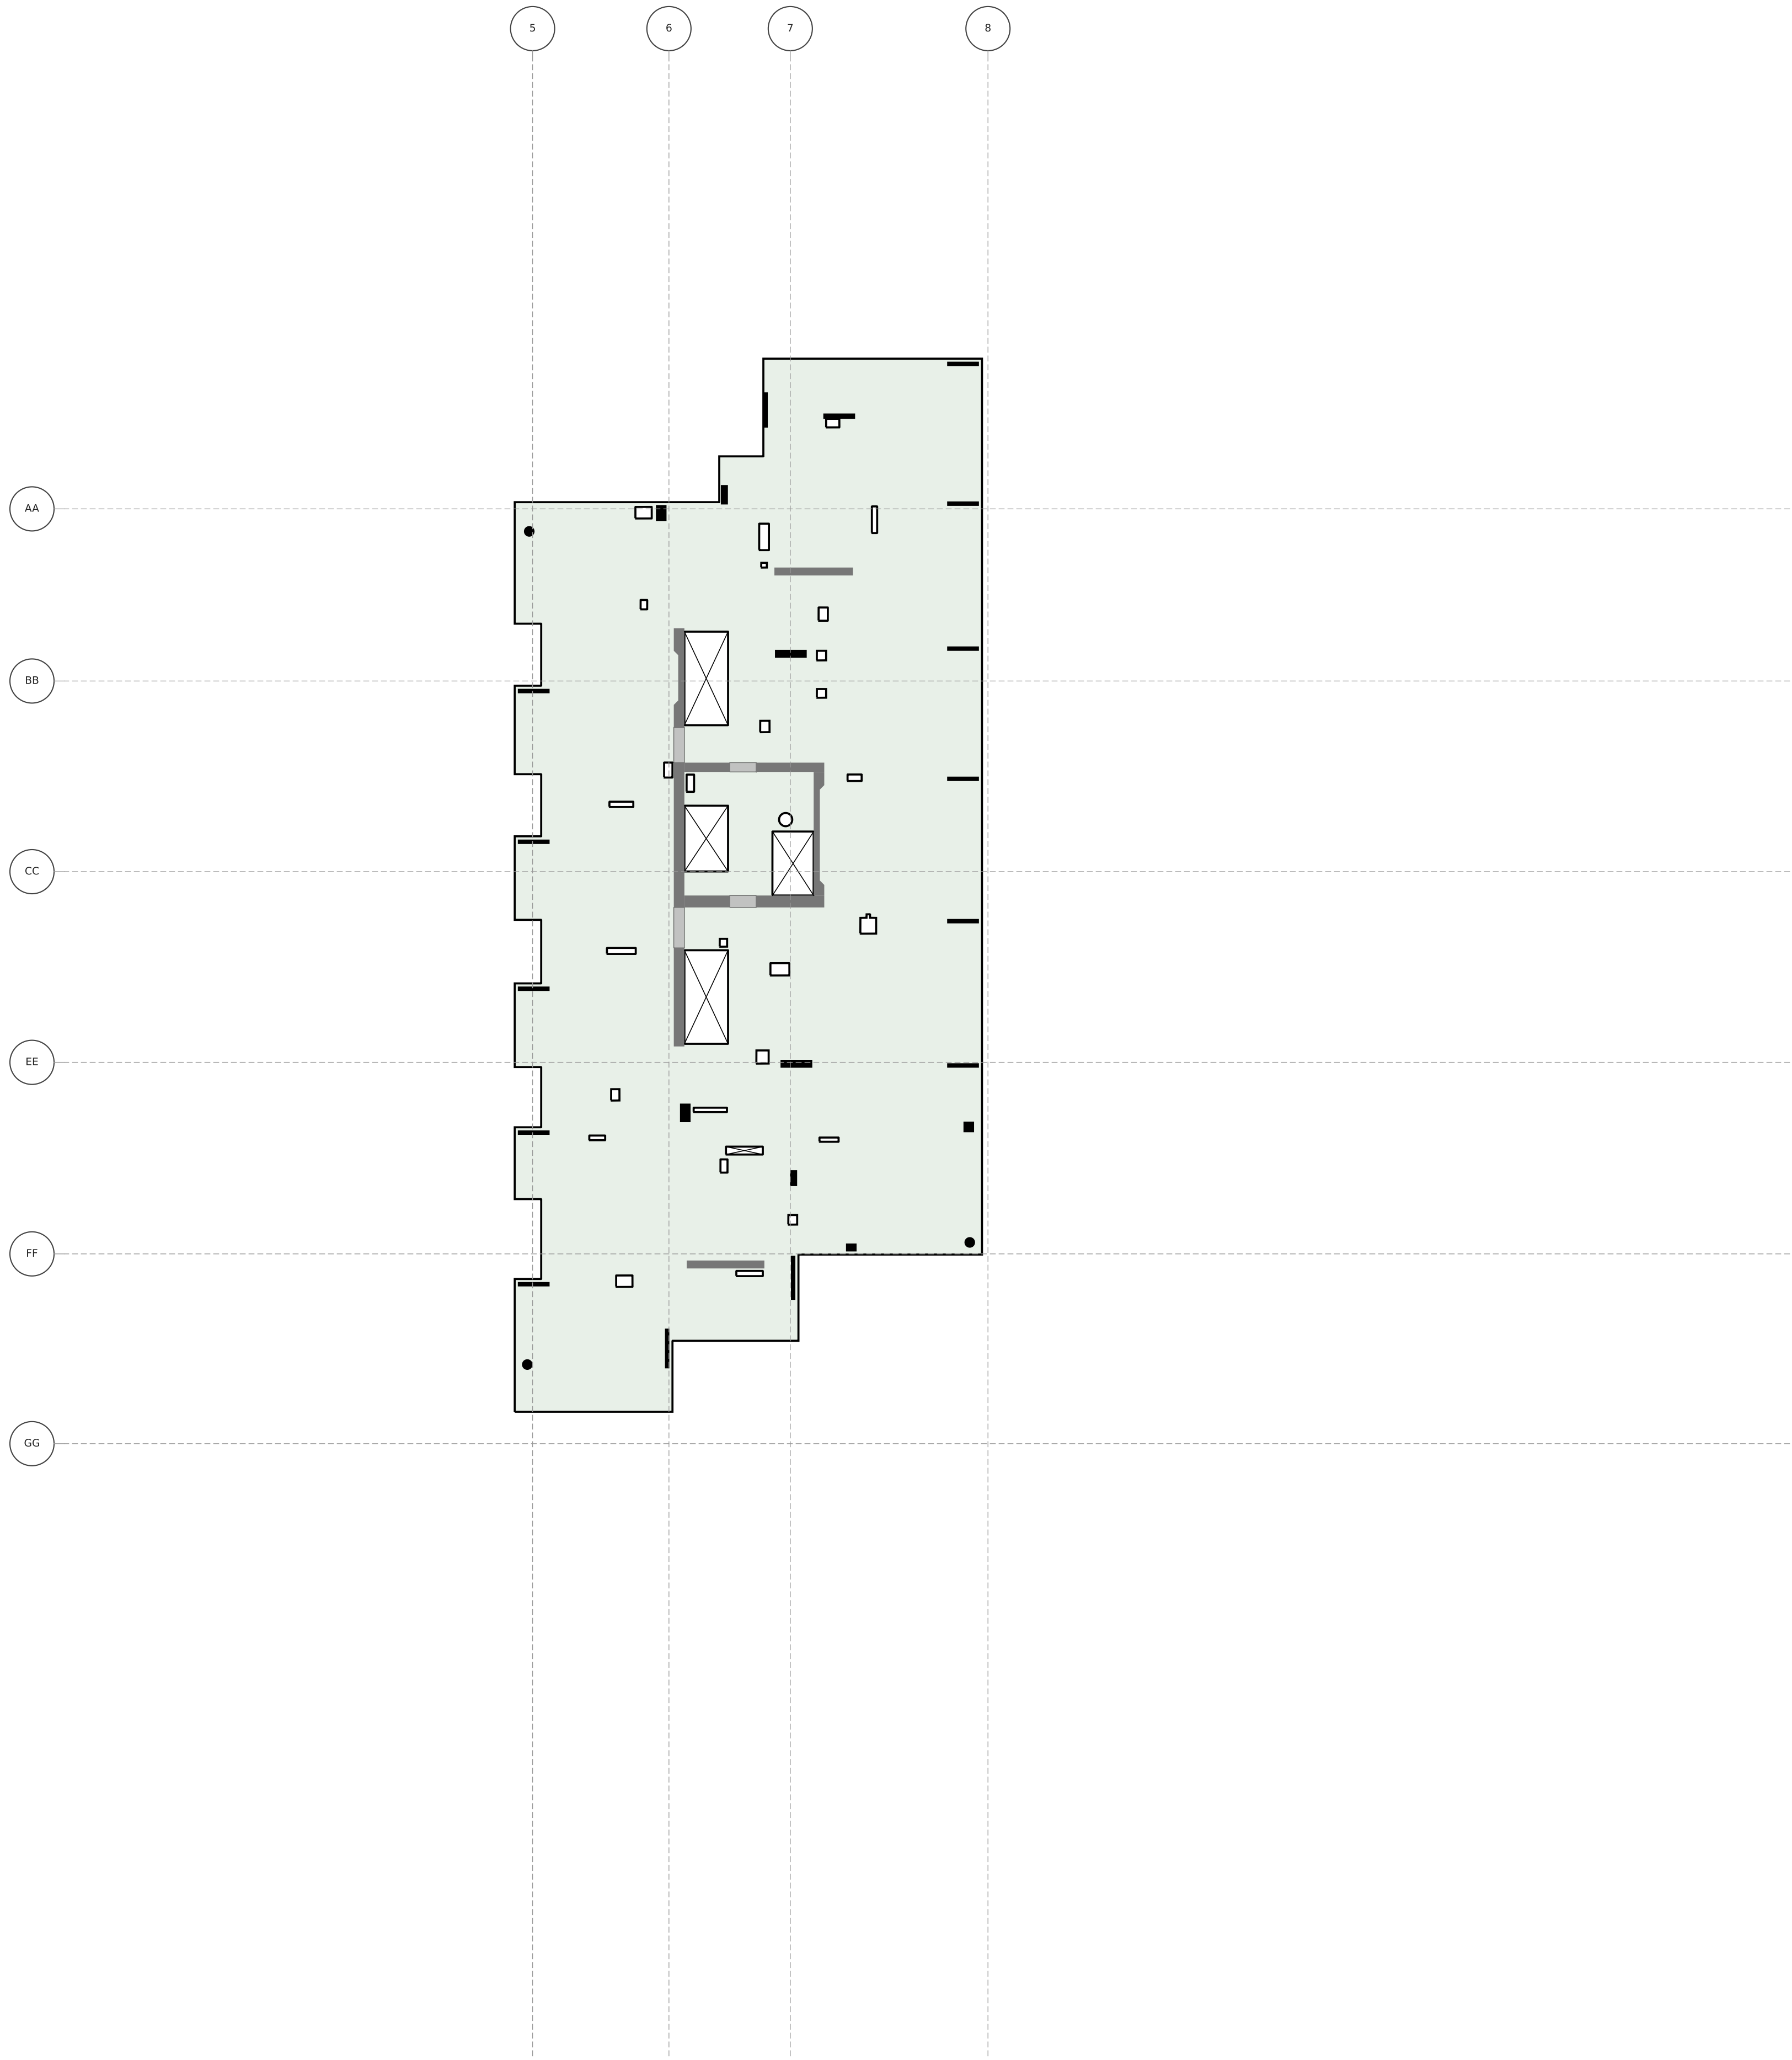


1268 KALAE

LEVEL 36 FLOOR PLAN

T.O.S. 450'-9" · typical slab 7.5" · scale 1" = 20'

Generated from 92743ac6-HI_KALAE_MCC_ST.ifc (Revit scope model) for the McClone Reshore Calculator — geometry only; loading marks are drawn in the calculator.

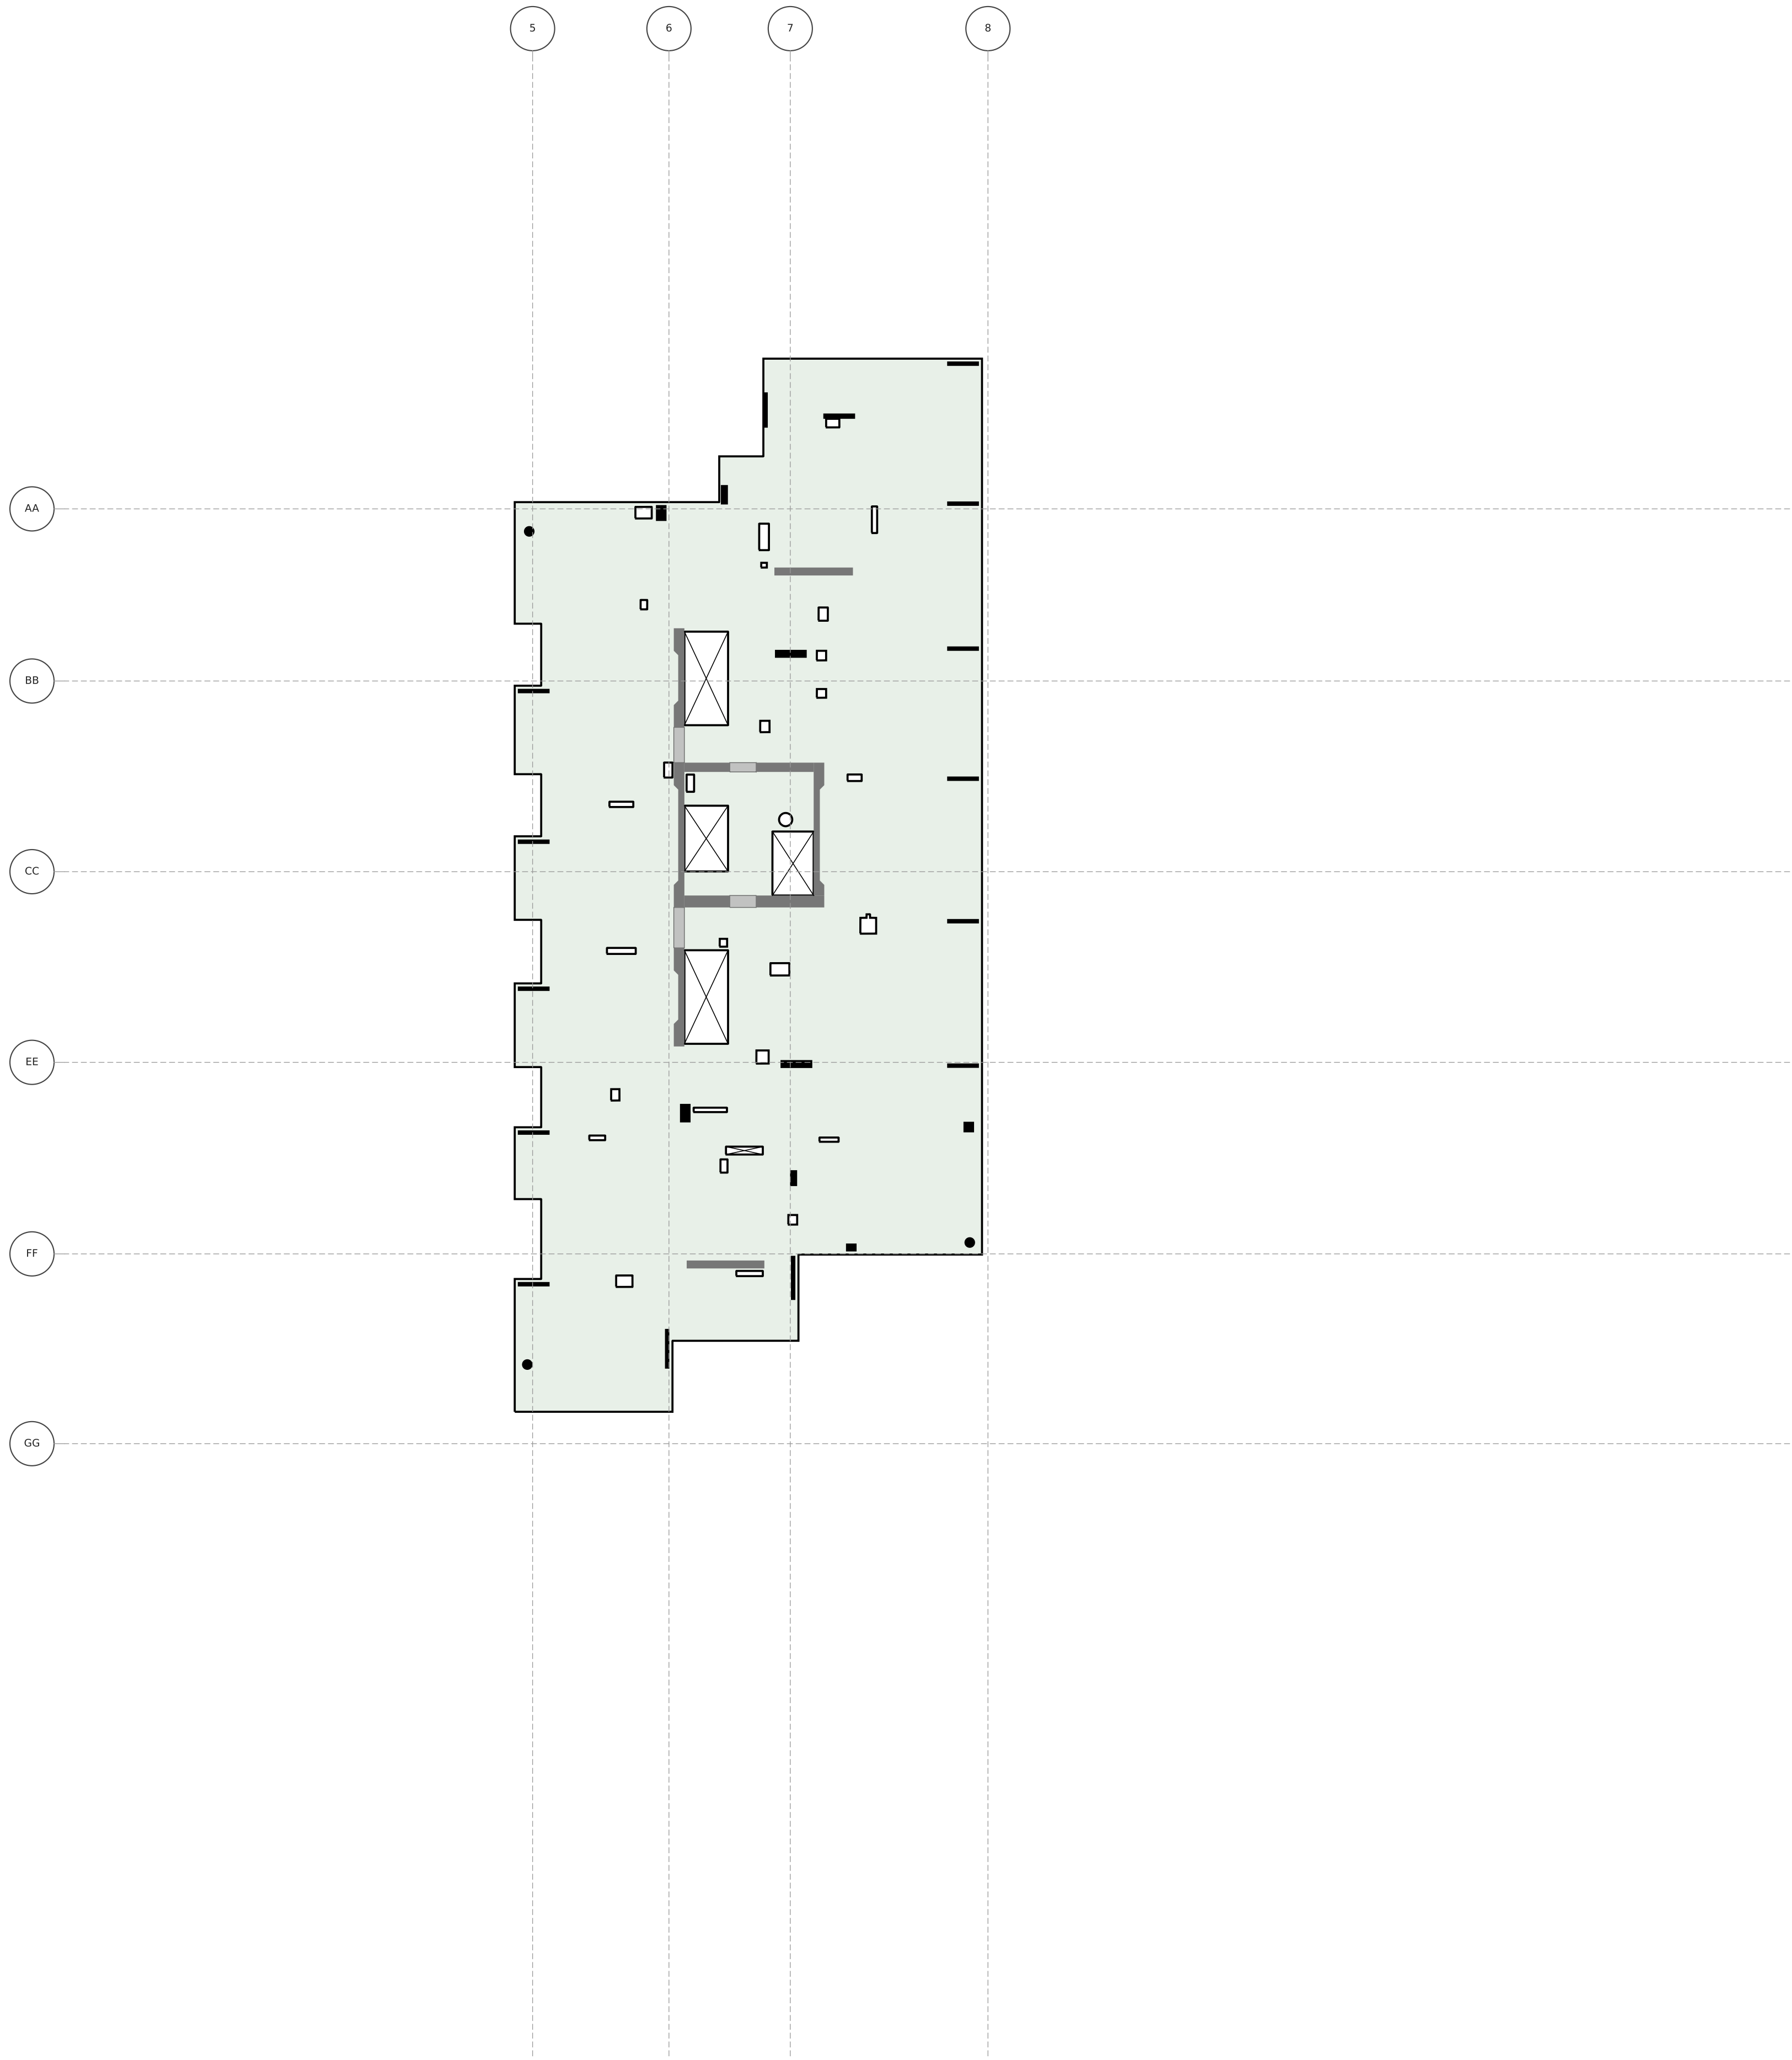


1268 KALAE

LEVEL 37 FLOOR PLAN

T.O.S. 460'-5.5" · typical slab 7.5" · scale 1" = 20'

Generated from 92743ac6-HI_KALAE_MCC_ST.ifc (Revit scope model) for the McClone Reshore Calculator — geometry only; loading marks are drawn in the calculator.

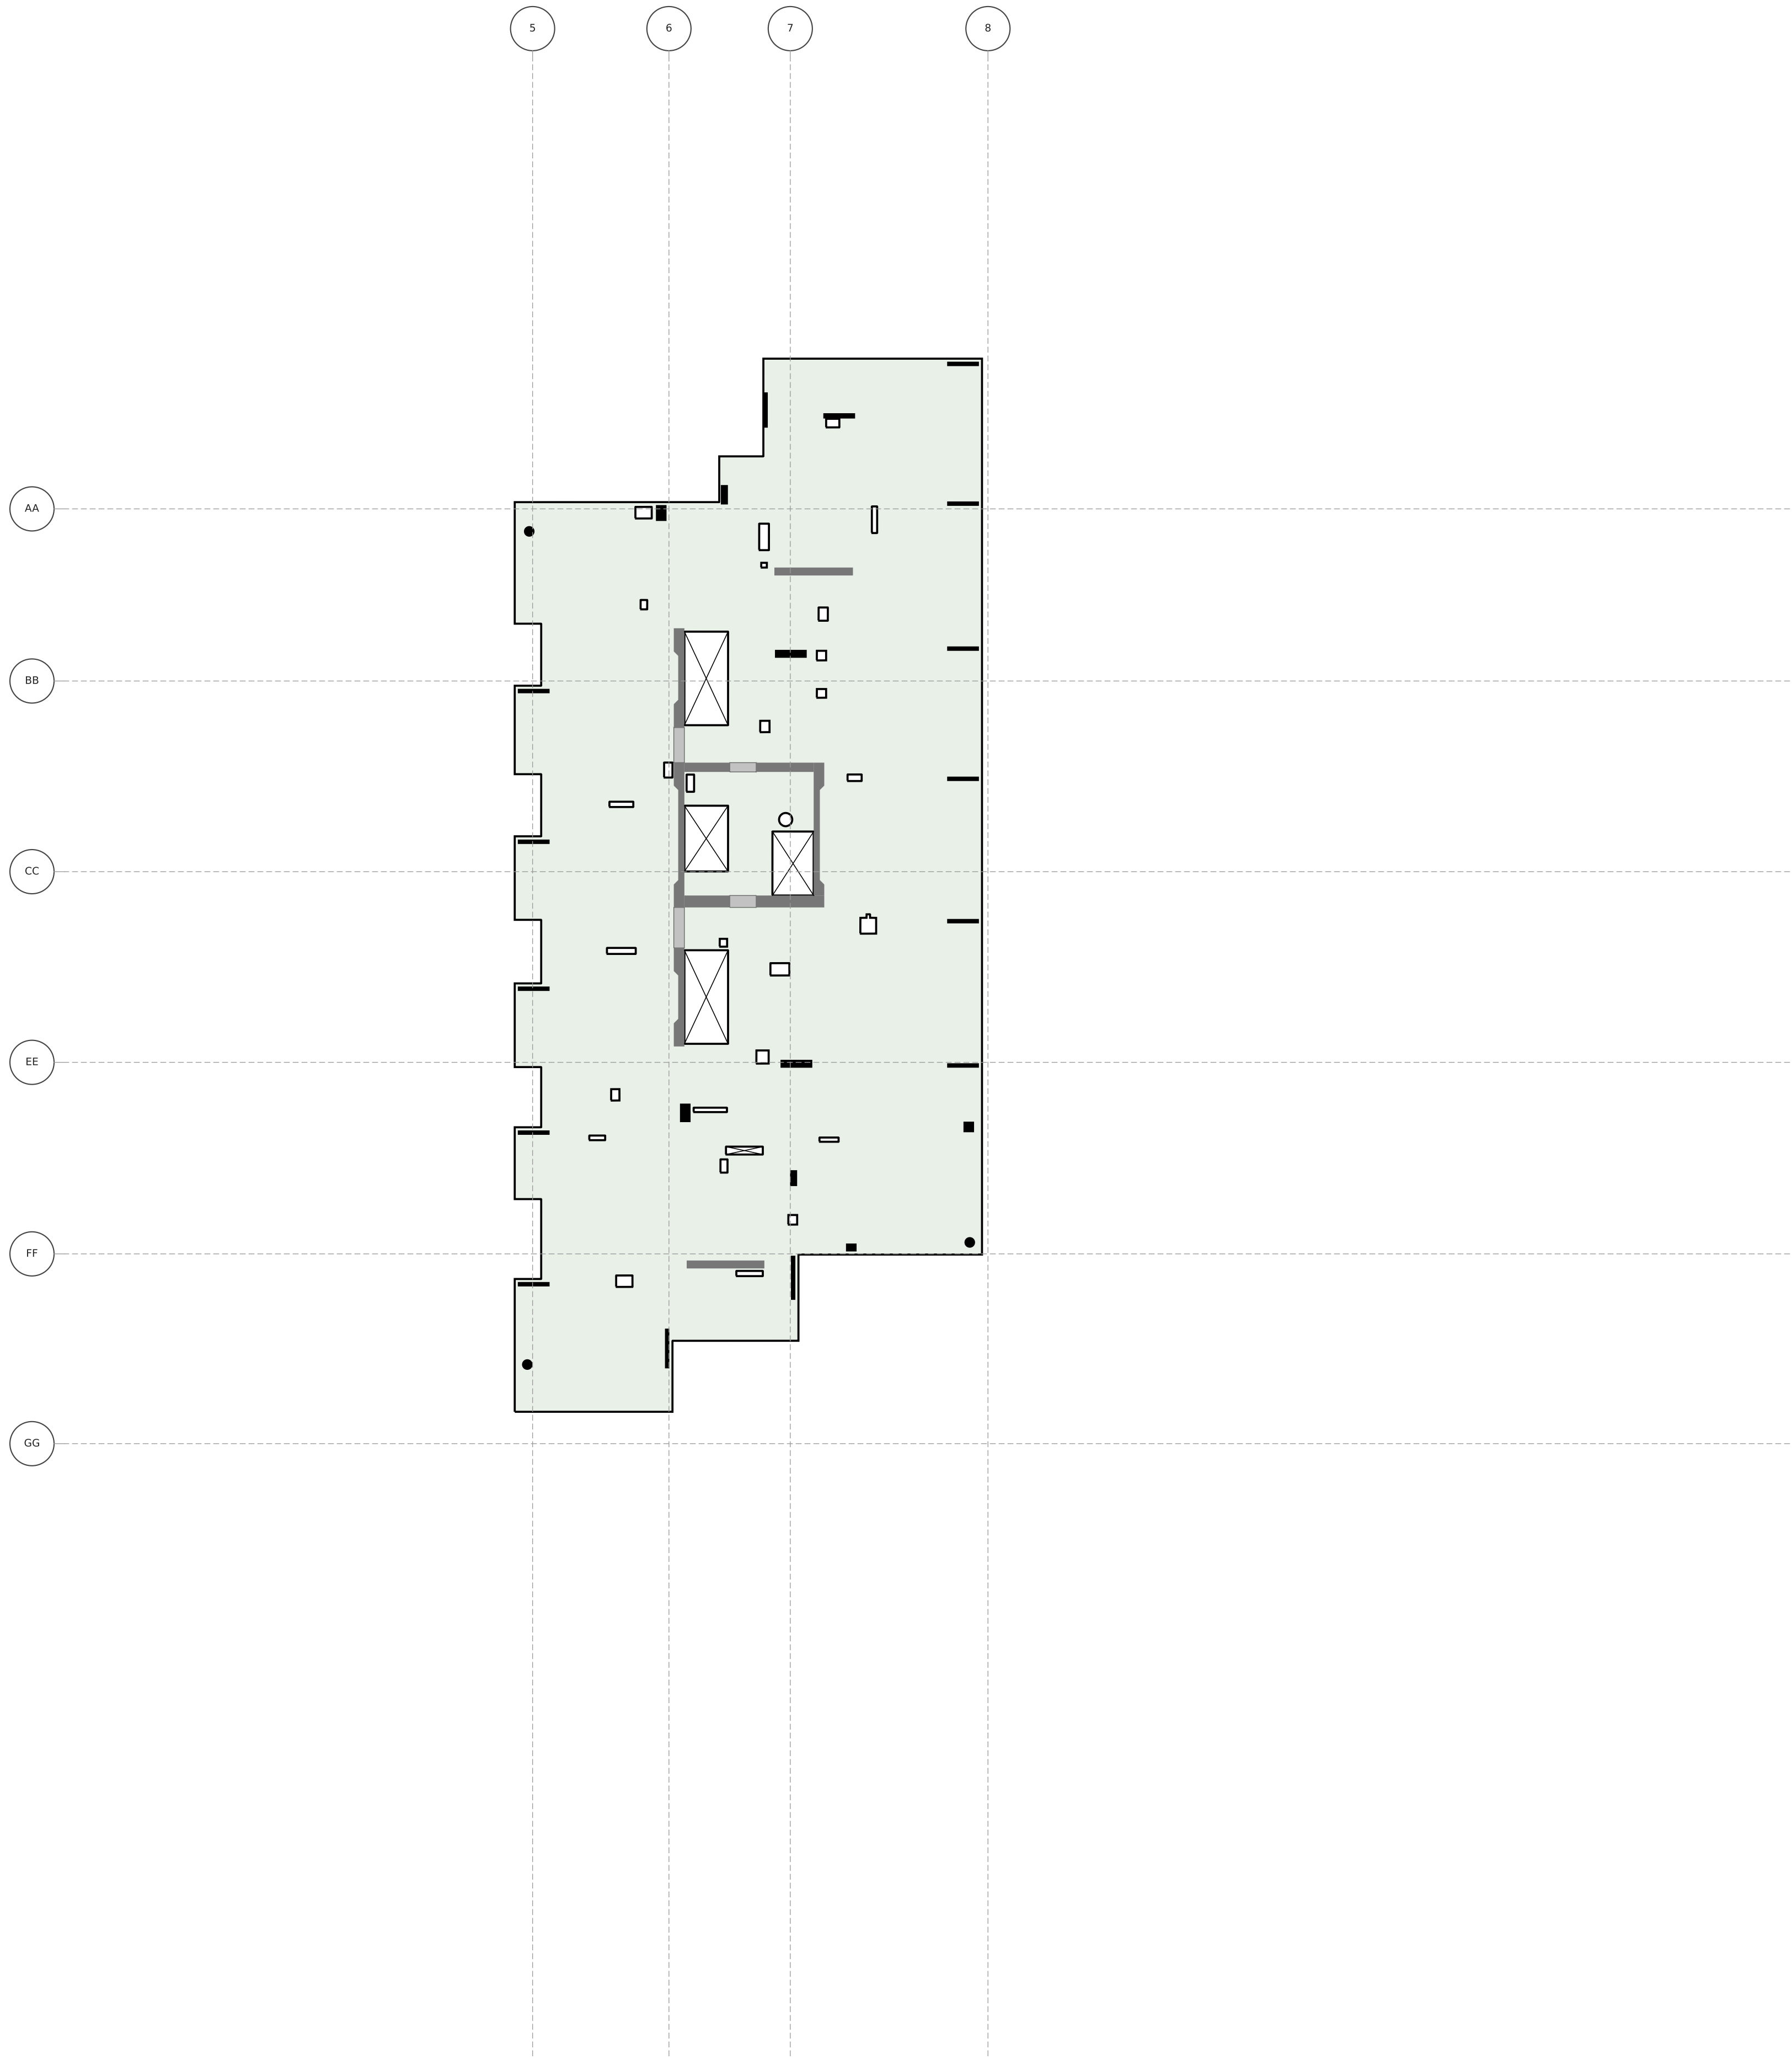


1268 KALAE

LEVEL 38 FLOOR PLAN

T.O.S. 471'-2" · typical slab 7.5" · scale 1" = 20'

Generated from 92743ac6-HI_KALAE_MCC_ST.ifc (Revit scope model) for the McClone Reshore Calculator — geometry only; loading marks are drawn in the calculator.

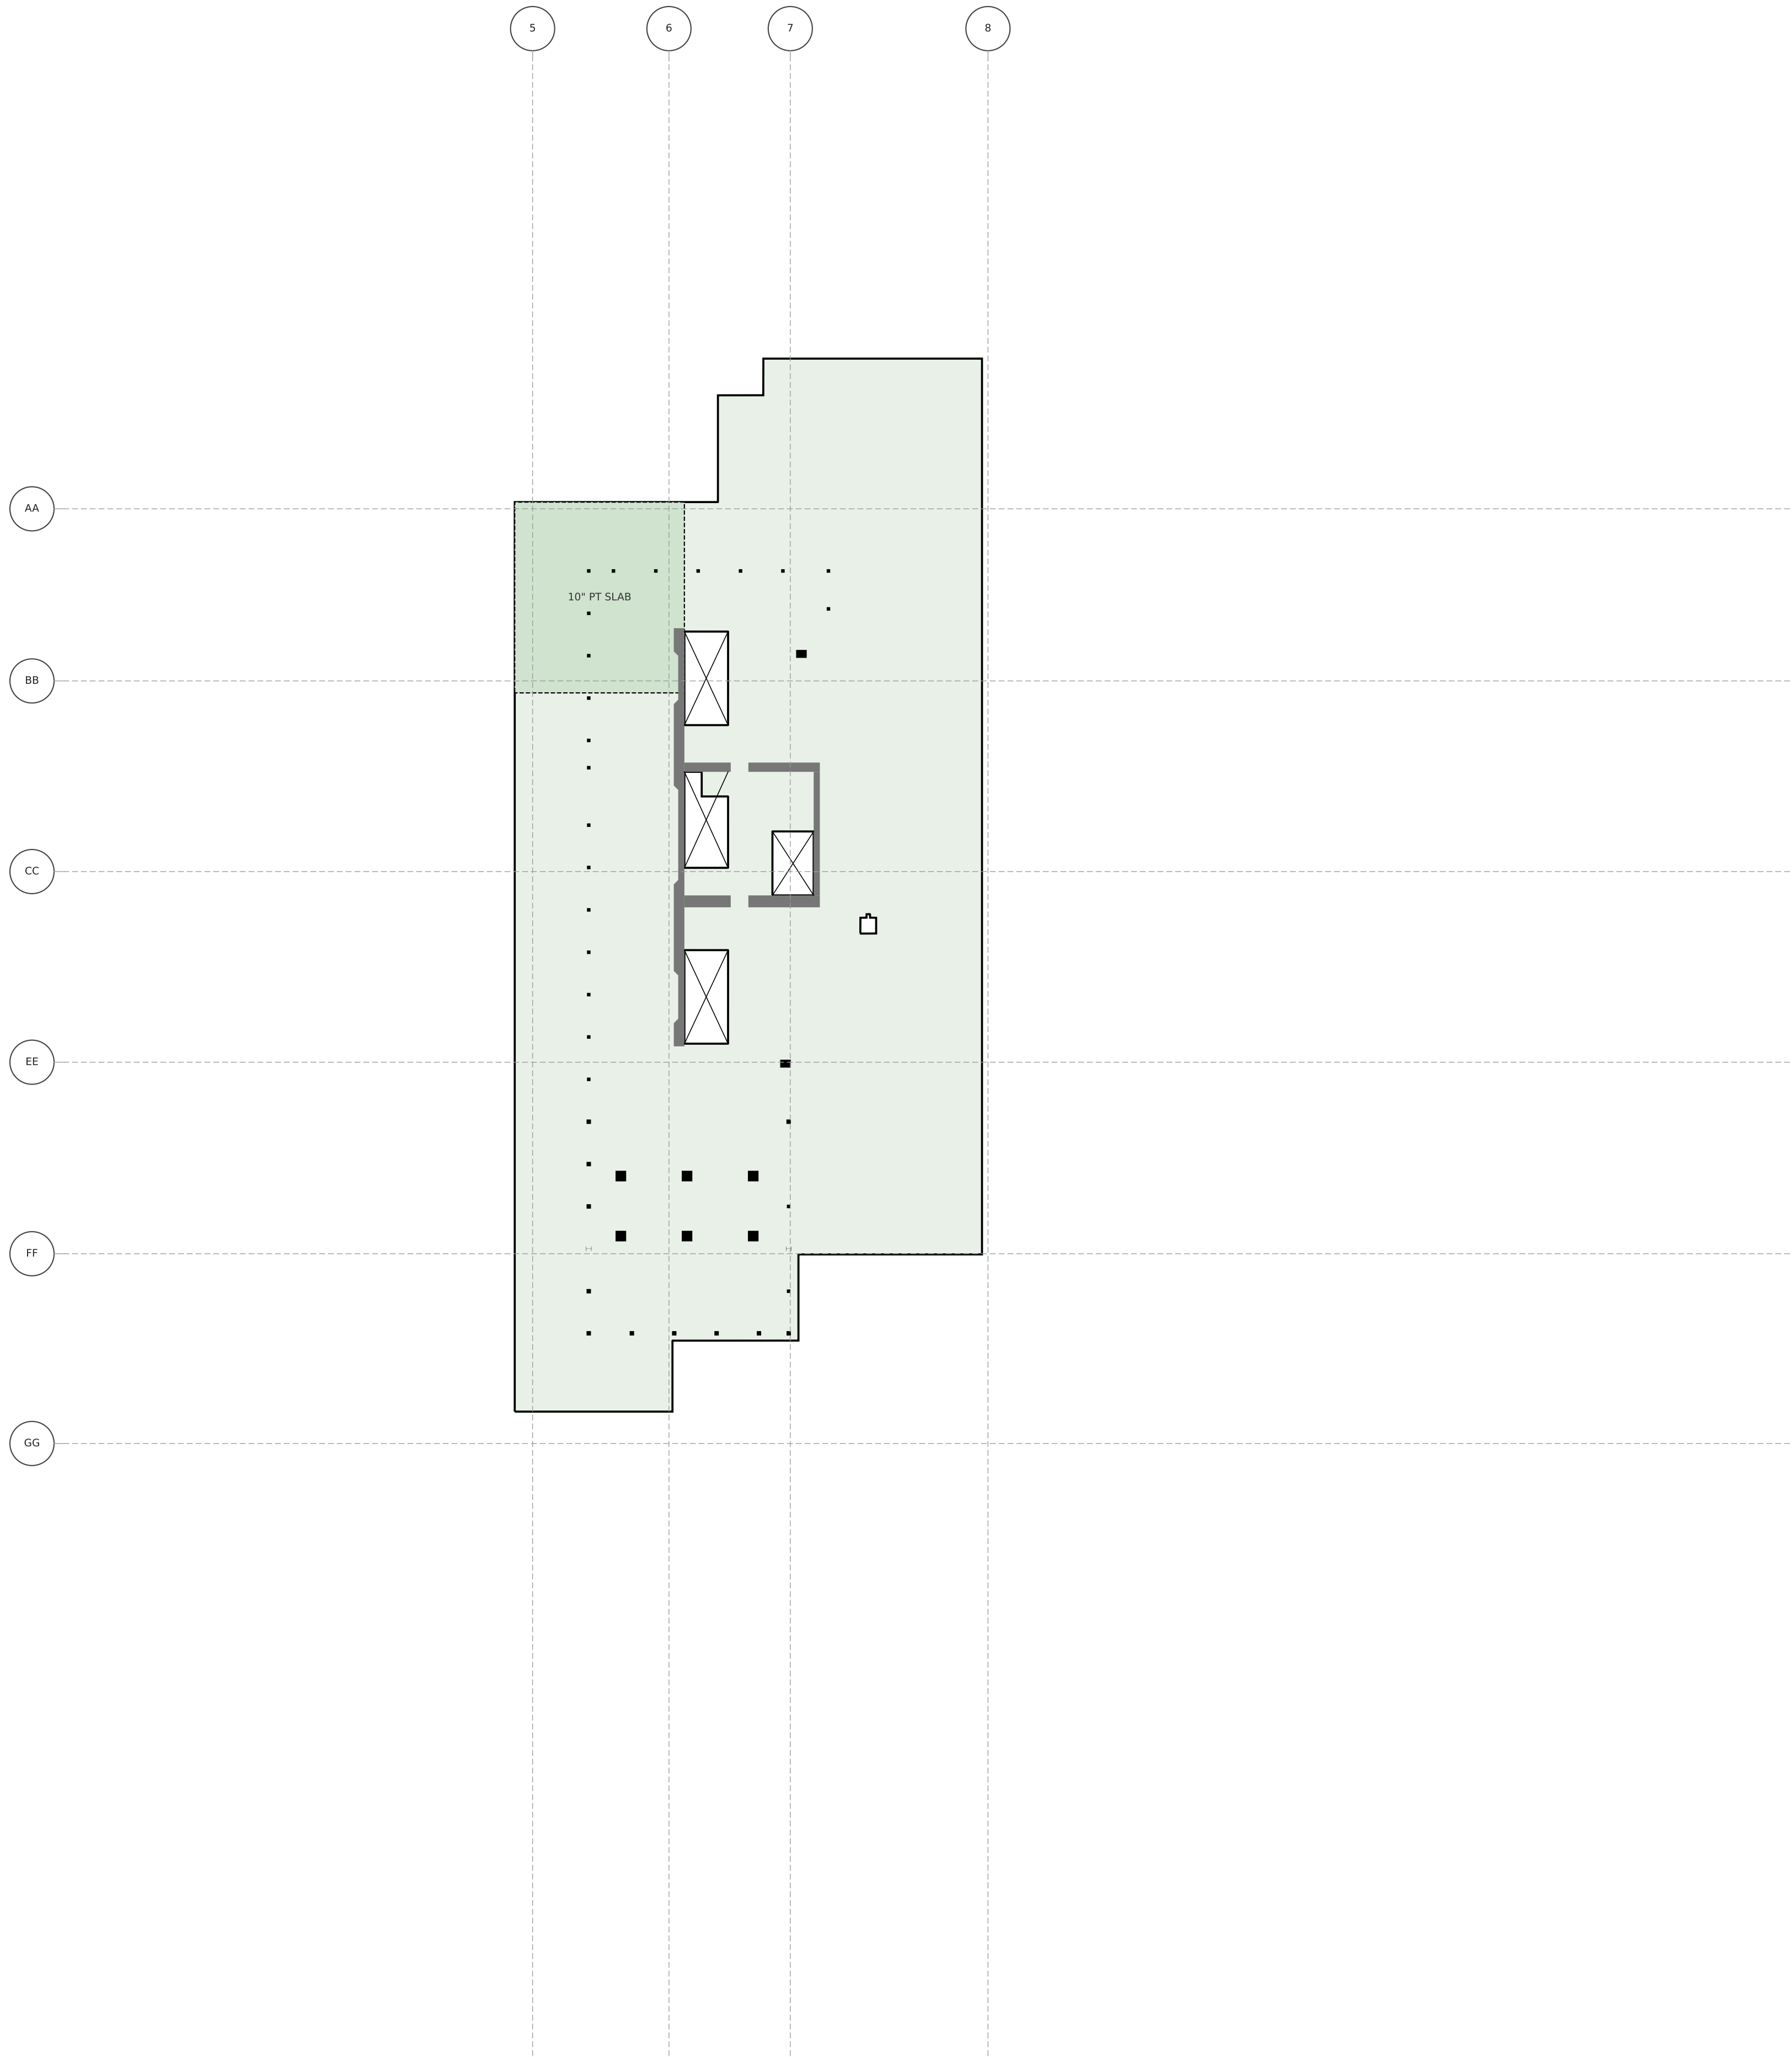


1268 KALAE

LEVEL ROOF FLOOR PLAN

T.O.S. 483'-8" · typical slab 7.5" · scale 1" = 20'

Generated from 92743ac6-HI_KALAE_MCC_ST.ifc (Revit scope model) for the McClone Reshore Calculator — geometry only; loading marks are drawn in the calculator.

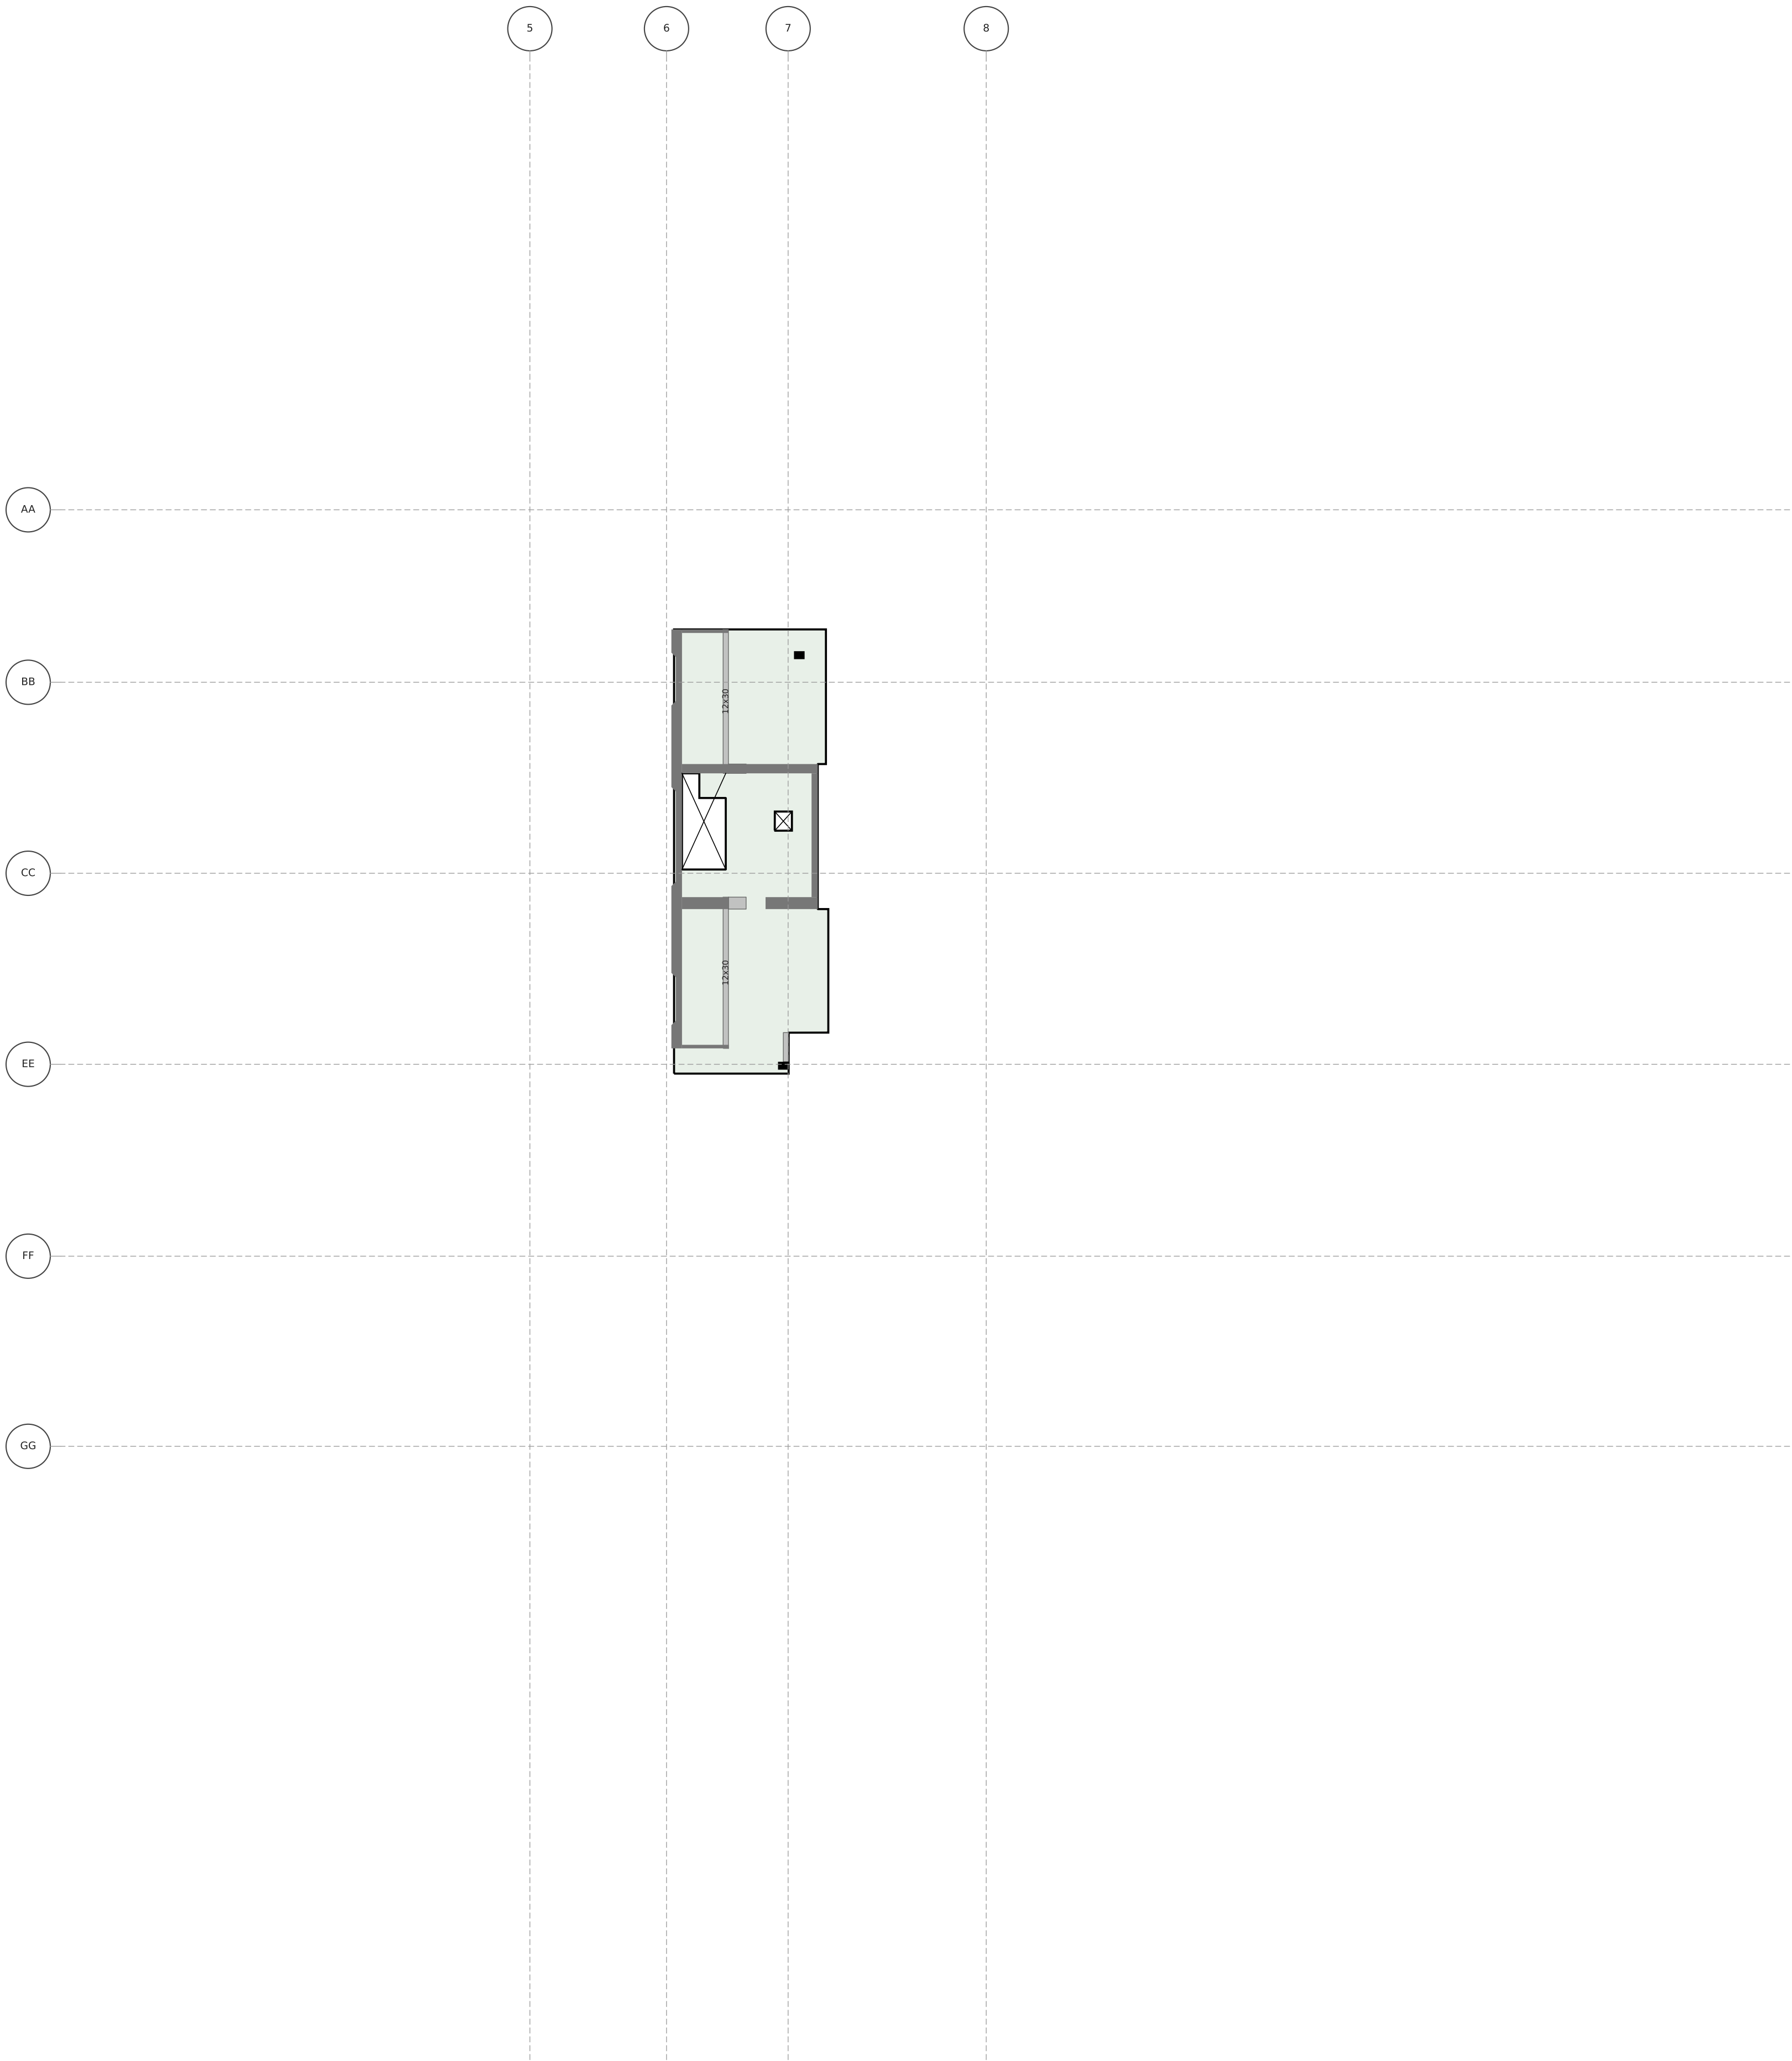


1268 KALAE

LEVEL ELEV MECH RM FLOOR PLAN

T.O.S. 492'-4" · typical slab 10" · scale 1" = 20'

Generated from 92743ac6-HI_KALAE_MCC_ST.ifc (Revit scope model) for the McClone Reshore Calculator — geometry only; loading marks are drawn in the calculator.

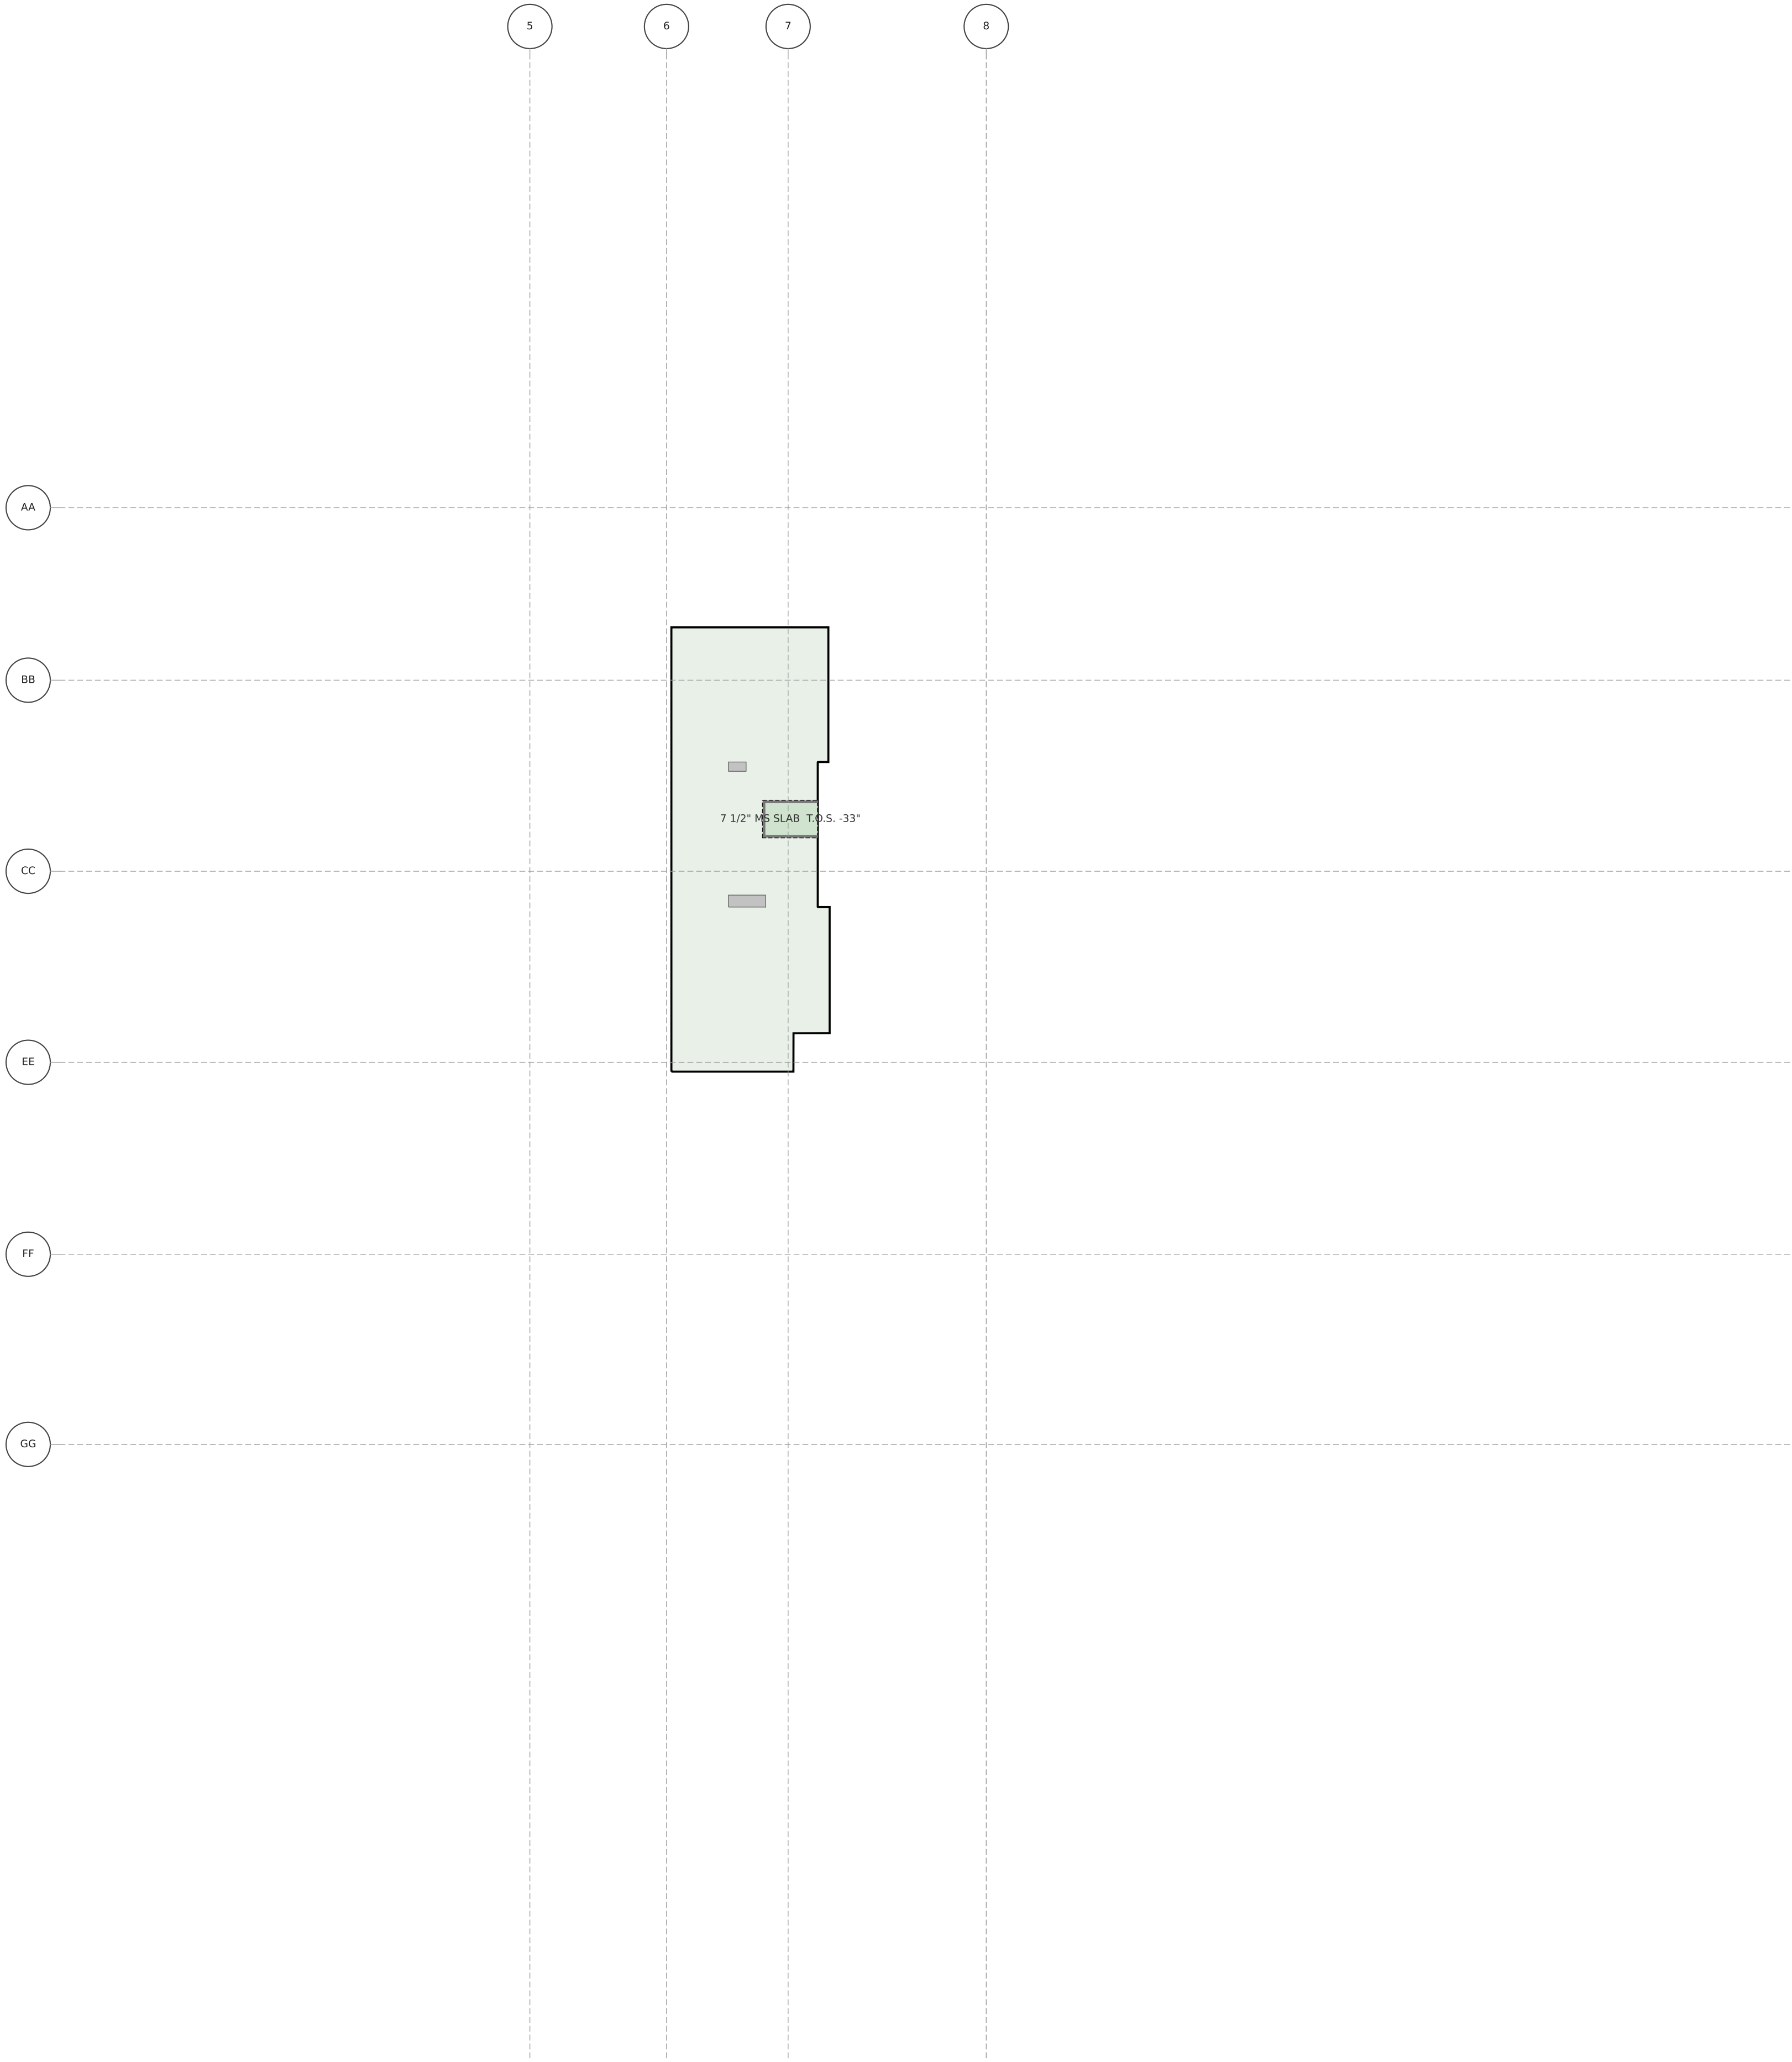

1268 KALAE

LEVEL MECH ROOF FLOOR PLAN

T.O.S. 501'-2" · typical slab 7.5" · scale 1" = 20'

Generated from 92743ac6-HI_KALAE_MCC_ST.ifc (Revit scope model) for the McClone Reshore Calculator — geometry only; loading marks are drawn in the calculator.