

PROJECT

BOTHELL STEM 4

LOCATION
18330 110TH AVE NE
BOTHELL, WA 98011

PREPARED FOR
**CASCADIA COLLEGE &
UNIVERSITY OF
WASHINGTON BOTHELL**

kpff

1601 Fifth Avenue, Suite 1600
Seattle, WA 98101
206.622.5822
kpff.com

NO.	DATE	REVISION
-----	------	----------

DESIGN PARTNER:

KPFF CO
PROJECT MANAGER

MMM

PROJECT DESIGNER
LTERA, A

PROJECT TEAM MEMBERS

CDL

CHECK

TITLE

LOAD MAPS

PROJECT NO.
2000095
DATE
05/21/2021

SHEET NUMBER

S0.10

80% DESIGN




© 2021 MITHUN, INC.

LIVE LOAD SCHEDULE			
TYPE MARK	DESCRIPTION	LOAD, PSF (R=REDUCIBLE)	TYPE COMMENTS
A	TYP ROOF	40 (R) LIVE	-
B	TYPICAL FLOOR	100	-
C	STAIRS	100	-
D	LIGHT MECHANICAL	75	NOTE 5
E	MECHANICAL	90	NOTE 5
F	STEEL FRAMED ROOFS	25	-
G	LIGHT STORAGE	125	-

SUPERIMPOSED DEAD LOAD SCHEDULE			
TYPE MARK	DESCRIPTION	LOAD, PSF	TYPE COMMENTS
1	TYP ROOF	30	NOTE 7
2	TYPICAL FLOOR	15	-
3	CONCRETE TOPPING	90	-
4	CANOPSIS	15	-
5	SKYLIGHT	10	-





LOAD SCHEDULE NOTES:

1.  INDICATES LIVE LOAD AND SUPERIMPOSED LOAD PER SCHEDULES. LOADING OCCURS WITHIN REGIONS BOUNDED BY BOLD LINES
2. (R)  INDICATES LIVE LOADS ARE REDUCED IN ACCORDANCE WITH BUILDING CODE PROVISIONS.
3.  INDICATES CLADDING SUPERIMPOSED DEAD LOAD APPLIED AT BUILDING PERIMETER IN POUNDS PER LINEAR FOOT.
4. EXTERIOR BALCONIES AND DECKS ARE DESIGNED FOR THE SAME LIVE LOAD AS THE OCCUPANCY SERVED.
5. WHERE NOTED EQUIPMENT WEIGHTS ARE EXCEEDED, FLOORS ARE DESIGNED FOR ACTUAL EQUIPMENT WEIGHT + 4" HOUSEKEEPING PAD + 40 PSF IN OPEN AREAS.
6. REFER TO TABLE 1607.1 IN THE IBC FOR RELEVANT CONCENTRATED LIVE LOADS.
7. SOL INCLUDES 5 PSF FOR PV PANELS WHERE NOTED.
8. ALL ROOFTOP STRUCTURE ROOFS ARE DESIGNED FOR 25 PSF LIVE LOAD AND 15 PSF SUPERIMPOSED DEAD LOAD.

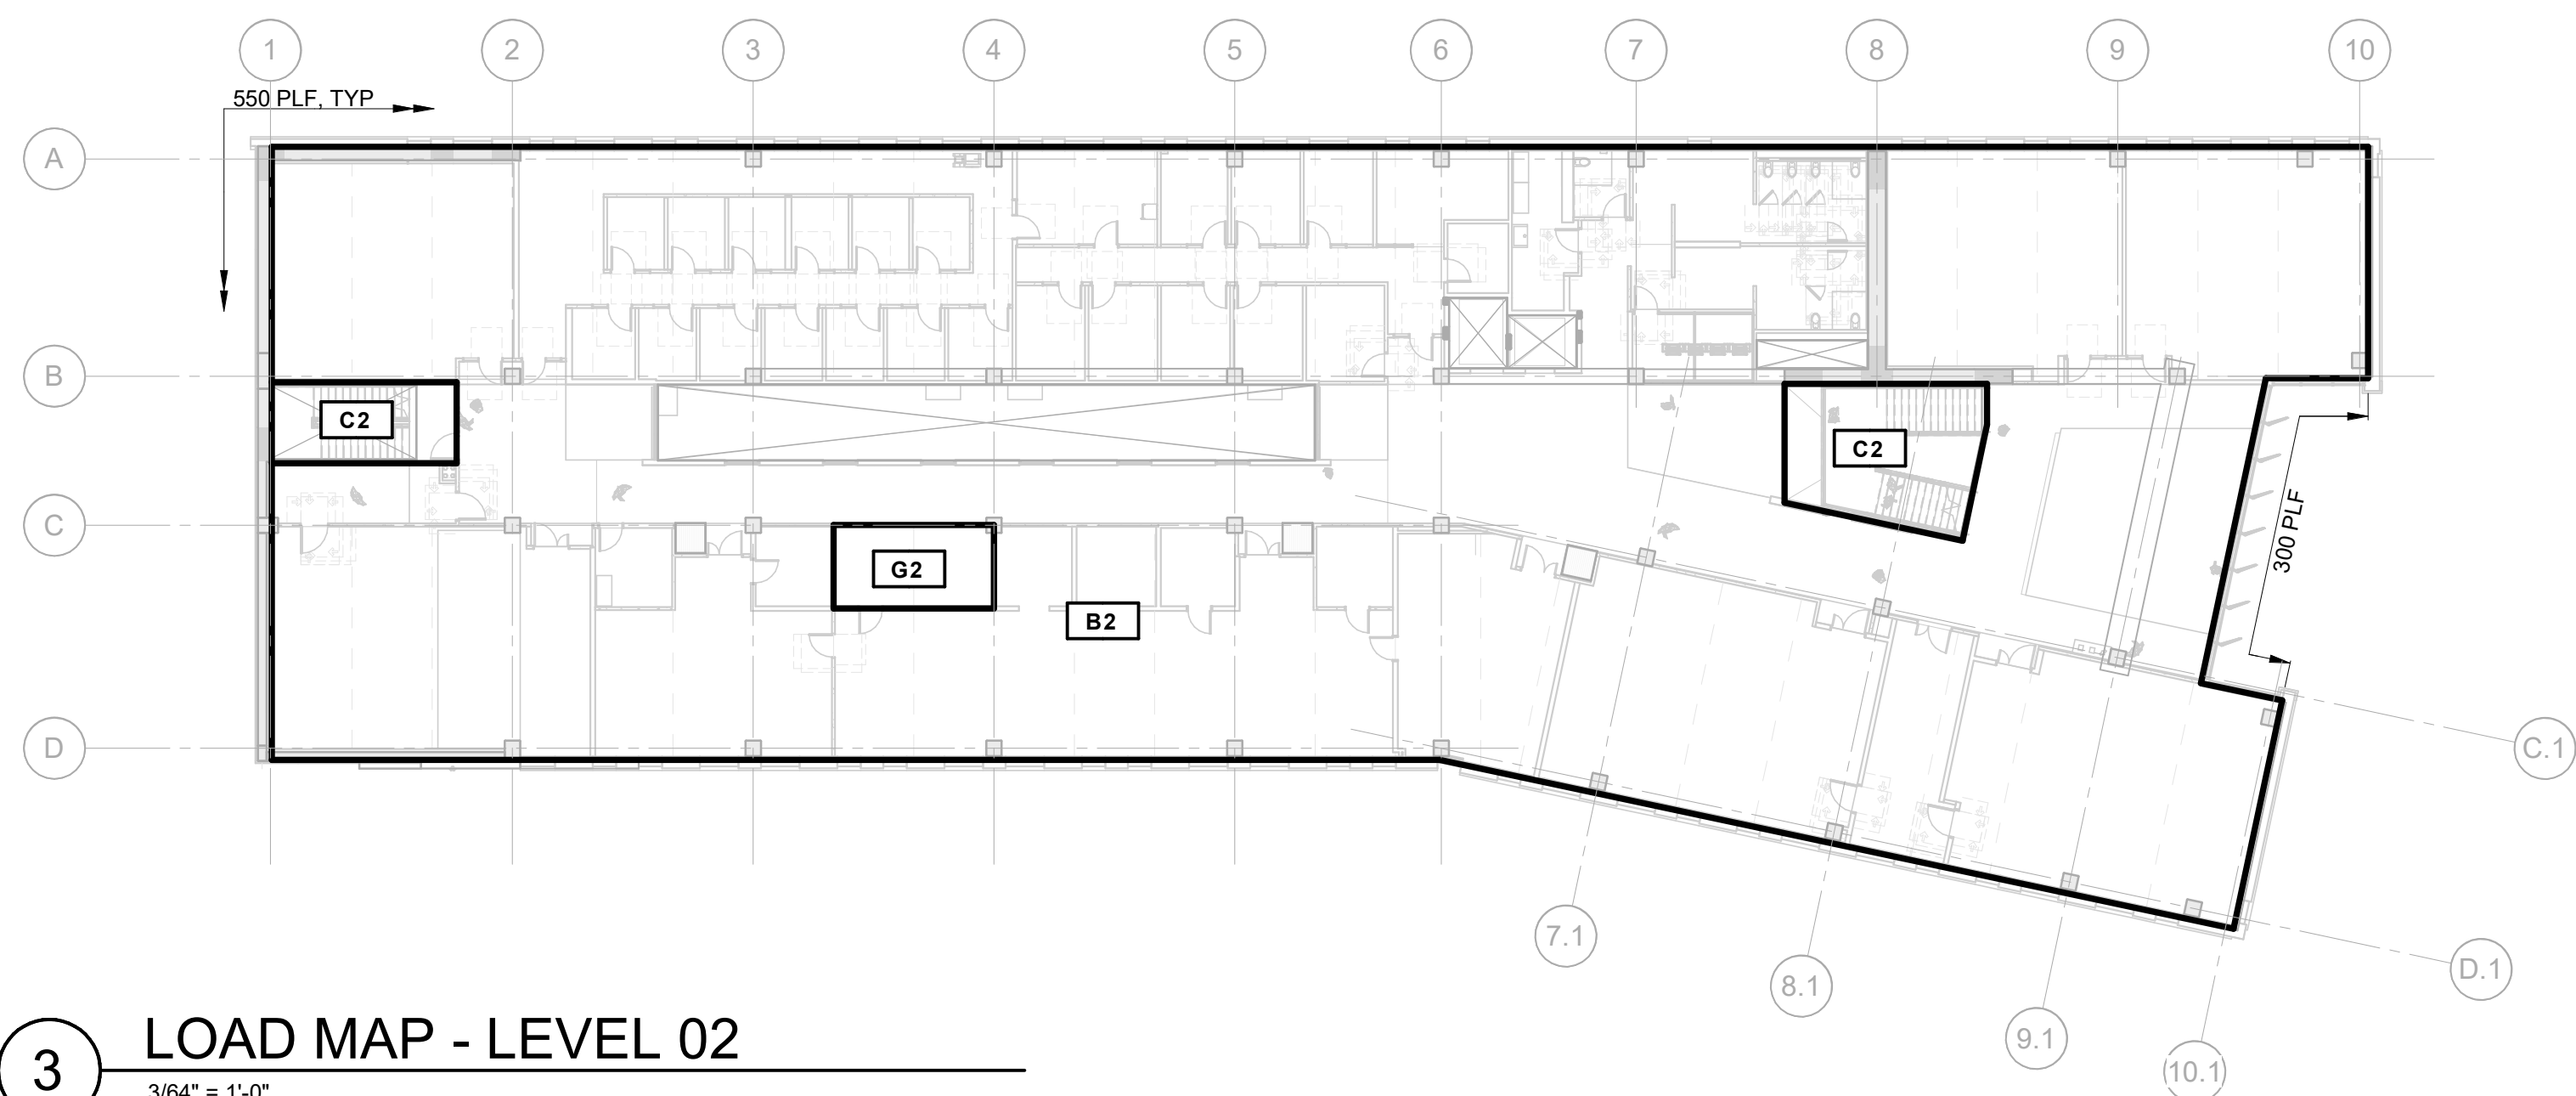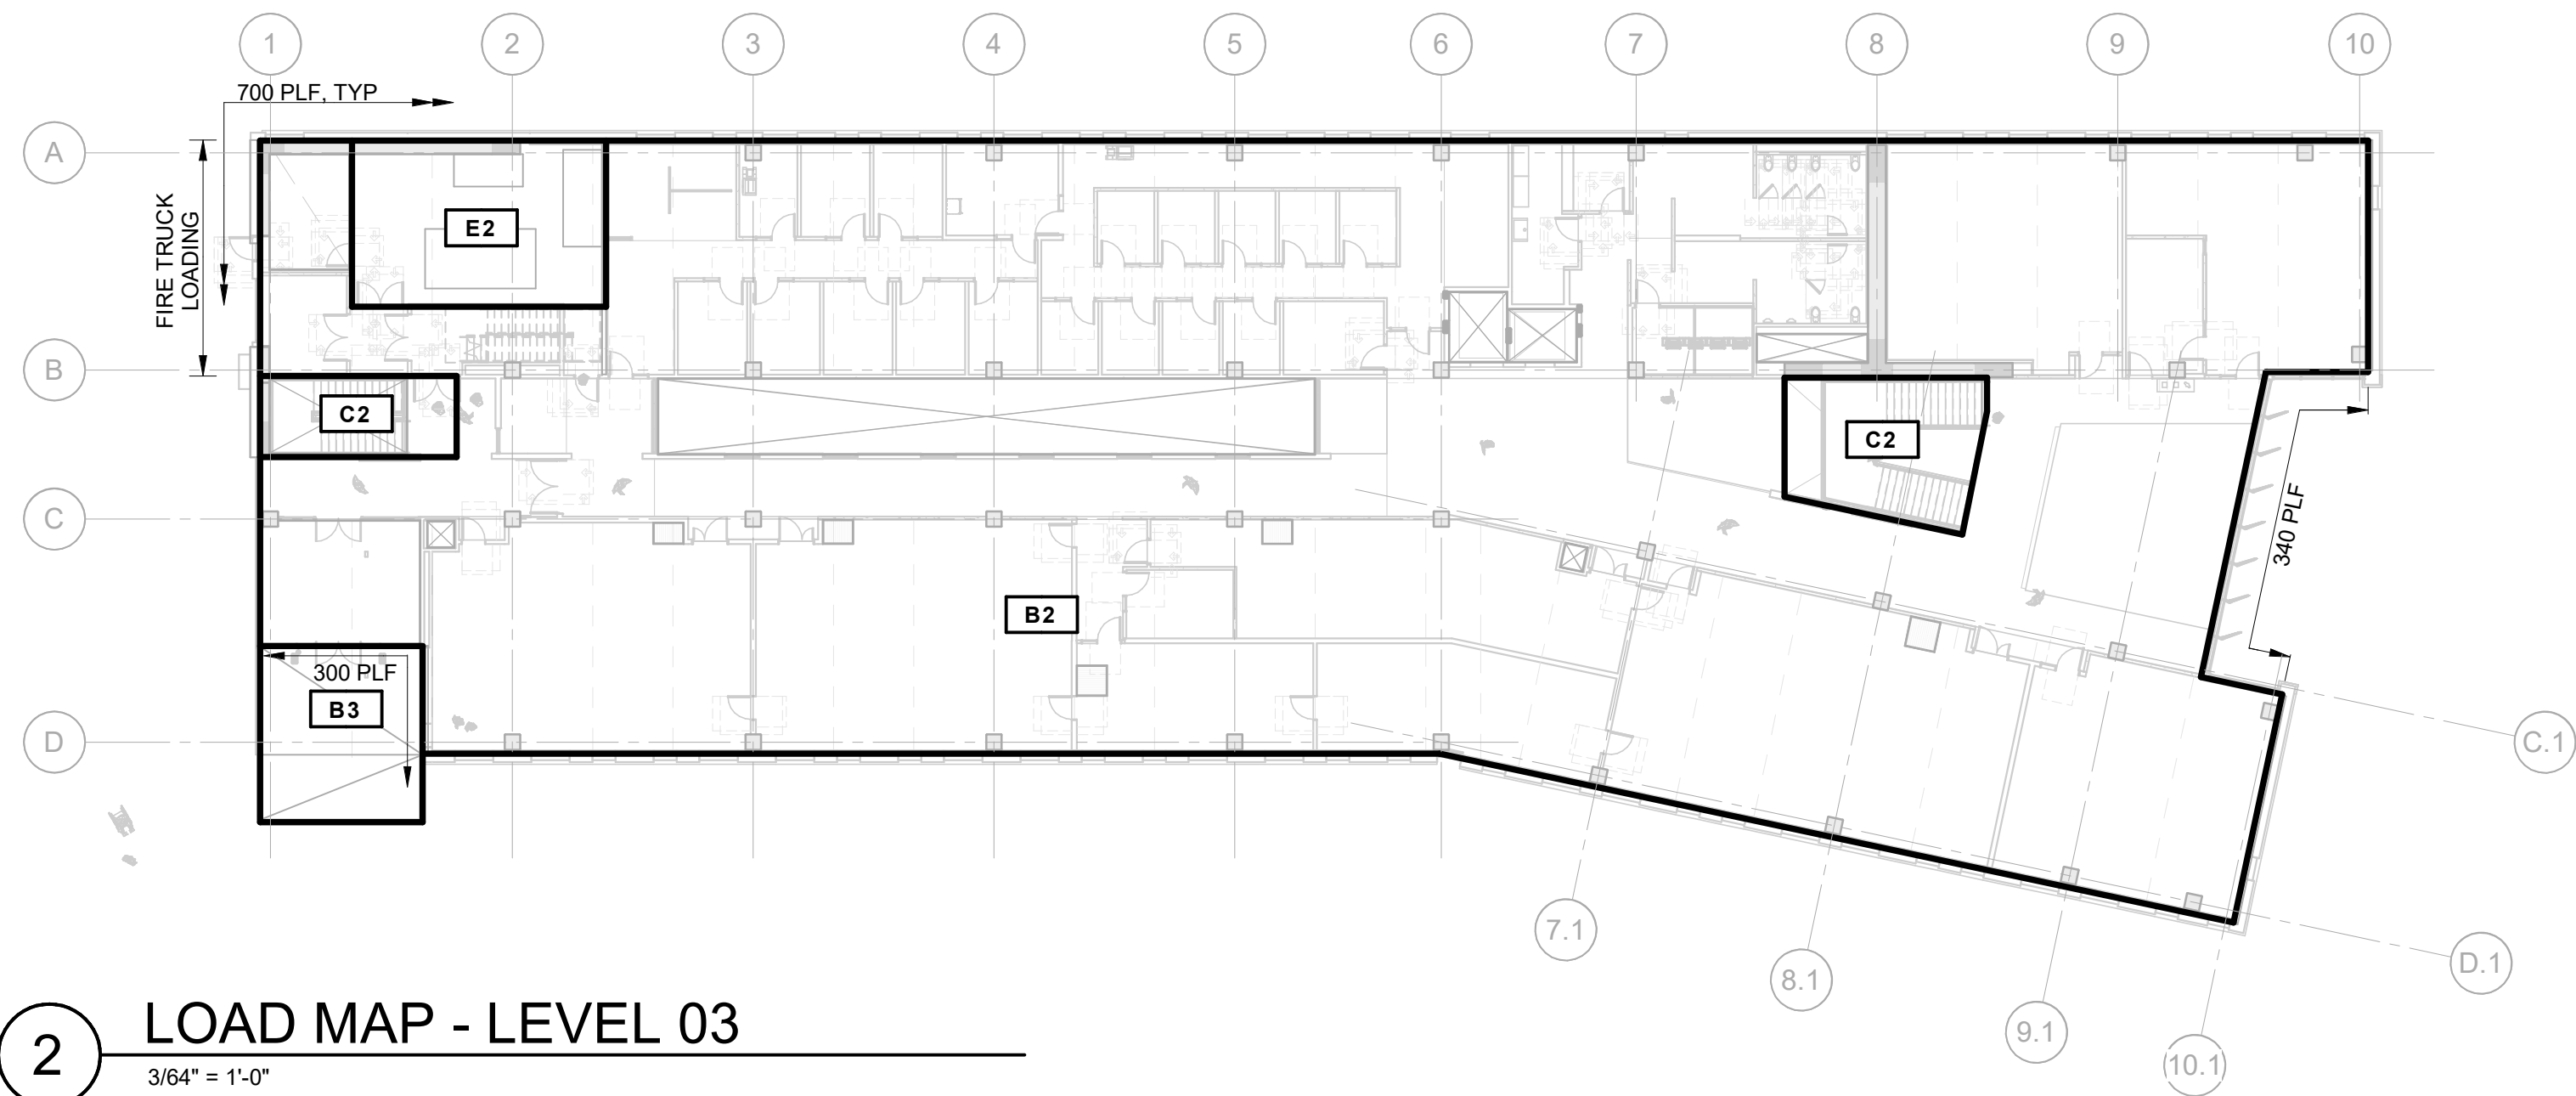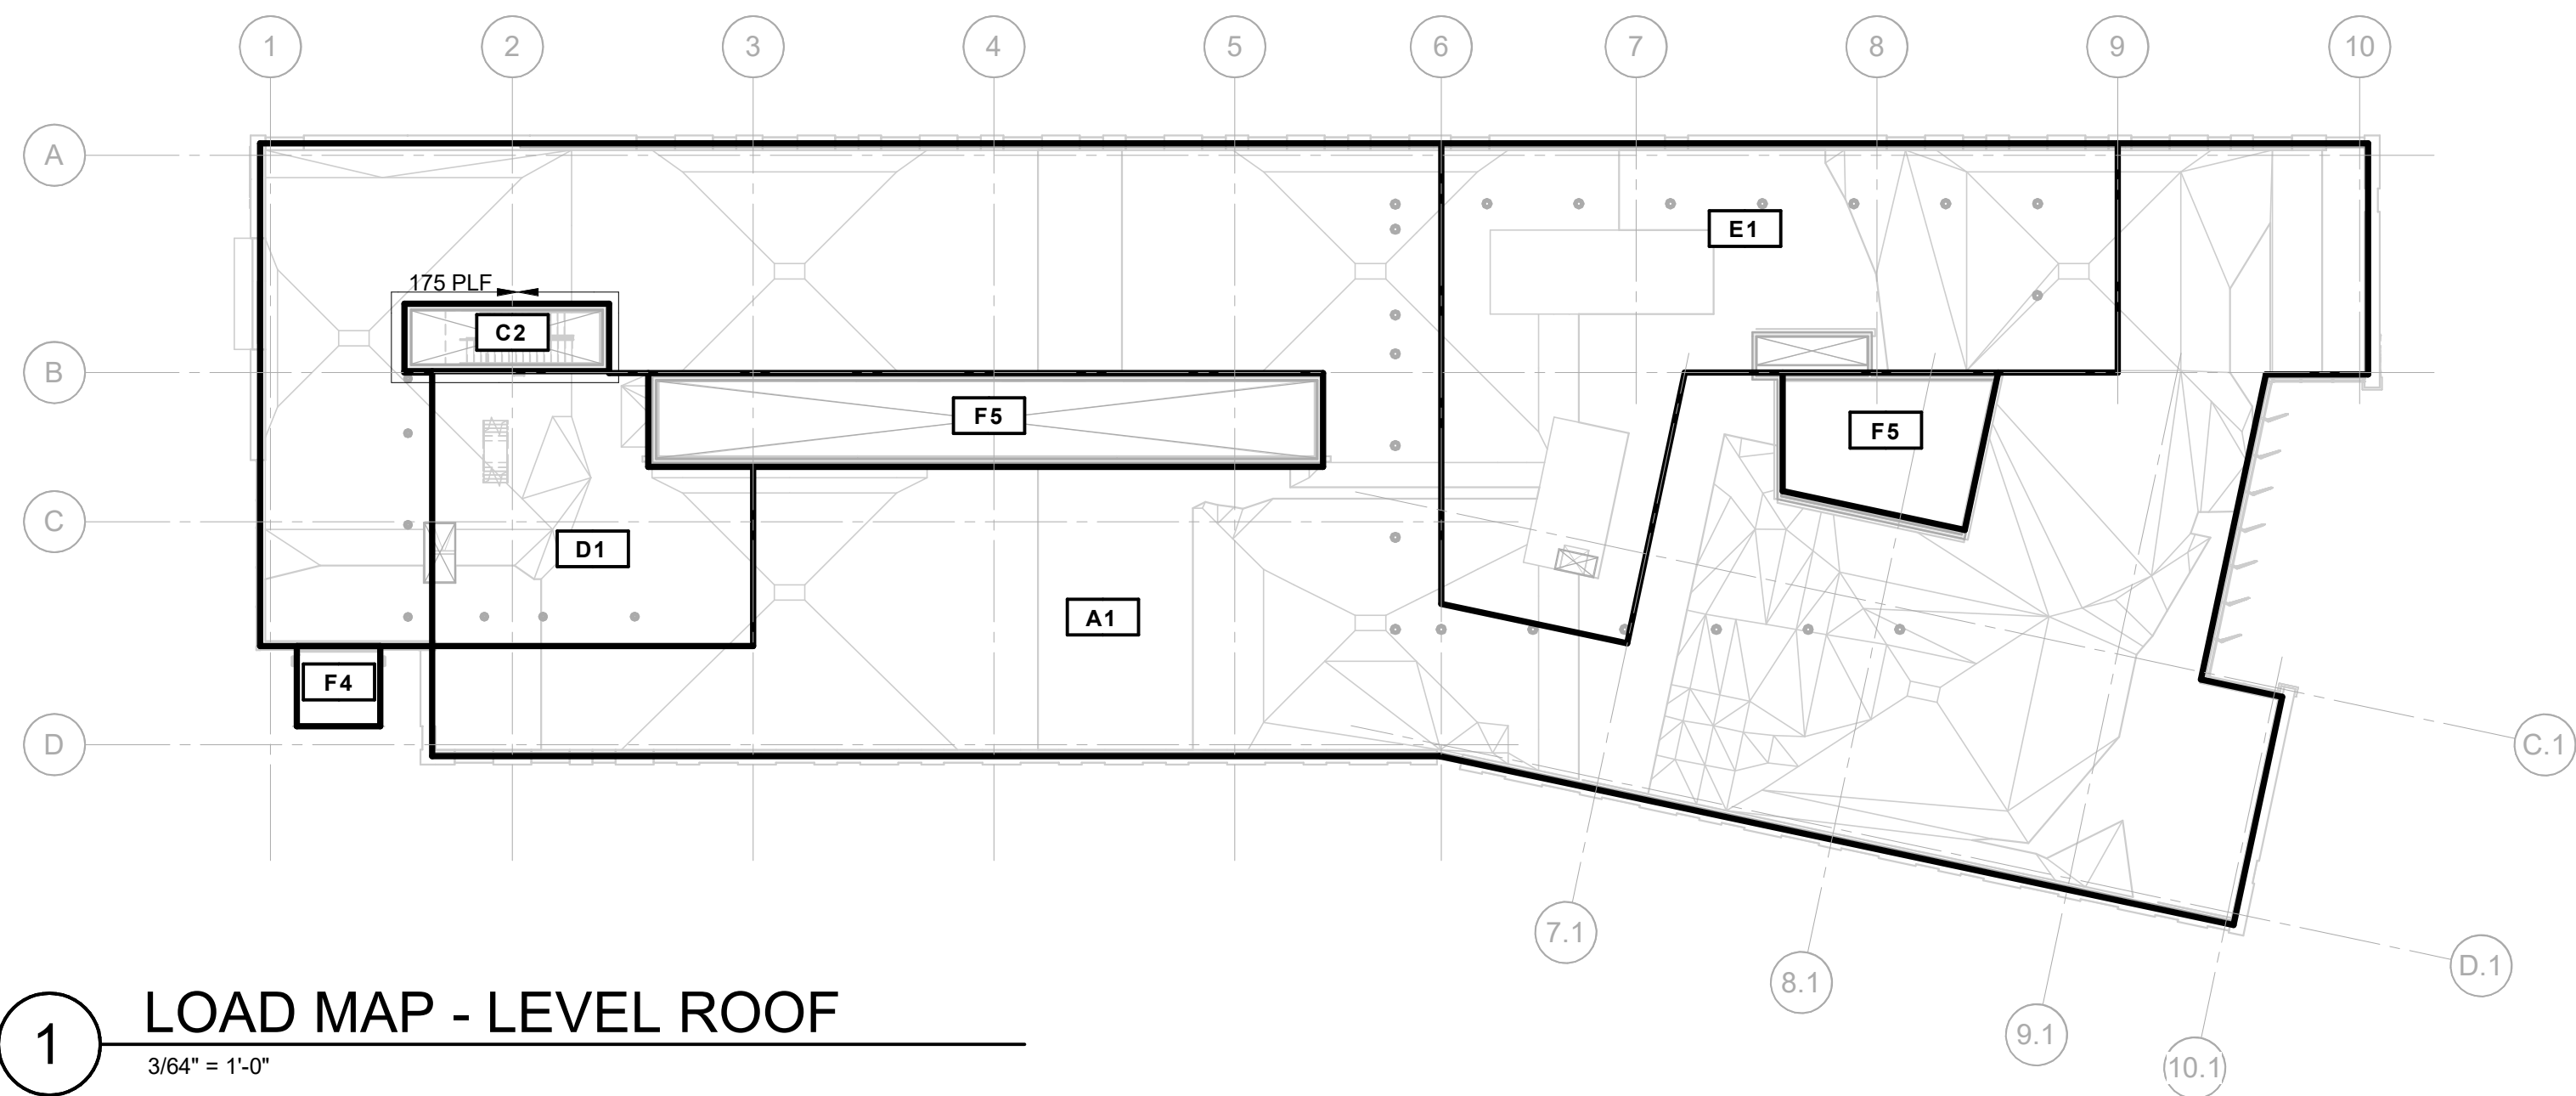

CITY OF BOTHELL APPROVAL STAMP


THIS DRAWING IS FOR THE EXCLUSIVE USE OF MCCLONE CONSTRUCTION COMPANY, ON THIS PROJECT ONLY. UTILIZATION OF THIS DRAWING BY OTHER PARTIES AND/OR ON OTHER PROJECTS WITHOUT THE EXPRESSED WRITTEN CONSENT OF MCCLONE CONSTRUCTION COMPANY IS STRICTLY PROHIBITED.

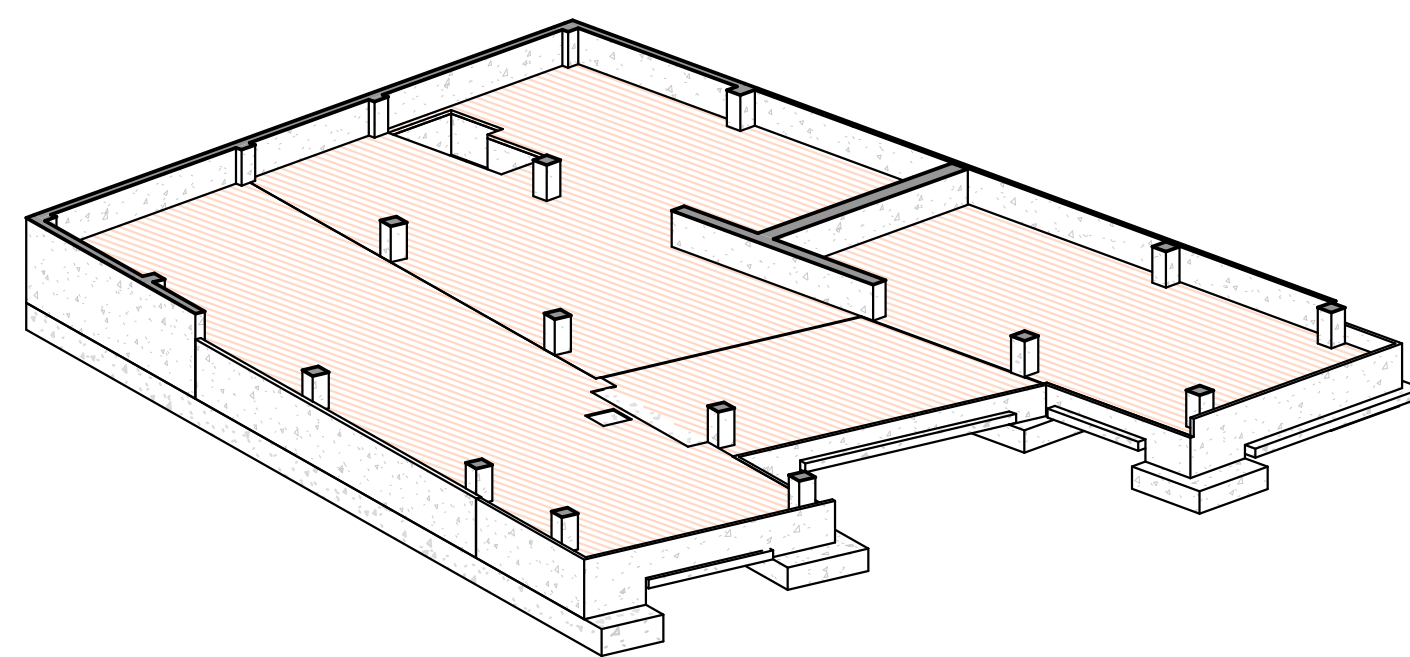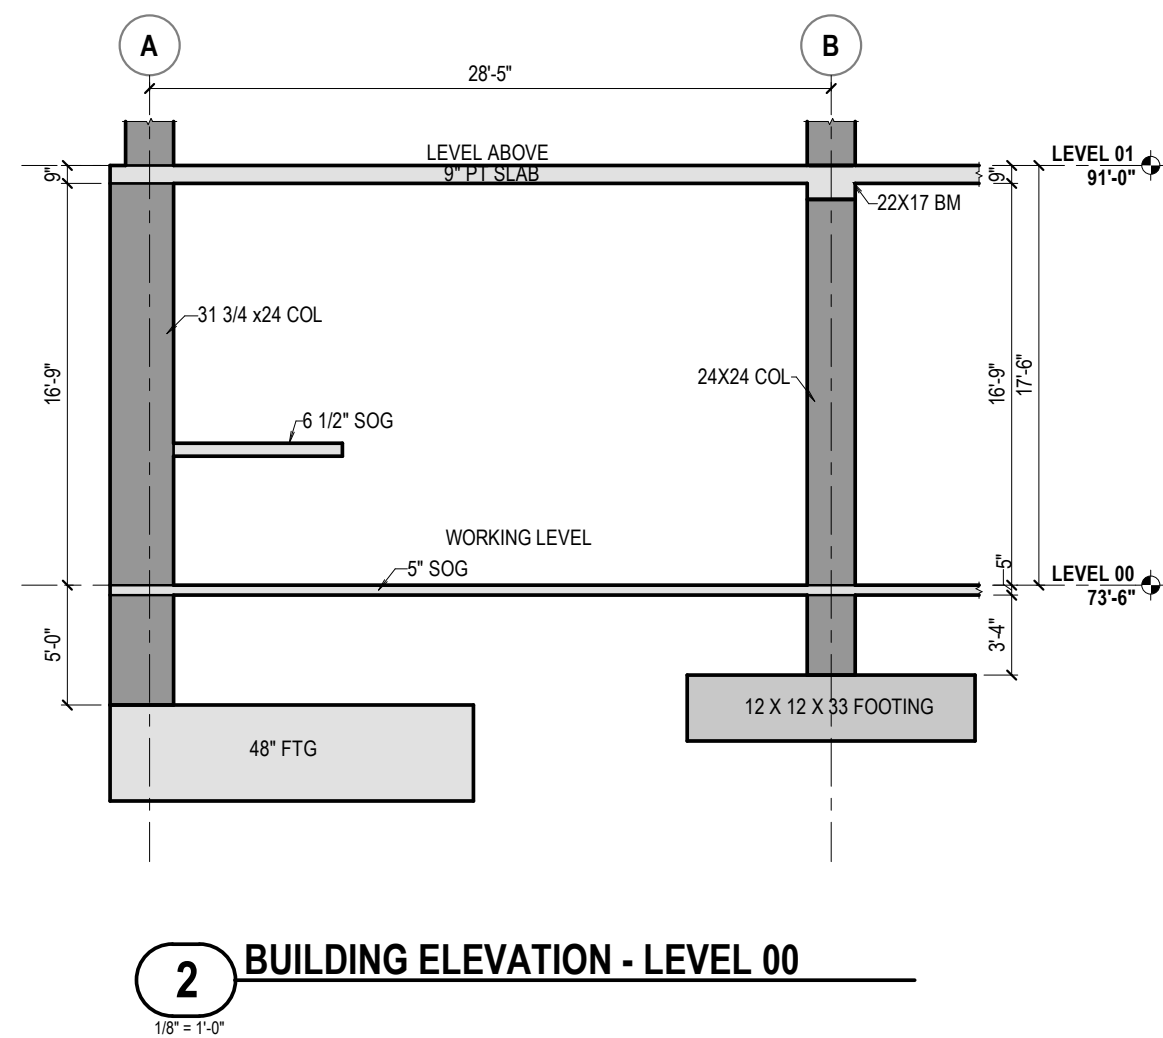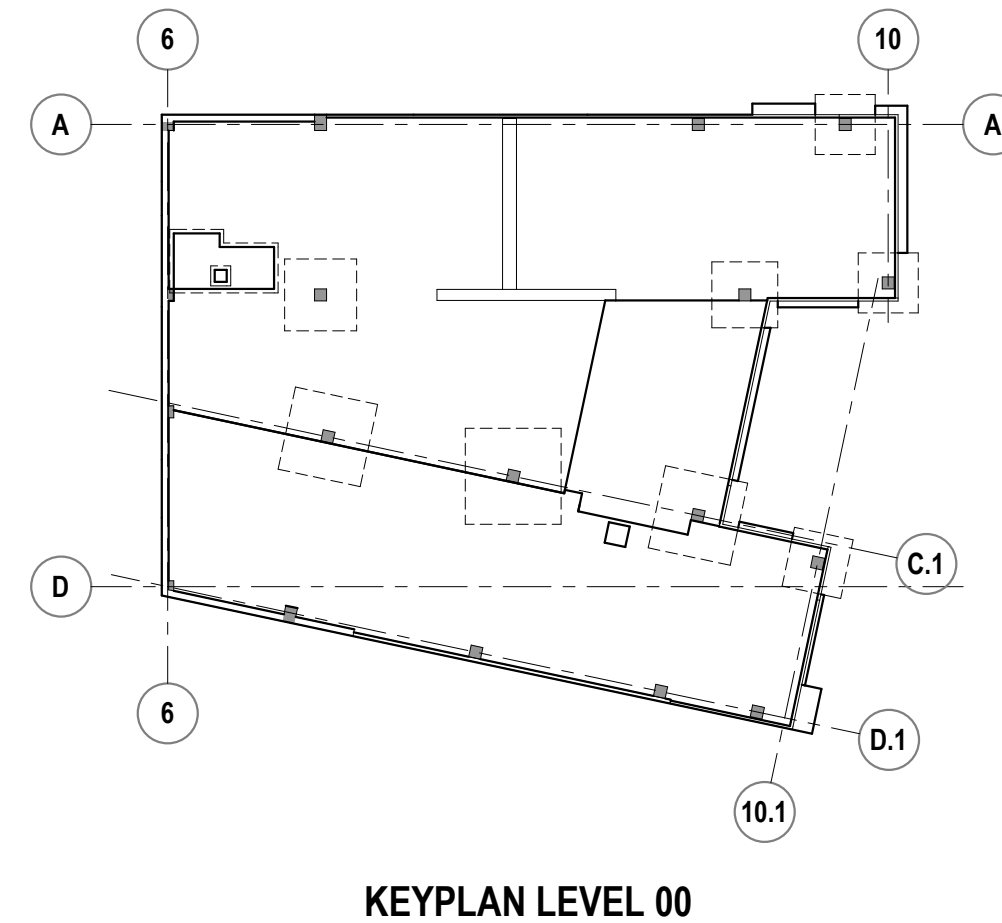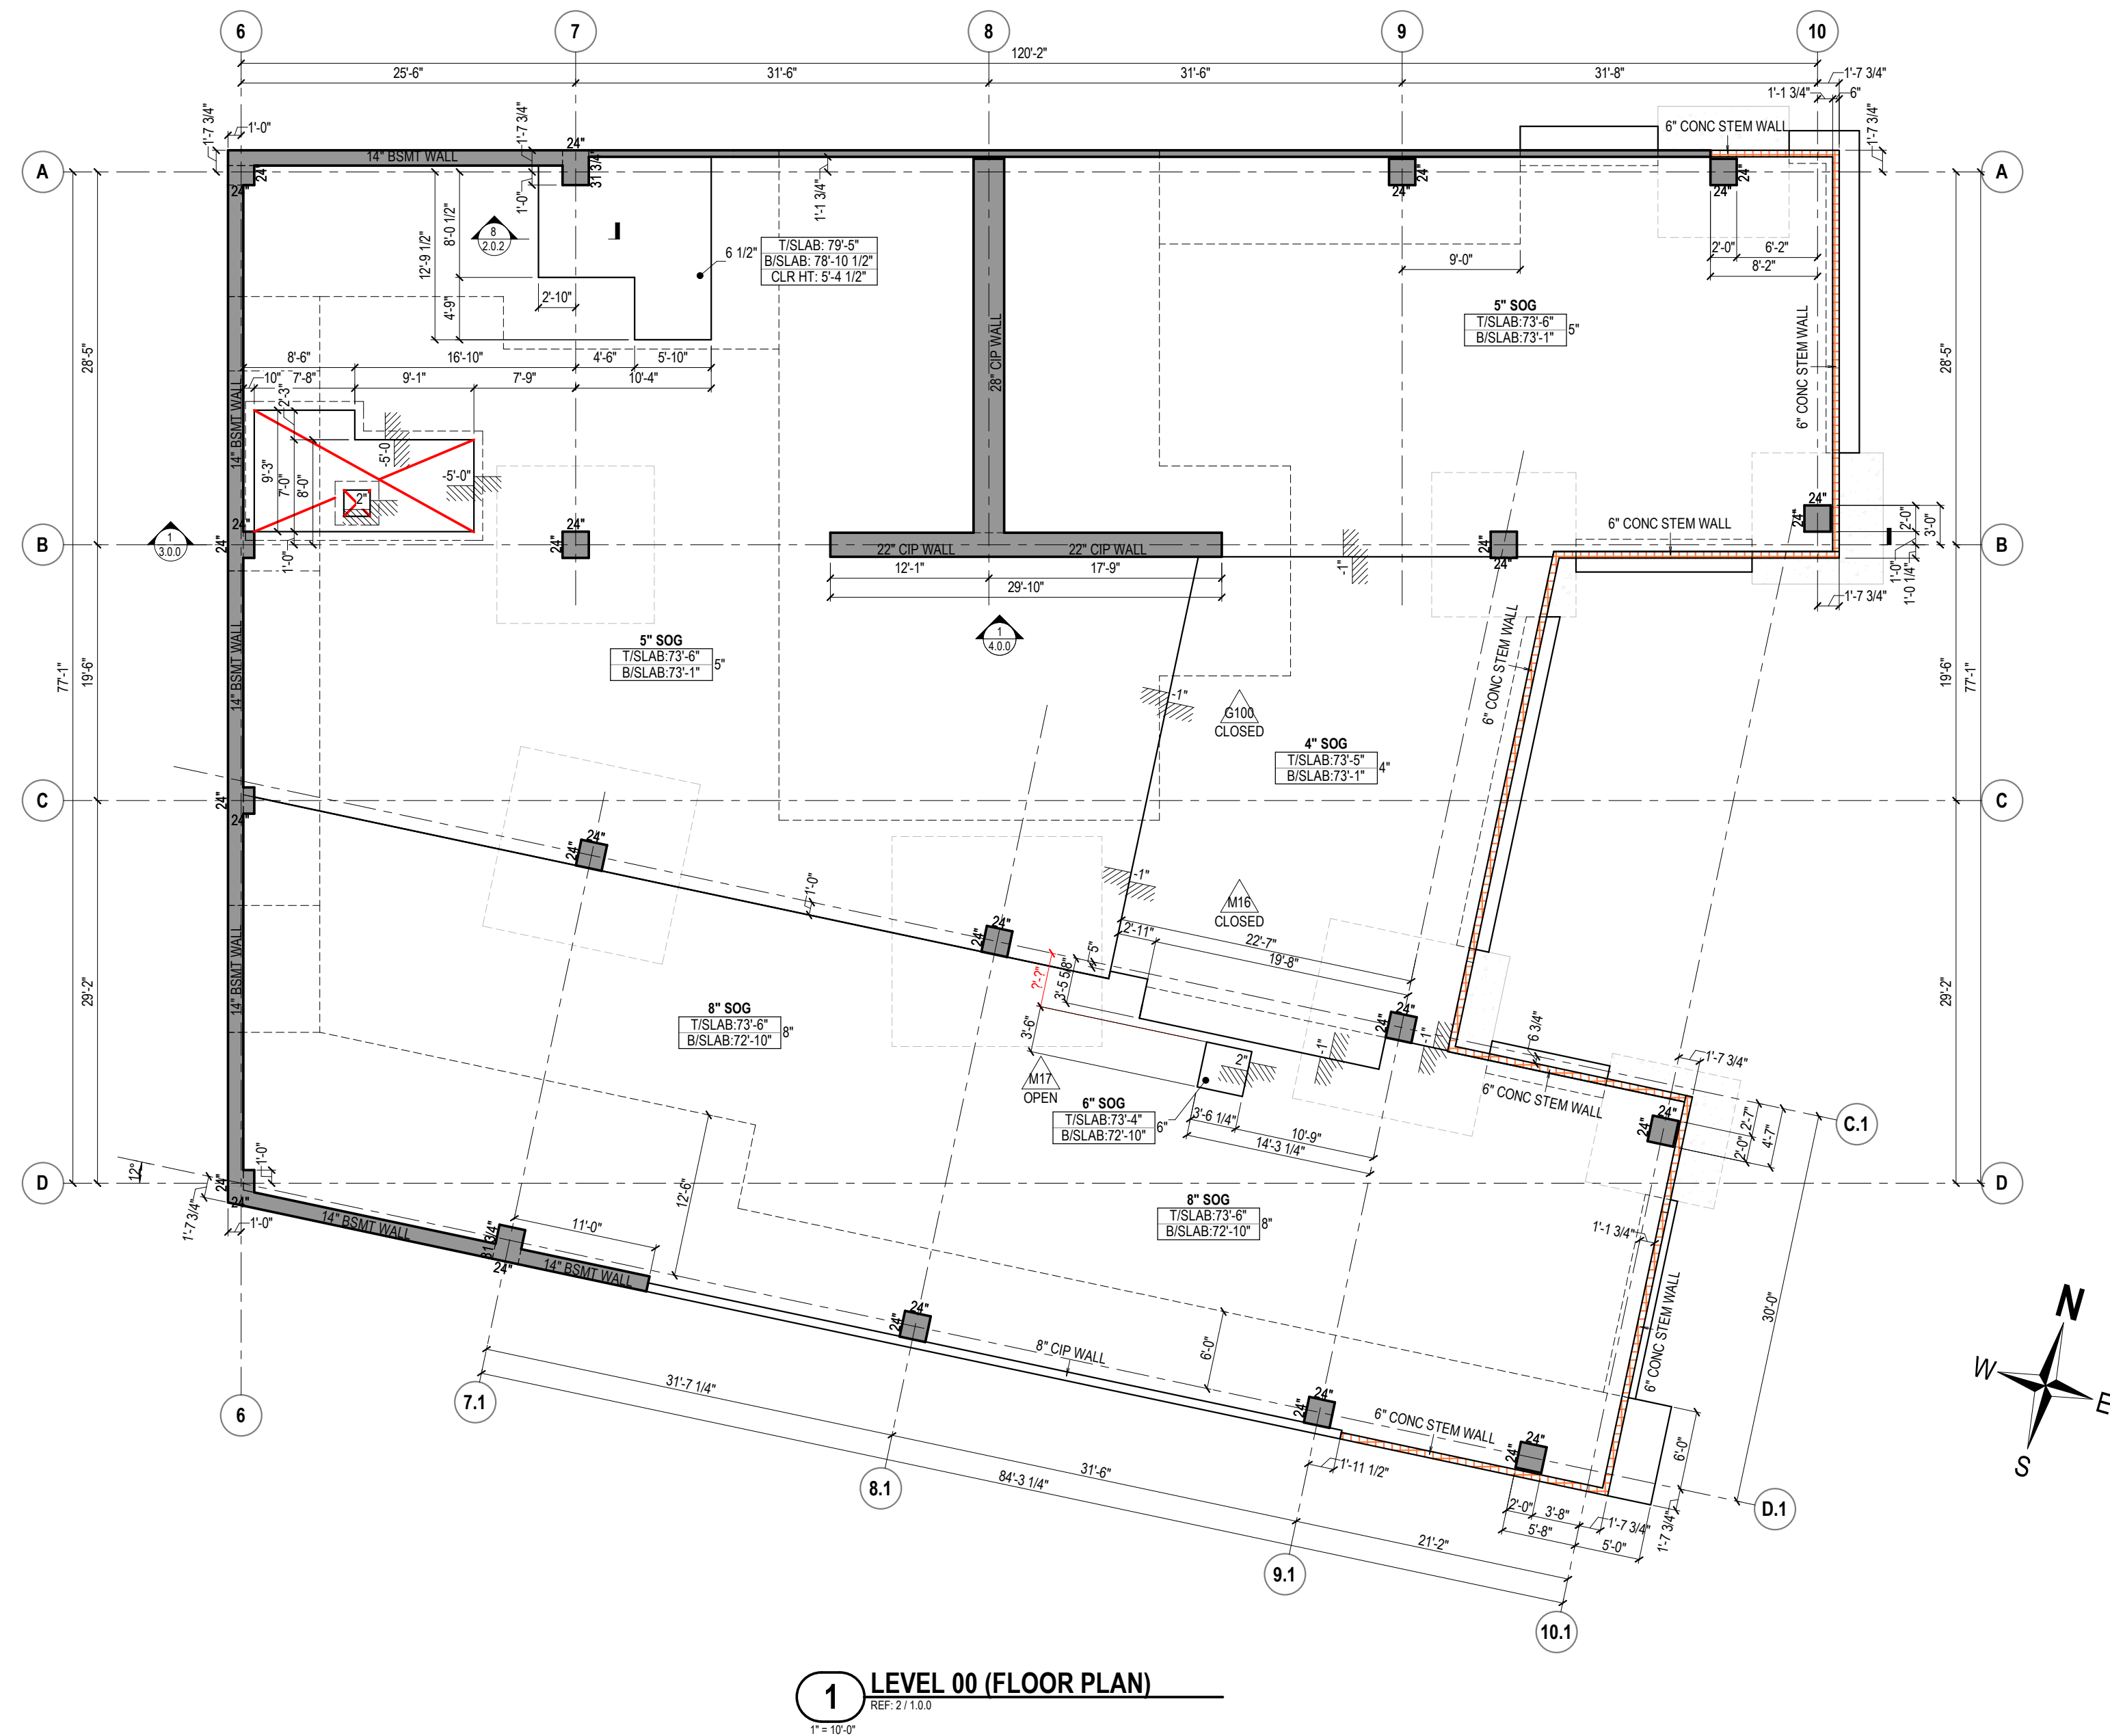

- NOTES:**
- 3/4" CHAMFER ON ALL EXPOSED CONCRETE CORNERS TYP.
 - ALL COLUMNS ARE CENTERED ON GRID LINES U.N.O.
 - ALL BEAMS ARE CENTERED ON GRID LINES U.N.O.
 - SLAB THICKNESS IS 5" TYP. U.N.O.
 - DO NOT SCALE THIS DRAWING. USE DIMENSIONS PROVIDED.


SYMBOLS		SHADE DESIGNATIONS	
1-BOX (ROUND-ENDS) TOP OF CONCRETE ELEVATIONS	(TOP ELEV)	FOOTINGS OR FOUNDATIONS	
1-BOX BOTTOM OF CONCRETE ELEVATIONS	(BOT ELEV)	WALLS OR COLUMNS	
2-BOX (PLAN VIEWS) TOP & BOTTOM ELEVATIONS D - DEPTH OF CONC. MEMBER	(TOP ELEV) (BOT ELEV) 1"	CMU WALLS	
3-BOX (FLOOR PLANS) TOP & BOTTOM ELEVATIONS COLUMN ELEVATION ABOVE REF. LEVEL D - DEPTH OF CONC. MEMBER	(TOP ELEV) (BOT ELEV) (TO COL. ELEV) 1"	DELAY STRIP OR CLOSURE POUR	
		GRADE OR SOIL	
		6" STEM WALL	
SECTION VIEW		LINE DESIGNATIONS	
SHEET NUMBER	Ref. 1.0.0	INDICATES TOP OF FTG CHANGE OR EDGE OF FTG	
ELEVATION VIEW	1.0.0	INDICATES BOTTOM OF FTG CHANGE	
SHEET NUMBER	1.0.0	INDICATES CONSTRUCTION JOINT	
		INDICATES GRID LINE	

THIS DRAWING IS FOR THE EXCLUSIVE USE OF MCCLONE CONSTRUCTION COMPANY, ON THIS PROJECT ONLY. UTILIZATION OF THIS DRAWING BY OTHER PARTIES AND/OR ON OTHER PROJECTS WITHOUT THE EXPRESSED WRITTEN CONSENT OF MCCLONE CONSTRUCTION COMPANY IS STRICTLY PROHIBITED.

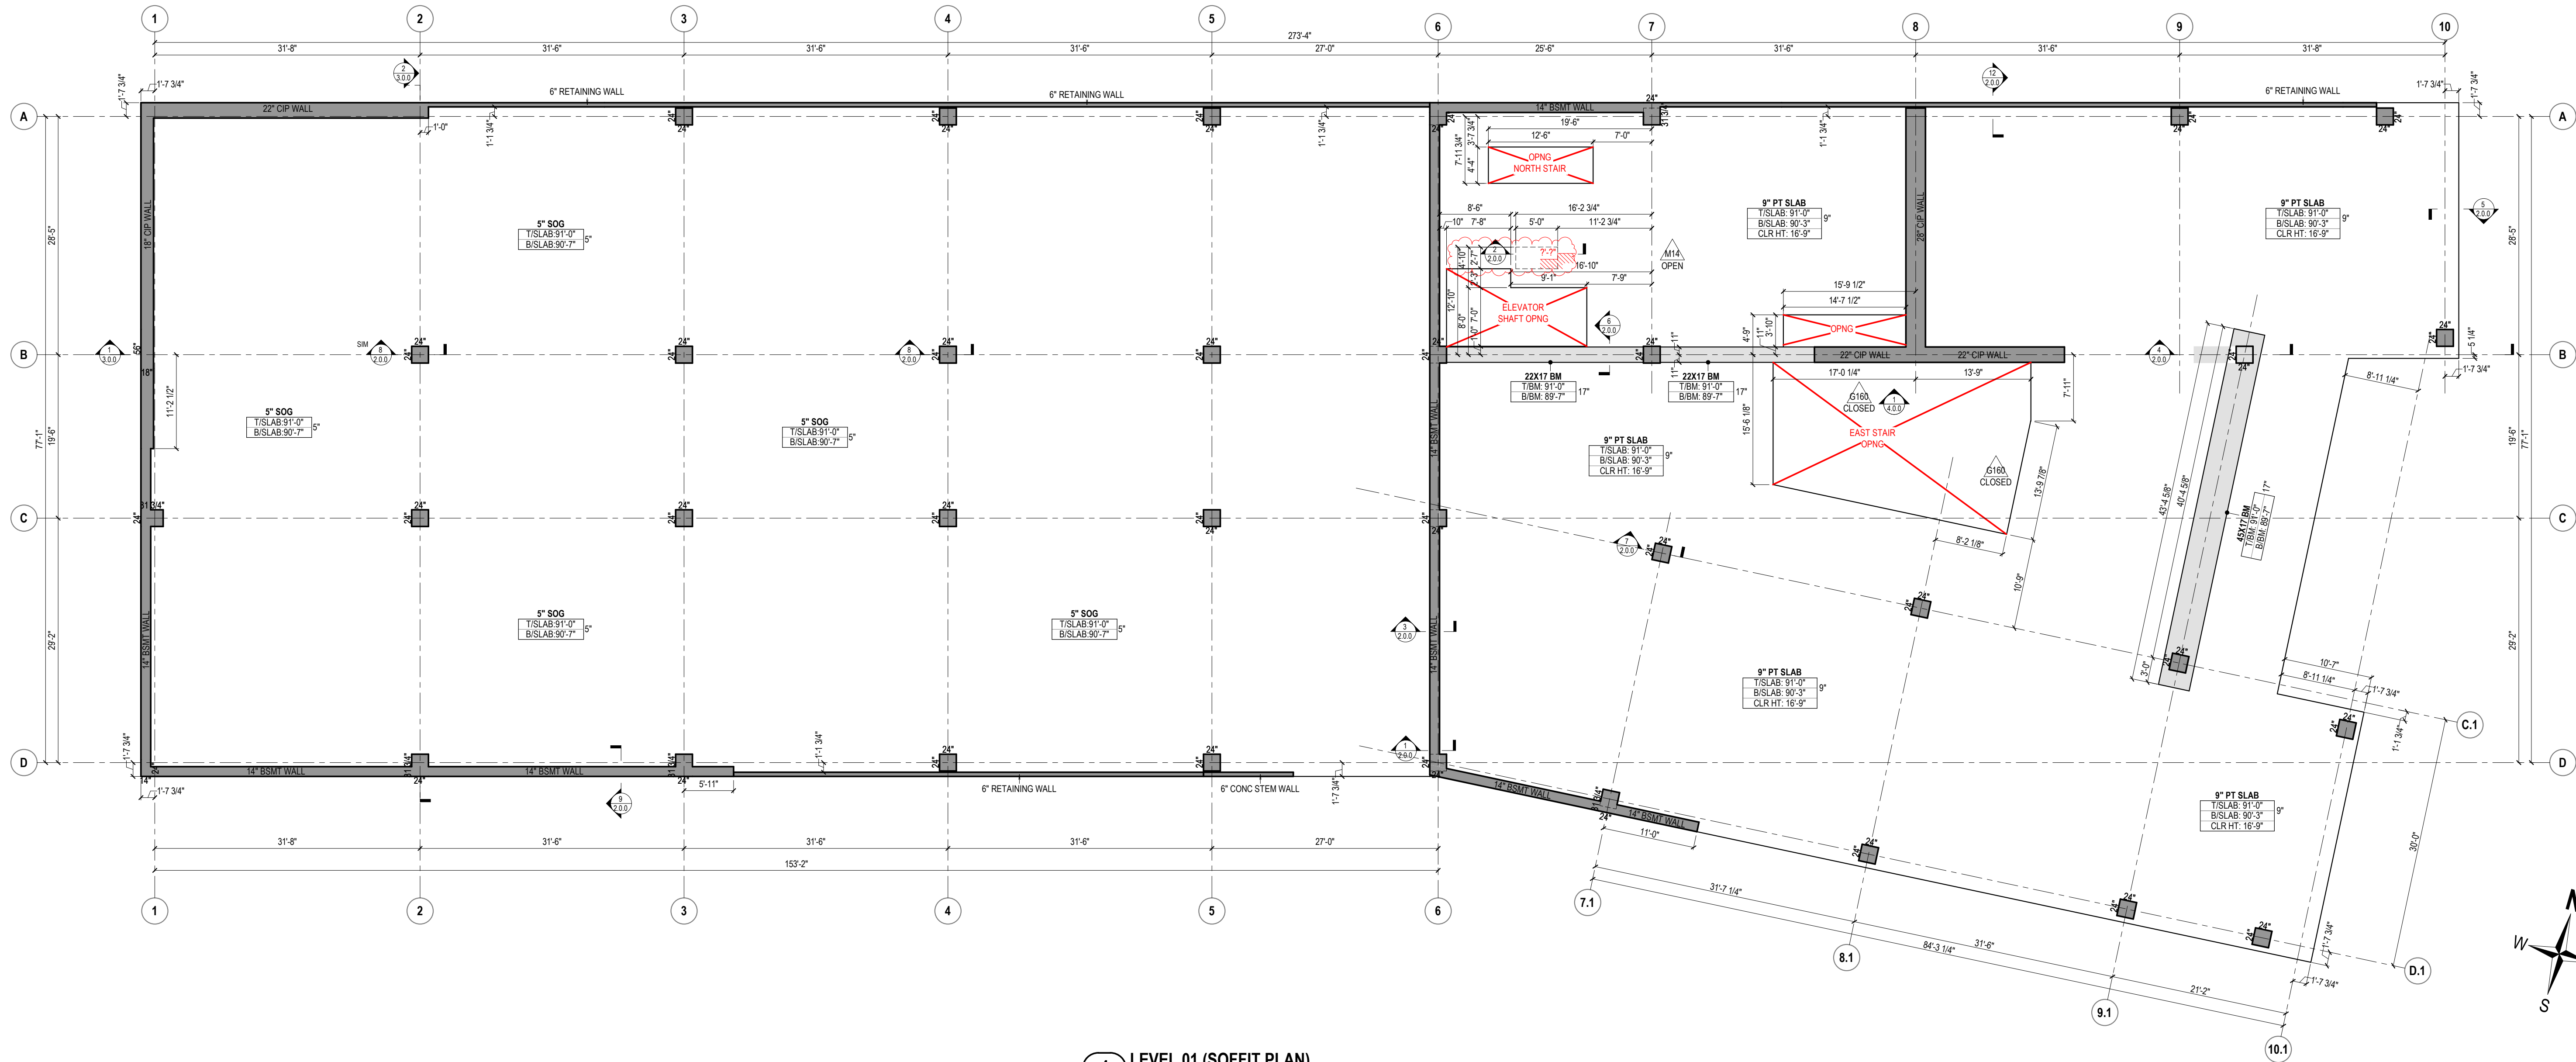


1 LEVEL 01 (SOFFIT PLAN)

1" = 10'-0"

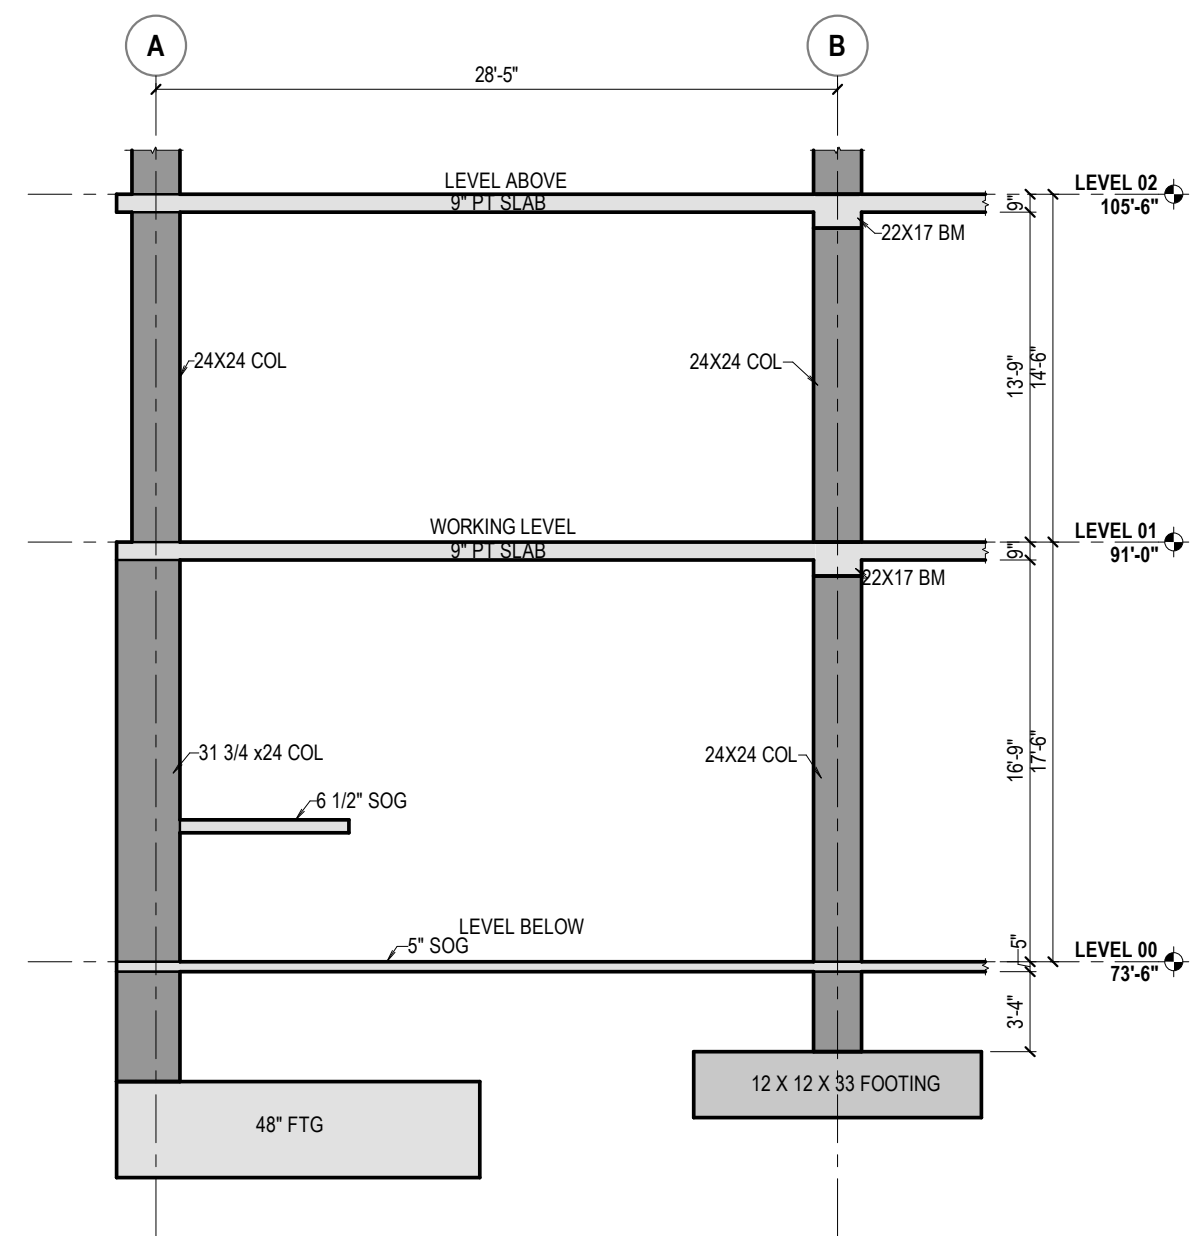


2 BUILDING ELEVATION - LEVEL 01

1/8" = 1'-0"

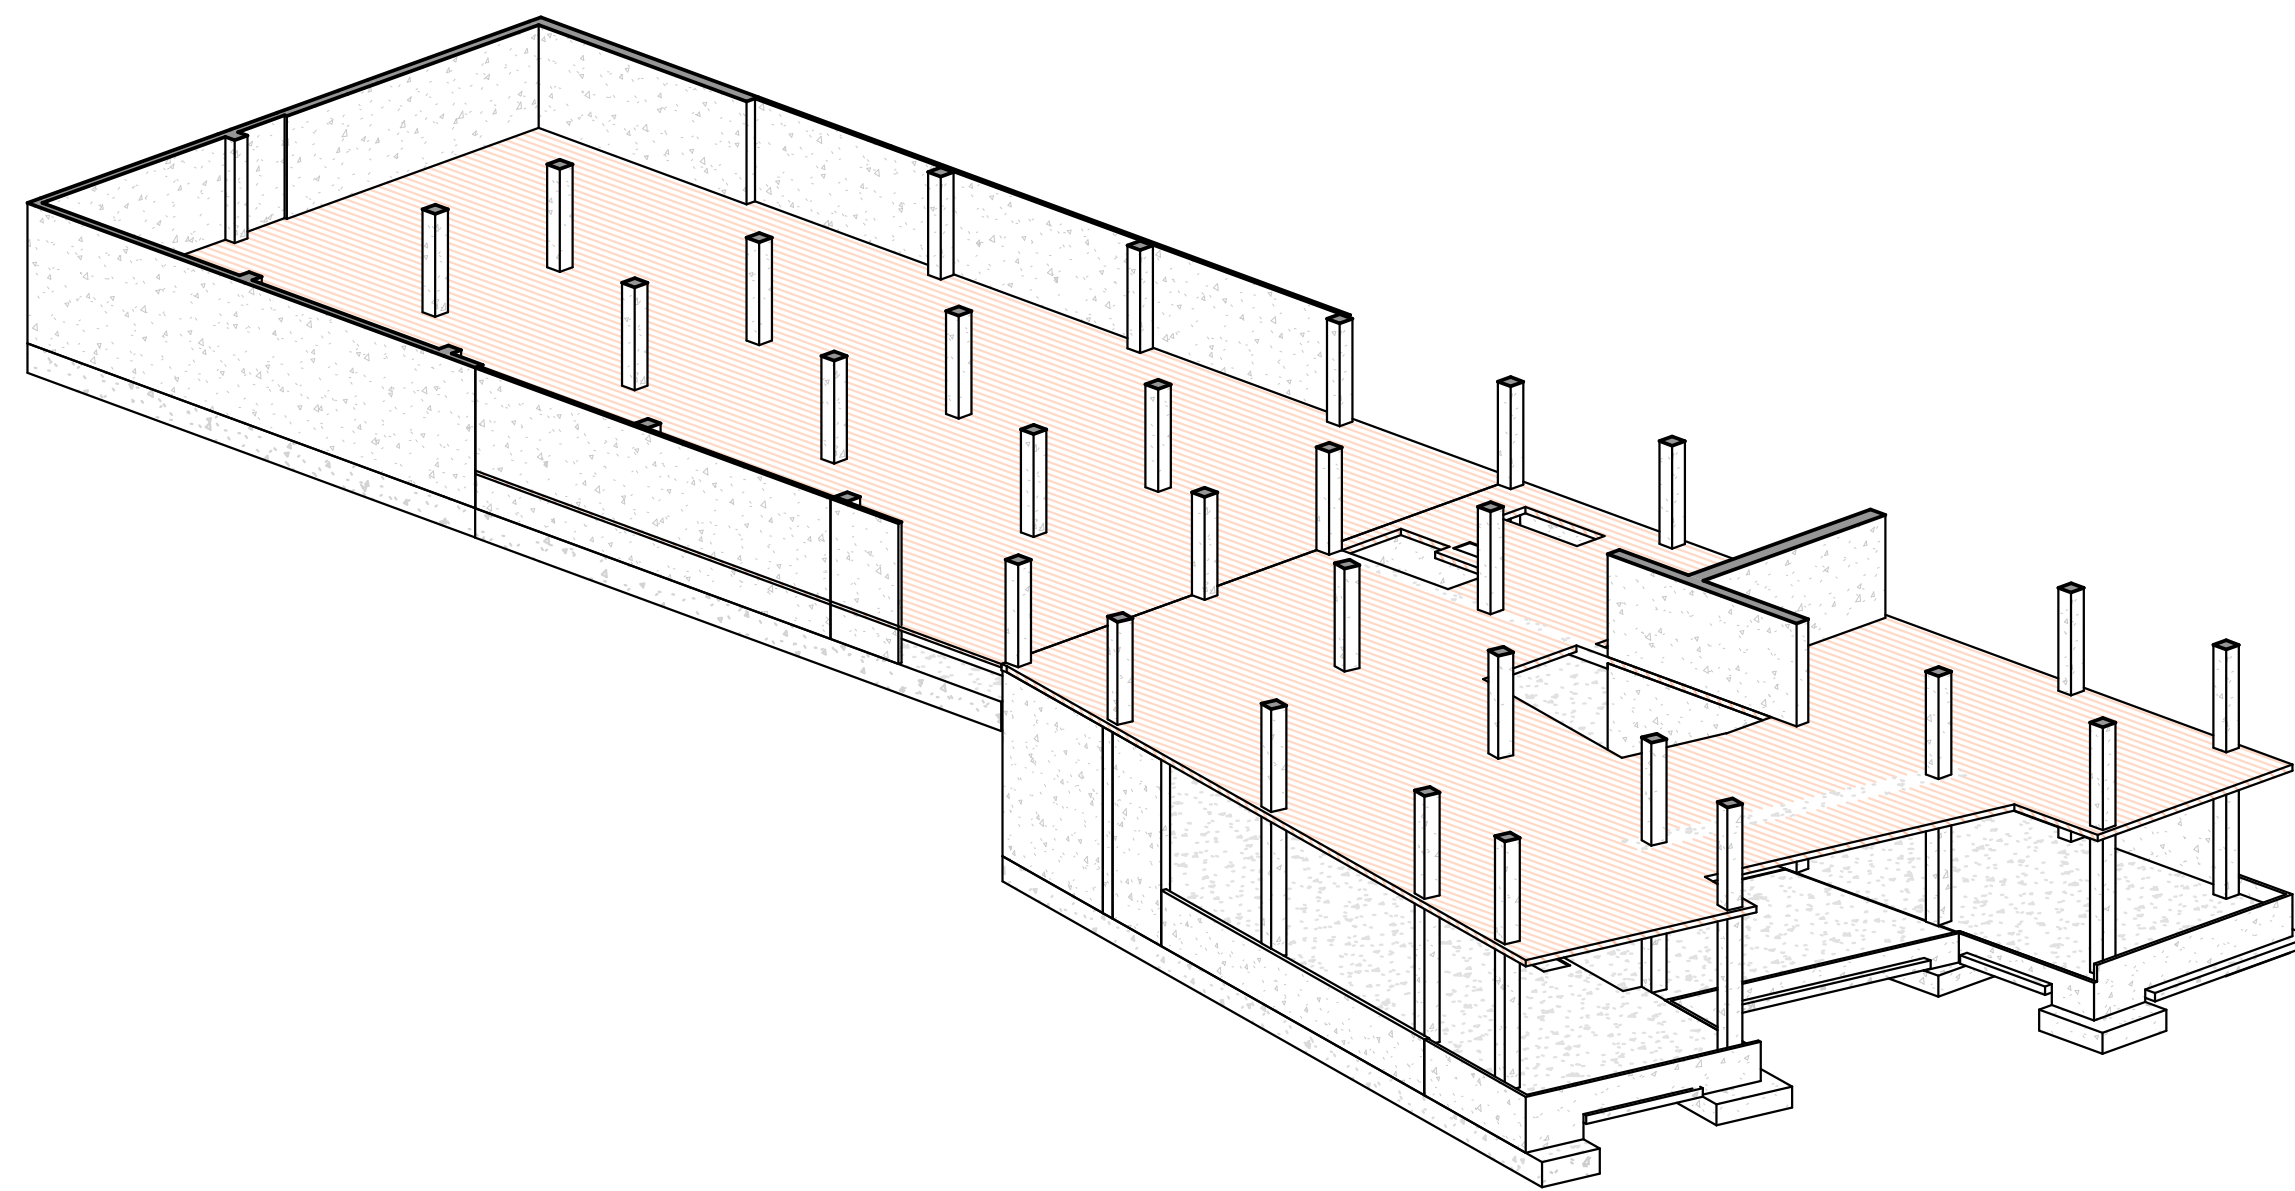

3 3D VIEW - LEVEL 01

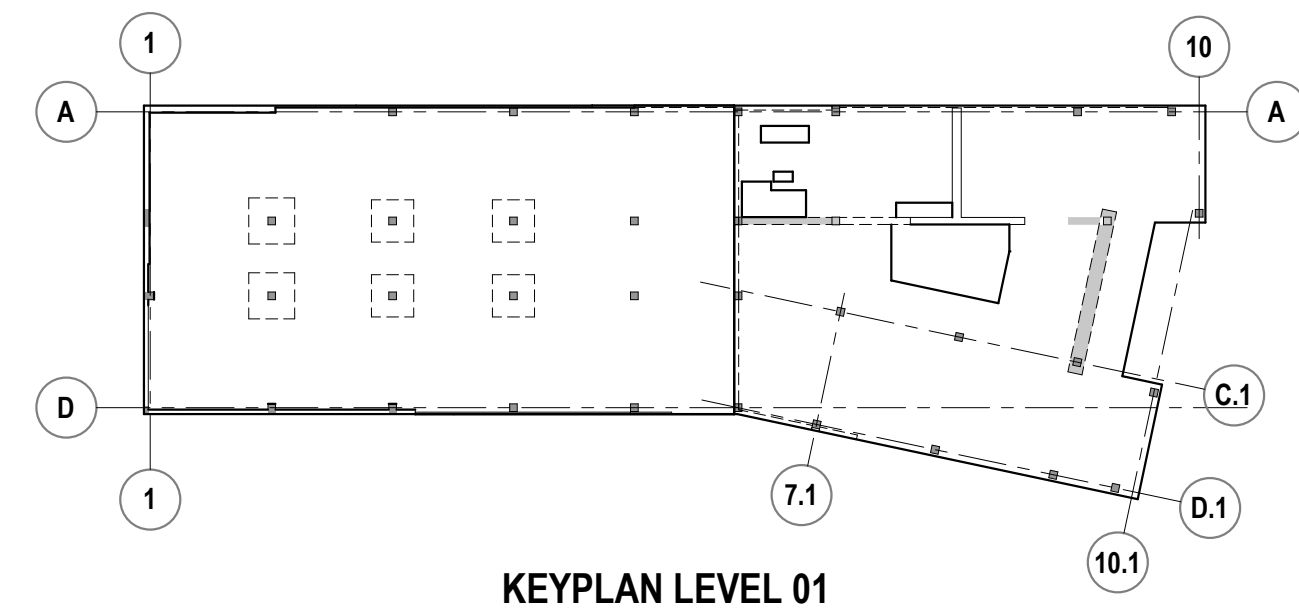

KEYPLAN LEVEL 01

NOTES:

- 3/4" CHAMFER ON ALL EXPOSED CONCRETE CORNERS TYP.
- ALL COLUMNS ARE CENTERED ON GRID LINES U.N.O.
- ALL BEAMS ARE CENTERED ON GRID LINES U.N.O.
- SLAB THICKNESS IS 8" TYP U.N.O.
- DO NOT SCALE THIS DRAWING, USE DIMENSIONS PROVIDED.

LEGEND

SYMBOLS

- 1-BOX (ROUND-ENDS)
TOP OF CONCRETE ELEVATIONS
- 1-BOX
BOTTOM OF CONCRETE ELEVATIONS
- 2-BOX (PLAN VIEWS)
TOP & BOTTOM ELEVATIONS
D = DEPTH OF CONC. MEMBER
- 3-BOX (SOFFIT PLANS)
TOP & BOTTOM ELEVATIONS
HEIGHT BELOW REFERENCE LEVEL
D = DEPTH OF CONC. MEMBER

SECTION VIEW

Ref. DETAIL NUMBER

ELEVATION VIEW

Ref. DETAIL NUMBER


SHADE DESIGNATIONS

- BEAM OR DROP CAP
- WALLS OR COLUMNS
- CMU WALLS
- DELAY STRIP OR CLOSURE POUR
- GRADE OR SOIL
- 12" SLAB DEPRESSION


LINE DESIGNATIONS

- INDICATES TOP OF SLAB CHANGE OR EDGE OF SLAB
- INDICATES SOFFIT CHANGE
- INDICATES CONSTRUCTION JOINT
- INDICATES GRID LINE


THIS DRAWING IS FOR THE EXCLUSIVE USE OF MCCLONE CONSTRUCTION COMPANY, ON THIS PROJECT ONLY. UTILIZATION OF THIS DRAWING BY OTHER PARTIES AND/OR OTHER PROJECTS WITHOUT THE EXPRESSED WRITTEN CONSENT OF MCCLONE CONSTRUCTION COMPANY IS STRICTLY PROHIBITED.

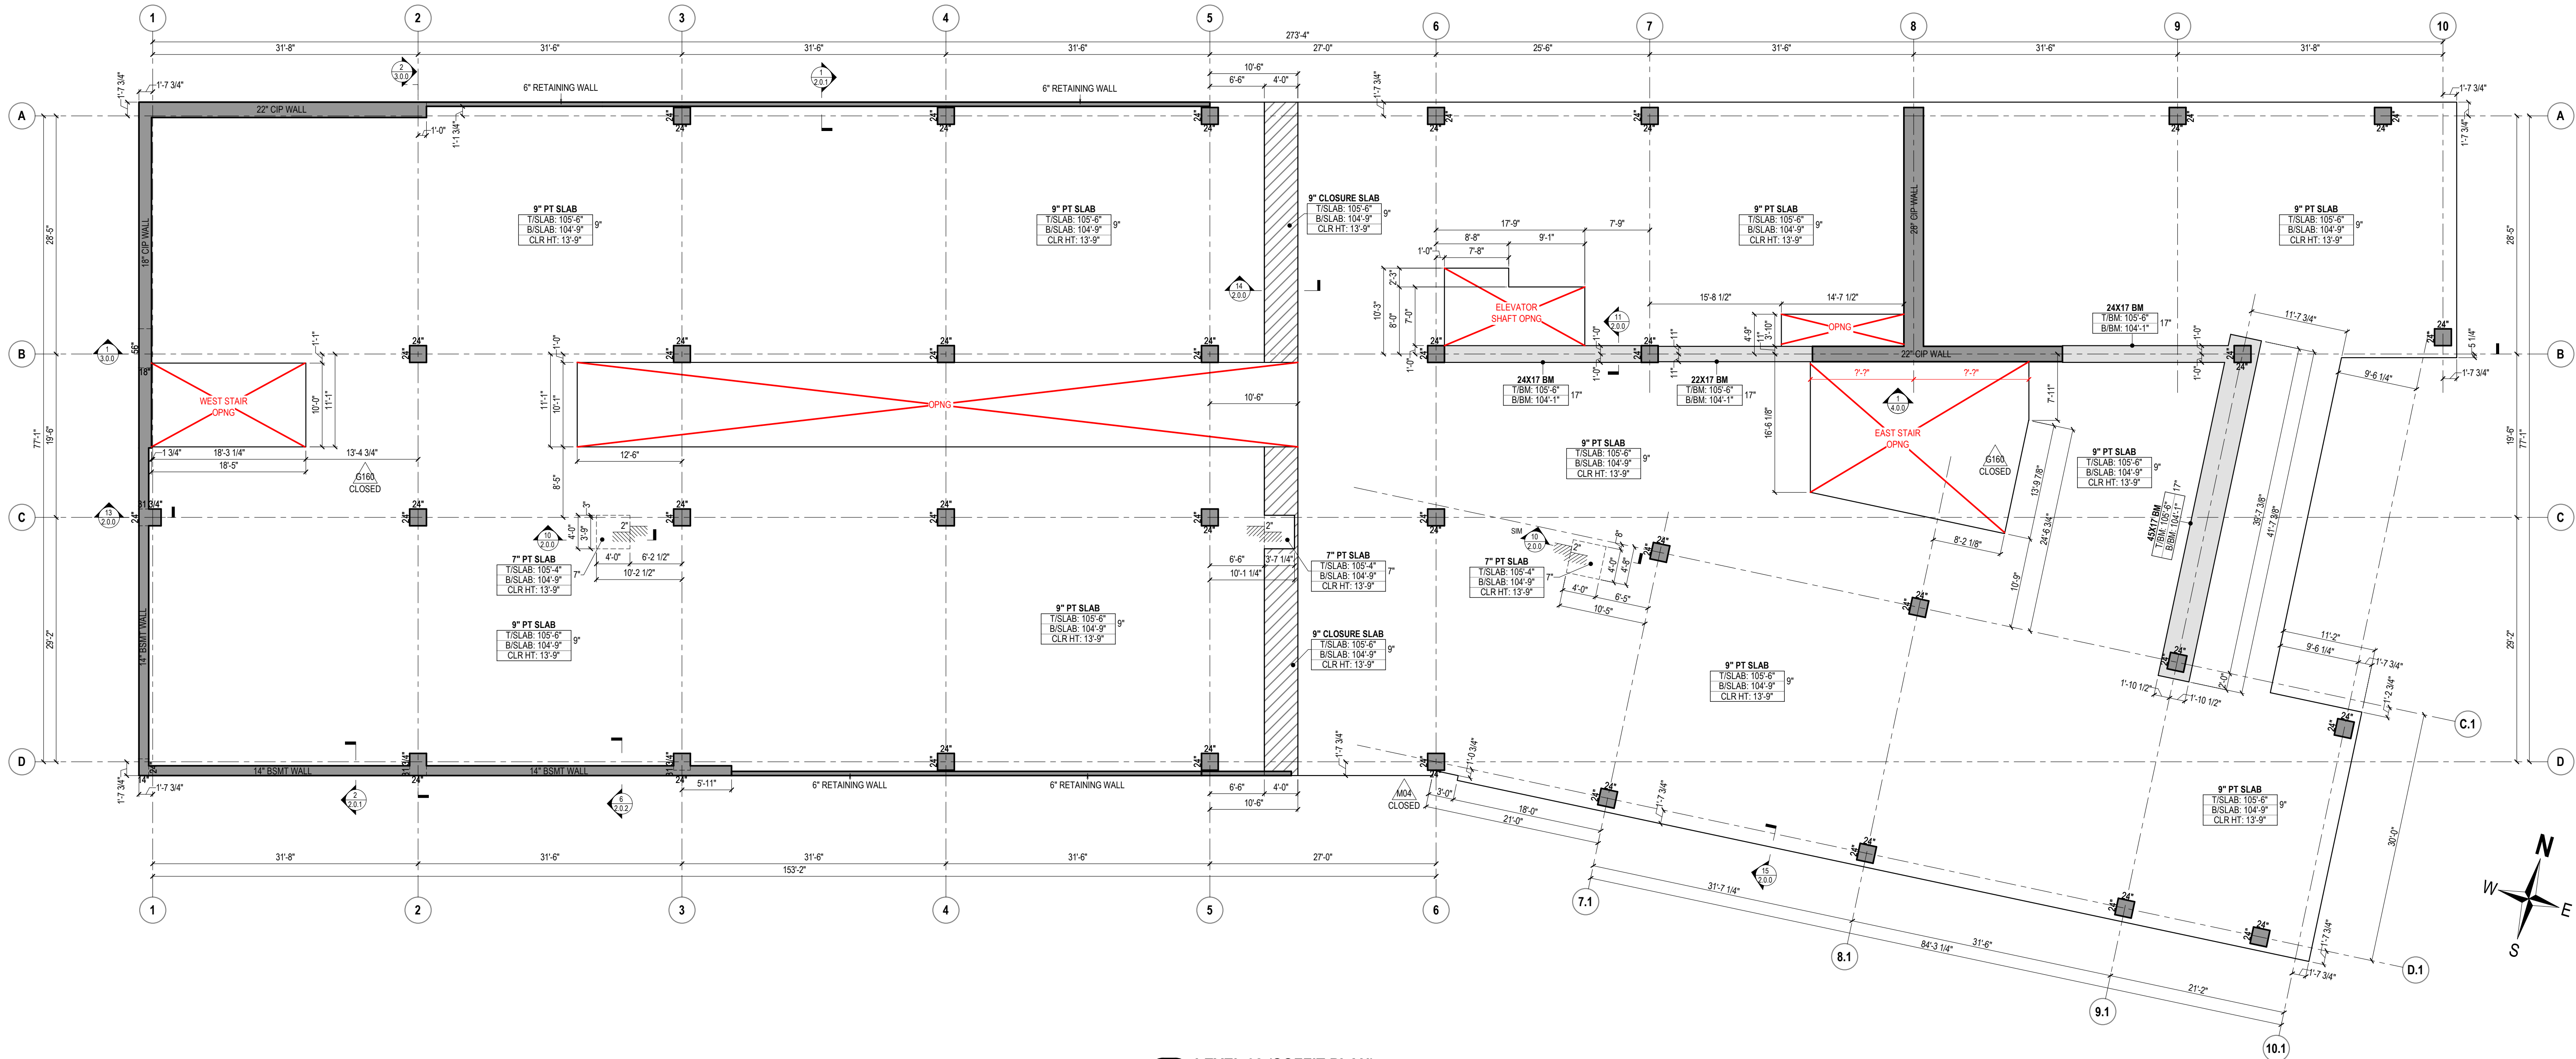


1 LEVEL 02 (SOFFIT PLAN)
REF: 2/1.1.0
1\"/>

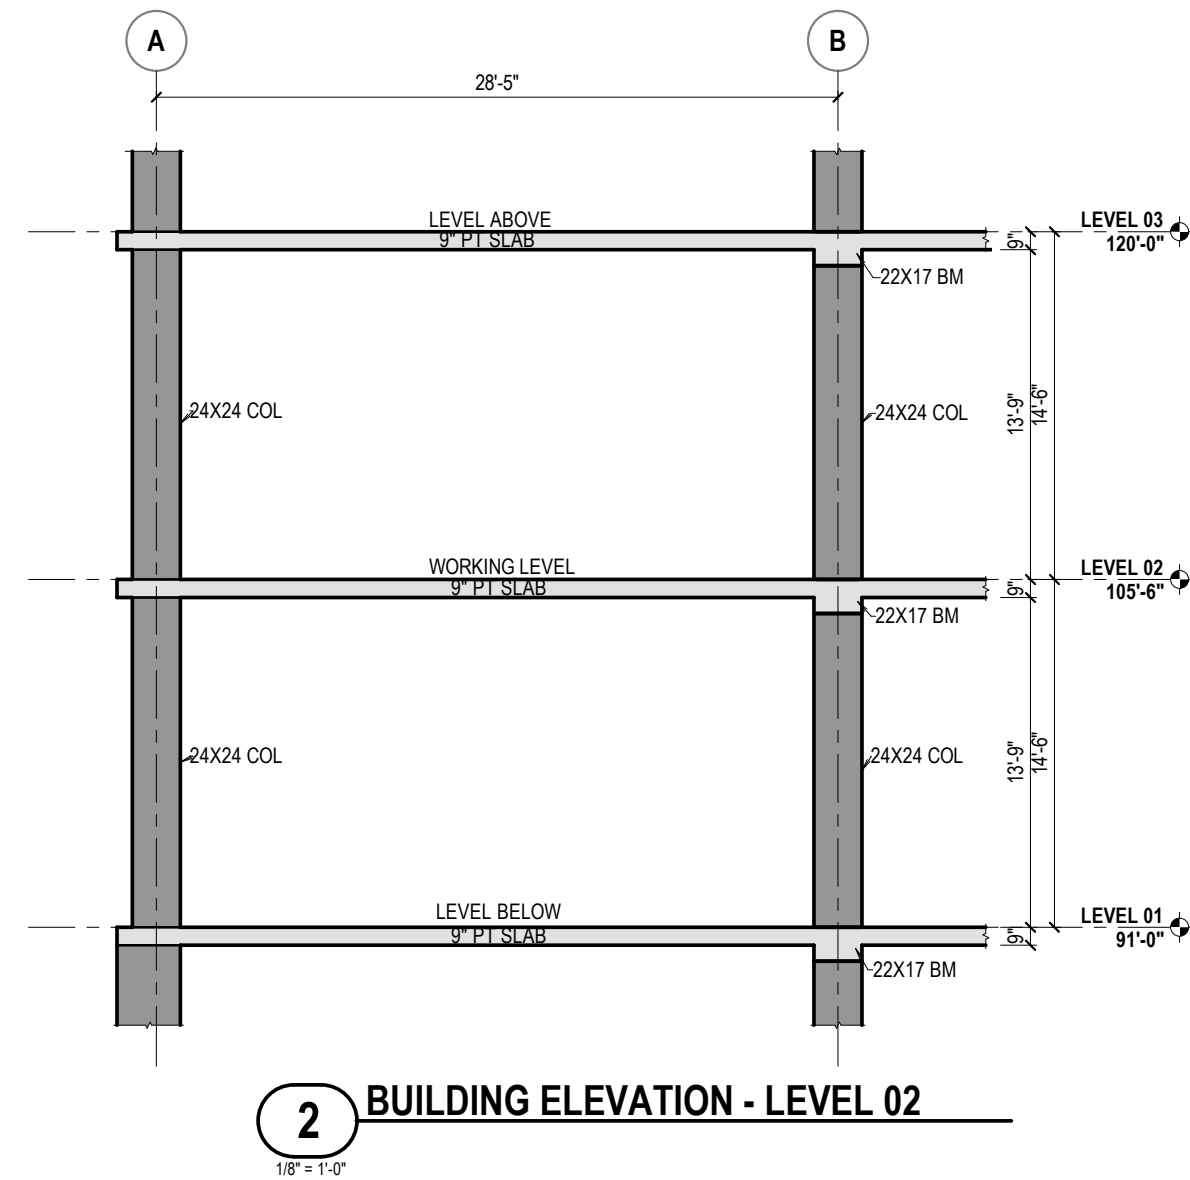

2 BUILDING ELEVATION - LEVEL 02
1/8\"/>

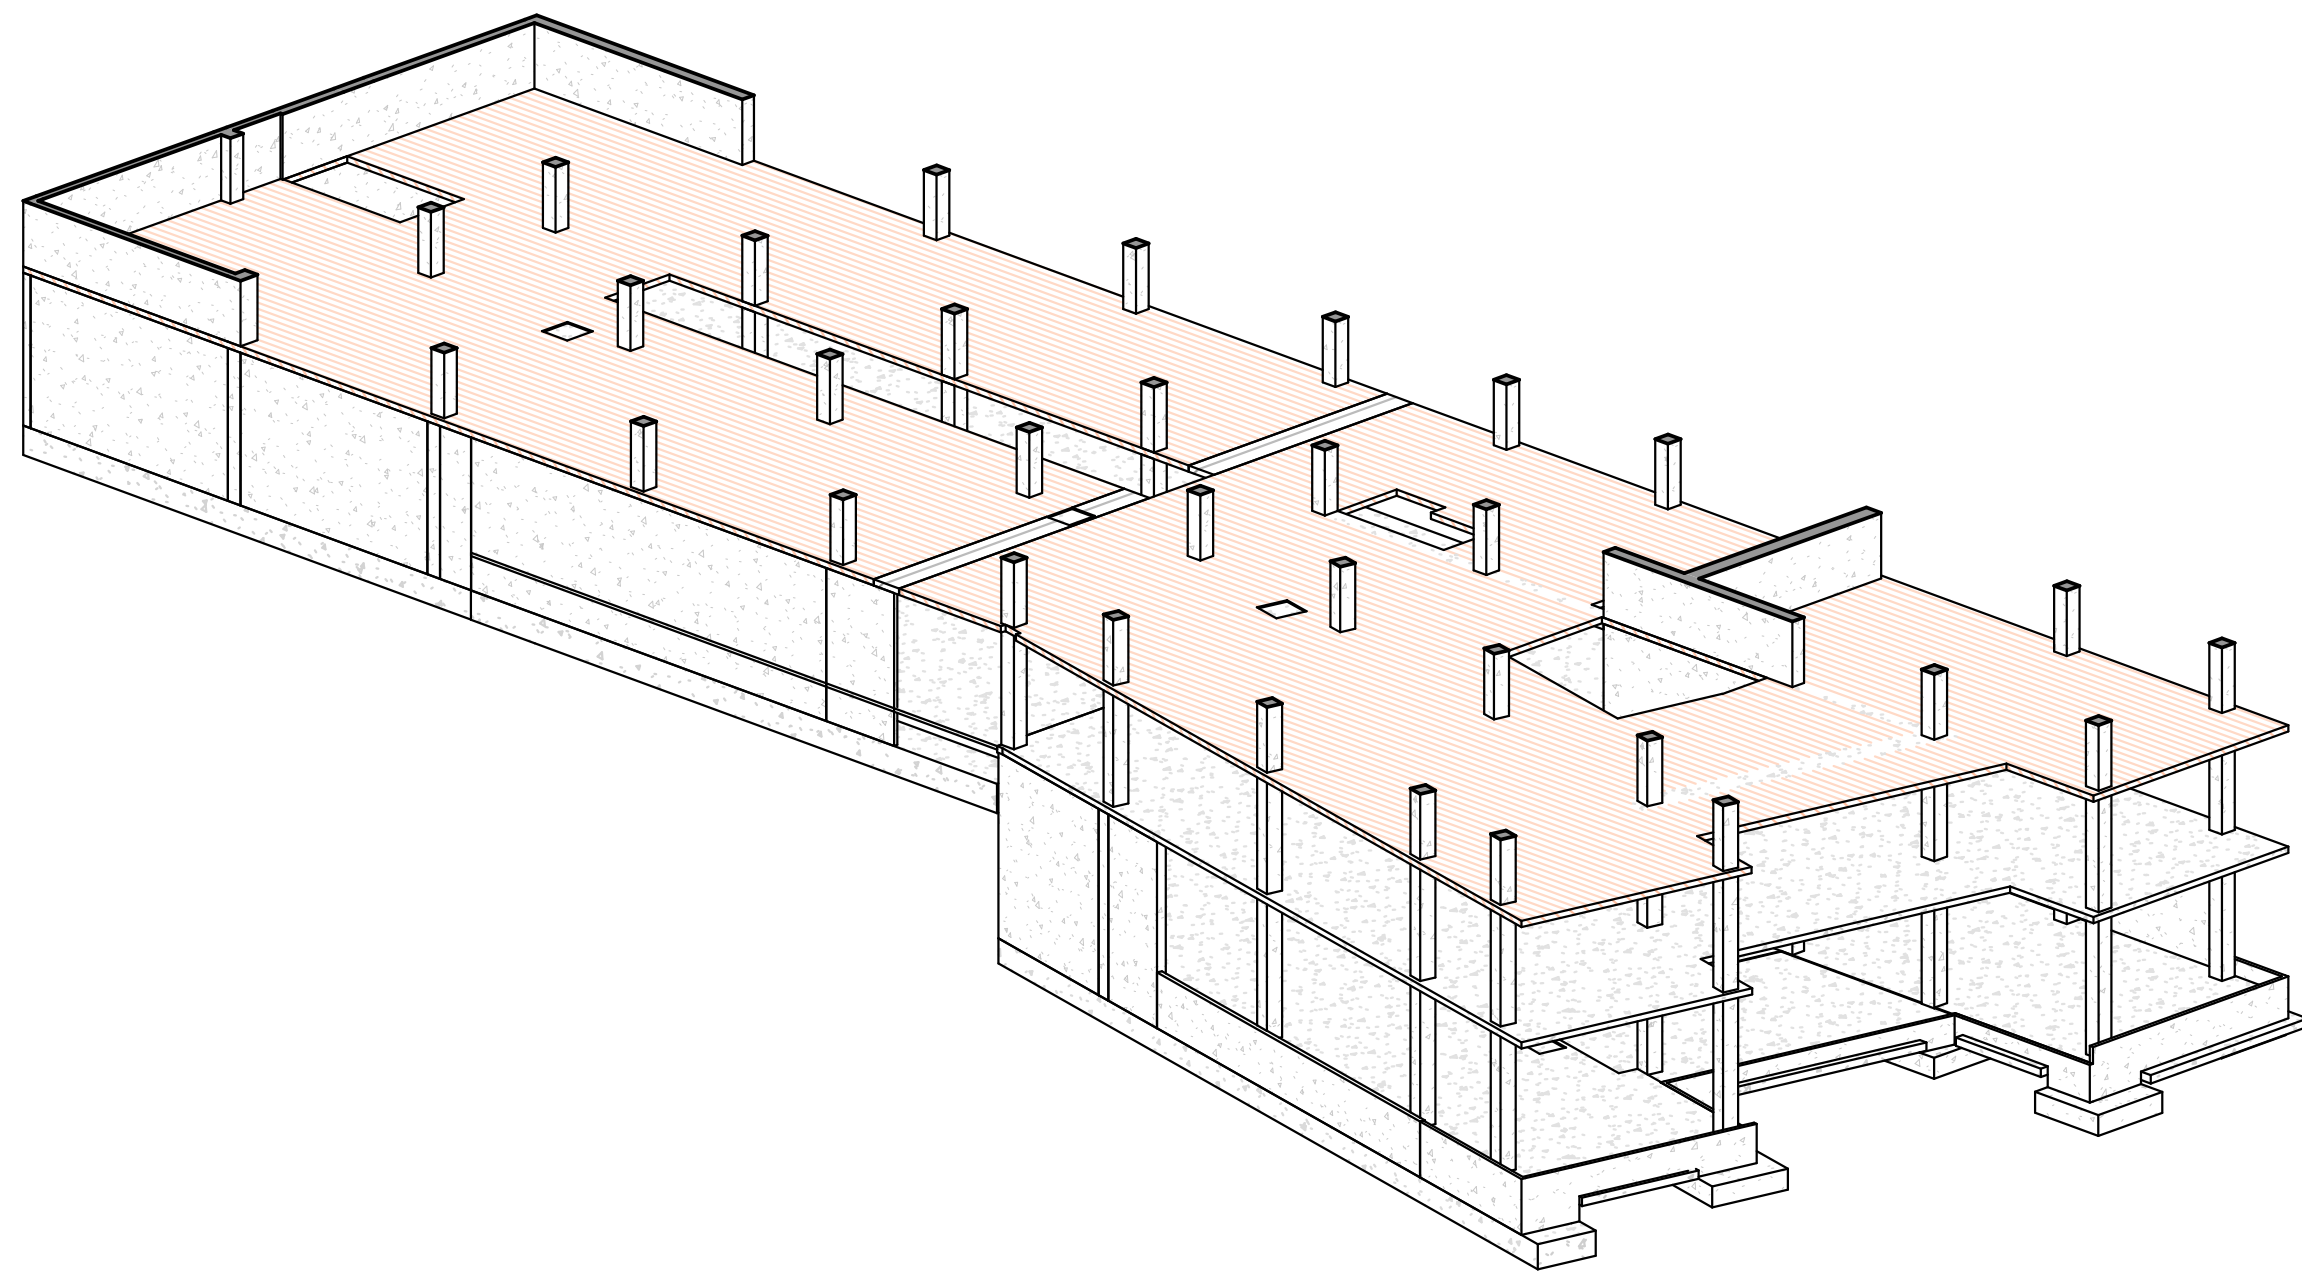

3 3D VIEW - LEVEL 02

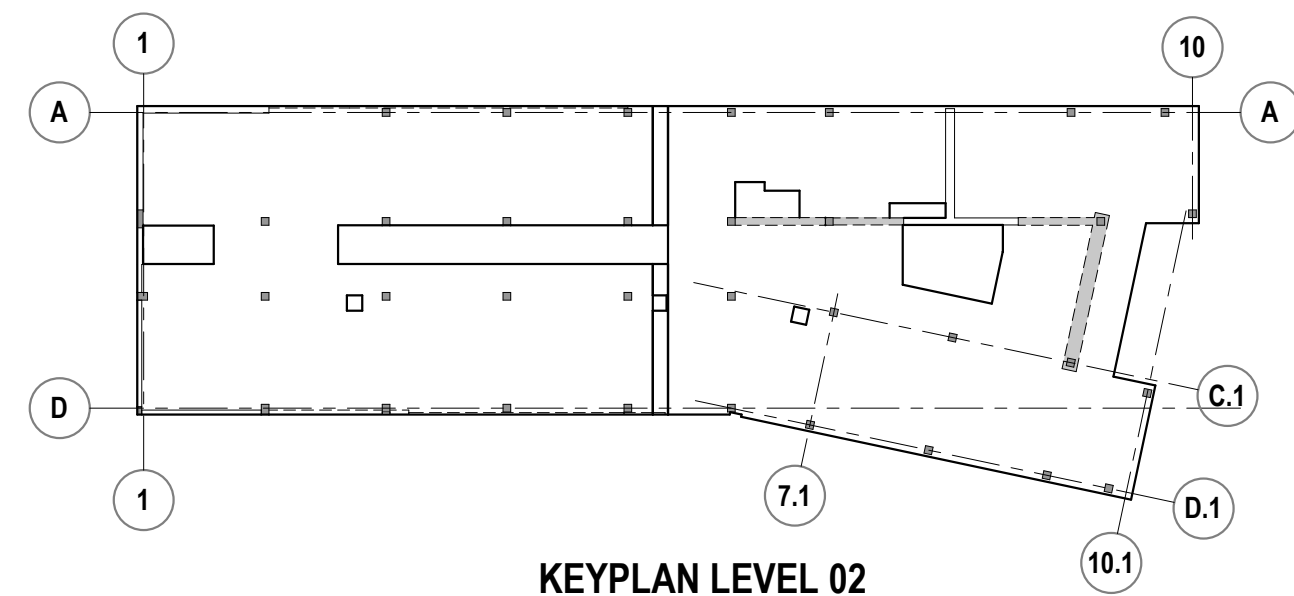

KEYPLAN LEVEL 02

NOTES:

- 3/4" CHAMFER ON ALL EXPOSED CONCRETE CORNERS TYP.
- ALL COLUMNS ARE CENTERED ON GRID LINES U.N.O.
- ALL BEAMS ARE CENTERED ON GRID LINES U.N.O.
- SLAB THICKNESS IS 9" TYP. U.N.O.
- DO NOT SCALE THIS DRAWING. USE DIMENSIONS PROVIDED.

LEGEND

SYMBOLS

- 1-BOX (ROUND-ENDS)
TOP OF CONCRETE ELEVATIONS
- 1-BOX
BOTTOM OF CONCRETE ELEVATIONS
- 2-BOX (PLAN VIEWS)
TOP & BOTTOM ELEVATIONS
D = DEPTH OF CONC. MEMBER
- 3-BOX (SOFFIT PLANS)
TOP & BOTTOM ELEVATIONS
HEIGHT BELOW REFERENCE LEVEL
D = DEPTH OF CONC. MEMBER

SECTION VIEW

SHEET NUMBER

ELEVATION VIEW

SHEET NUMBER

SHADE DESIGNATIONS

- BEAM OR DROP CAP
- WALLS OR COLUMNS
- CMU WALLS
- DELAY STRIP OR CLOSURE POUR
- GRADE OR SOIL
- 1/2" SLAB DEPRESSION

LINE DESIGNATIONS

- INDICATES TOP OF SLAB CHANGE OR EDGE OF SLAB
- INDICATES SOFFIT CHANGE
- INDICATES CONSTRUCTION JOINT
- INDICATES GRID LINE

McCLONE
CONSTRUCTION | SINCE 1975

WASHINGTON OFFICE
28810 MAPLE VALLEY, WA 98038
MAPLE VALLEY, WA 98038 | 425-143-1440


LEVEL-02 (SOFFIT PLAN)

1175 - Bothell STEM 4

BOITTEL, WA 98011


SHEET NO. DATE
06/21/2022
SCALE
As indicated
DRAWN BY
DALVAREZ
1175
1.2.0

THIS DRAWING IS FOR THE EXCLUSIVE USE OF MCCLONE CONSTRUCTION COMPANY. ON THIS PROJECT ONLY. UTILIZATION OF THIS DRAWING BY OTHER PARTIES AND/OR ON OTHER PROJECTS WITHOUT THE EXPRESSED WRITTEN CONSENT OF MCCLONE CONSTRUCTION COMPANY IS STRICTLY PROHIBITED.

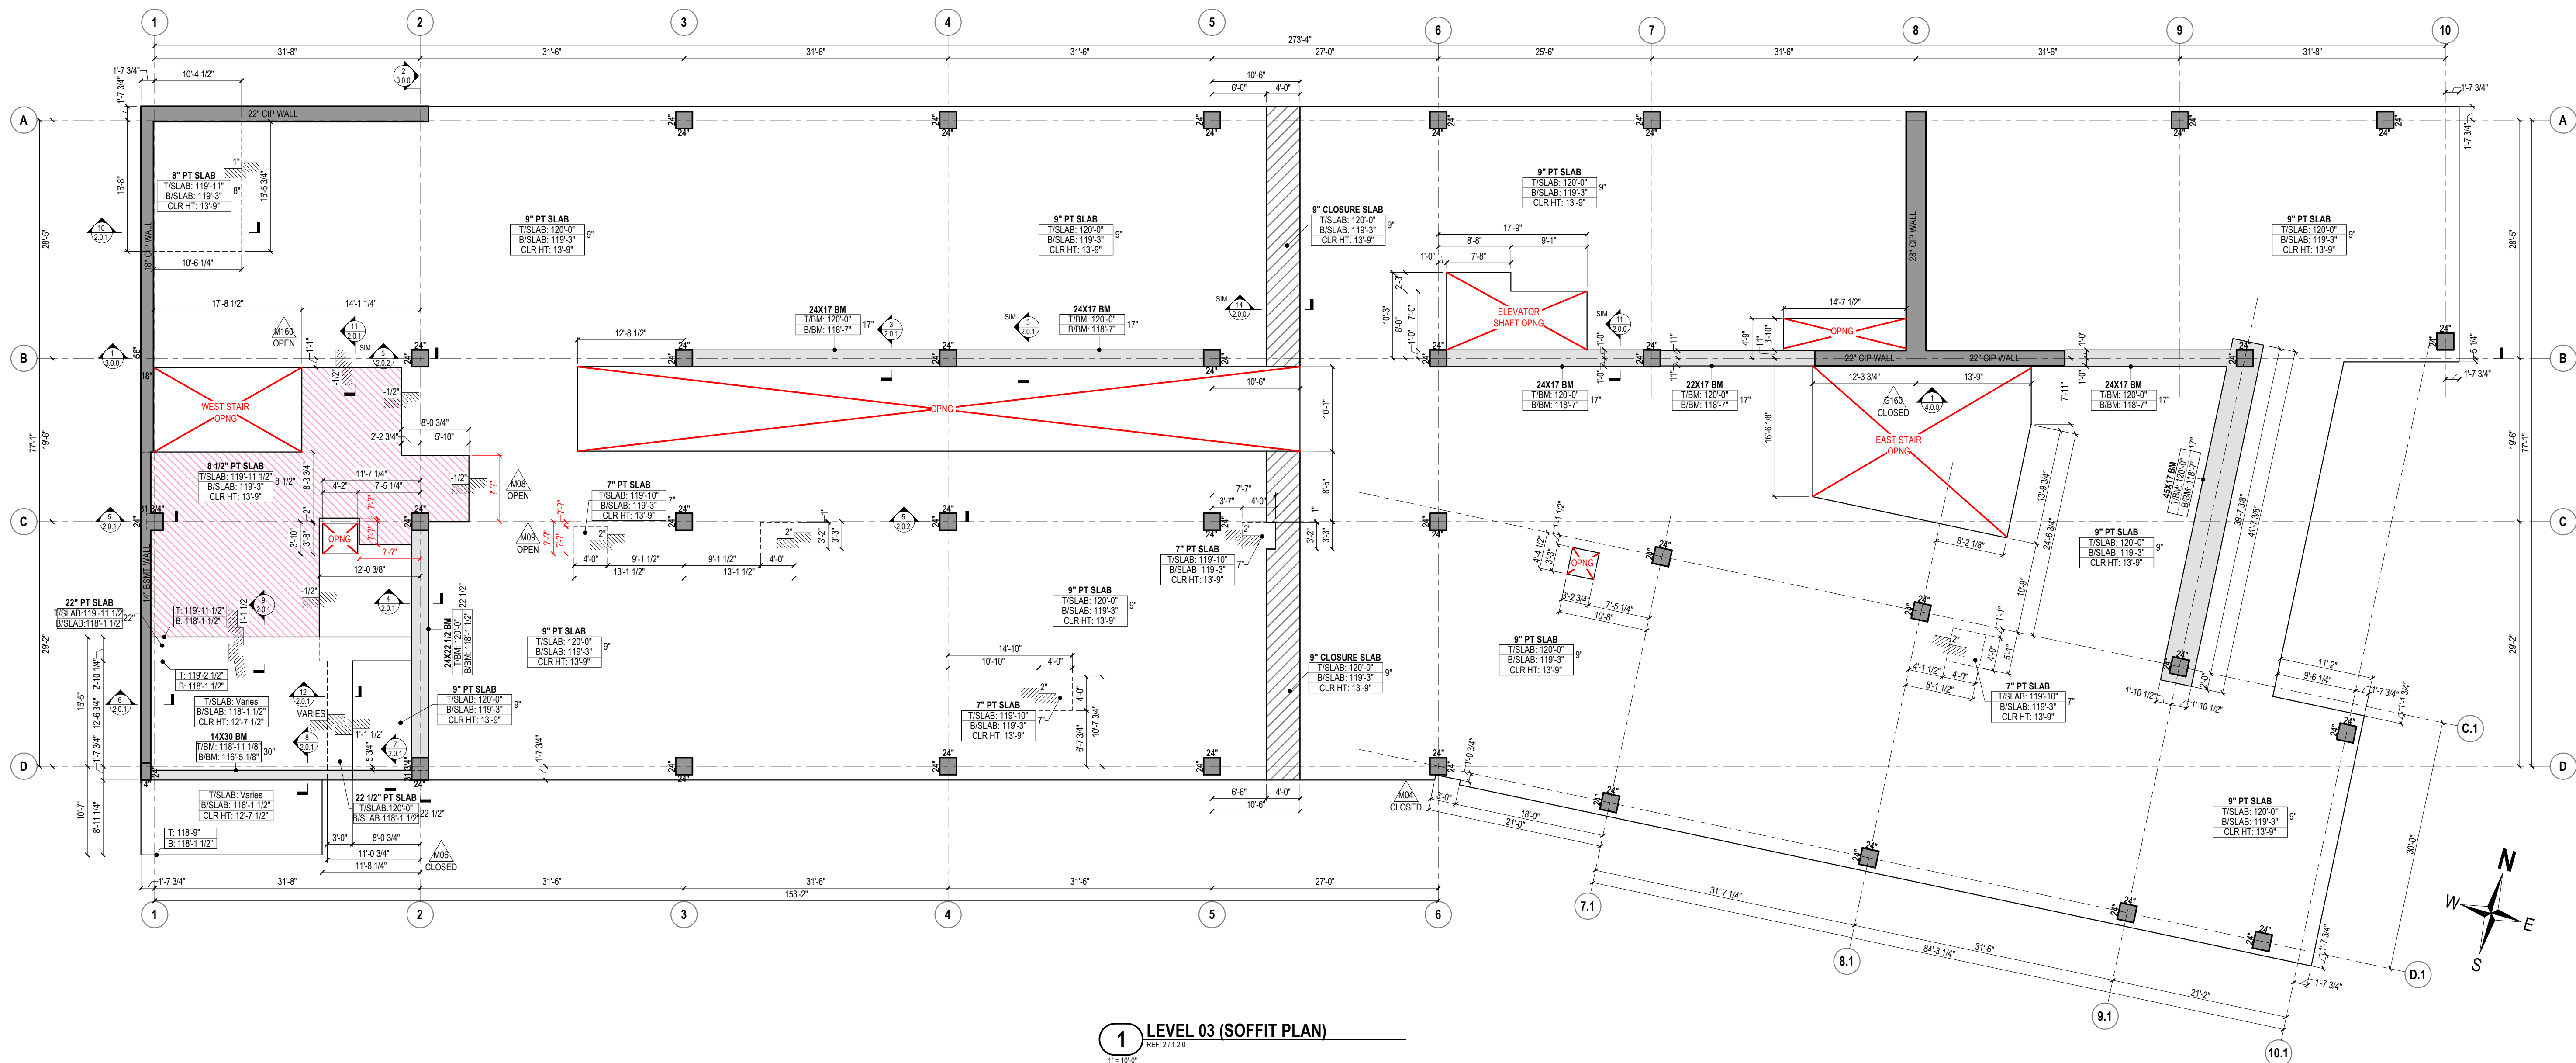


1 LEVEL 03 (SOFFIT PLAN)

1" = 10'-0"

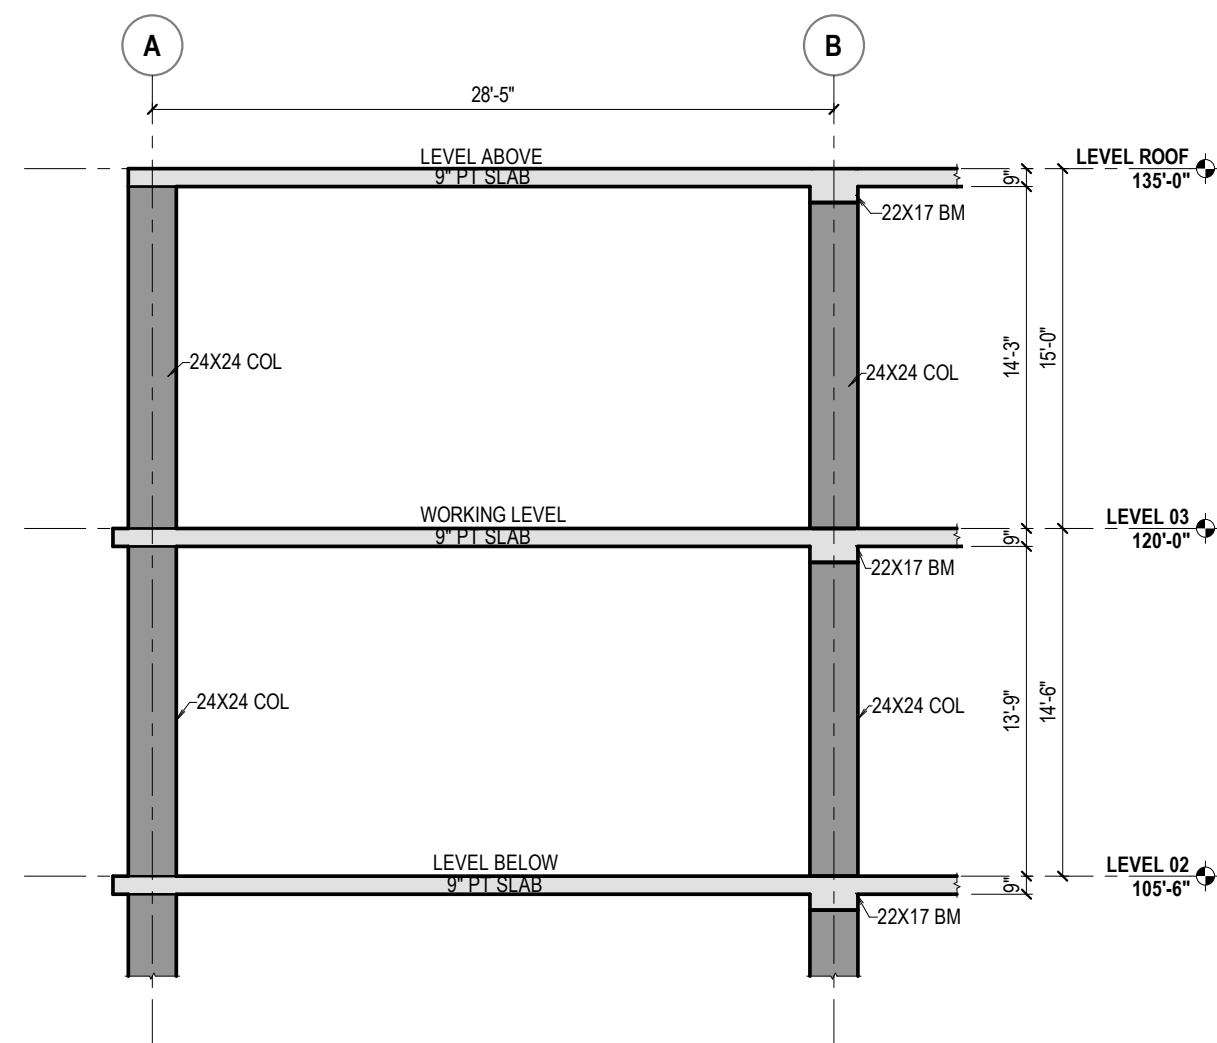


2 BUILDING ELEVATION - LEVEL 03

1/8" = 1'-0"

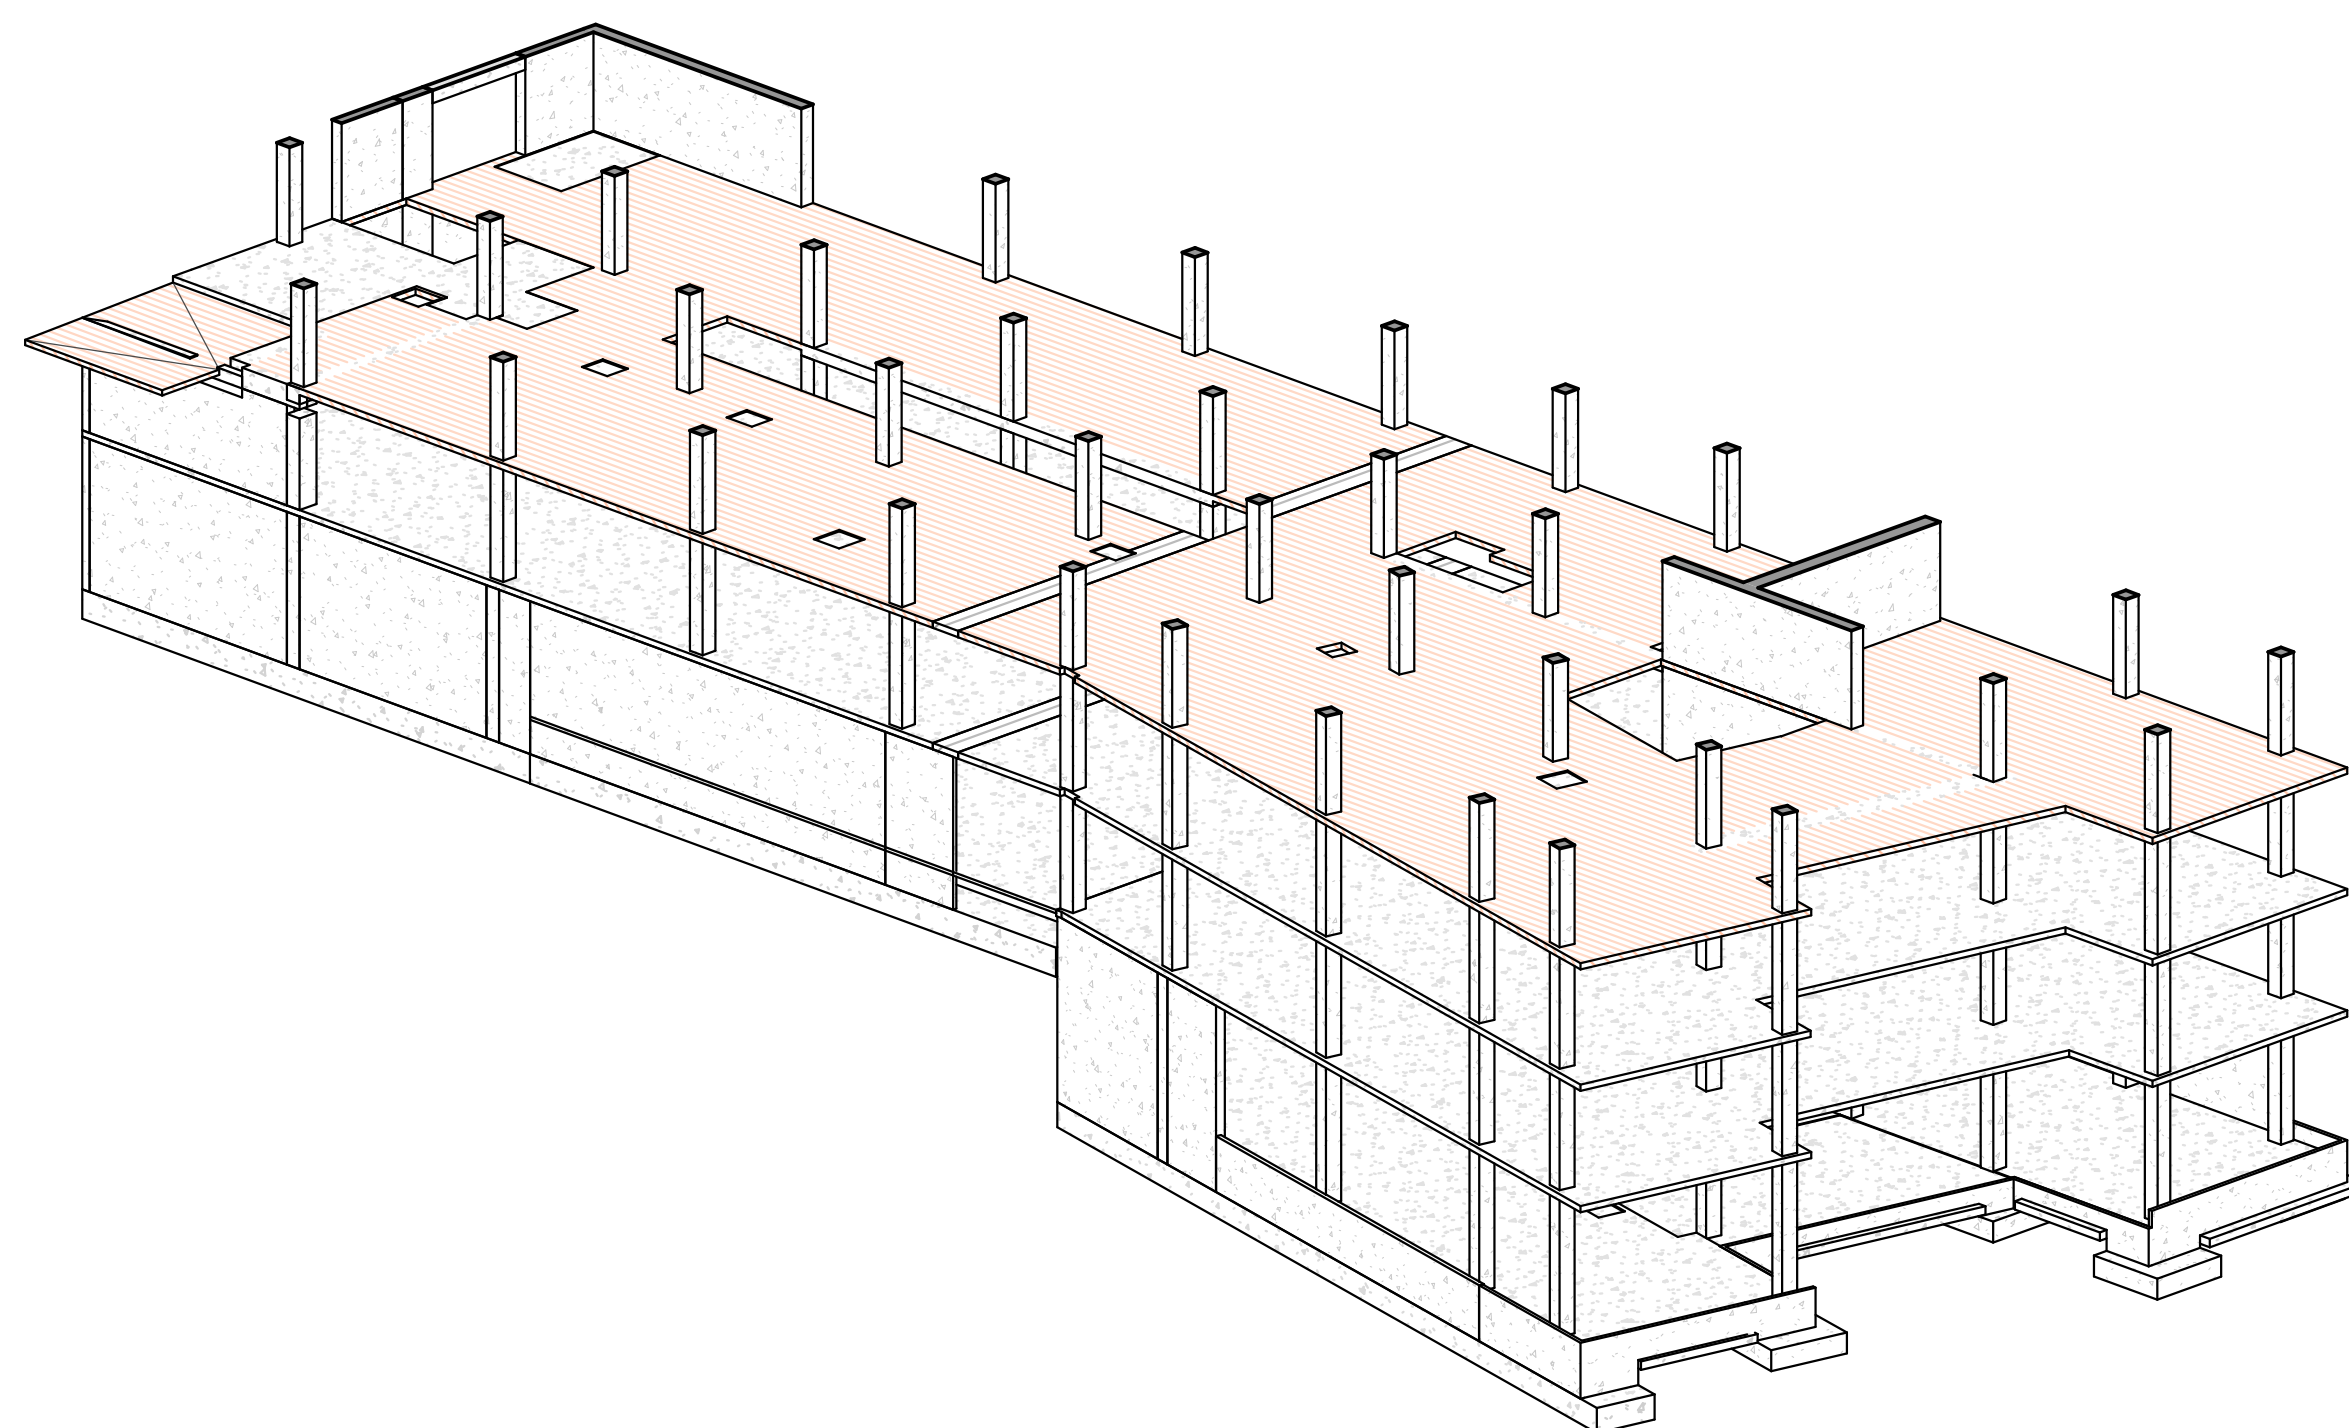

3 3D VIEW - LEVEL 03

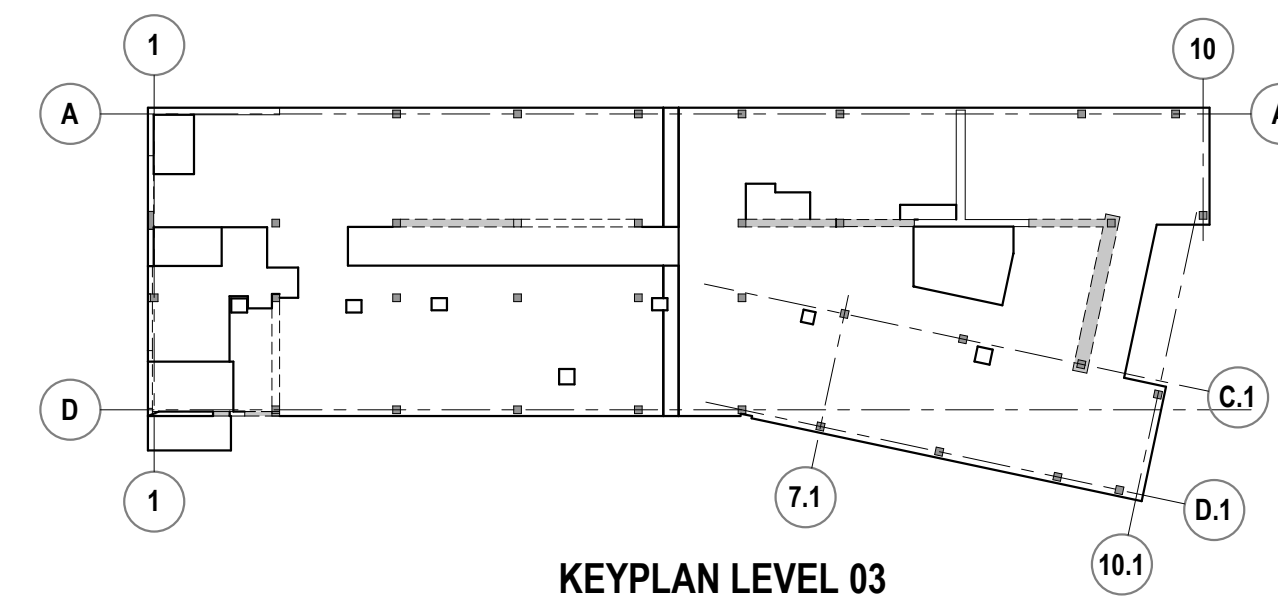

KEYPLAN LEVEL 03

NOTES:

- 3/4" CHAMFER ON ALL EXPOSED CONCRETE CORNERS TYP.
- ALL COLUMNS ARE CENTERED ON GRID LINES U.N.O.
- ALL BEAMS ARE CENTERED ON GRID LINES U.N.O.
- SLAB THICKNESS IS 9" TYP. U.N.O.
- DO NOT SCALE THIS DRAWING. USE DIMENSIONS PROVIDED.

LEGEND

SYMBOLS

- 1-BOX (ROUND-ENDS)
TOP OF CONCRETE ELEVATIONS
- 1-BOX
BOTTOM OF CONCRETE ELEVATIONS
- 2-BOX (PLAN VIEWS)
TOP & BOTTOM ELEVATIONS
D = DEPTH OF CONC. MEMBER
- 3-BOX (SOFFIT PLANS)
TOP & BOTTOM ELEVATIONS
HEIGHT BELOW REFERENCE LEVEL
D = DEPTH OF CONC. MEMBER

- SECTION VIEW
SHEET NUMBER
ELEVATION VIEW
SHEET NUMBER
- DETAIL NUMBER
DETAIL NUMBER





SHADE DESIGNATIONS

- BEAM OR DROP CAP
- WALLS OR COLUMNS
- CMU WALLS
- DELAY STRIP OR CLOSURE POUR
- GRADE OR SOIL
- 1/2" SLAB DEPRESSION

LINE DESIGNATIONS

- INDICATES TOP OF SLAB CHANGE OR EDGE OF SLAB
- INDICATES SOFFIT CHANGE
- INDICATES CONSTRUCTION JOINT
- INDICATES GRID LINE

THIS DRAWING IS FOR THE EXCLUSIVE USE OF MCCLONE CONSTRUCTION COMPANY. ON THIS PROJECT ONLY. UTILIZATION OF THIS DRAWING BY OTHER PARTIES AND/OR ON OTHER PROJECTS WITHOUT THE EXPRESSED WRITTEN CONSENT OF MCCLONE CONSTRUCTION COMPANY IS STRICTLY PROHIBITED.

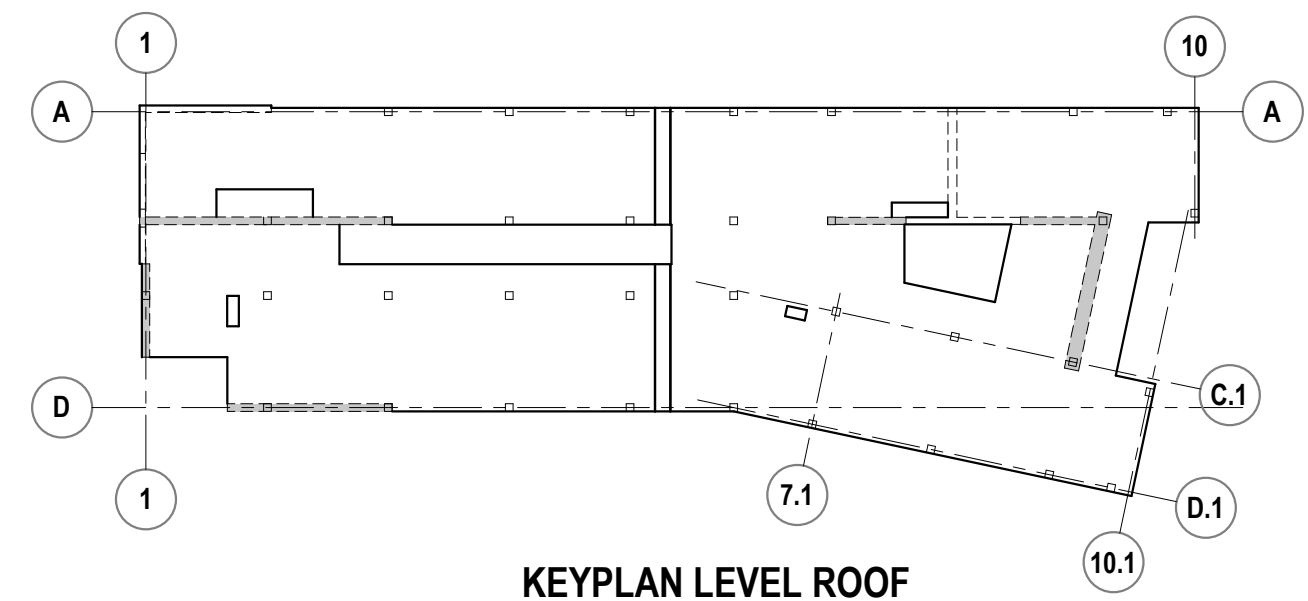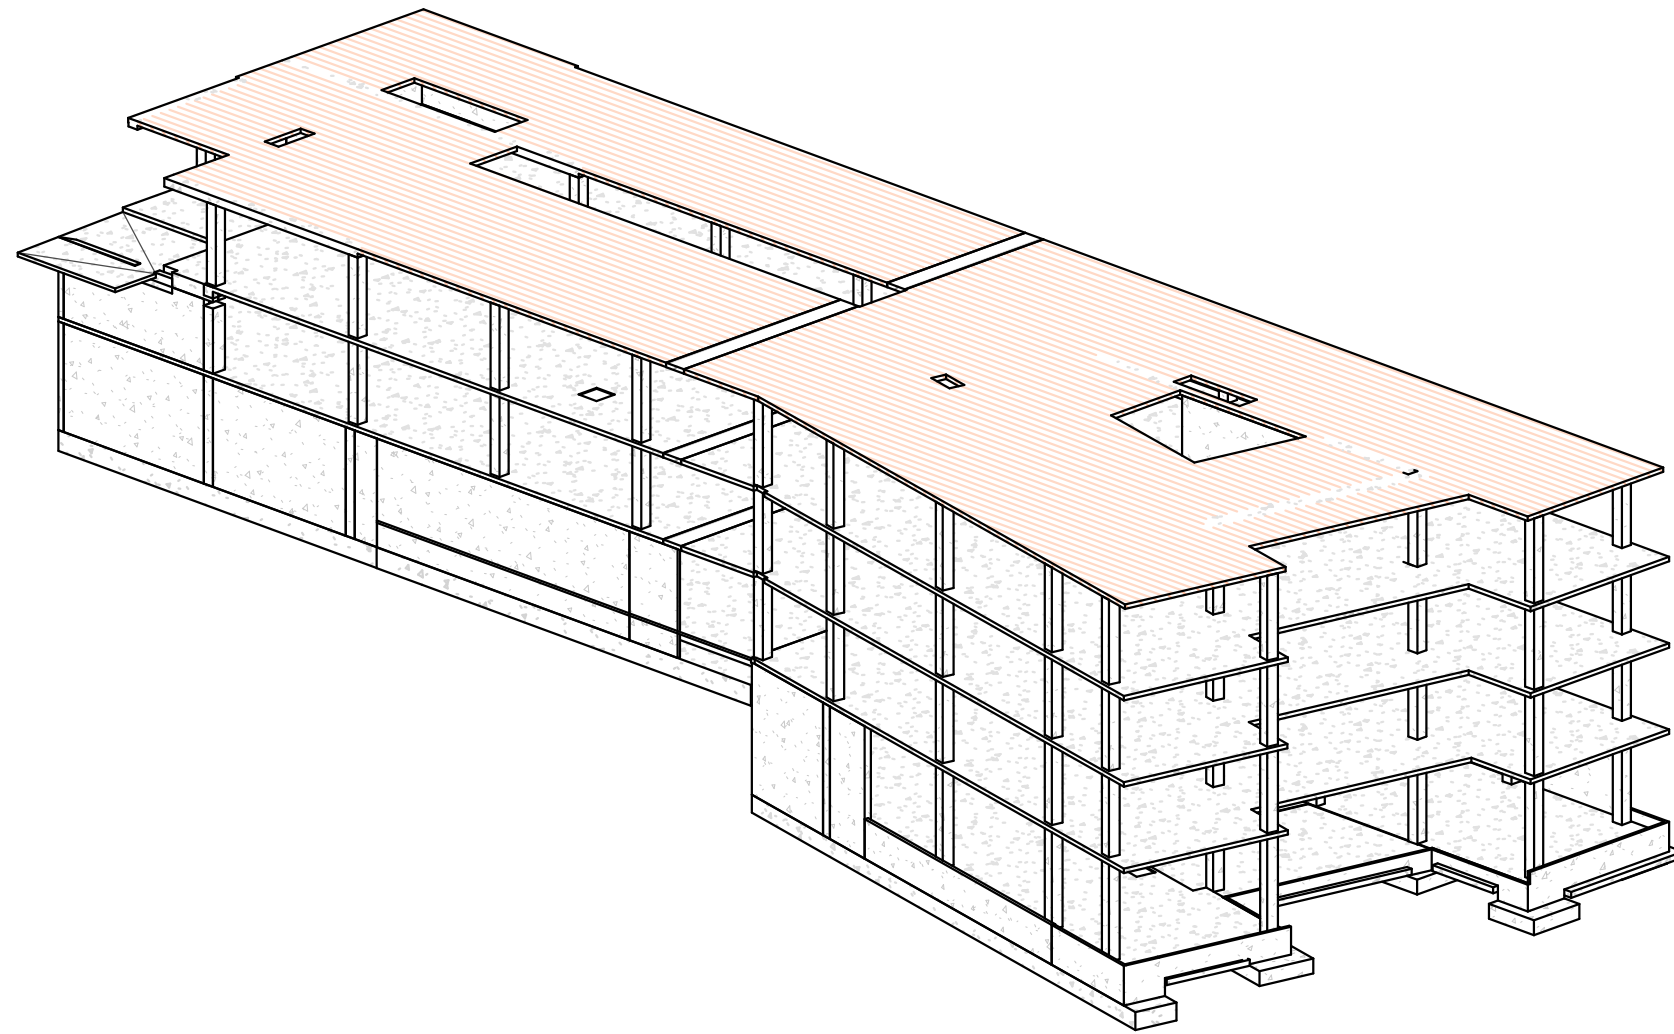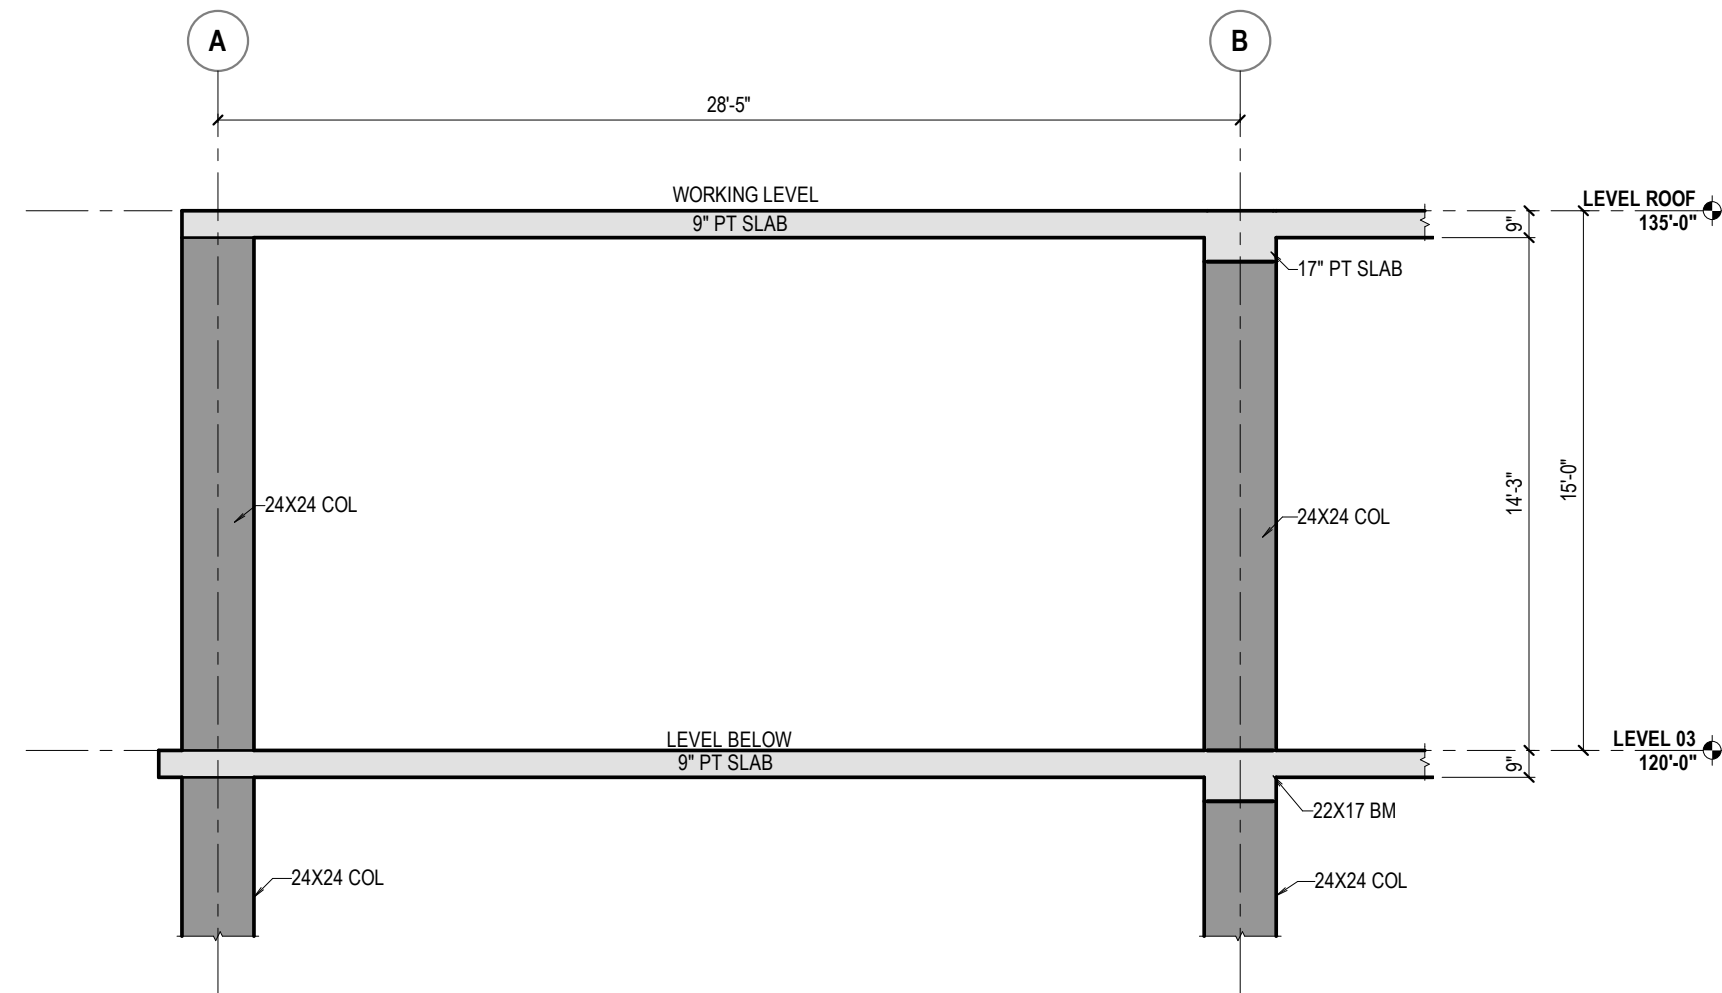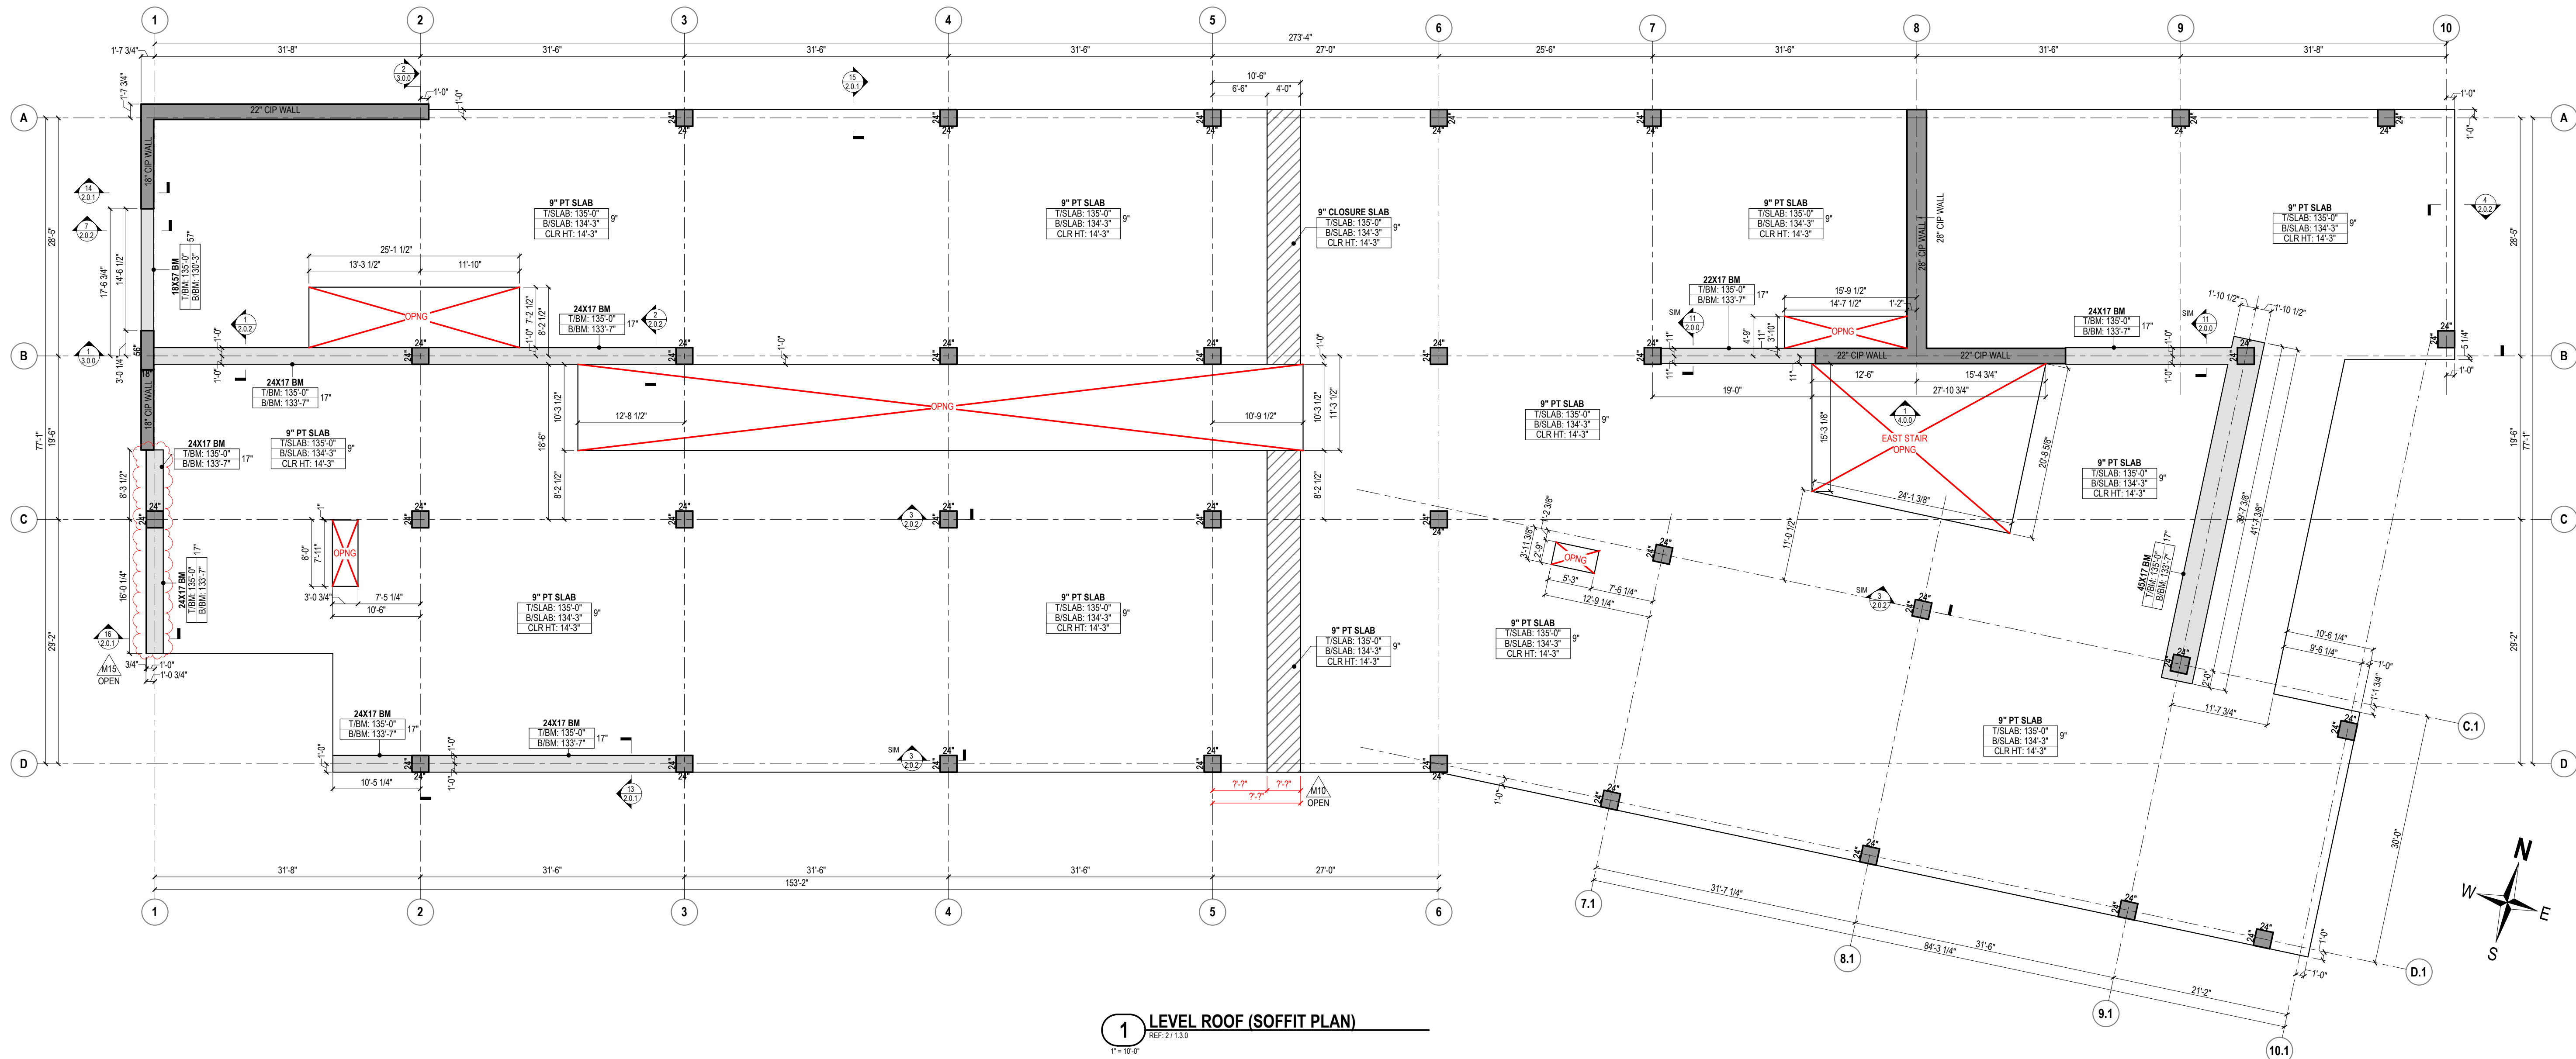

NOTES:

- 3/4\"/>
- ALL COLUMNS ARE CENTERED ON GRID LINES U.N.O.
- ALL BEAMS ARE CENTERED ON GRID LINES U.N.O.
- SLAB THICKNESS IS 9\"/>
- DO NOT SCALE THIS DRAWING. USE DIMENSIONS PROVIDED.

LEGEND

SYMBOLS

- 1-BOX (ROUND-ENDS)
TOP OF CONCRETE ELEVATIONS
- 1-BOX
BOTTOM OF CONCRETE ELEVATIONS
- 2-BOX (PLAN VIEWS)
TOP & BOTTOM ELEVATIONS
D = DEPTH OF CONC. MEMBER
- 3-BOX (SOFFIT PLANS)
TOP & BOTTOM ELEVATIONS
HEIGHT BELOW REFERENCE LEVEL
D = DEPTH OF CONC. MEMBER

SECTION VIEW

Ref. DETAIL NUMBER

SHEET NUMBER

ELEVATION VIEW

SHEET NUMBER



SHADE DESIGNATIONS

- BEAM OR DROP CAP
- WALLS OR COLUMNS
- CMU WALLS
- DELAY STRIP OR CLOSURE POUR
- GRADE OR SOIL
- 12\"/>

LINE DESIGNATIONS

- INDICATES TOP OF SLAB CHANGE OR EDGE OF SLAB
- INDICATES SOFFIT CHANGE
- INDICATES CONSTRUCTION JOINT
- INDICATES GRID LINE

THIS DRAWING IS FOR THE EXCLUSIVE USE OF McCLONE CONSTRUCTION COMPANY, ON THIS PROJECT ONLY. UTILIZATION OF THIS DRAWING BY OTHER PARTIES AND/OR ON OTHER PROJECTS WITHOUT THE EXPRESSED WRITTEN CONSENT OF McCLONE CONSTRUCTION COMPANY IS STRICTLY PROHIBITED.

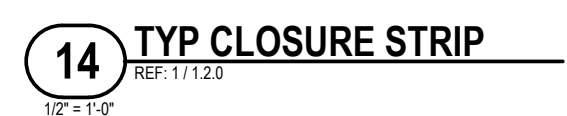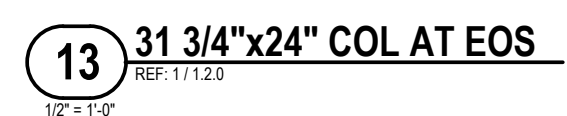


SECTIONS AND DETAILS

1175 - Bothell STEM 4
BOTTEL, WA, 98011


SHEET ISSUE DATE	06/21/2022	
SHEET ISSUED FOR	SUBMITTAL	
SCALE	As indicated	
DRAWN BY	DALVAREZ	
JOB	1175	
SHEET	2.0.0	
SHEET GIVEN		

24X36 ORIGINAL SHEET SIZE


THIS DRAWING IS FOR THE EXCLUSIVE USE OF MCCLONE CONSTRUCTION COMPANY, ON THIS PROJECT ONLY. UTILIZATION OF THIS DRAWING BY OTHER PARTIES AND/OR ON OTHER PROJECTS WITHOUT THE EXPRESSED WRITTEN CONSENT OF MCCLONE CONSTRUCTION COMPANY IS STRICTLY PROHIBITED.

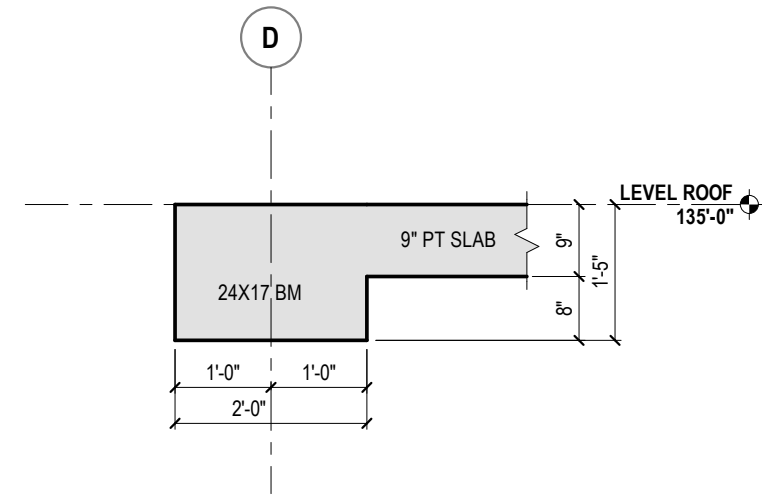


13 24"x17" BEAM AT EDGE
REF: 1/1/140
1/2" = 1'-0"

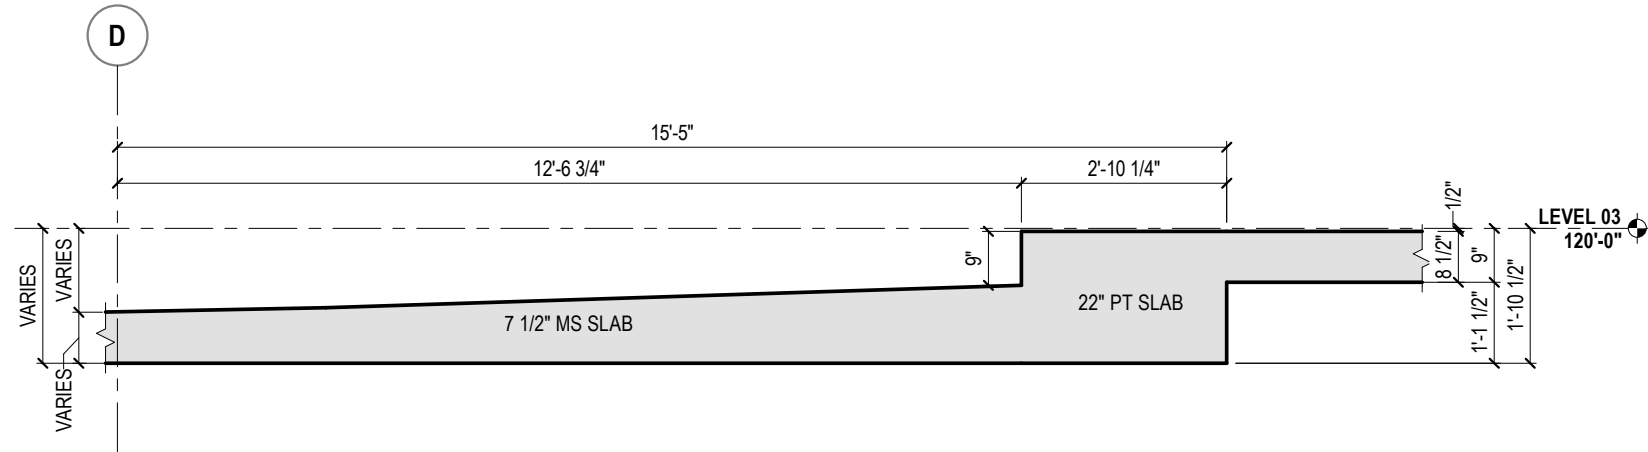


9 THICKENED SLAB AT SLAB STEP
REF: 1/1/130
3/8" = 1'-0"

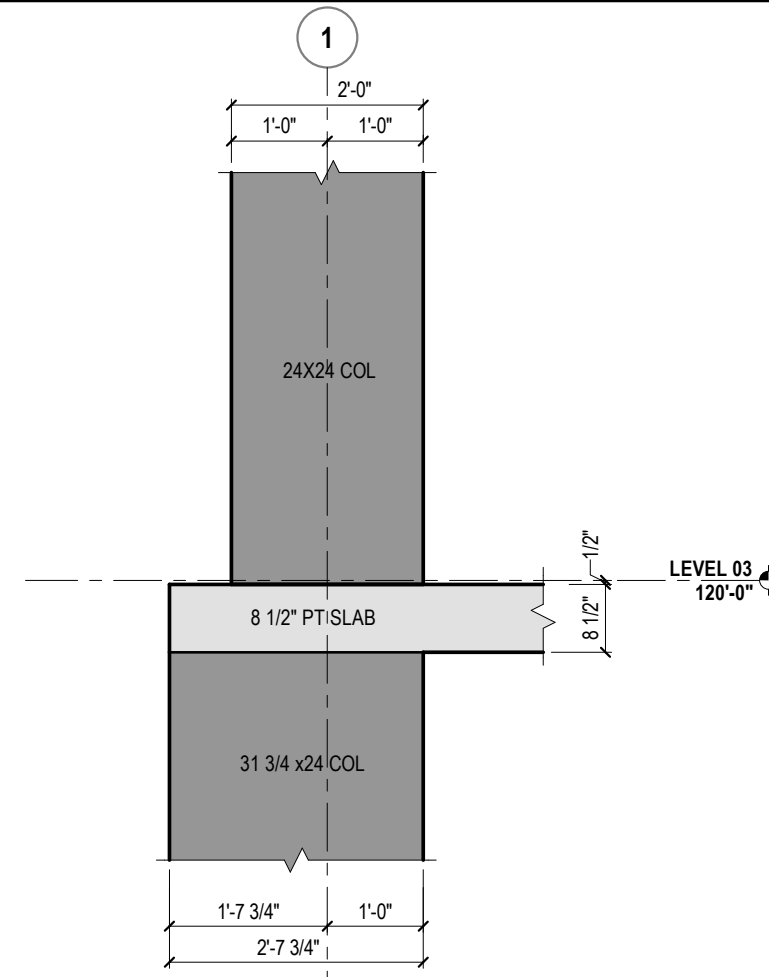


5 COLUMN TRANSITION
REF: 1/1/130
1/2" = 1'-0"

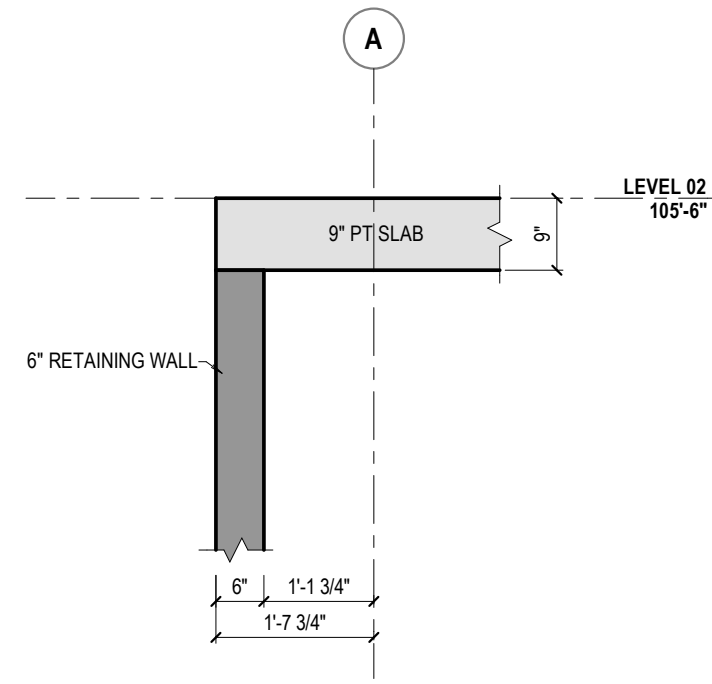


1 EOS AT RETAINING WALL LEVEL 02
REF: 1/1/120
1/2" = 1'-0"

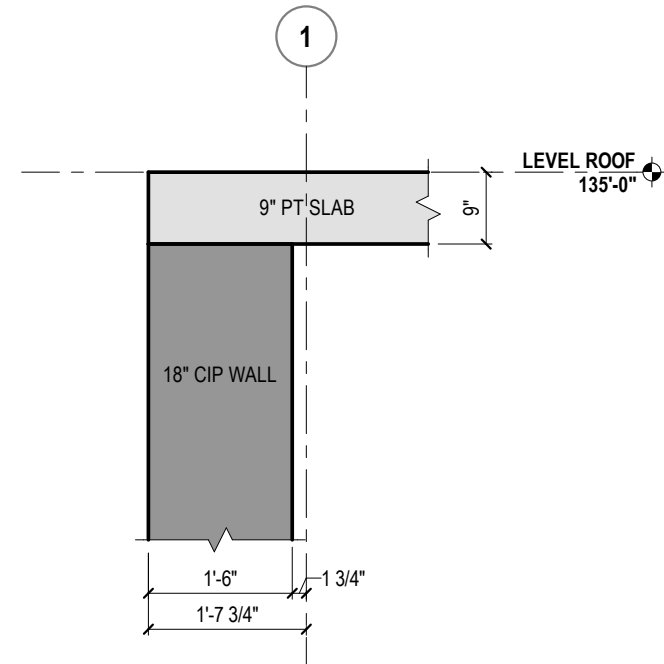


14 EOS LEVEL ROOF
REF: 1/1/140
1/2" = 1'-0"

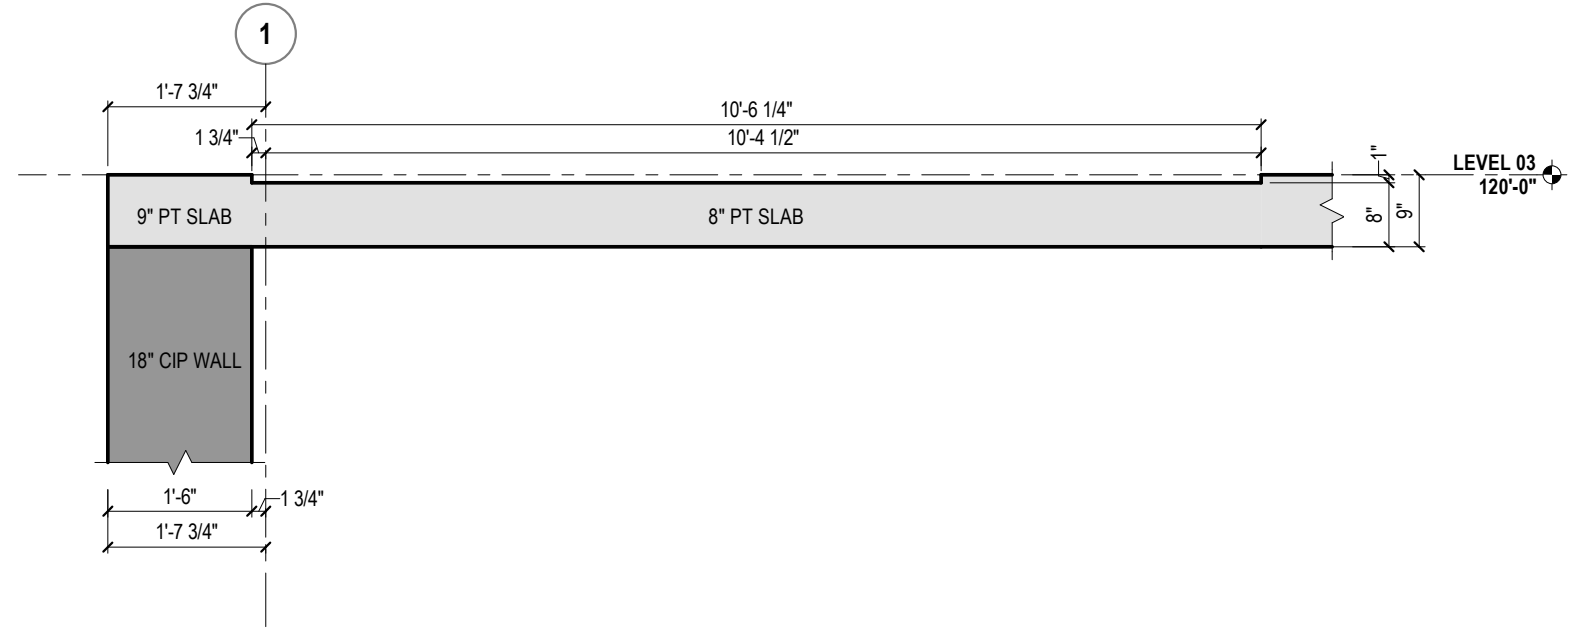


10 1" SLAB DEPRESSION AT EOS
REF: 1/1/130
1/2" = 1'-0"

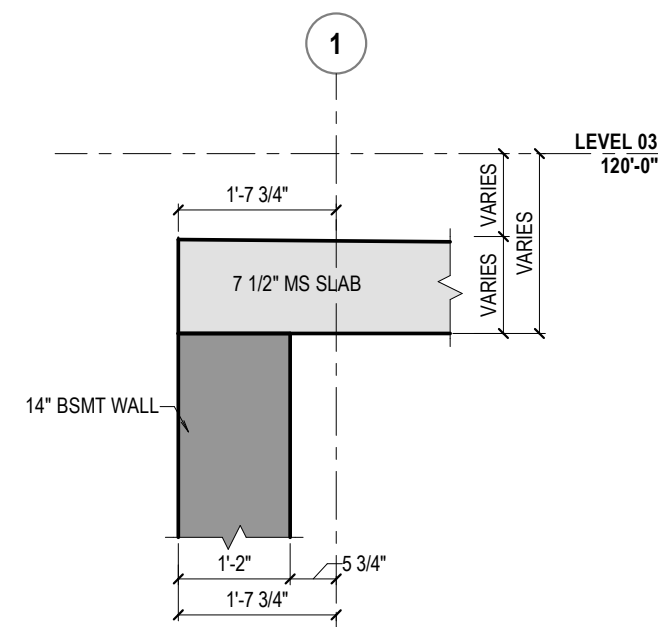


6 MILD-REINFORCED SLAB AT SIDEWALK INTRFACE
REF: 1/1/130
1/2" = 1'-0"

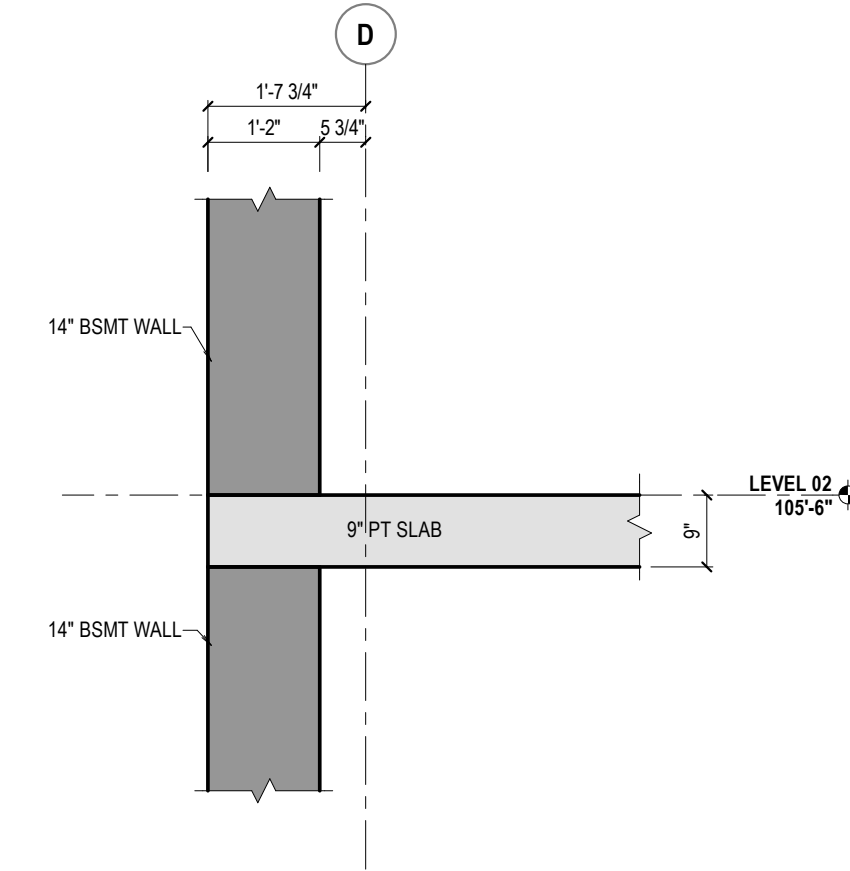


2 EOS AT BSMT WALL
REF: 1/1/120
1/2" = 1'-0"

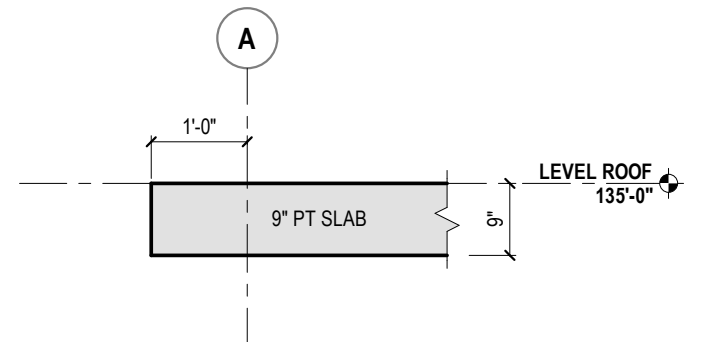


15 SLAB EDGE AT ROOF LEVEL
REF: 1/1/140
1/2" = 1'-0"

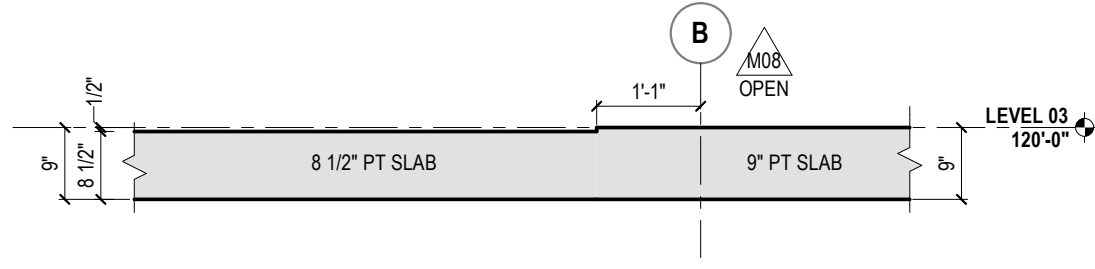


11 1/2" SLAB DEPRESSION
REF: 1/1/130
1/2" = 1'-0"

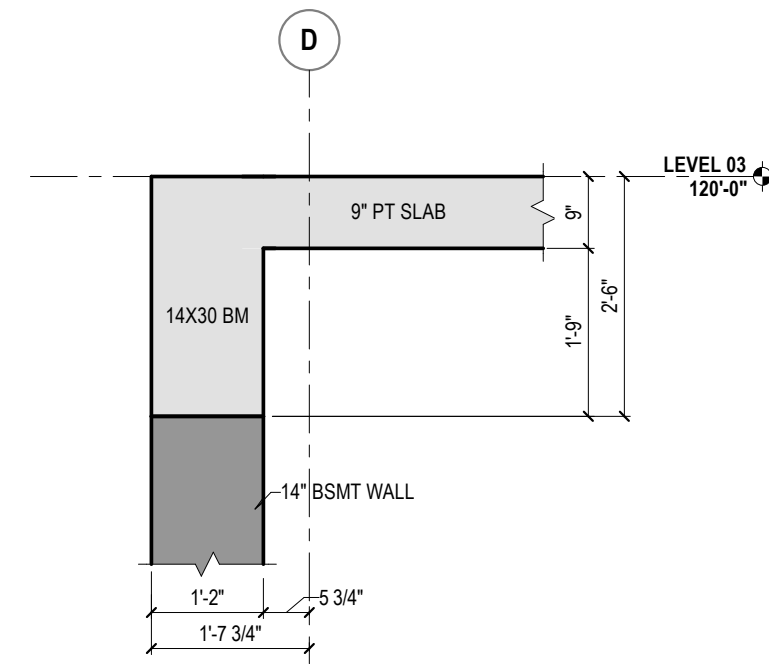


7 14"x30" BEAM AT WALL
REF: 1/1/130
1/2" = 1'-0"

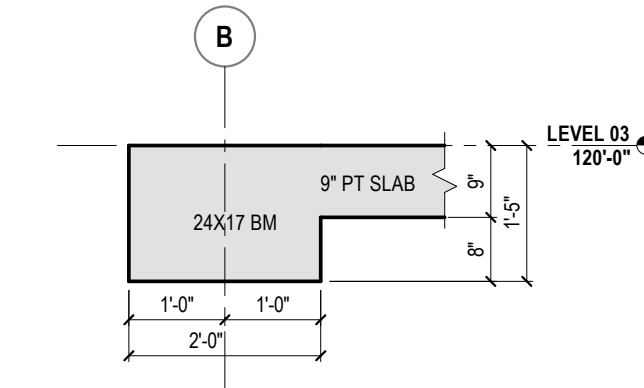


3 24"x17" BEAM LEVEL 03
REF: 1/1/130
1/2" = 1'-0"

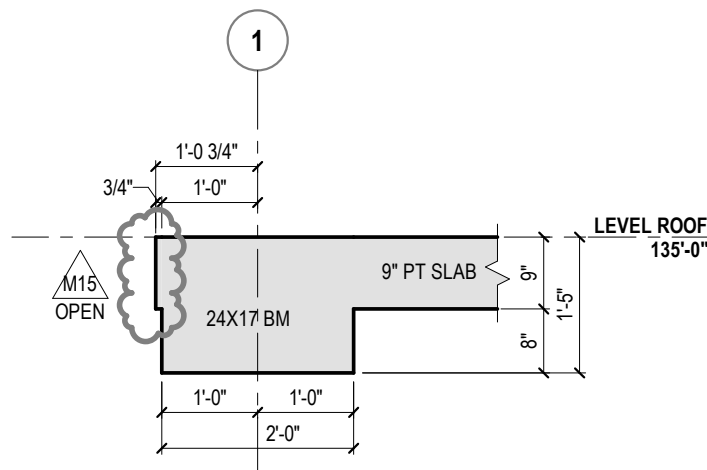


16 24"x17" BEAM AT EOS - ROOF
REF: 1/1/140
1/2" = 1'-0"

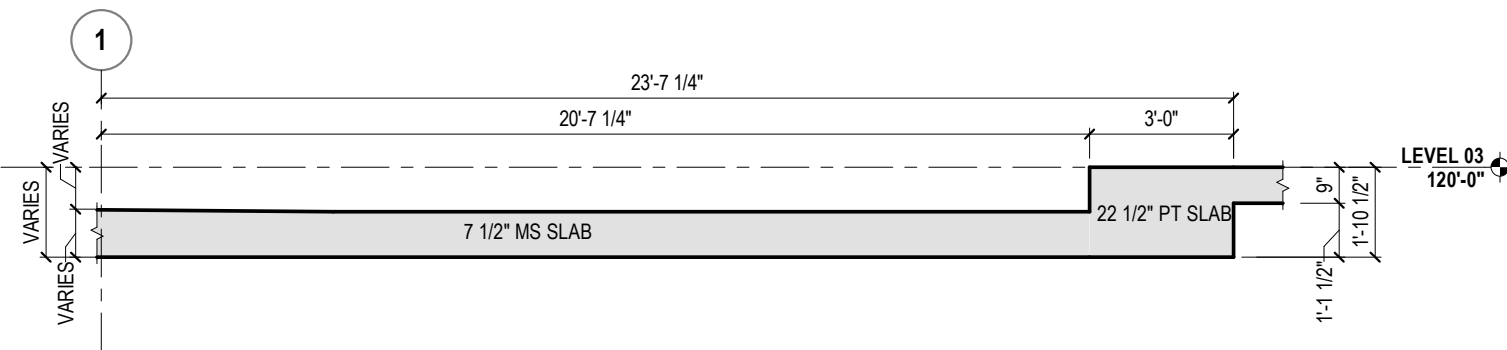

12 TICKENED SLAB AT SLAB STEP LEVEL 03
REF: 1/1/130
1/4" = 1'-0"

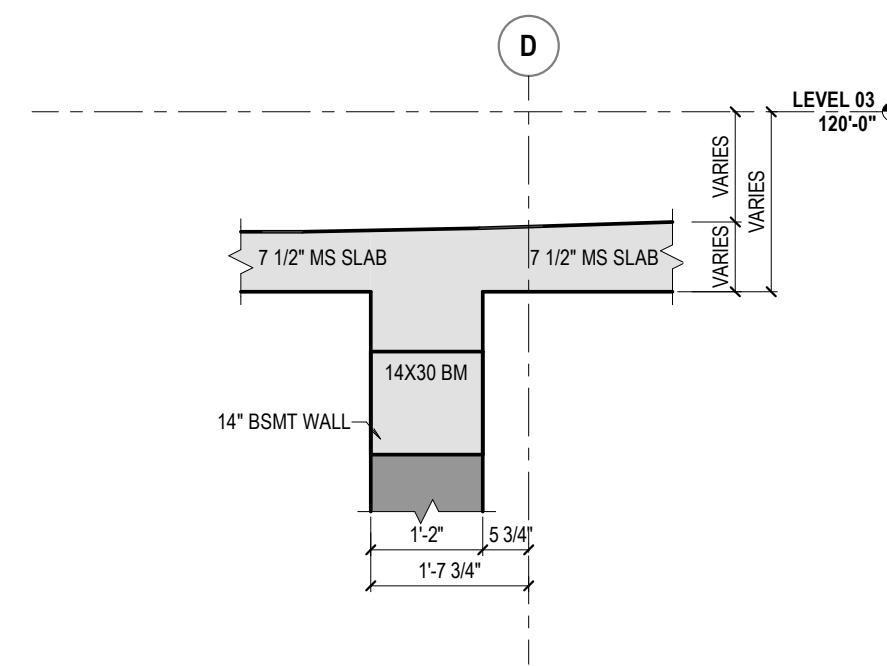


8 MILD REINFORCED BEAT AT BSMT WALL
REF: 1/1/130
1/2" = 1'-0"

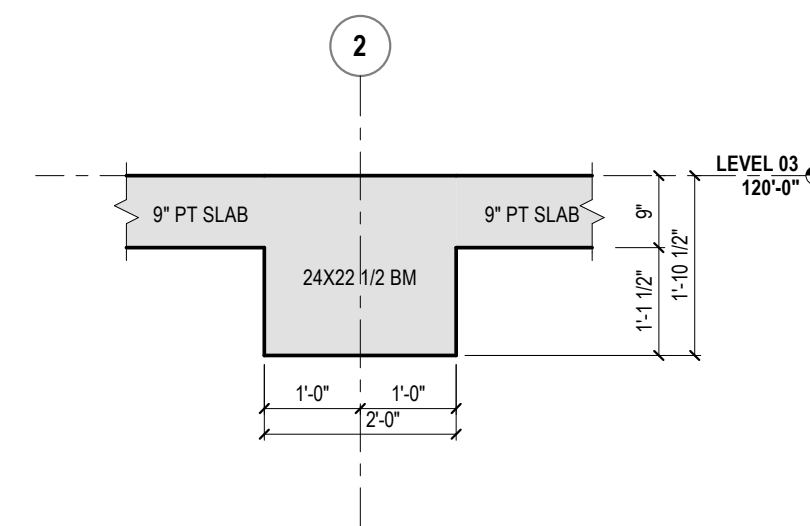


4 24"x22 1/2" BEAM AT LEVEL 03
REF: 1/1/130
1/2" = 1'-0"

THIS DRAWING IS FOR THE EXCLUSIVE USE OF MCCLONE CONSTRUCTION COMPANY. ON THIS PROJECT ONLY. UTILIZATION OF THIS DRAWING BY OTHER PARTIES AND/OR ON OTHER PROJECTS WITHOUT THE EXPRESSED WRITTEN CONSENT OF MCCLONE CONSTRUCTION COMPANY IS STRICTLY PROHIBITED.


PLOT DATE/TIME STAMP: 6/21/2022 10:03:38 AM
Z:\Shared\WAP\p06a01175 Botthel STEM 4\MCCL Drawings\Sheet Model\1175 - Botthel STEM 4.rvt

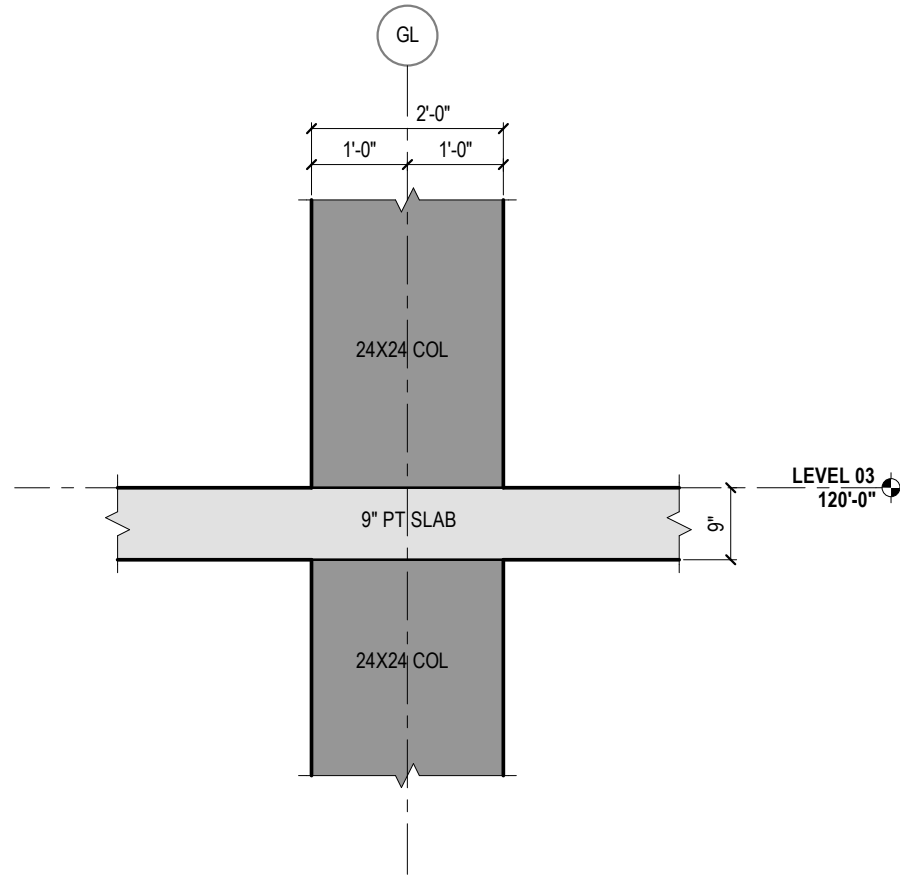


5 24"x24" COLUMN AT LEVEL 03
REF: 1/11.3.0
1/2" = 1'-0"

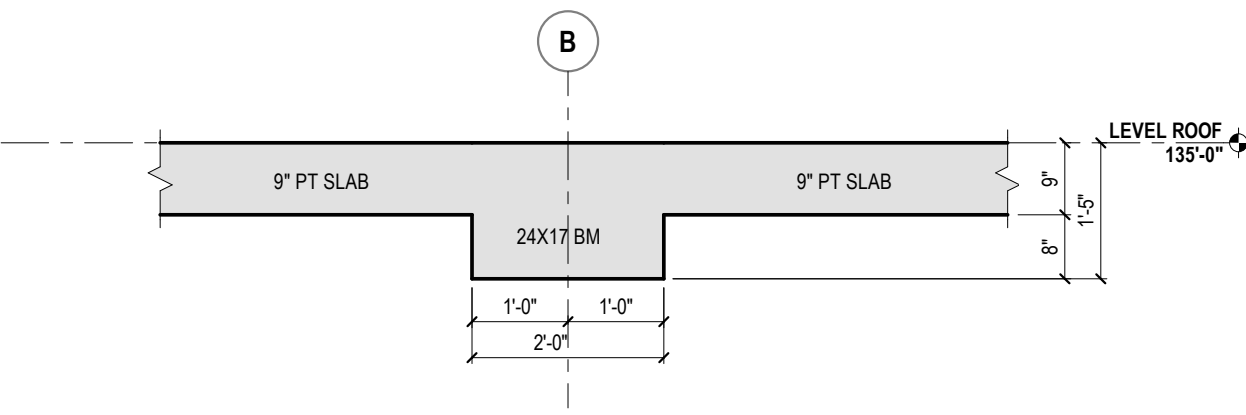


1 24"x17" BEAM AT ROOF LEVEL
REF: 1/11.4.0
1/2" = 1'-0"

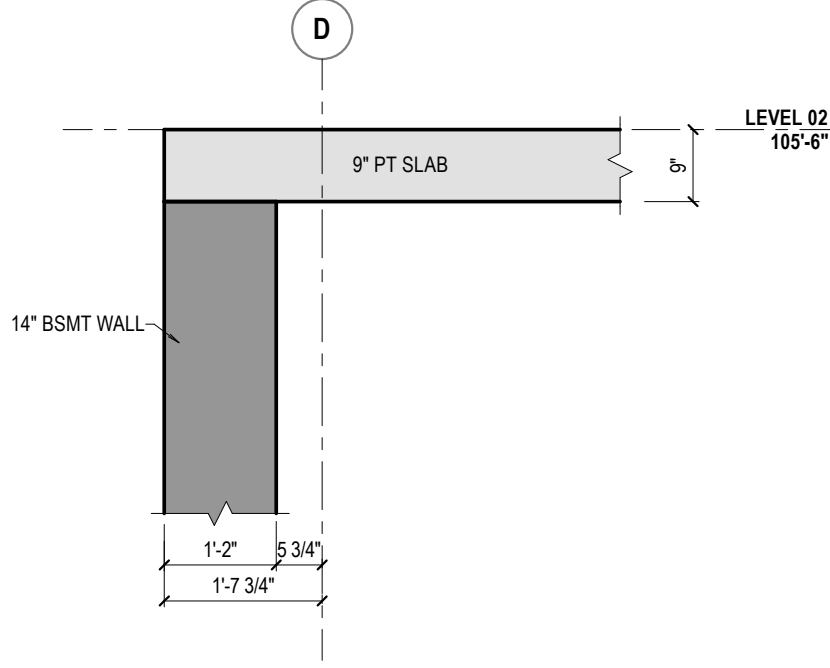


6 BSMNT WALL AT EOS LEVEL 02
REF: 1/11.2.0
1/2" = 1'-0"

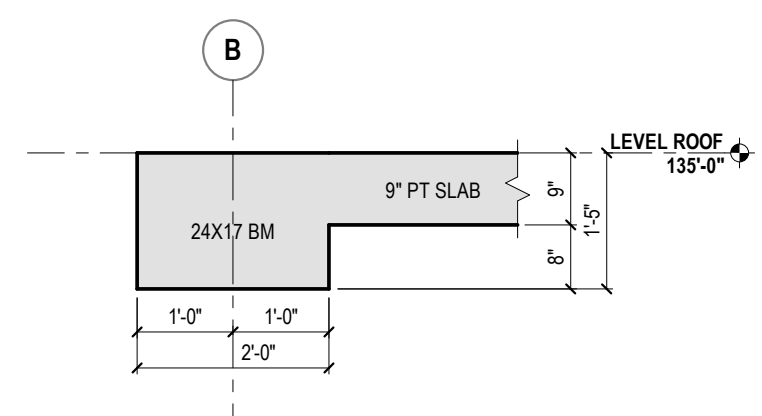


2 24"x17" BEAM AT ROOF
REF: 1/11.4.0
1/2" = 1'-0"

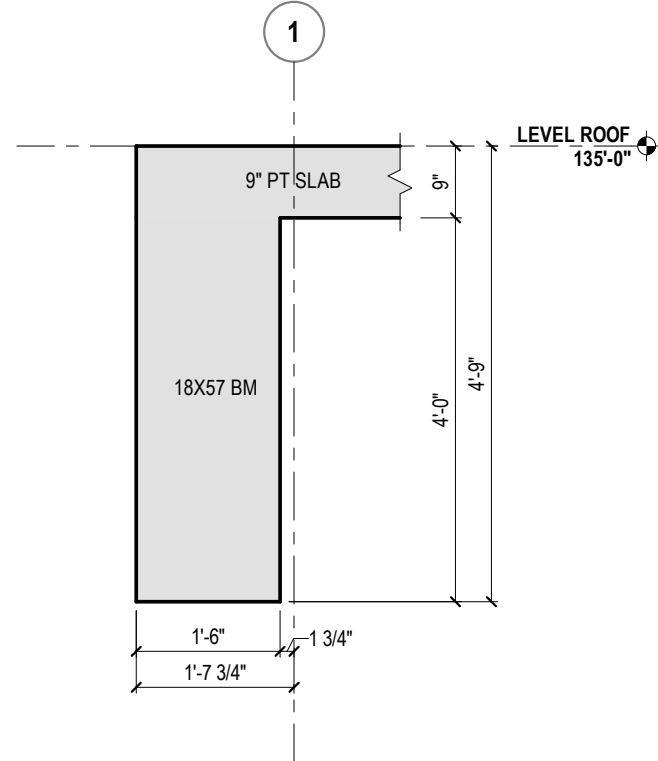


7 18x57 BM AT ROOF
REF: 1/11.4.0
1/2" = 1'-0"

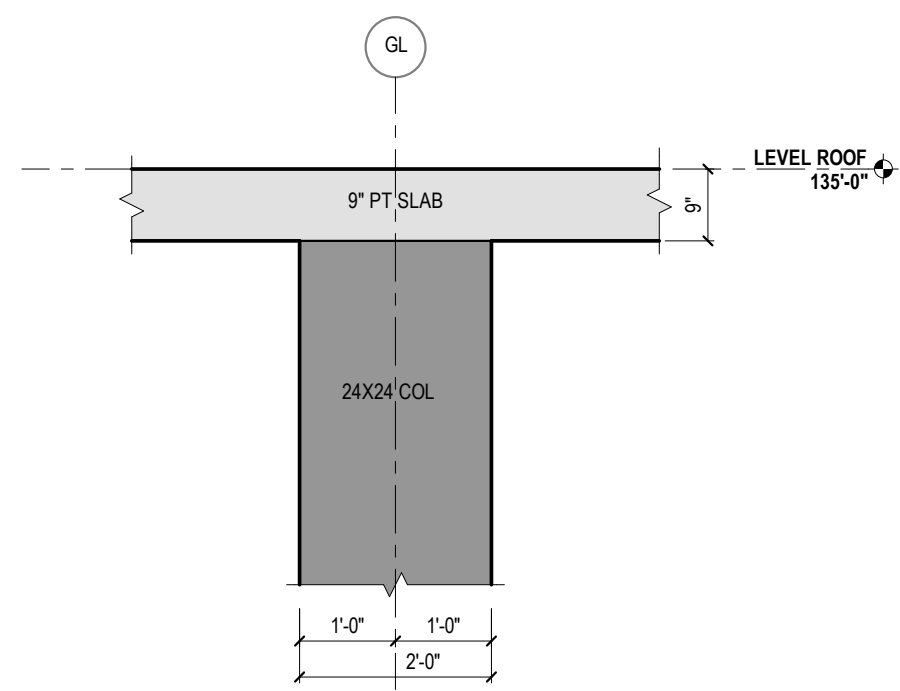

3 24"x24" COLUMN AT ROOF
REF: 1/11.4.0
1/2" = 1'-0"

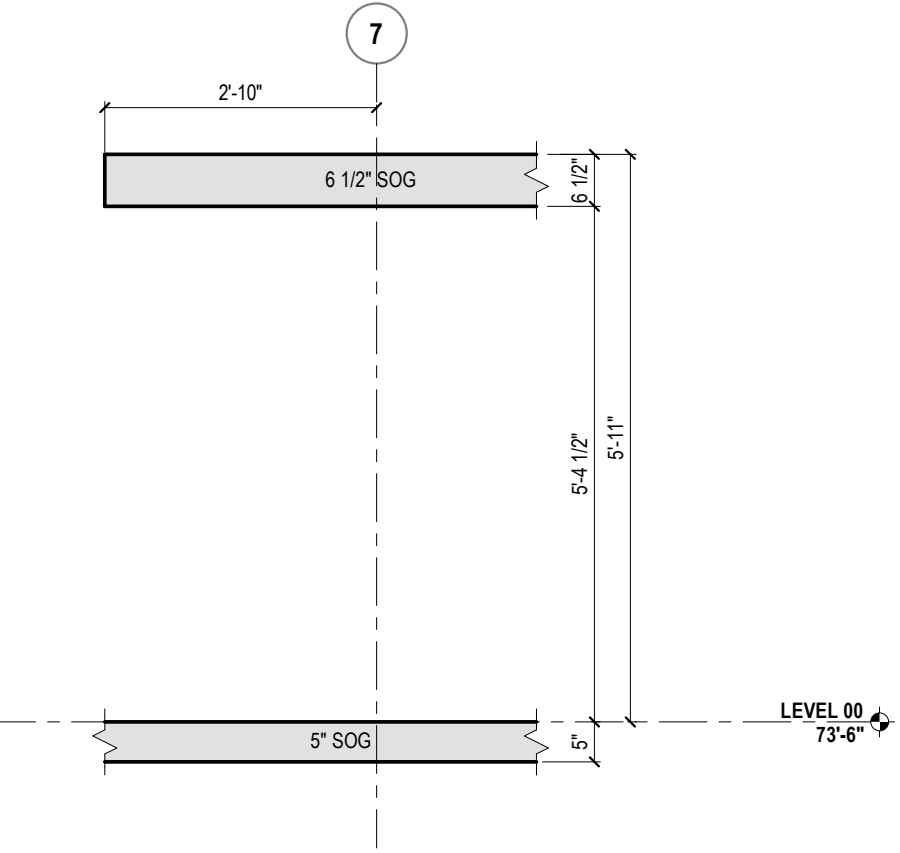

8 SLAB EDGE - MID LANDING
REF: 1/11.0.0
1/2" = 1'-0"

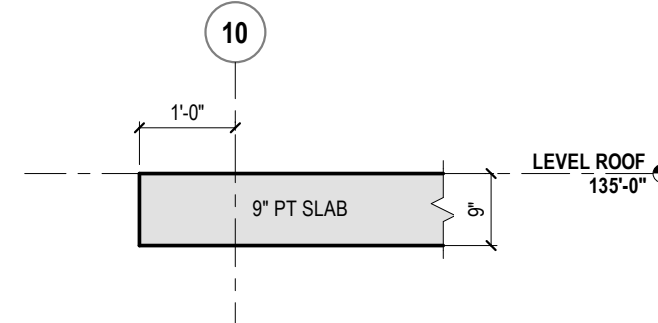

4 EDGE OF SLAB GL 10
REF: 1/11.4.0
1/2" = 1'-0"

**McCLONE**
CONSTRUCTION | SINCE 1975

WASHINGTON OFFICE
28810 MAPLE VALLEY, WA 98038 | 425-143-1440

SECTIONS AND DETAILS

1175 - Botthel STEM 4
BOTTEL, WA, 98011

SHEET TITLE: 06/21/2022

SHEET NUMBER: SUBMITTAL


SCALE: 1/2" = 1'-0"

DRAWN BY: DALVAREZ


FOR: 1175

SHEET: 2.02

THIS DRAWING IS FOR THE EXCLUSIVE USE OF MCCLONE CONSTRUCTION COMPANY, ON THIS PROJECT ONLY. UTILIZATION OF THIS DRAWING BY OTHER PARTIES AND/OR ON OTHER PROJECTS WITHOUT THE EXPRESSED WRITTEN CONSENT OF MCCLONE CONSTRUCTION COMPANY IS STRICTLY PROHIBITED.

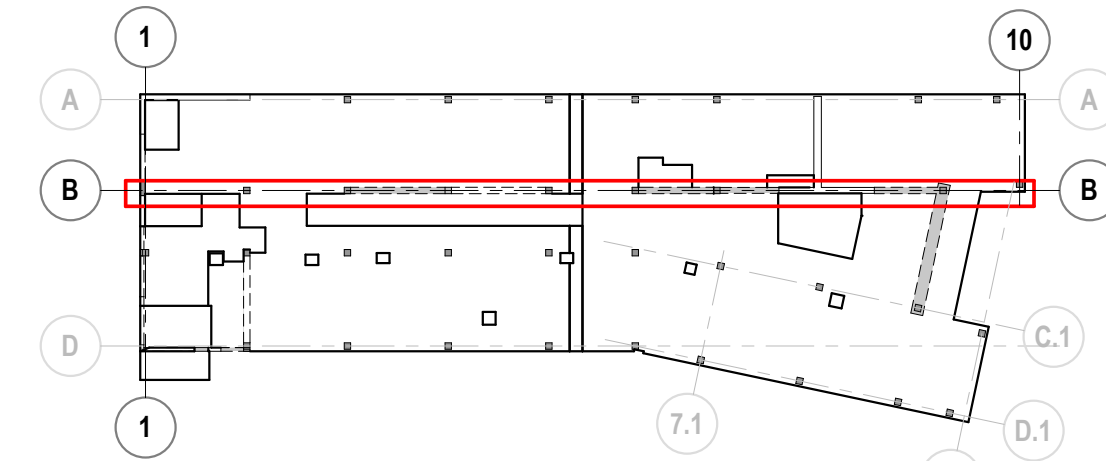

KEYPLAN BUILDING ELEVATION GL B

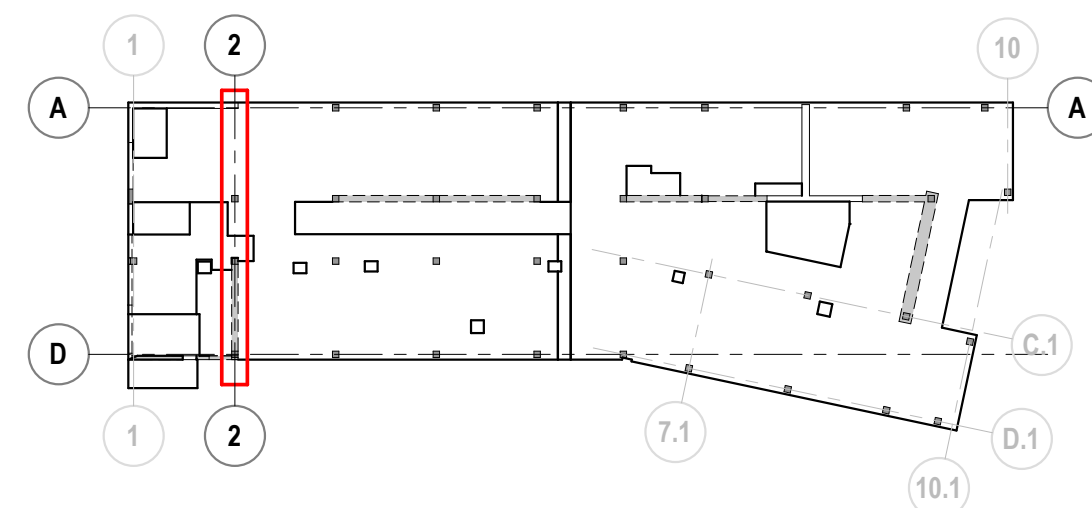


KEYPLAN BUILDING ELEVATION GL 2

SHEET ISSUE DATE	06/21/2022	
SHEET ISSUED FOR	SUBMITTAL	
SCALE	As indicated	
DRAWING BY	DALVAREZ	
JOB	1175	
SHEET	3.0.0	
SHEET SUFFIX		


24X36 ORIGINAL SHEET SIZE

PLOT DATE/TIME STAMP: 6/21/2022 10:09:41 AM
Z:\Shared\WAP\p06201175 Bofthel STEM 4\IMCC ENG\Drawings\Sheet Model\1175 - Bofthel STEM 4.rvt


THIS DRAWING IS FOR THE EXCLUSIVE USE OF MACCLONE CONSTRUCTION COMPANY, ON THIS PROJECT ONLY. UTILIZATION OF THIS DRAWING BY OTHER PARTIES AND/OR ON OTHER PROJECTS WITHOUT THE EXPRESSED WRITTEN CONSENT OF MACCLONE CONSTRUCTION COMPANY IS STRICTLY PROHIBITED.

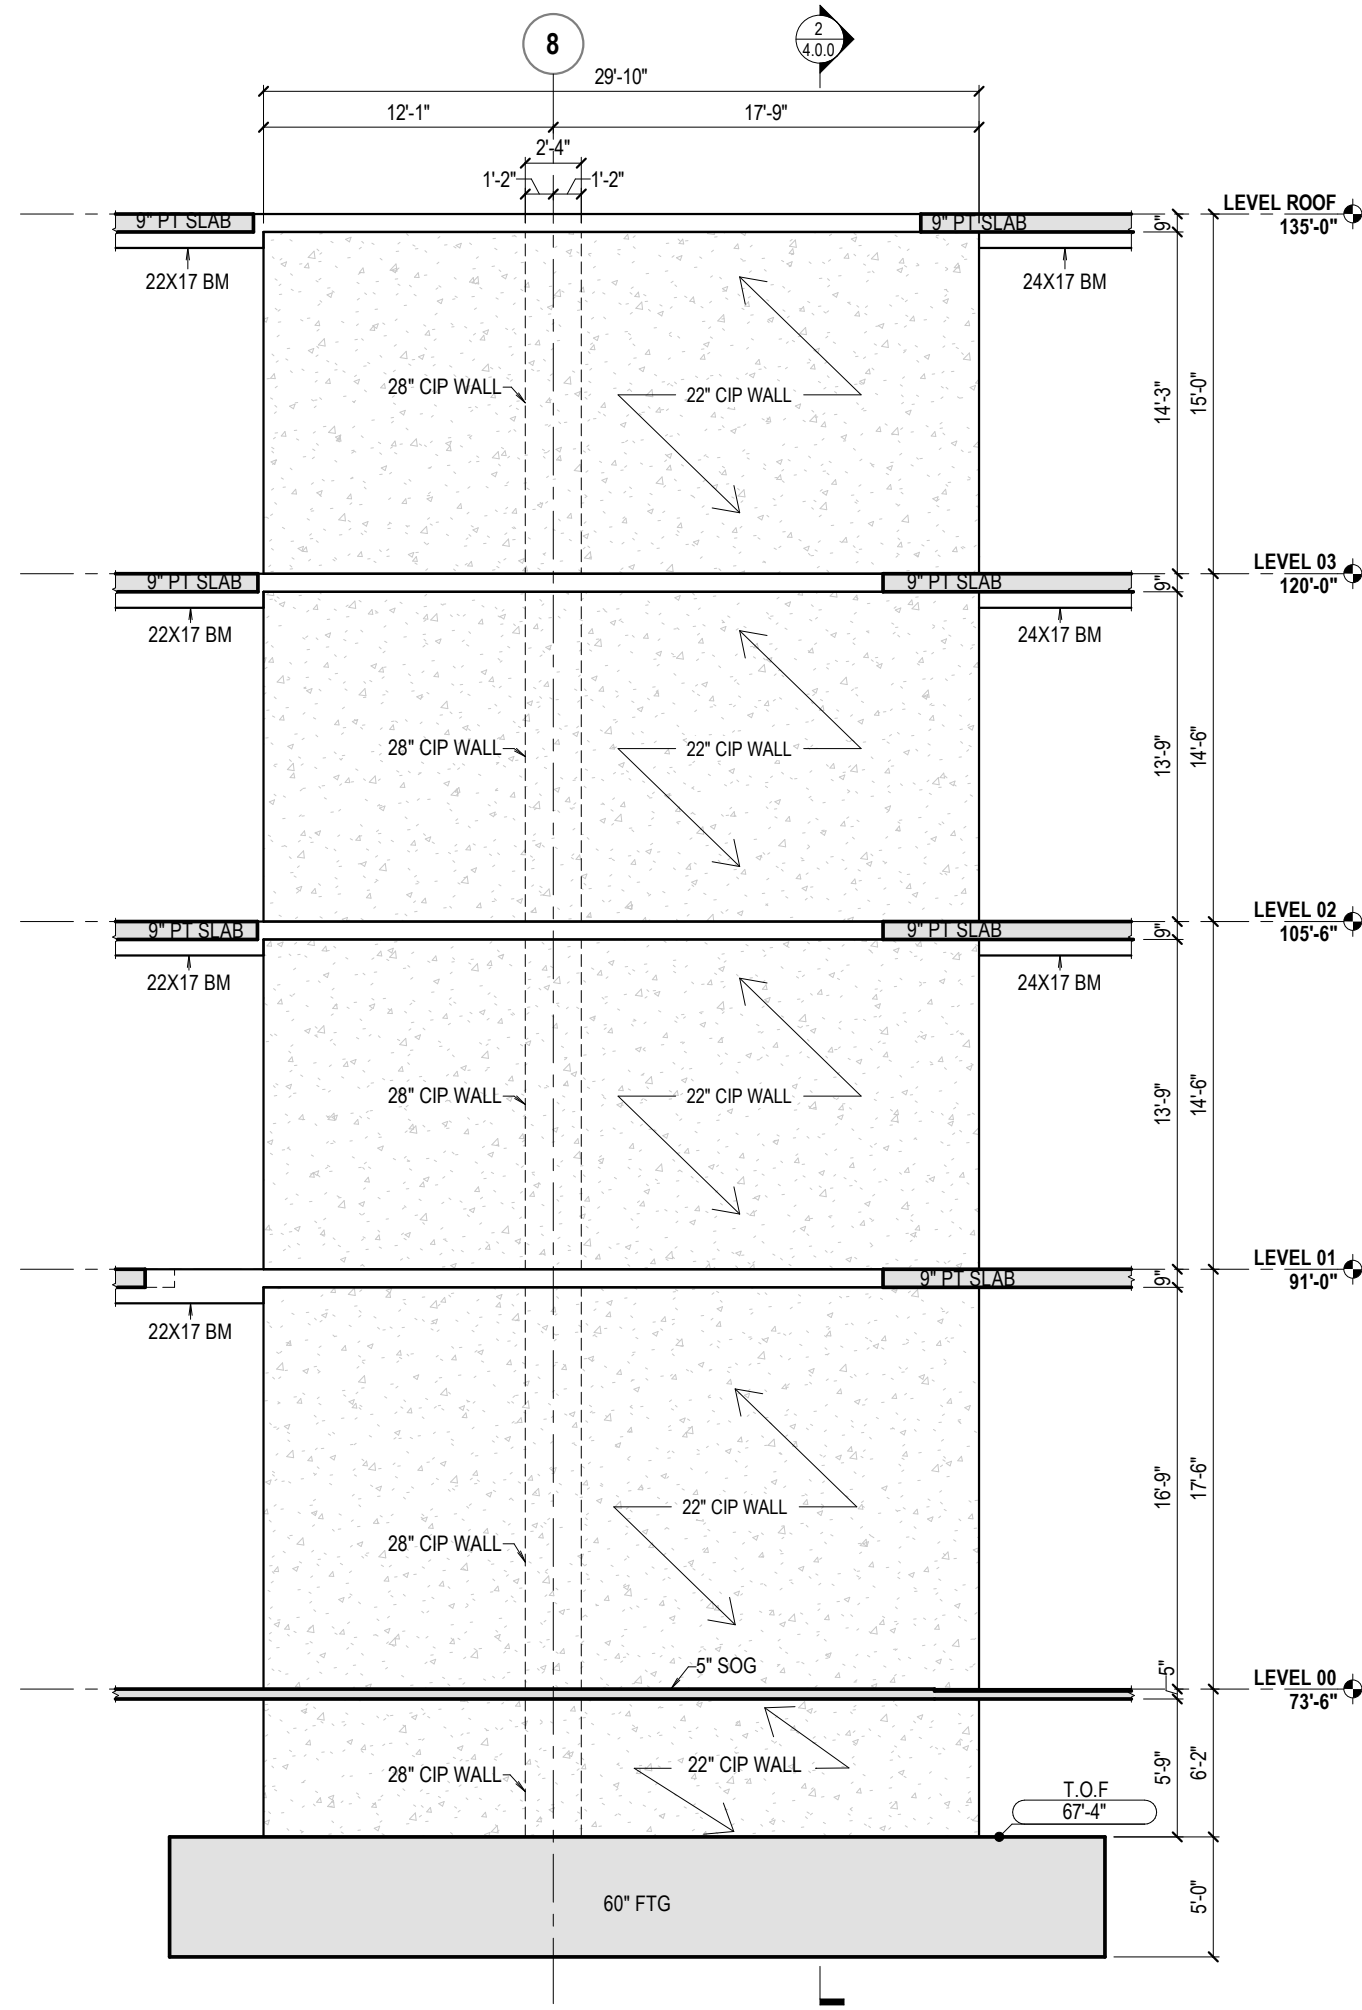



1 SHEAR WALL ELEVATION GL B
1/8" = 1'-0"

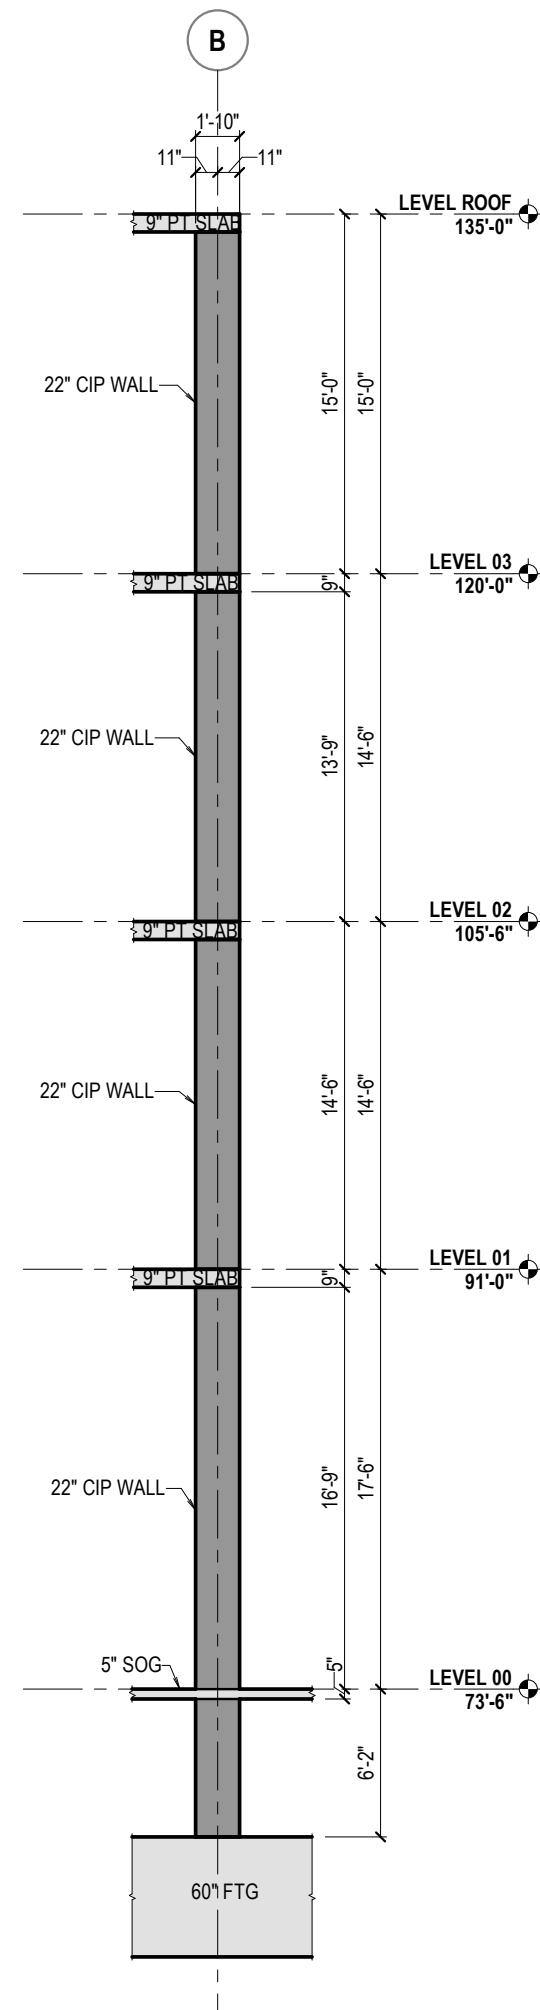

2 WALL SECTION - SHEAR WALL ELEVATION GL B
1/8" = 1'-0"

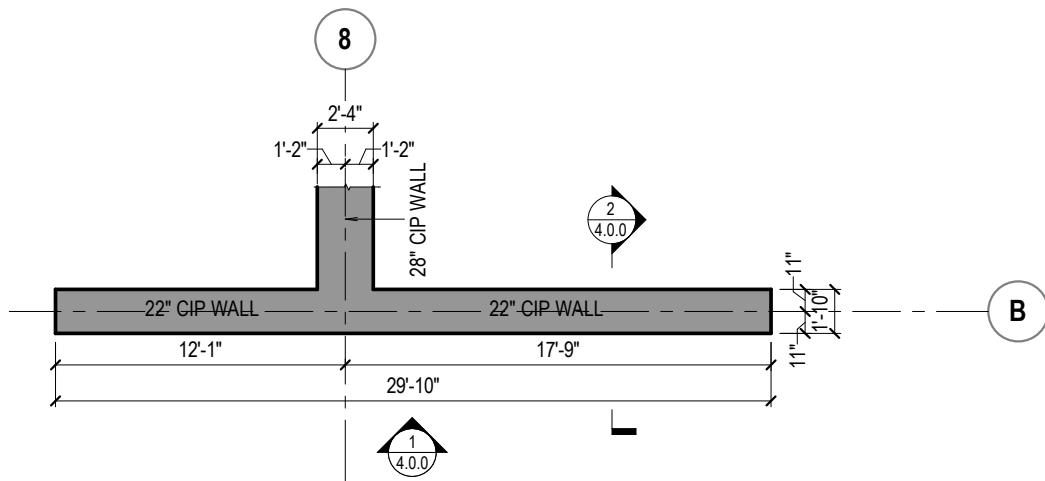

3 PLAN VIEW - SHEAR WALL ELEVATION GL B
1/8" = 1'-0"

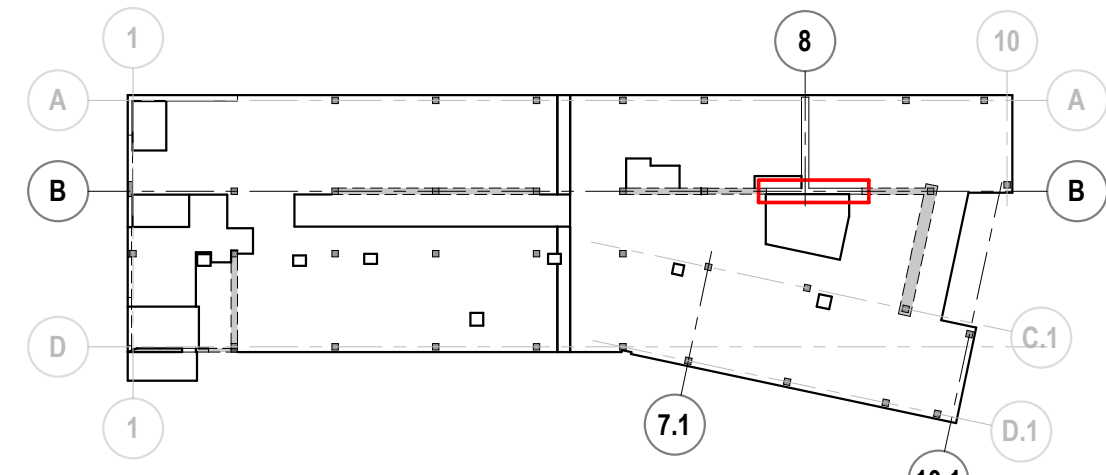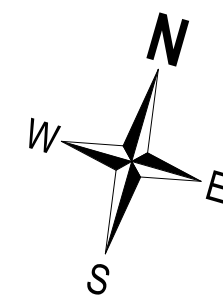

KEYPLAN SHEAR WALL ELEVATION GL B