



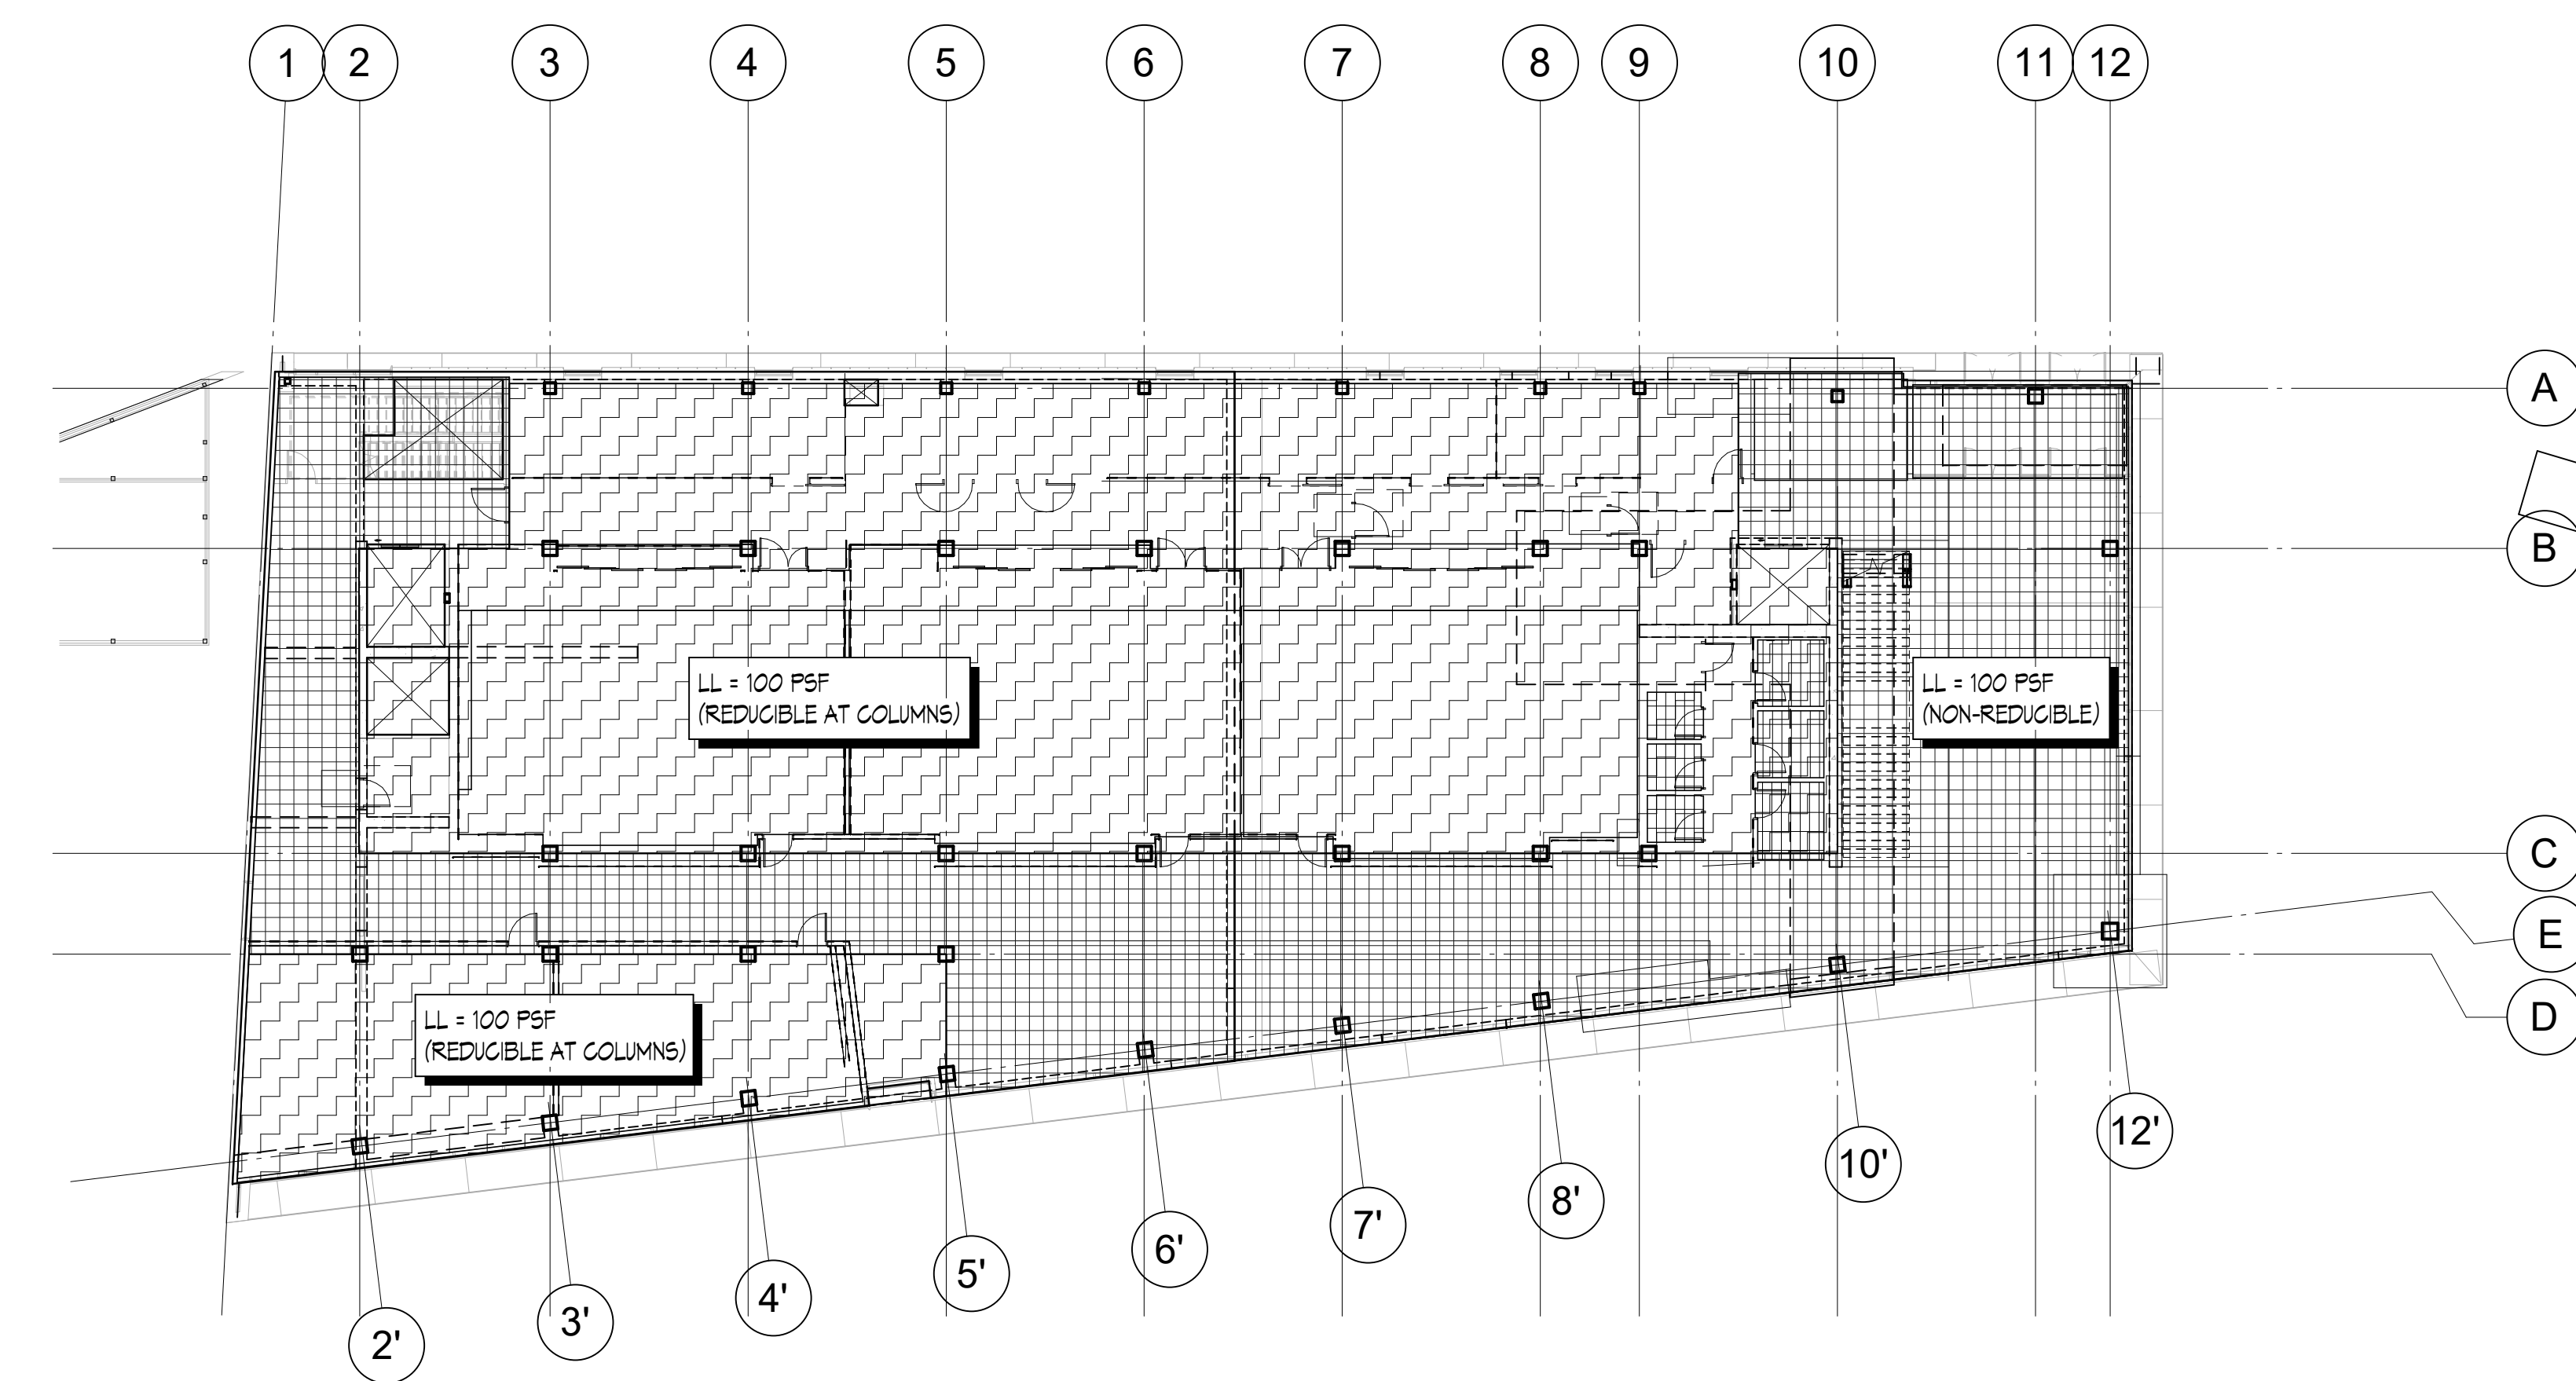

4 LEVEL 2 - LIVE LOAD
1/16" = 1'-0"

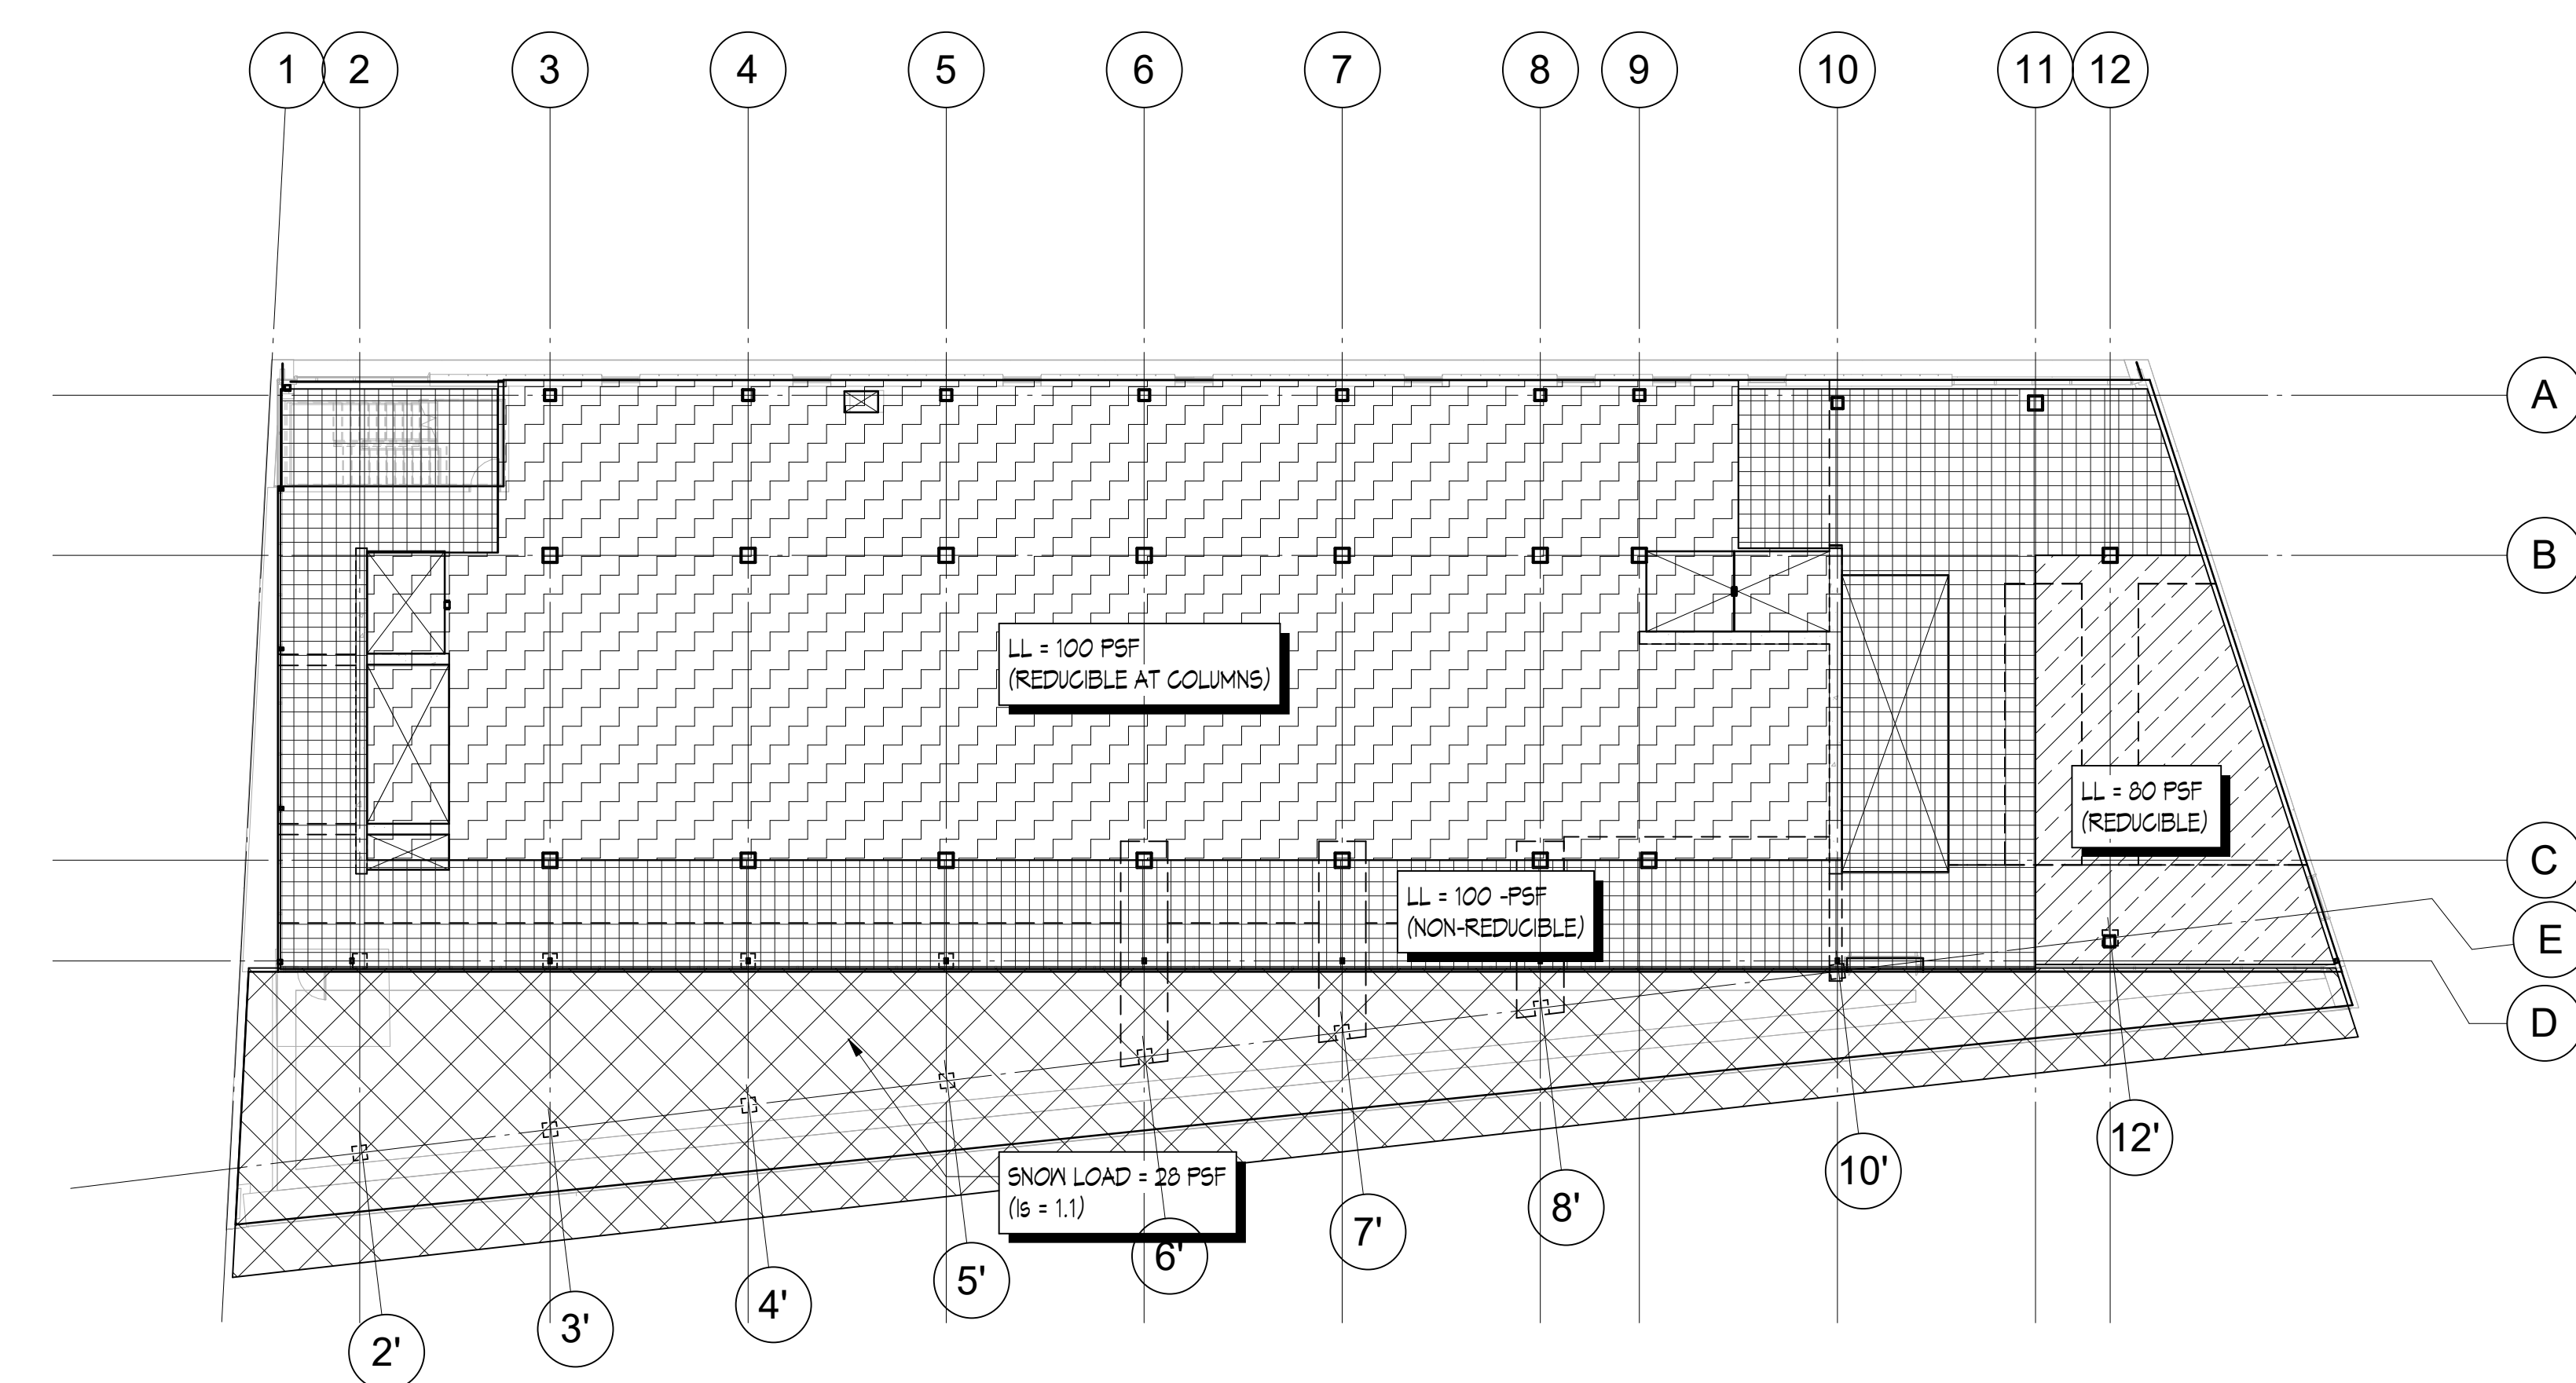

6 LEVEL 3 - LIVE LOAD
1/16" = 1'-0" |




PROJECT

WESTERN
WASHINGTON
UNIVERSITY
INTERDISCIPLINARY
SCIENCE BUILDING
1755 BILL McDONALD
PARKWAY
BELLINGHAM, WA 98225

CONFORMED
SET

08/26/2020

KEYPLAN

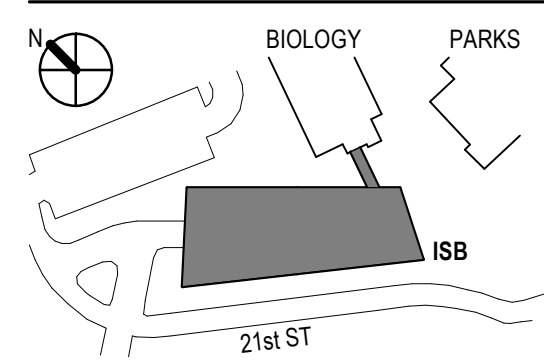

REVISIONS

ASB/001 (SHECH BUILDING PERMIT REV 2) 08/26/2020
DATE

Job Number S191620-06

Drawn CRH

Checked MAS

Approved BWB

TITLE


LOADING DIAGRAMS

SHEET NUMBER


S10-04

WWU SHEET NUMBER


Copyright © 2019 Perkins+Will

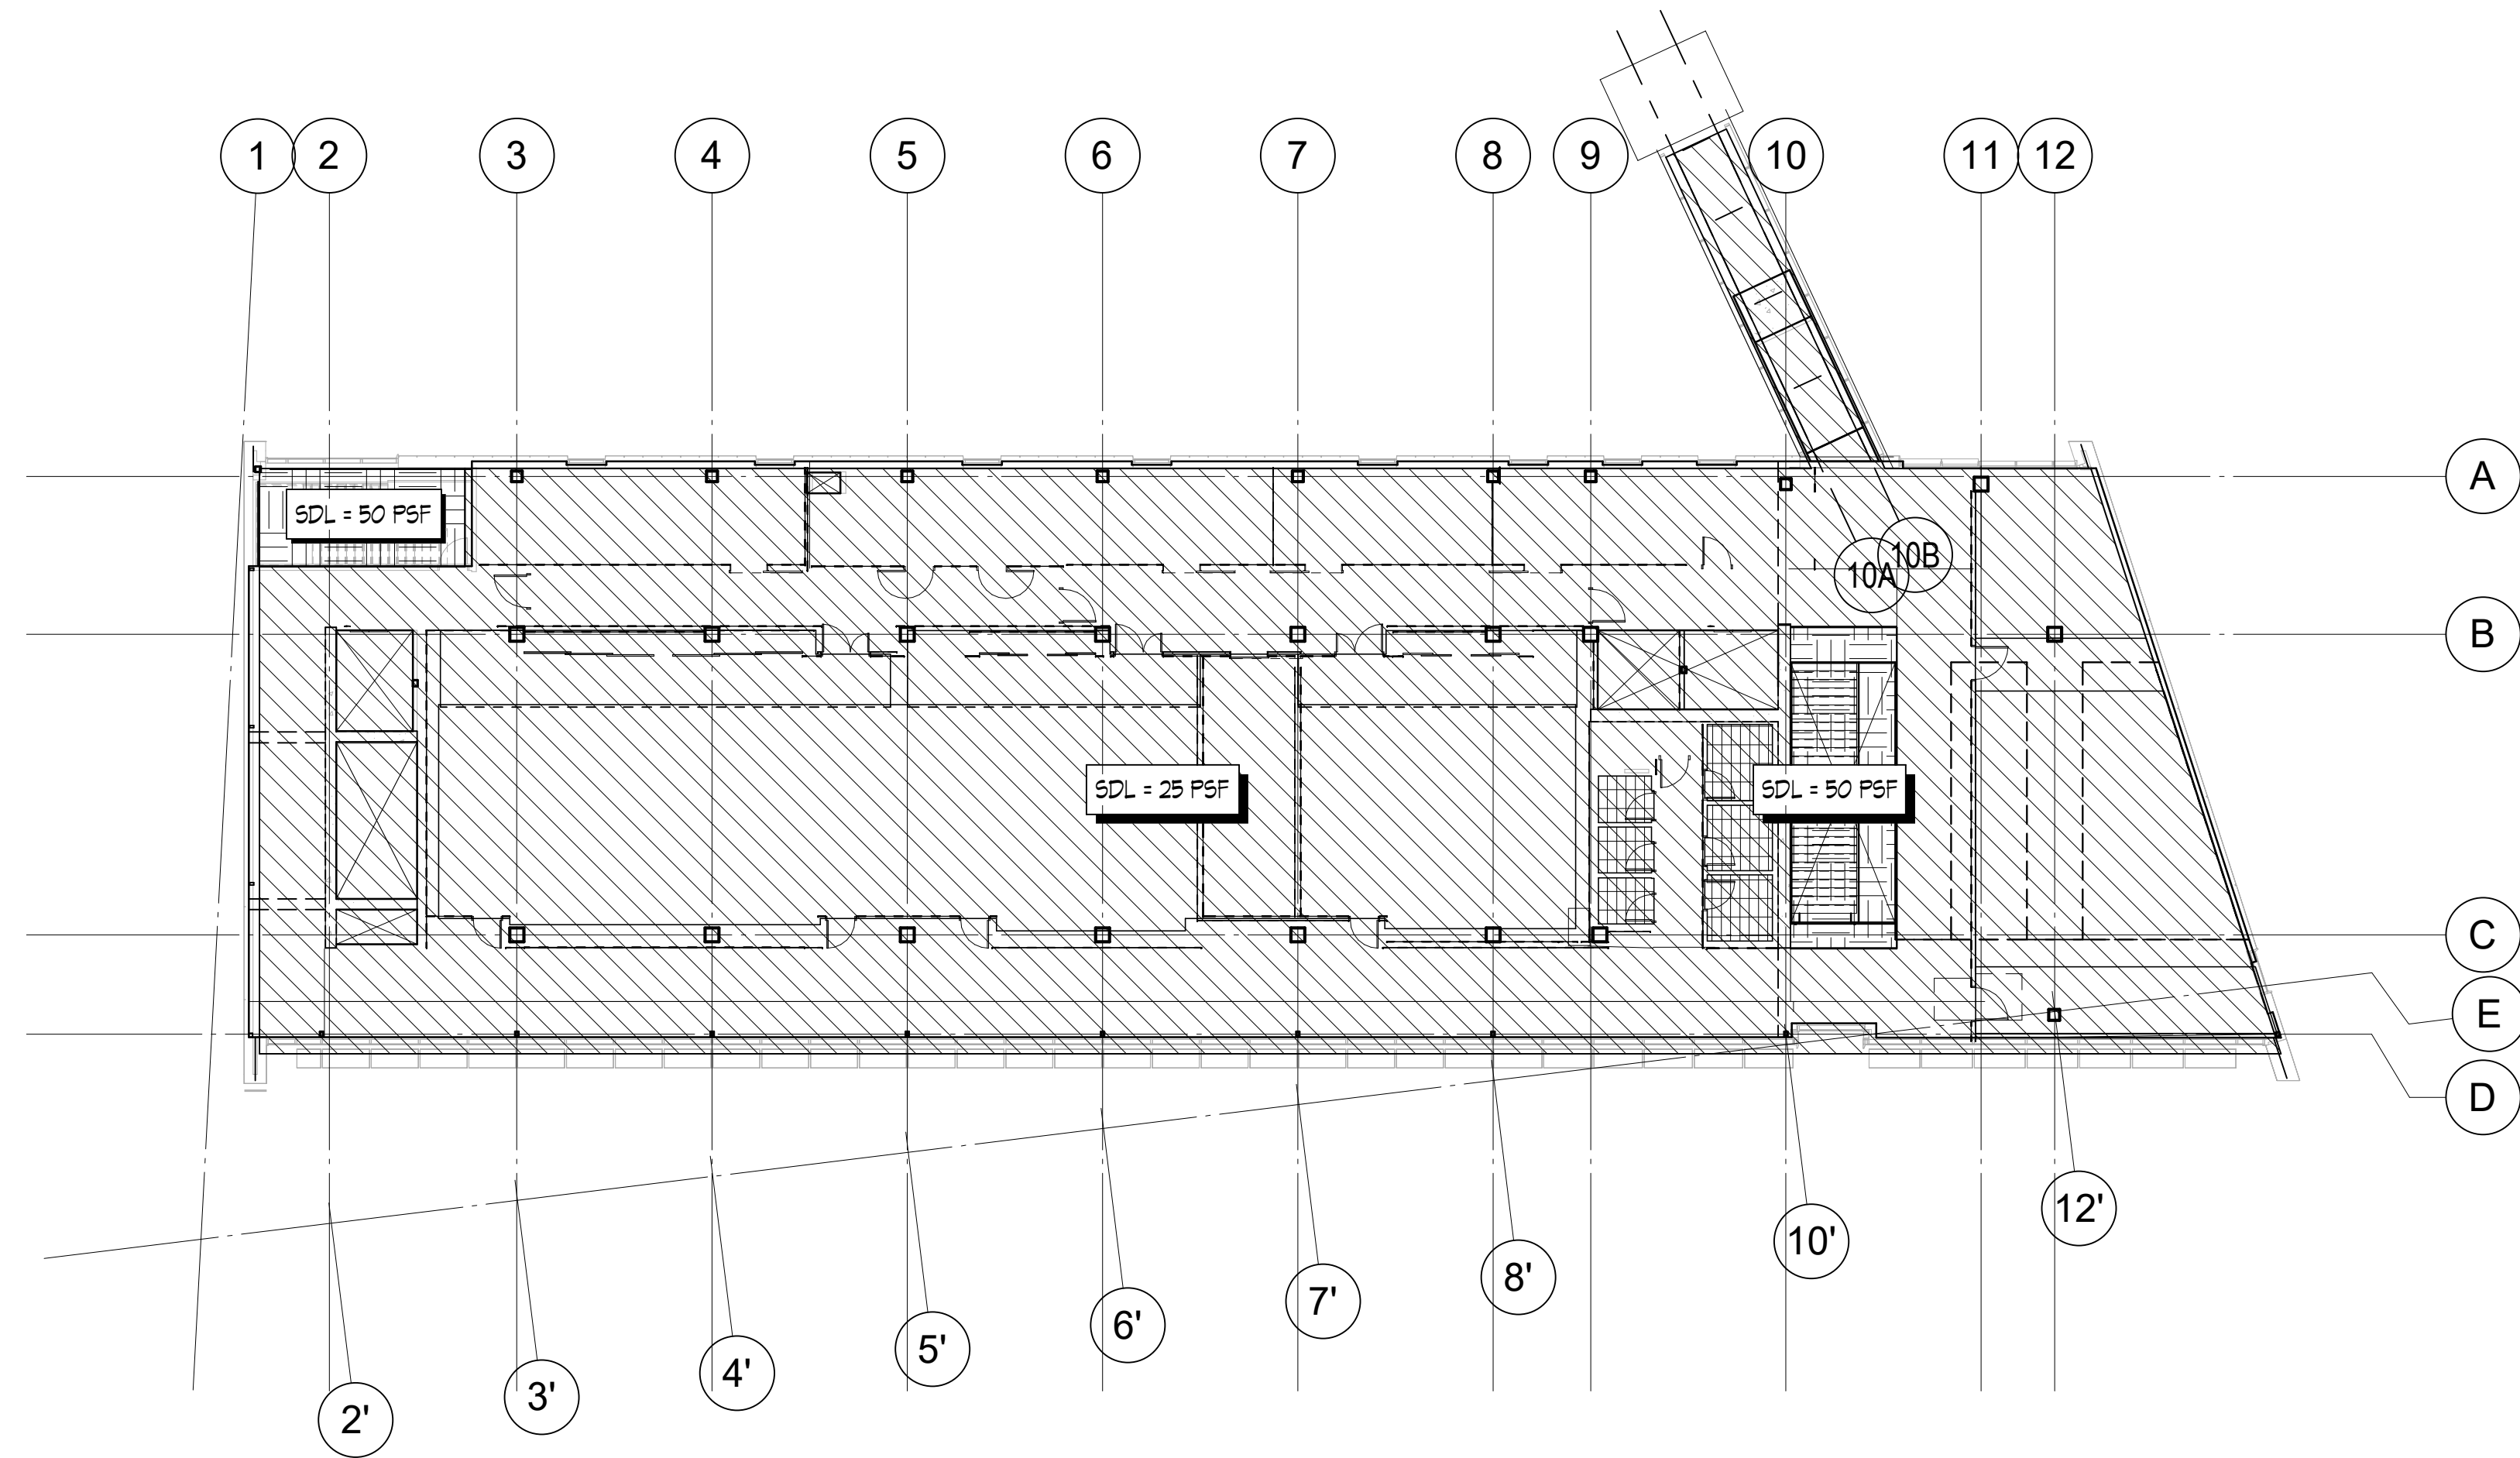


1 LEVEL 4 - SUPERIMPOSED DEAD LOAD
1/16" = 1'-0"

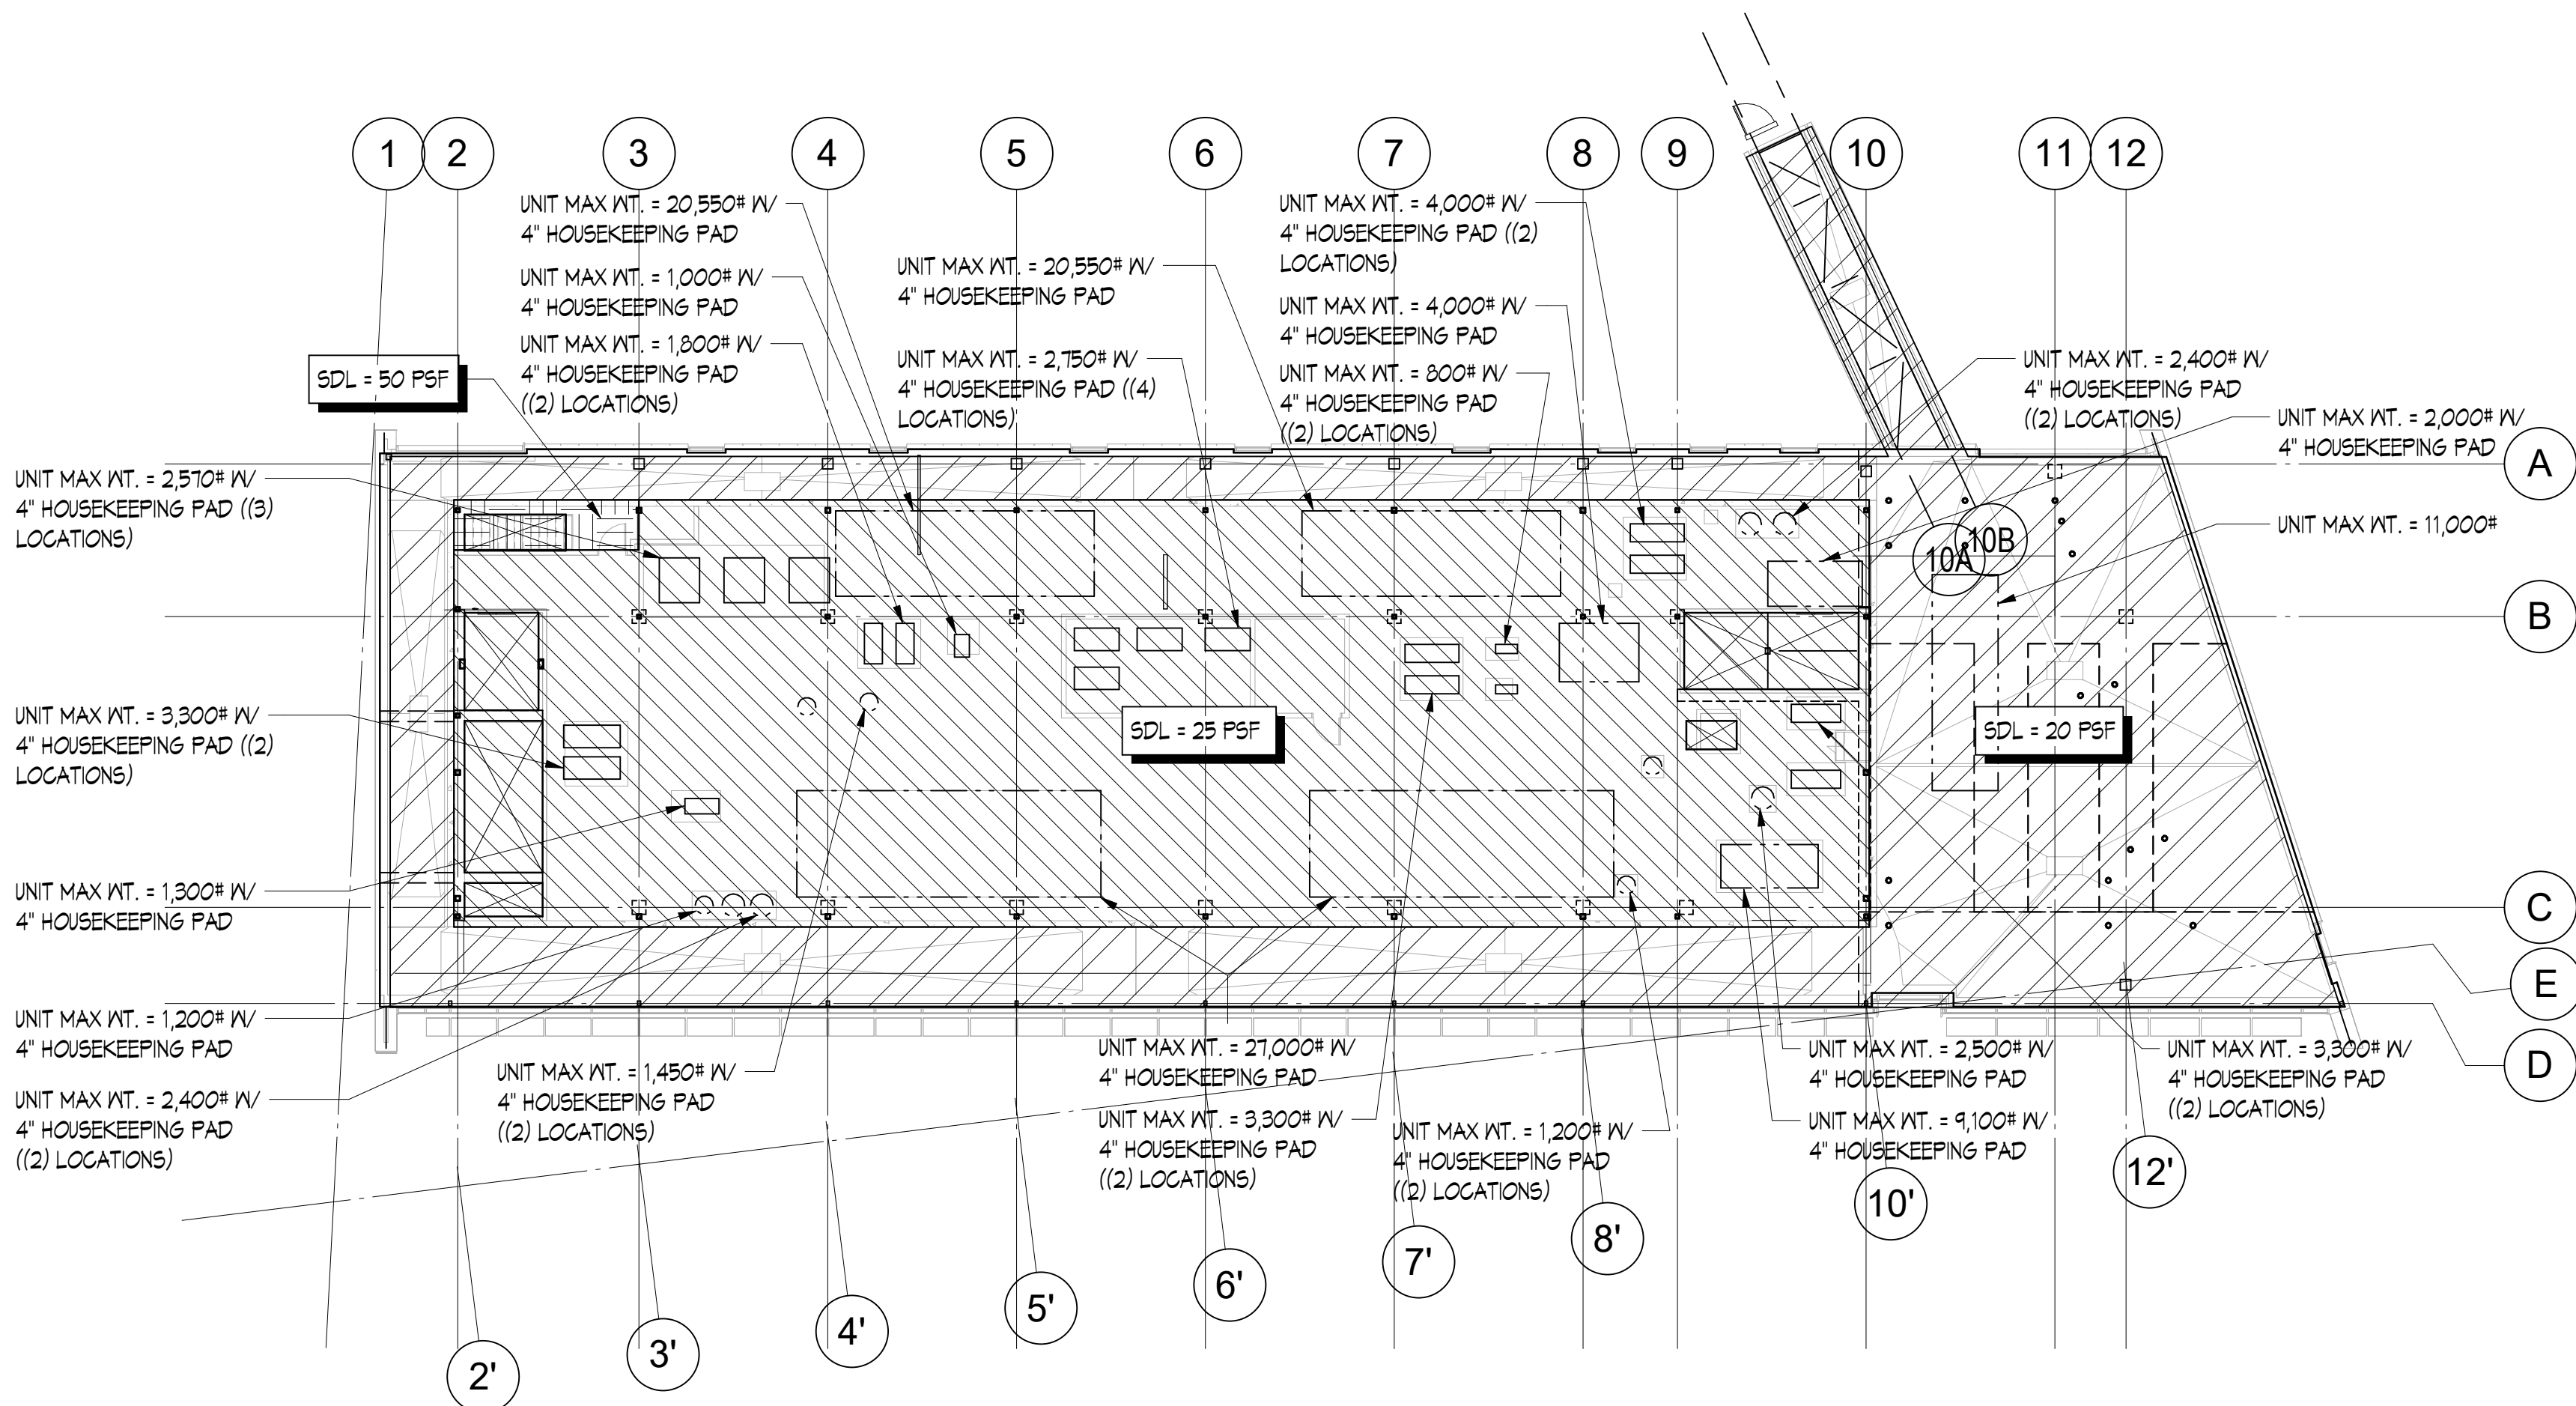


3 PENTHOUSE - SUPERIMPOSED DEAD LOAD
1/16" = 1'-0"

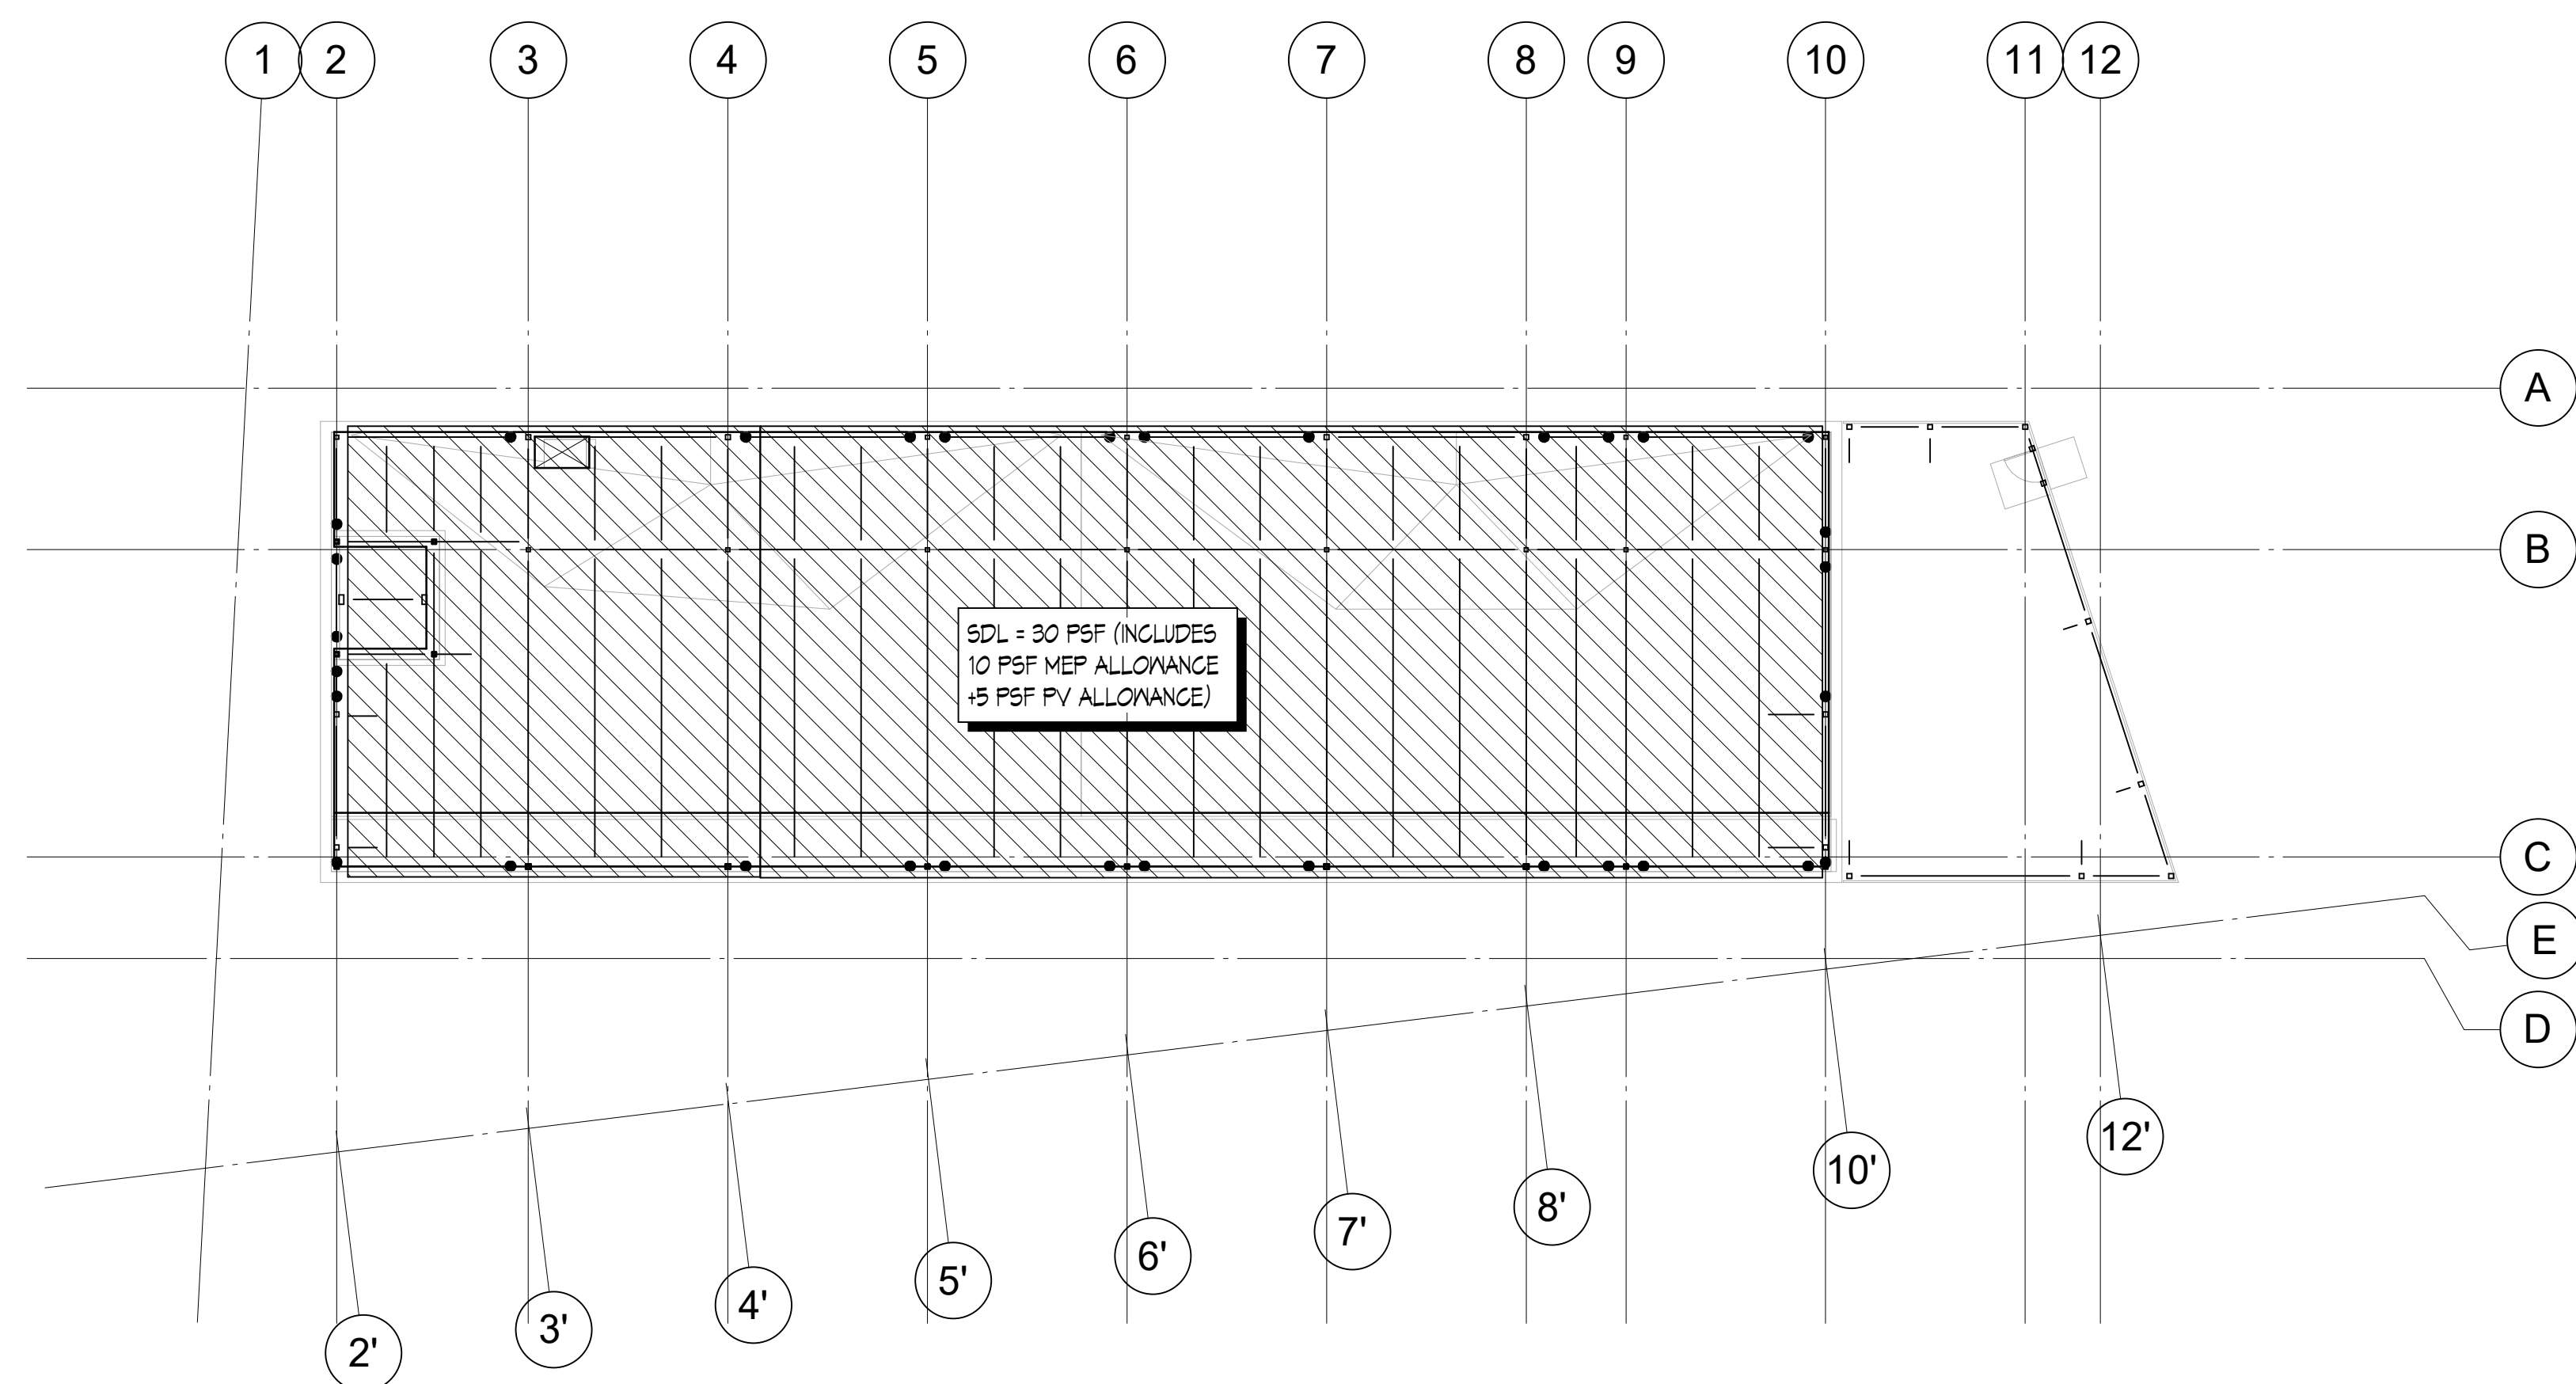


5 ROOF - SUPERIMPOSED DEAD LOAD
1/16" = 1'-0"

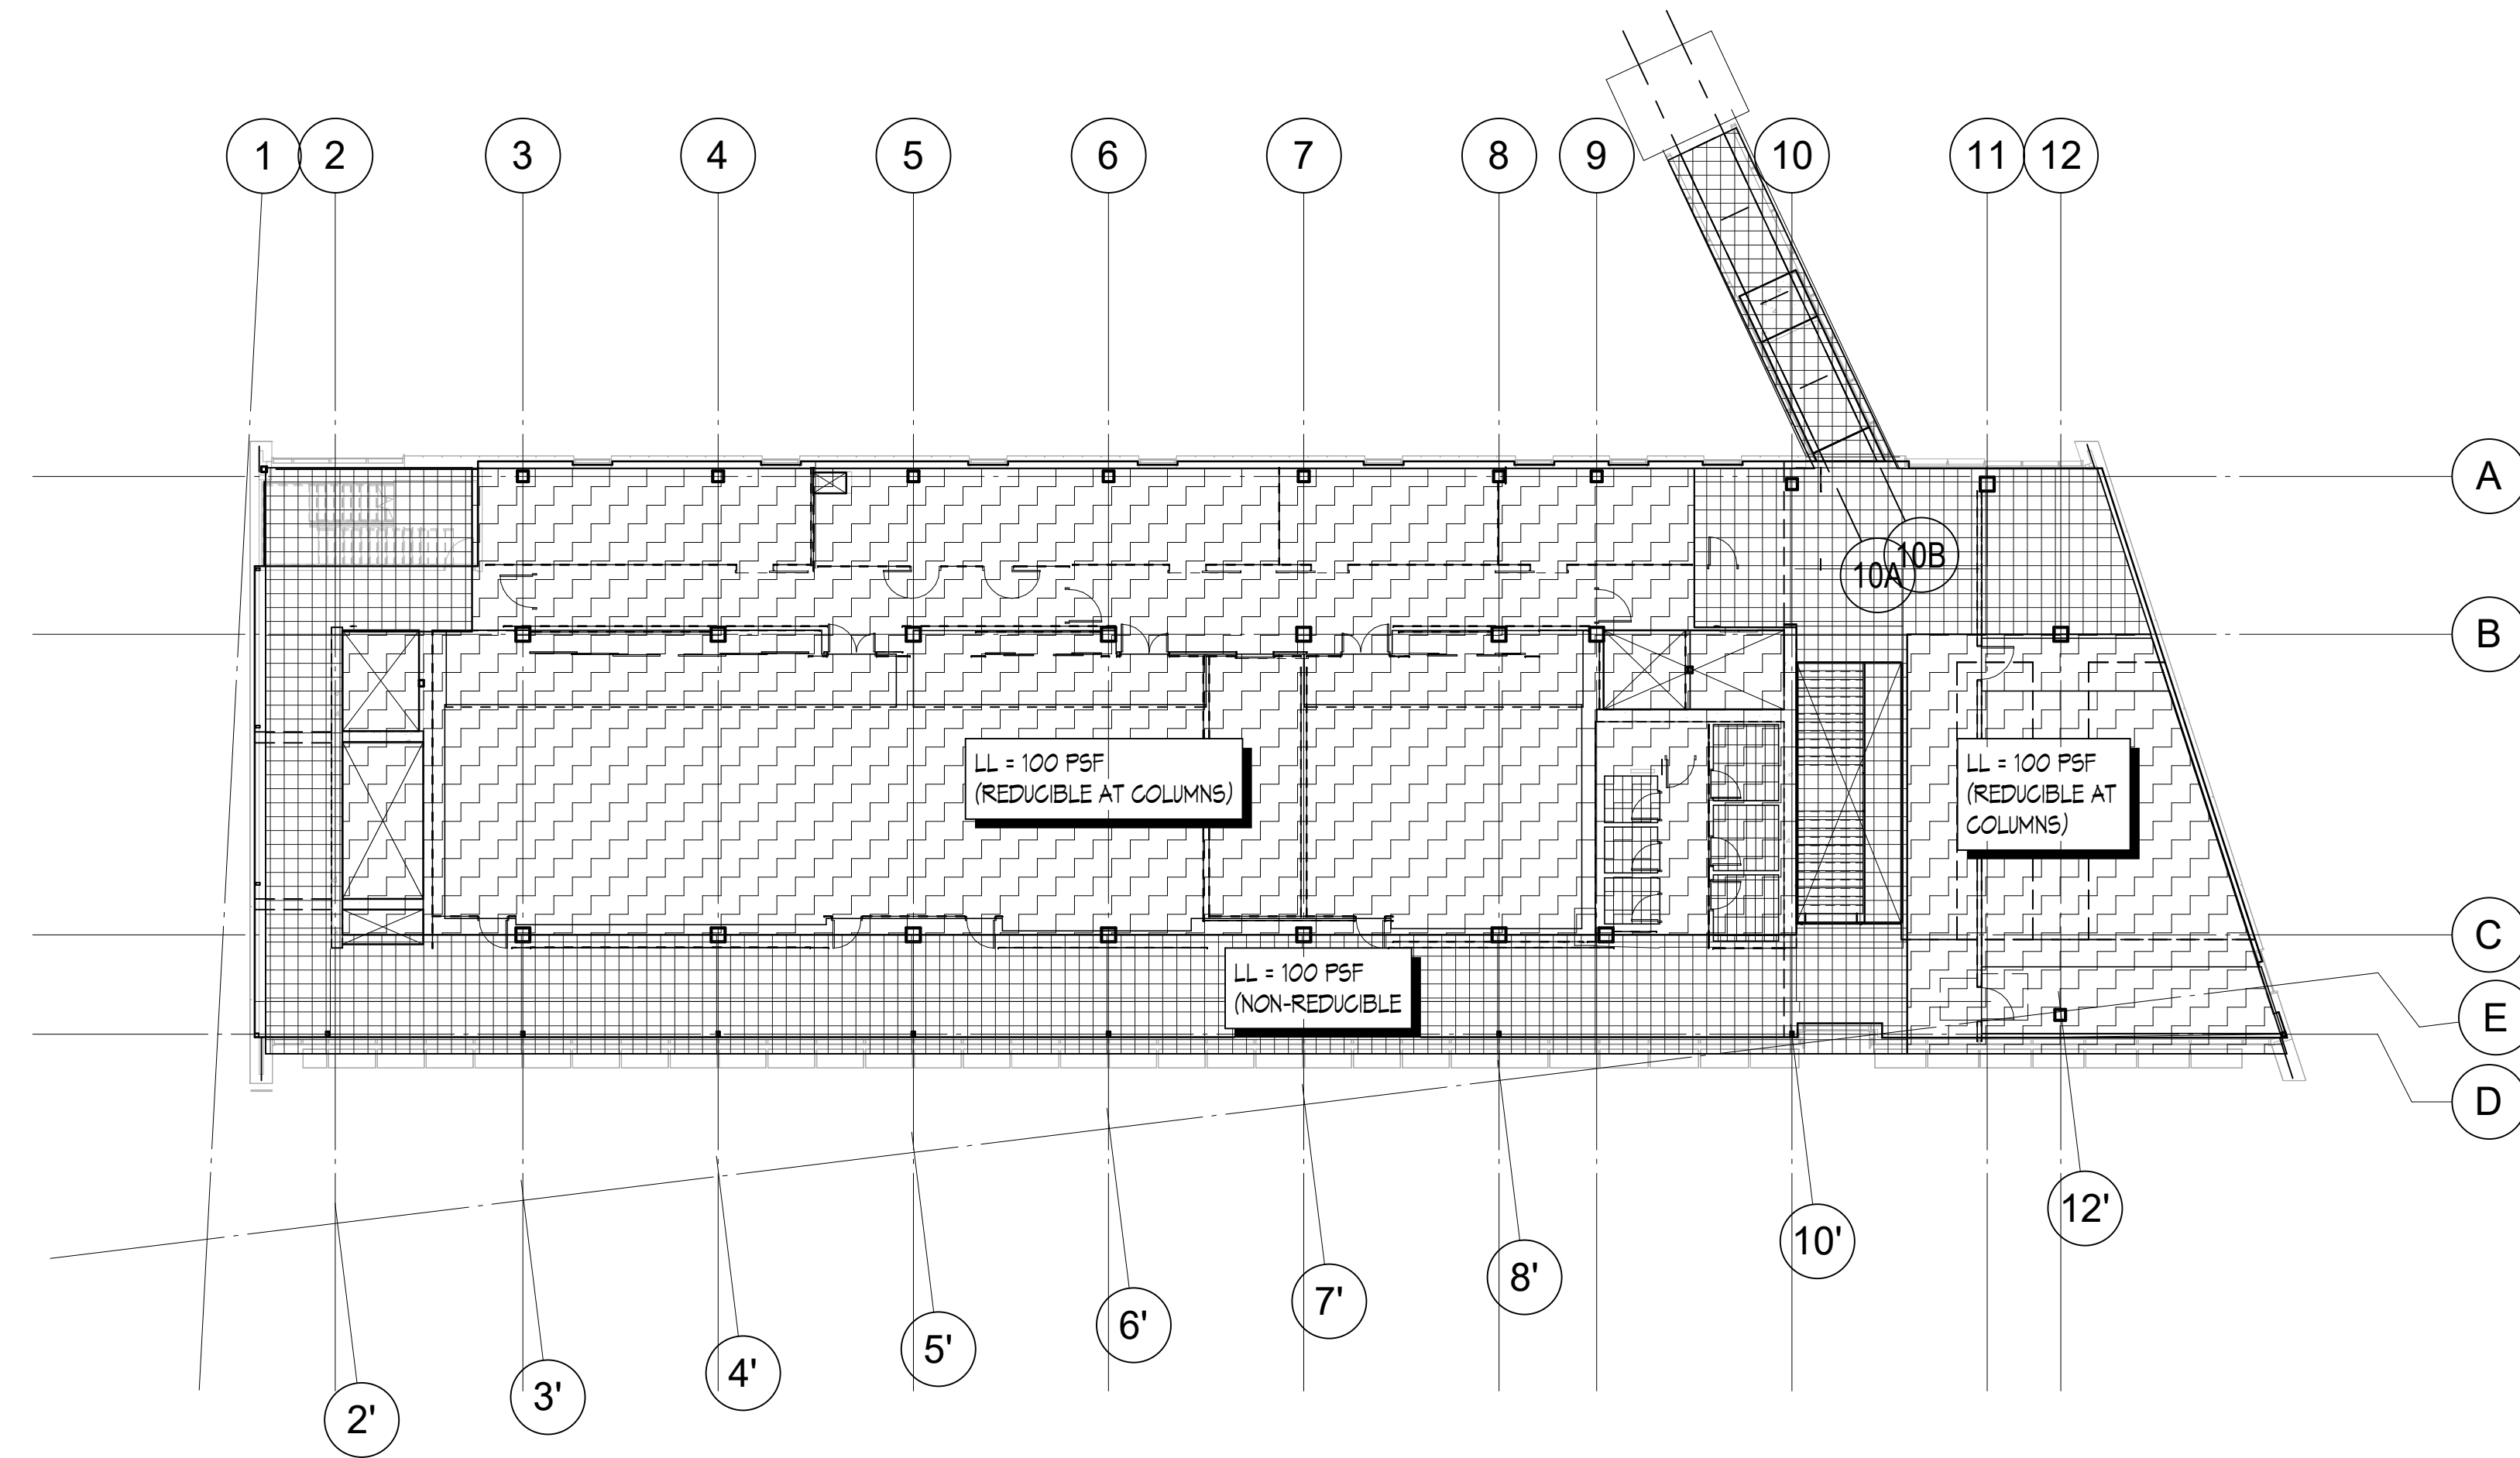


2 LEVEL 4 - LIVE LOAD
1/16" = 1'-0"

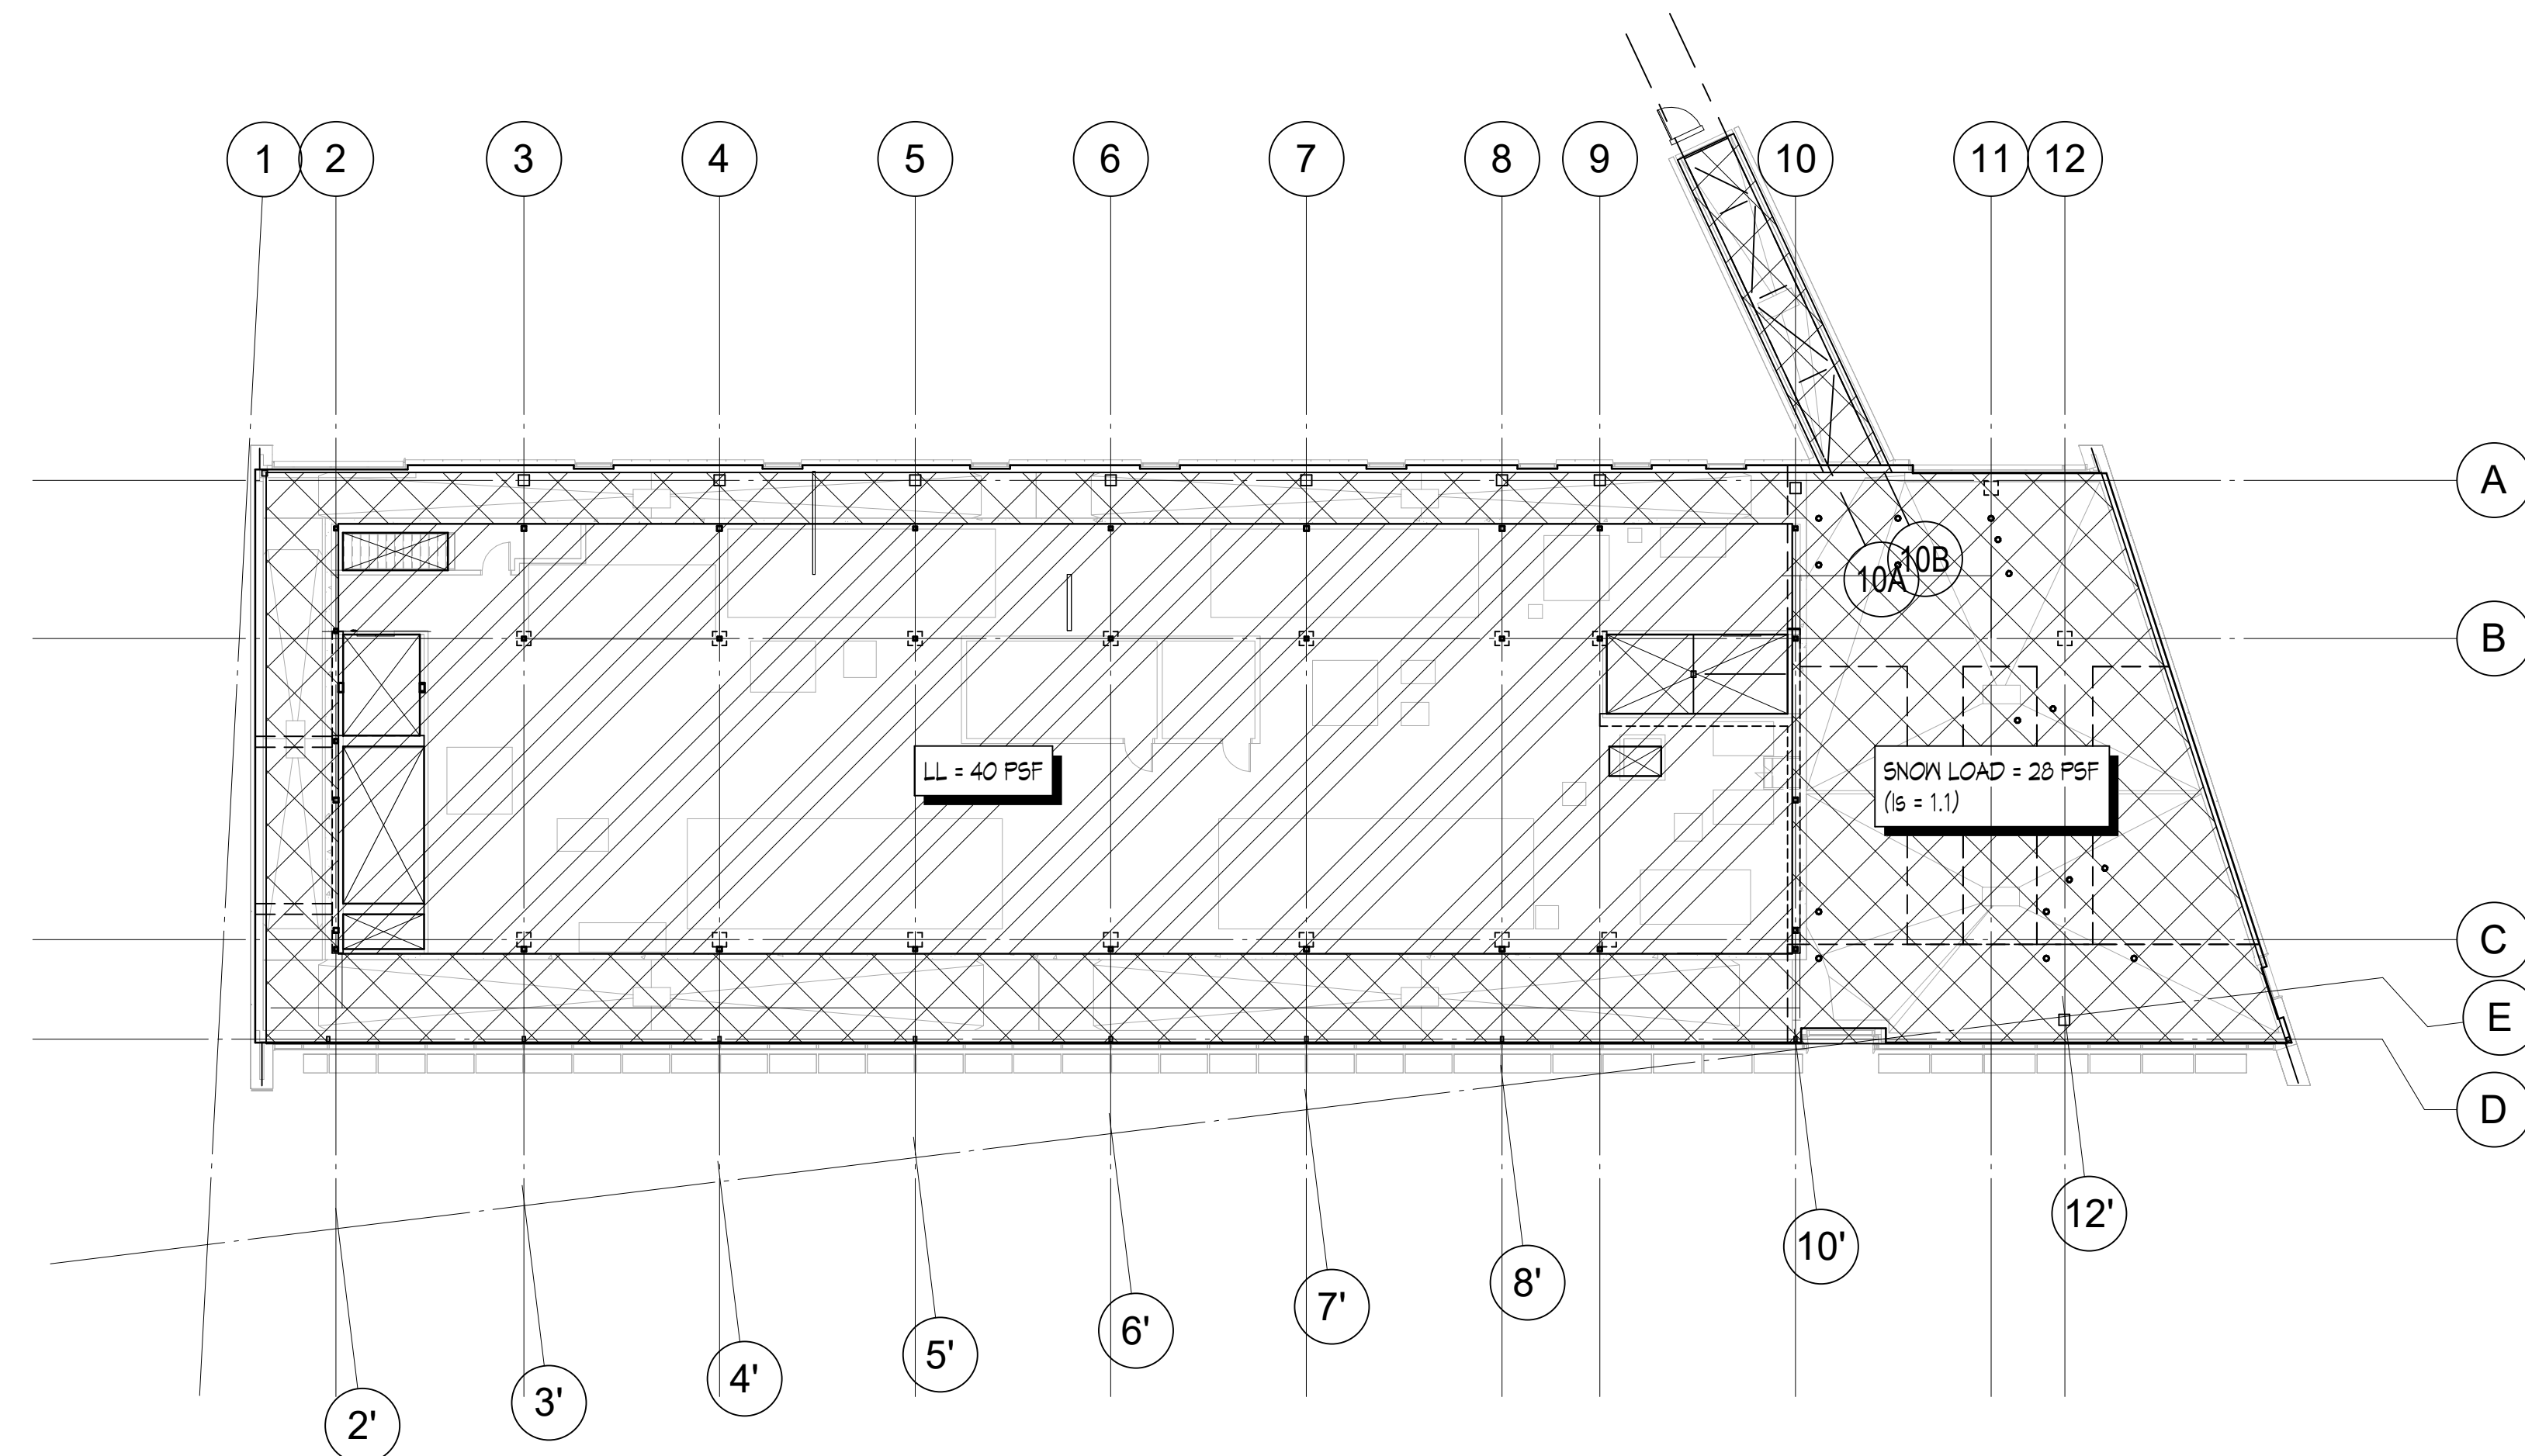


4 PENTHOUSE - LIVE LOAD
1/16" = 1'-0"

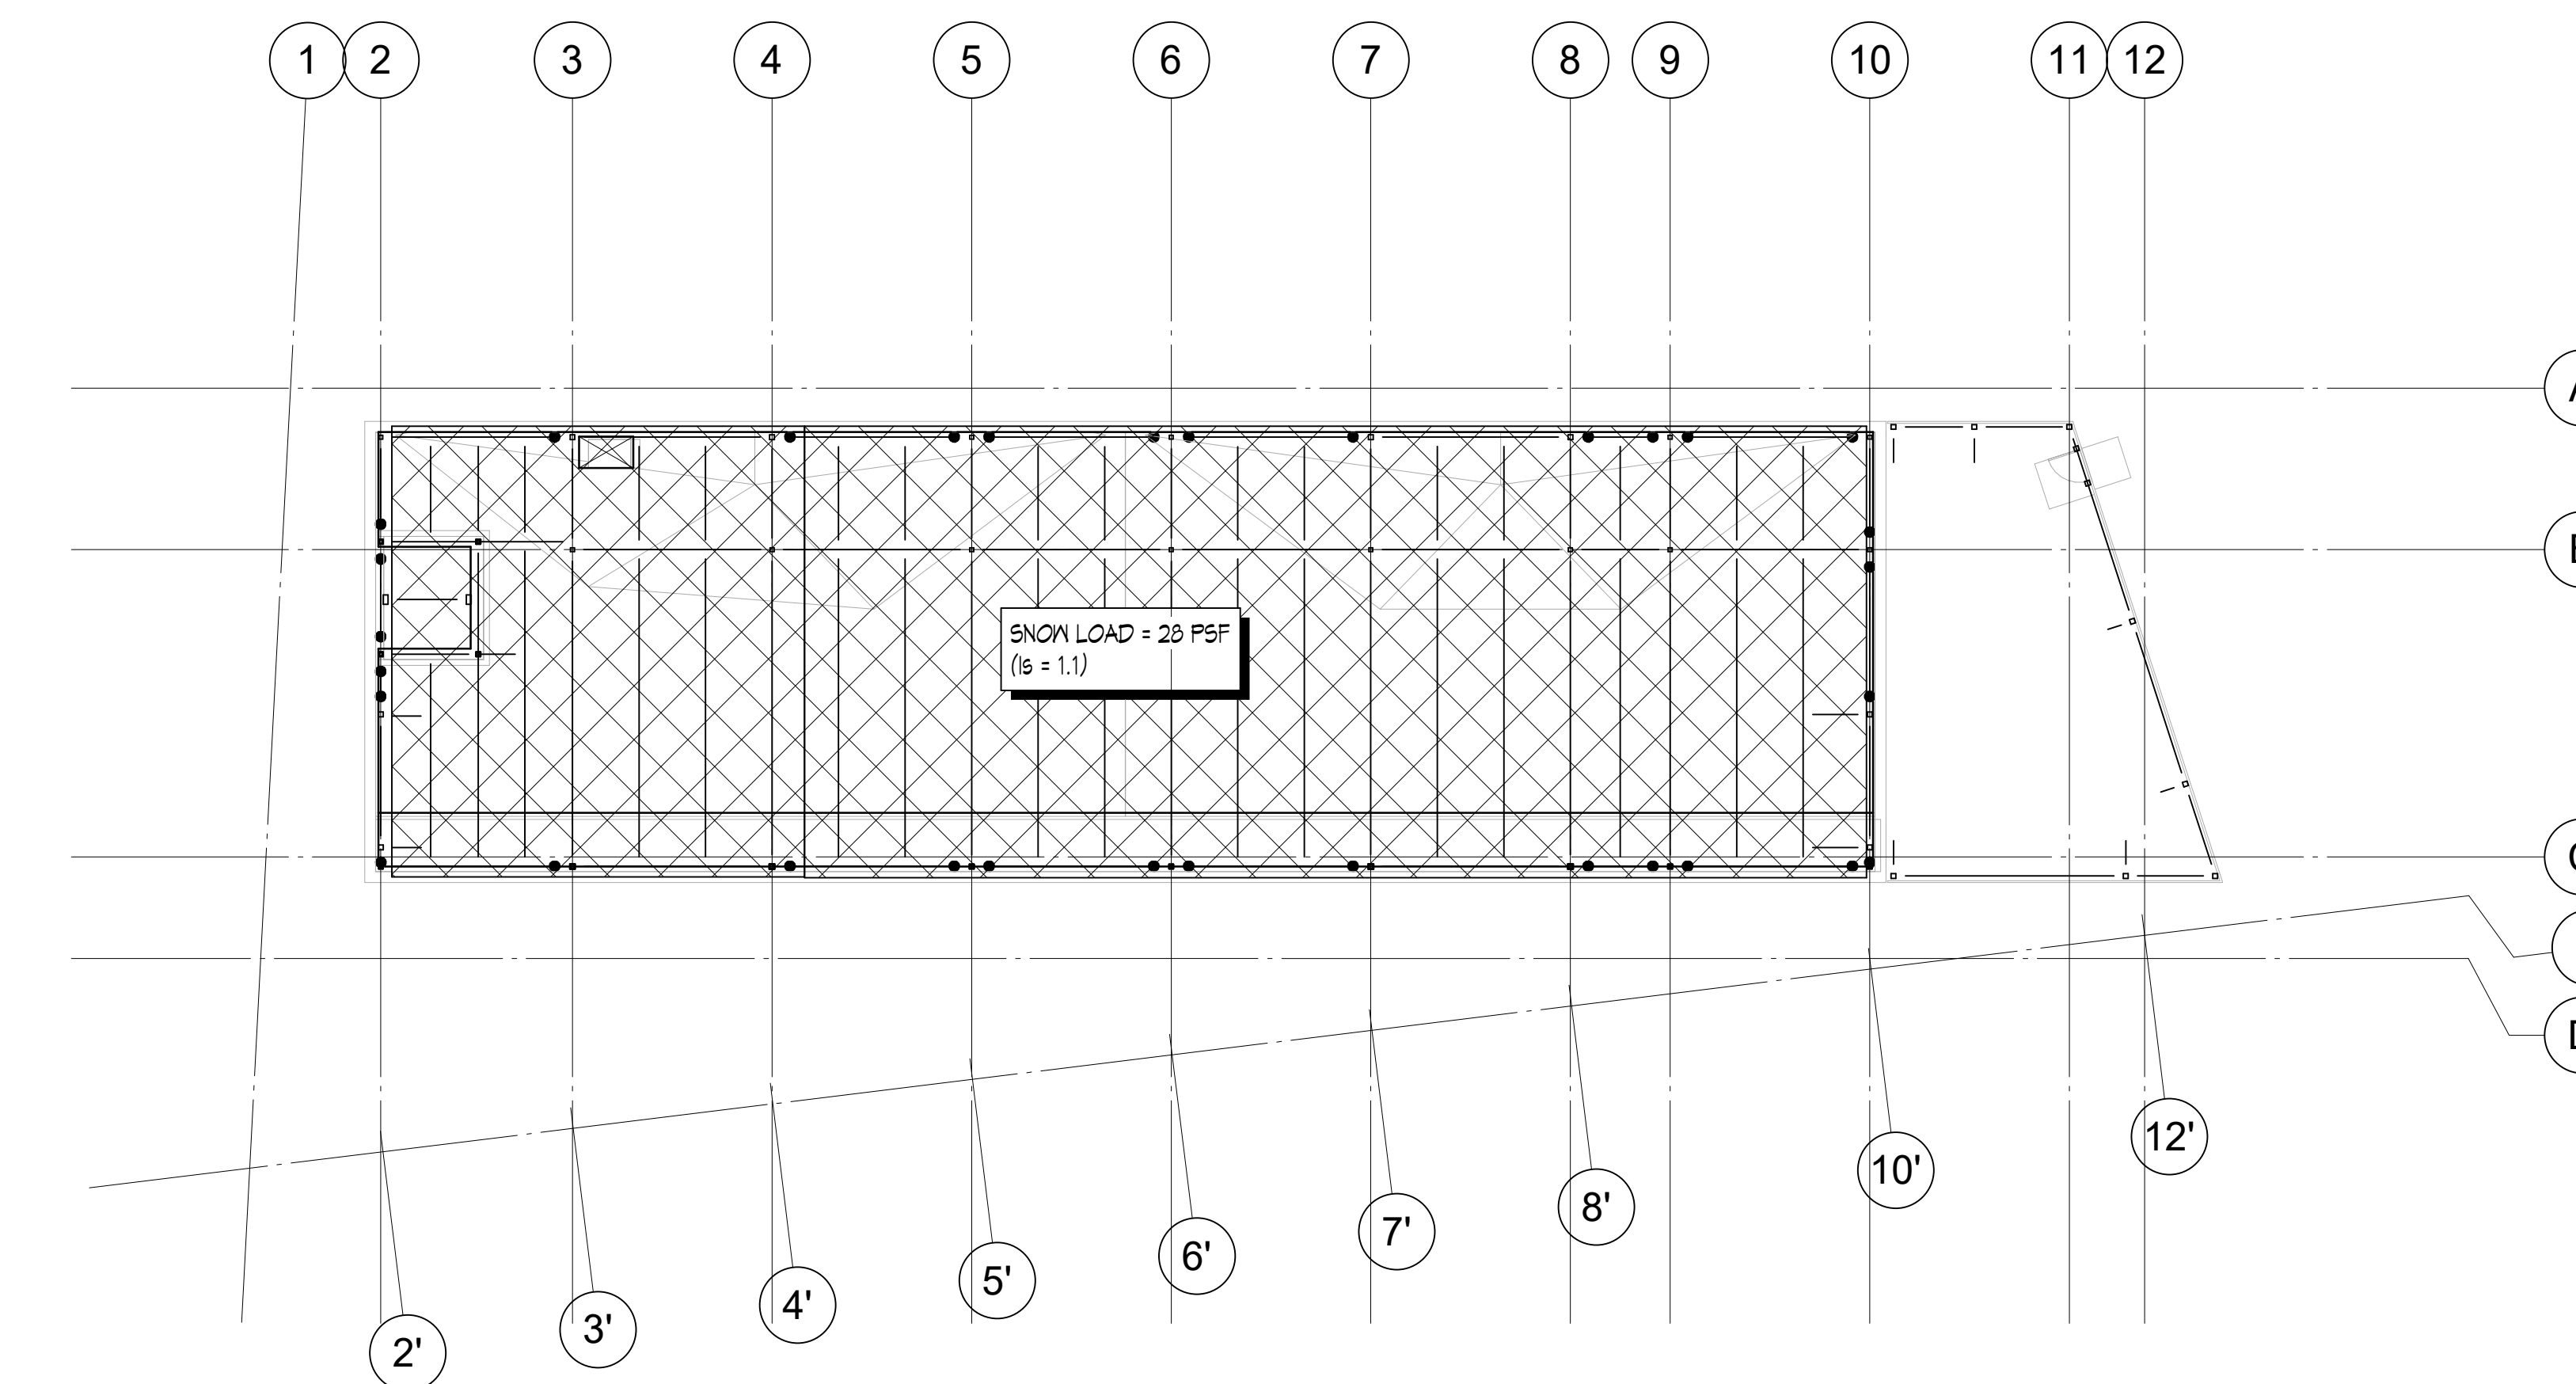

6 ROOF - LIVE LOAD
1/16" = 1'-0"

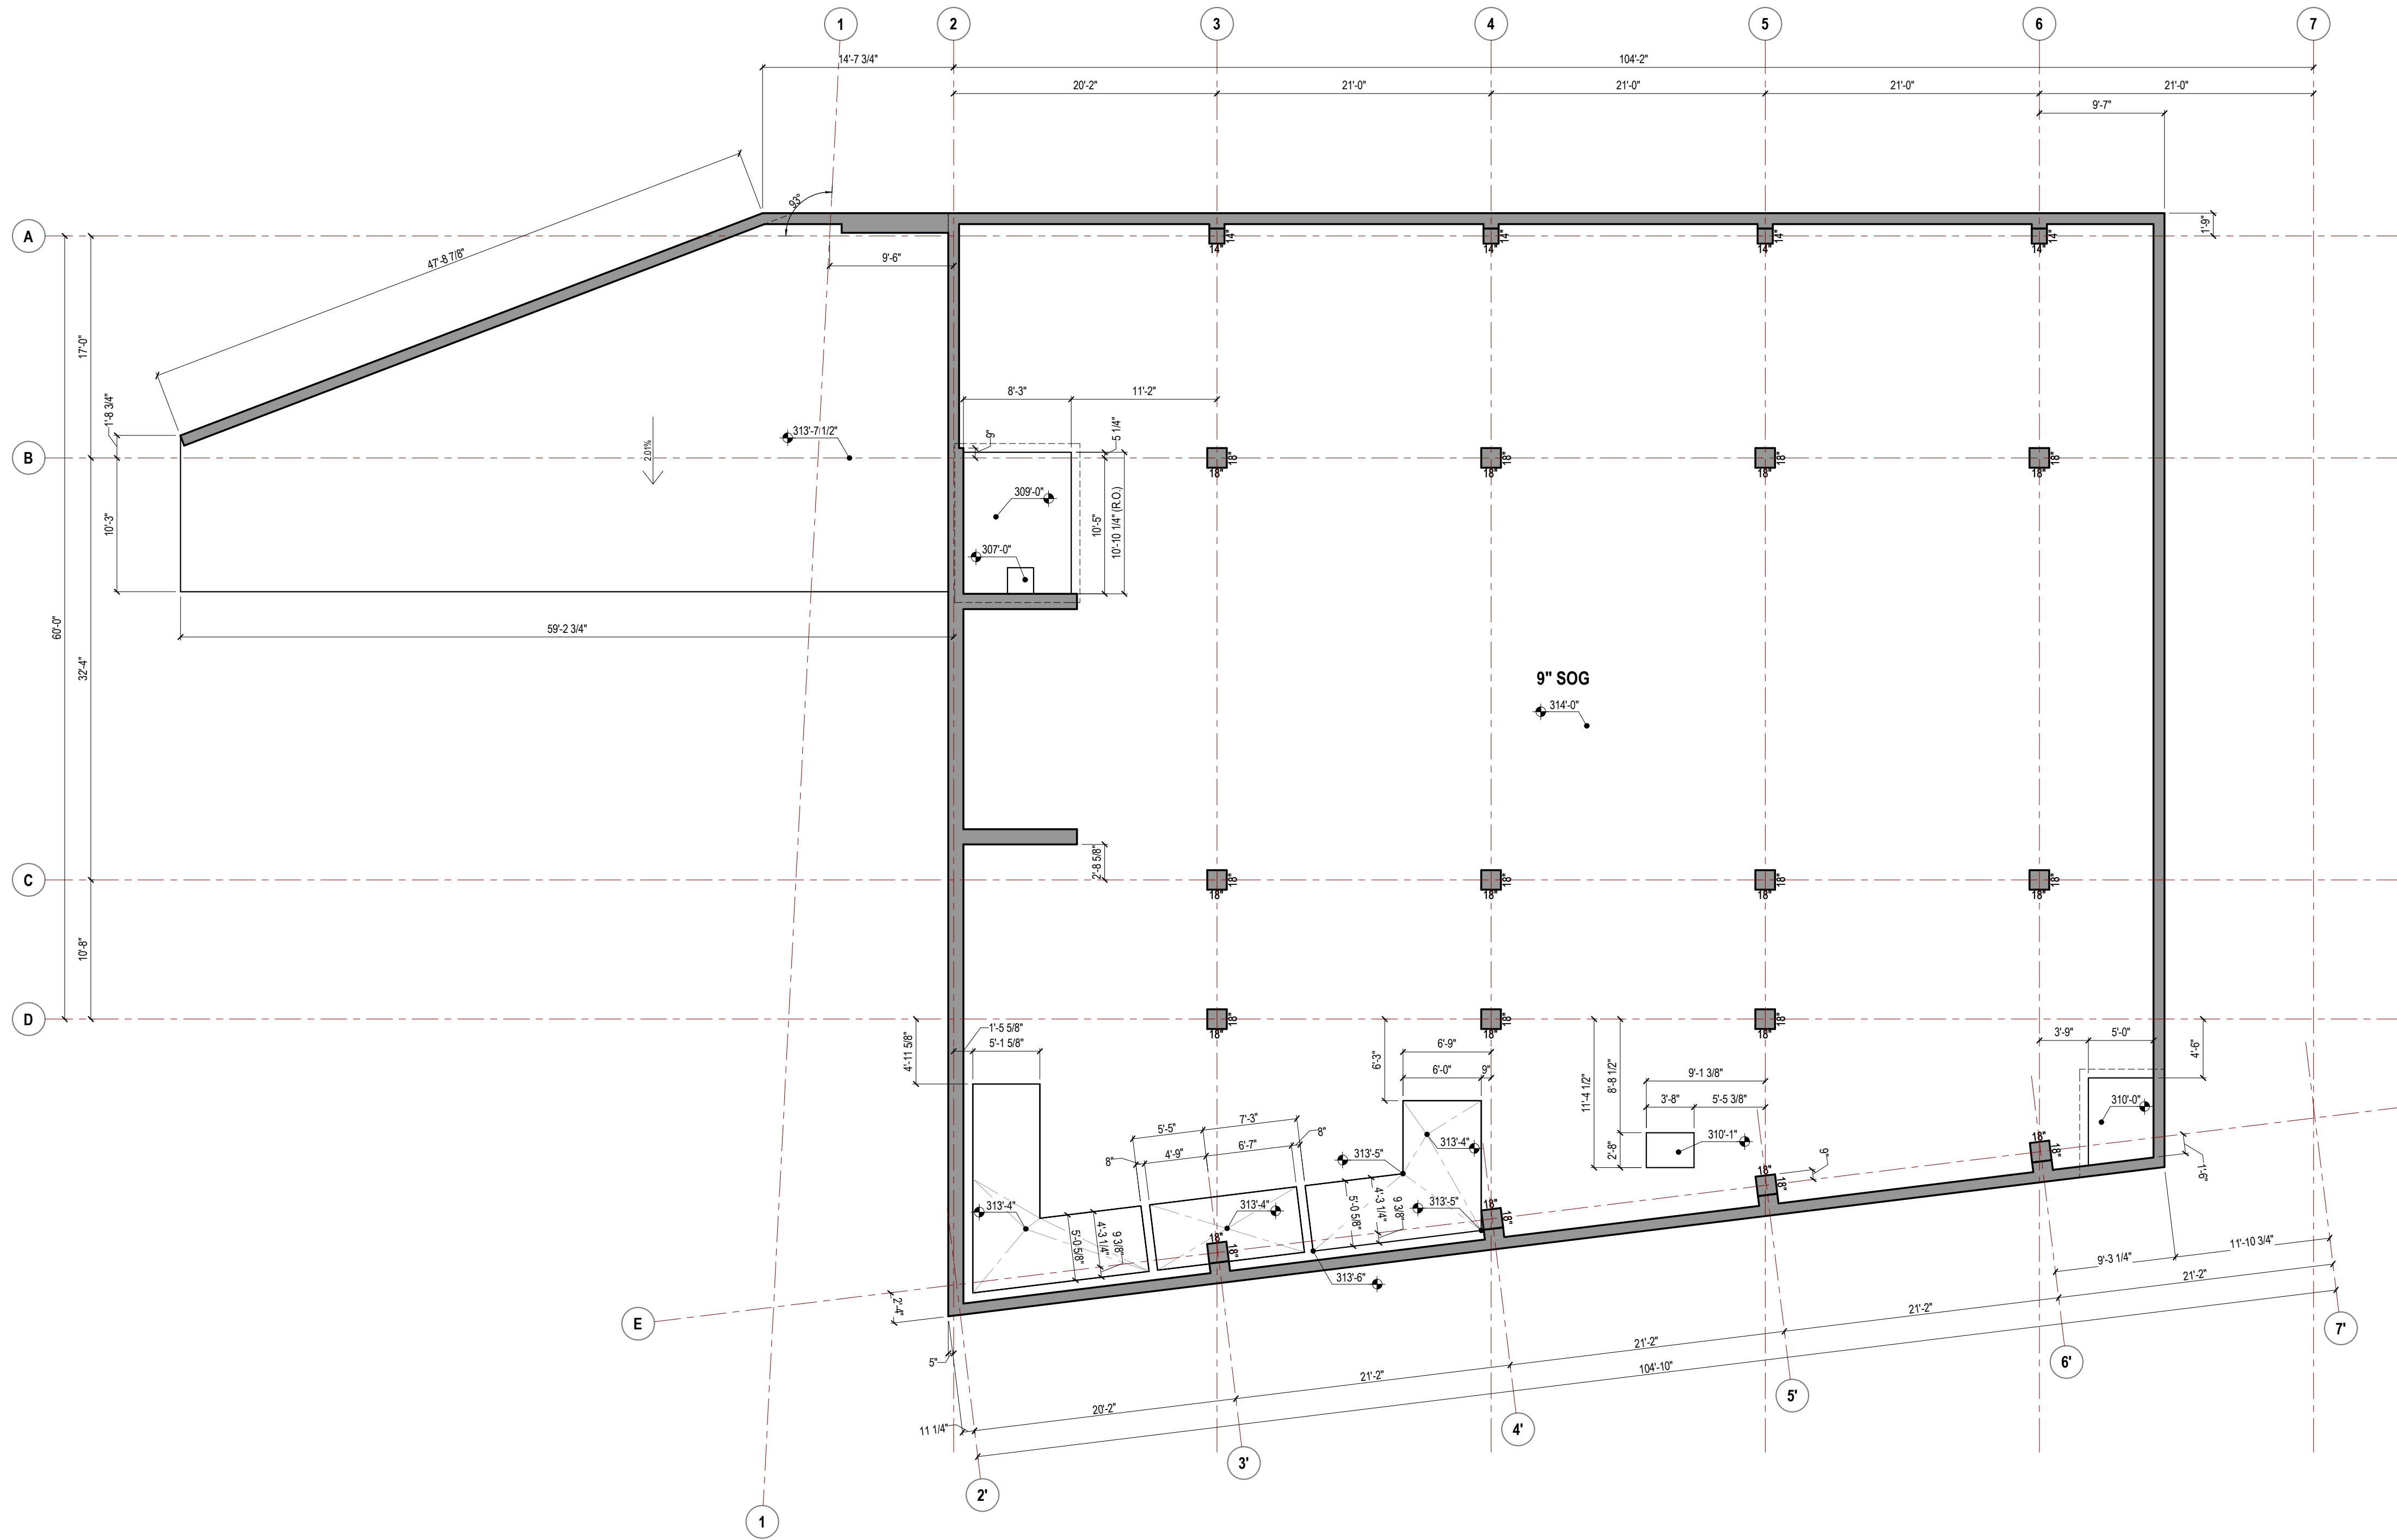


1 LEVEL-1 SLAB ON GRADE FLOOR PLAN
REF: 311.10
1/8" = 1'-0"

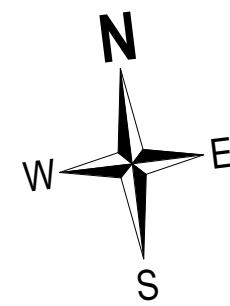

- NOTES:**
- 3/4" CHAMFER ON ALL EXPOSED CONCRETE CORNERS TYP.
 - ALL COLUMNS ARE CENTERED ON GRID LINES U.N.O.
 - ALL BEAMS ARE CENTERED ON GRID LINES U.N.O.
 - SLAB ON GRADE THICKNESS IS 9" TYP. U.N.O.


SYMBOLS		SHADE DESIGNATIONS	
1-BOX (ROUND-ENDS) TOP OF CONCRETE ELEVATIONS	(TOP ELEV)	BEAM OR DROP CAP	
1-BOX BOTTOM OF CONCRETE ELEVATIONS	(BOT ELEV)	WALLS OR COLUMNS	
2-BOX (PLAN VIEWS) TOP & BOTTOM ELEVATIONS D = DEPTH OF CONC. MEMBER	(TOP ELEV) (BOT ELEV)	CMU WALLS	
3-BOX (FLOOR PLANS) TOP & BOTTOM ELEVATIONS COLUMN ELEVATION ABOVE REF. LEVEL D = DEPTH OF CONC. MEMBER	(TOP ELEV) (BOT ELEV) (TO COL. ELEV)	DELAY STRIP OR CLOSURE POUR	
SECTION VIEW		GRADE OR SOIL	
ELEVATION VIEW		Y" PT/MS/CIP SLAB	
		Z" PT/MS/CIP SLAB	
LEGEND		LINE DESIGNATIONS	
		INDICATES TOP OF SLAB CHANGE OR EDGE OF SLAB	
		INDICATES SOFFIT CHANGE	
		INDICATES CONSTRUCTION JOINT	
		INDICATES GRID LINE	

2 3D-VIEW

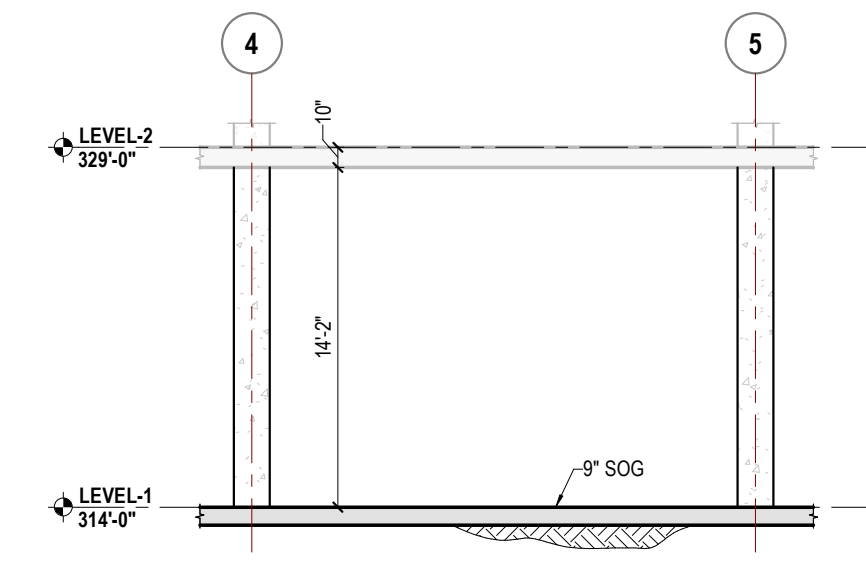


3 BUILDING SECTION
1/8" = 1'-0"


THIS DRAWING IS FOR THE EXCLUSIVE USE OF MCCLONE CONSTRUCTION COMPANY. ON THIS PROJECT ONLY. UTILIZATION OF THIS DRAWING BY OTHER PARTIES AND/OR ON OTHER PROJECTS WITHOUT THE EXPRESSED WRITTEN CONSENT OF MCCLONE CONSTRUCTION COMPANY IS STRICTLY PROHIBITED.

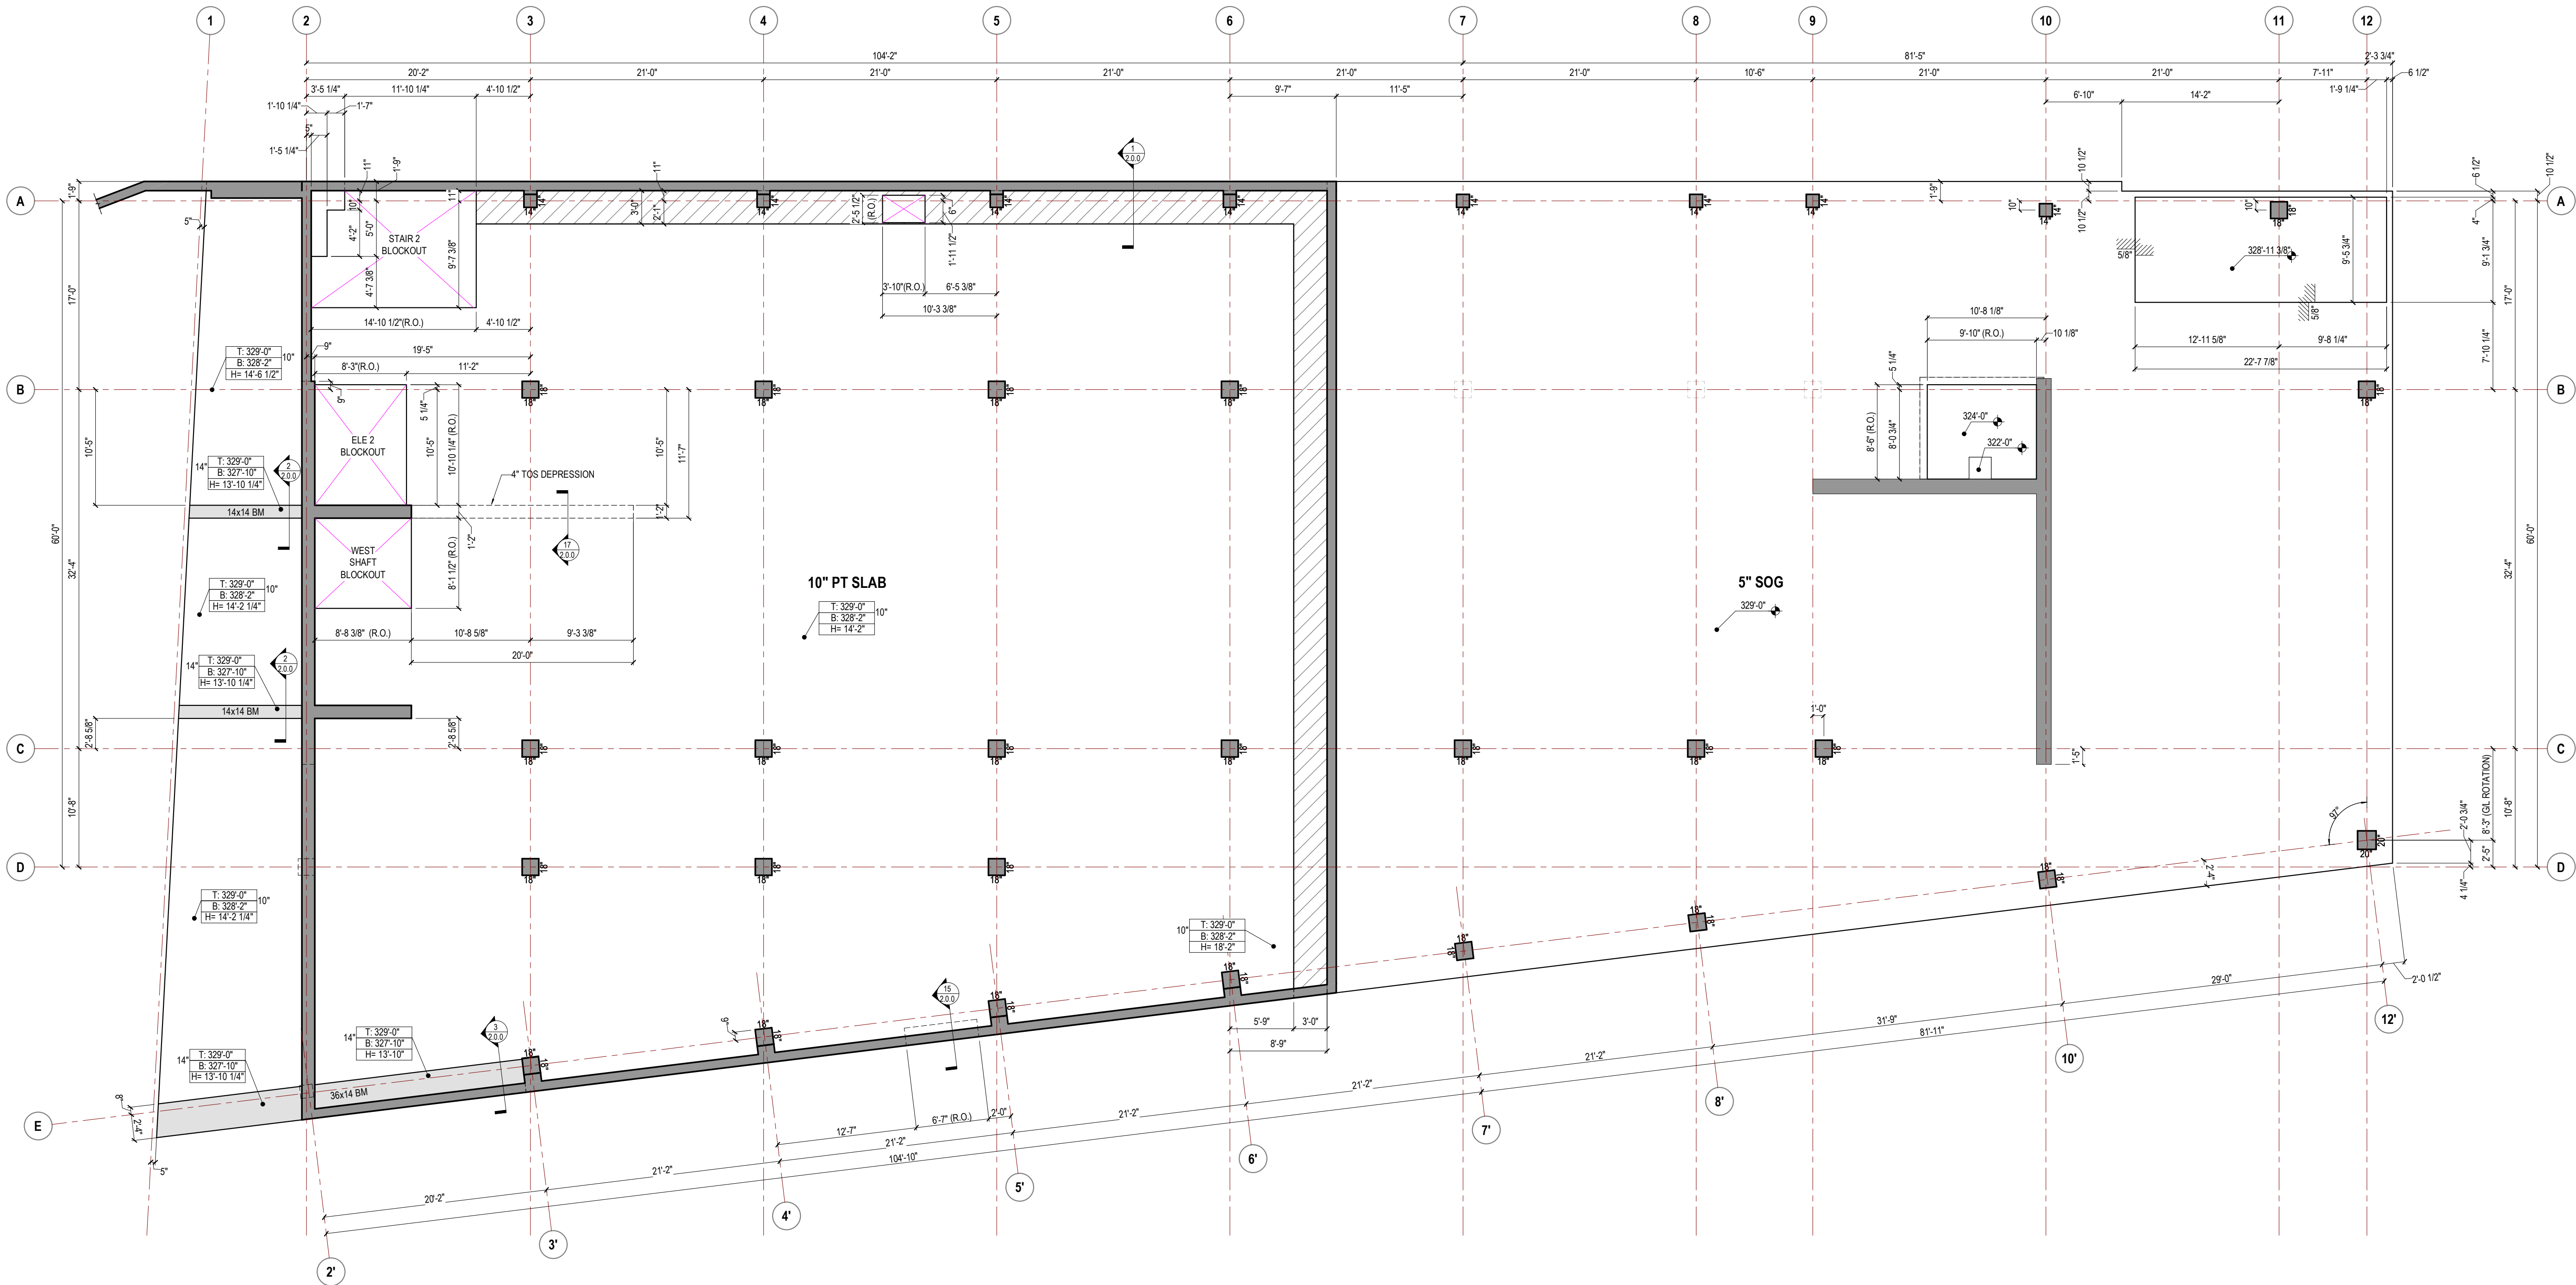


1 LEVEL-2 SOFFIT PLAN
REF: 311.1.0
1/8" = 1'-0"

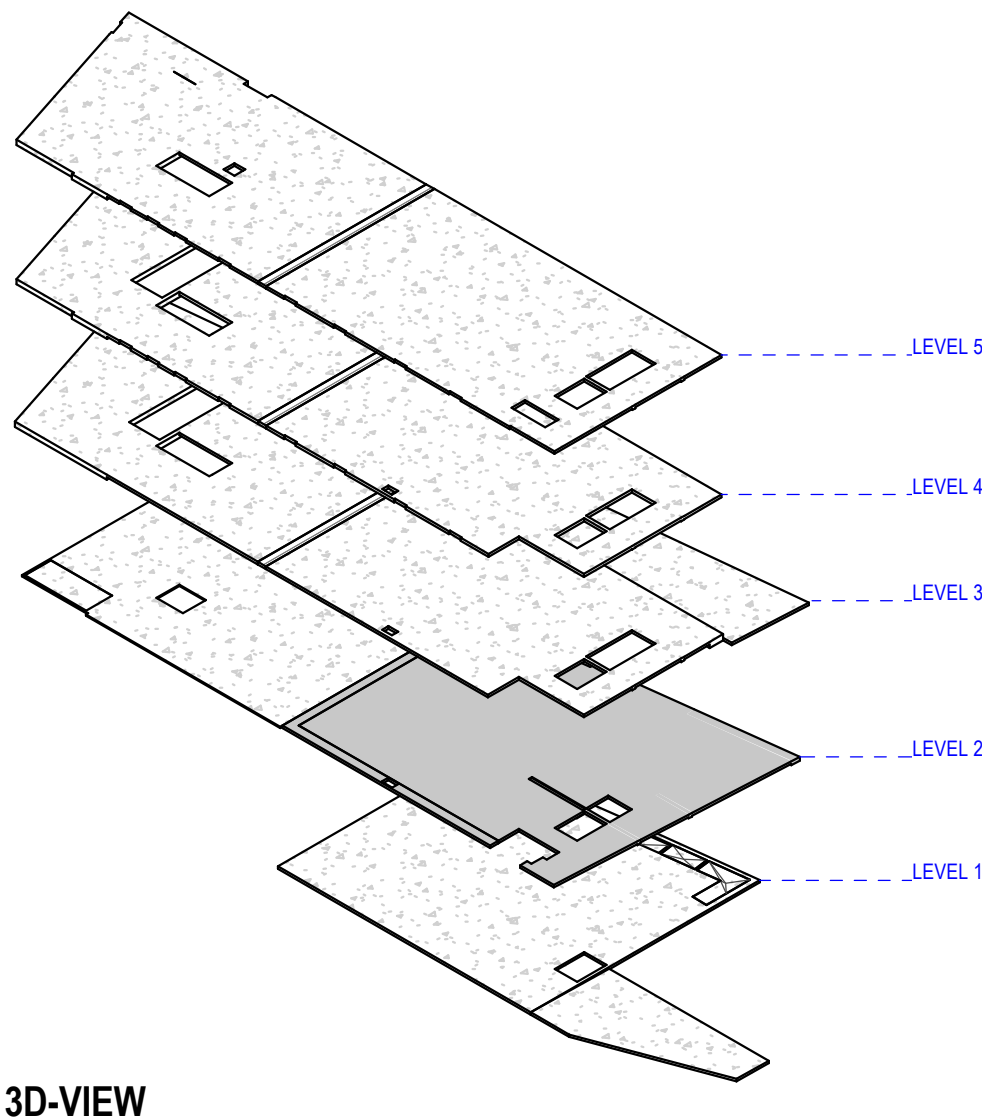

2 3D-VIEW

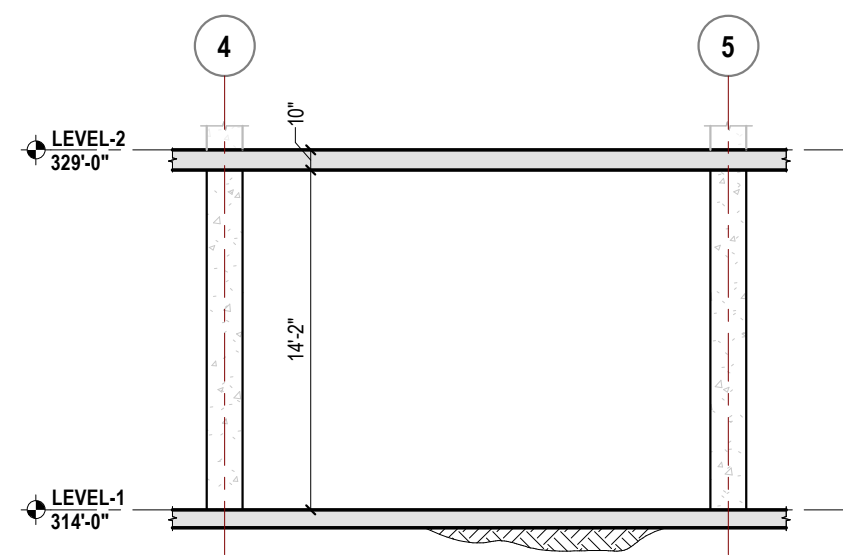

3 BUILDING SECTION
1/8" = 1'-0"

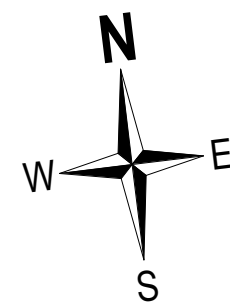

NOTES:

- 3/4" CHAMFER ON ALL EXPOSED CONCRETE CORNERS TYP.
- ALL COLUMNS ARE CENTERED ON GRID LINES U.N.O.
- ALL BEAMS ARE CENTERED ON GRID LINES U.N.O.
- SLAB THICKNESS IS 10" TYP. U.N.O.

LEGEND

SYMBOLS

- 1-BOX (ROUND-ENDS)
TOP OF CONCRETE ELEVATIONS
- 1-BOX
BOTTOM OF CONCRETE ELEVATIONS
- 2-BOX (PLAN VIEWS)
TOP & BOTTOM ELEVATIONS
D - DEPTH OF CONC. MEMBER
- 3-BOX (FLOOR PLANS)
TOP & BOTTOM ELEVATIONS
COLUMN ELEVATION ABOVE REF. LEVEL
D - DEPTH OF CONC. MEMBER

SECTION VIEW

- SHEET NUMBER
- DETAIL NUMBER
- ELEVATION VIEW
- SHEET NUMBER
- DETAIL NUMBER


SHADE DESIGNATIONS

- BEAM OR DROP CAP
- WALLS OR COLUMNS
- CMU WALLS
- DELAY STRIP OR CLOSURE POUR
- GRADE OR SOIL
- Y" PTMS/CIP SLAB
- Z" PTMS/CIP SLAB


LINE DESIGNATIONS

- INDICATES TOP OF SLAB CHANGE OR EDGE OF SLAB
- INDICATES SOFFIT CHANGE
- INDICATES CONSTRUCTION JOINT
- INDICATES GRID LINE


THIS DRAWING IS FOR THE EXCLUSIVE USE OF MCCLONE CONSTRUCTION COMPANY. ON THIS PROJECT ONLY. UTILIZATION OF THIS DRAWING BY OTHER PARTIES AND/OR OTHER PROJECTS WITHOUT THE EXPRESSED WRITTEN CONSENT OF MCCLONE CONSTRUCTION COMPANY IS STRICTLY PROHIBITED.

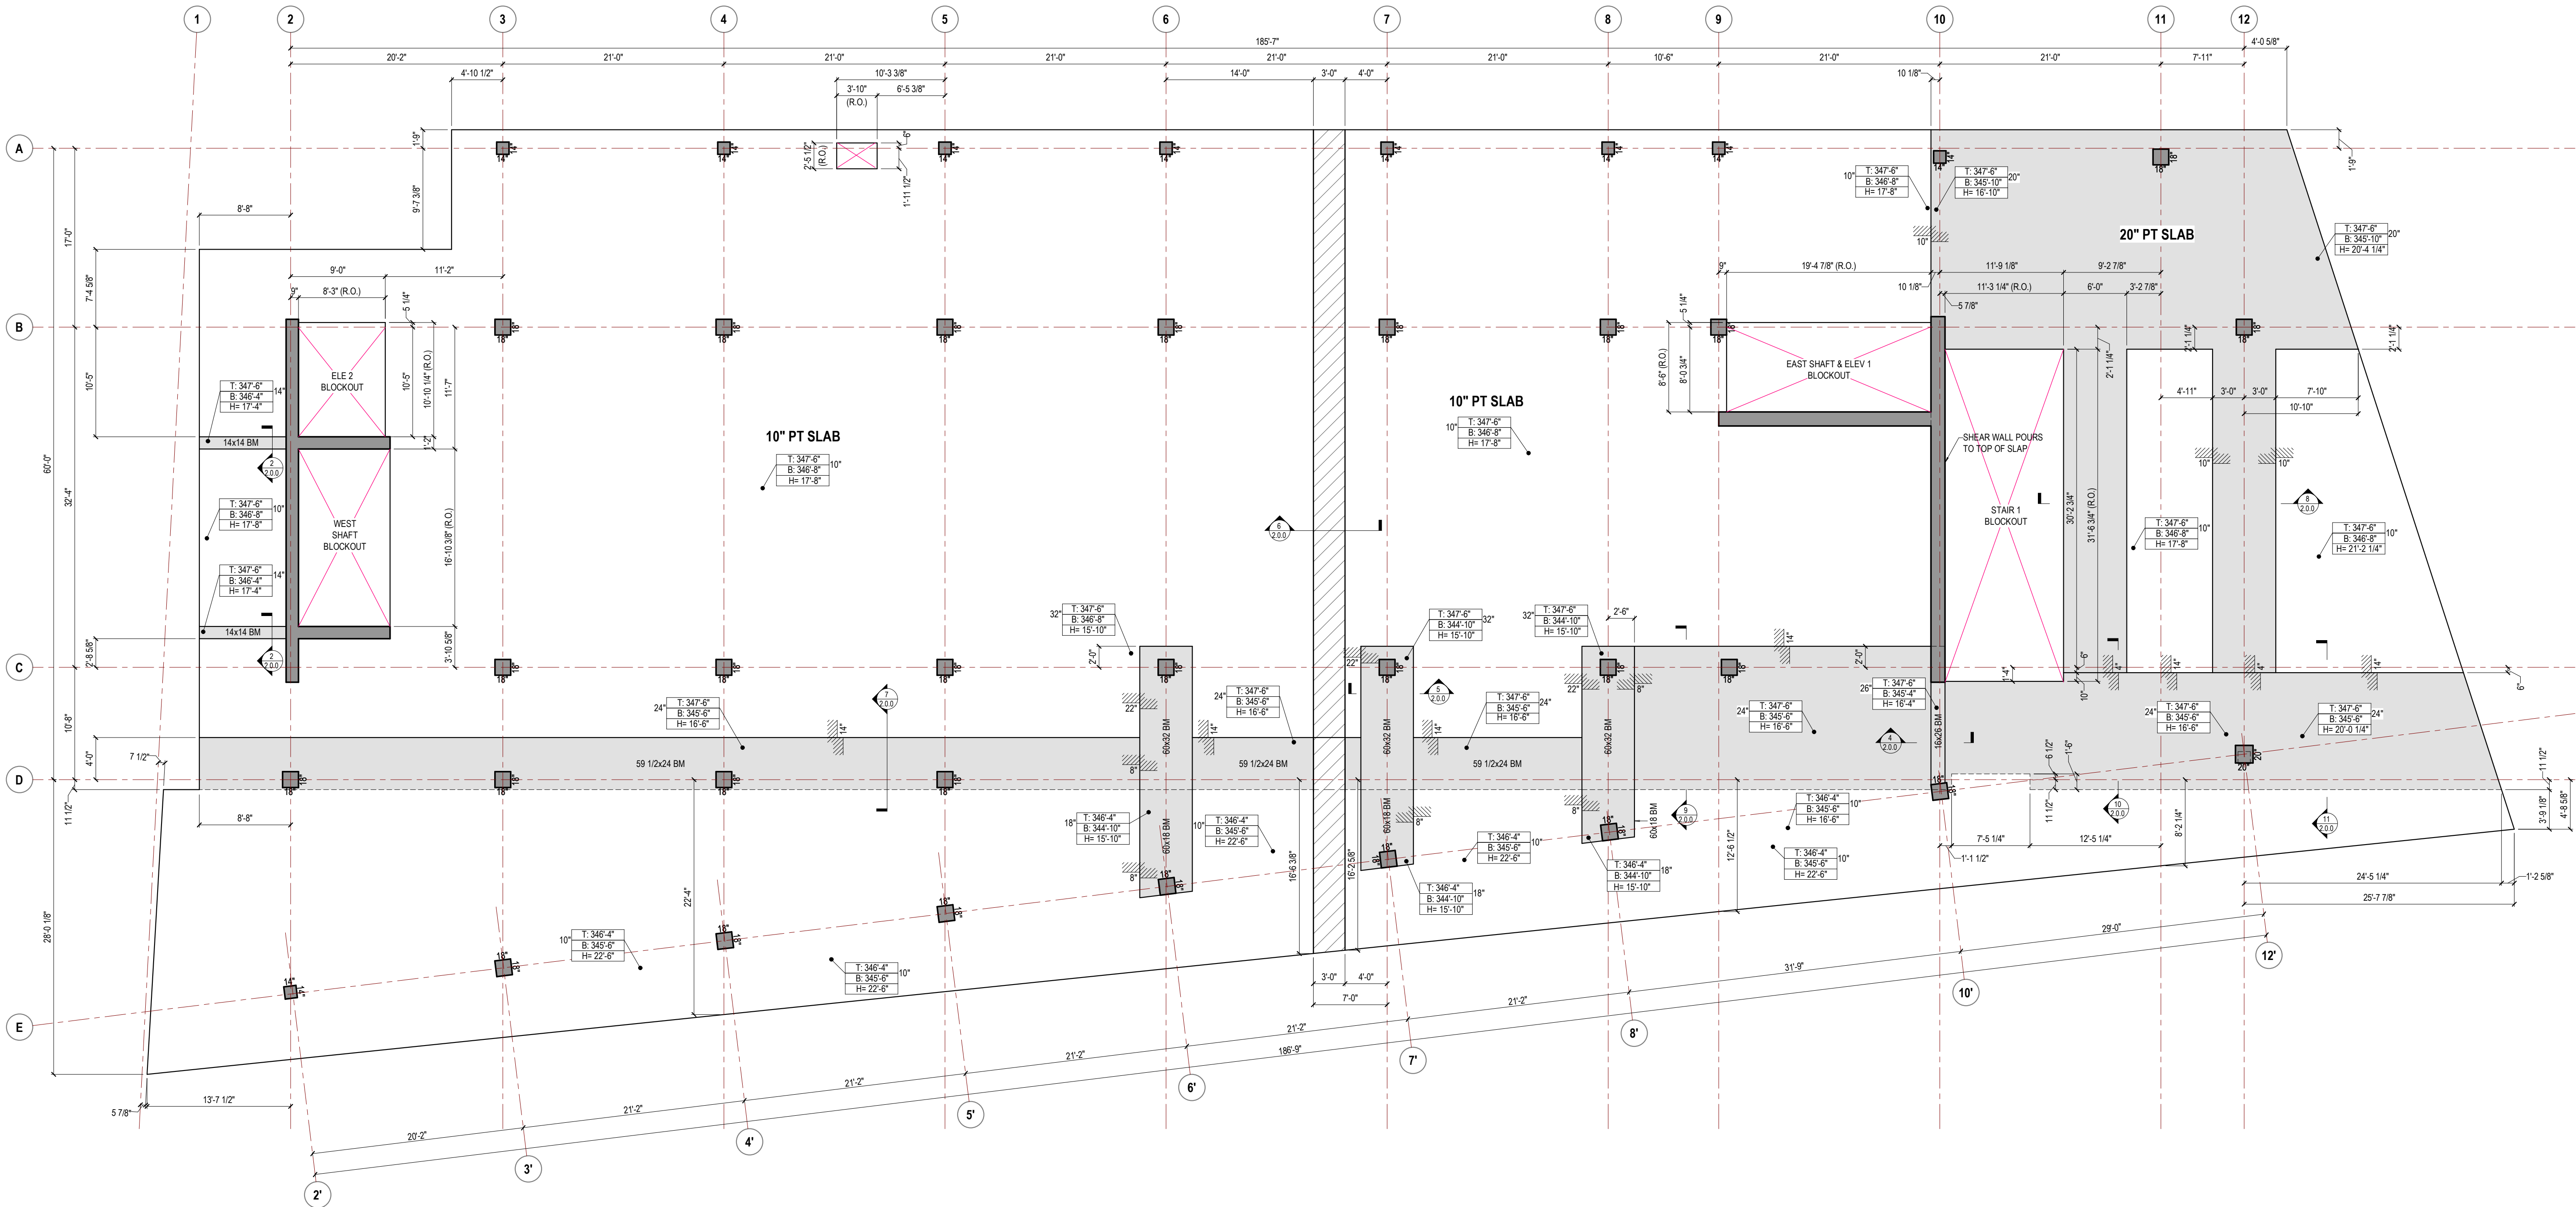


1 LEVEL-3 SOFFIT PLAN
REF: 3/11/20

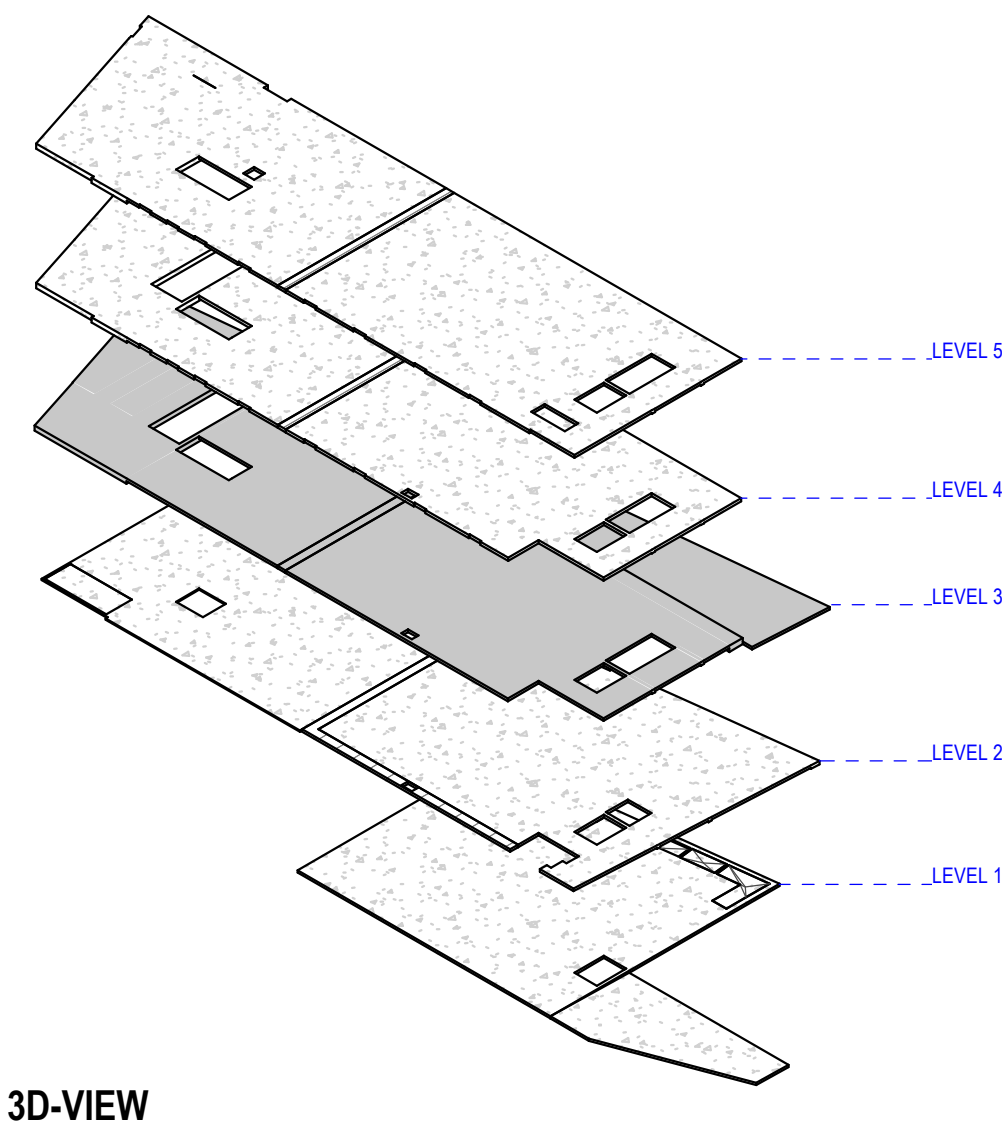

2 3D-VIEW

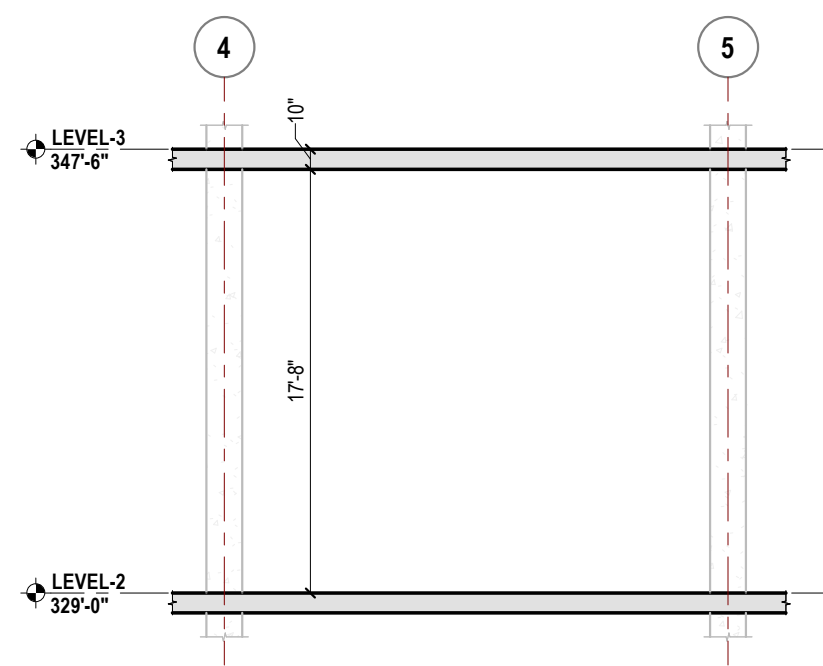

3 BUILDING SECTION
1/8" = 1'-0"

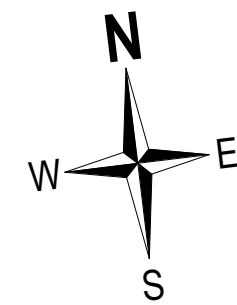

NOTES:

1. 3/4" CHAMFER ON ALL EXPOSED CONCRETE CORNERS TYP.
2. ALL COLUMNS ARE CENTERED ON GRID LINES U.N.O.
3. ALL BEAMS ARE CENTERED ON GRID LINES U.N.O.
4. SLAB THICKNESS IS 10" TYP. U.N.O.

LEGEND

SYMBOLS

- 1-BOX (ROUND-ENDS)
TOP OF CONCRETE ELEVATIONS
- 2-BOX (PLAN VIEWS)
TOP & BOTTOM ELEVATIONS
D = DEPTH OF CONC. MEMBER
- 3-BOX (SOFFIT PLANS)
TOP & BOTTOM ELEVATIONS
HEIGHT BELOW REFERENCE LEVEL
D = DEPTH OF CONC. MEMBER

- SECTION VIEW
SHEET NUMBER
- ELEVATION VIEW
SHEET NUMBER

SHADE DESIGNATIONS


- BEAM OR DROP CAP
- WALLS OR COLUMNS
- CMU WALLS
- DELAY STRIP OR CLOSURE POUR
- GRADE OR SOIL
- Y" PTMS/CIP SLAB
- Z" PTMS/CIP SLAB

LINE DESIGNATIONS


- INDICATES TOP OF SLAB CHANGE OR EDGE OF SLAB
- INDICATES SOFFIT CHANGE
- INDICATES CONSTRUCTION JOINT
- INDICATES GRID LINE

THIS DRAWING IS FOR THE EXCLUSIVE USE OF MCCLONE CONSTRUCTION COMPANY. ON THIS PROJECT ONLY. UTILIZATION OF THIS DRAWING BY OTHER PARTIES AND/OR OTHER PROJECTS WITHOUT THE EXPRESSED WRITTEN CONSENT OF MCCLONE CONSTRUCTION COMPANY IS STRICTLY PROHIBITED.


PLOT DATE/TIME STAMP: 11/11/2020 3:59:30 PM
Z:\Shared\Projects\1147 WWU - ISBMC EKGEDrawings\Sheet Models\WWU-SSB.mxd

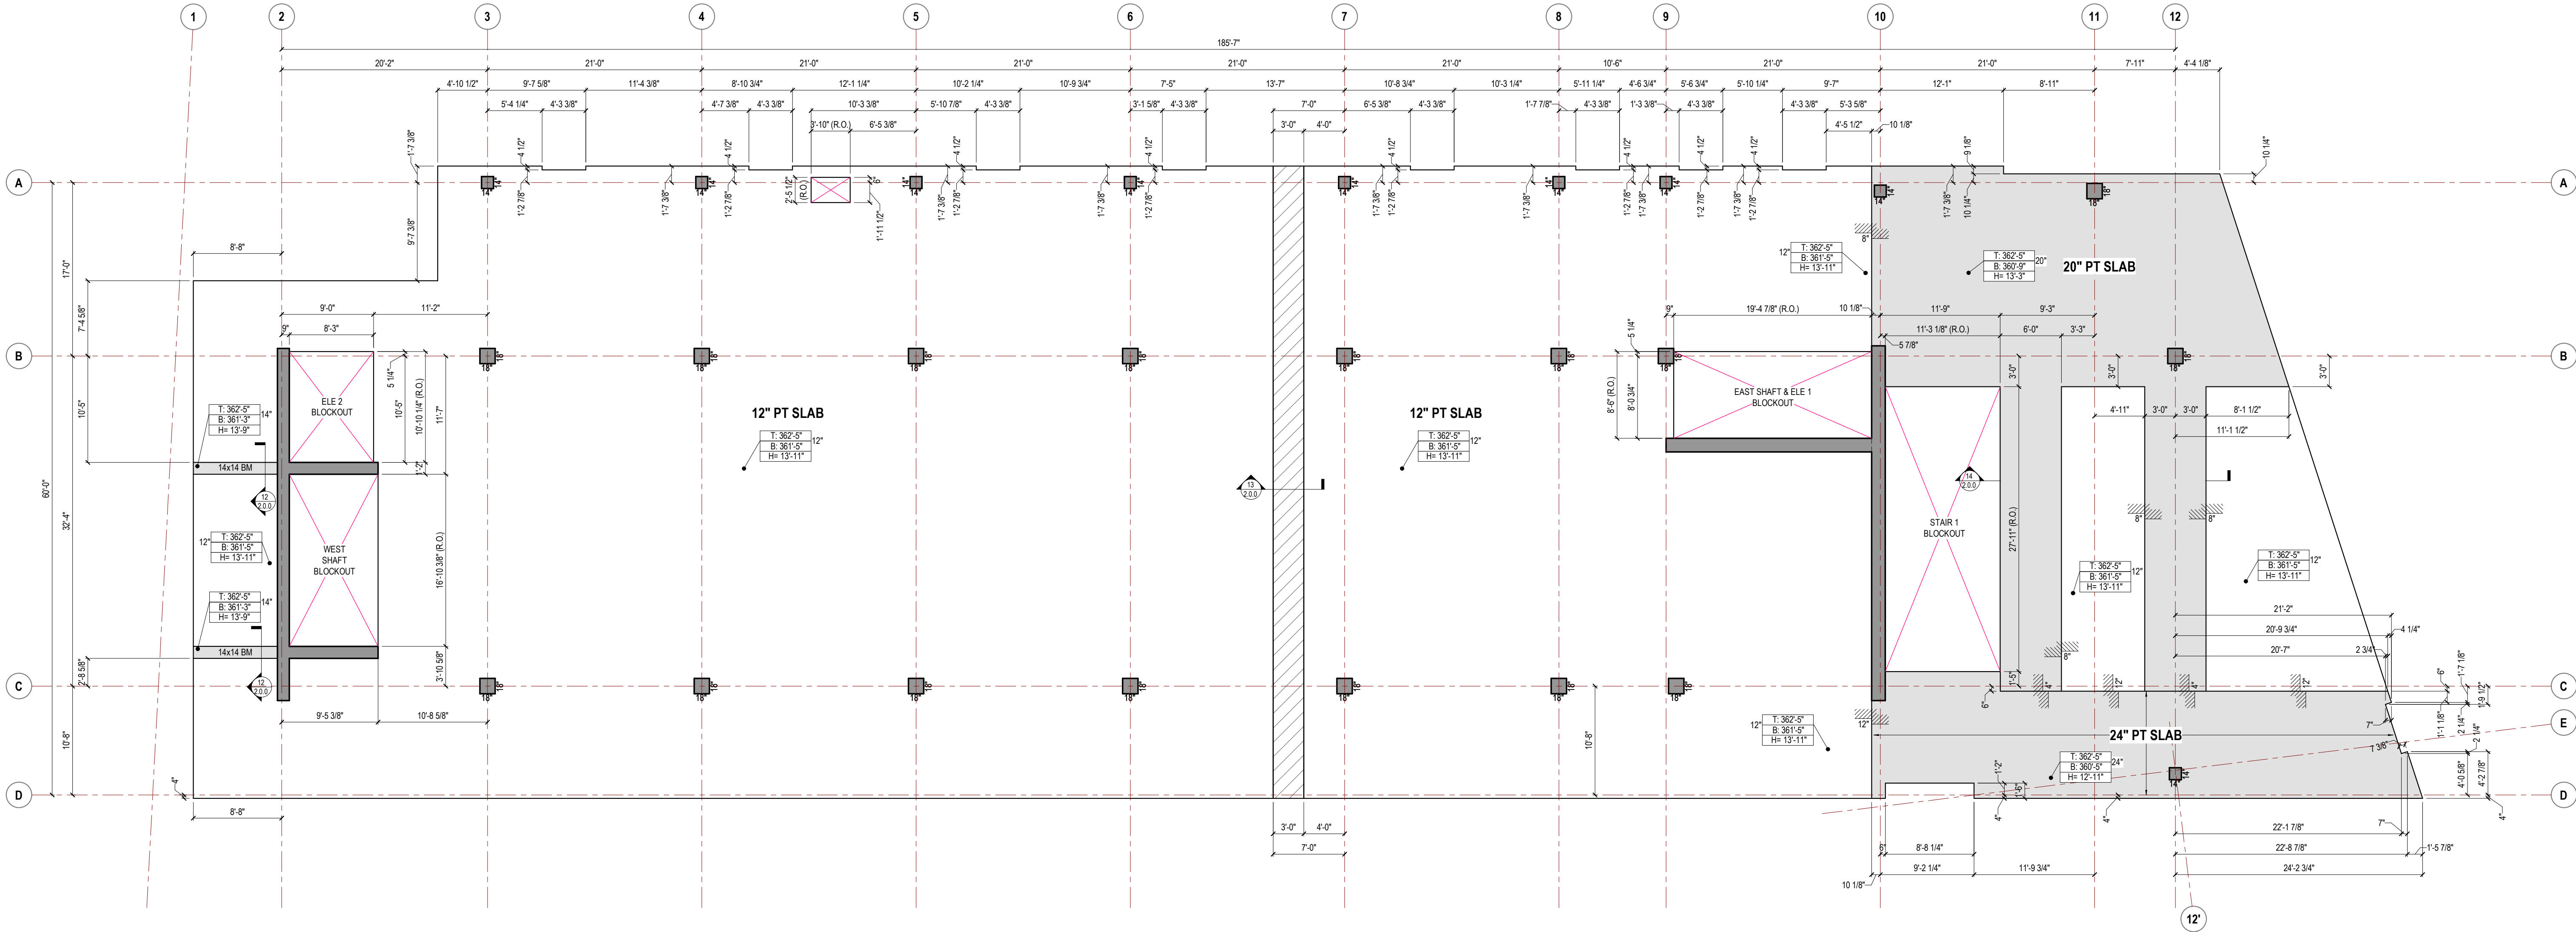


1 LEVEL-4 SOFFIT PLAN
REF: 31140
1/8" = 1'-0"

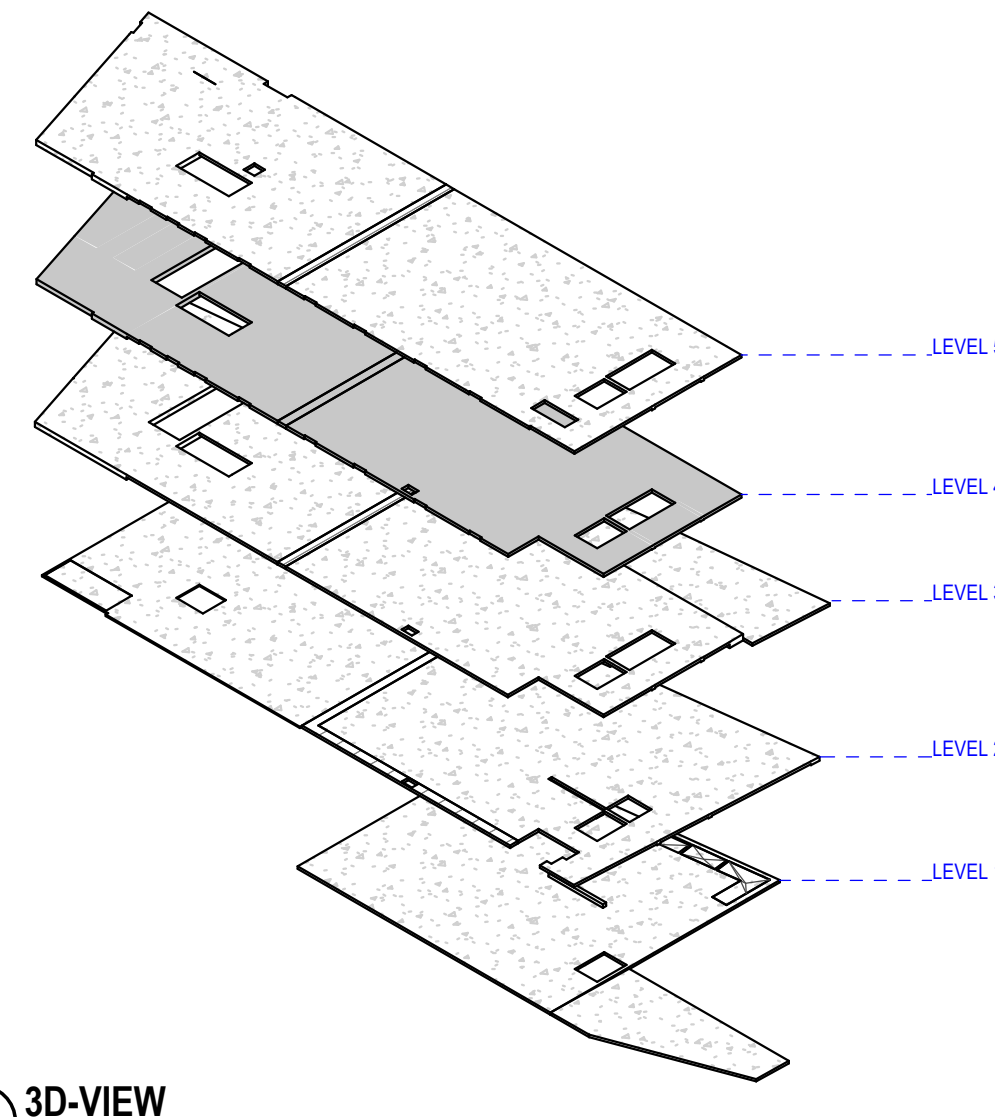

2 3D-VIEW

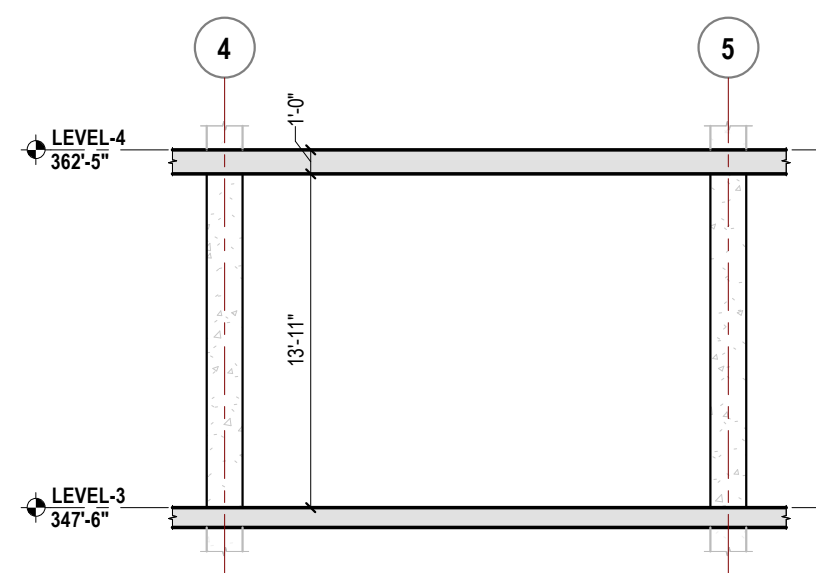

3 BUILDING SECTION
1/8" = 1'-0"

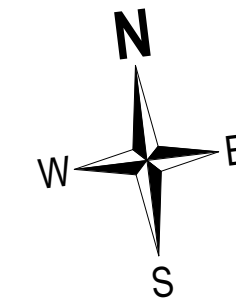

NOTES:

- 3/4" CHAMFER ON ALL EXPOSED CONCRETE CORNERS TYP.
- ALL COLUMNS ARE CENTERED ON GRID LINES U.N.O.
- ALL BEAMS ARE CENTERED ON GRID LINES U.N.O.
- SLAB THICKNESS IS 12" TYP. U.N.O.

LEGEND

SYMBOLS

- 1-BOX (ROUND-ENDS)**
TOP OF CONCRETE ELEVATIONS
- 1-BOX**
BOTTOM OF CONCRETE ELEVATIONS
- 2-BOX (PLAN VIEWS)**
TOP & BOTTOM ELEVATIONS
D = DEPTH OF CONC. MEMBER
- 3-BOX (FLOOR PLANS)**
TOP & BOTTOM ELEVATIONS
COLUMN ELEVATION ABOVE REF. LEVEL
D = DEPTH OF CONC. MEMBER

SECTION VIEW

- SHEET NUMBER
- DETAIL NUMBER

ELEVATION VIEW

- SHEET NUMBER
- DETAIL NUMBER

SHADE DESIGNATIONS

- BEAM OR DROP CAP
- WALLS OR COLUMNS
- CMU WALLS
- DELAY STRIP OR CLOSURE POUR
- GRADE OR SOIL
- Y" PT/MS/CIP SLAB
- Z" PT/MS/CIP SLAB

LINE DESIGNATIONS

- INDICATES TOP OF SLAB CHANGE OR EDGE OF SLAB
- INDICATES SOFFIT CHANGE
- INDICATES CONSTRUCTION JOINT
- INDICATES GRID LINE


McCLONE
CONSTRUCTION | SINCE 1975
WASHINGTON OFFICE
28810 MAPLE VALLEY, WA 98038 • 425-143-1440

LEVEL-4 SOFFIT PLAN
WWU-INTERDISCIPLINARY SCIENCE BUILDING
BELLINGHAM, WA & 98225


SHEET NO. DATE
11/11/20
SCALE
1/8" = 1'-0"
DRAWN BY
TV
PBA
1147
SHEET
1.40
SHEET TOTAL

THIS DRAWING IS FOR THE EXCLUSIVE USE OF MCCLONE CONSTRUCTION COMPANY. ON THIS PROJECT ONLY. UTILIZATION OF THIS DRAWING BY OTHER PARTIES AND/OR OTHER PROJECTS WITHOUT THE EXPRESSED WRITTEN CONSENT OF MCCLONE CONSTRUCTION COMPANY IS STRICTLY PROHIBITED.


PLOT DATE/TIME STAMP: 12/6/2020 2:42:32 PM
Z:\Shared\WIP\Projects\1147 WWU - ISBMDC EKG\Drawings\Sheet Models\WWU-SSB.rvt

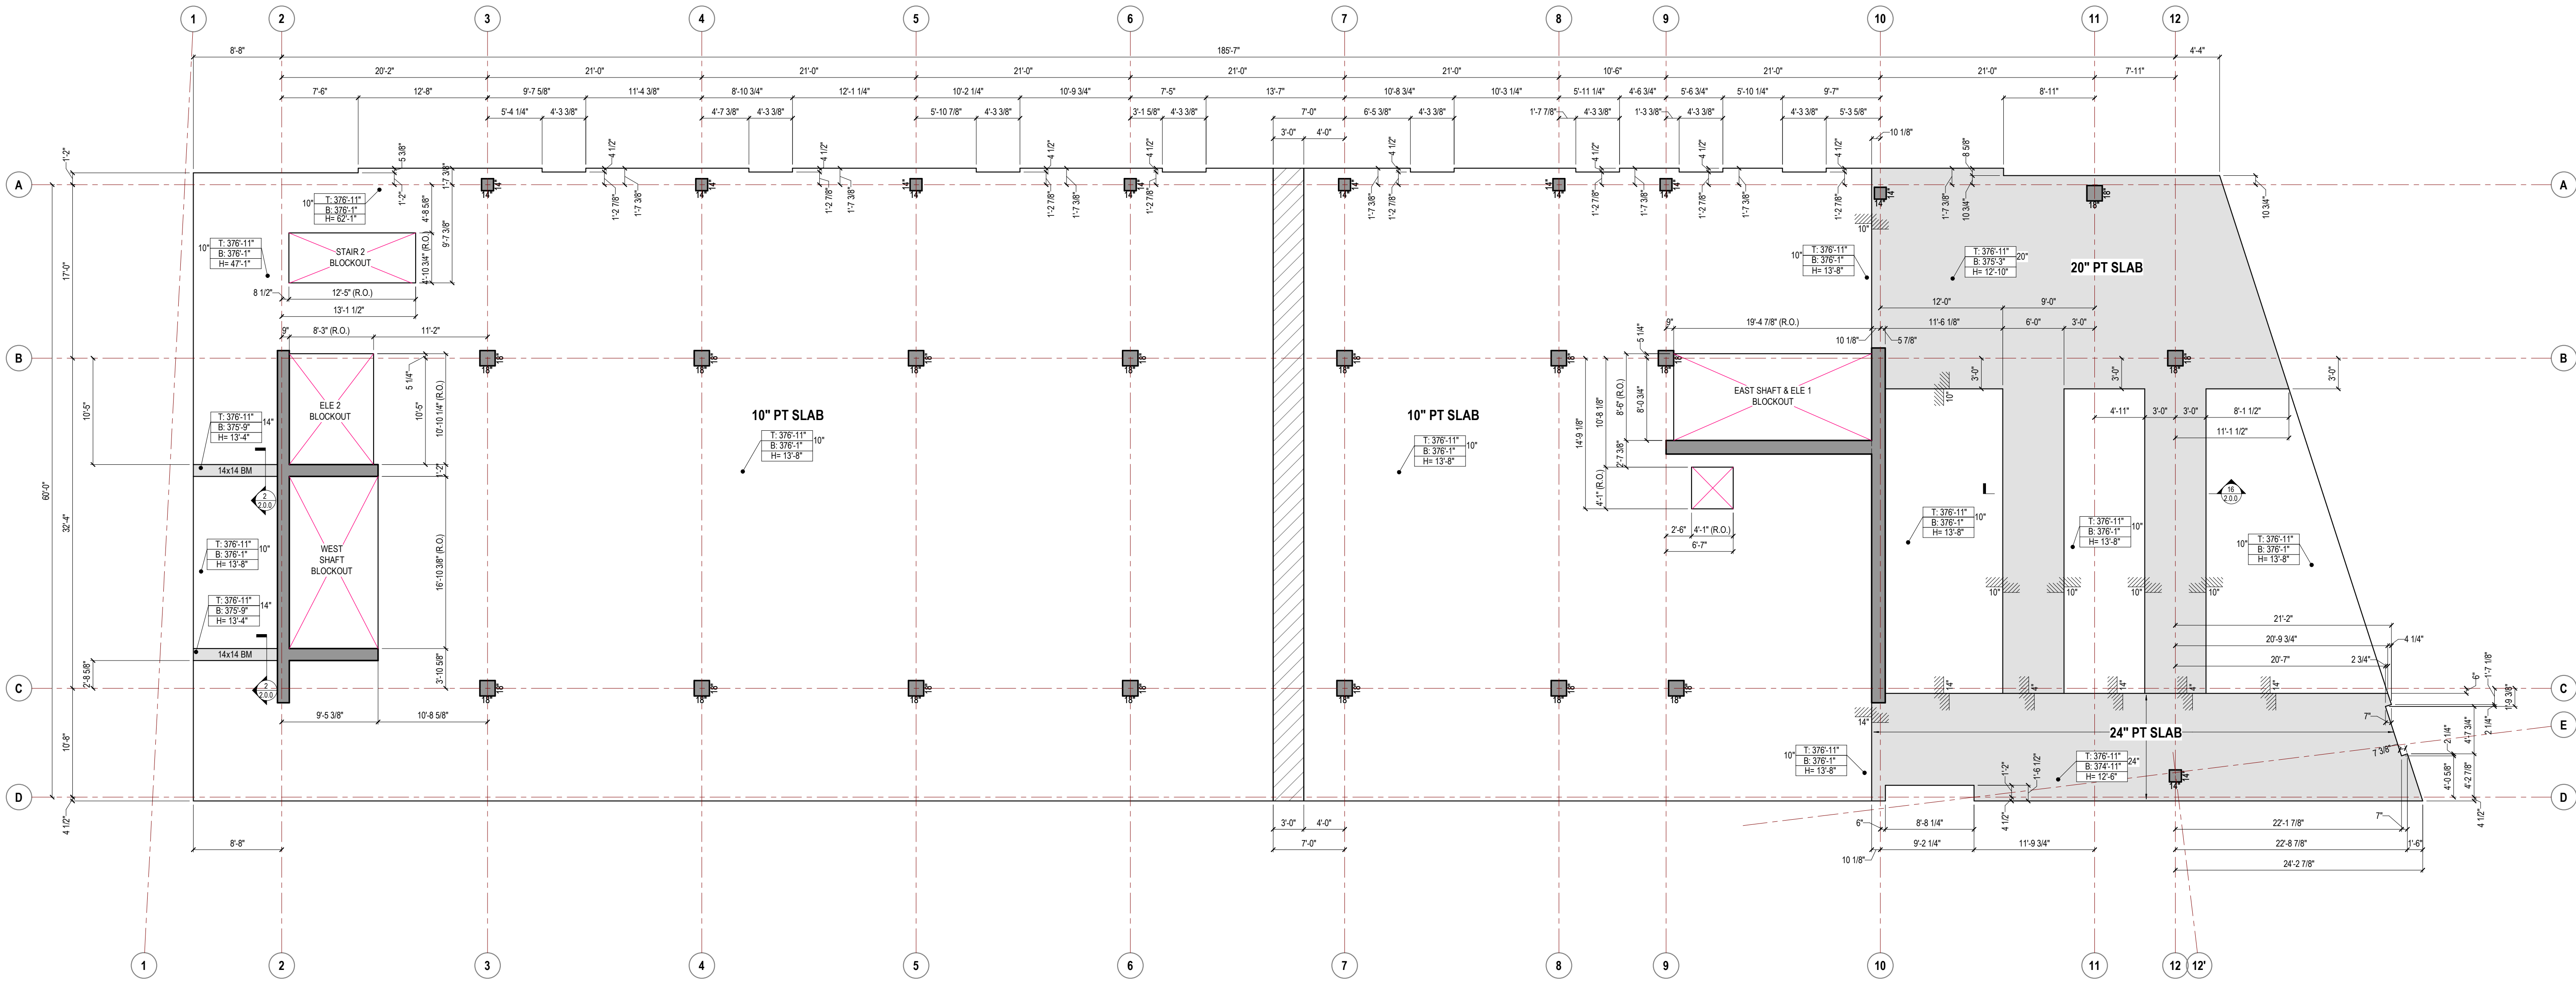


1 LEVEL-5 SOFFIT PLAN
REF: 3/11.5.0
1/8" = 1'-0"

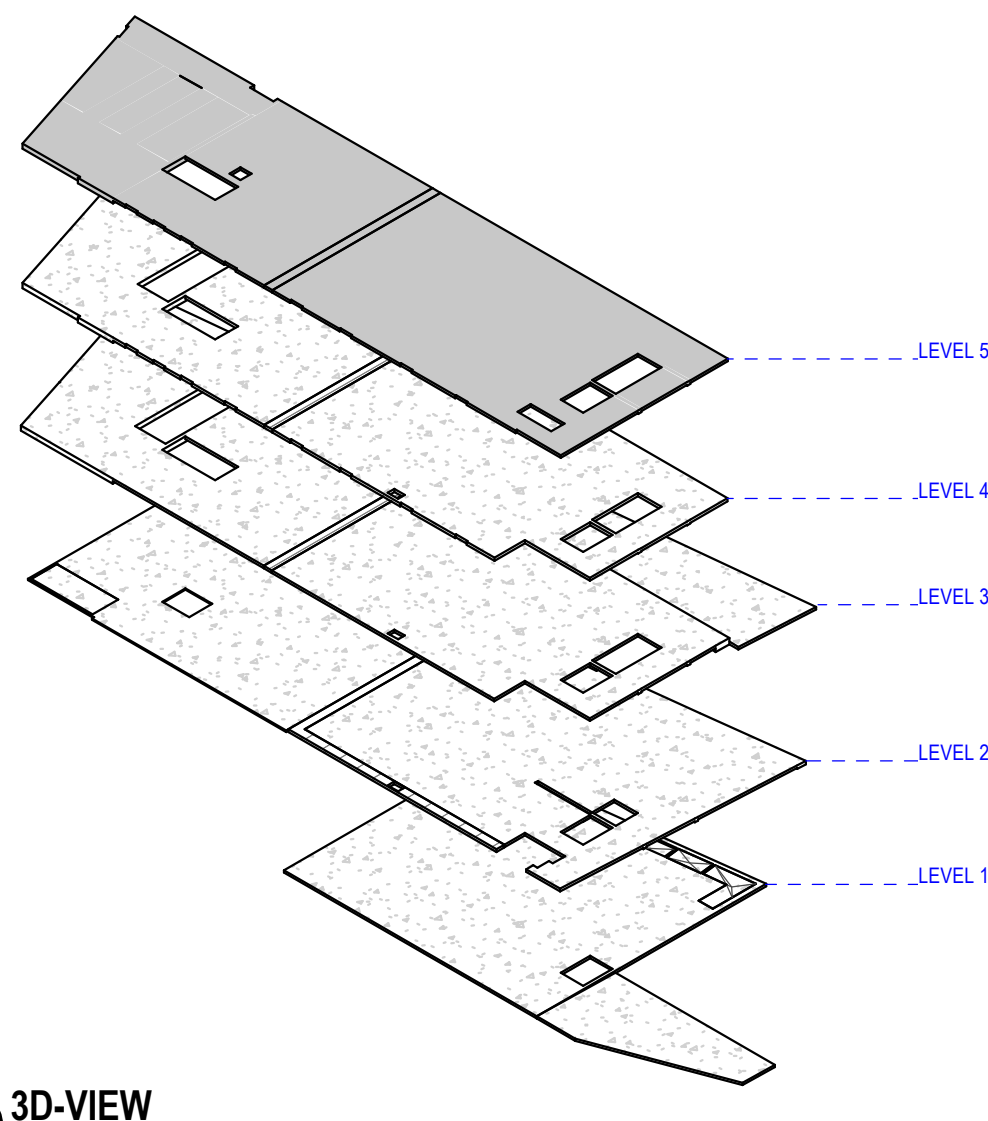

2 3D-VIEW

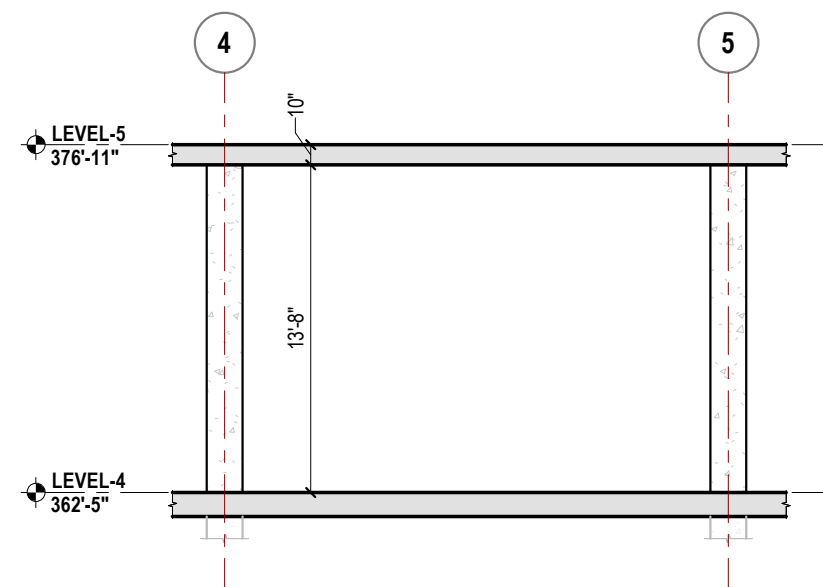

3 BUILDING SECTION
1/8" = 1'-0"

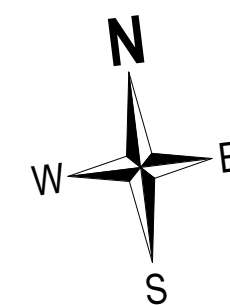

NOTES:

- 3/4" CHAMFER ON ALL EXPOSED CONCRETE CORNERS TYP.
- ALL COLUMNS ARE CENTERED ON GRID LINES U.N.O.
- ALL BEAMS ARE CENTERED ON GRID LINES U.N.O.
- SLAB THICKNESS IS 10" TYP. U.N.O.

LEGEND

SYMBOLS

- 1-BOX (ROUND-ENDS)**
TOP OF CONCRETE ELEVATIONS
- 1-BOX**
BOTTOM OF CONCRETE ELEVATIONS
- 2-BOX (PLAN VIEWS)**
TOP & BOTTOM ELEVATIONS
D = DEPTH OF CONC. MEMBER
- 3-BOX (SOFFIT PLANS)**
TOP & BOTTOM ELEVATIONS
HEIGHT BELOW REFERENCE LEVEL
D = DEPTH OF CONC. MEMBER

SECTION VIEW

SHEET NUMBER

ELEVATION VIEW

SHEET NUMBER

- (TOP ELEV)
- (BOT ELEV)
- (TOP ELEV) 10"
- (BOT ELEV) 10"
- (TOP ELEV) 10"
- (BOT ELEV) 10"
- COL. HT. (FT. IN.)

SHADE DESIGNATIONS

- BEAM OR DROP CAP
- WALLS OR COLUMNS
- CMU WALLS
- DELAY STRIP OR CLOSURE POUR
- GRADE OR SOIL
- Y" PT/MS/CIP SLAB
- Z" PT/MS/CIP SLAB

LINE DESIGNATIONS

- INDICATES TOP OF SLAB CHANGE OR EDGE OF SLAB
- INDICATES SOFFIT CHANGE
- INDICATES CONSTRUCTION JOINT
- INDICATES GRID LINE

McCLONE
CONSTRUCTION | SINCE 1975
WASHINGTON OFFICE
28810 MAPLE VALLEY ROAD, SE SUITE 200
MAPLE VALLEY, WA 98038 • 425-413-1440

LEVEL-5 SOFFIT PLAN
WWU-INTERDISCIPLINARY SCIENCE BUILDING
BELLINGHAM, WA & 98225

SHEET NO. DATE
12/09/20
SCALE
1/8" = 1'-0"
DRAWN BY
TV
P.A.
1147
SHEET
1.5.0
SHEET SOFFIT