


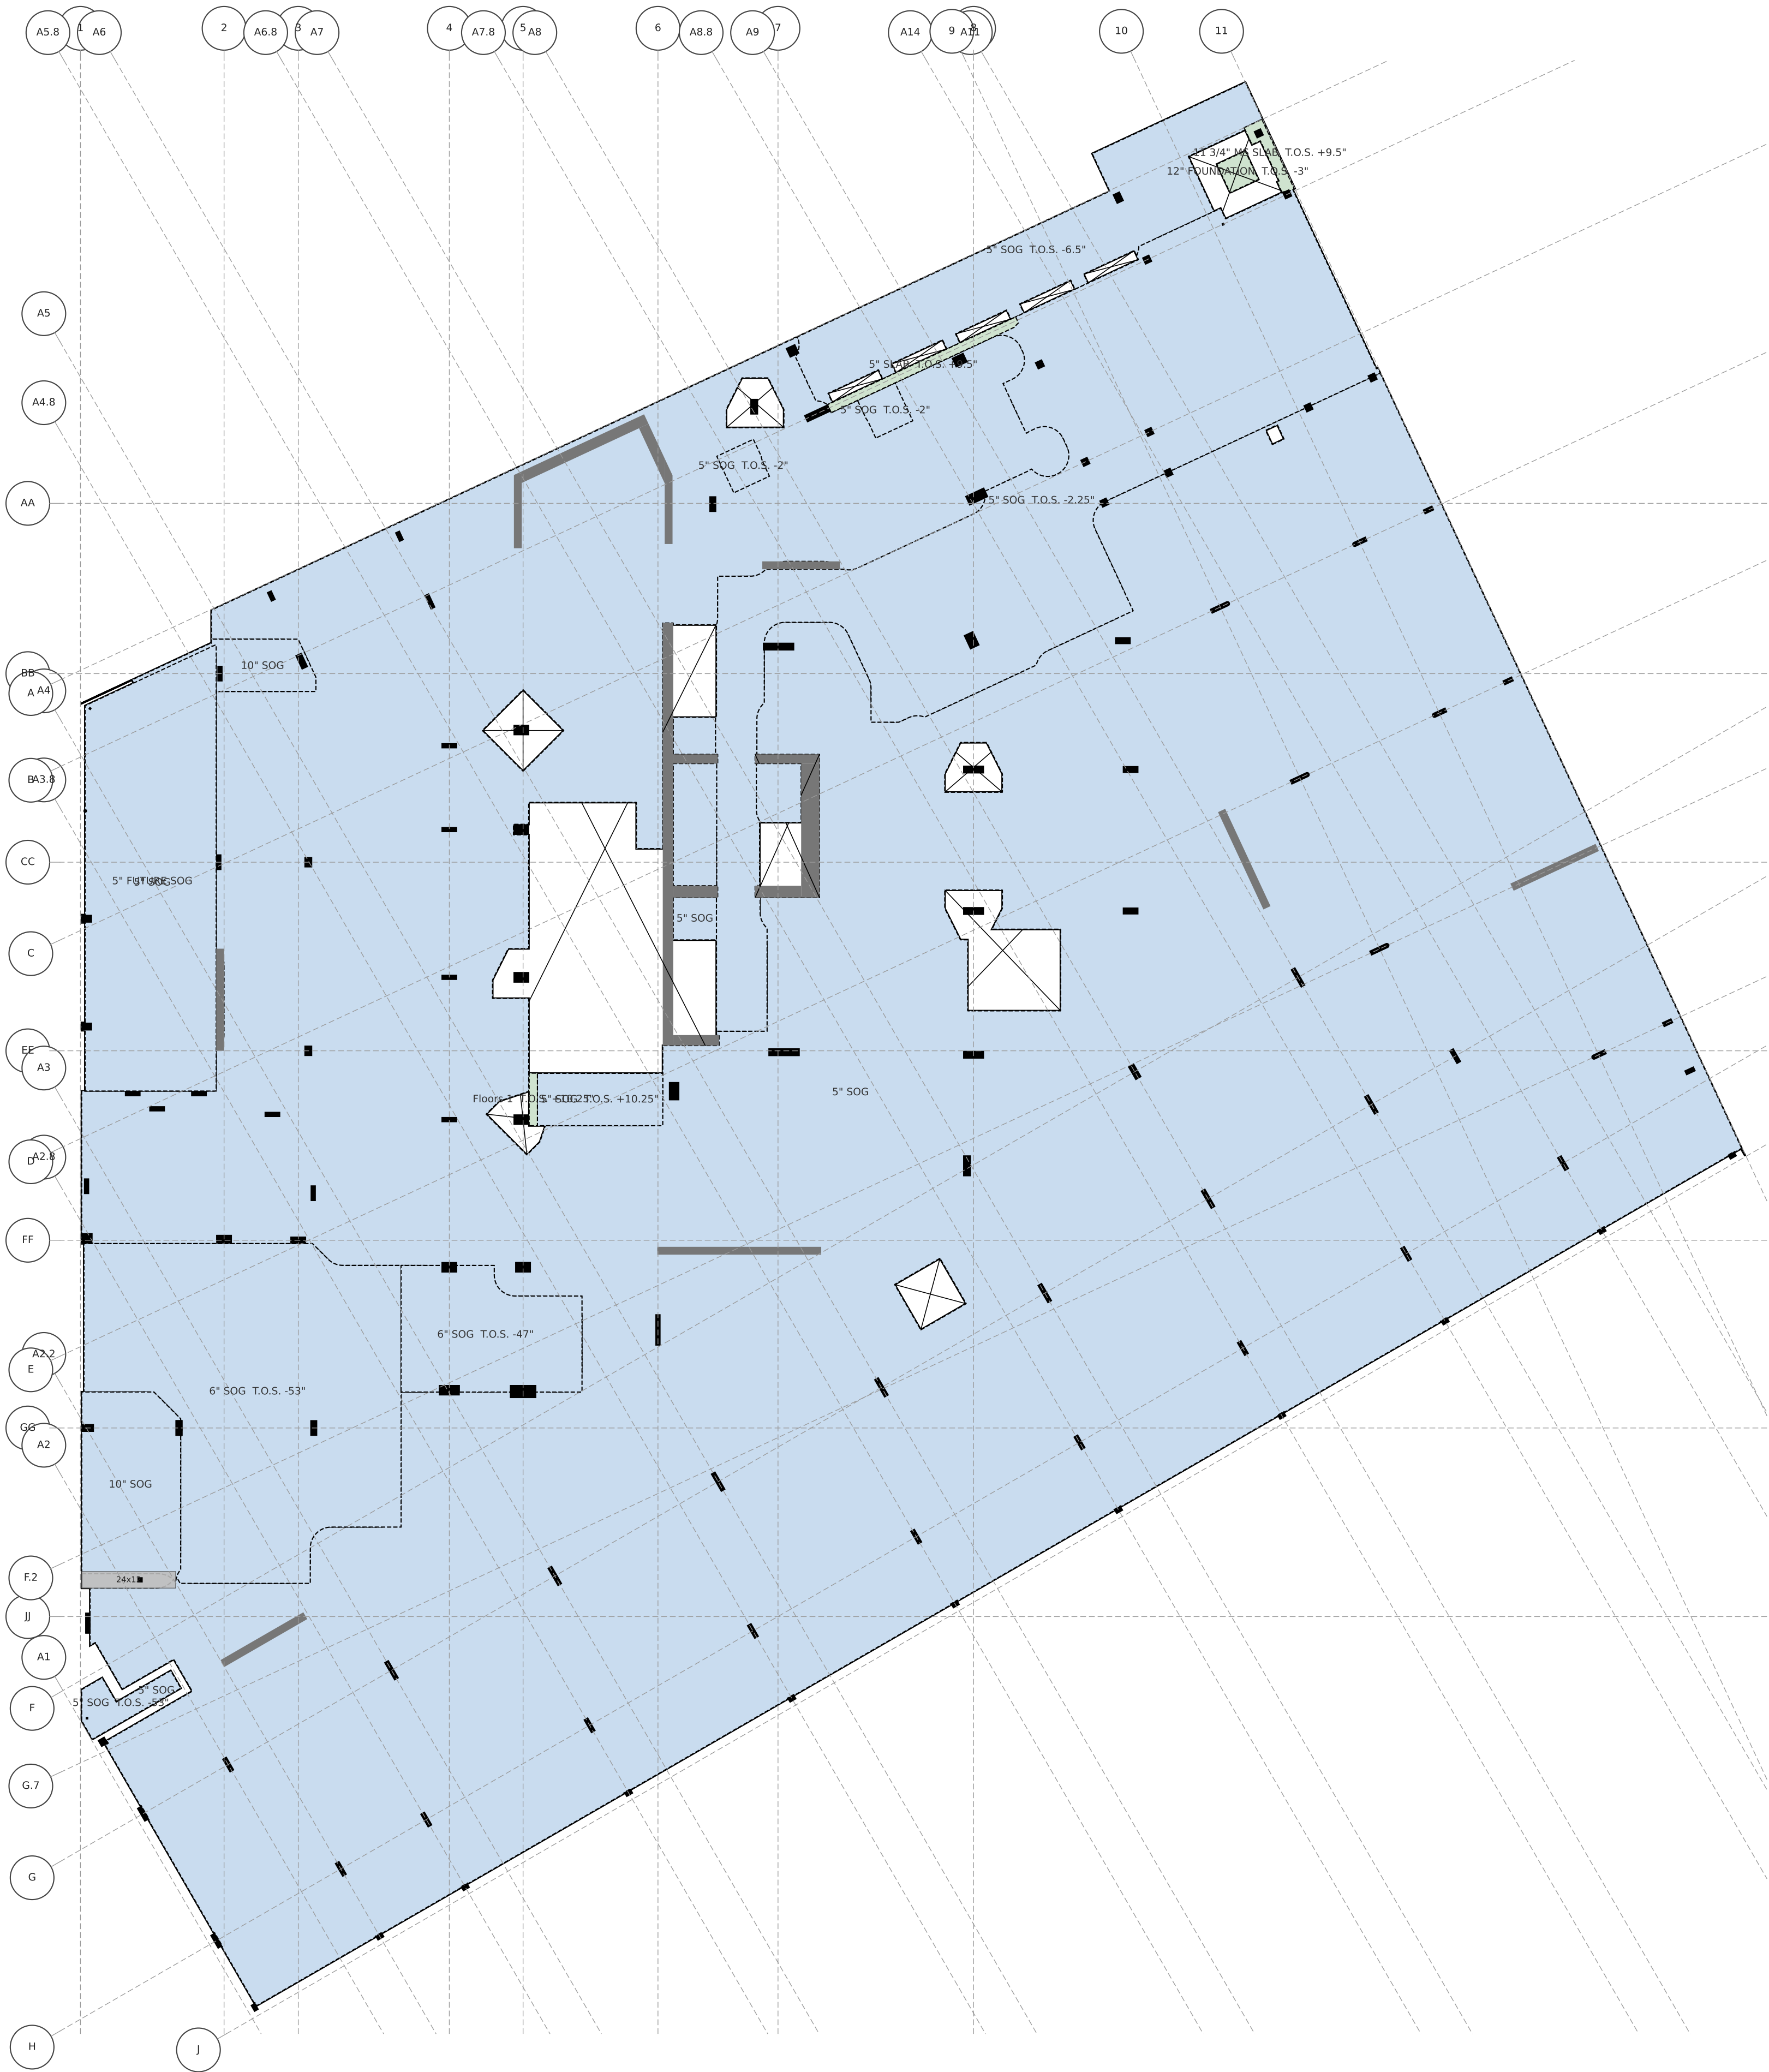


1268 KALAE

LEVEL 1 FLOOR PLAN

T.O.S. 9'-3" · typical slab 5" · scale 1" = 20' · SLAB ON GRADE

Generated from HJ_KALAE_MCC_ST.ifc (Revit scope model) for the McClone Reshore Calculator — geometry only; loading marks are drawn in the calculator.

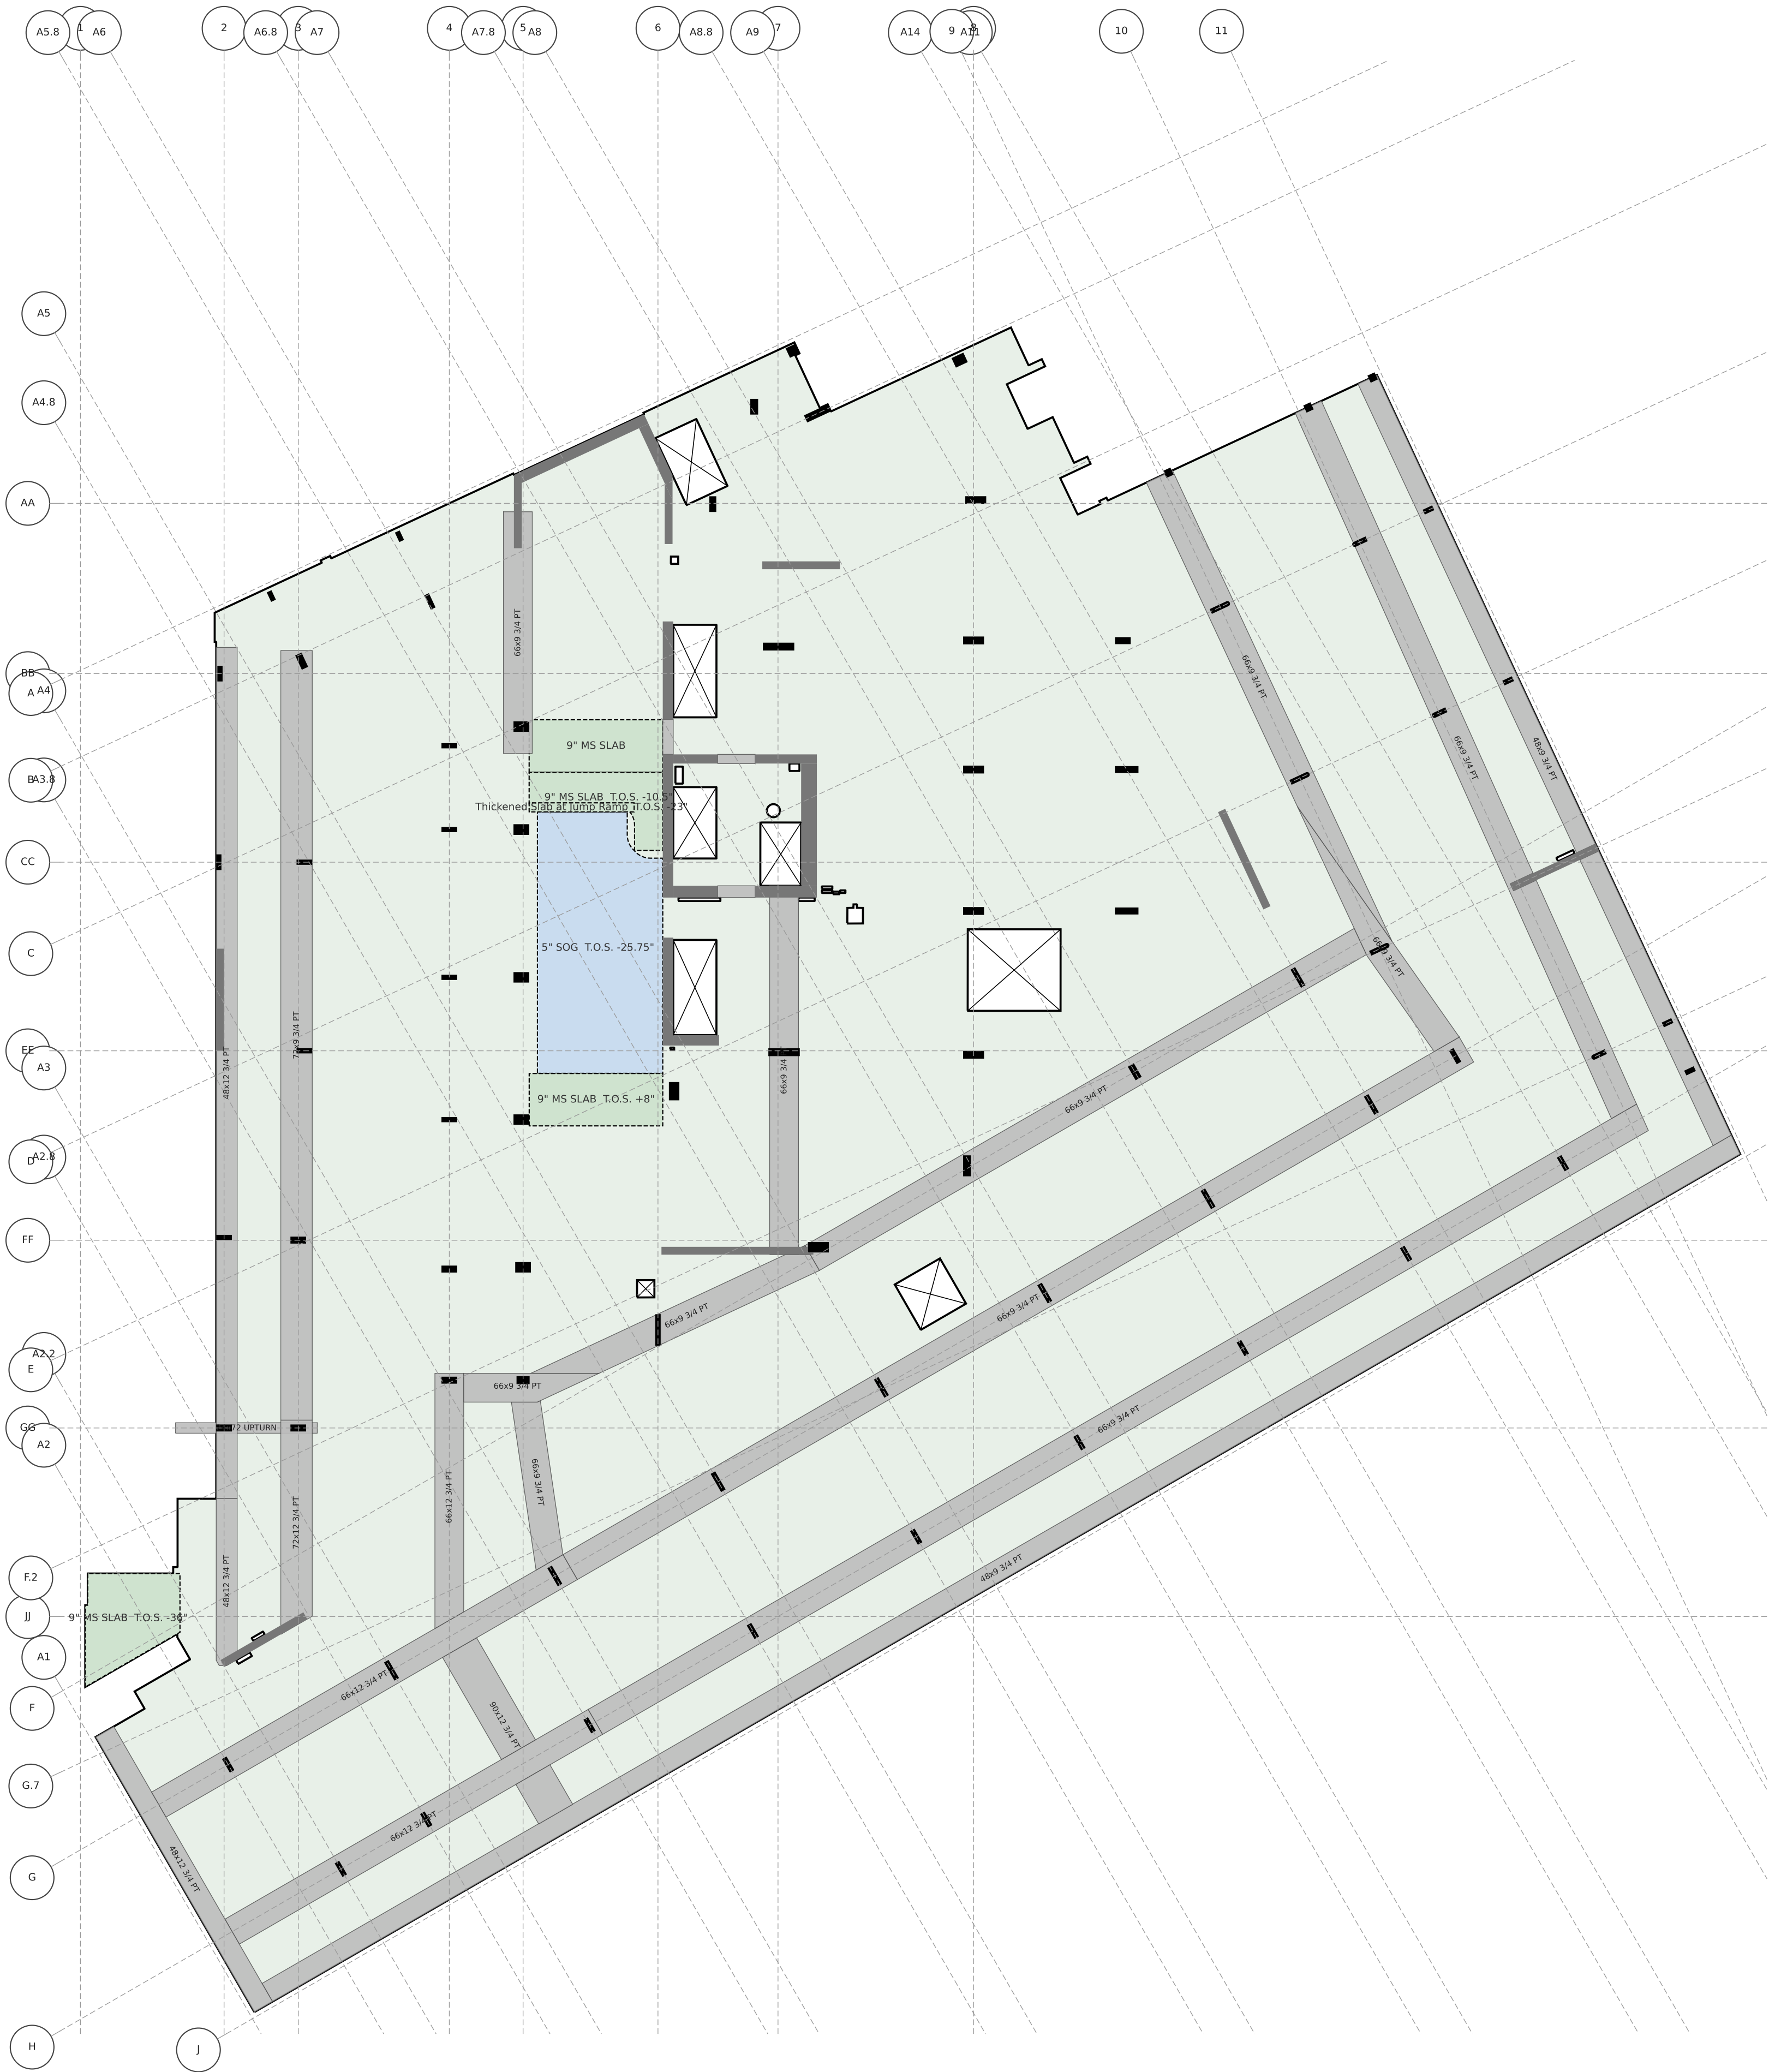


1268 KALAE

LEVEL 2 FLOOR PLAN

T.O.S. 20'-9" · typical slab 7 1/2" · scale 1" = 20'

Generated from HJ_KALAE_MCC_ST.ifc (Revit scope model) for the McClone Reshore Calculator — geometry only; loading marks are drawn in the calculator.

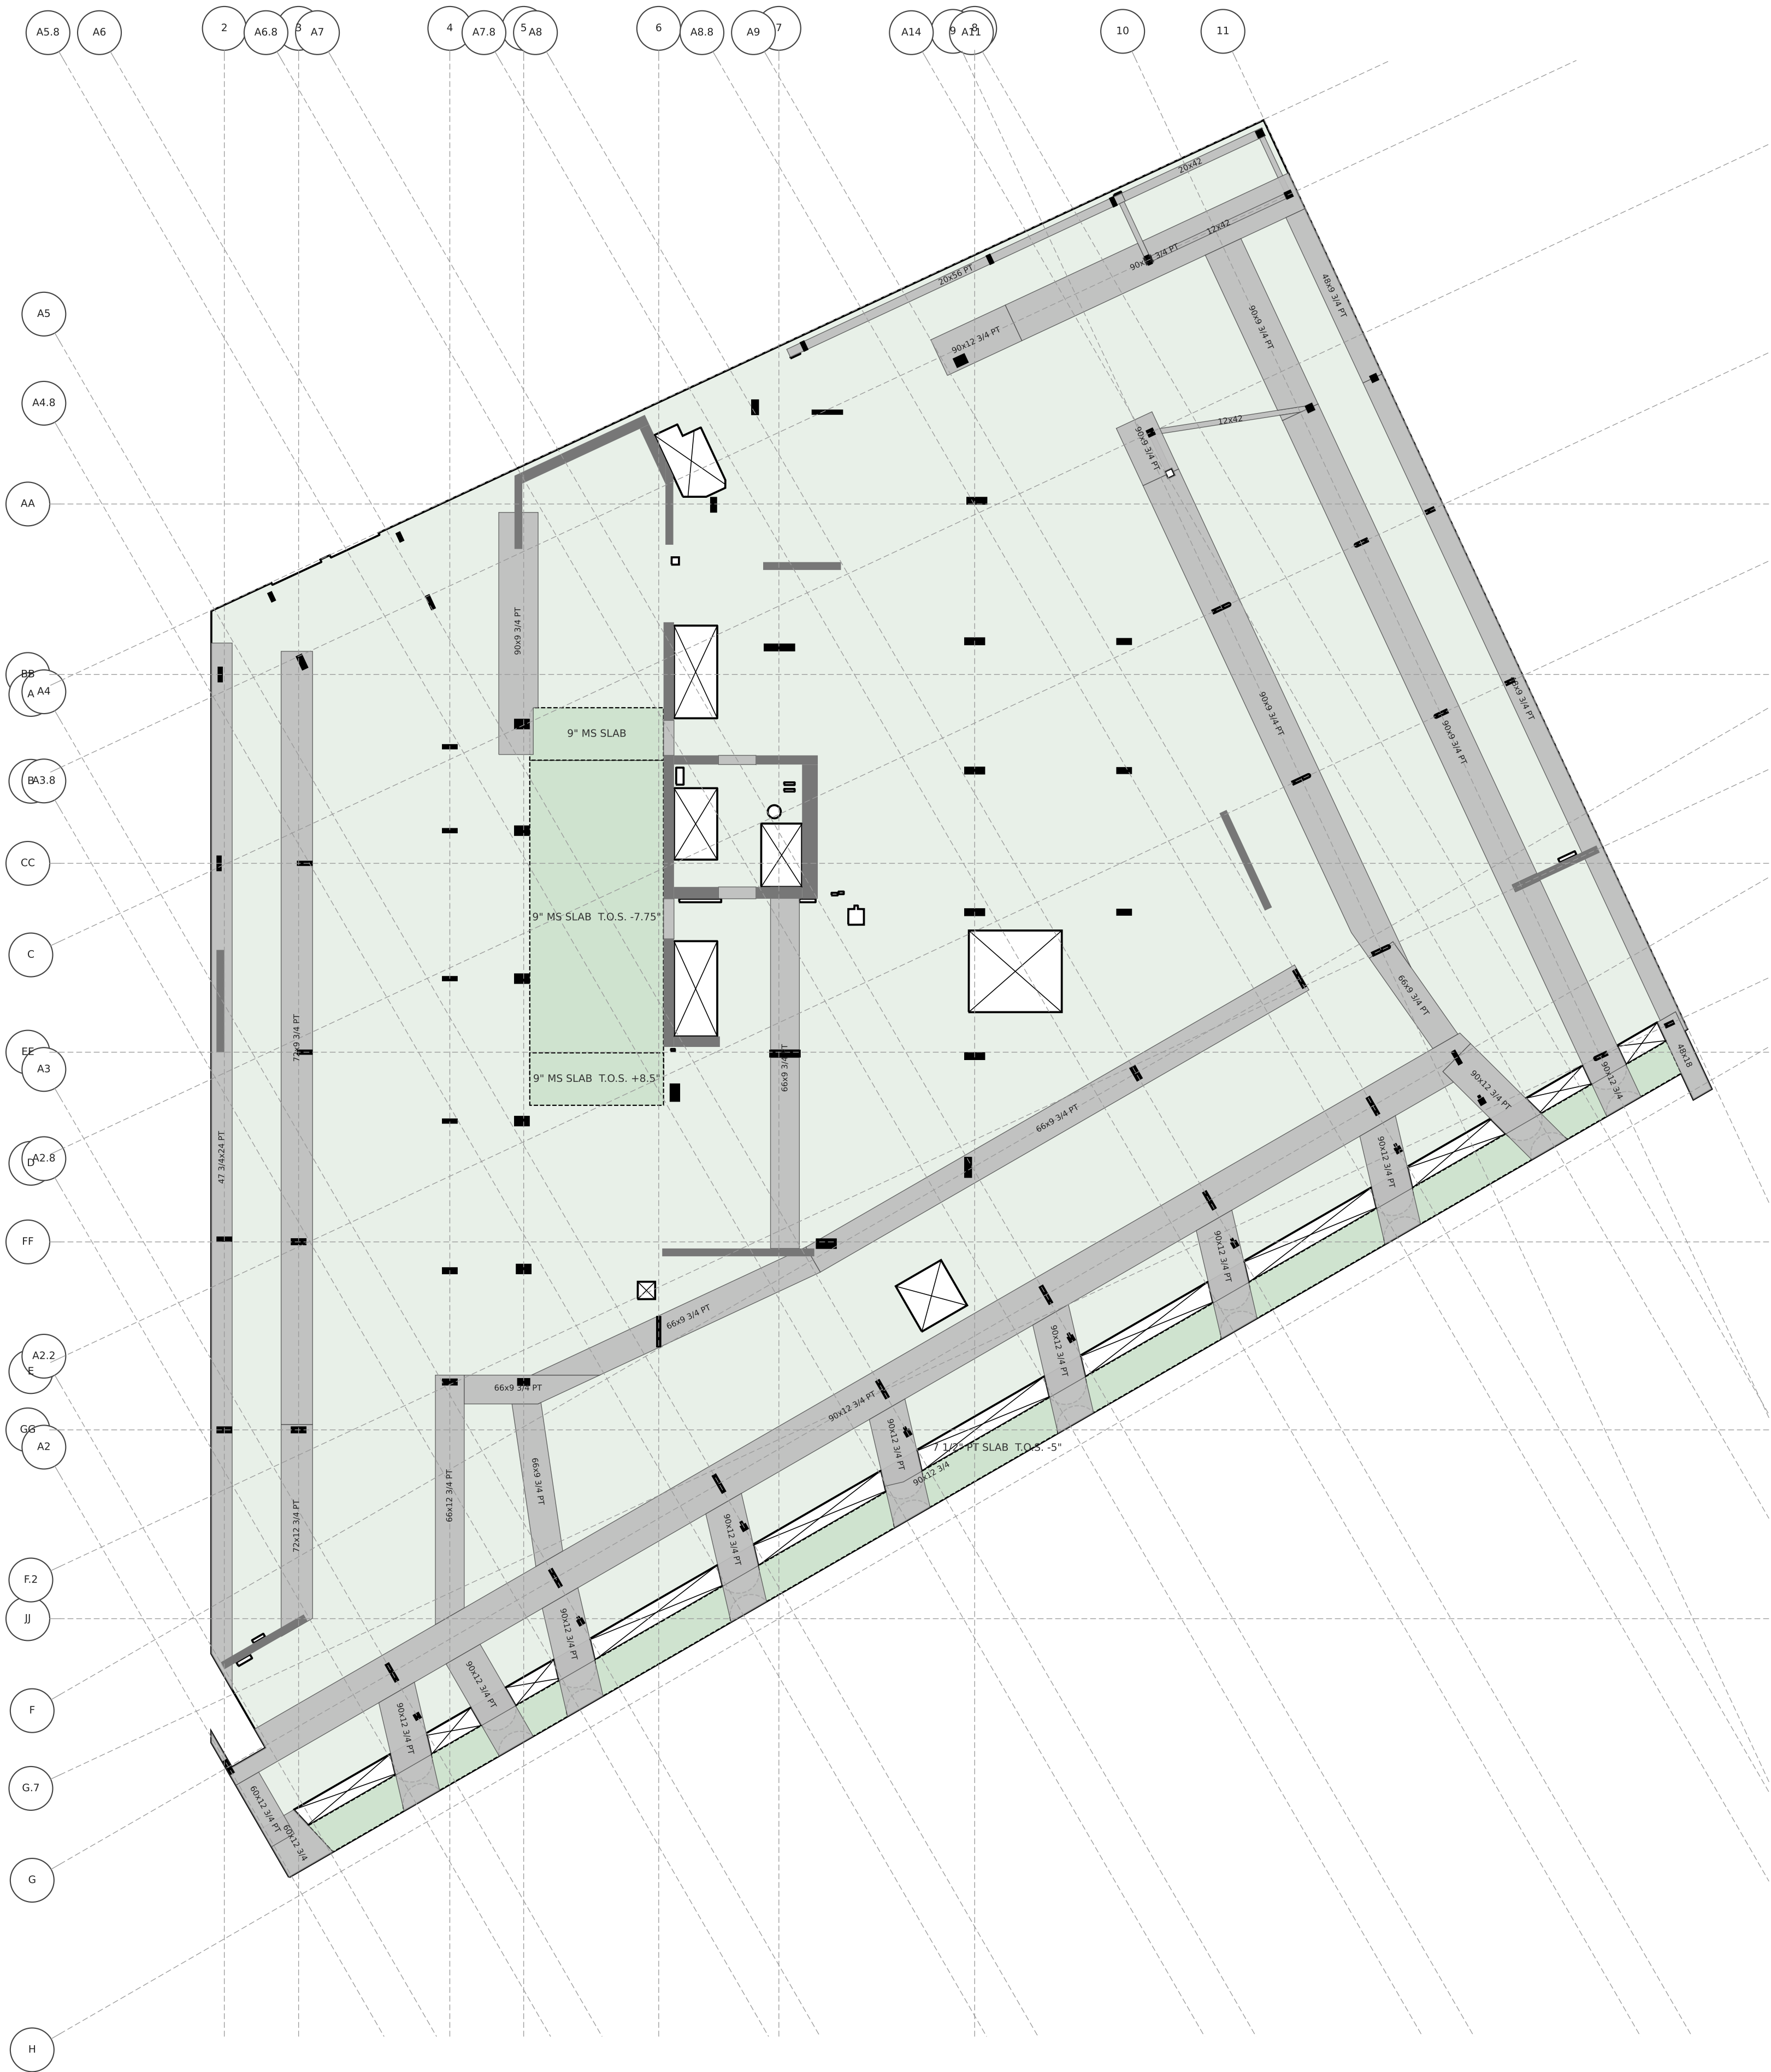


1268 KALAE

LEVEL 3 FLOOR PLAN

T.O.S. 29'-11" · typical slab 7 1/2" · scale 1" = 20'

Generated from HI_KALAE_MCC_ST.ifc (Revit scope model) for the McClone Reshore Calculator — geometry only; loading marks are drawn in the calculator.

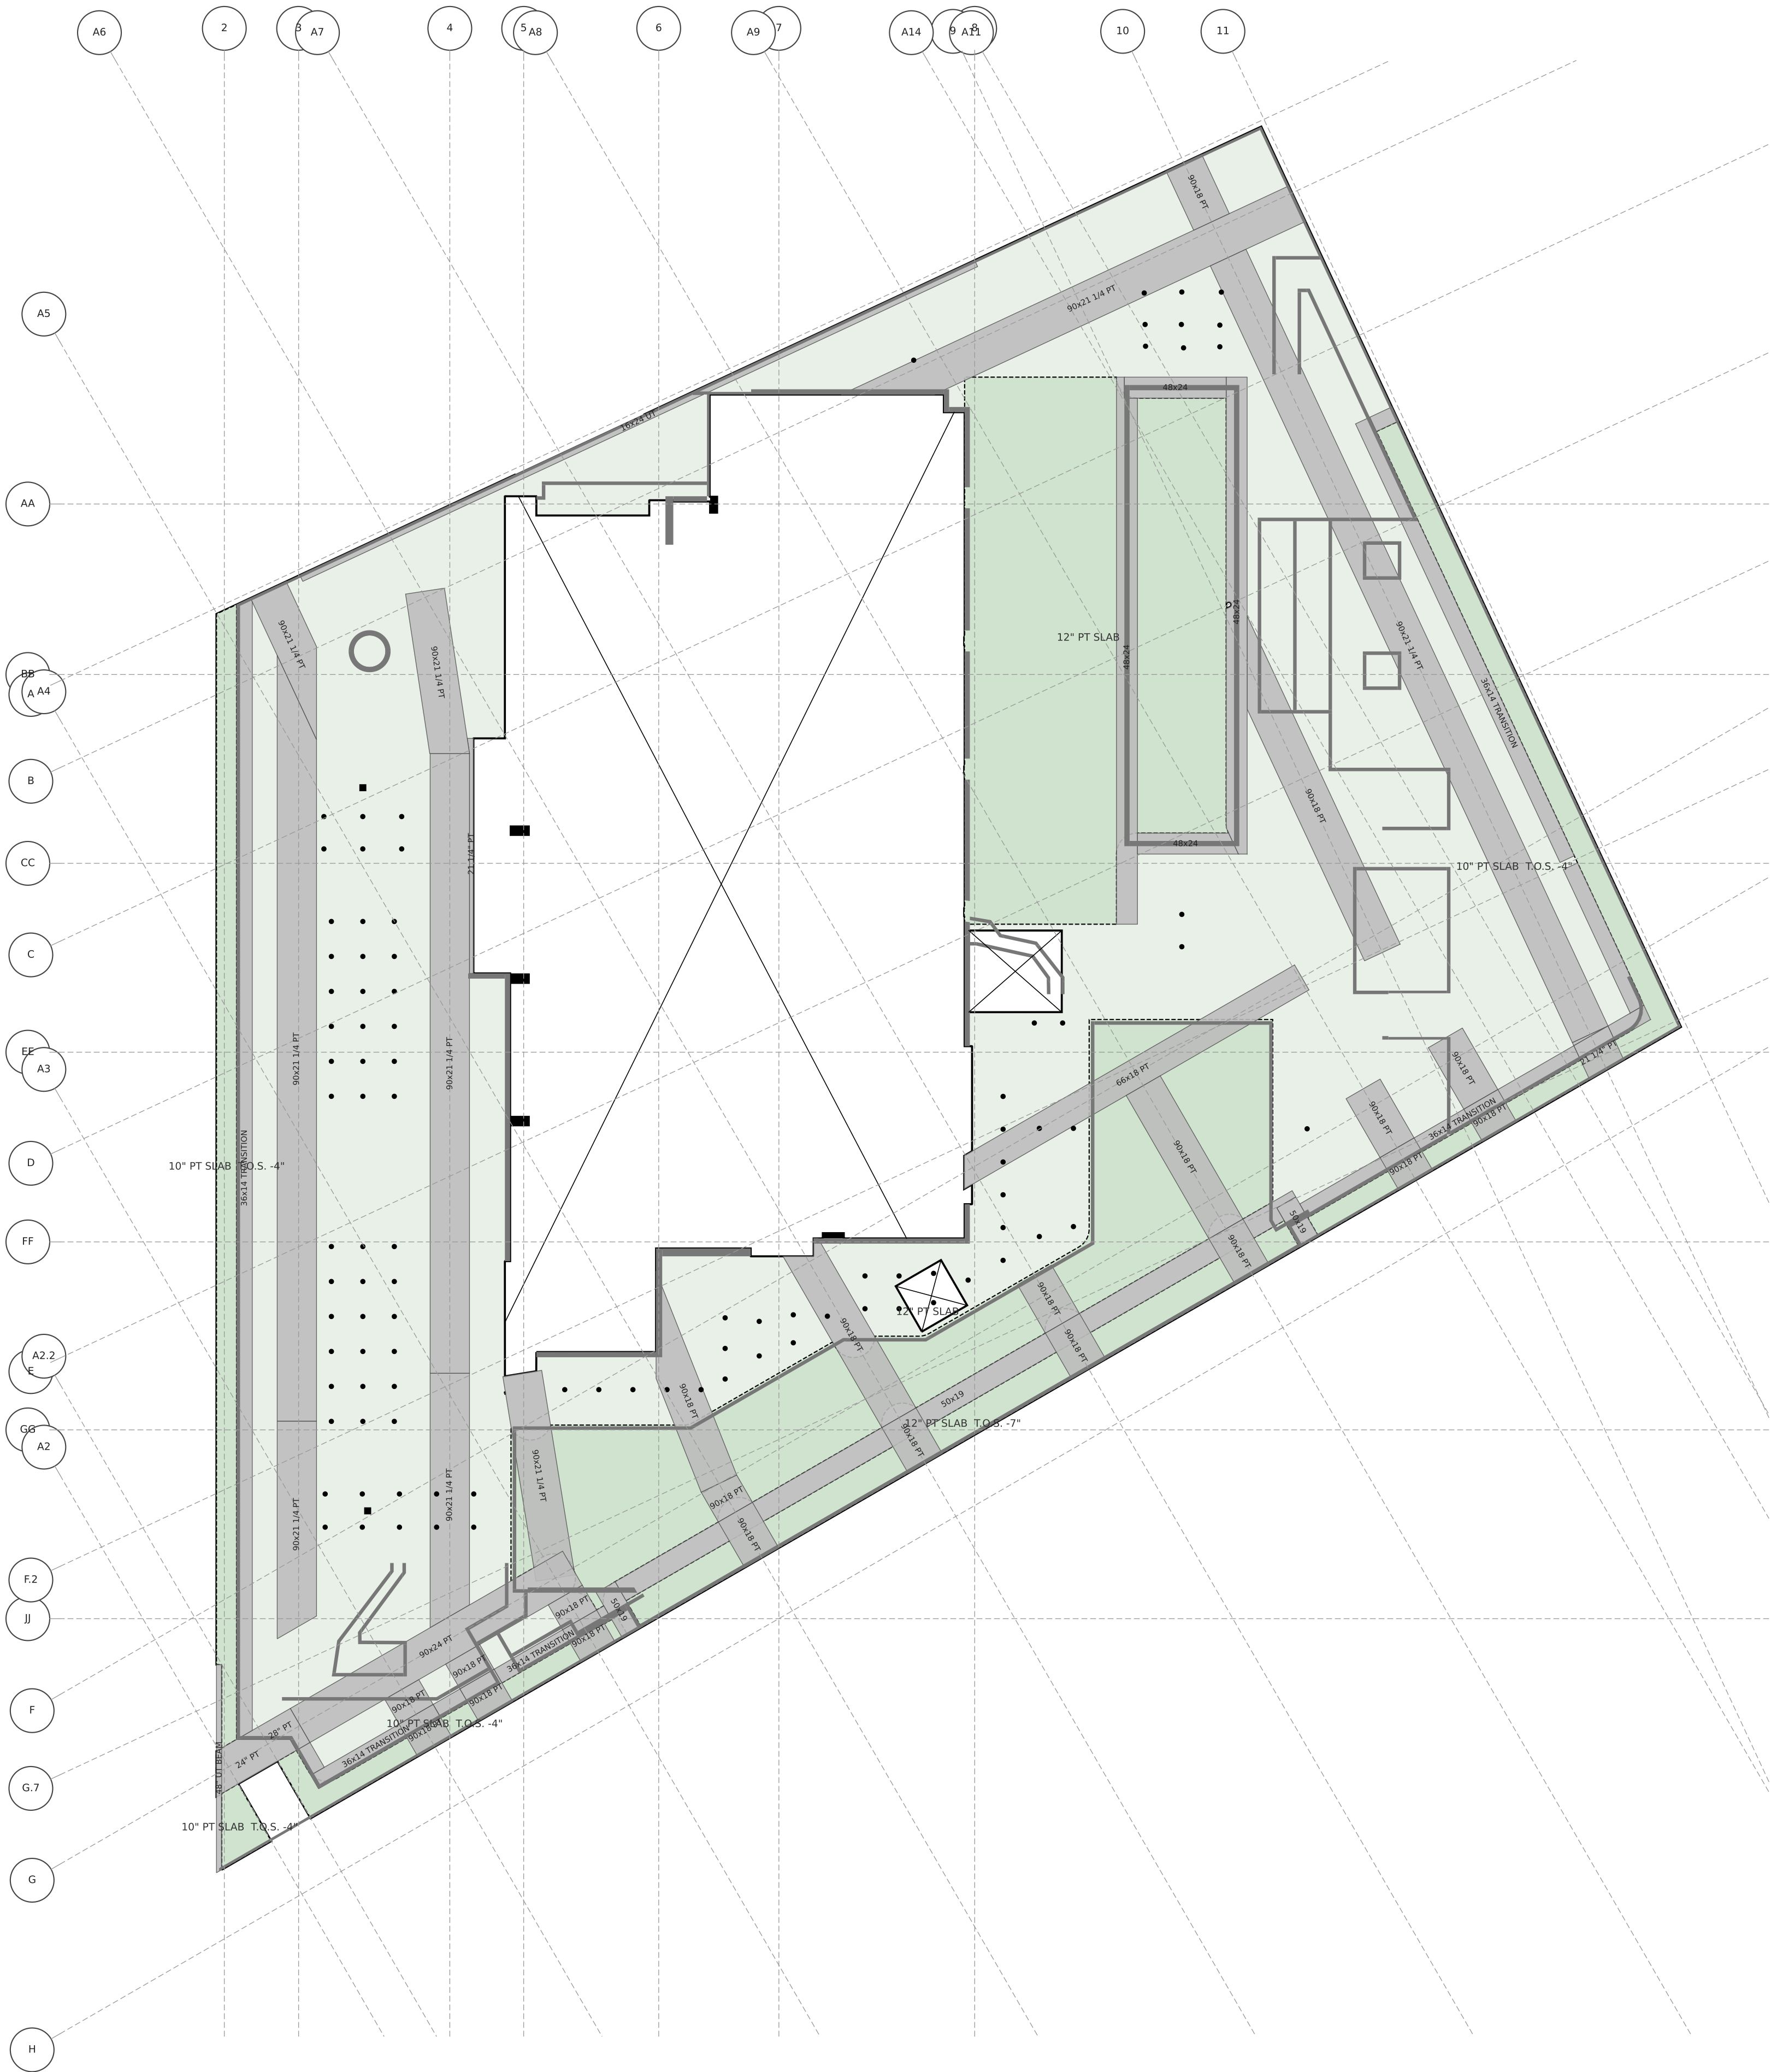


1268 KALAE

LEVEL 4.5 FLOOR PLAN

T.O.S. 48'-3" · typical slab 10" · scale 1" = 20'

Generated from HI_KALAE_MCC_ST.ifc (Revit scope model) for the McClone Reshore Calculator — geometry only; loading marks are drawn in the calculator.

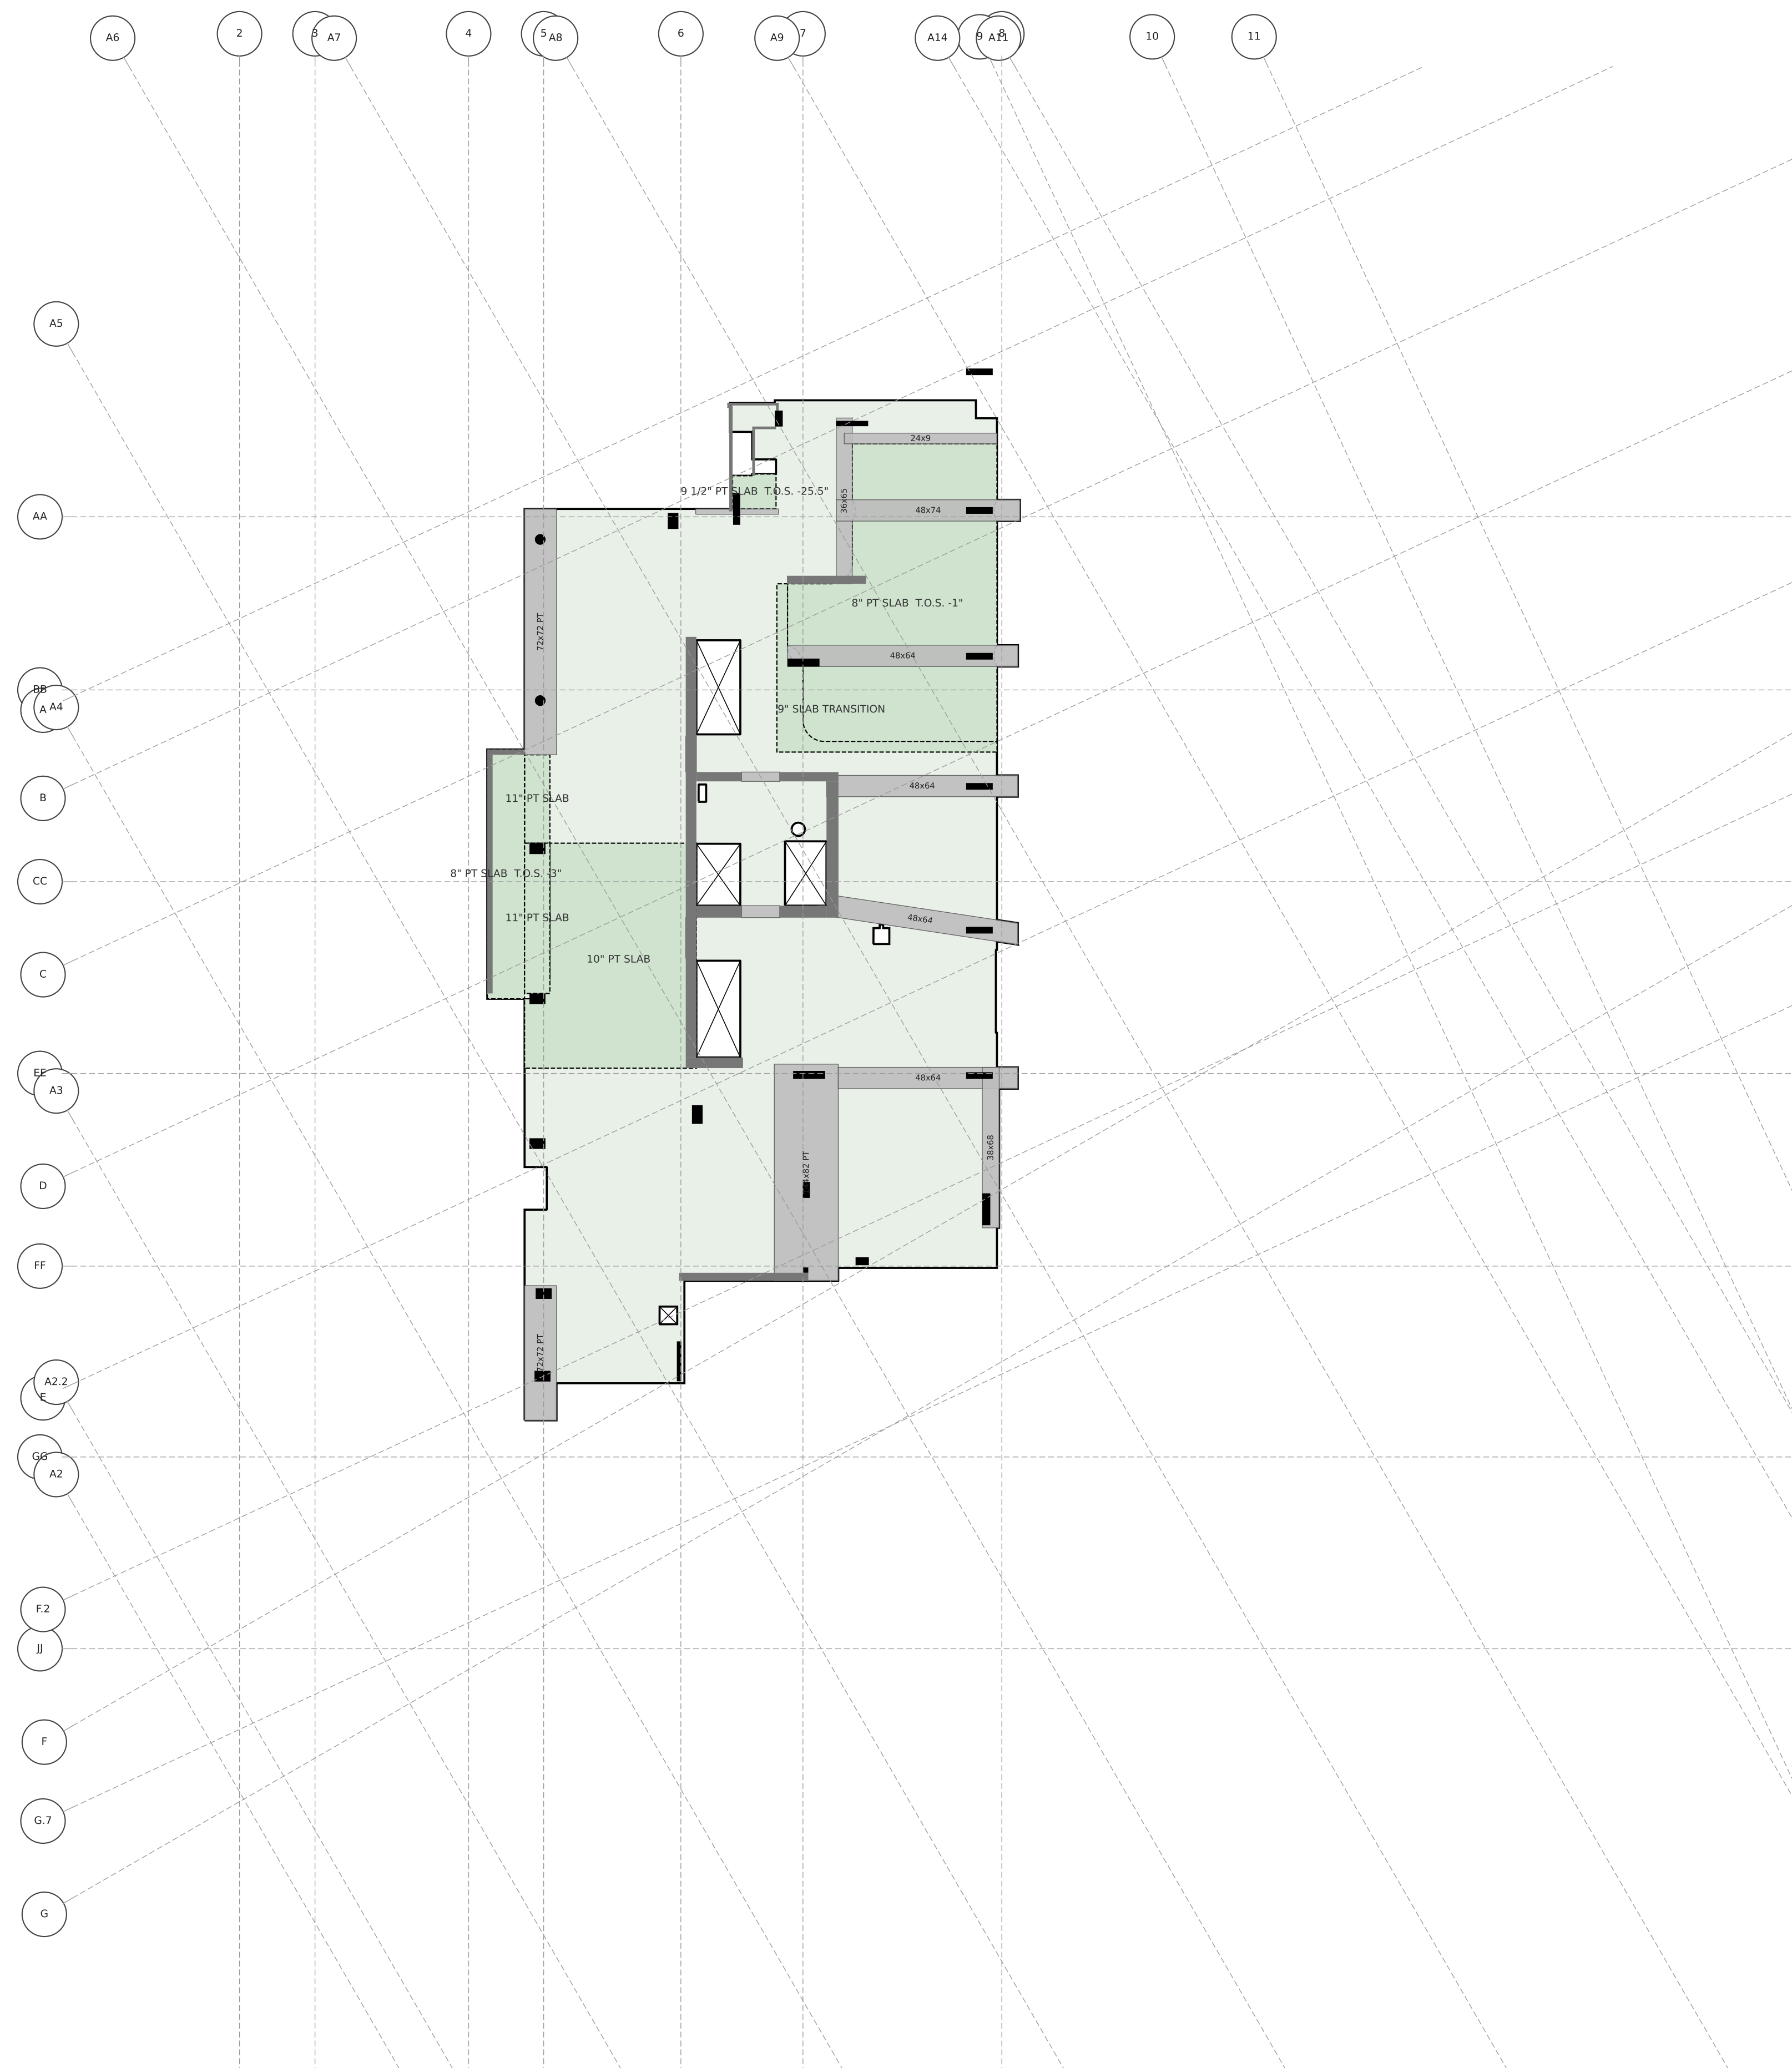

1268 KALAE


LEVEL 5 FLOOR PLAN

T.O.S. 53'-1" · typical slab 8" · scale 1" = 20'

Generated from HI_KALAE_MCC_ST.ifc (Revit scope model) for the McClone Reshore Calculator — geometry only; loading marks are drawn in the calculator.

S06

sheet 6 of 42

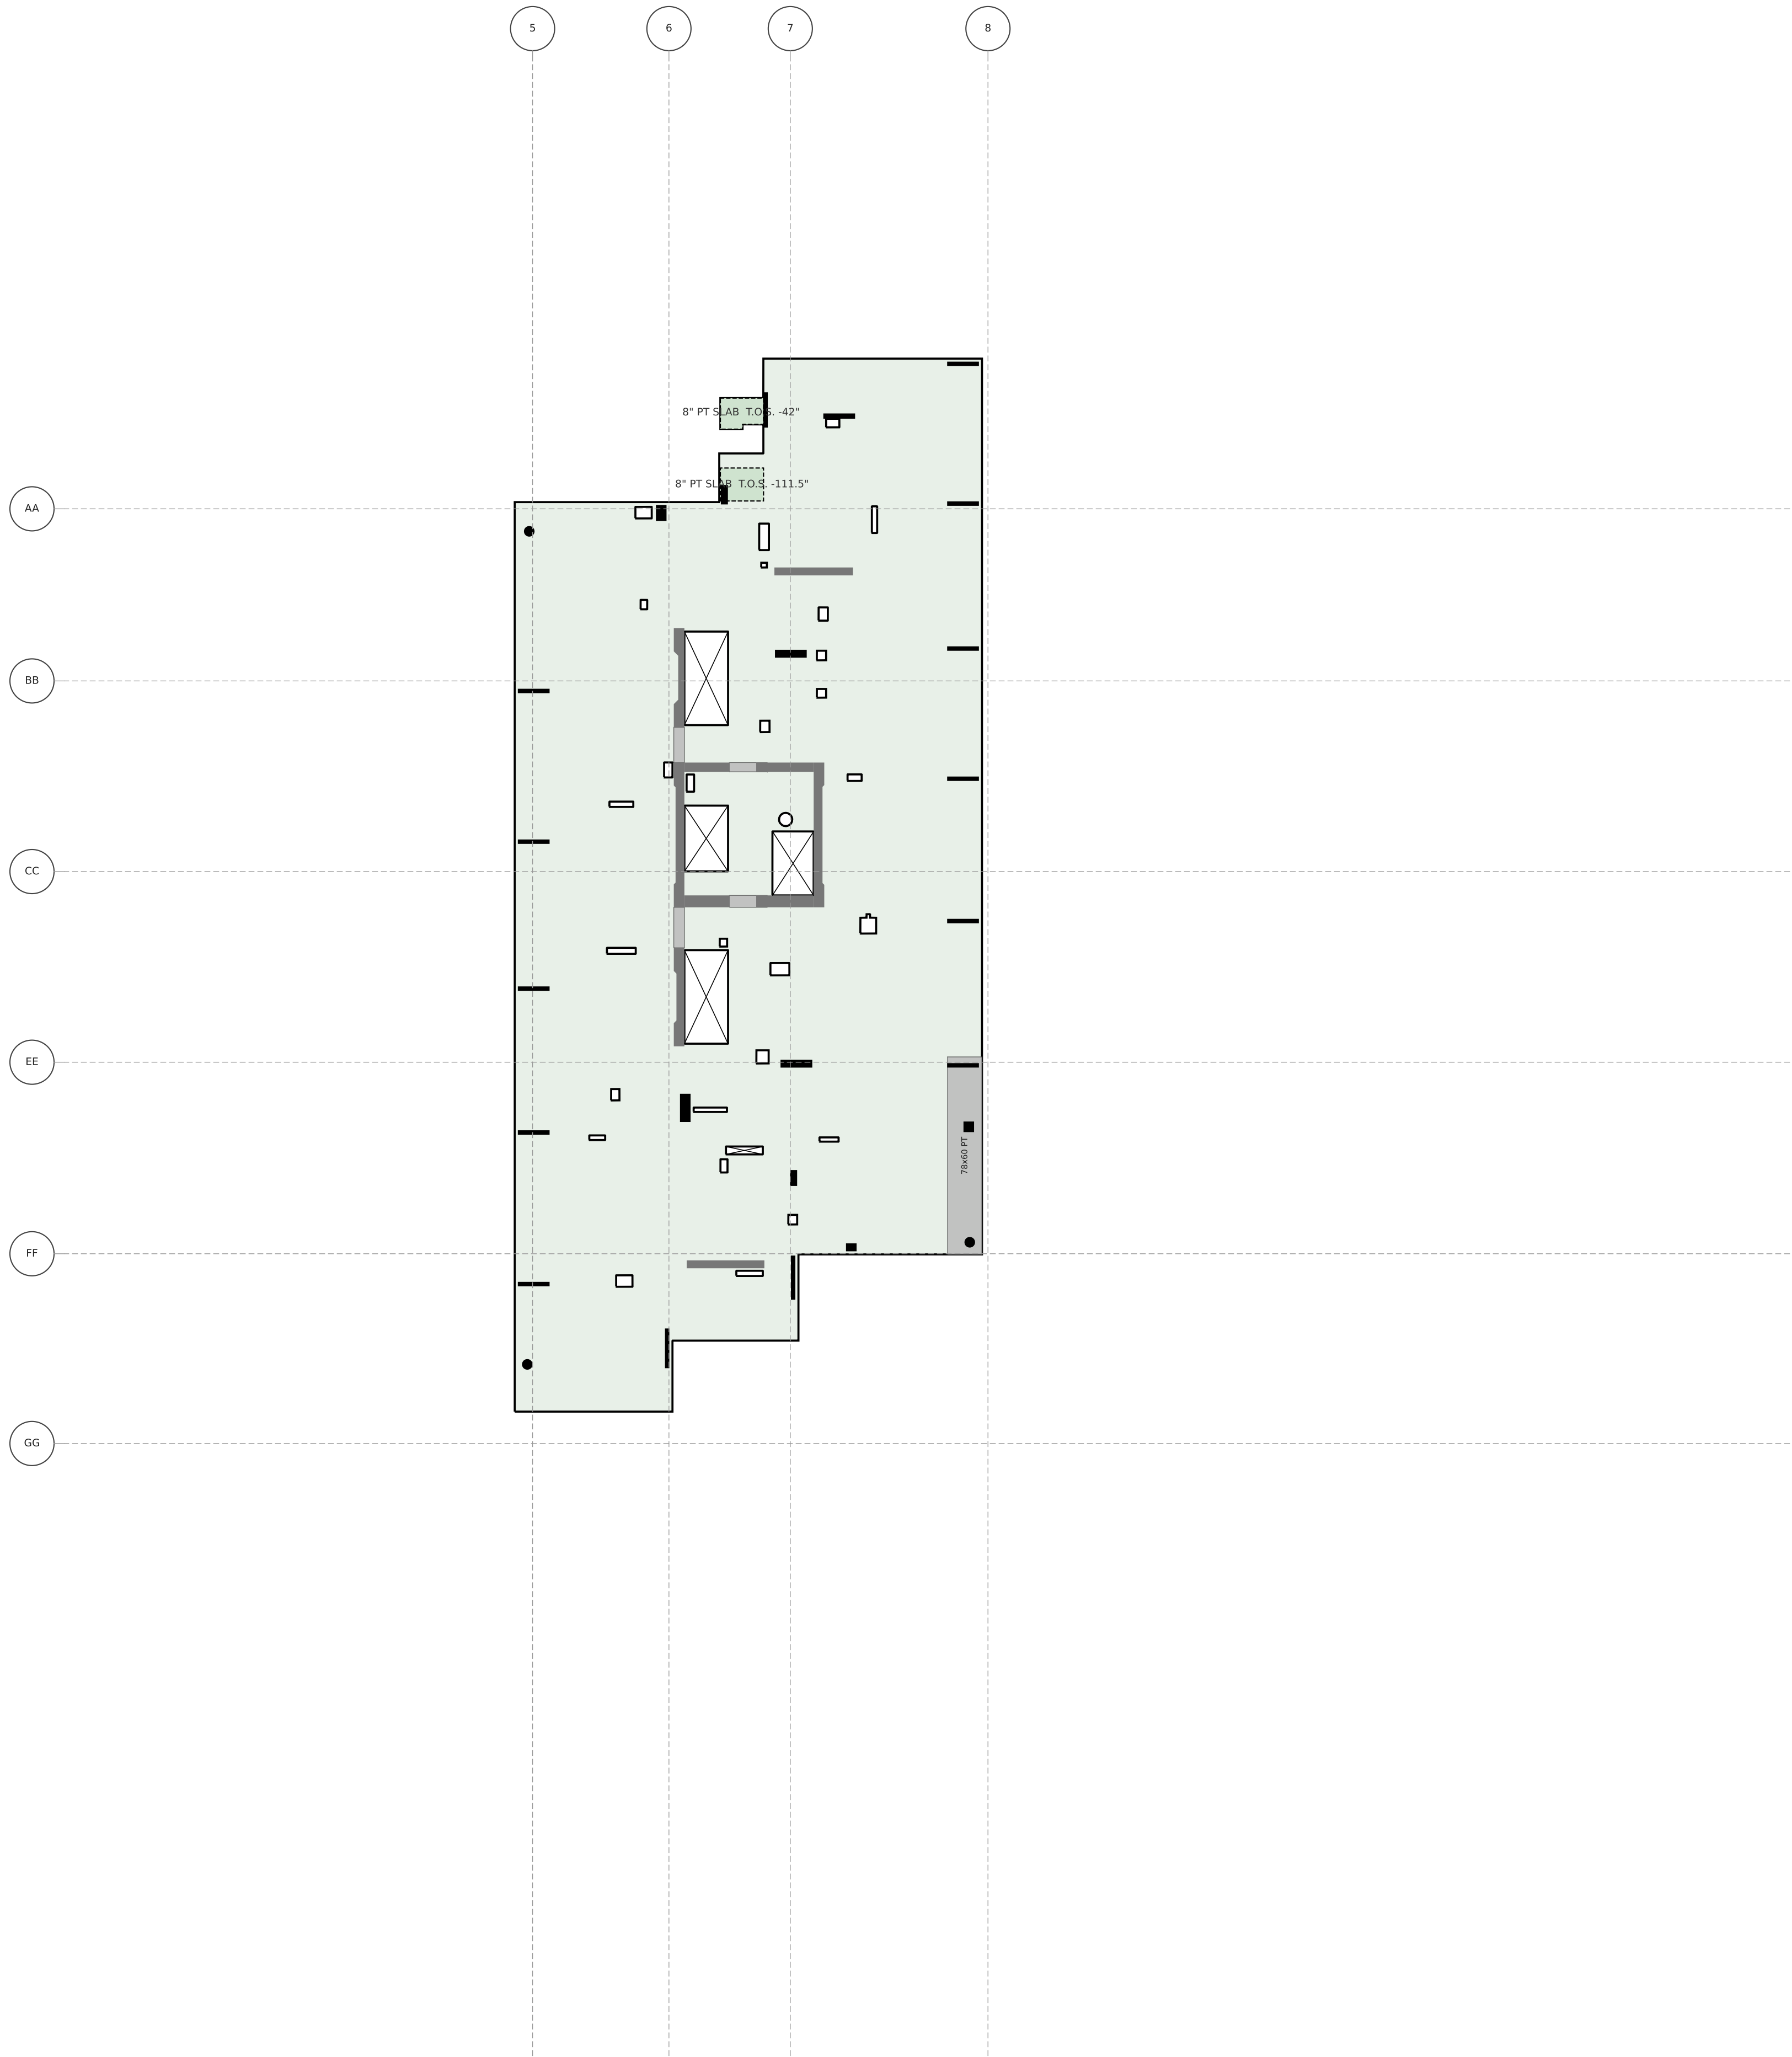


1268 KALAE

LEVEL 6 FLOOR PLAN

T.O.S. 68'-3" · typical slab 7 1/2" · scale 1" = 20'

Generated from HJ_KALAE_MCC_ST.ifc (Revit scope model) for the McClone Reshore Calculator — geometry only; loading marks are drawn in the calculator.

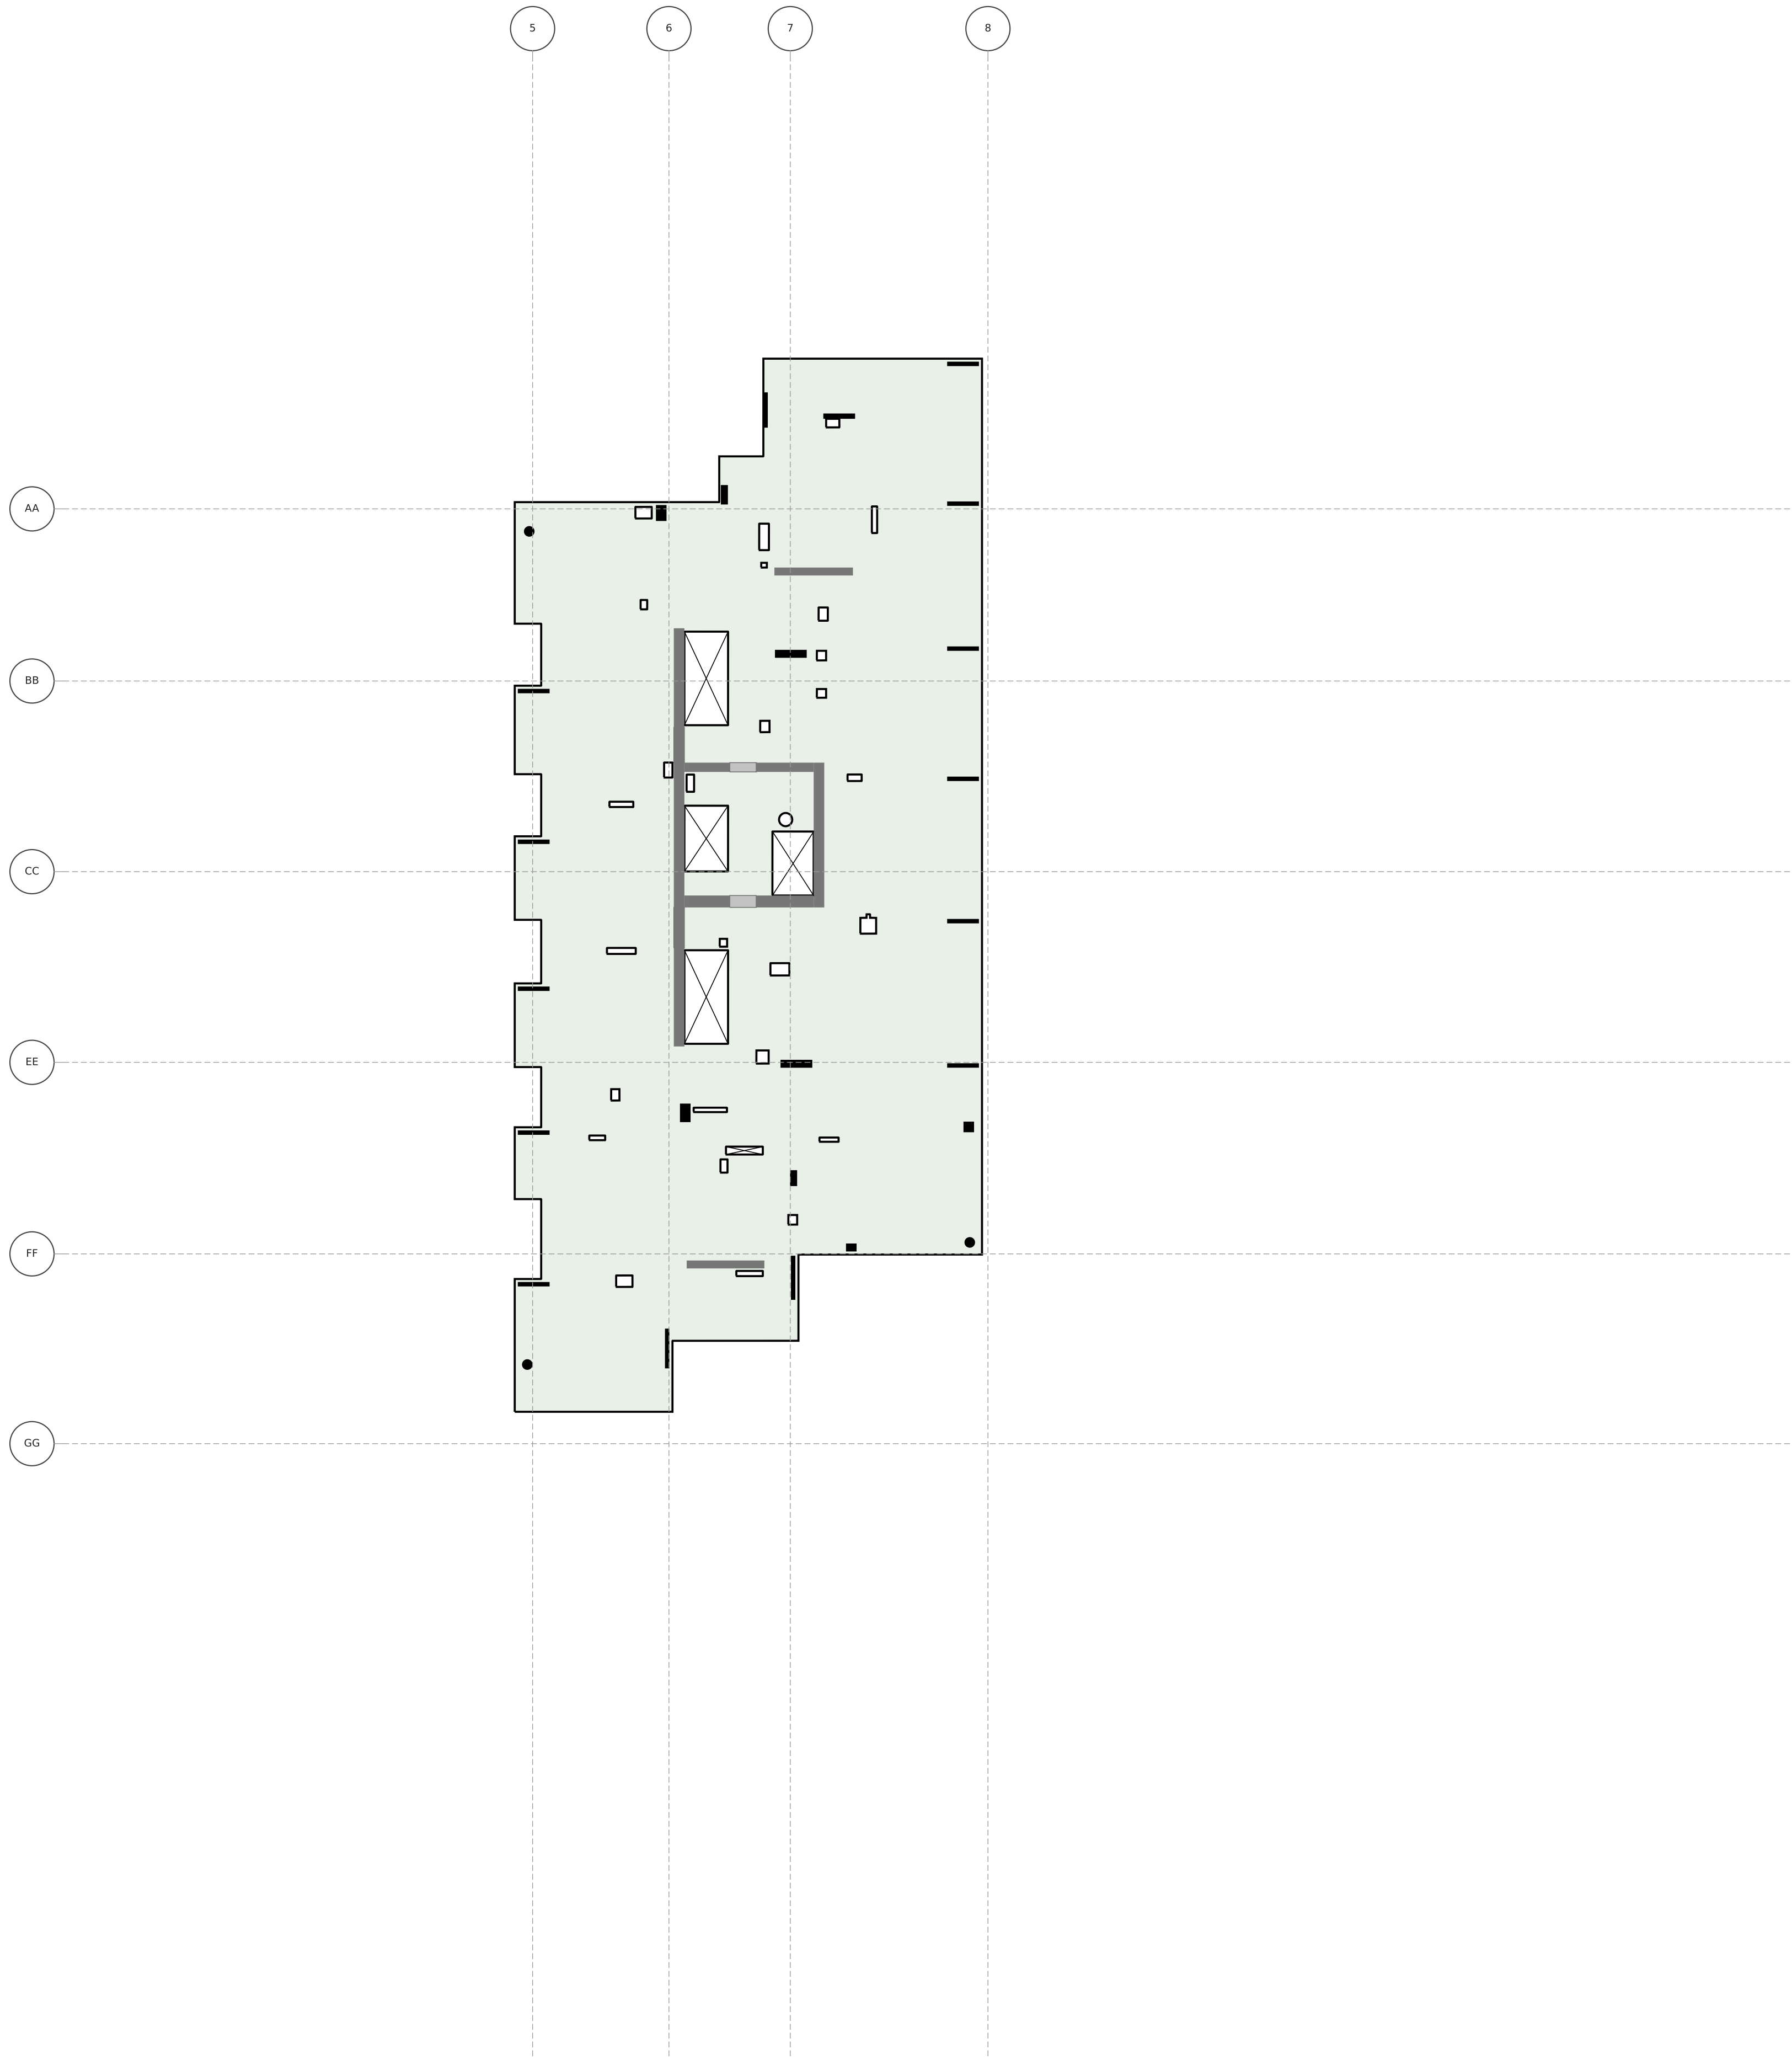


1268 KALAE

LEVEL 7 FLOOR PLAN

T.O.S. 77'-11 1/2" · typical slab 7 1/2" · scale 1" = 20'

Generated from HI_KALAE_MCC_ST.ifc (Revit scope model) for the McClone Reshore Calculator — geometry only; loading marks are drawn in the calculator.

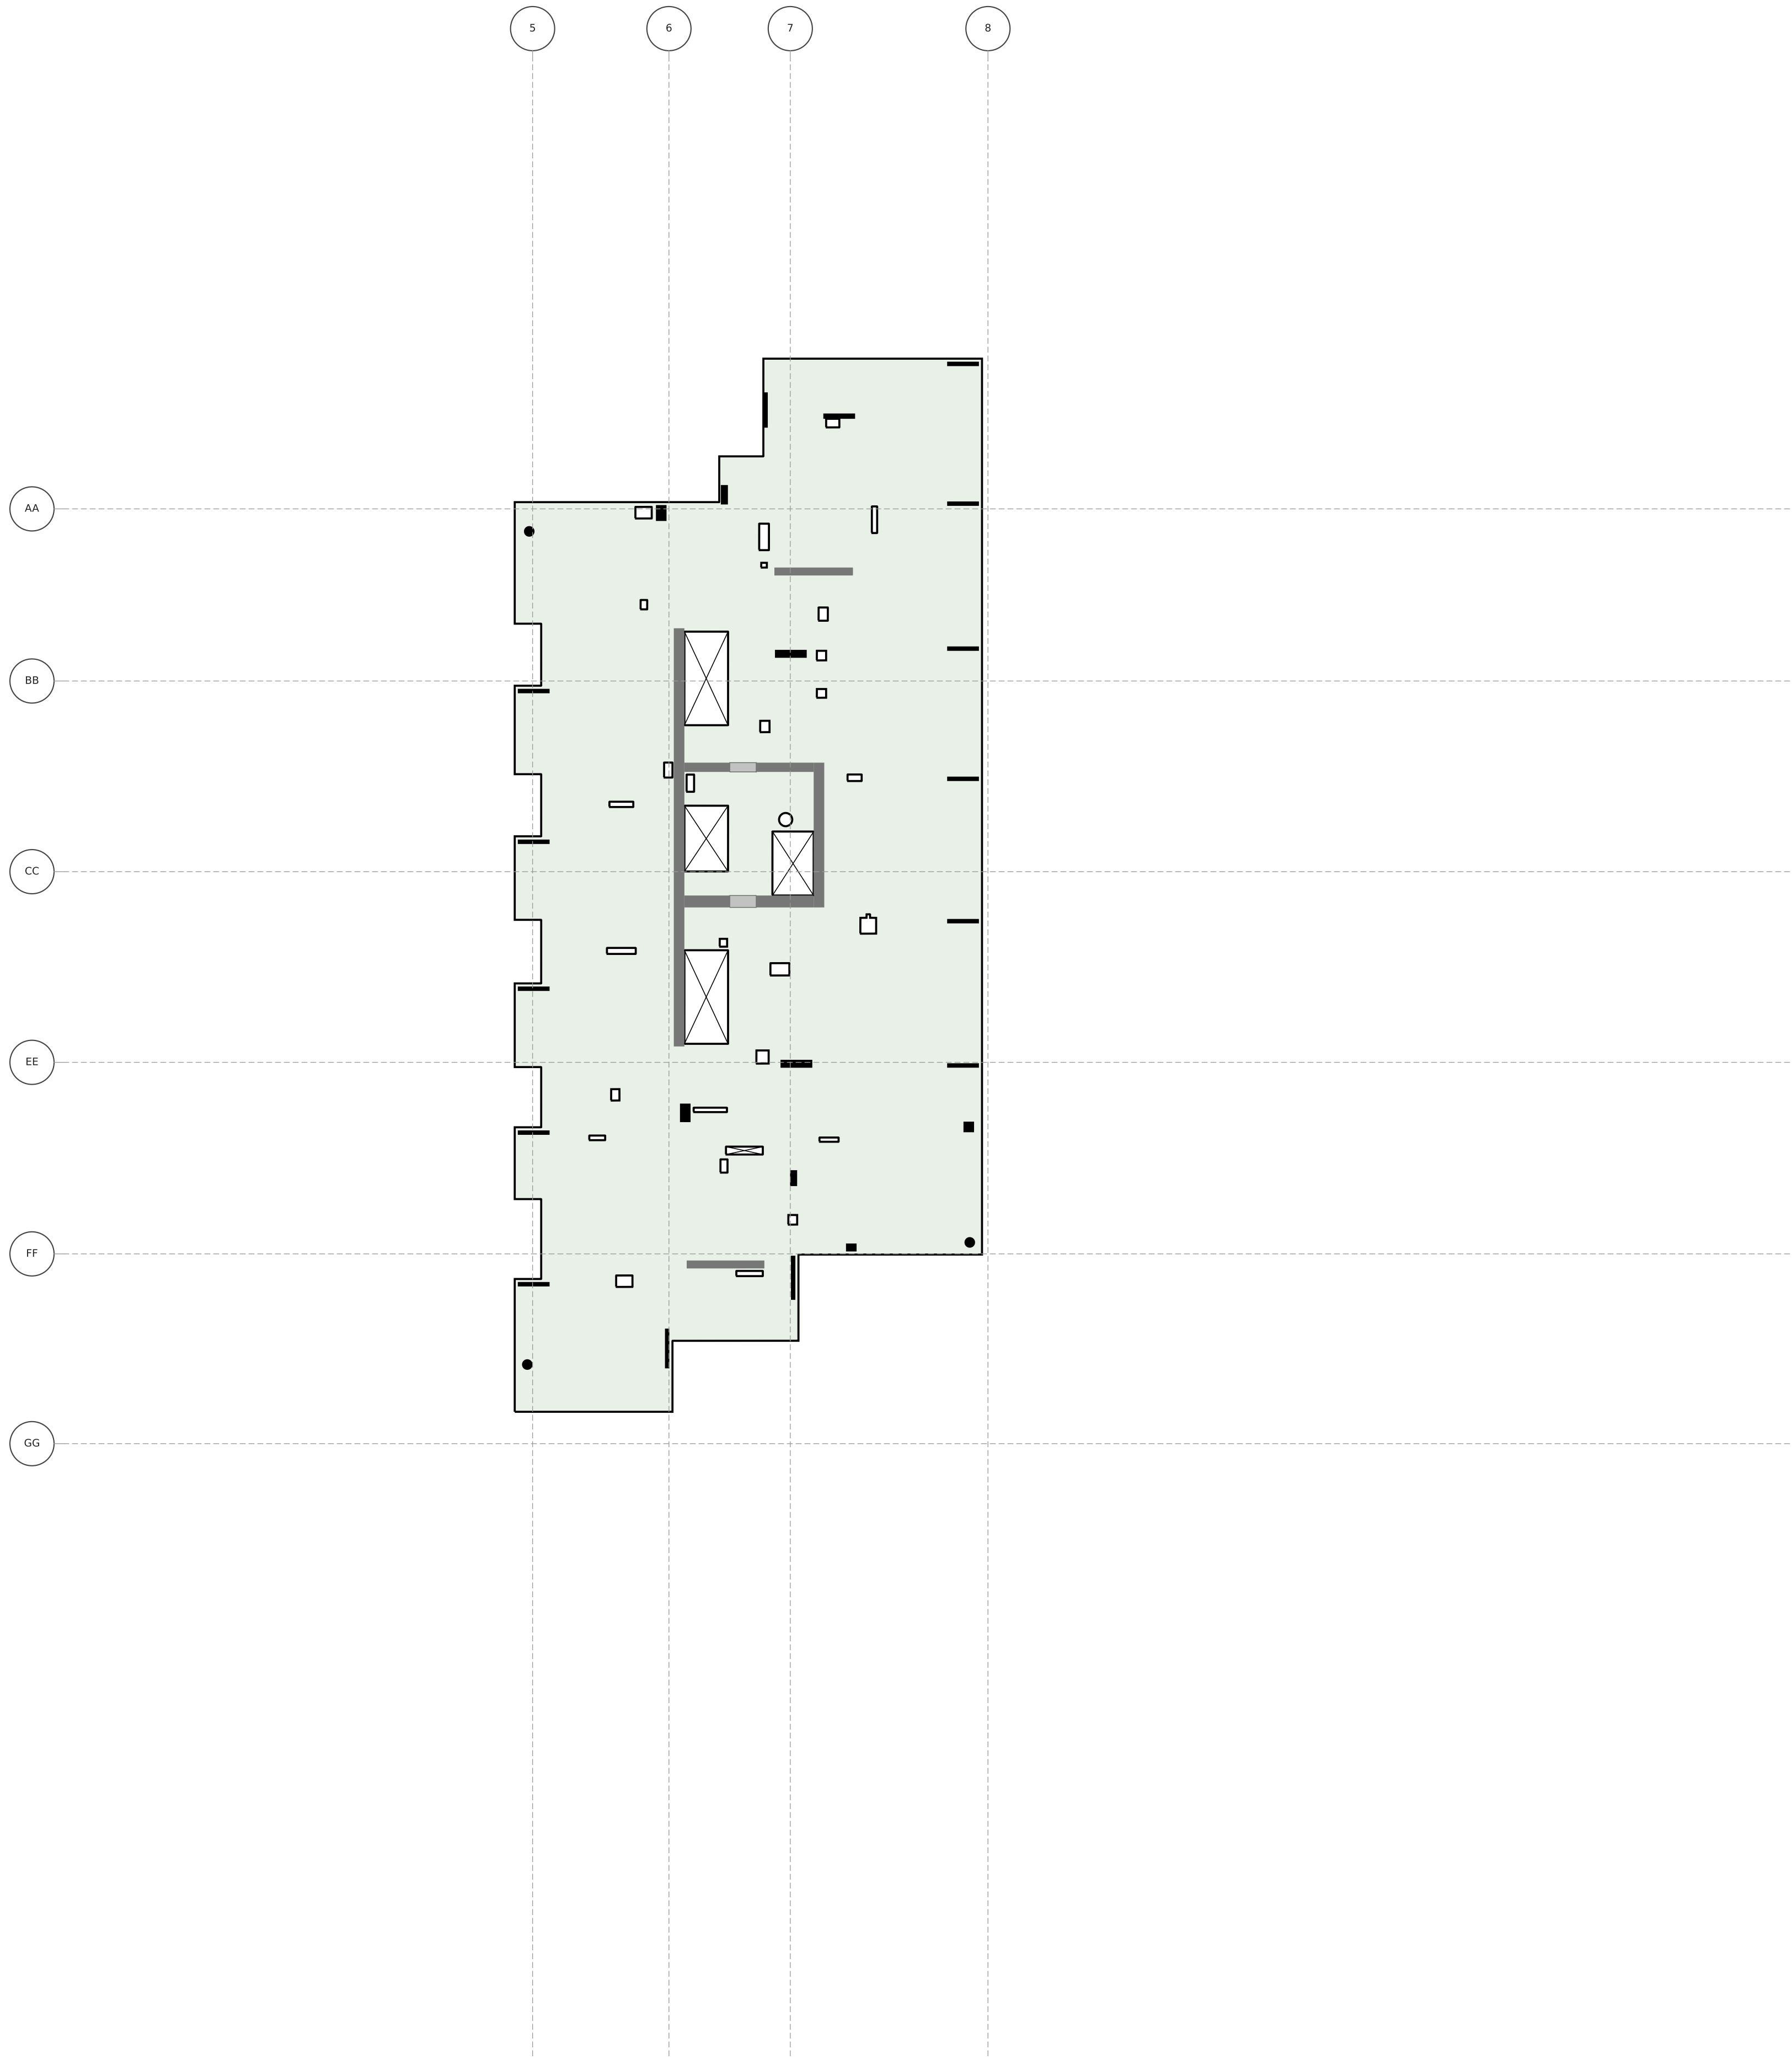


1268 KALAE

LEVEL 8 FLOOR PLAN

T.O.S. 87'-8" · typical slab 7 1/2" · scale 1" = 20'

Generated from HJ_KALAE_MCC_ST.ifc (Revit scope model) for the McClone Reshore Calculator — geometry only; loading marks are drawn in the calculator.

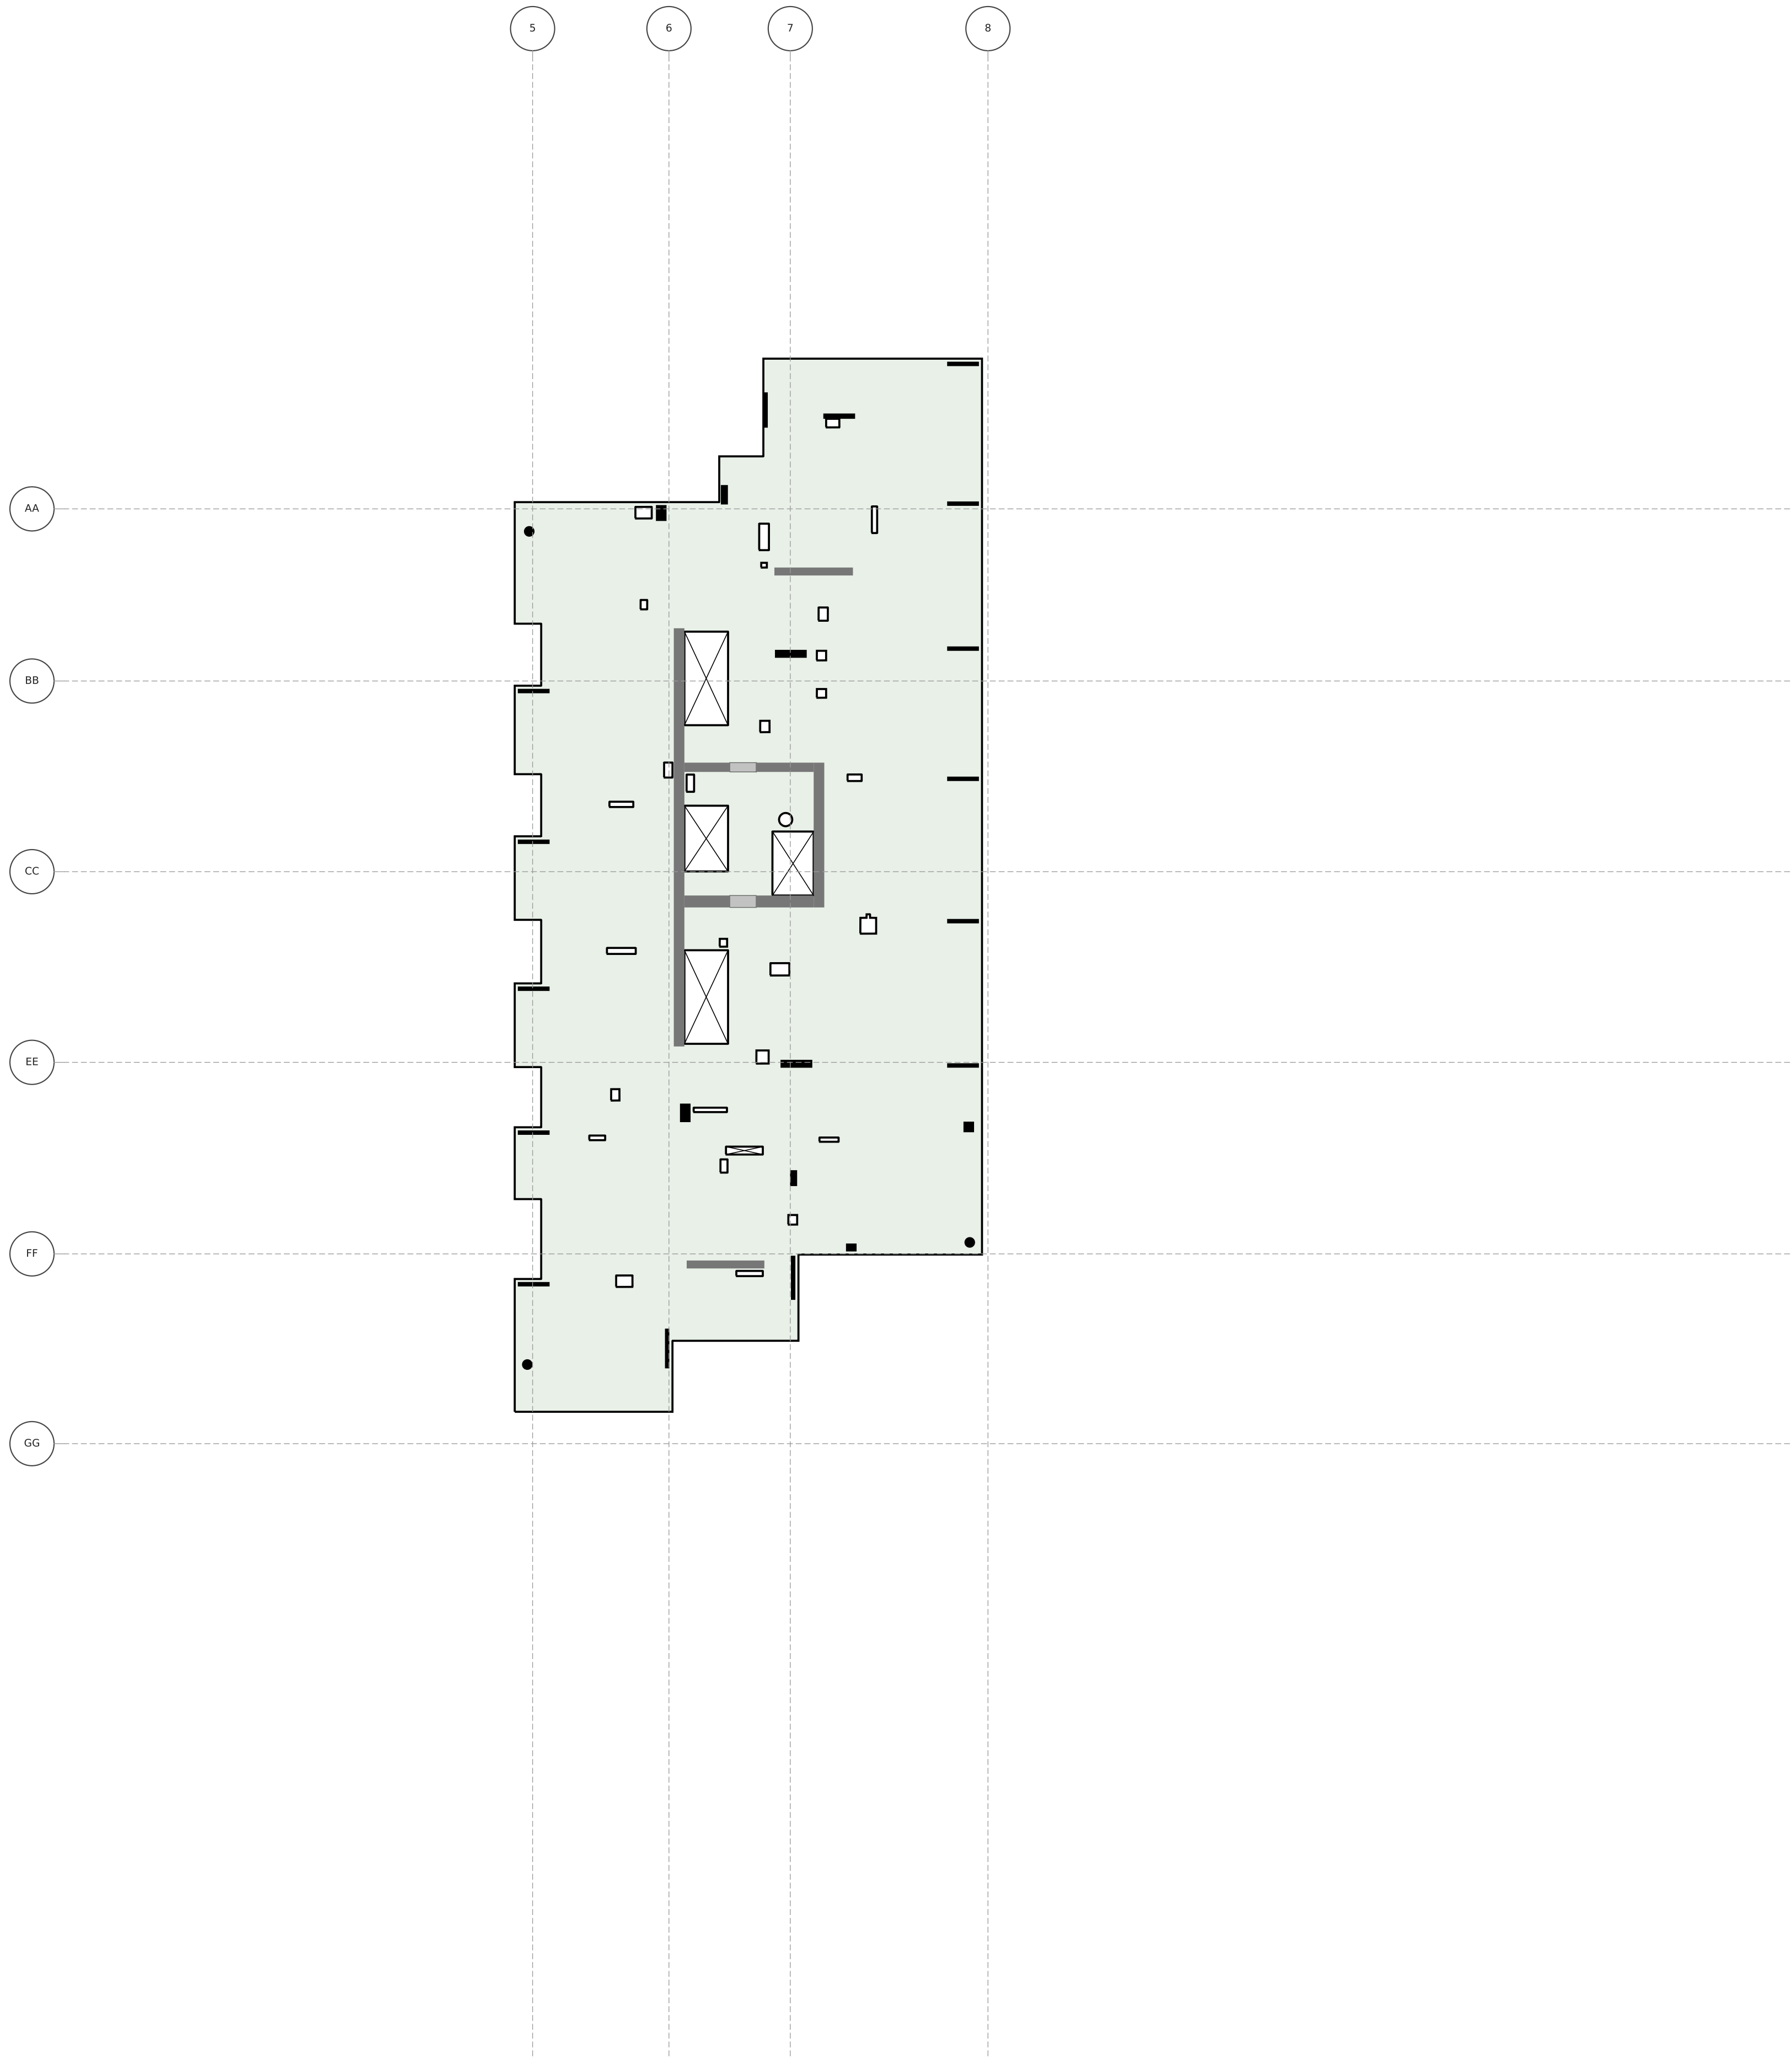


1268 KALAE

LEVEL 9 FLOOR PLAN

T.O.S. 97'-4 1/2" · typical slab 7 1/2" · scale 1" = 20'

Generated from HI_KALAE_MCC_ST.ifc (Revit scope model) for the McClone Reshore Calculator — geometry only; loading marks are drawn in the calculator.

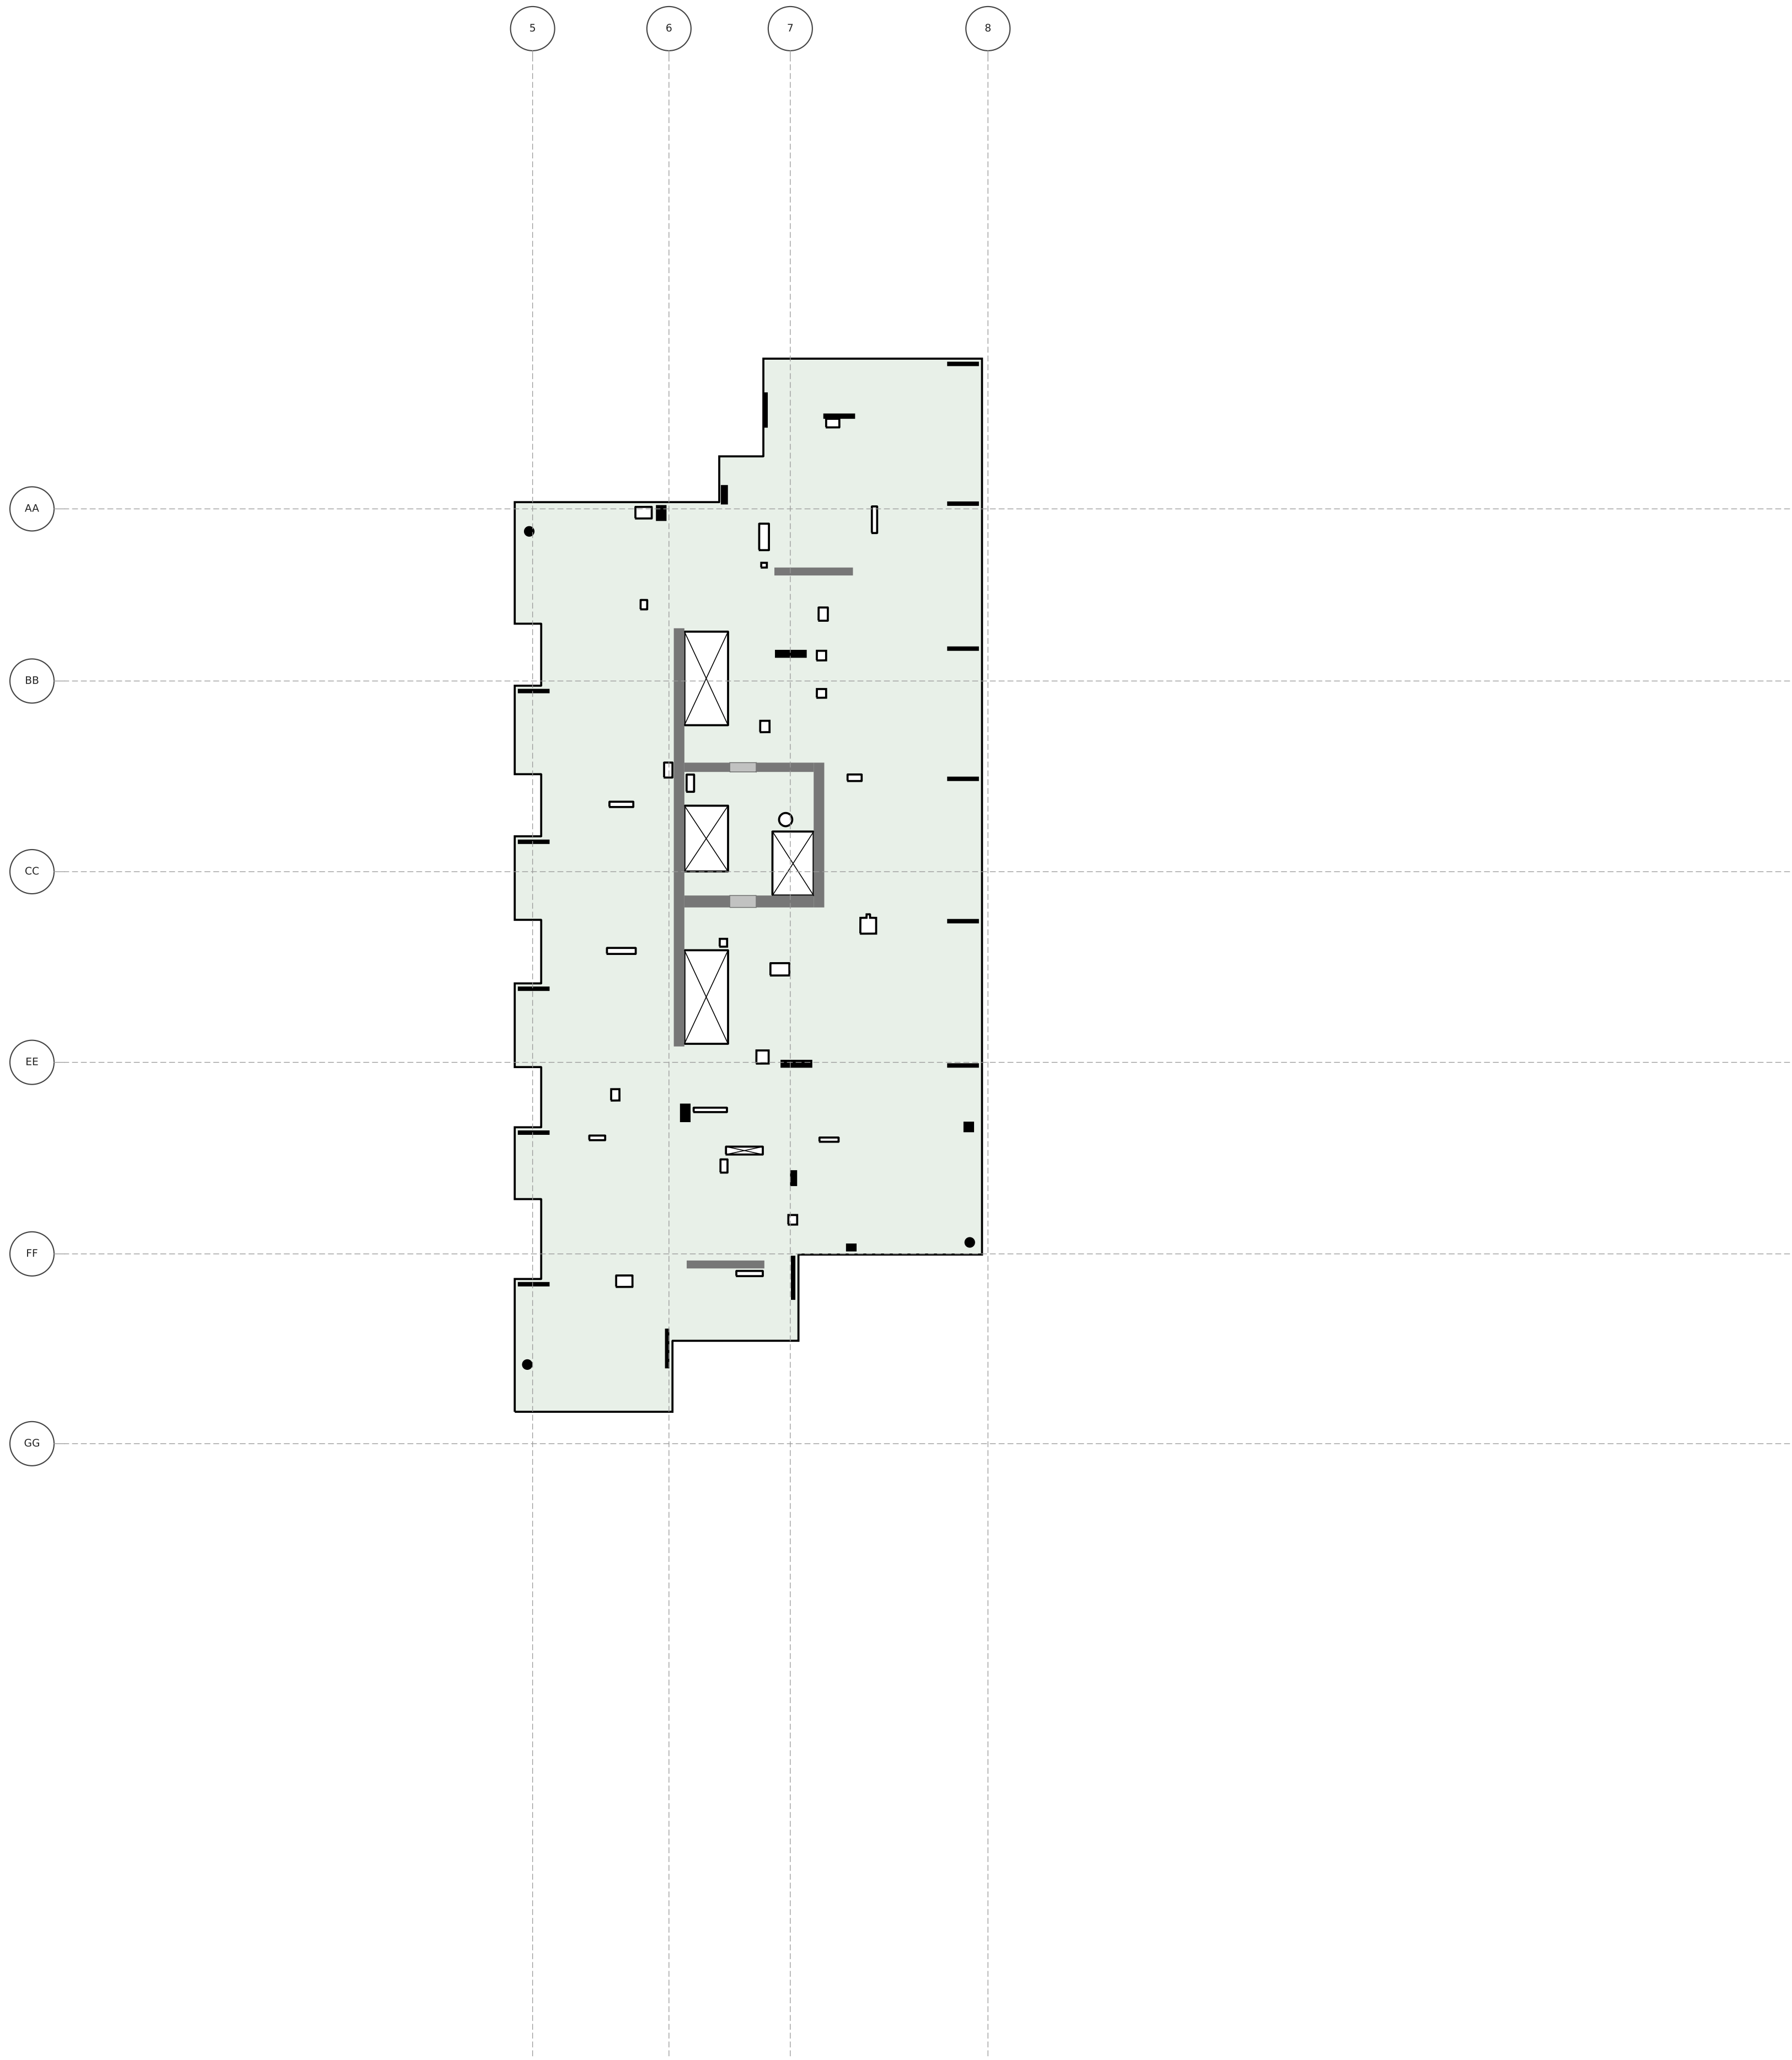


1268 KALAE

LEVEL 10 FLOOR PLAN

T.O.S. 107'-1" · typical slab 7 1/2" · scale 1" = 20'

Generated from HI_KALAE_MCC_ST.ifc (Revit scope model) for the McClone Reshore Calculator — geometry only; loading marks are drawn in the calculator.

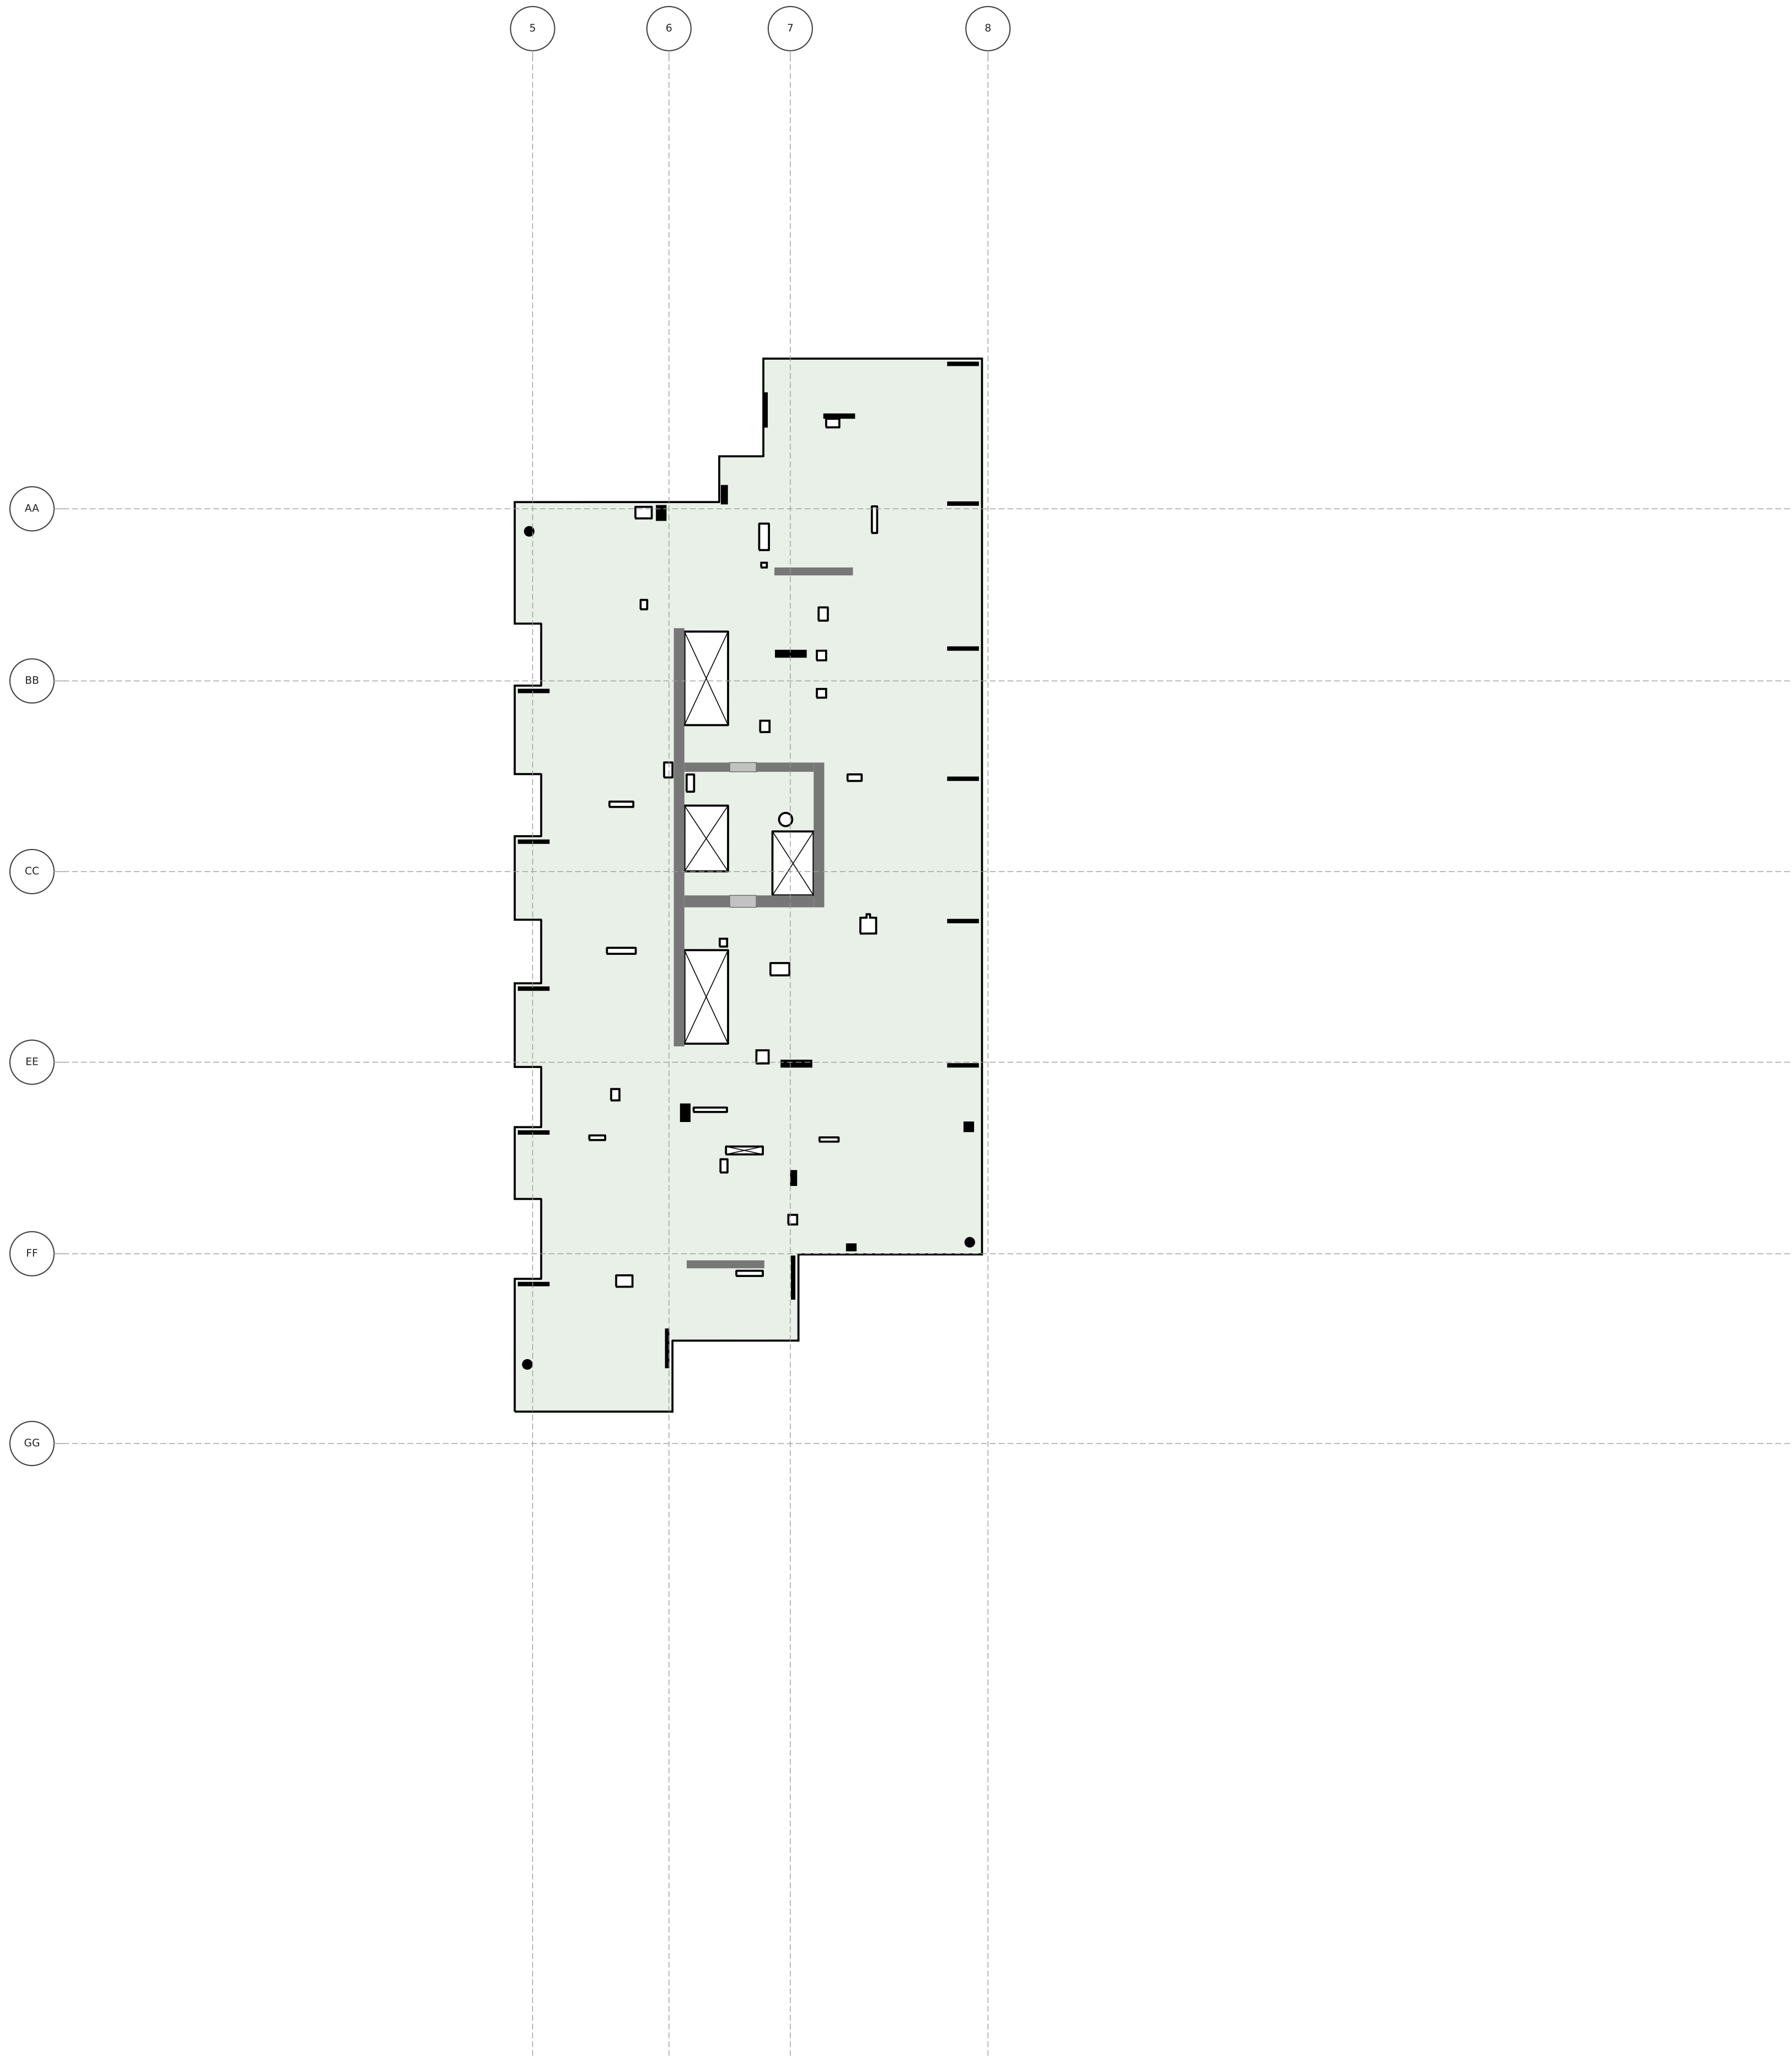


1268 KALAE

LEVEL 11 FLOOR PLAN

T.O.S. 116'-9 1/2" · typical slab 7 1/2" · scale 1" = 20'

Generated from HI_KALAE_MCC_ST.ifc (Revit scope model) for the McClone Reshore Calculator — geometry only; loading marks are drawn in the calculator.

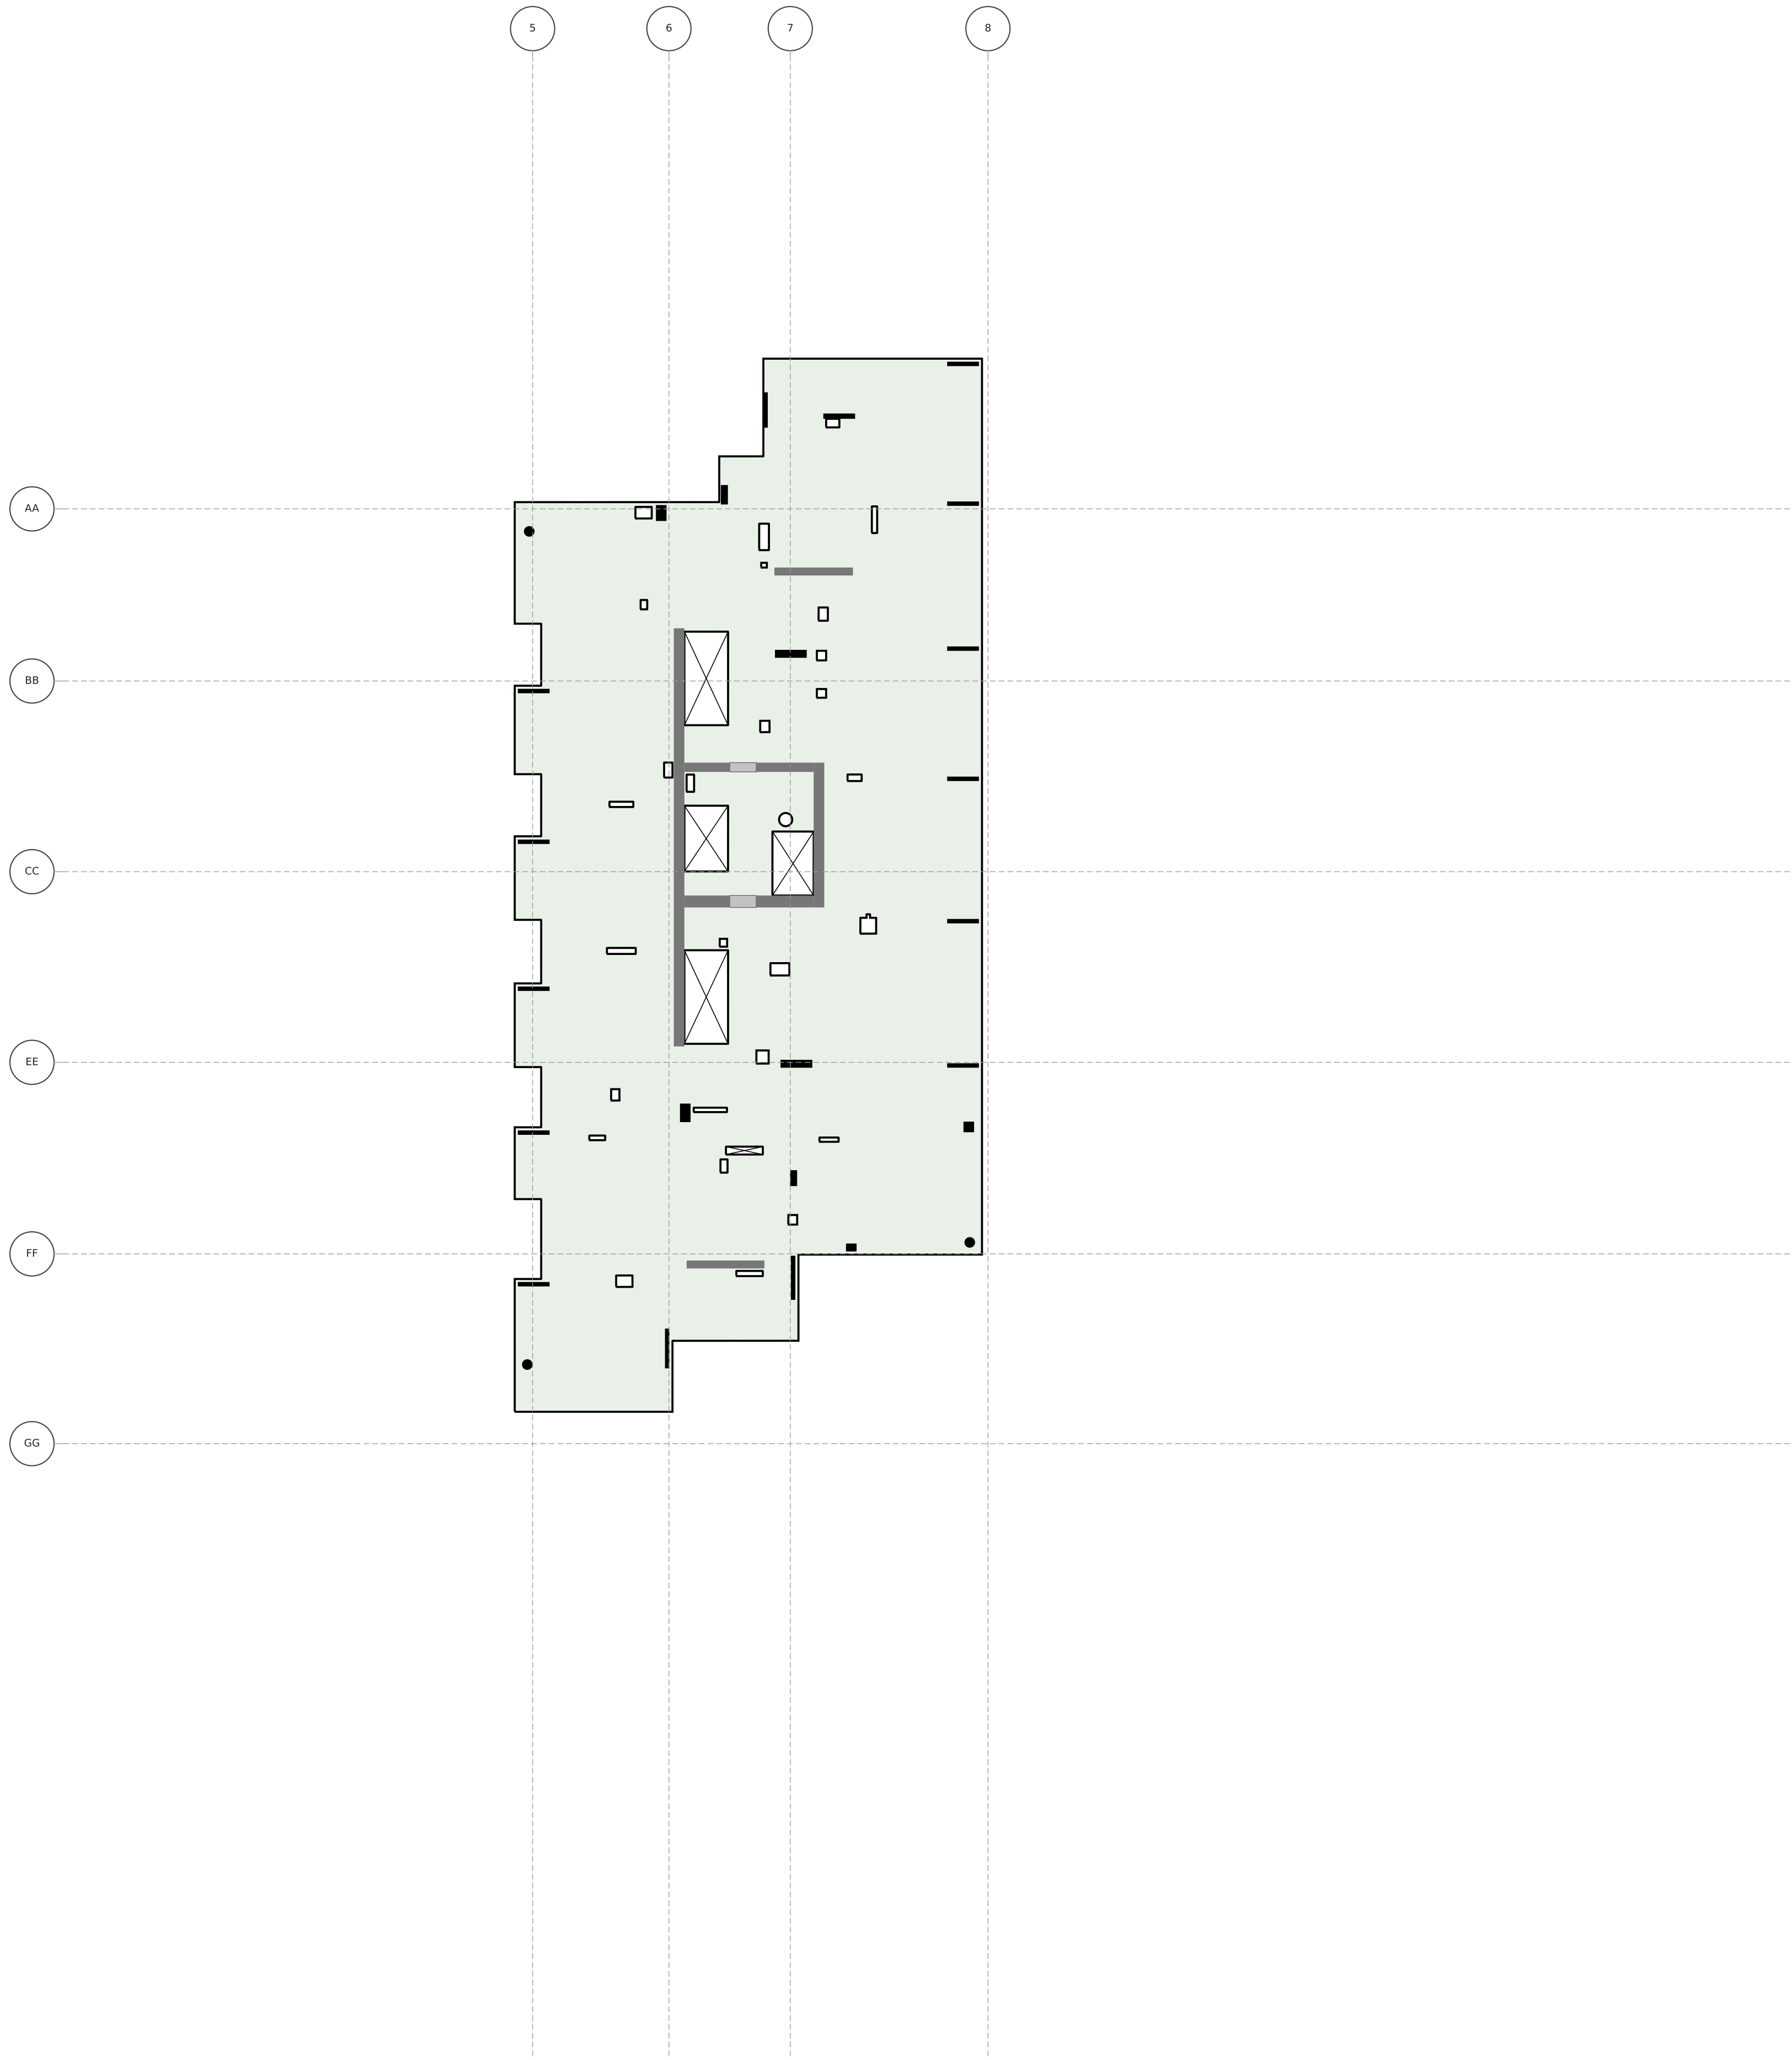


1268 KALAE

LEVEL 12 FLOOR PLAN

T.O.S. 126'-6" · typical slab 7 1/2" · scale 1" = 20'

Generated from HI_KALAE_MCC_ST.ifc (Revit scope model) for the McClone Reshore Calculator — geometry only; loading marks are drawn in the calculator.

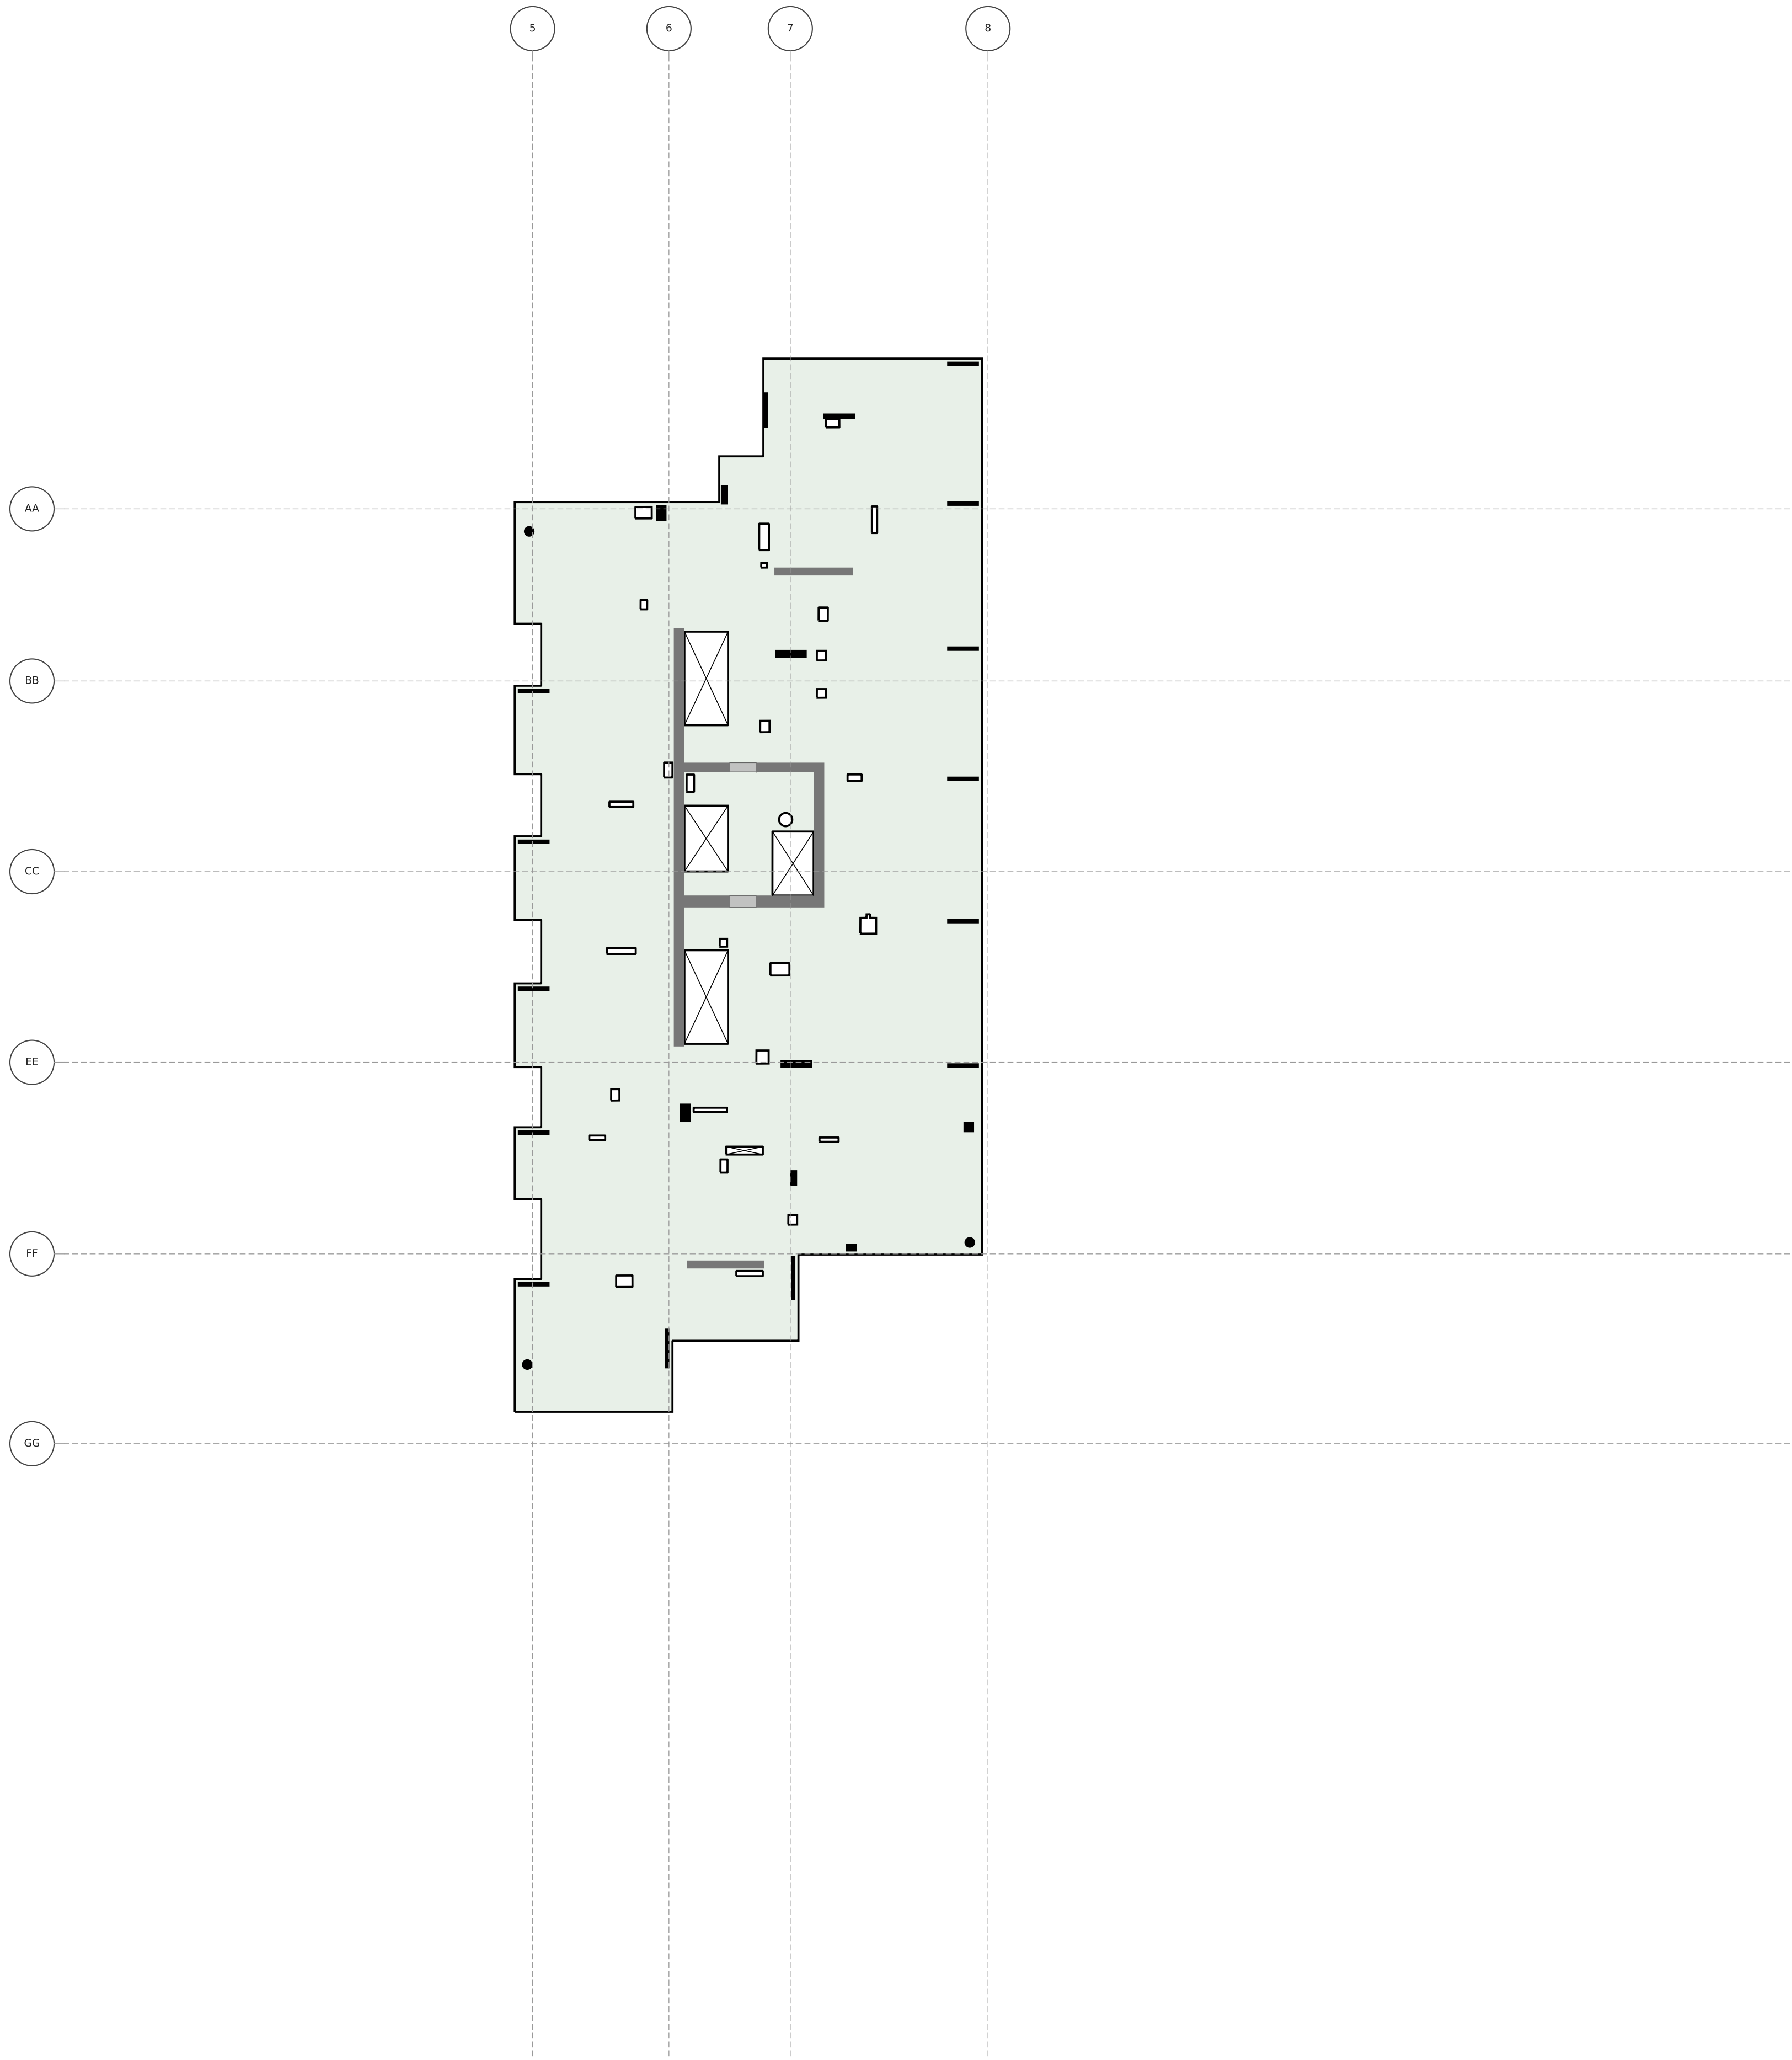


1268 KALAE

LEVEL 13 FLOOR PLAN

T.O.S. 136'-2 1/2" · typical slab 7 1/2" · scale 1" = 20'

Generated from HI_KALAE_MCC_ST.ifc (Revit scope model) for the McClone Reshore Calculator — geometry only; loading marks are drawn in the calculator.

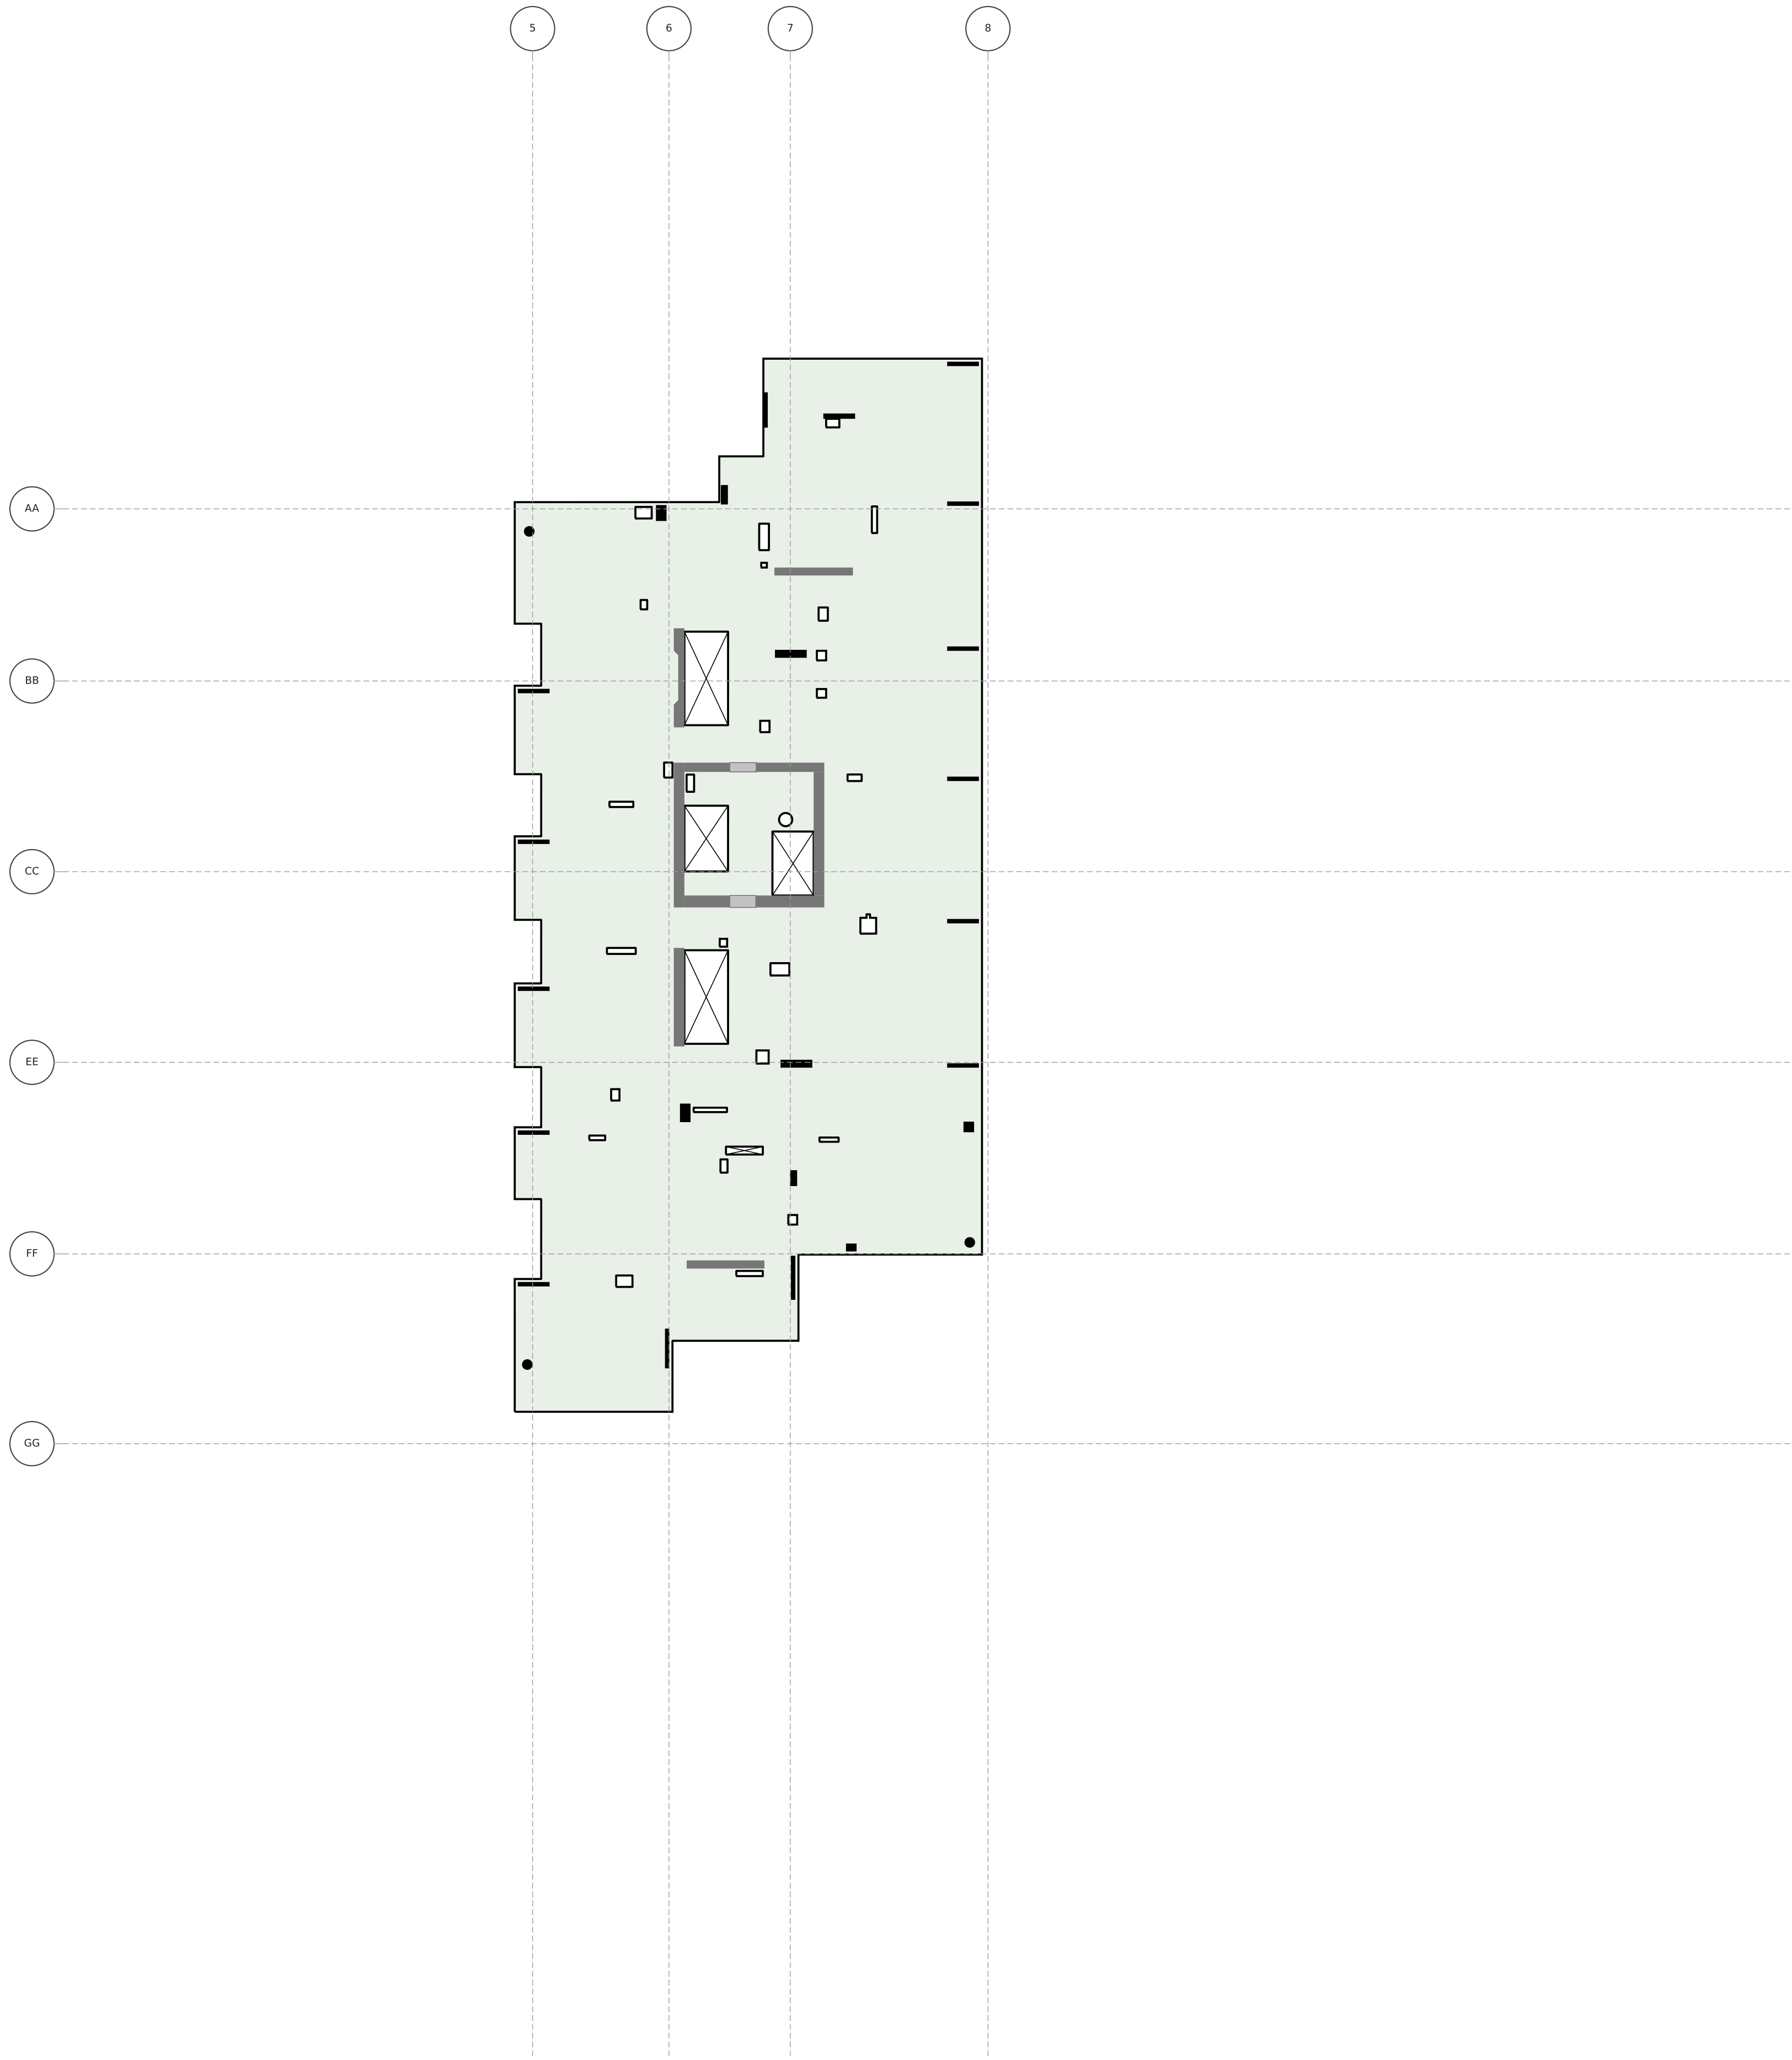


1268 KALAE

LEVEL 14 FLOOR PLAN


T.O.S. 145'-11" · typical slab 7 1/2" · scale 1" = 20'

Generated from HI_KALAE_MCC_ST.ifc (Revit scope model) for the McClone Reshore Calculator — geometry only; loading marks are drawn in the calculator.

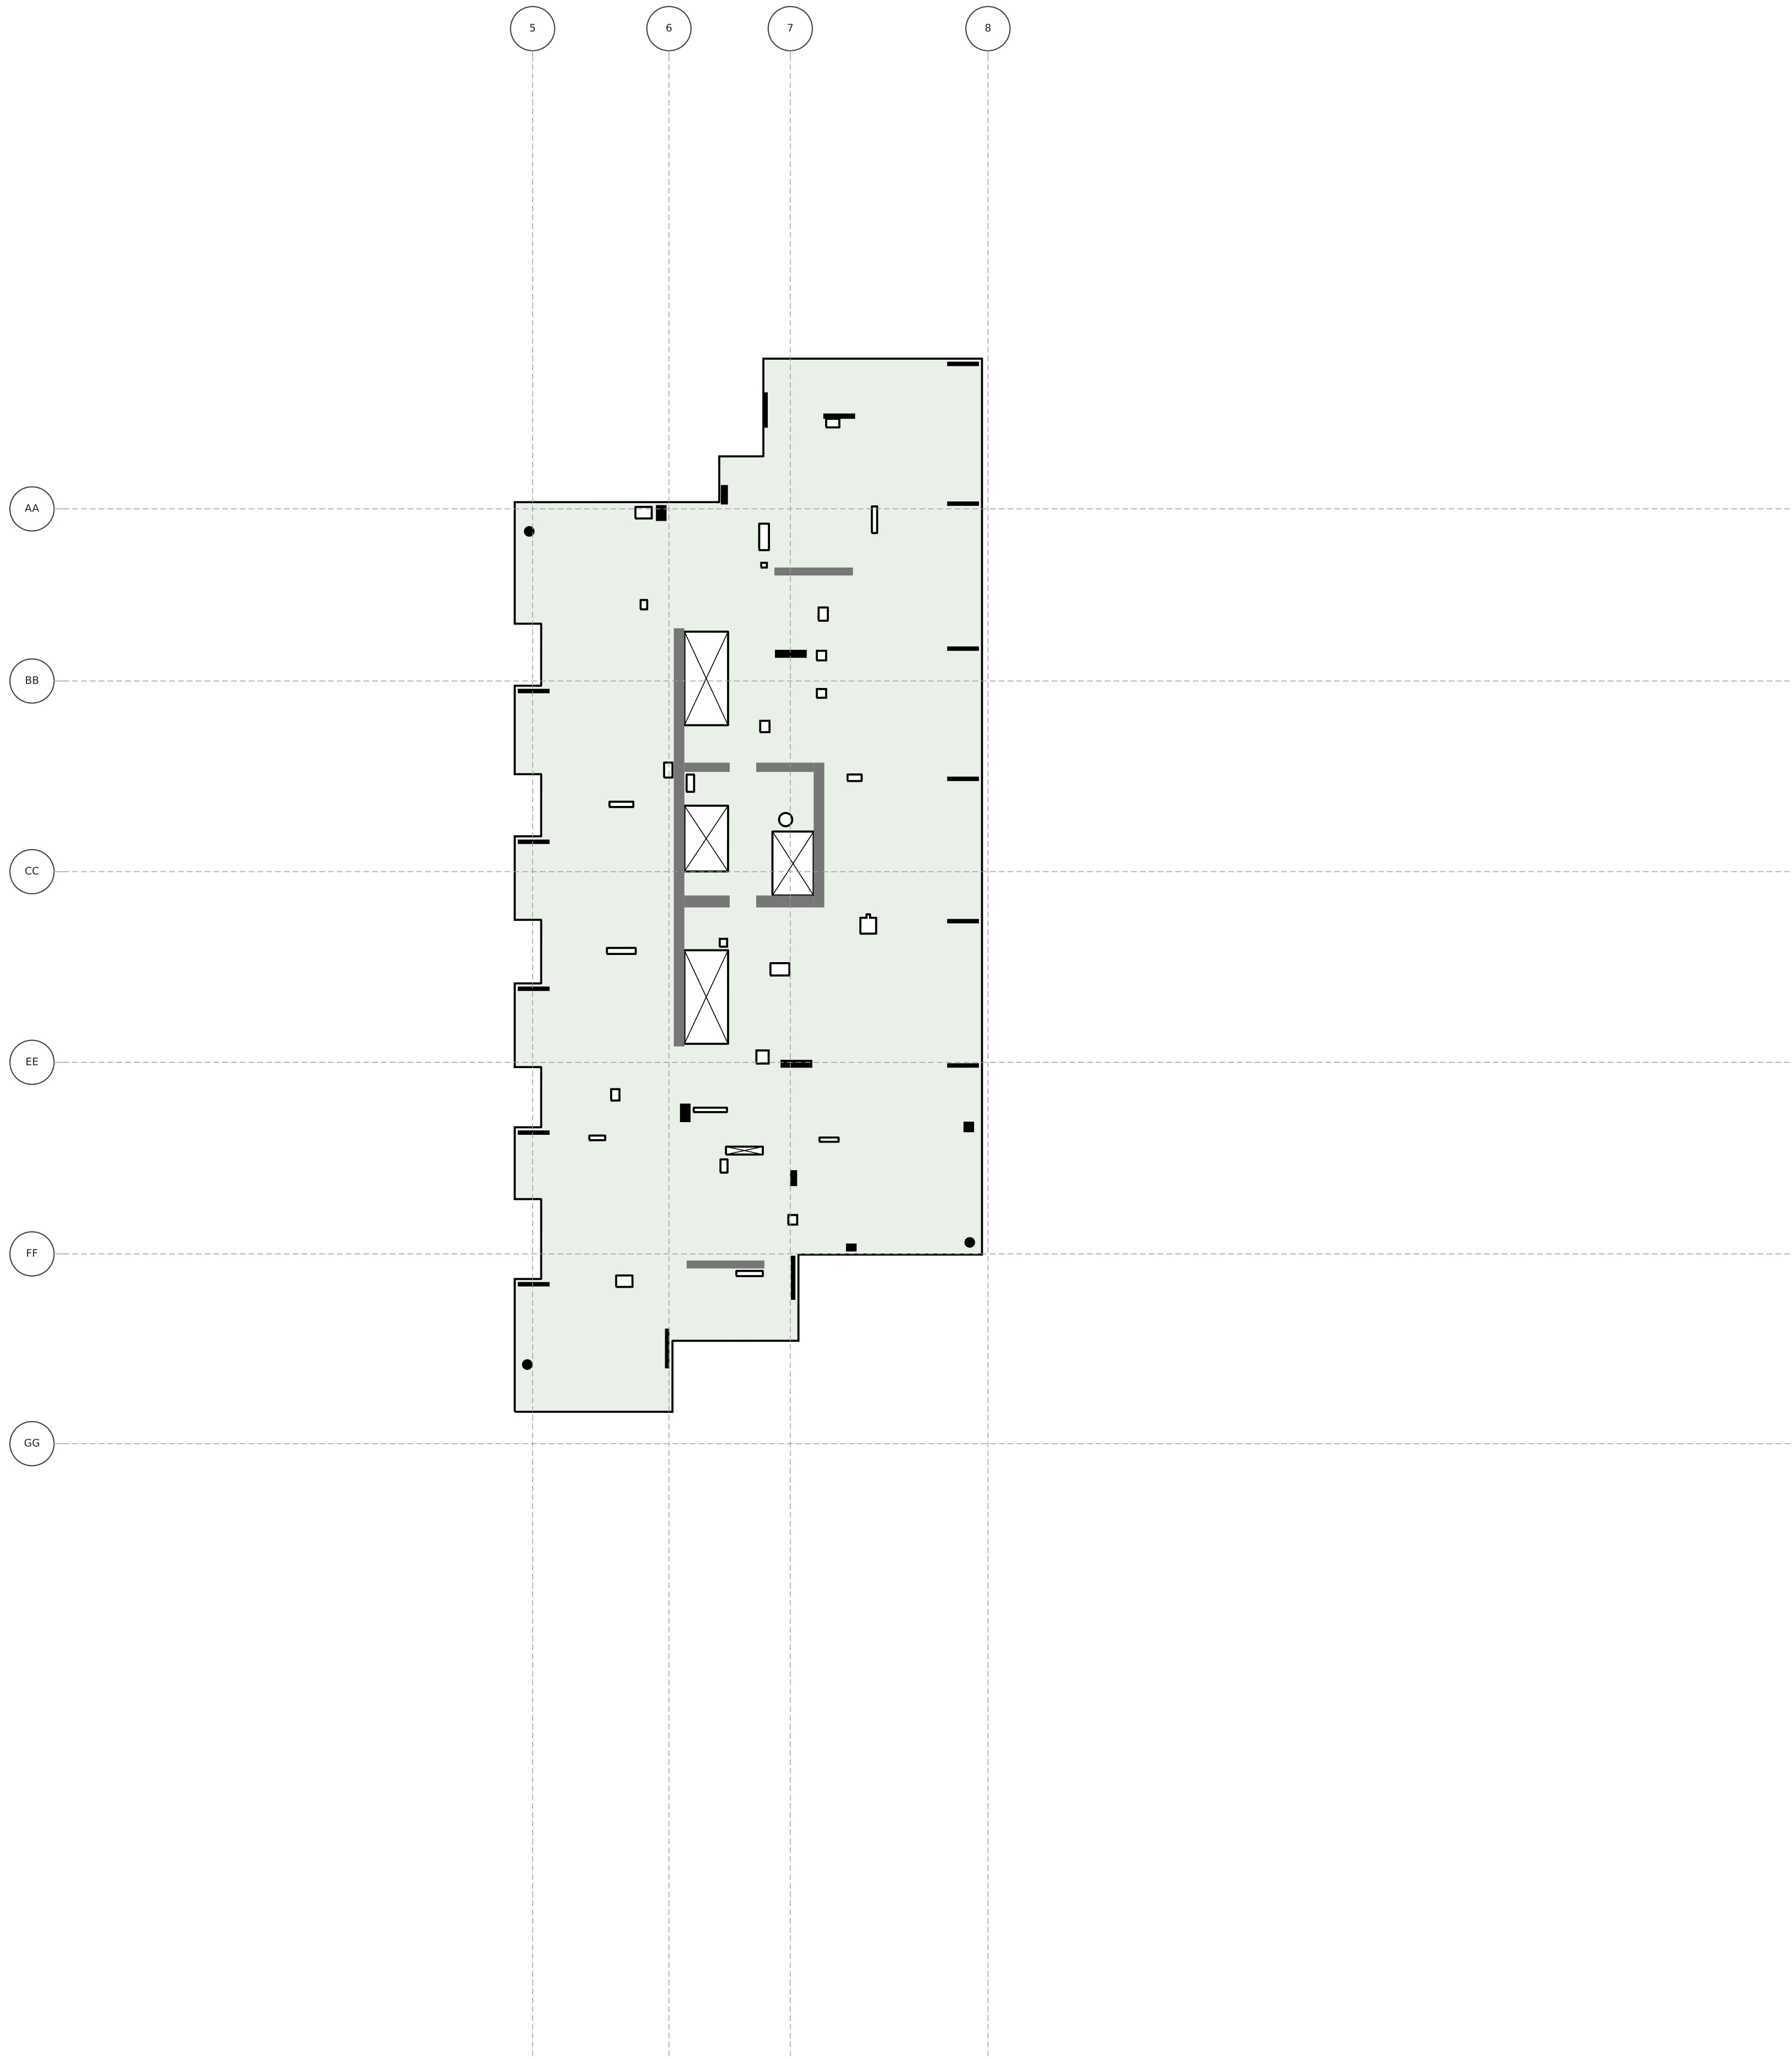

1268 KALAE
LEVEL 15 FLOOR PLAN

T.O.S. 155'-9 1/2" · typical slab 7 1/2" · scale 1" = 20'
Generated from HI_KALAE_MCC_ST.ifc (Revit scope model) for the McClone Reshore Calculator — geometry only; loading marks are drawn in the calculator.

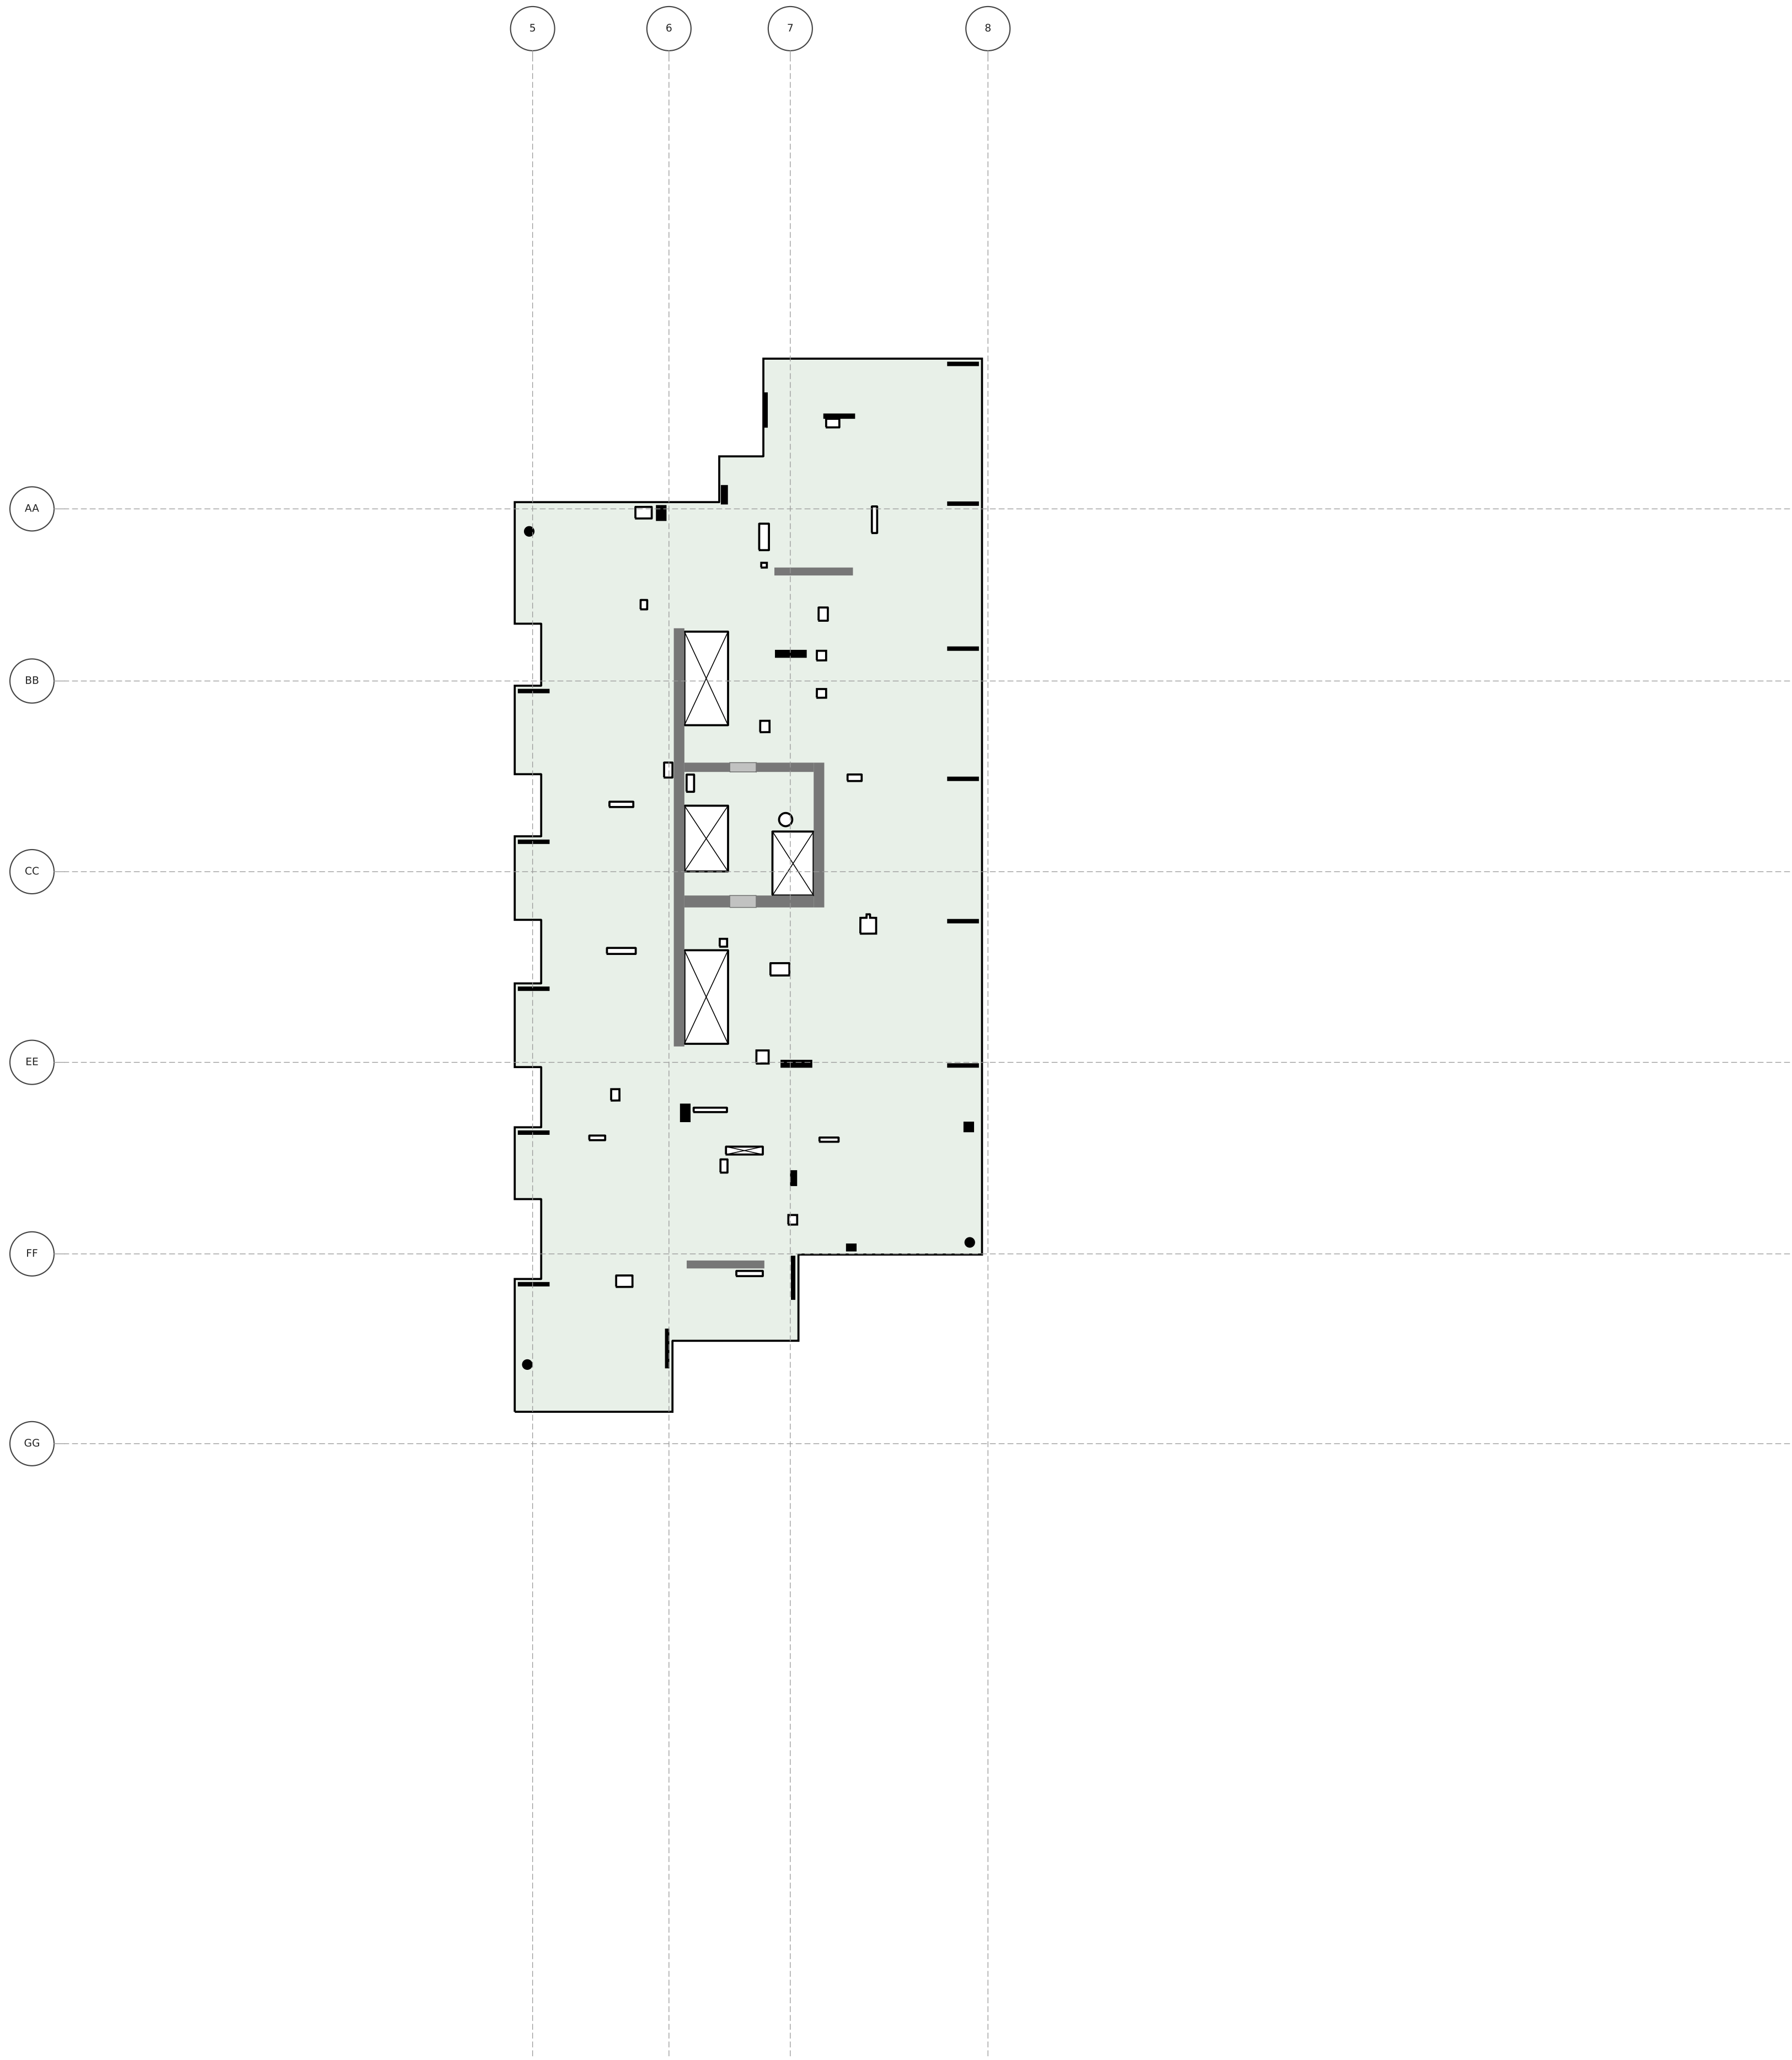


1268 KALAE

LEVEL 16 FLOOR PLAN

T.O.S. 165'-6" · typical slab 7 1/2" · scale 1" = 20'

Generated from HI_KALAE_MCC_ST.ifc (Revit scope model) for the McClone Reshore Calculator — geometry only; loading marks are drawn in the calculator.

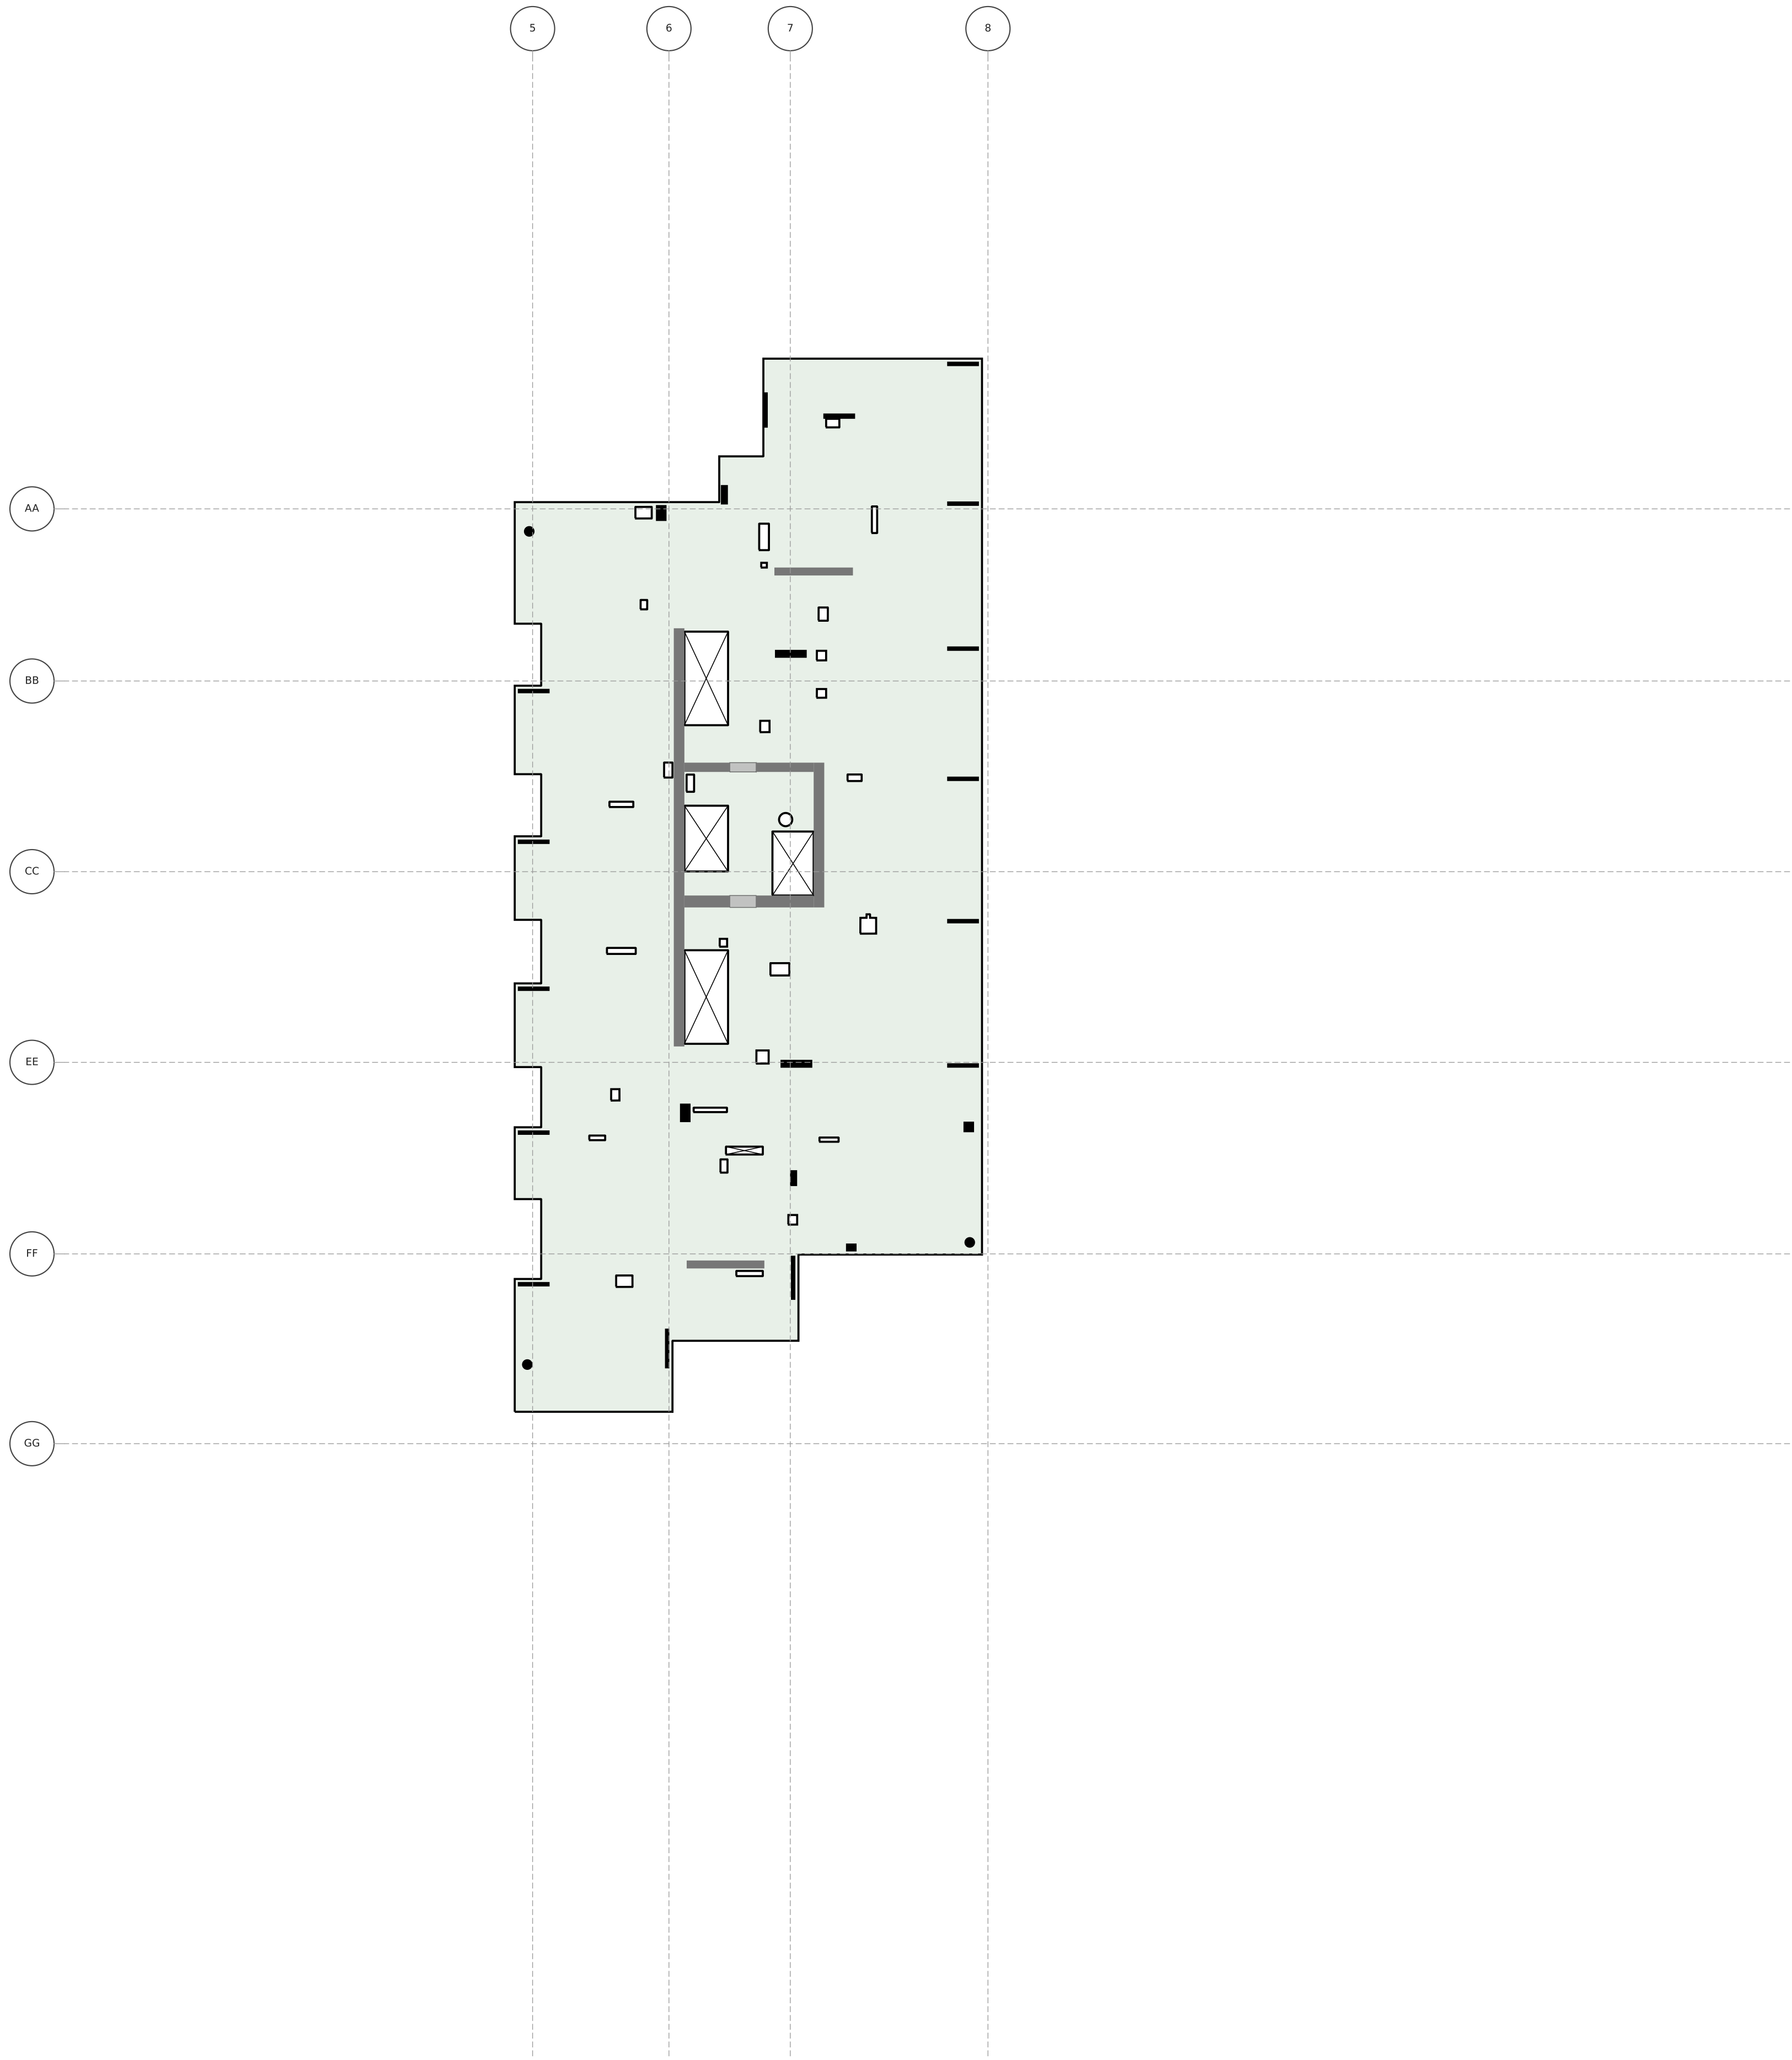


1268 KALAE

LEVEL 17 FLOOR PLAN

T.O.S. 175'-2 1/2" · typical slab 7 1/2" · scale 1" = 20'

Generated from HJ_KALAE_MCC_ST.ifc (Revit scope model) for the McClone Reshore Calculator — geometry only; loading marks are drawn in the calculator.

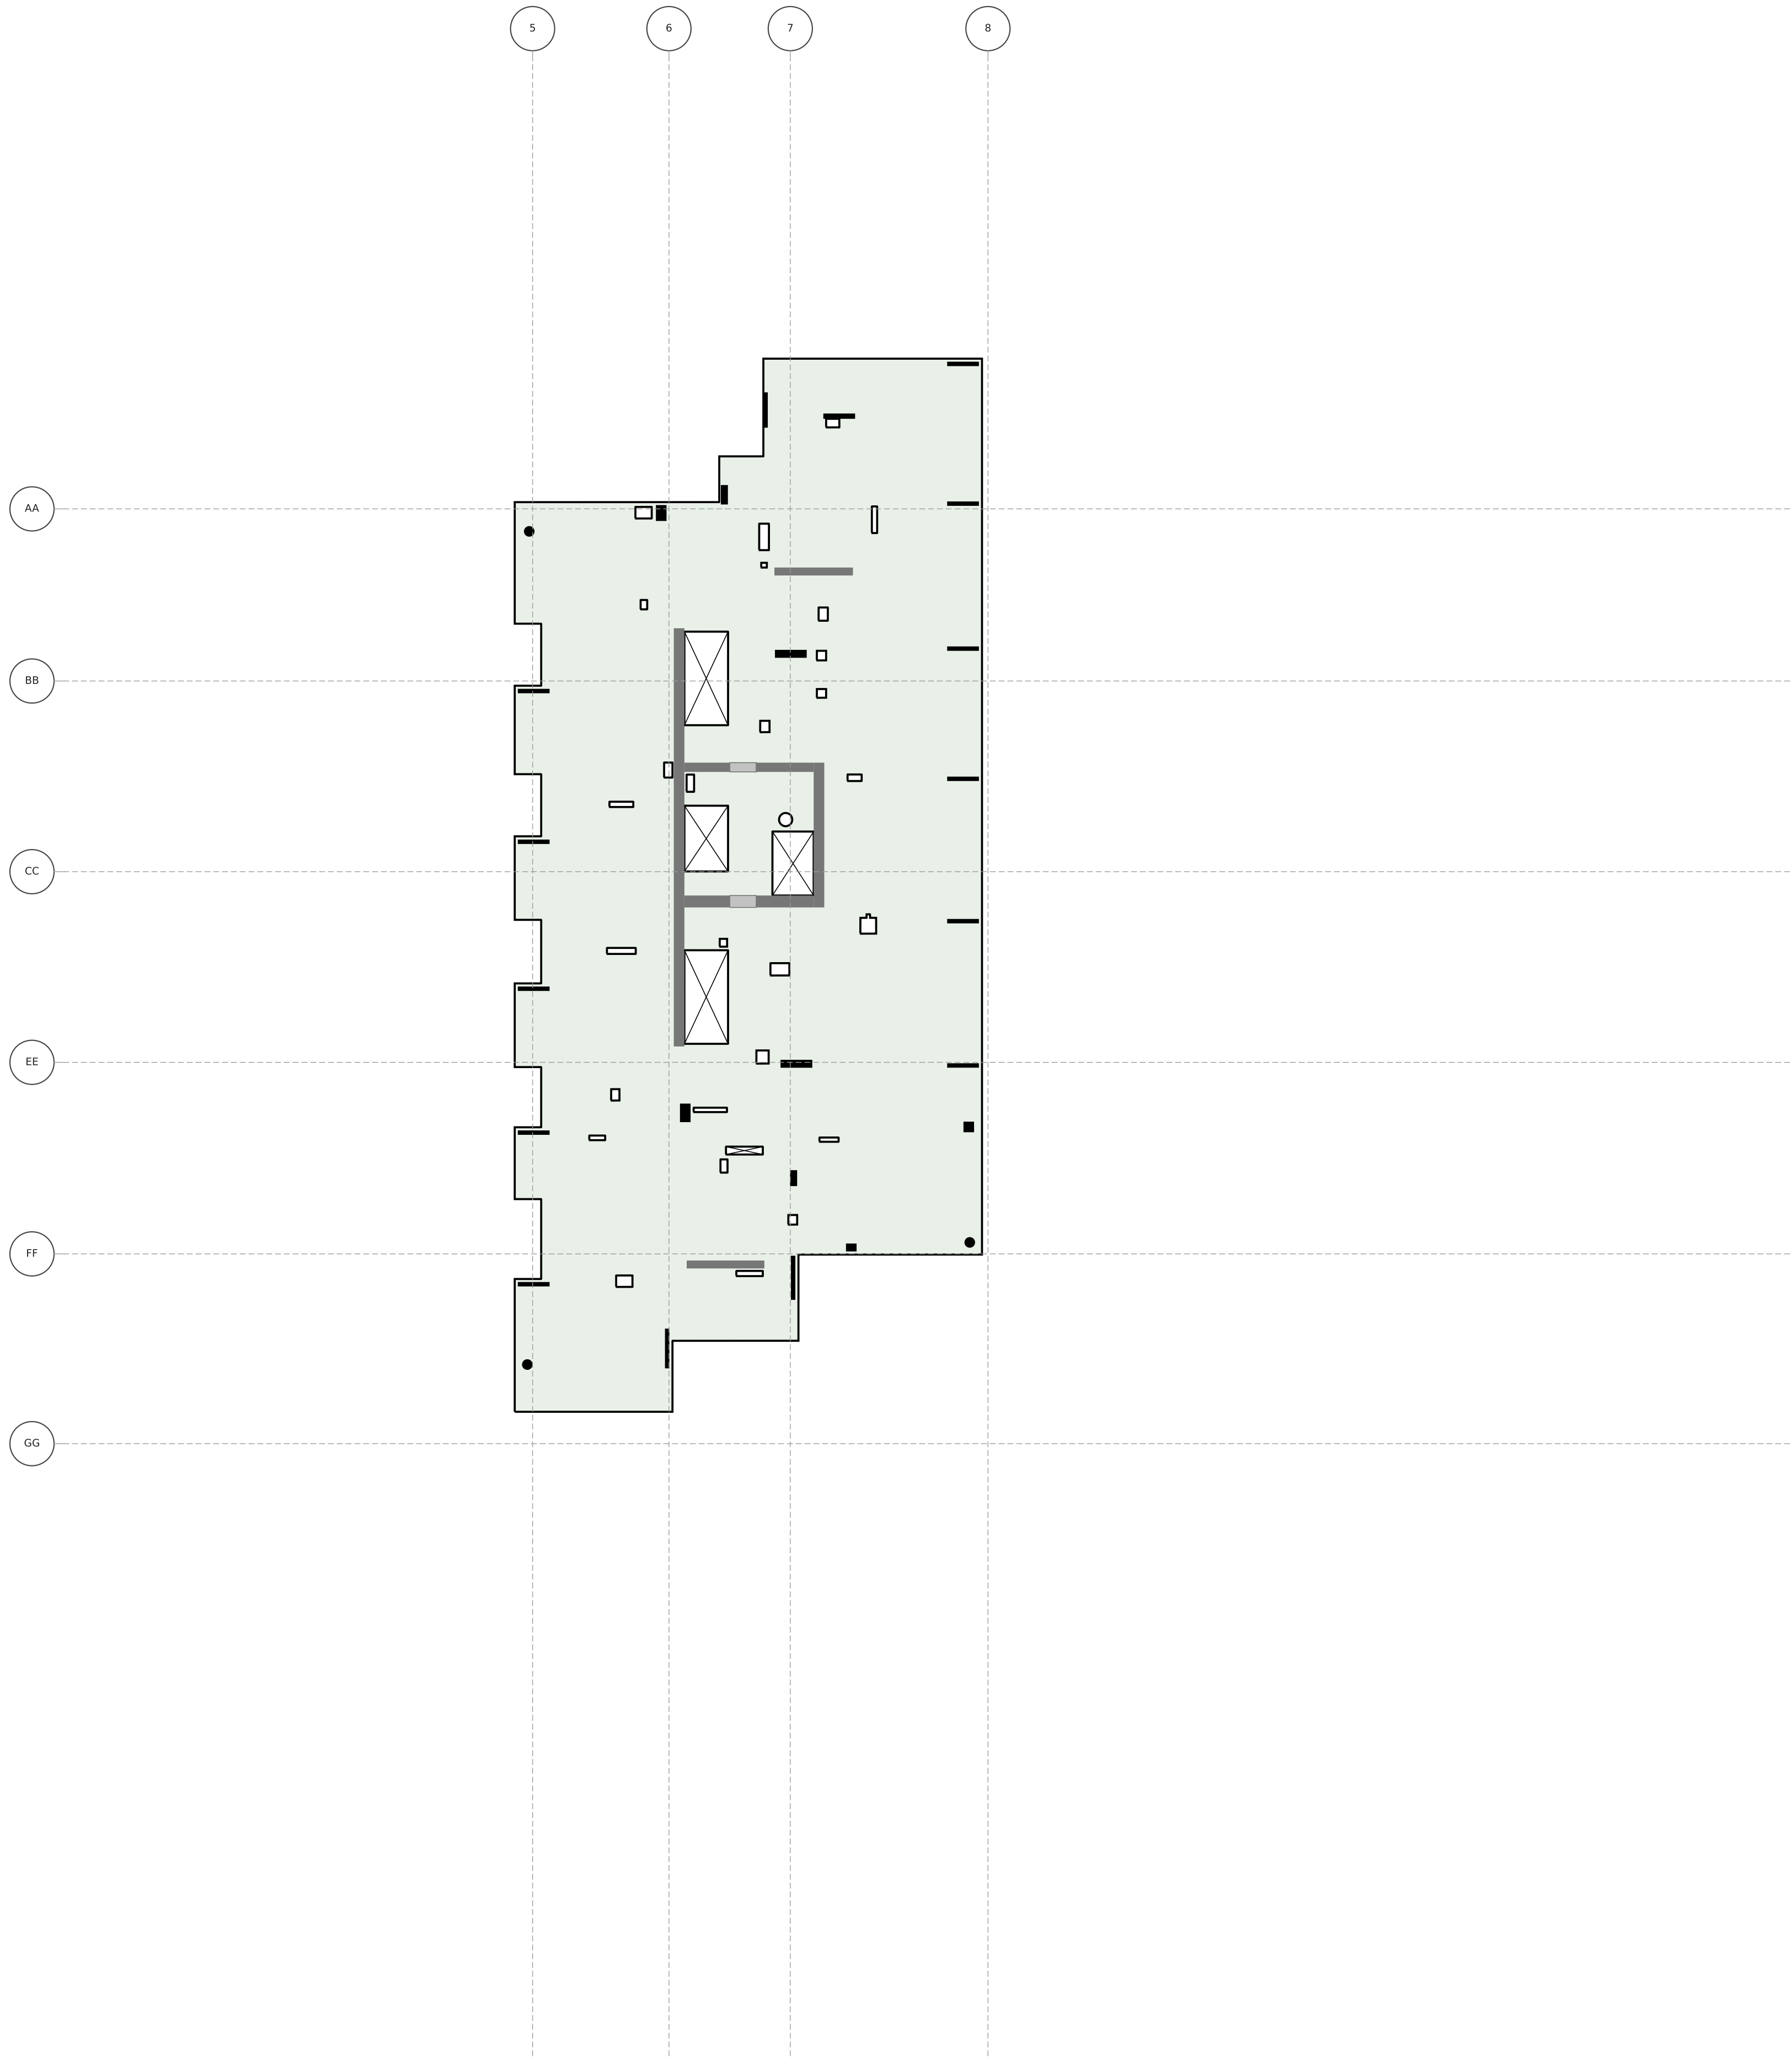


1268 KALAE

LEVEL 18 FLOOR PLAN


T.O.S. 184'-11" · typical slab 7 1/2" · scale 1" = 20'

Generated from HI_KALAE_MCC_ST.ifc (Revit scope model) for the McClone Reshore Calculator — geometry only; loading marks are drawn in the calculator.

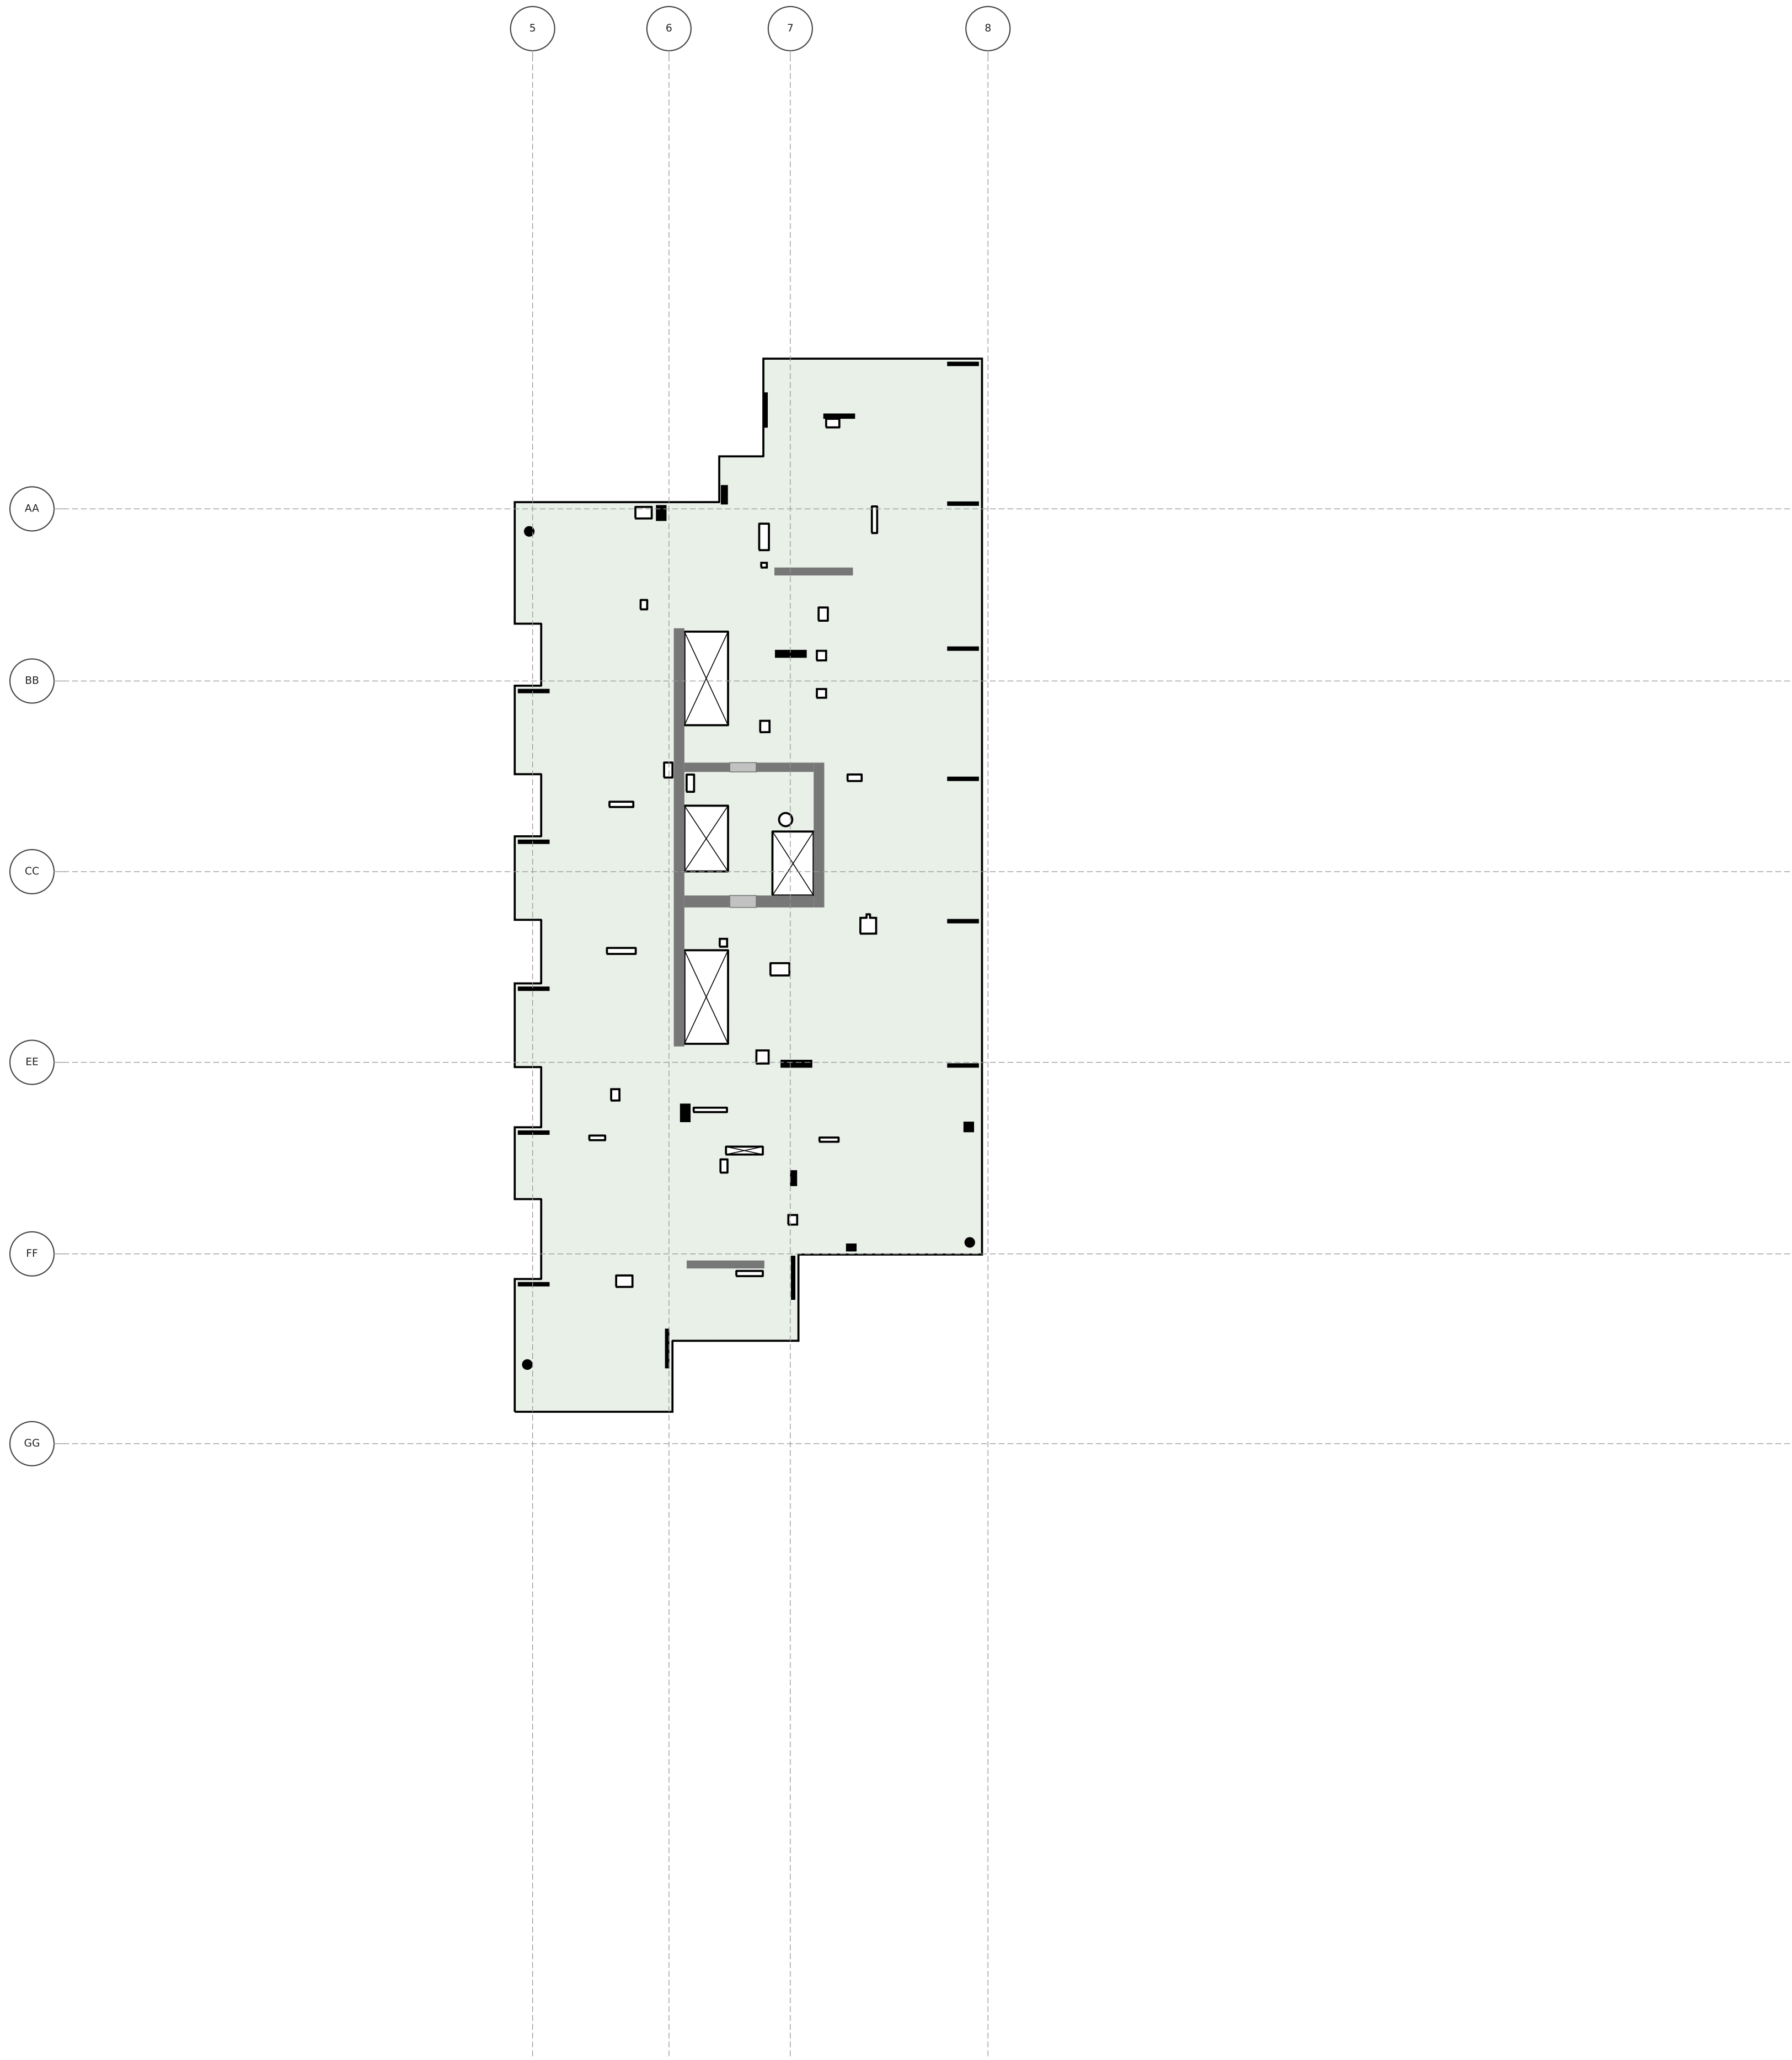

1268 KALAE
LEVEL 19 FLOOR PLAN

T.O.S. 194'-7 1/2" · typical slab 7 1/2" · scale 1" = 20'
Generated from HI_KALAE_MCC_ST.ifc (Revit scope model) for the McClone Reshore Calculator — geometry only; loading marks are drawn in the calculator.

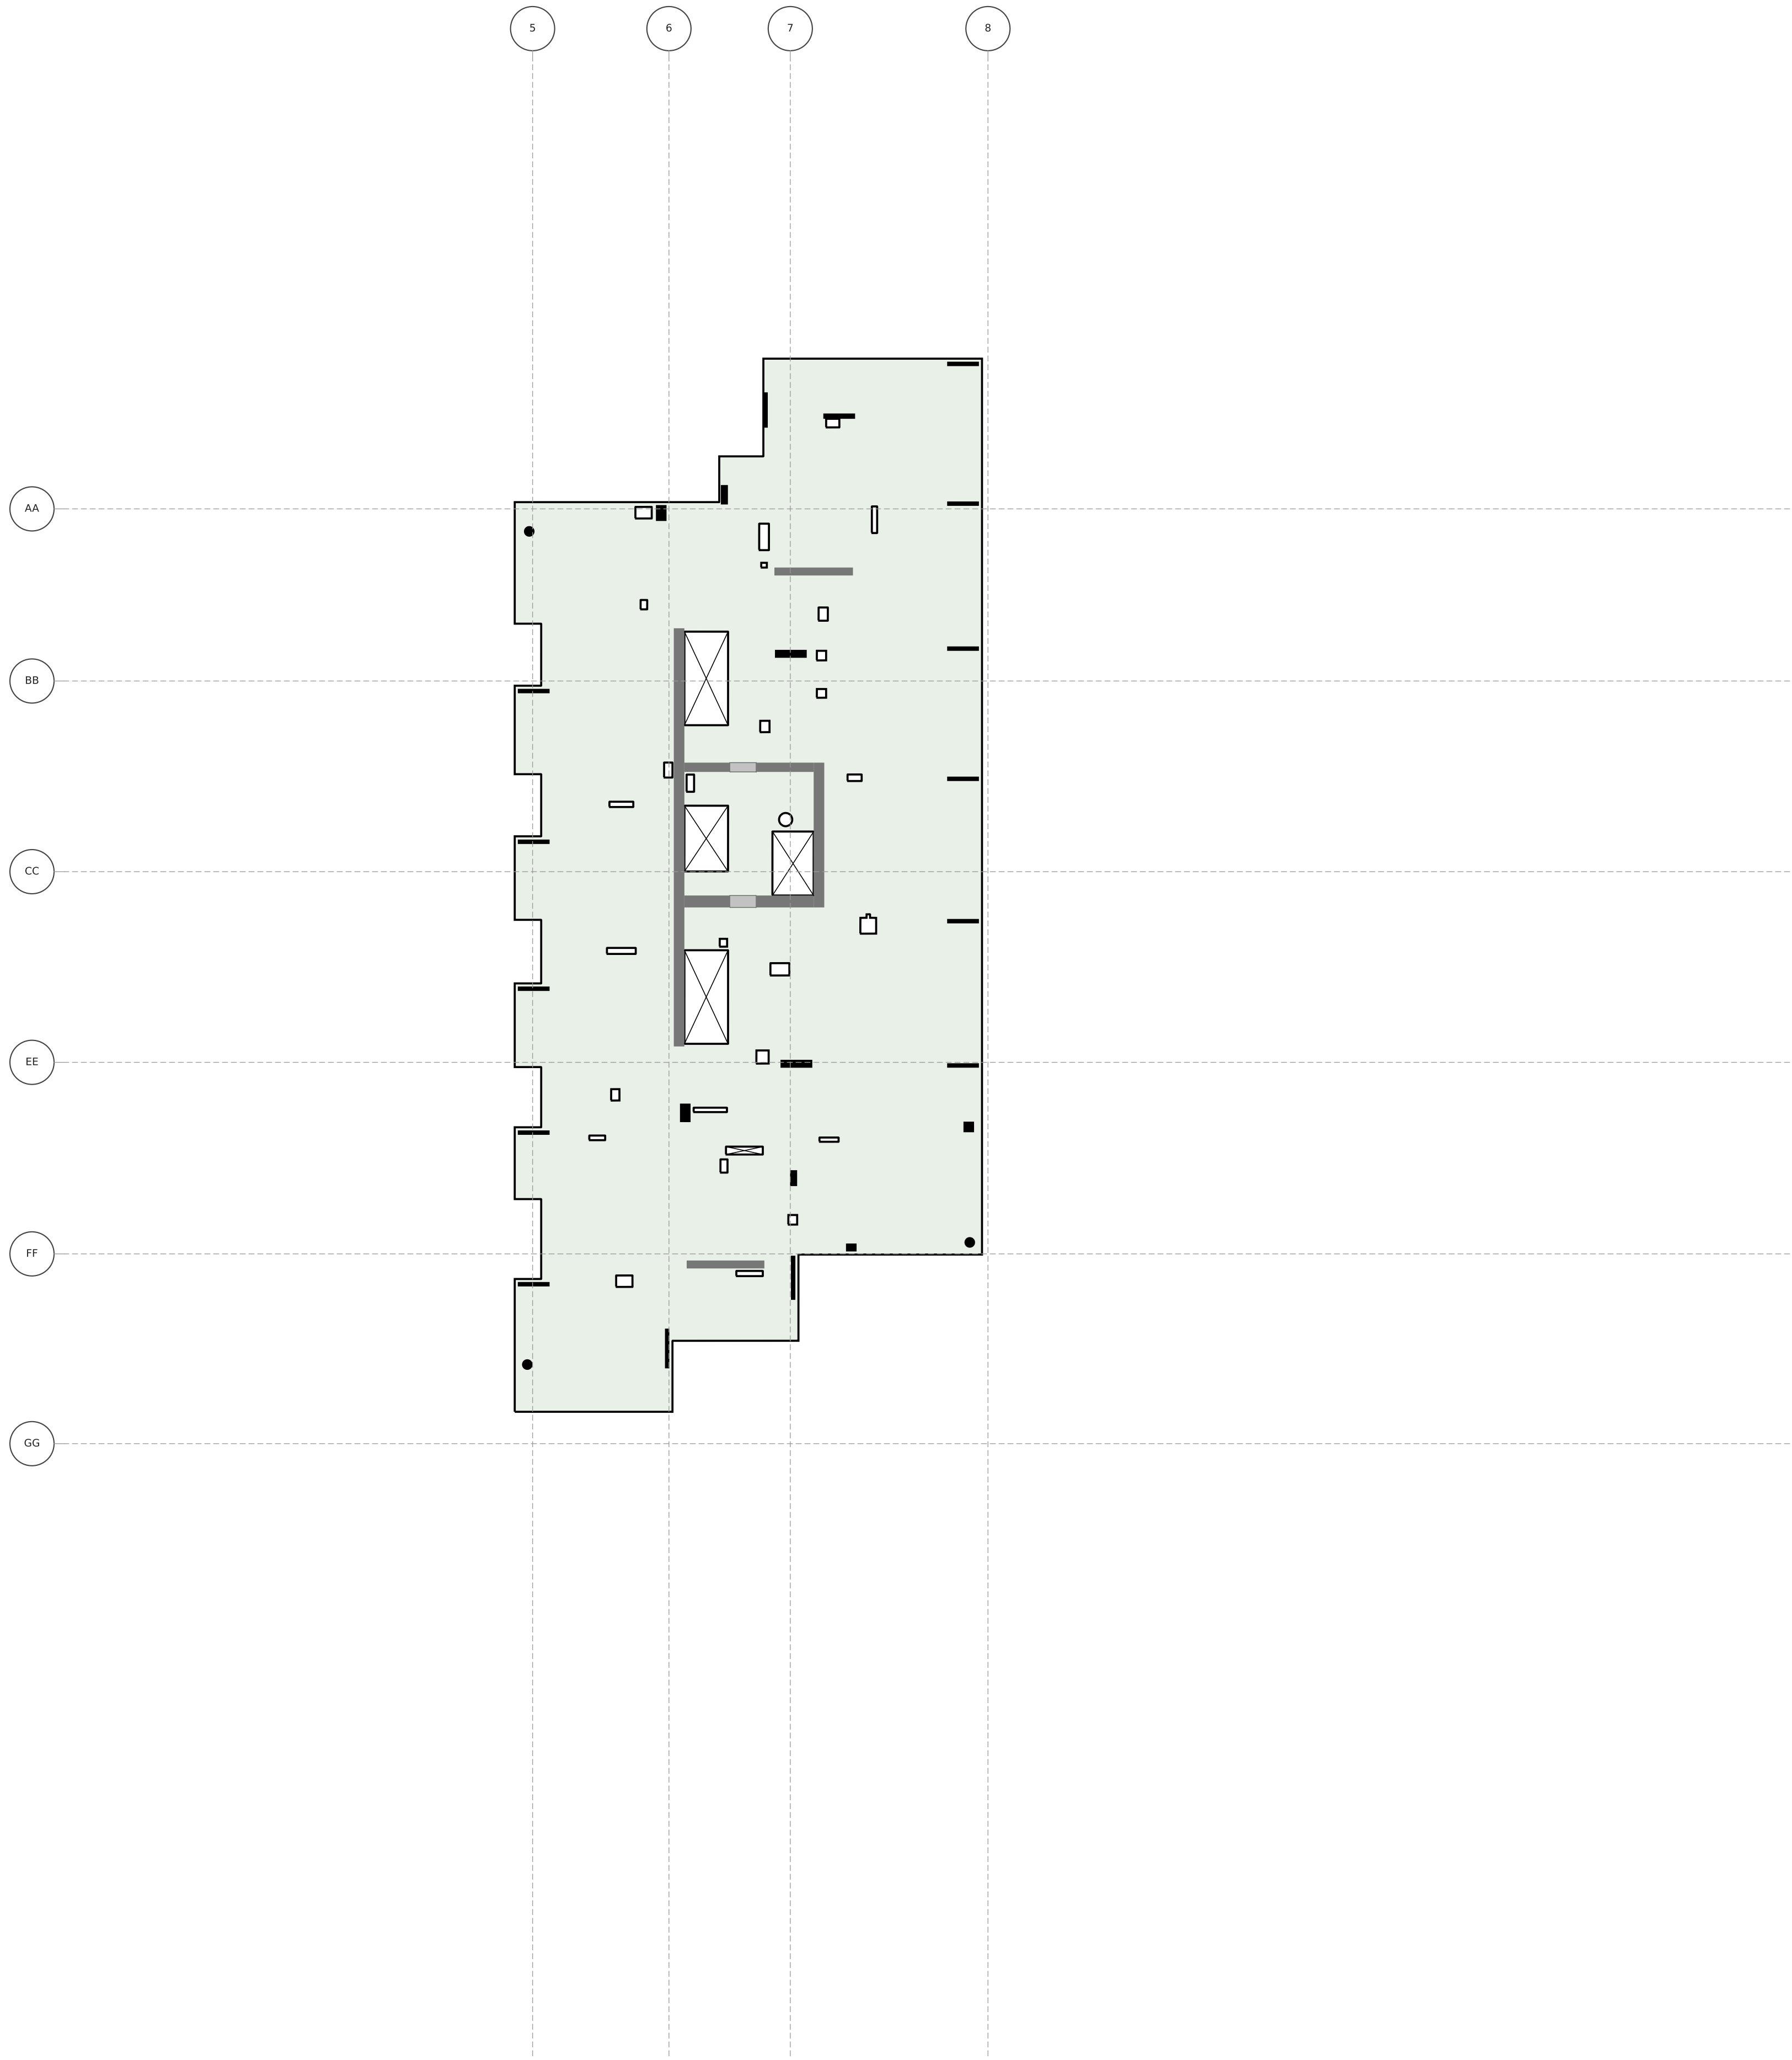


1268 KALAE

LEVEL 20 FLOOR PLAN


T.O.S. 204'-4" · typical slab 7 1/2" · scale 1" = 20'

Generated from HJ_KALAE_MCC_ST.ifc (Revit scope model) for the McClone Reshore Calculator — geometry only; loading marks are drawn in the calculator.

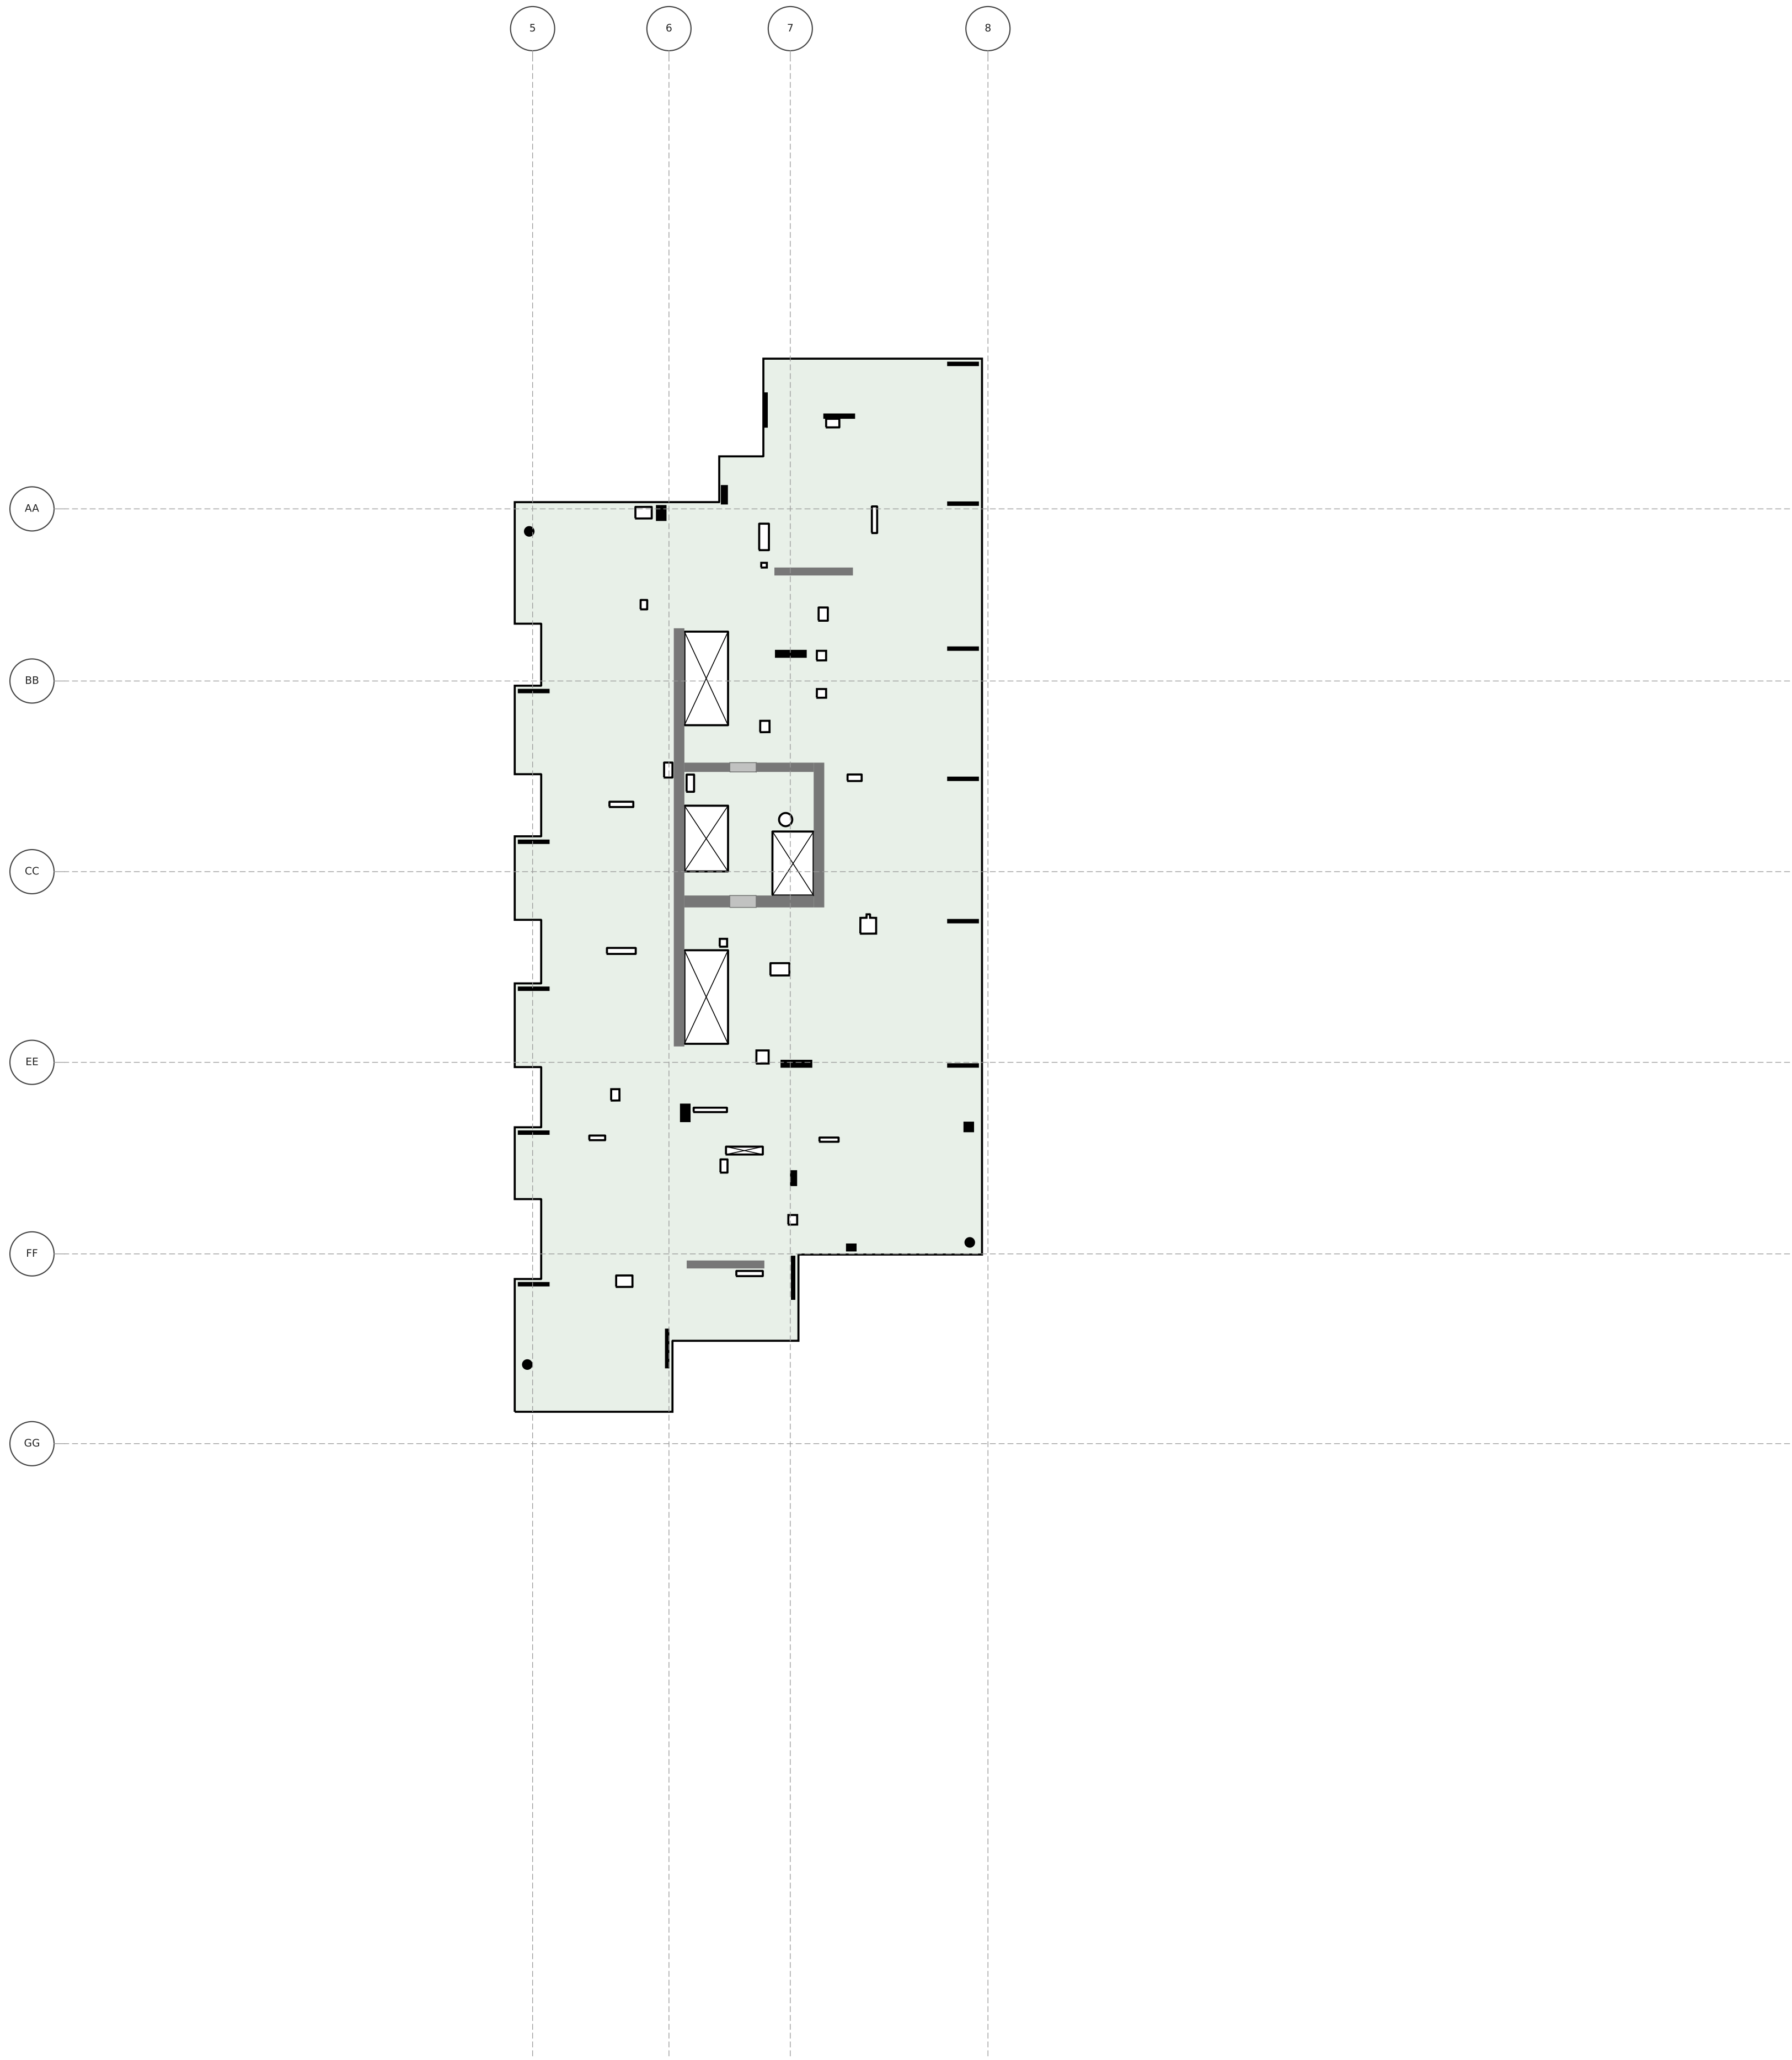

1268 KALAE
LEVEL 21 FLOOR PLAN

T.O.S. 214'-0 1/2" · typical slab 7 1/2" · scale 1" = 20'
Generated from HI_KALAE_MCC_ST.ifc (Revit scope model) for the McClone Reshore Calculator — geometry only; loading marks are drawn in the calculator.

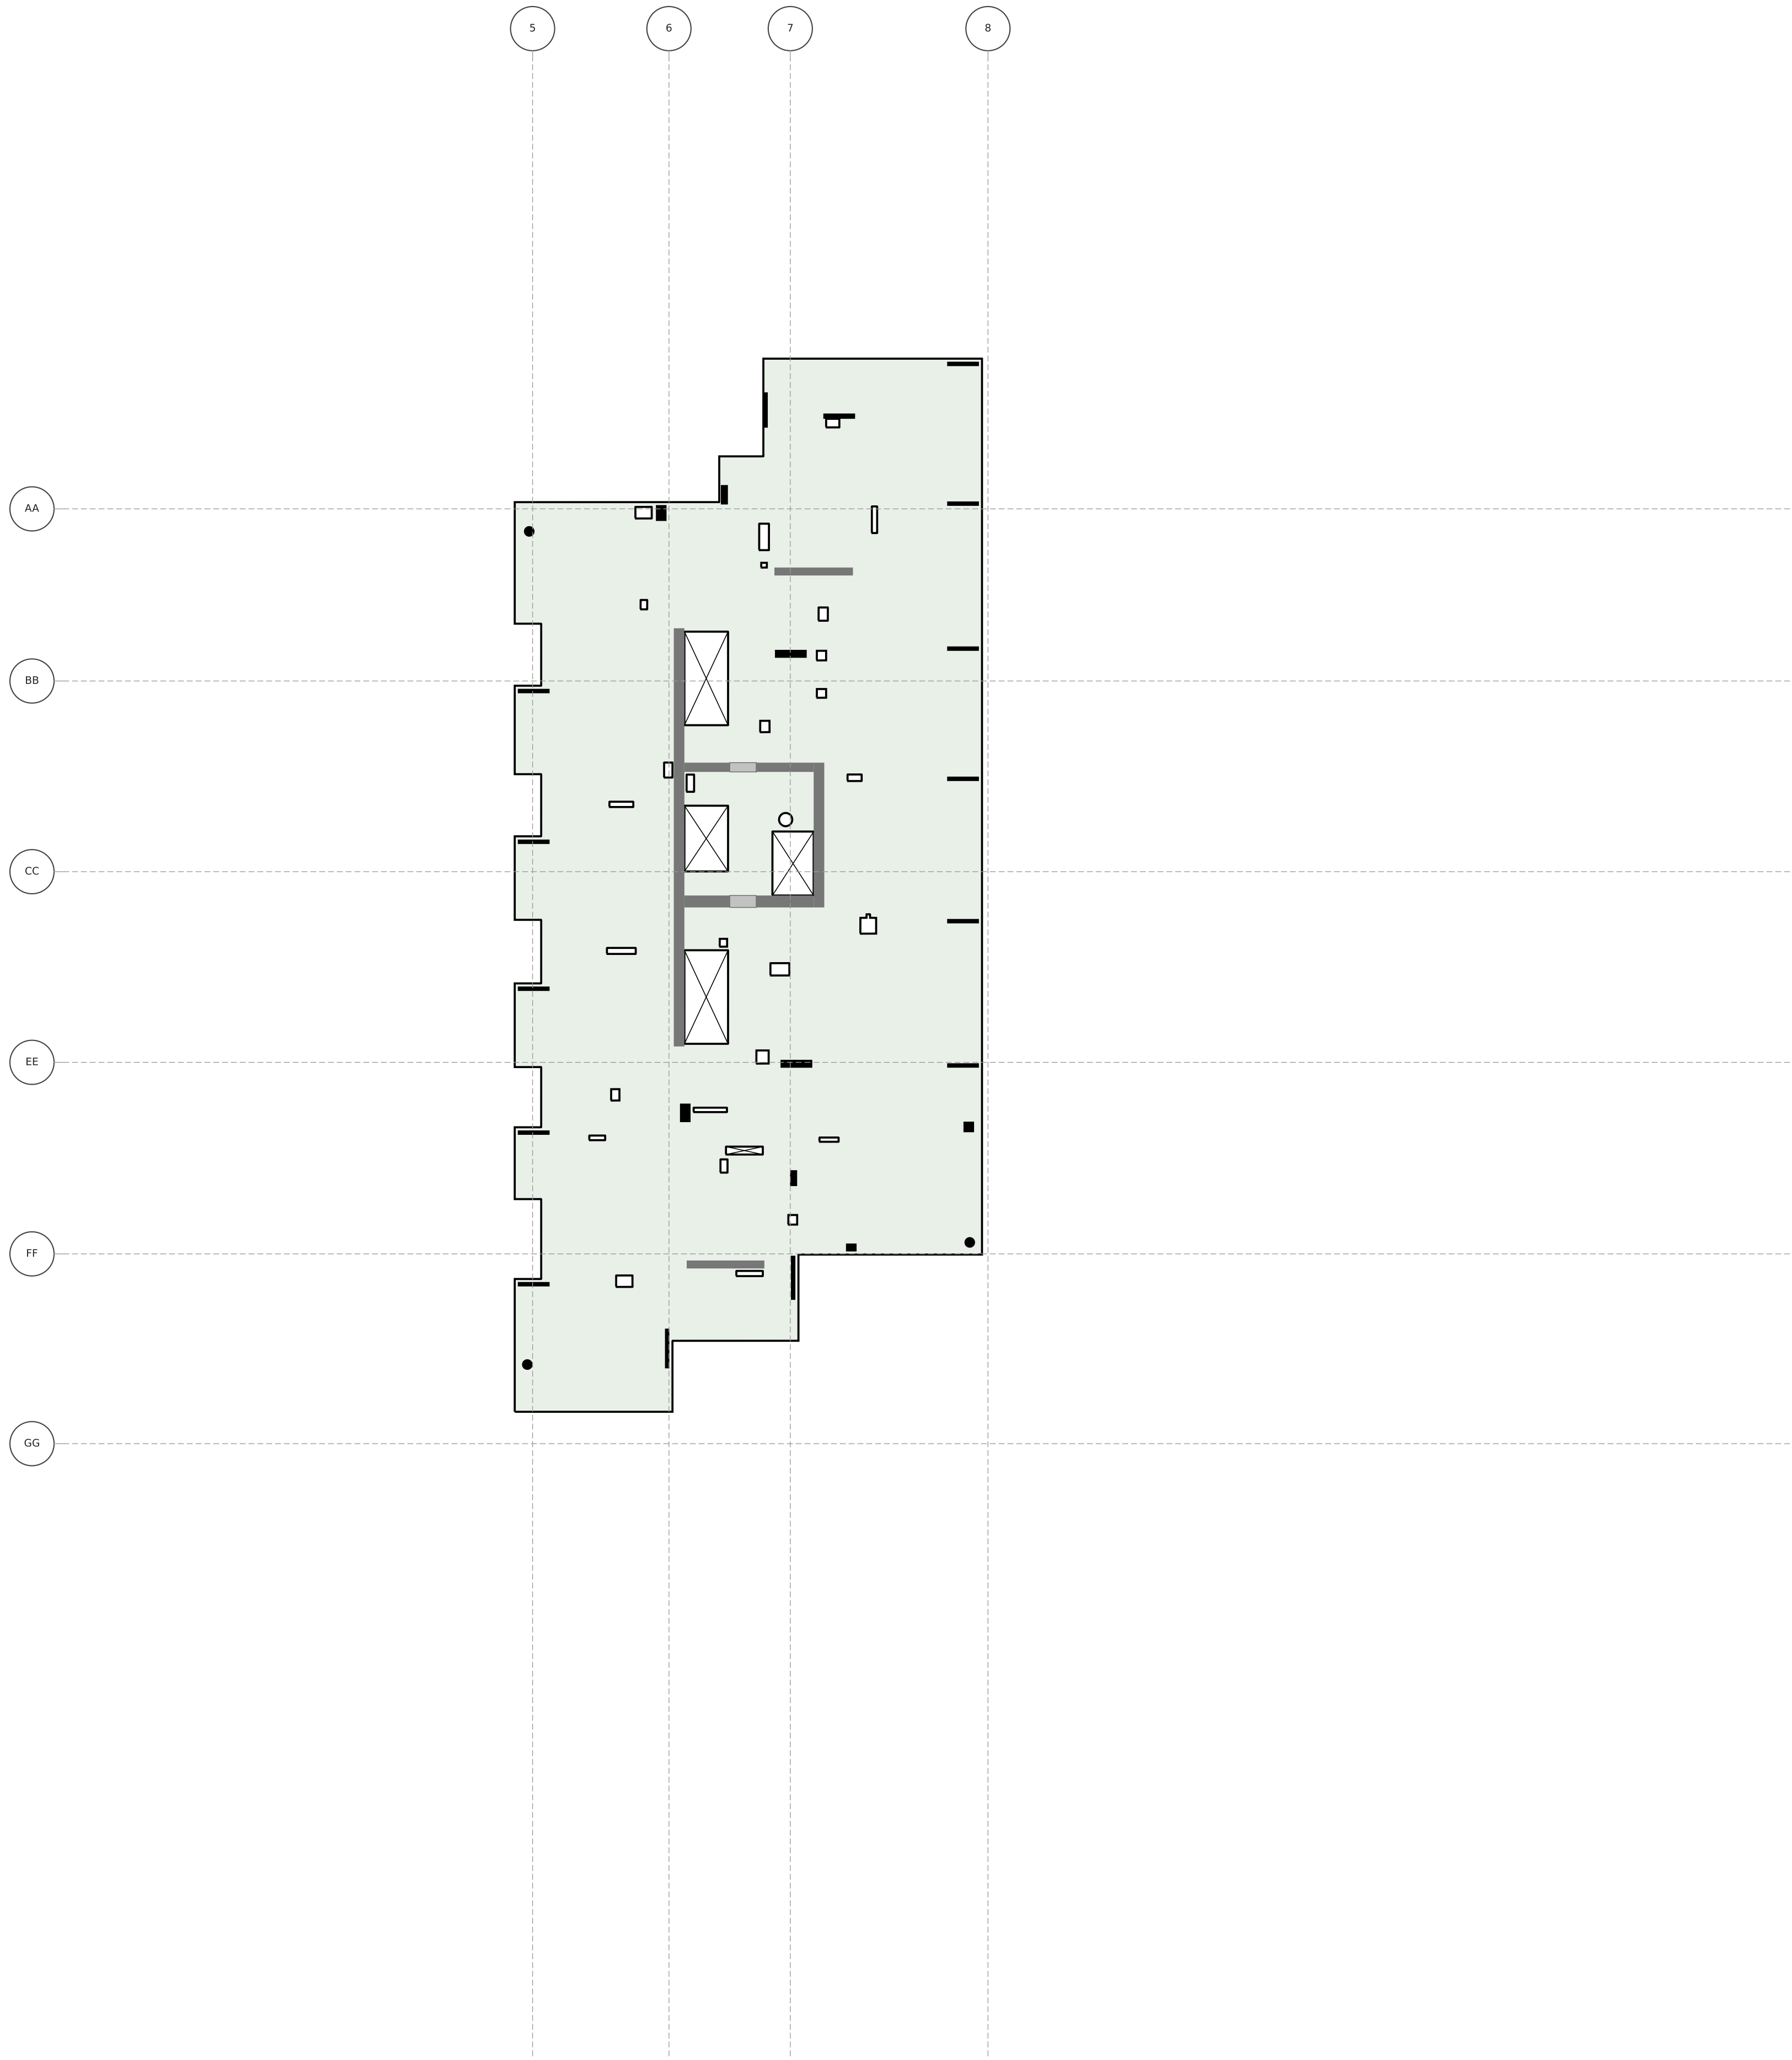


1268 KALAE

LEVEL 22 FLOOR PLAN


T.O.S. 223'-9" · typical slab 7 1/2" · scale 1" = 20'

Generated from HI_KALAE_MCC_ST.ifc (Revit scope model) for the McClone Reshore Calculator — geometry only; loading marks are drawn in the calculator.

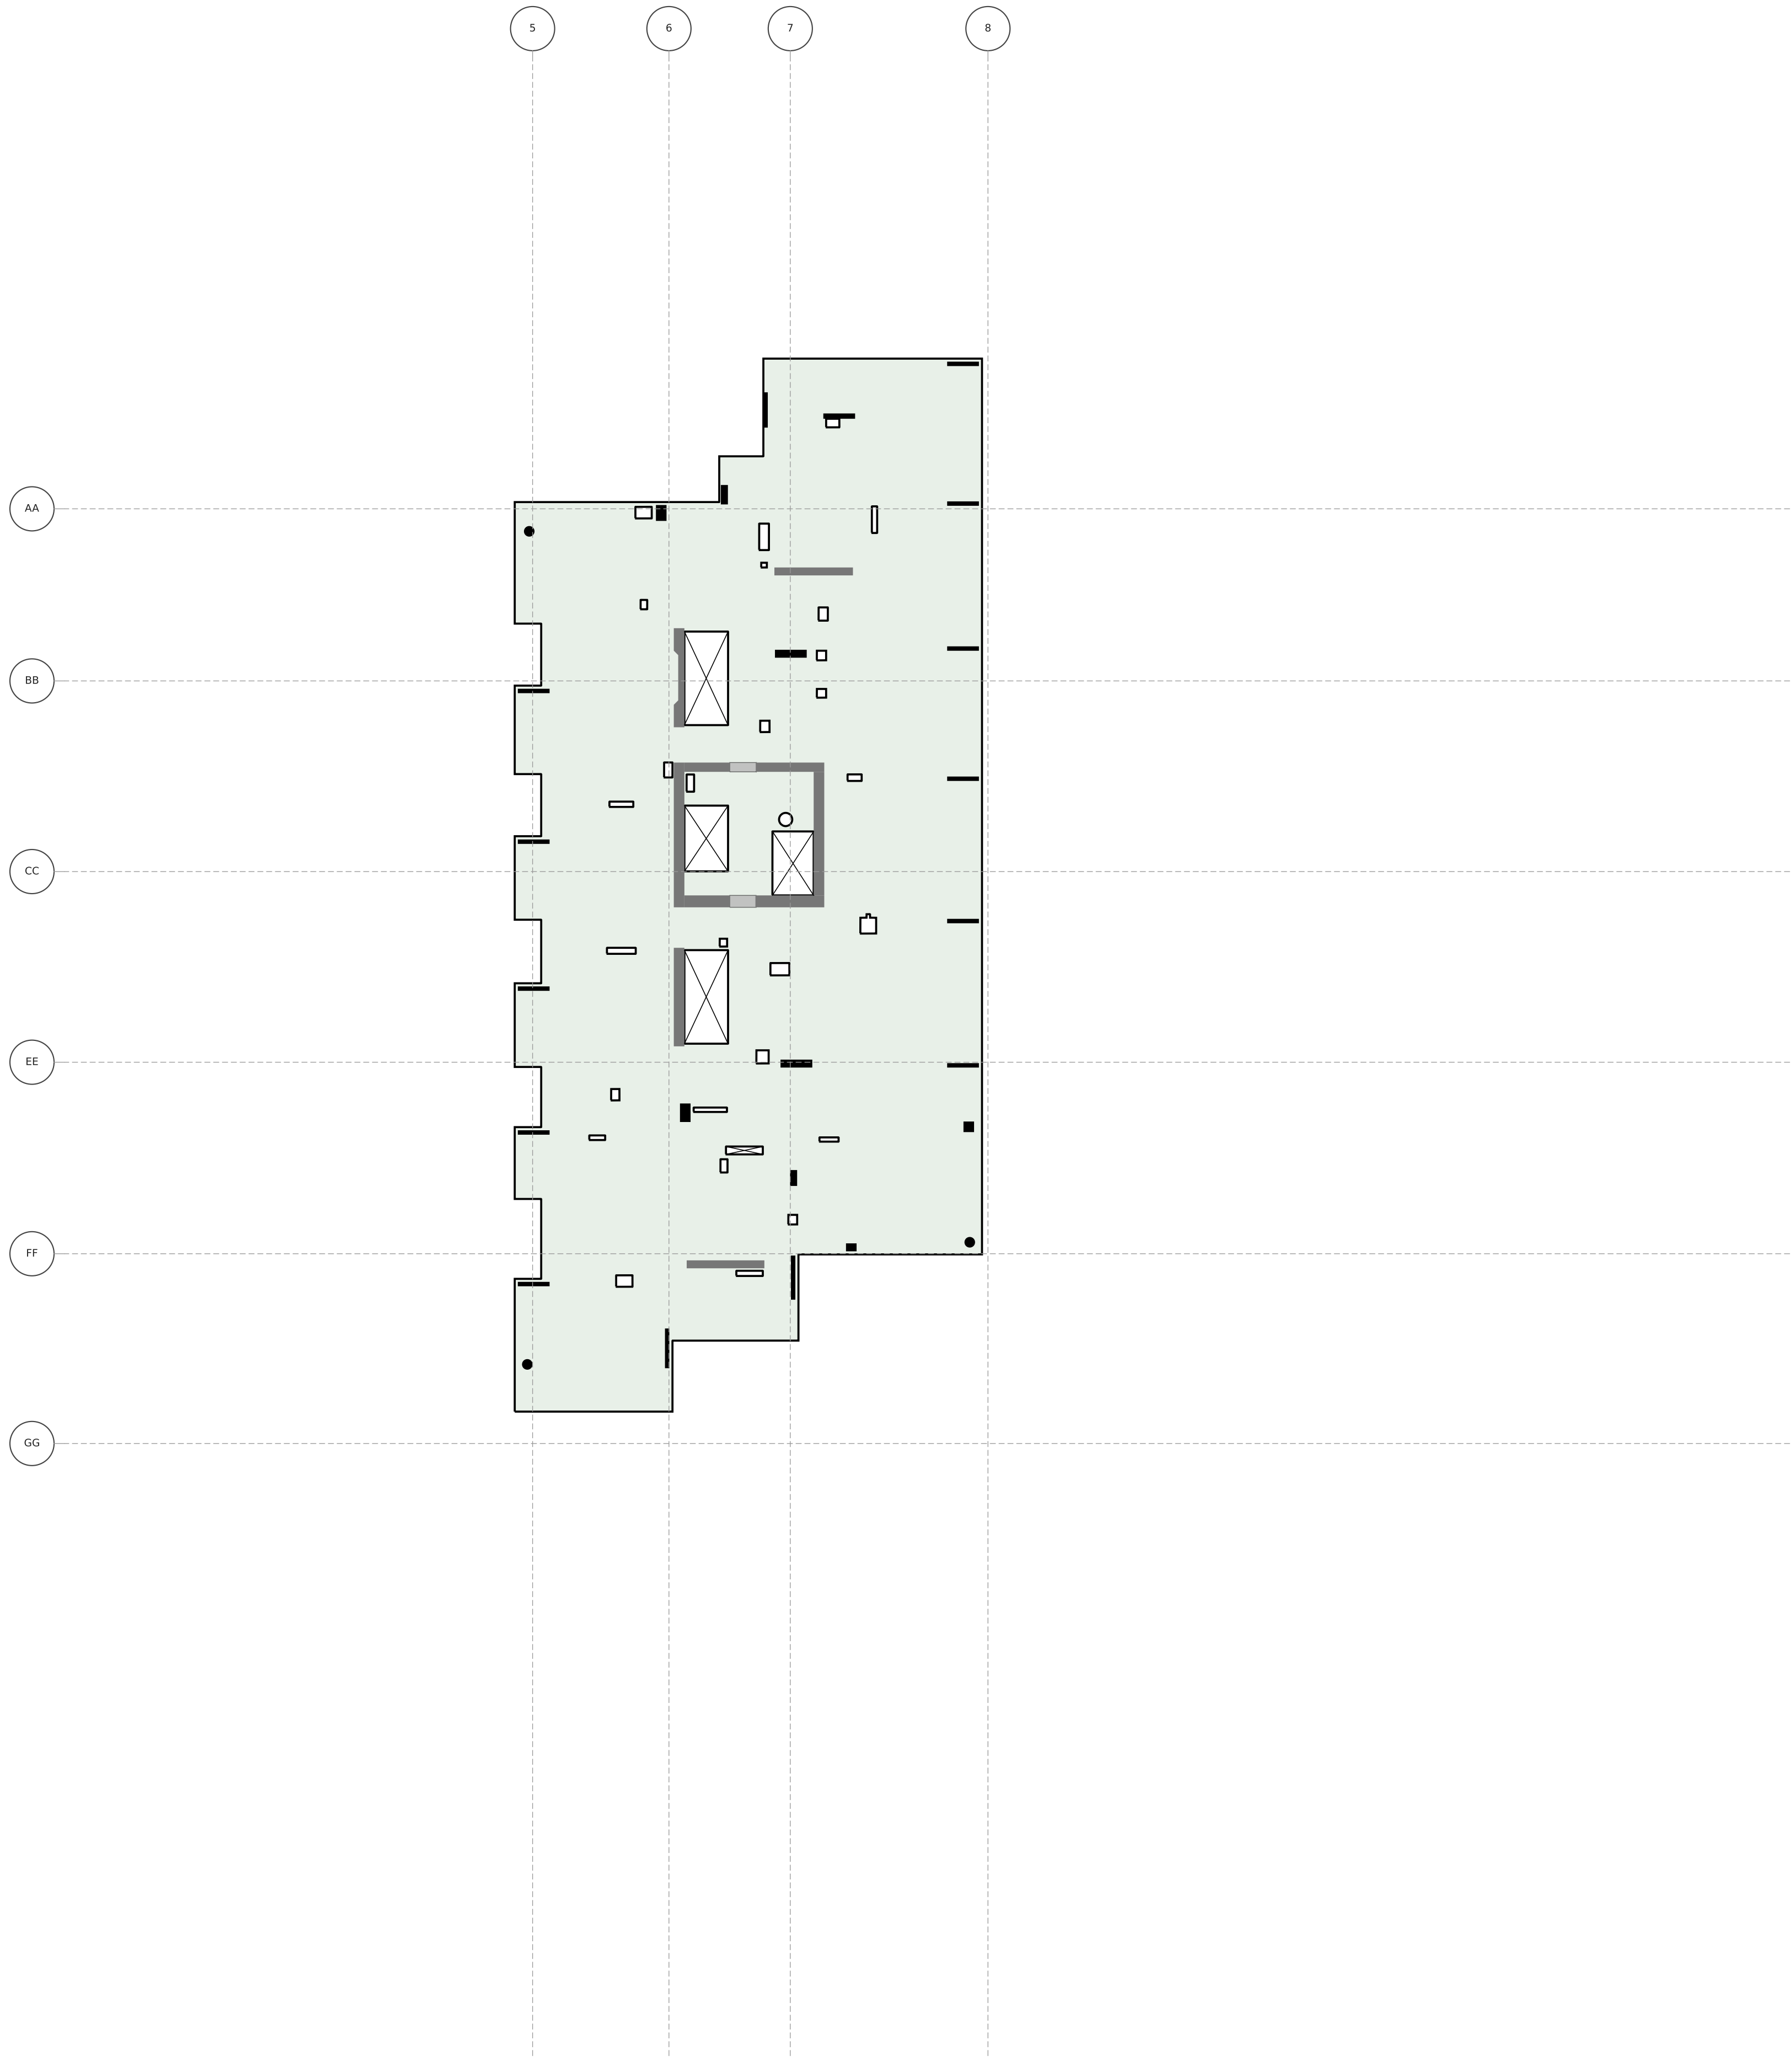

1268 KALAE
LEVEL 23 FLOOR PLAN

T.O.S. 233'-5 1/2" · typical slab 7 1/2" · scale 1" = 20'
Generated from HI_KALAE_MCC_ST.ifc (Revit scope model) for the McClone Reshore Calculator — geometry only; loading marks are drawn in the calculator.

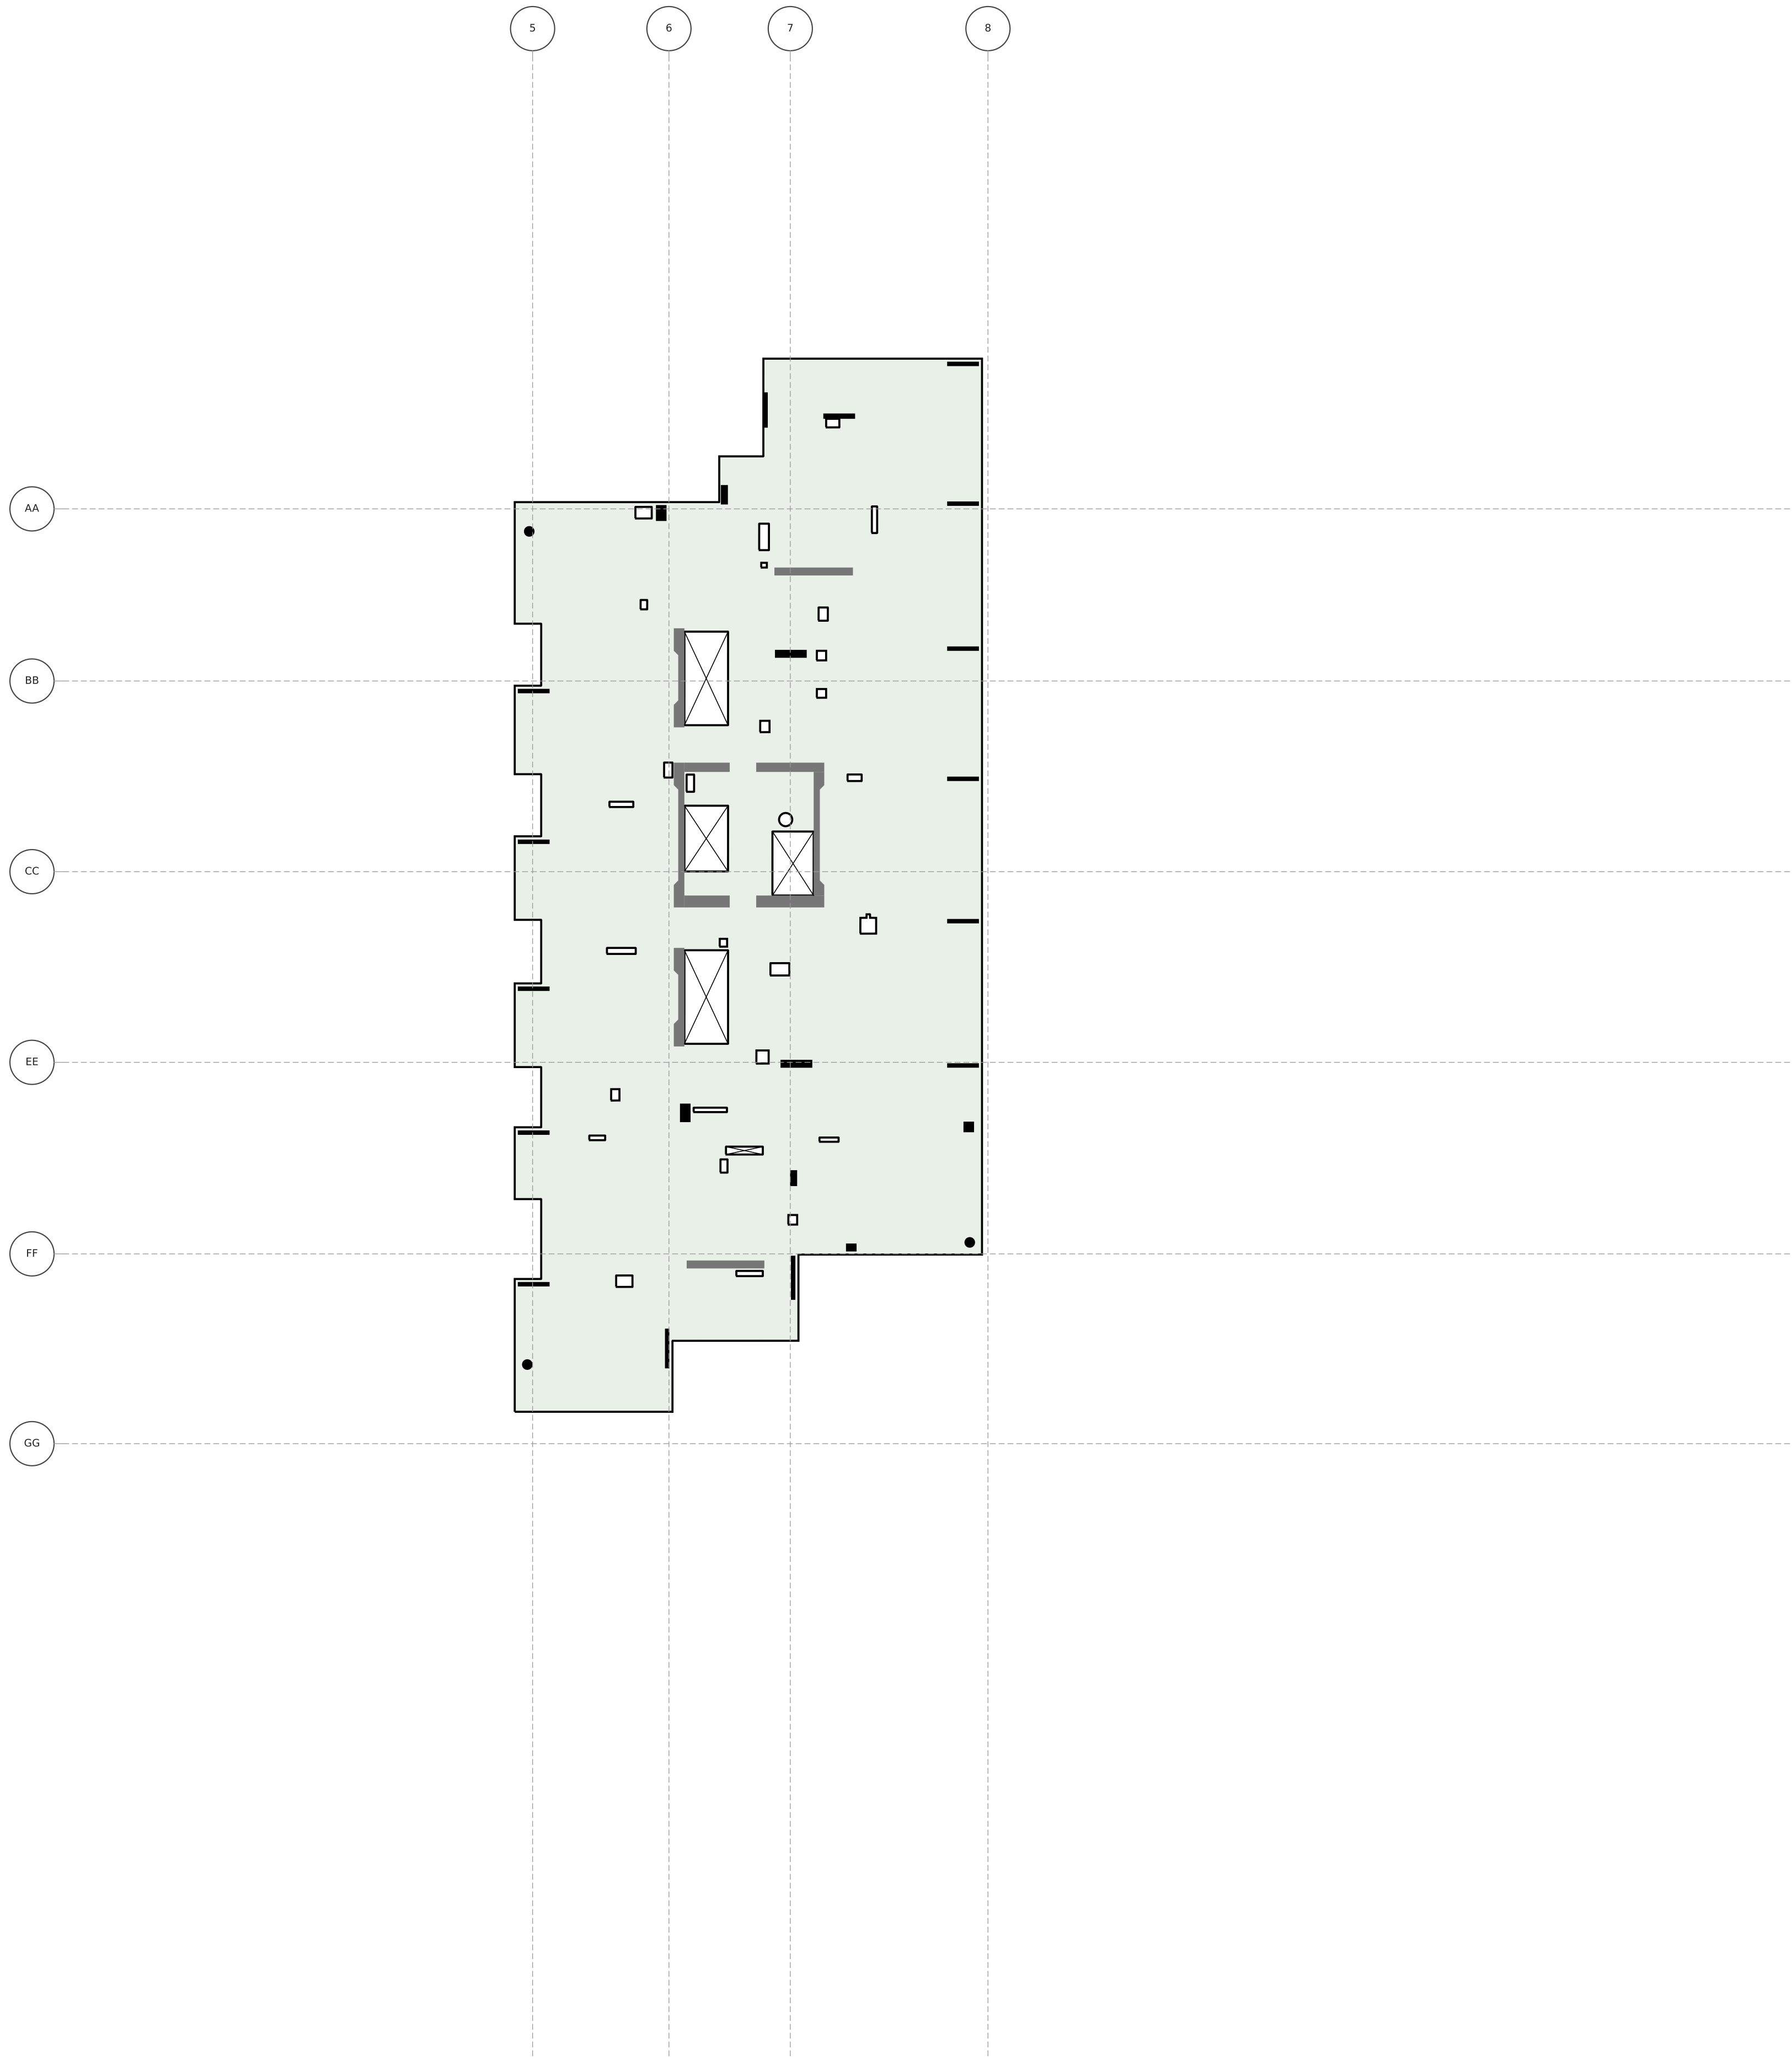


1268 KALAE

LEVEL 24 FLOOR PLAN

T.O.S. 243'-4" · typical slab 7 1/2" · scale 1" = 20'

Generated from HI_KALAE_MCC_ST.ifc (Revit scope model) for the McClone Reshore Calculator — geometry only; loading marks are drawn in the calculator.

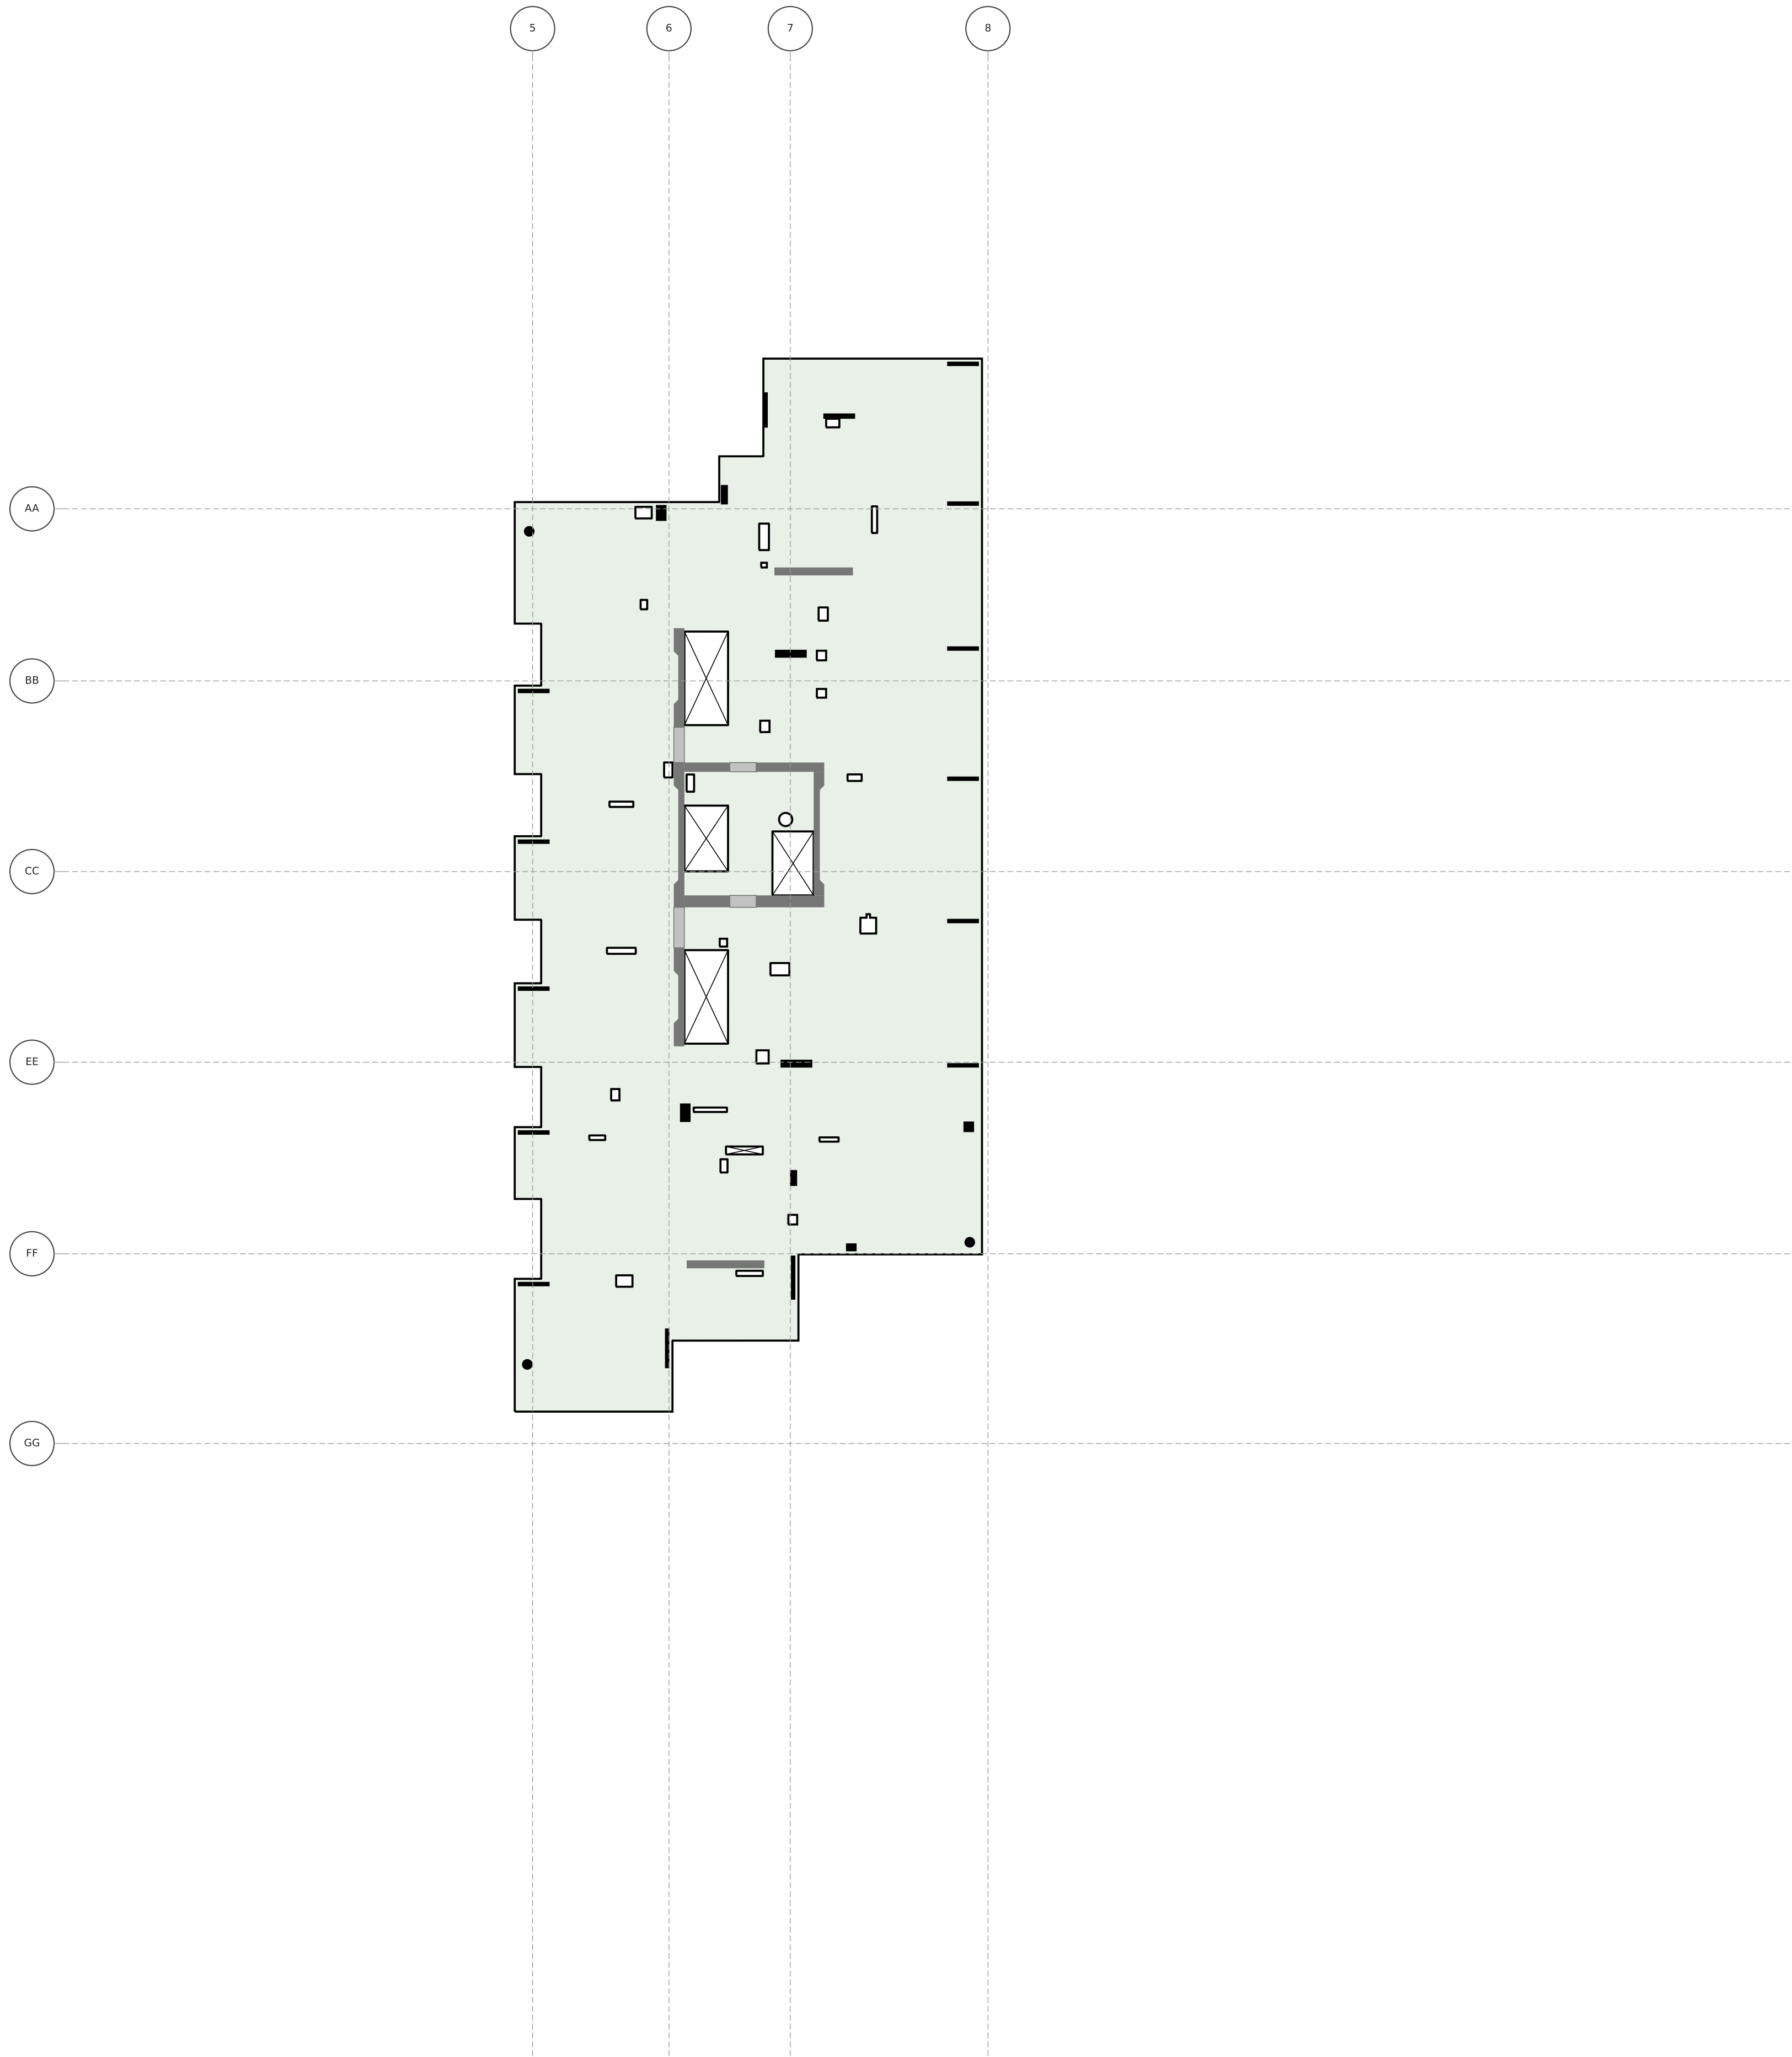


1268 KALAE

LEVEL 25 FLOOR PLAN


T.O.S. 253'-0 1/2" · typical slab 7 1/2" · scale 1" = 20'

Generated from HI_KALAE_MCC_ST.ifc (Revit scope model) for the McClone Reshore Calculator — geometry only; loading marks are drawn in the calculator.

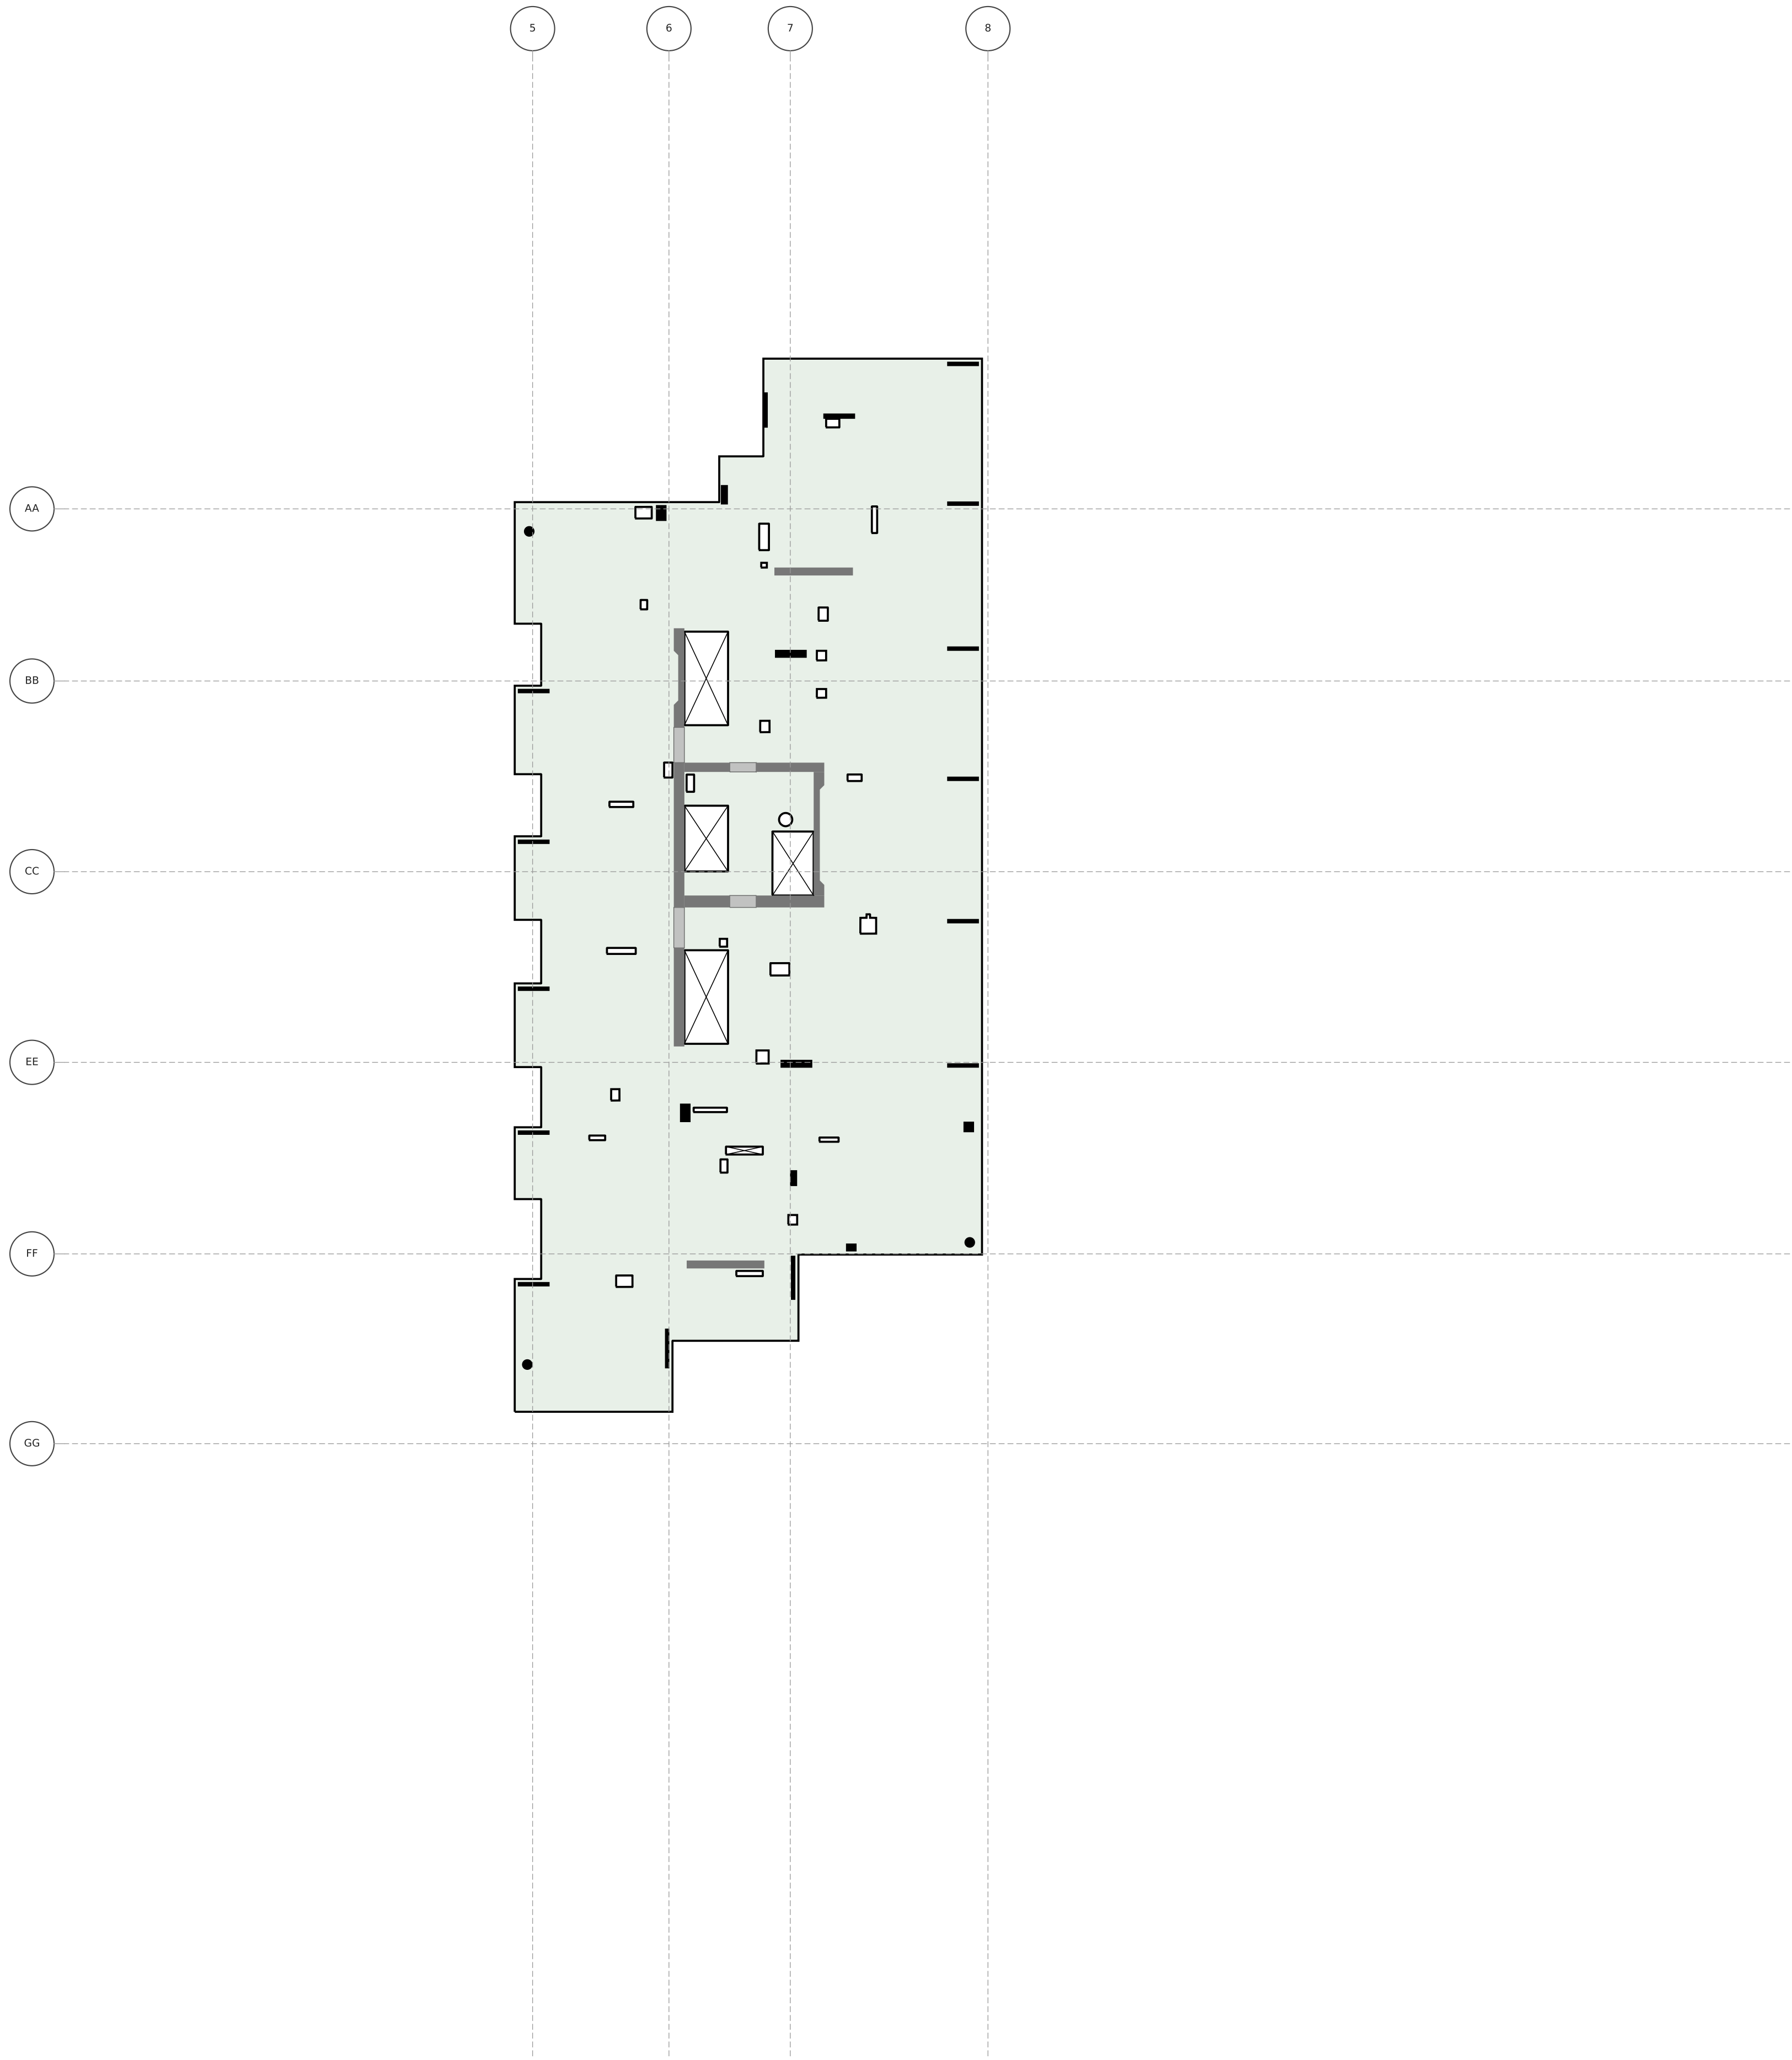

1268 KALAE
LEVEL 26 FLOOR PLAN

T.O.S. 262'-9" · typical slab 7 1/2" · scale 1" = 20'
Generated from HI_KALAE_MCC_ST.ifc (Revit scope model) for the McClone Reshore Calculator — geometry only; loading marks are drawn in the calculator.

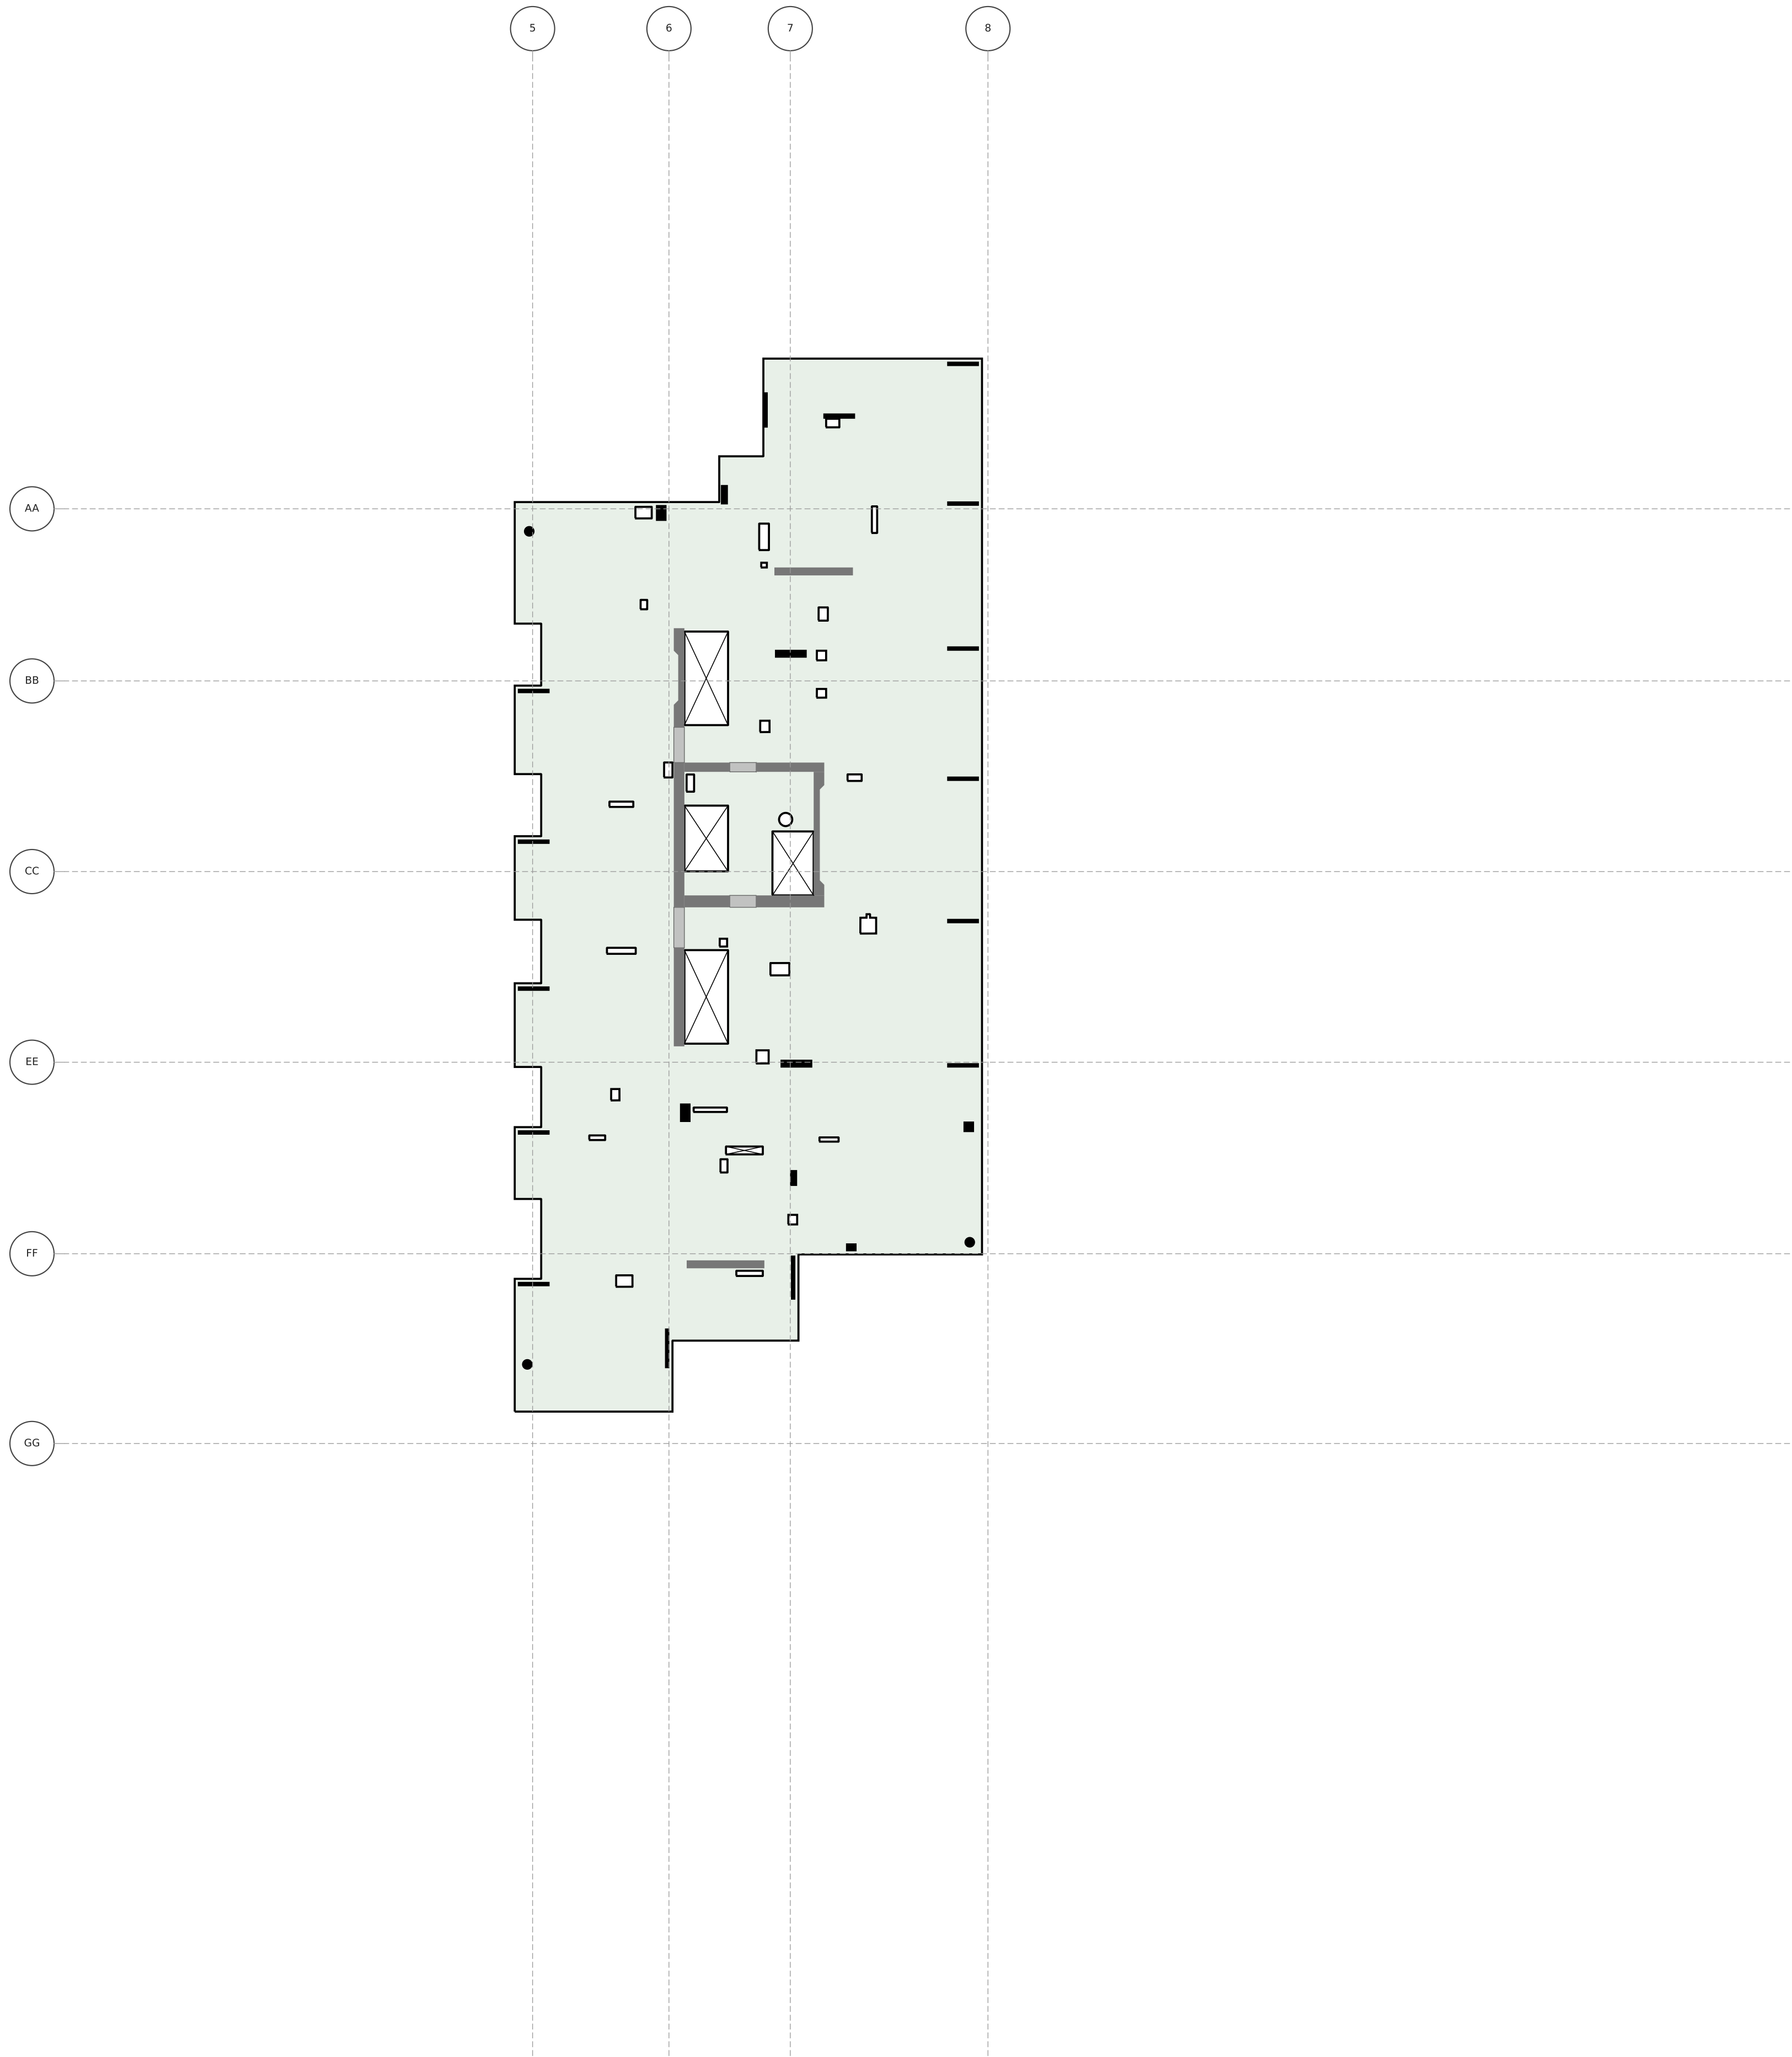


1268 KALAE

LEVEL 27 FLOOR PLAN

T.O.S. 272'-5 1/2" · typical slab 7 1/2" · scale 1" = 20'

Generated from HI_KALAE_MCC_ST.ifc (Revit scope model) for the McClone Reshore Calculator — geometry only; loading marks are drawn in the calculator.

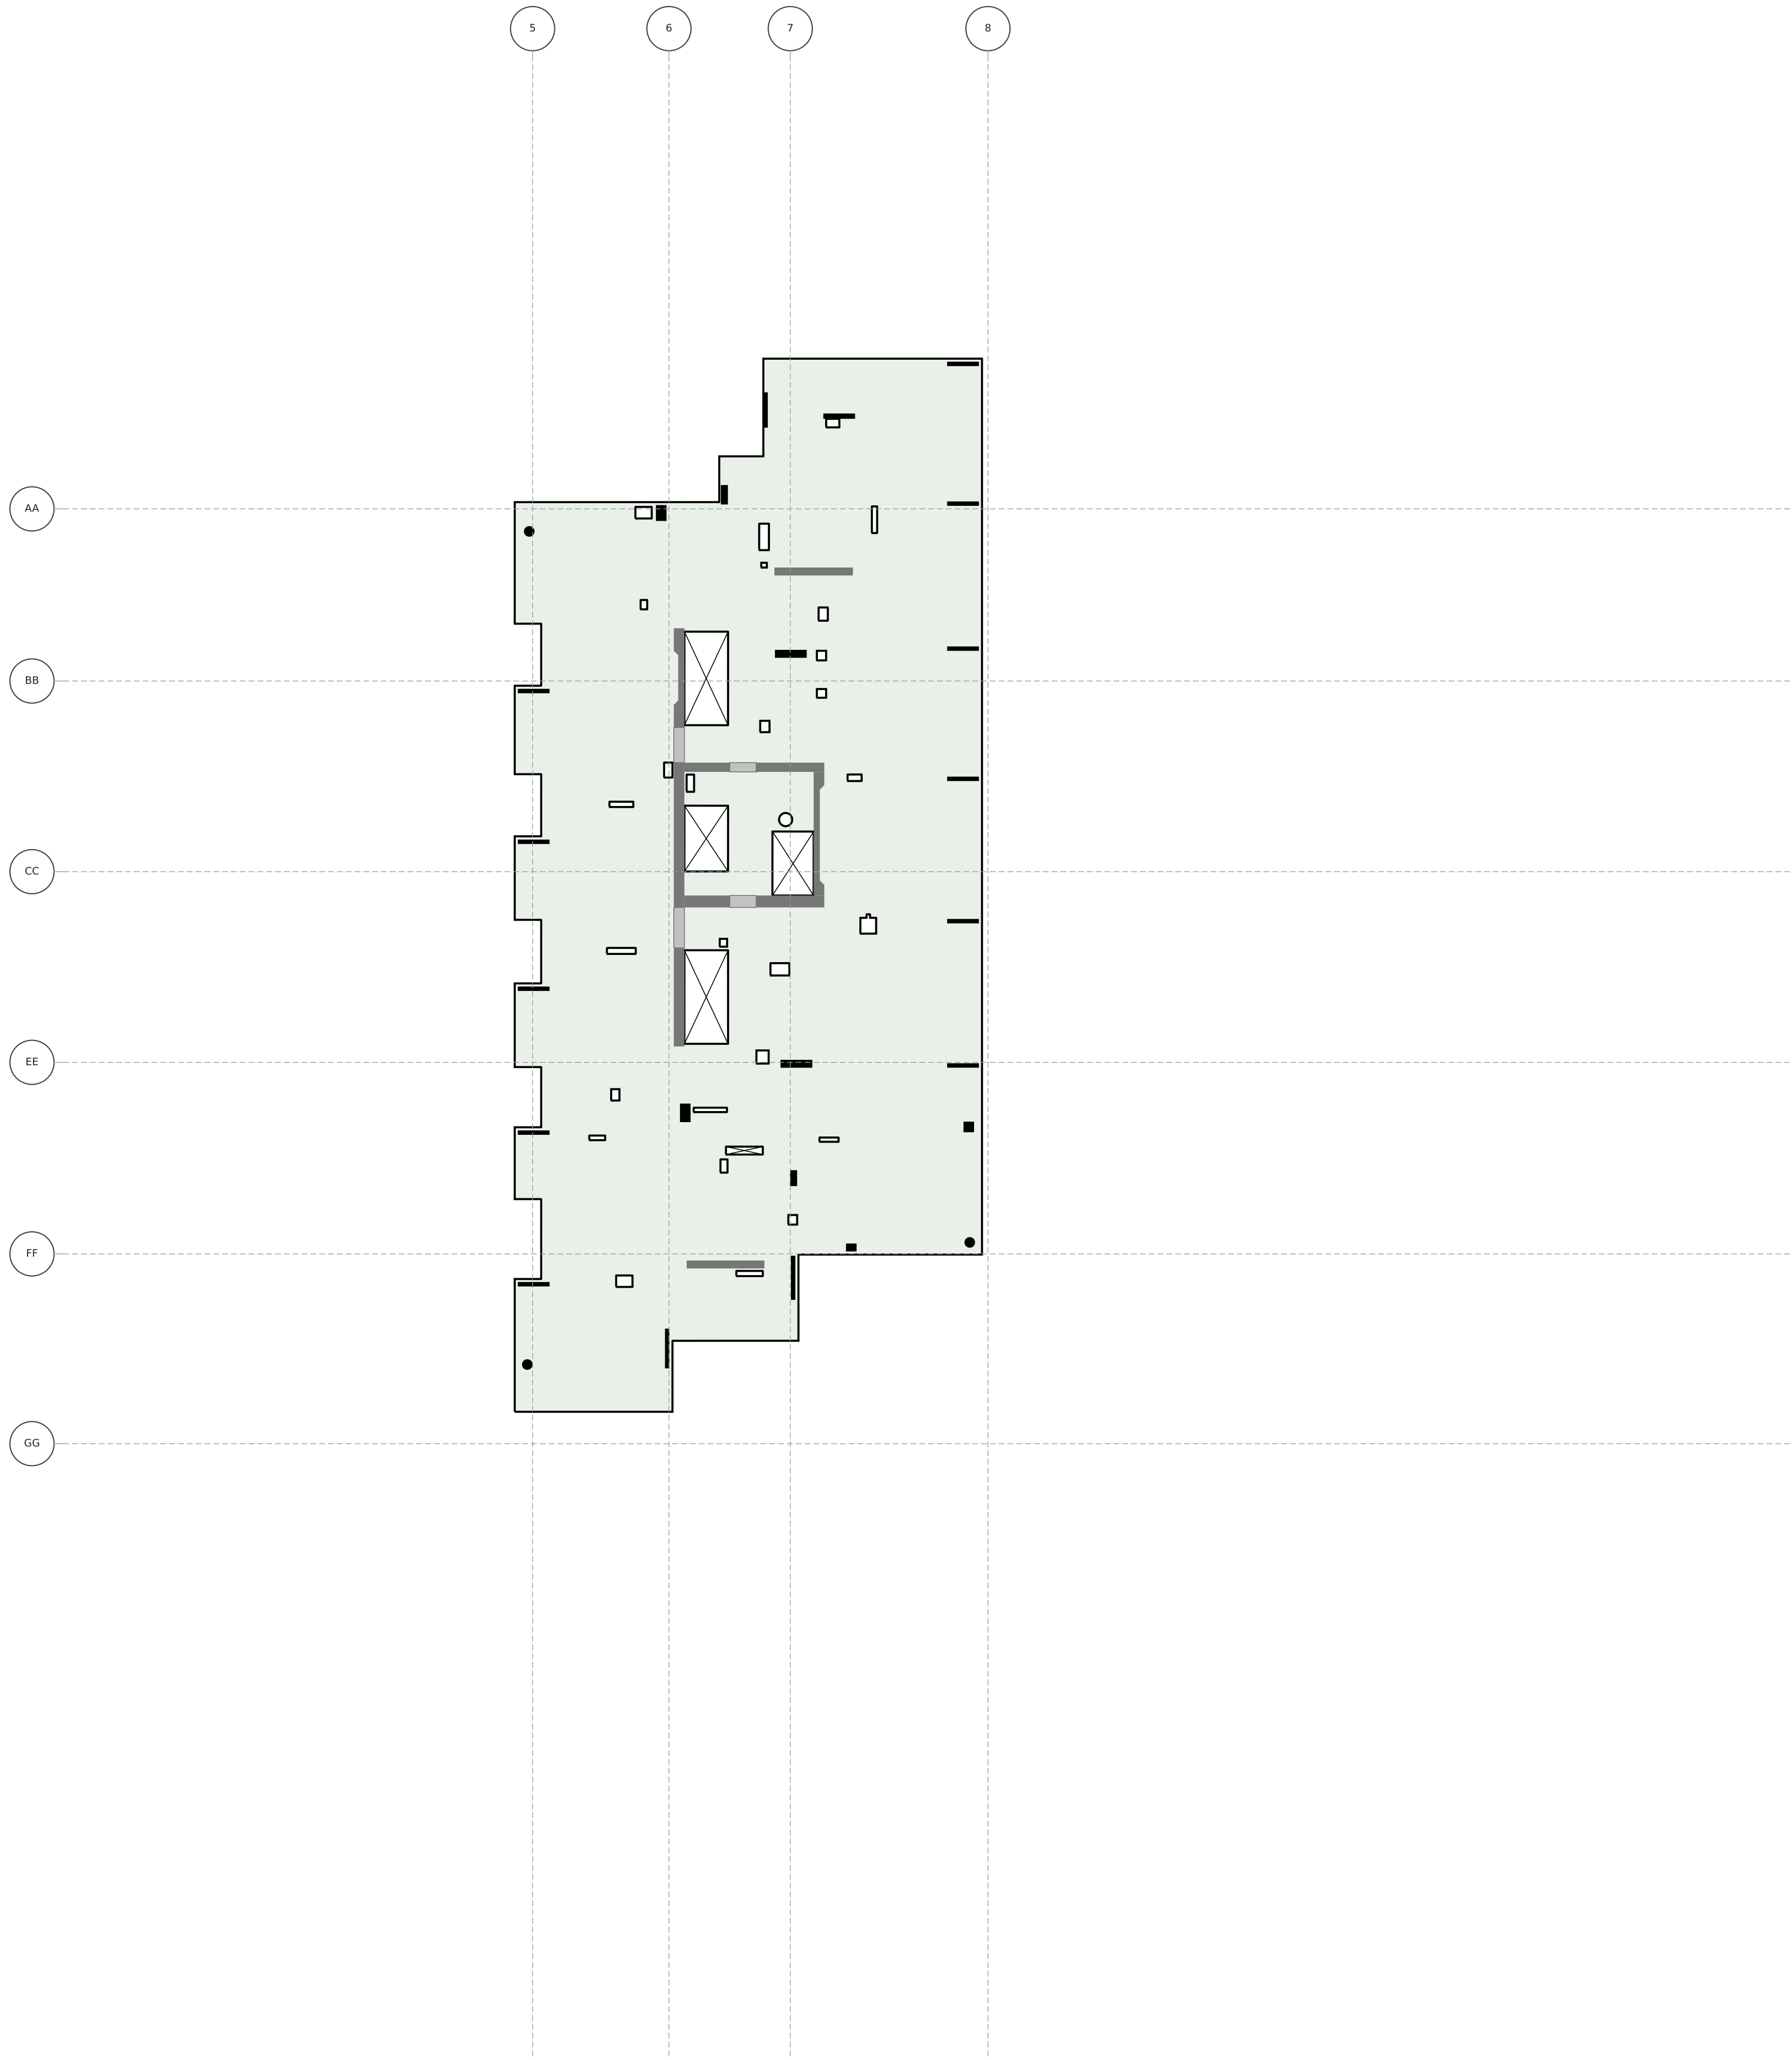


1268 KALAE

LEVEL 28 FLOOR PLAN

T.O.S. 282'-2" · typical slab 7 1/2" · scale 1" = 20'

Generated from HI_KALAE_MCC_ST.ifc (Revit scope model) for the McClone Reshore Calculator — geometry only; loading marks are drawn in the calculator.

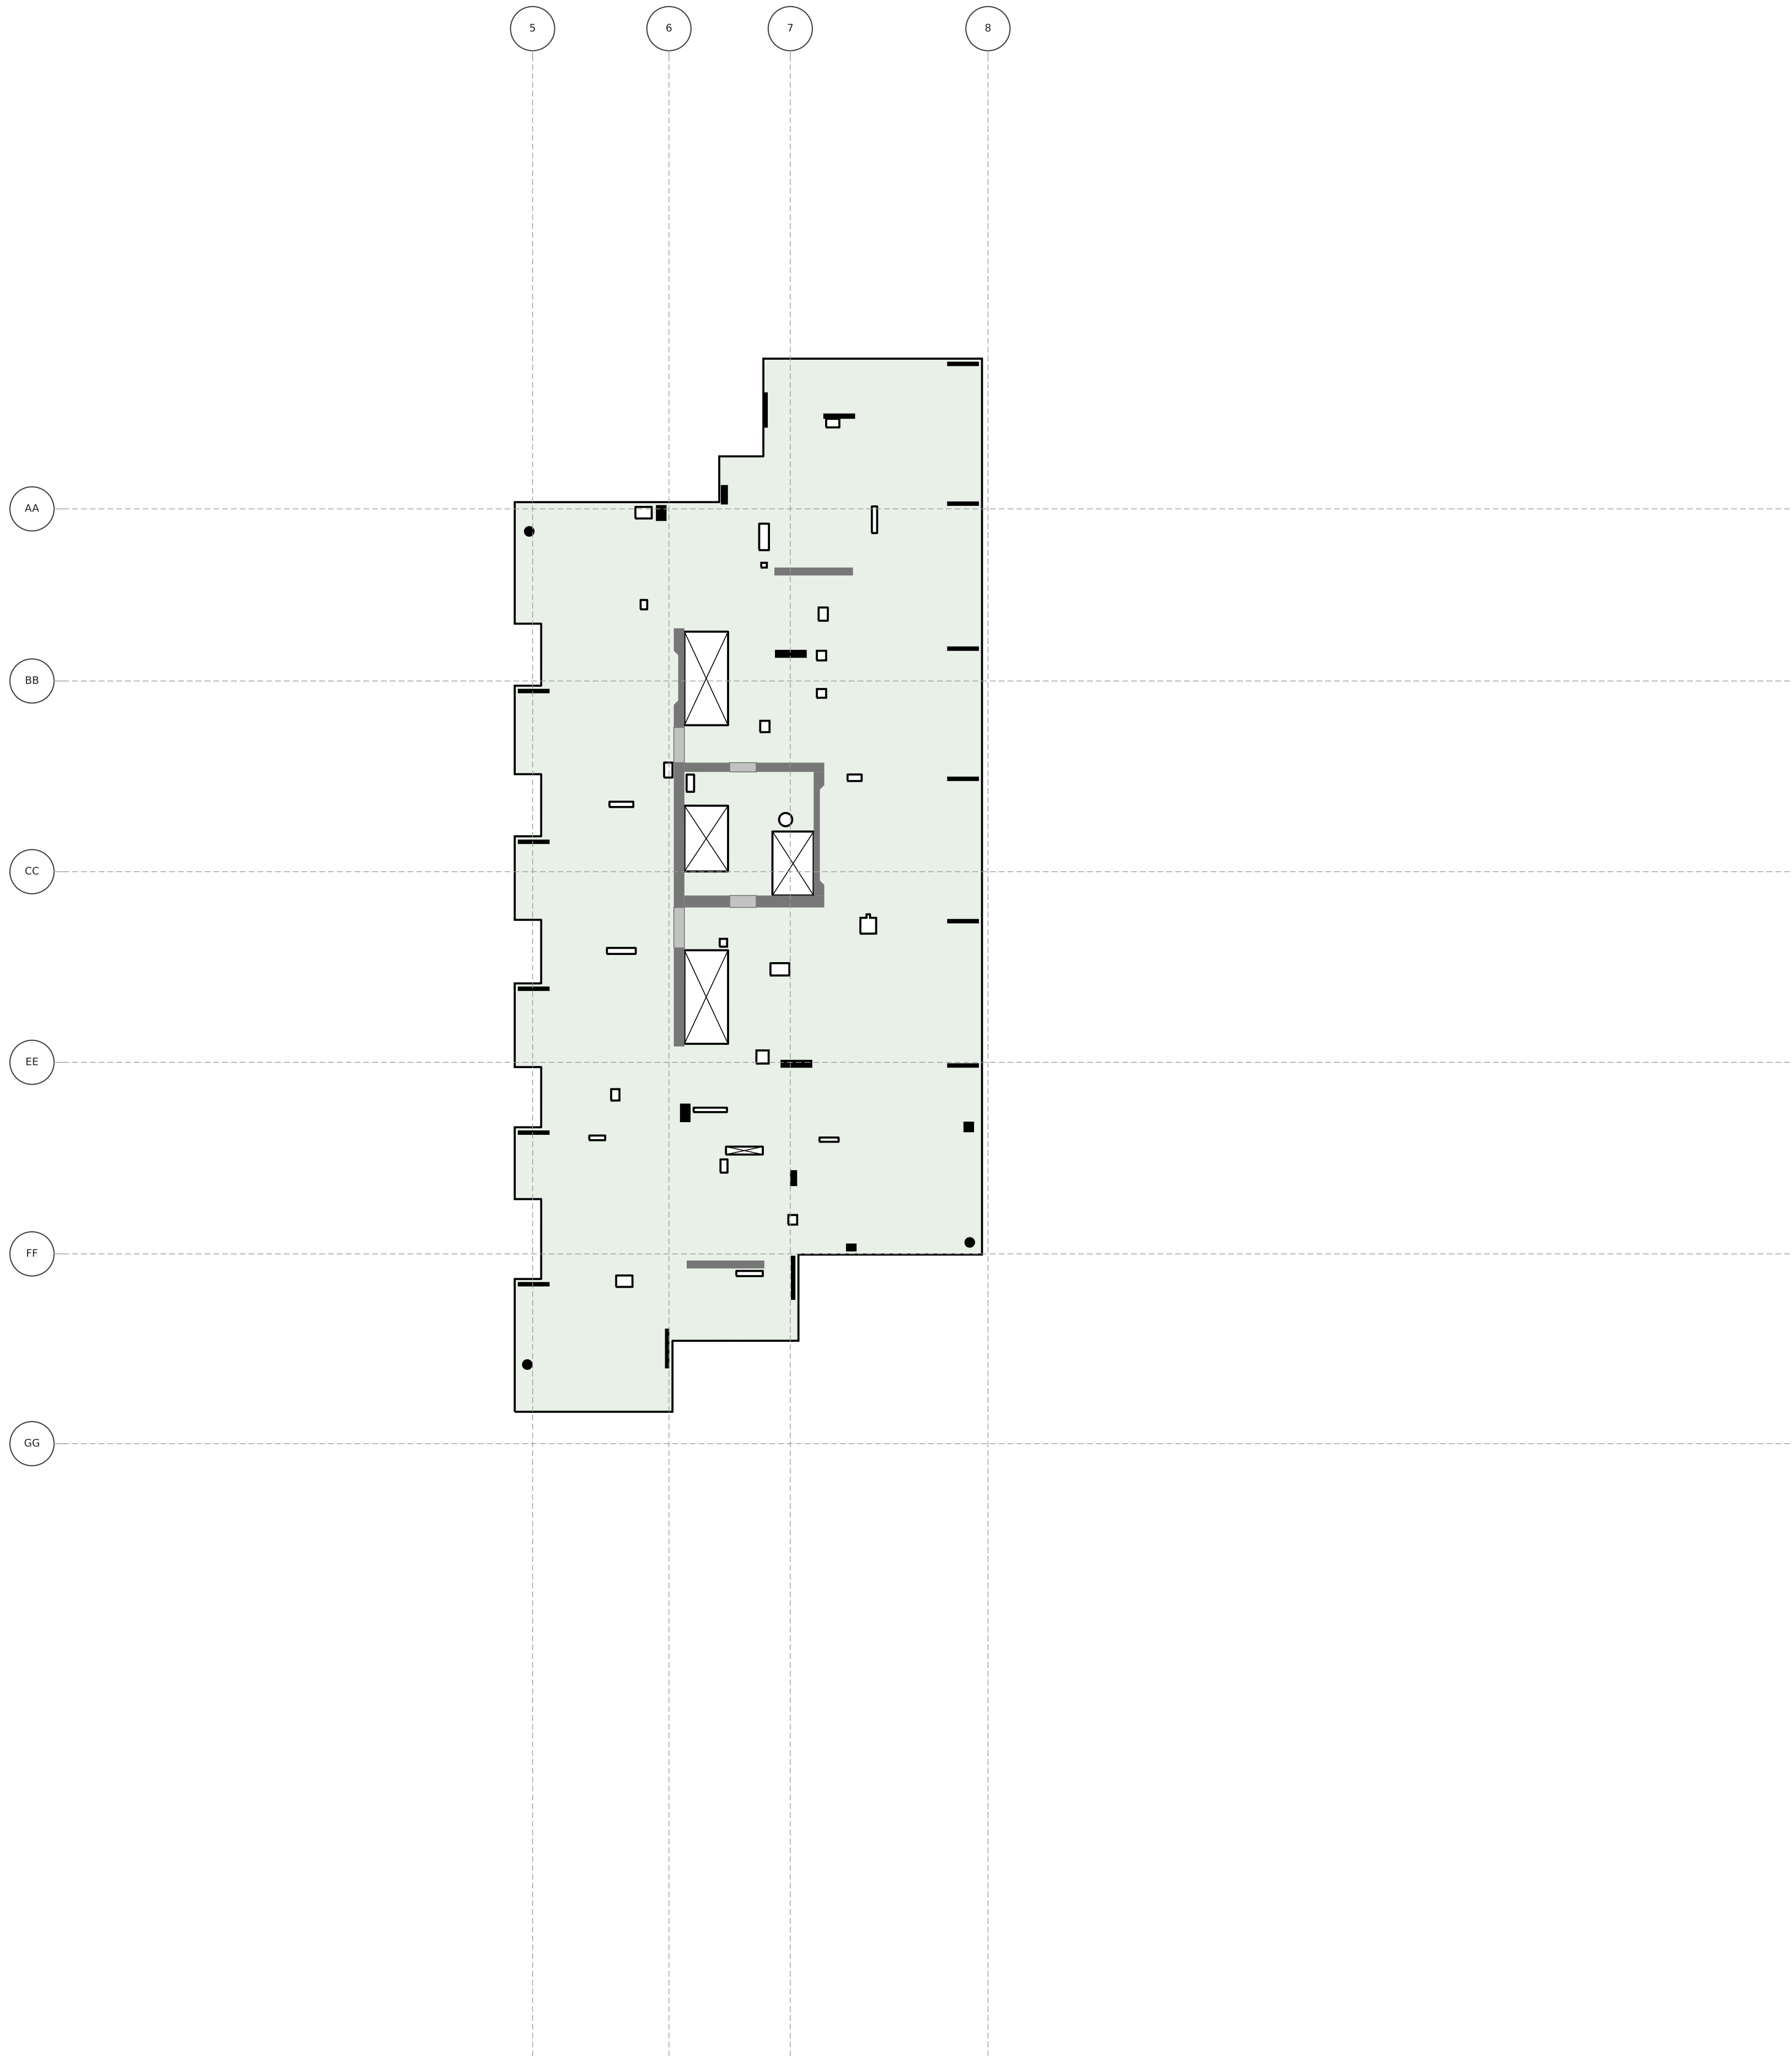


1268 KALAE

LEVEL 29 FLOOR PLAN

T.O.S. 291'-10 1/2" · typical slab 7 1/2" · scale 1" = 20'

Generated from HI_KALAE_MCC_ST.ifc (Revit scope model) for the McClone Reshore Calculator — geometry only; loading marks are drawn in the calculator.

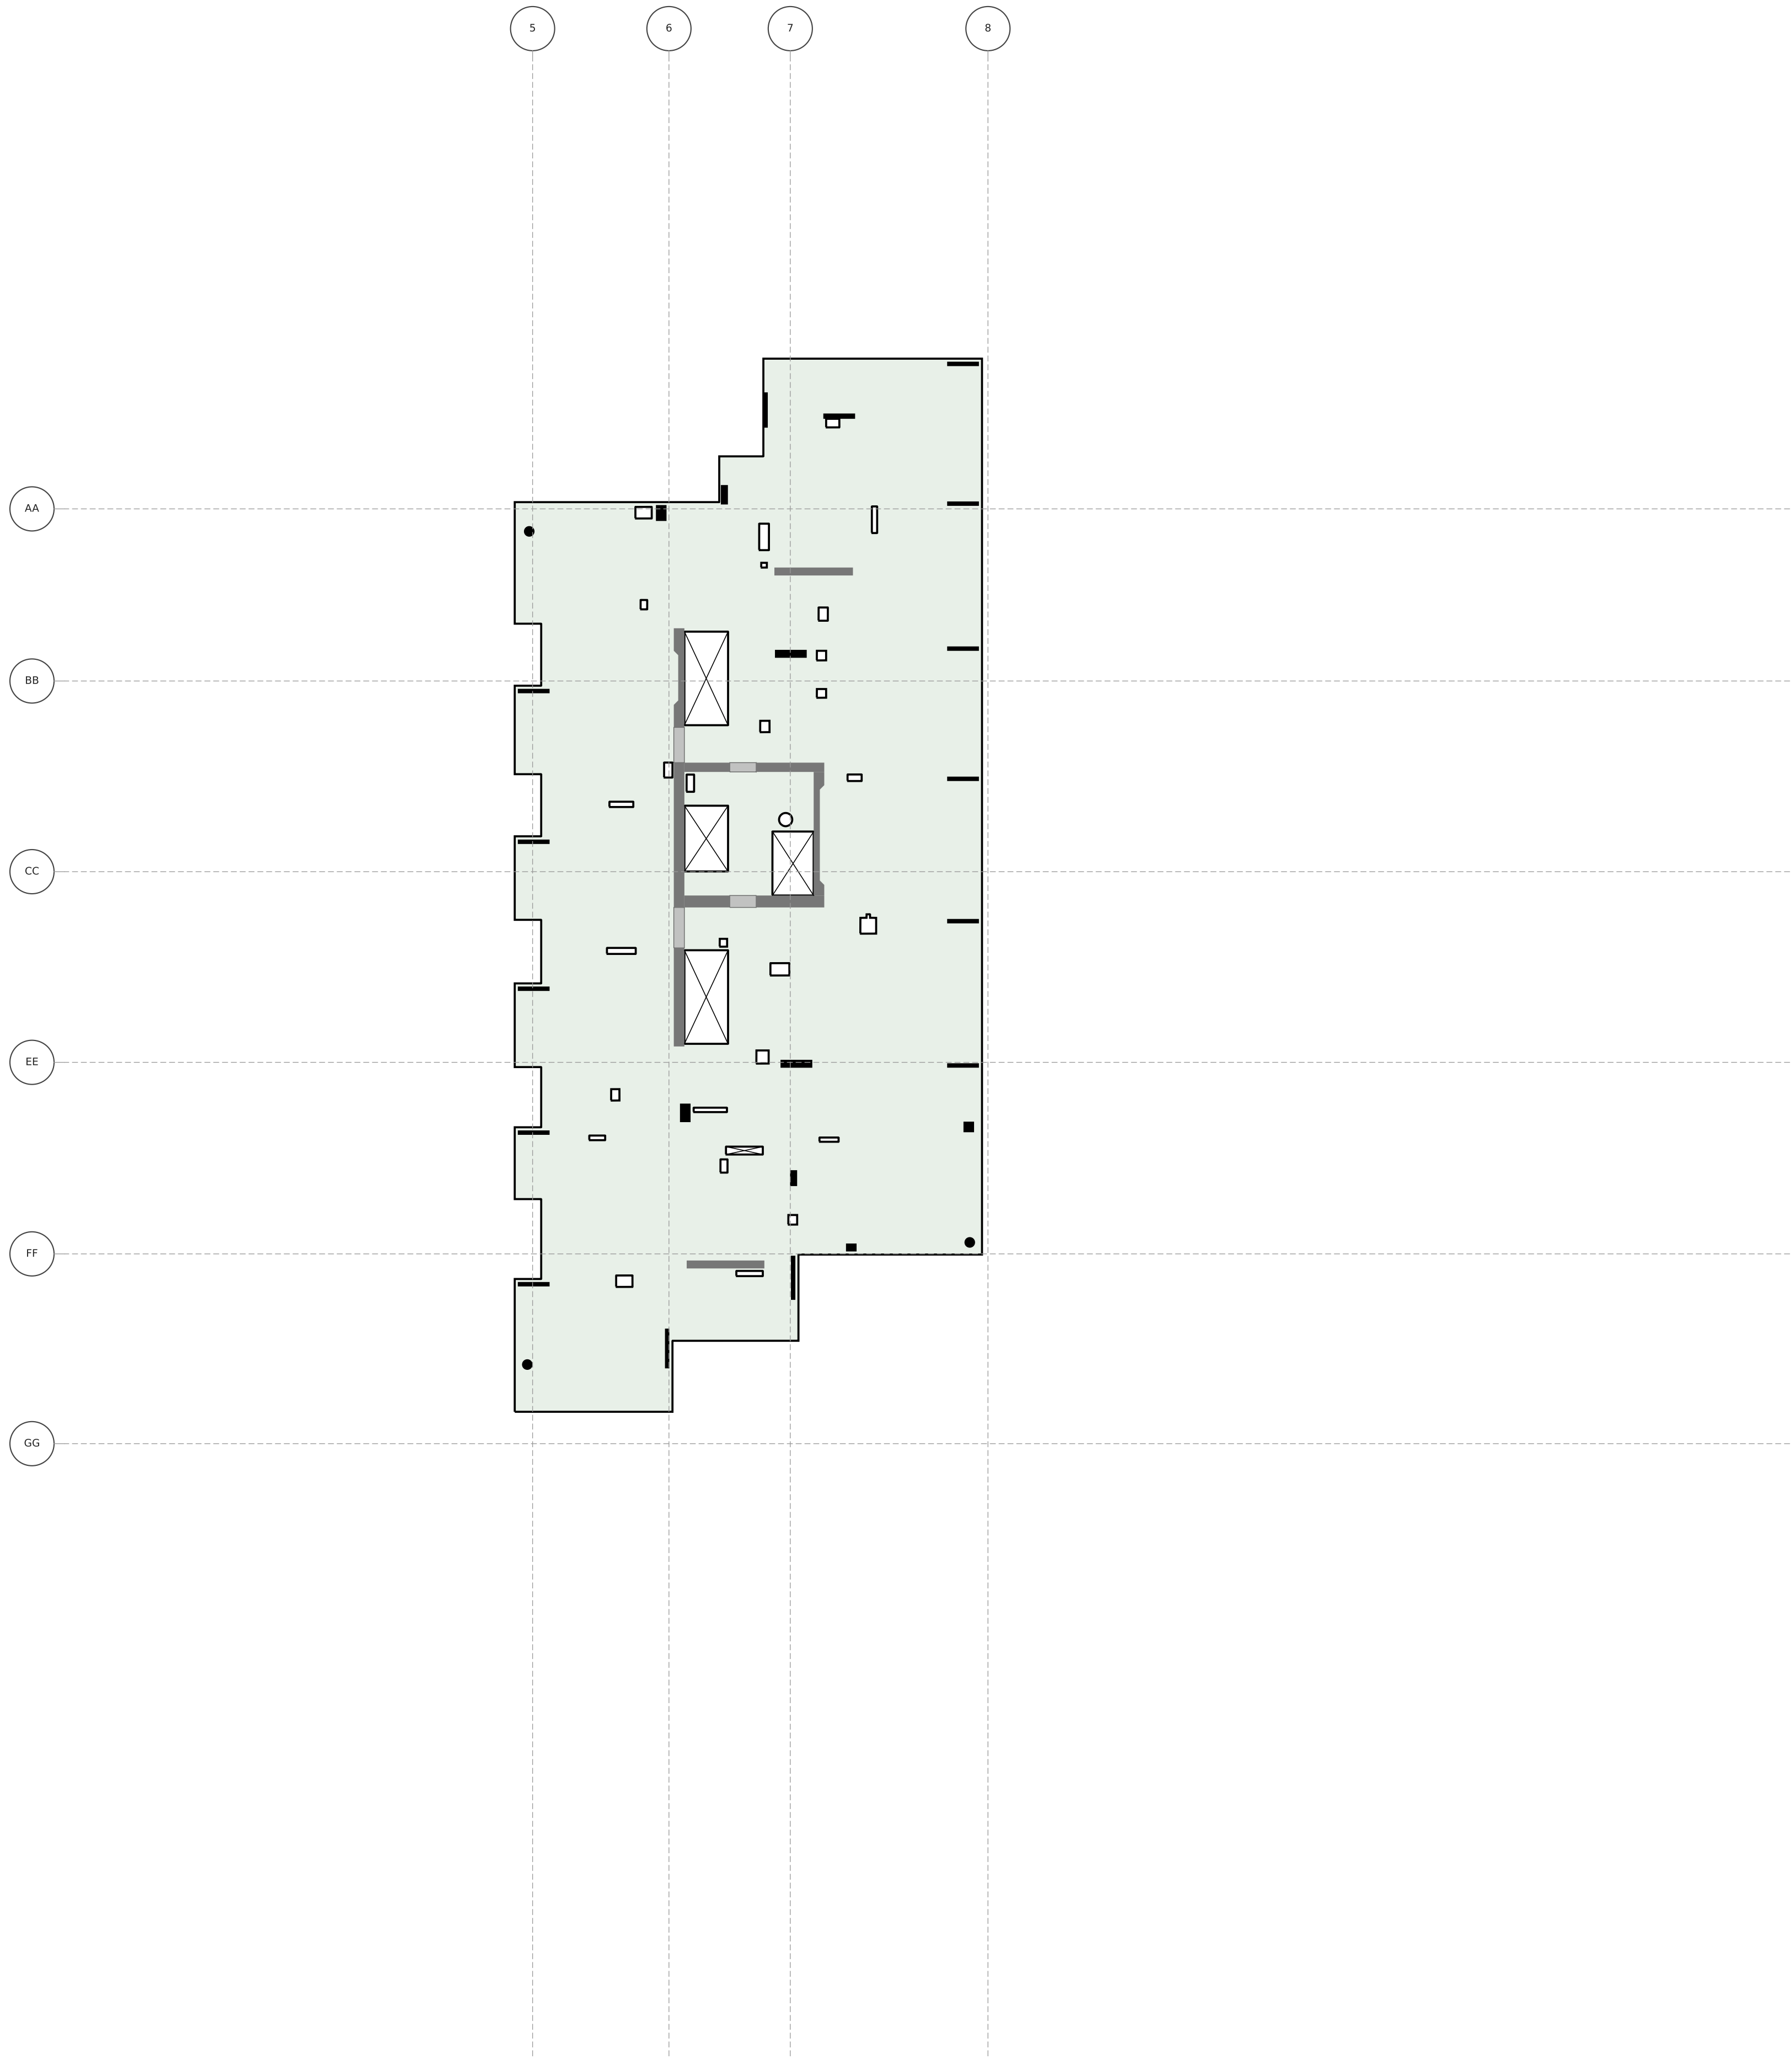


1268 KALAE

LEVEL 30 FLOOR PLAN

T.O.S. 301'-7" · typical slab 7 1/2" · scale 1" = 20'

Generated from HI_KALAE_MCC_ST.ifc (Revit scope model) for the McClone Reshore Calculator — geometry only; loading marks are drawn in the calculator.

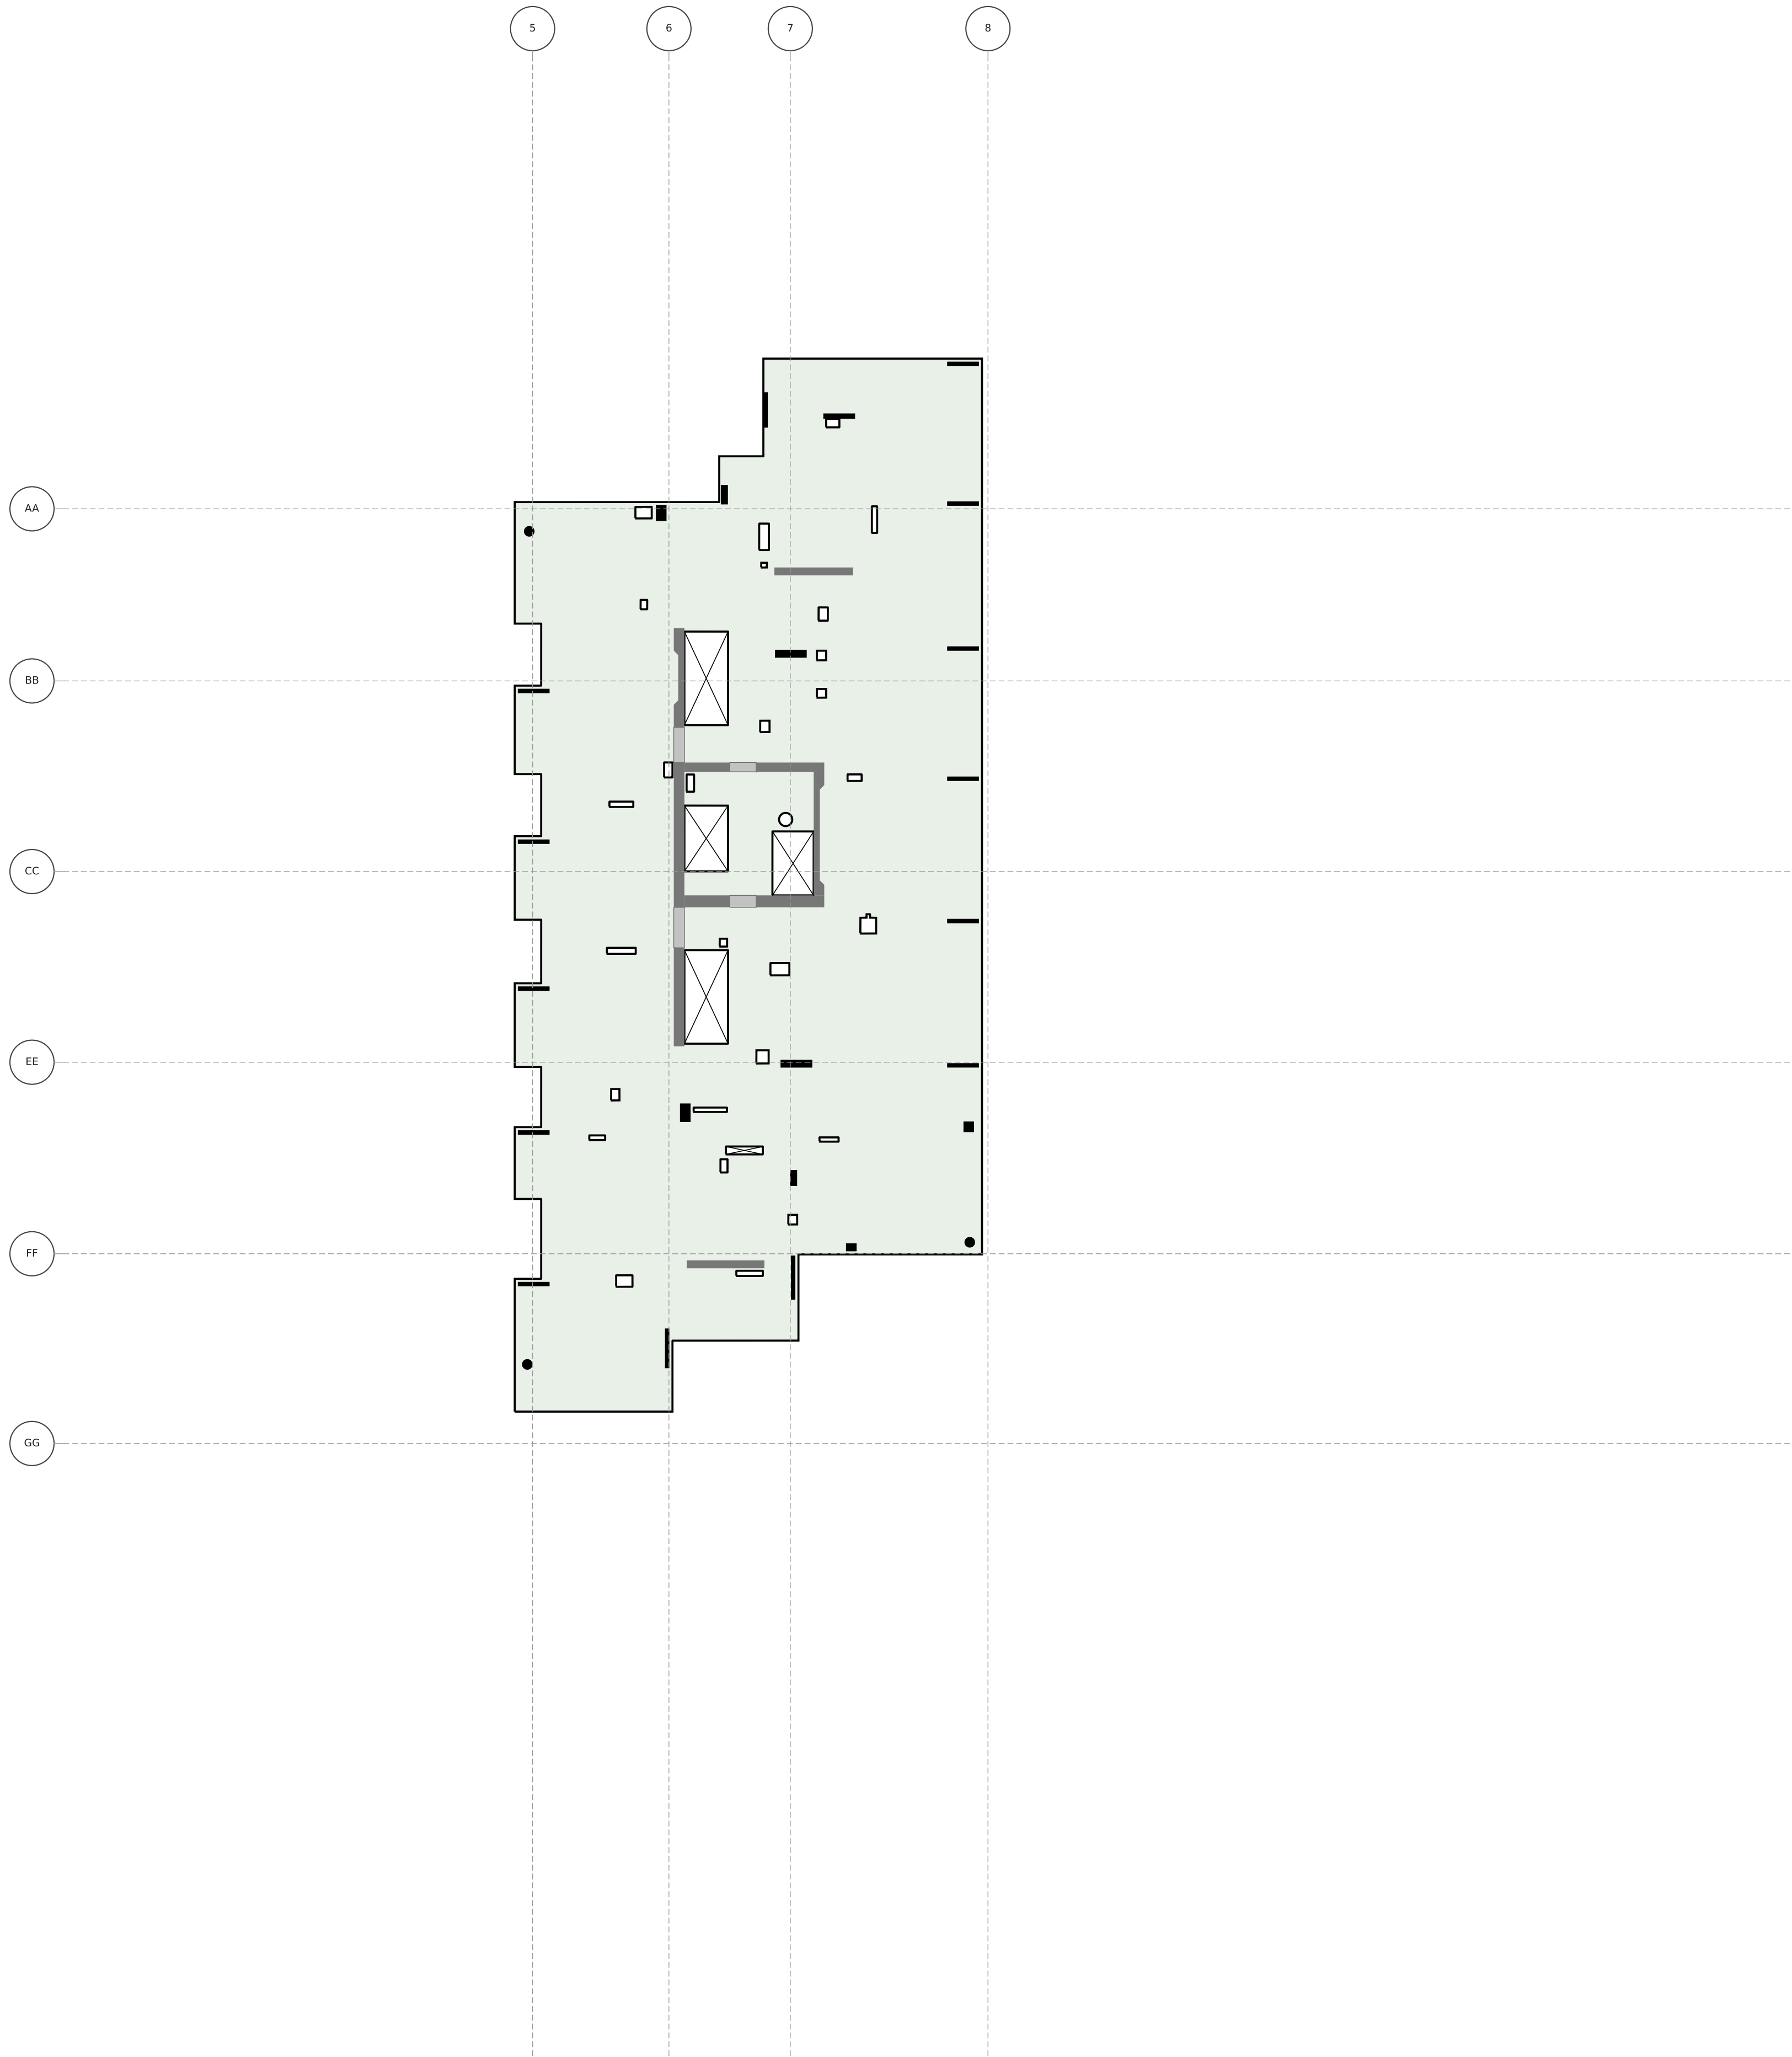


1268 KALAE

LEVEL 31 FLOOR PLAN

T.O.S. 311'-3 1/2" · typical slab 7 1/2" · scale 1" = 20'

Generated from HI_KALAE_MCC_ST.ifc (Revit scope model) for the McClone Reshore Calculator — geometry only; loading marks are drawn in the calculator.

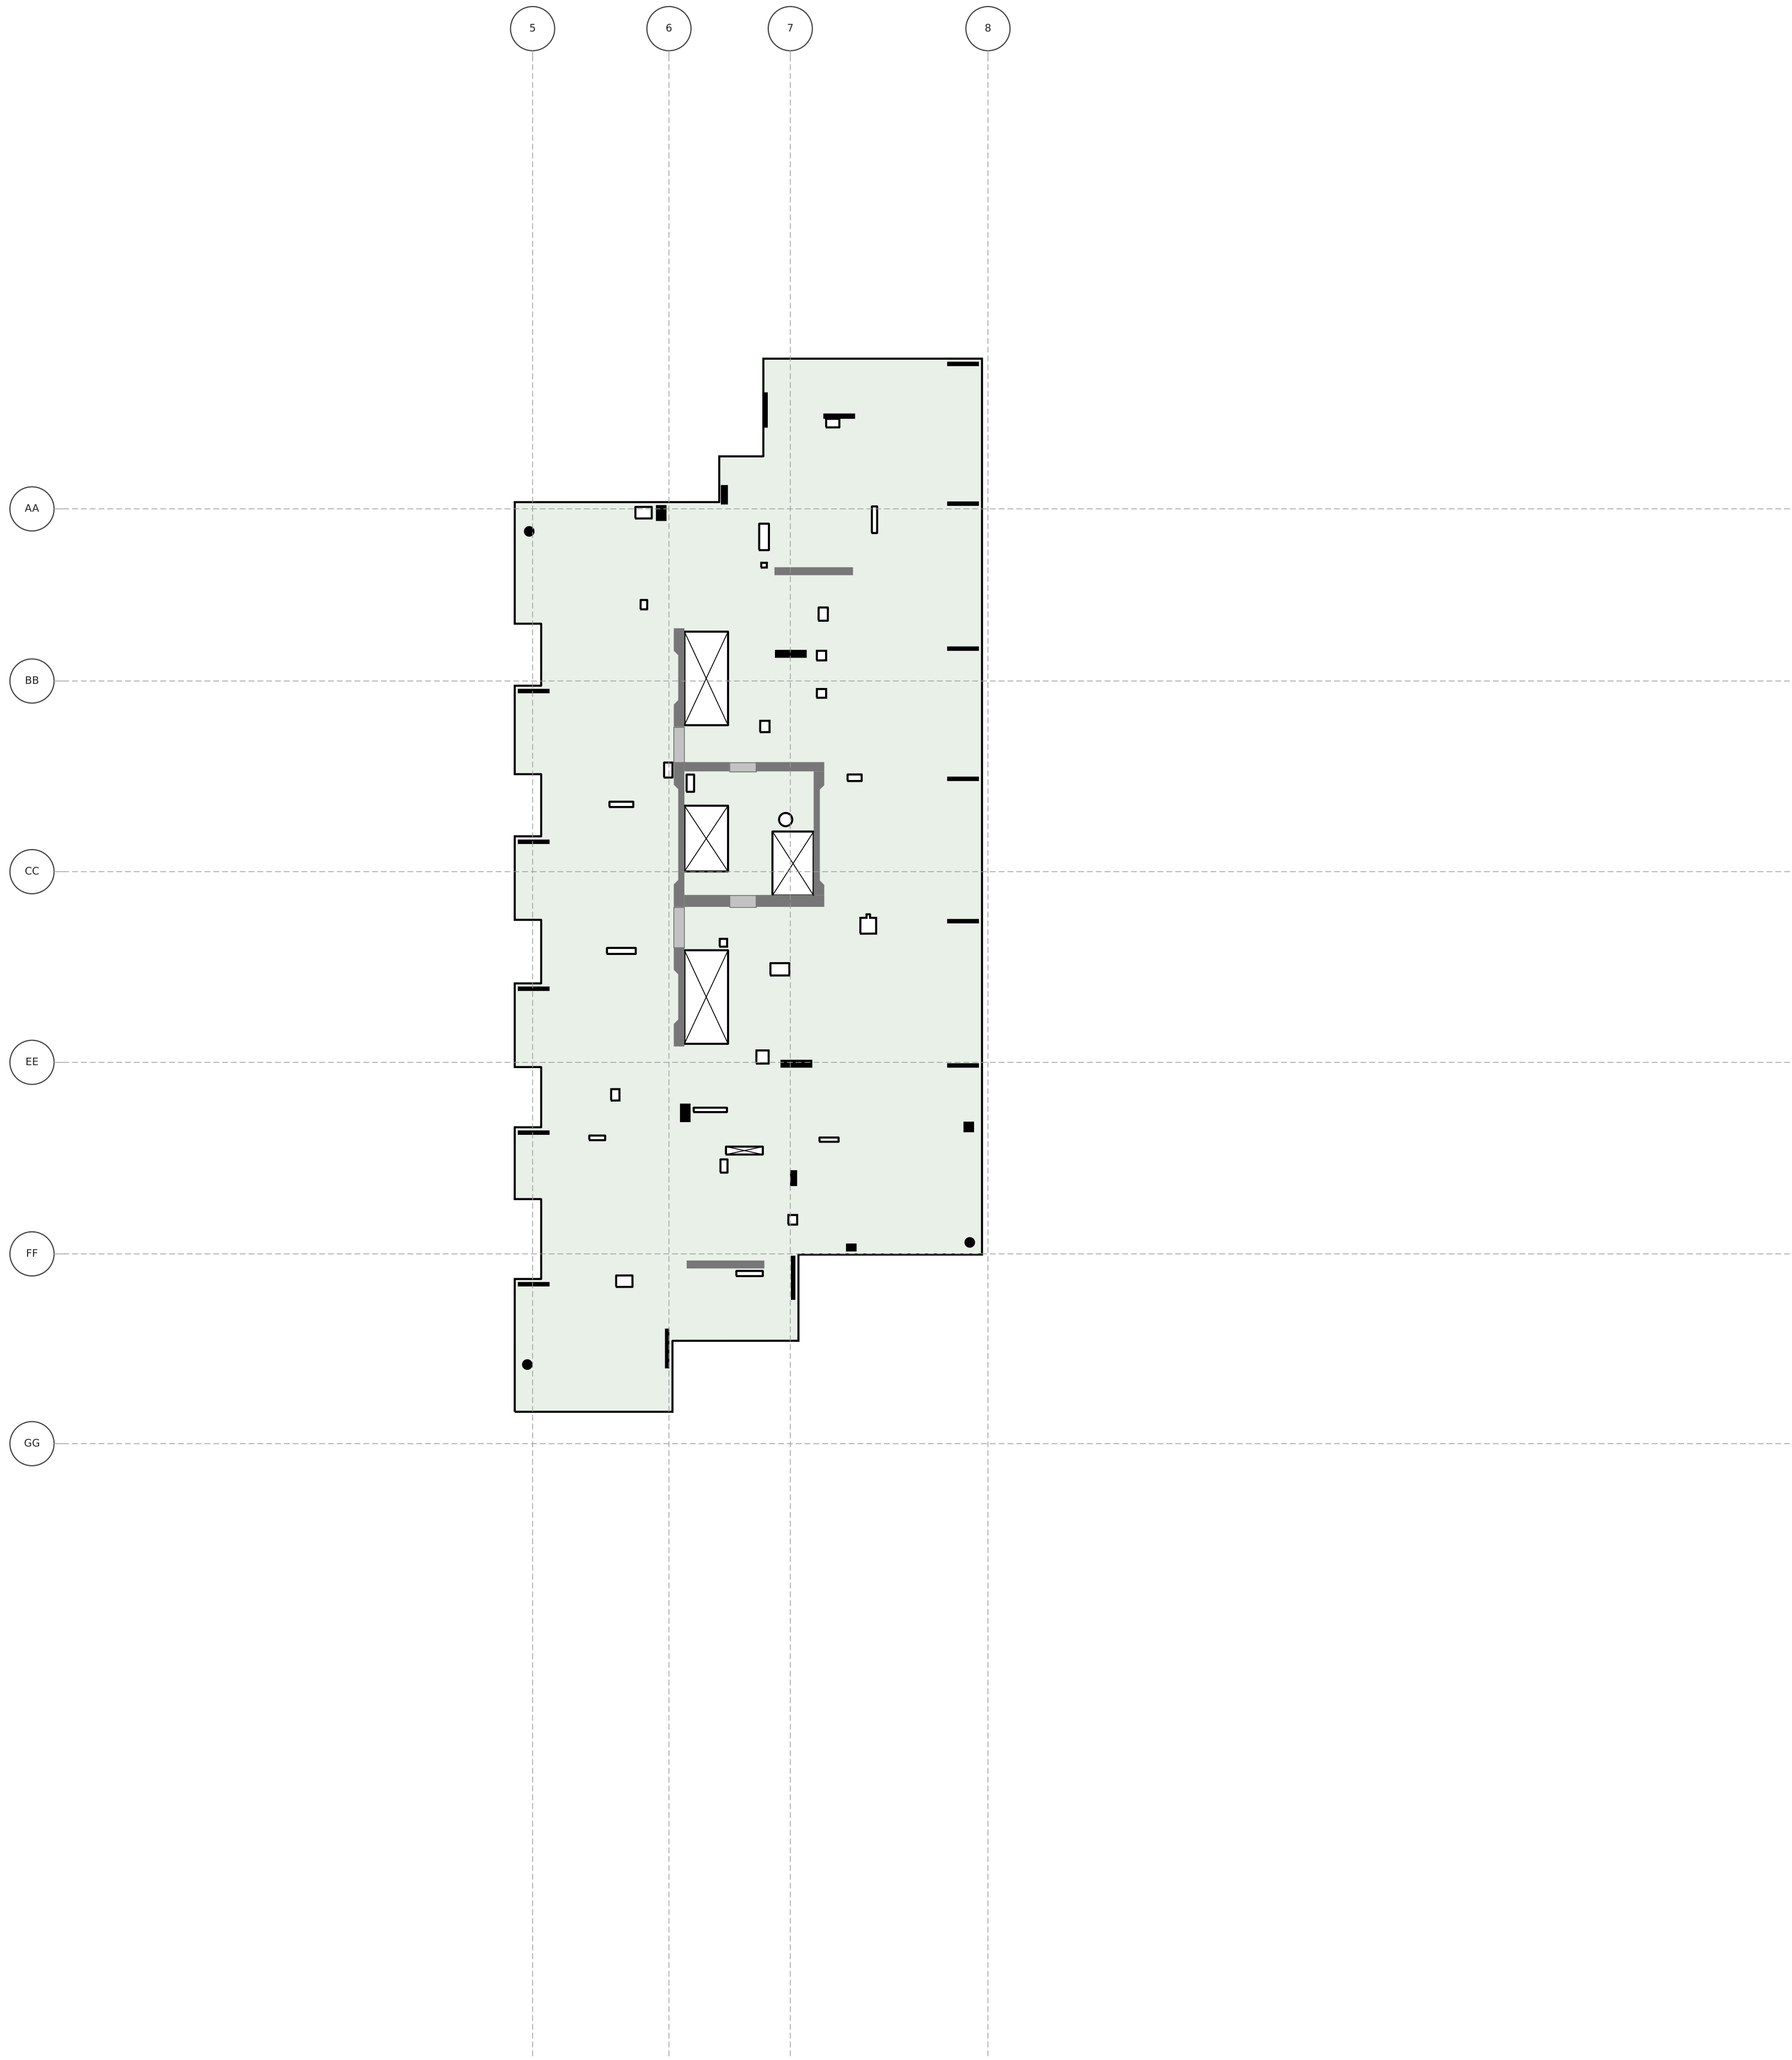


1268 KALAE

LEVEL 32 FLOOR PLAN

T.O.S. 321'-0" · typical slab 7 1/2" · scale 1" = 20'

Generated from HI_KALAE_MCC_ST.ifc (Revit scope model) for the McClone Reshore Calculator — geometry only; loading marks are drawn in the calculator.

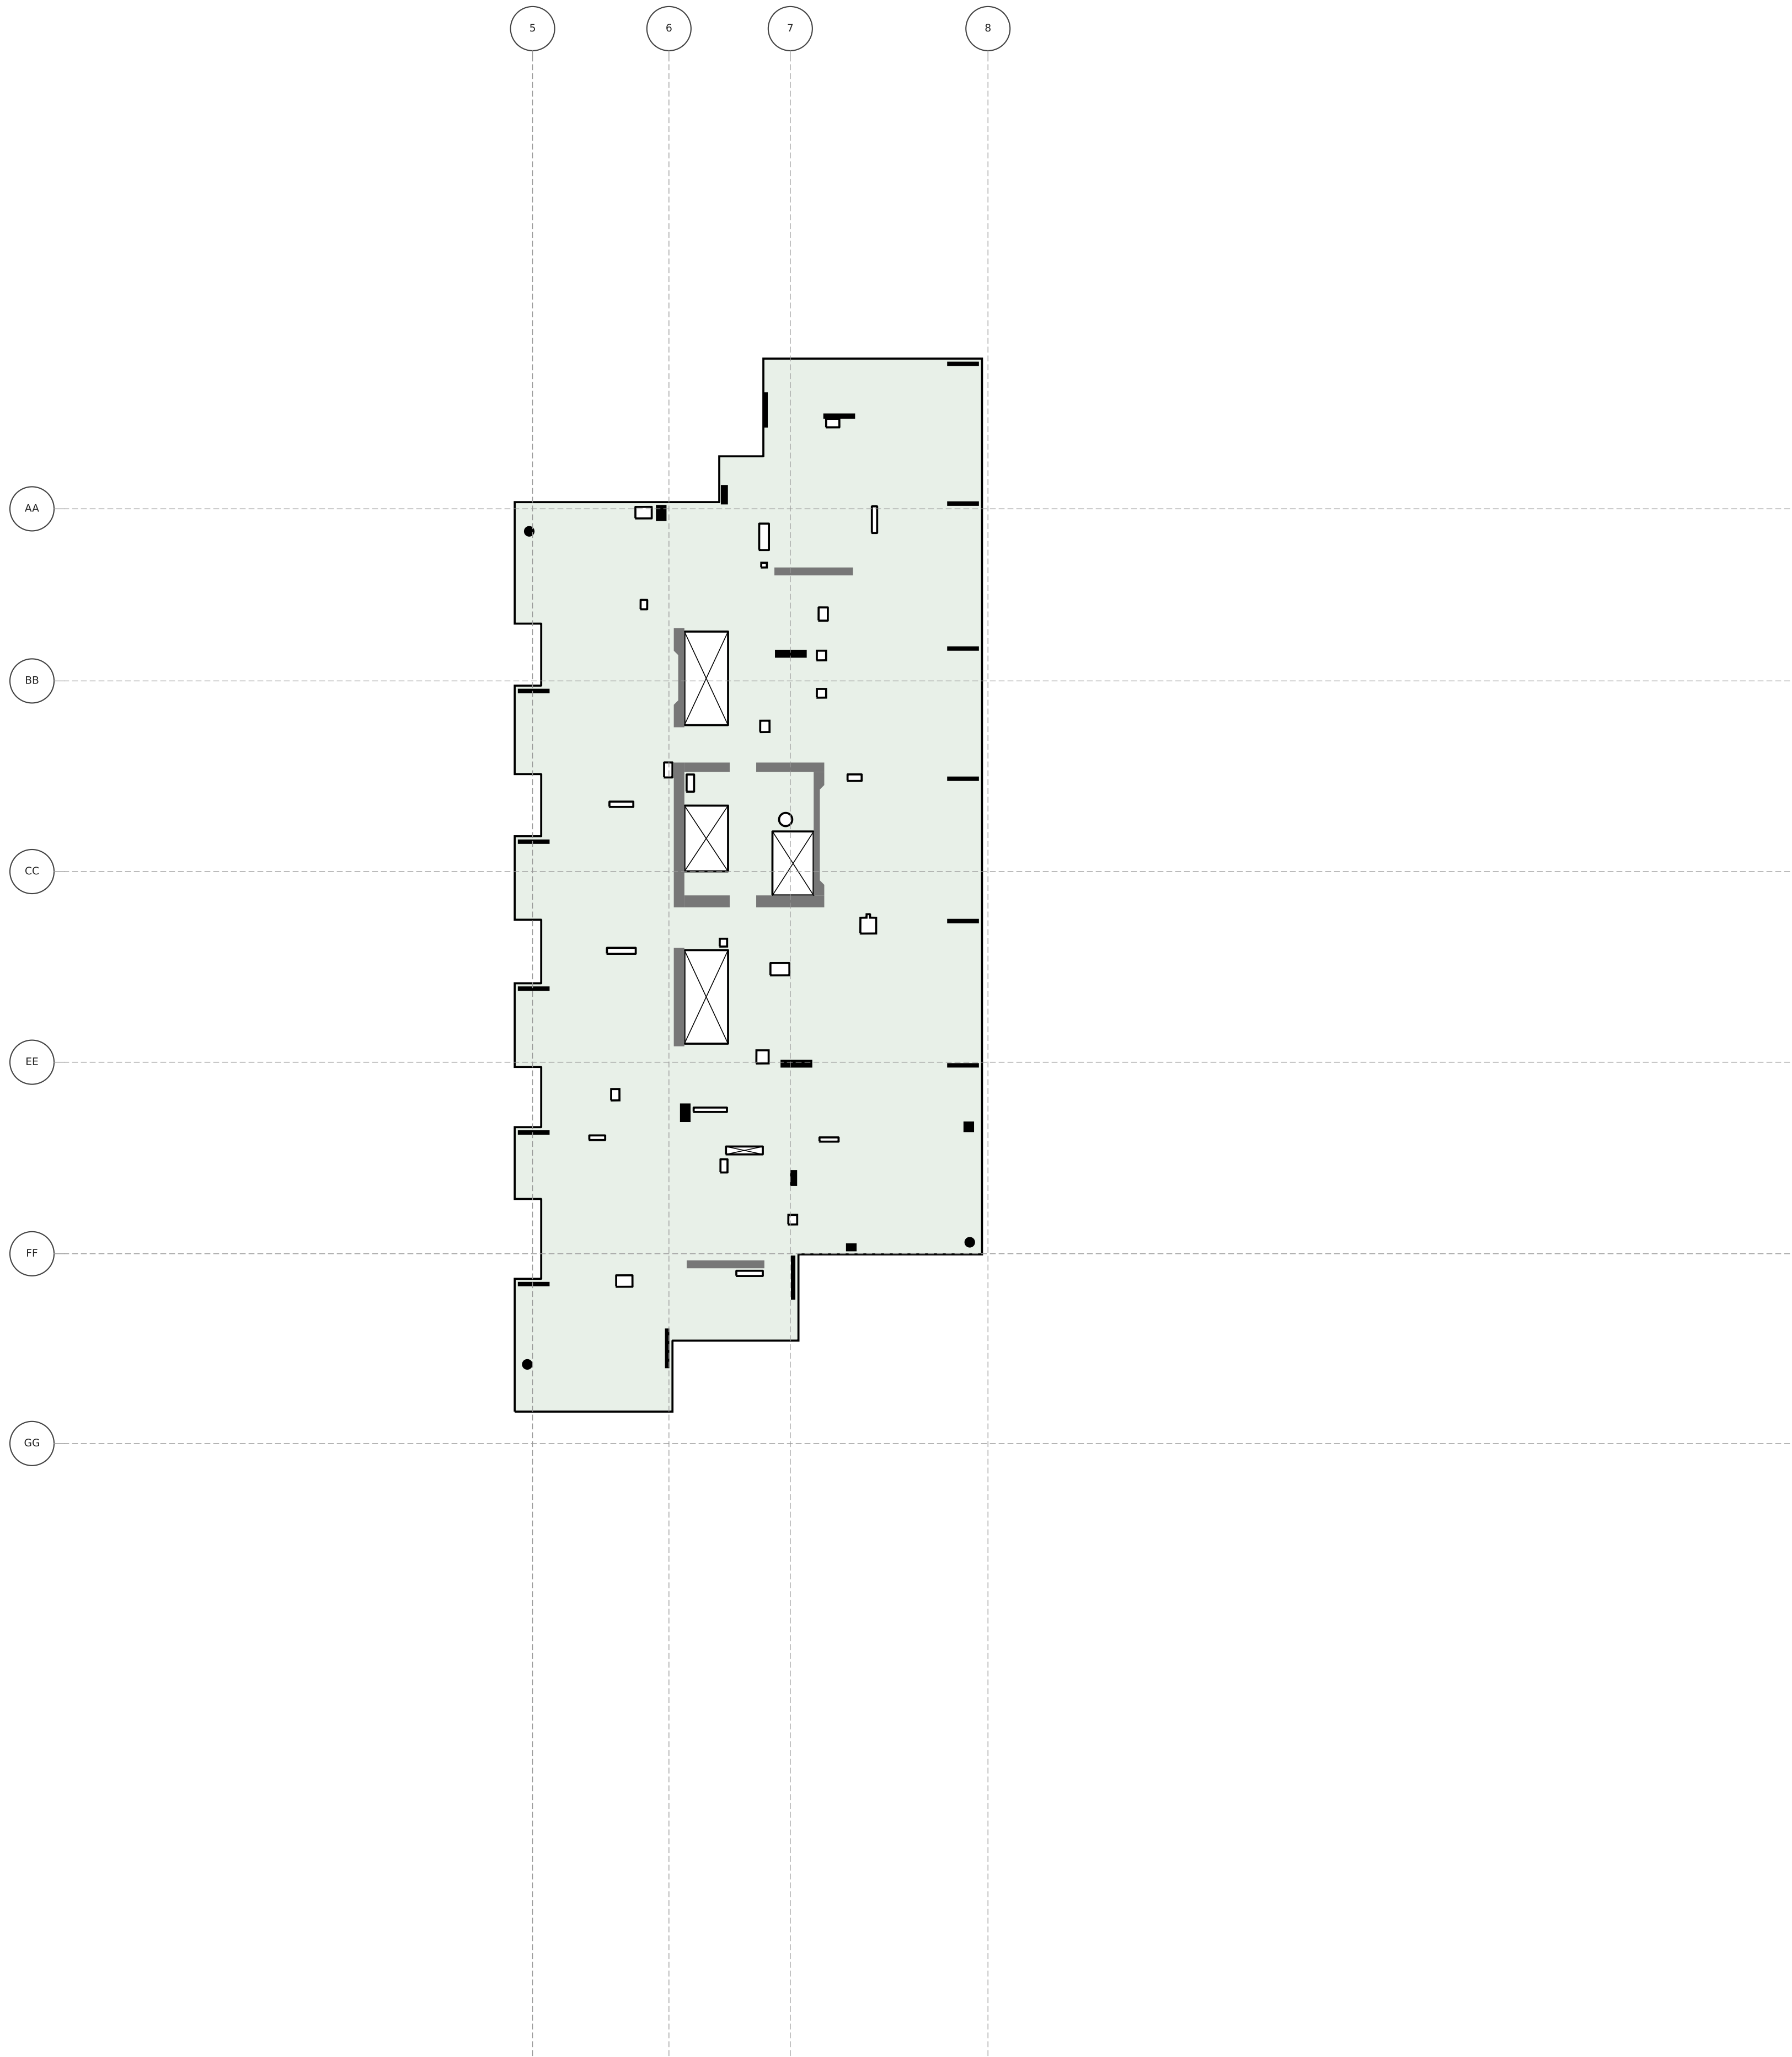


1268 KALAE

LEVEL 33 FLOOR PLAN

T.O.S. 330'-10 1/2" · typical slab 7 1/2" · scale 1" = 20'

Generated from HI_KALAE_MCC_ST.ifc (Revit scope model) for the McClone Reshore Calculator — geometry only; loading marks are drawn in the calculator.

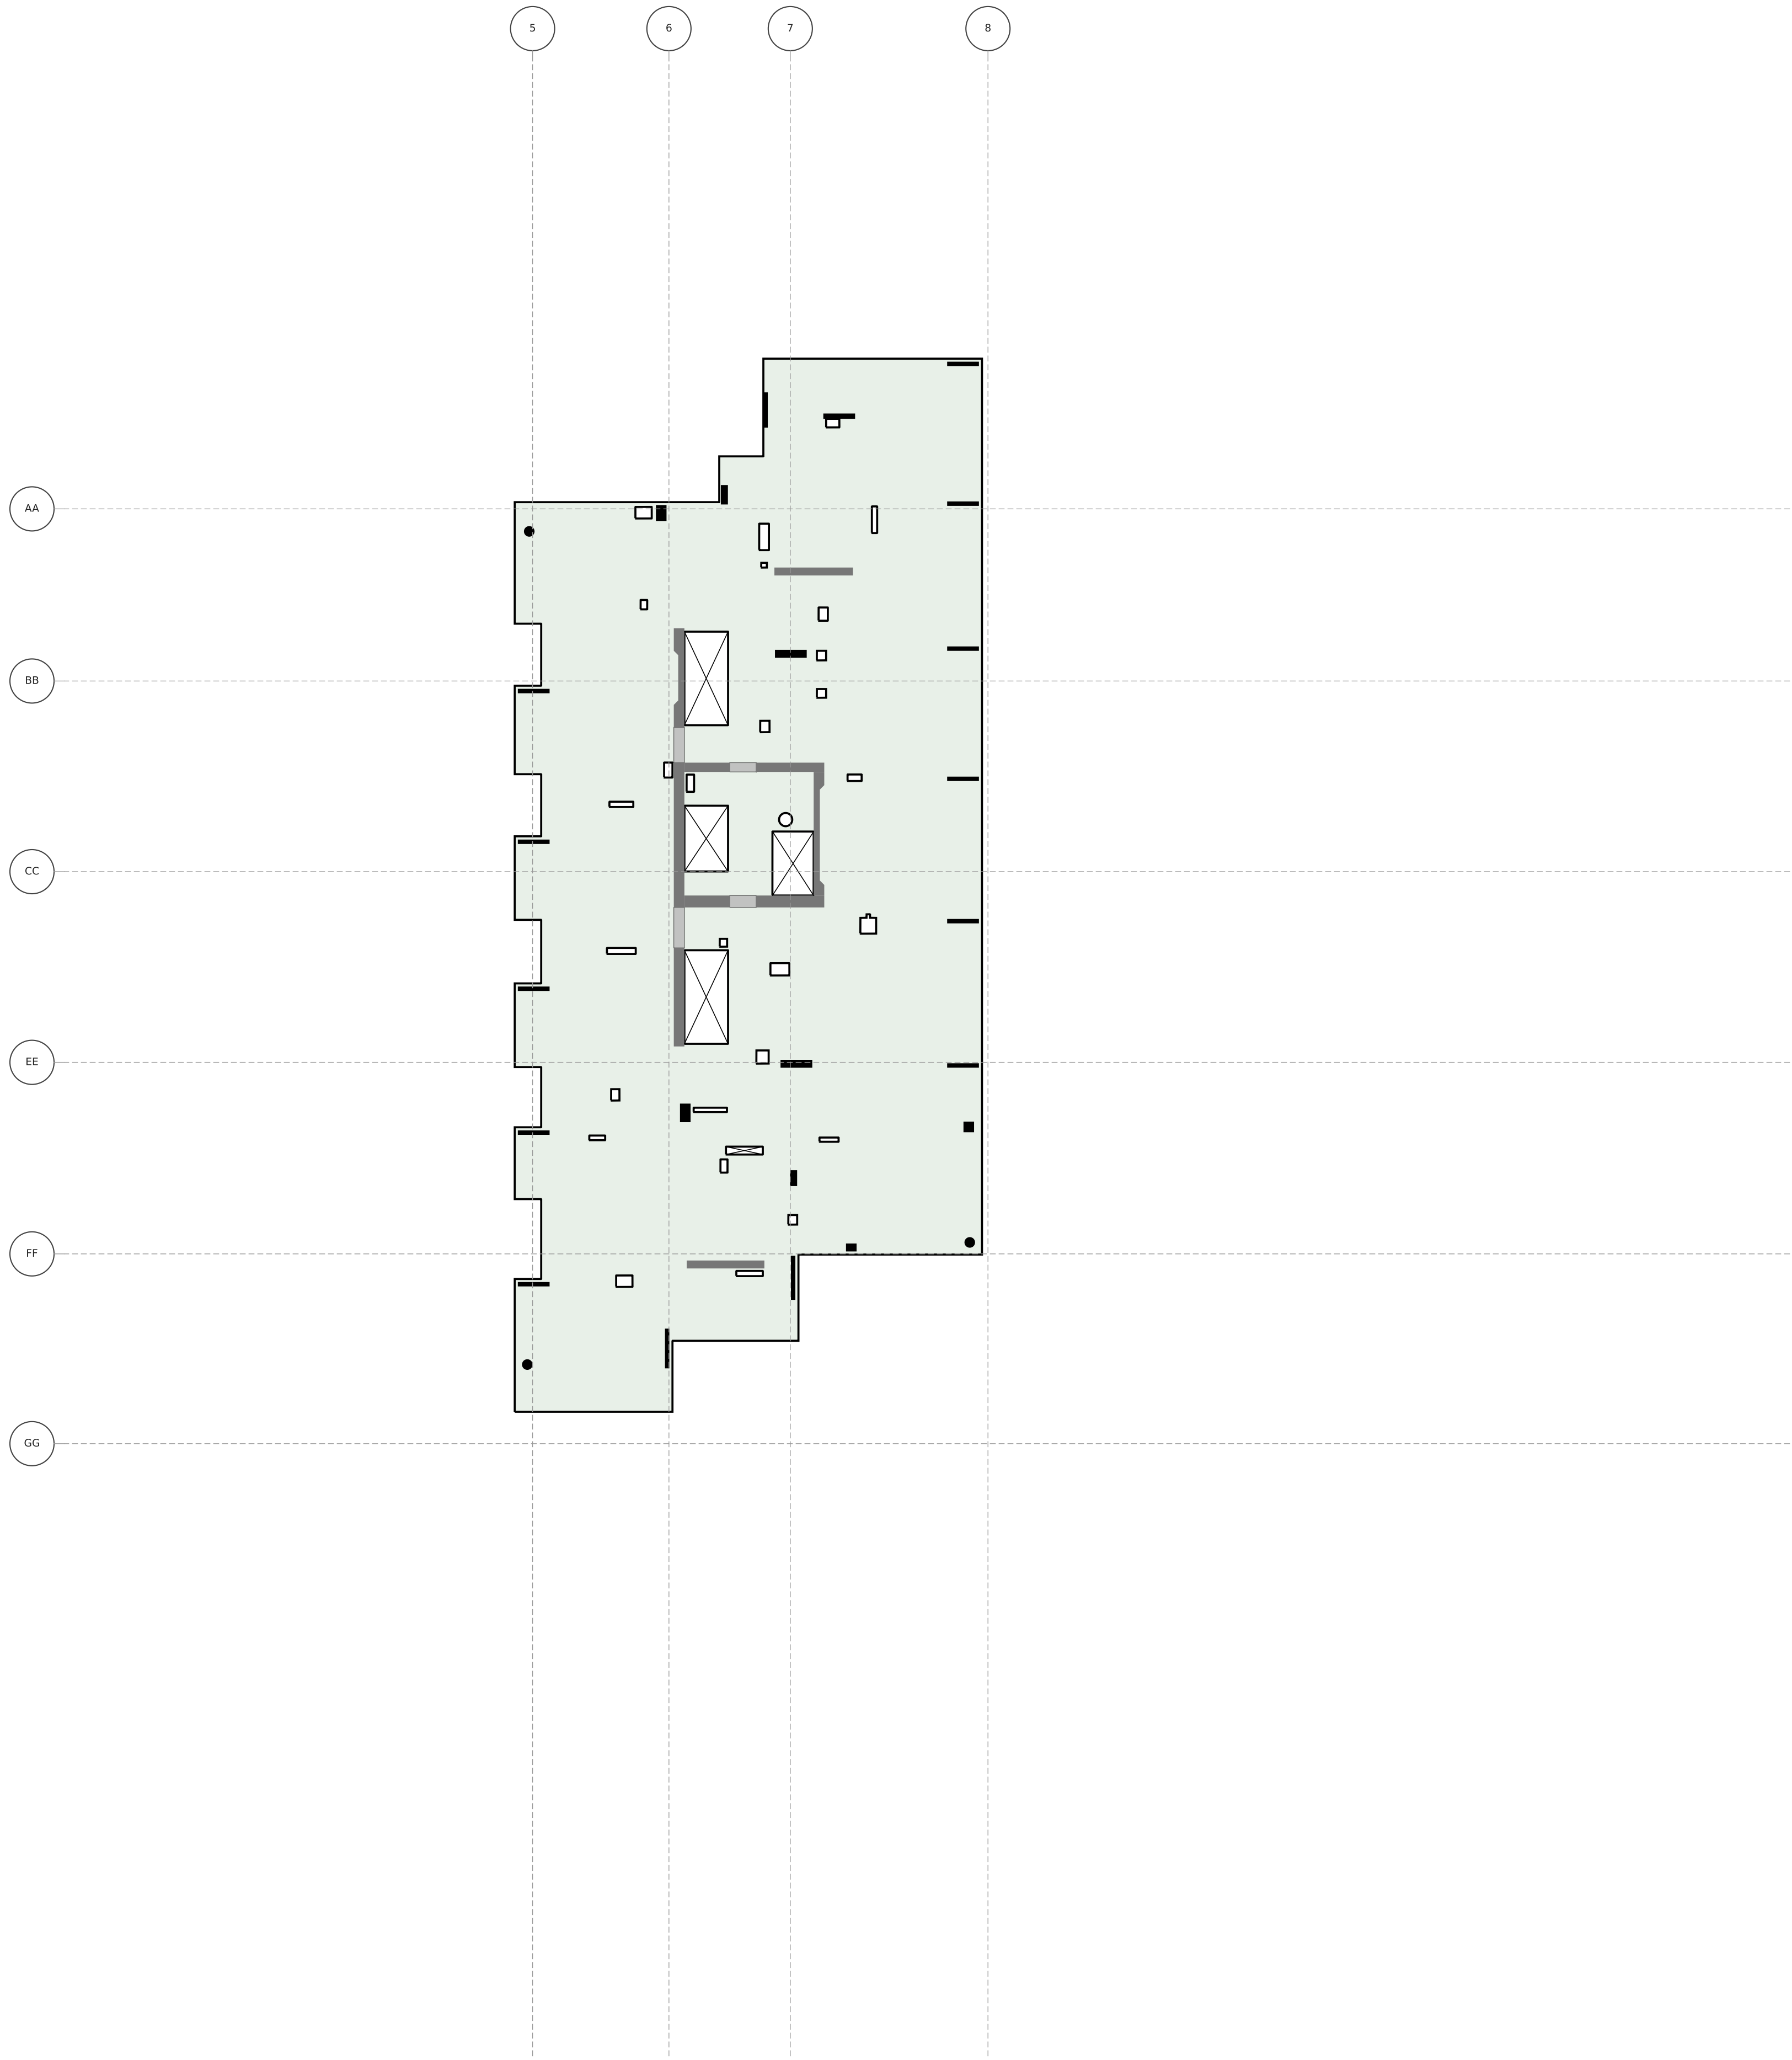


1268 KALAE

LEVEL 34 FLOOR PLAN

T.O.S. 340'-7" · typical slab 7 1/2" · scale 1" = 20'

Generated from HI_KALAE_MCC_ST.ifc (Revit scope model) for the McClone Reshore Calculator — geometry only; loading marks are drawn in the calculator.

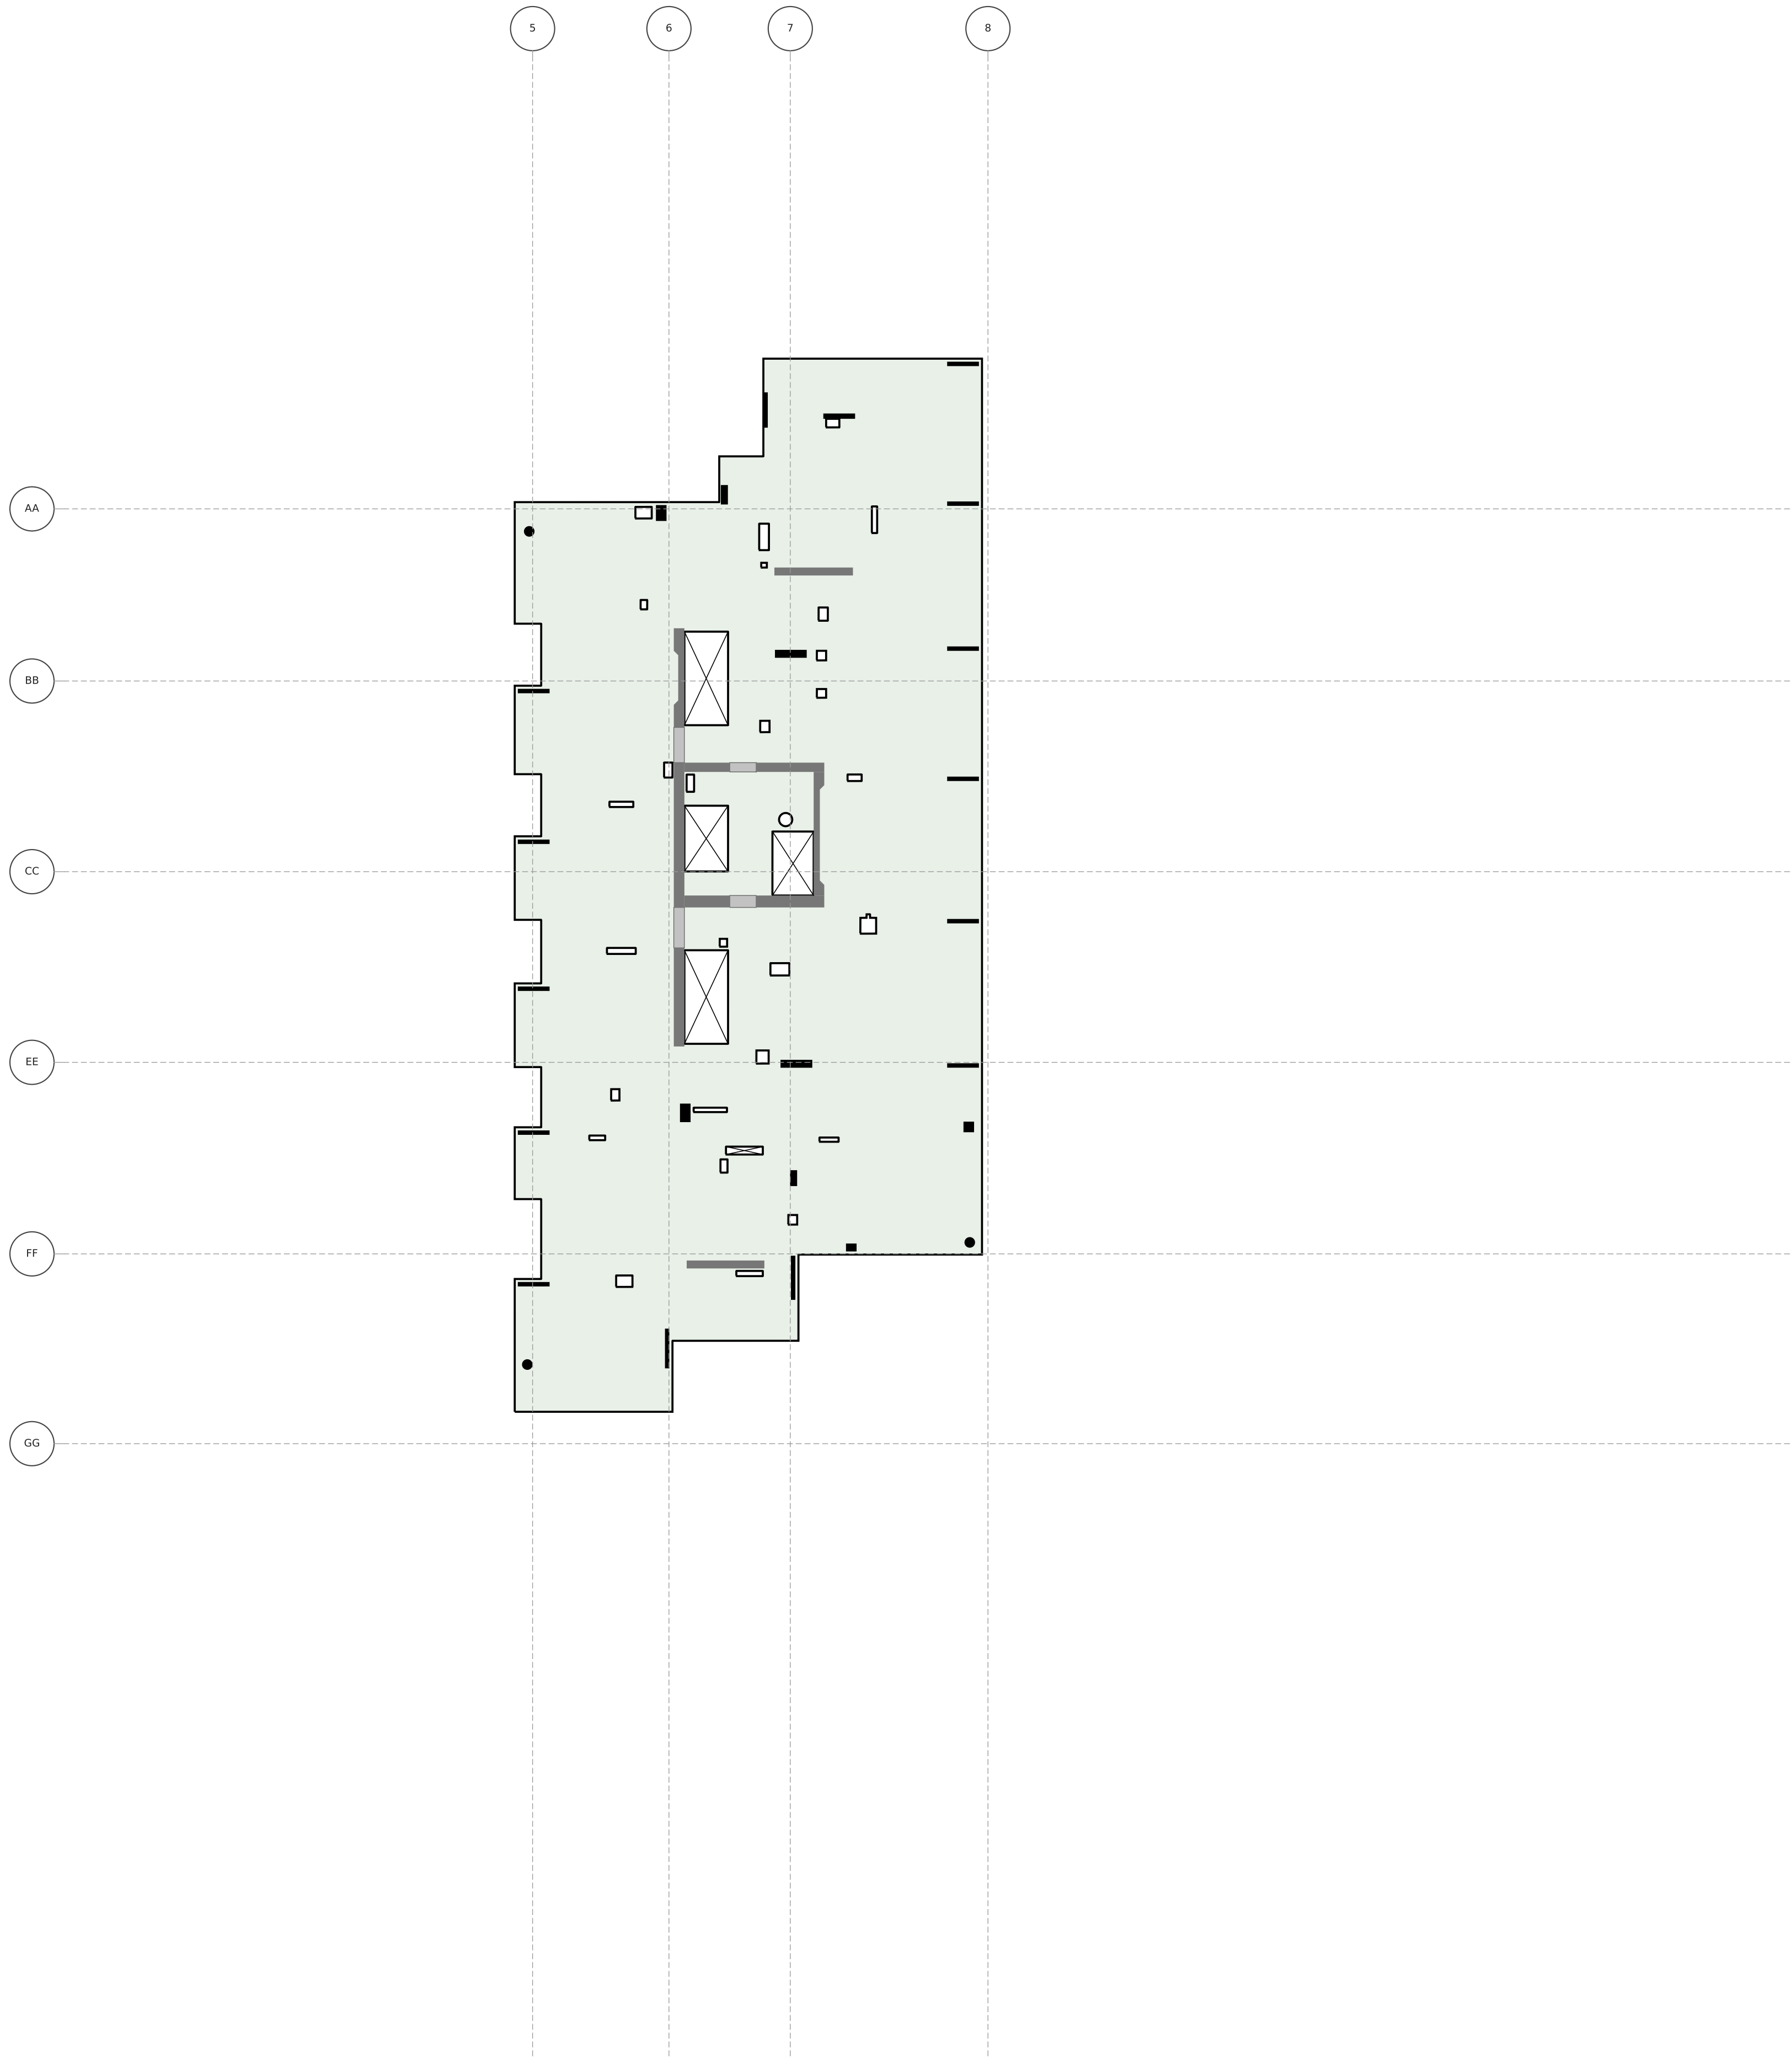


1268 KALAE

LEVEL 35 FLOOR PLAN


T.O.S. 350'-3 1/2" · typical slab 7 1/2" · scale 1" = 20'

Generated from HI_KALAE_MCC_ST.ifc (Revit scope model) for the McClone Reshore Calculator — geometry only; loading marks are drawn in the calculator.

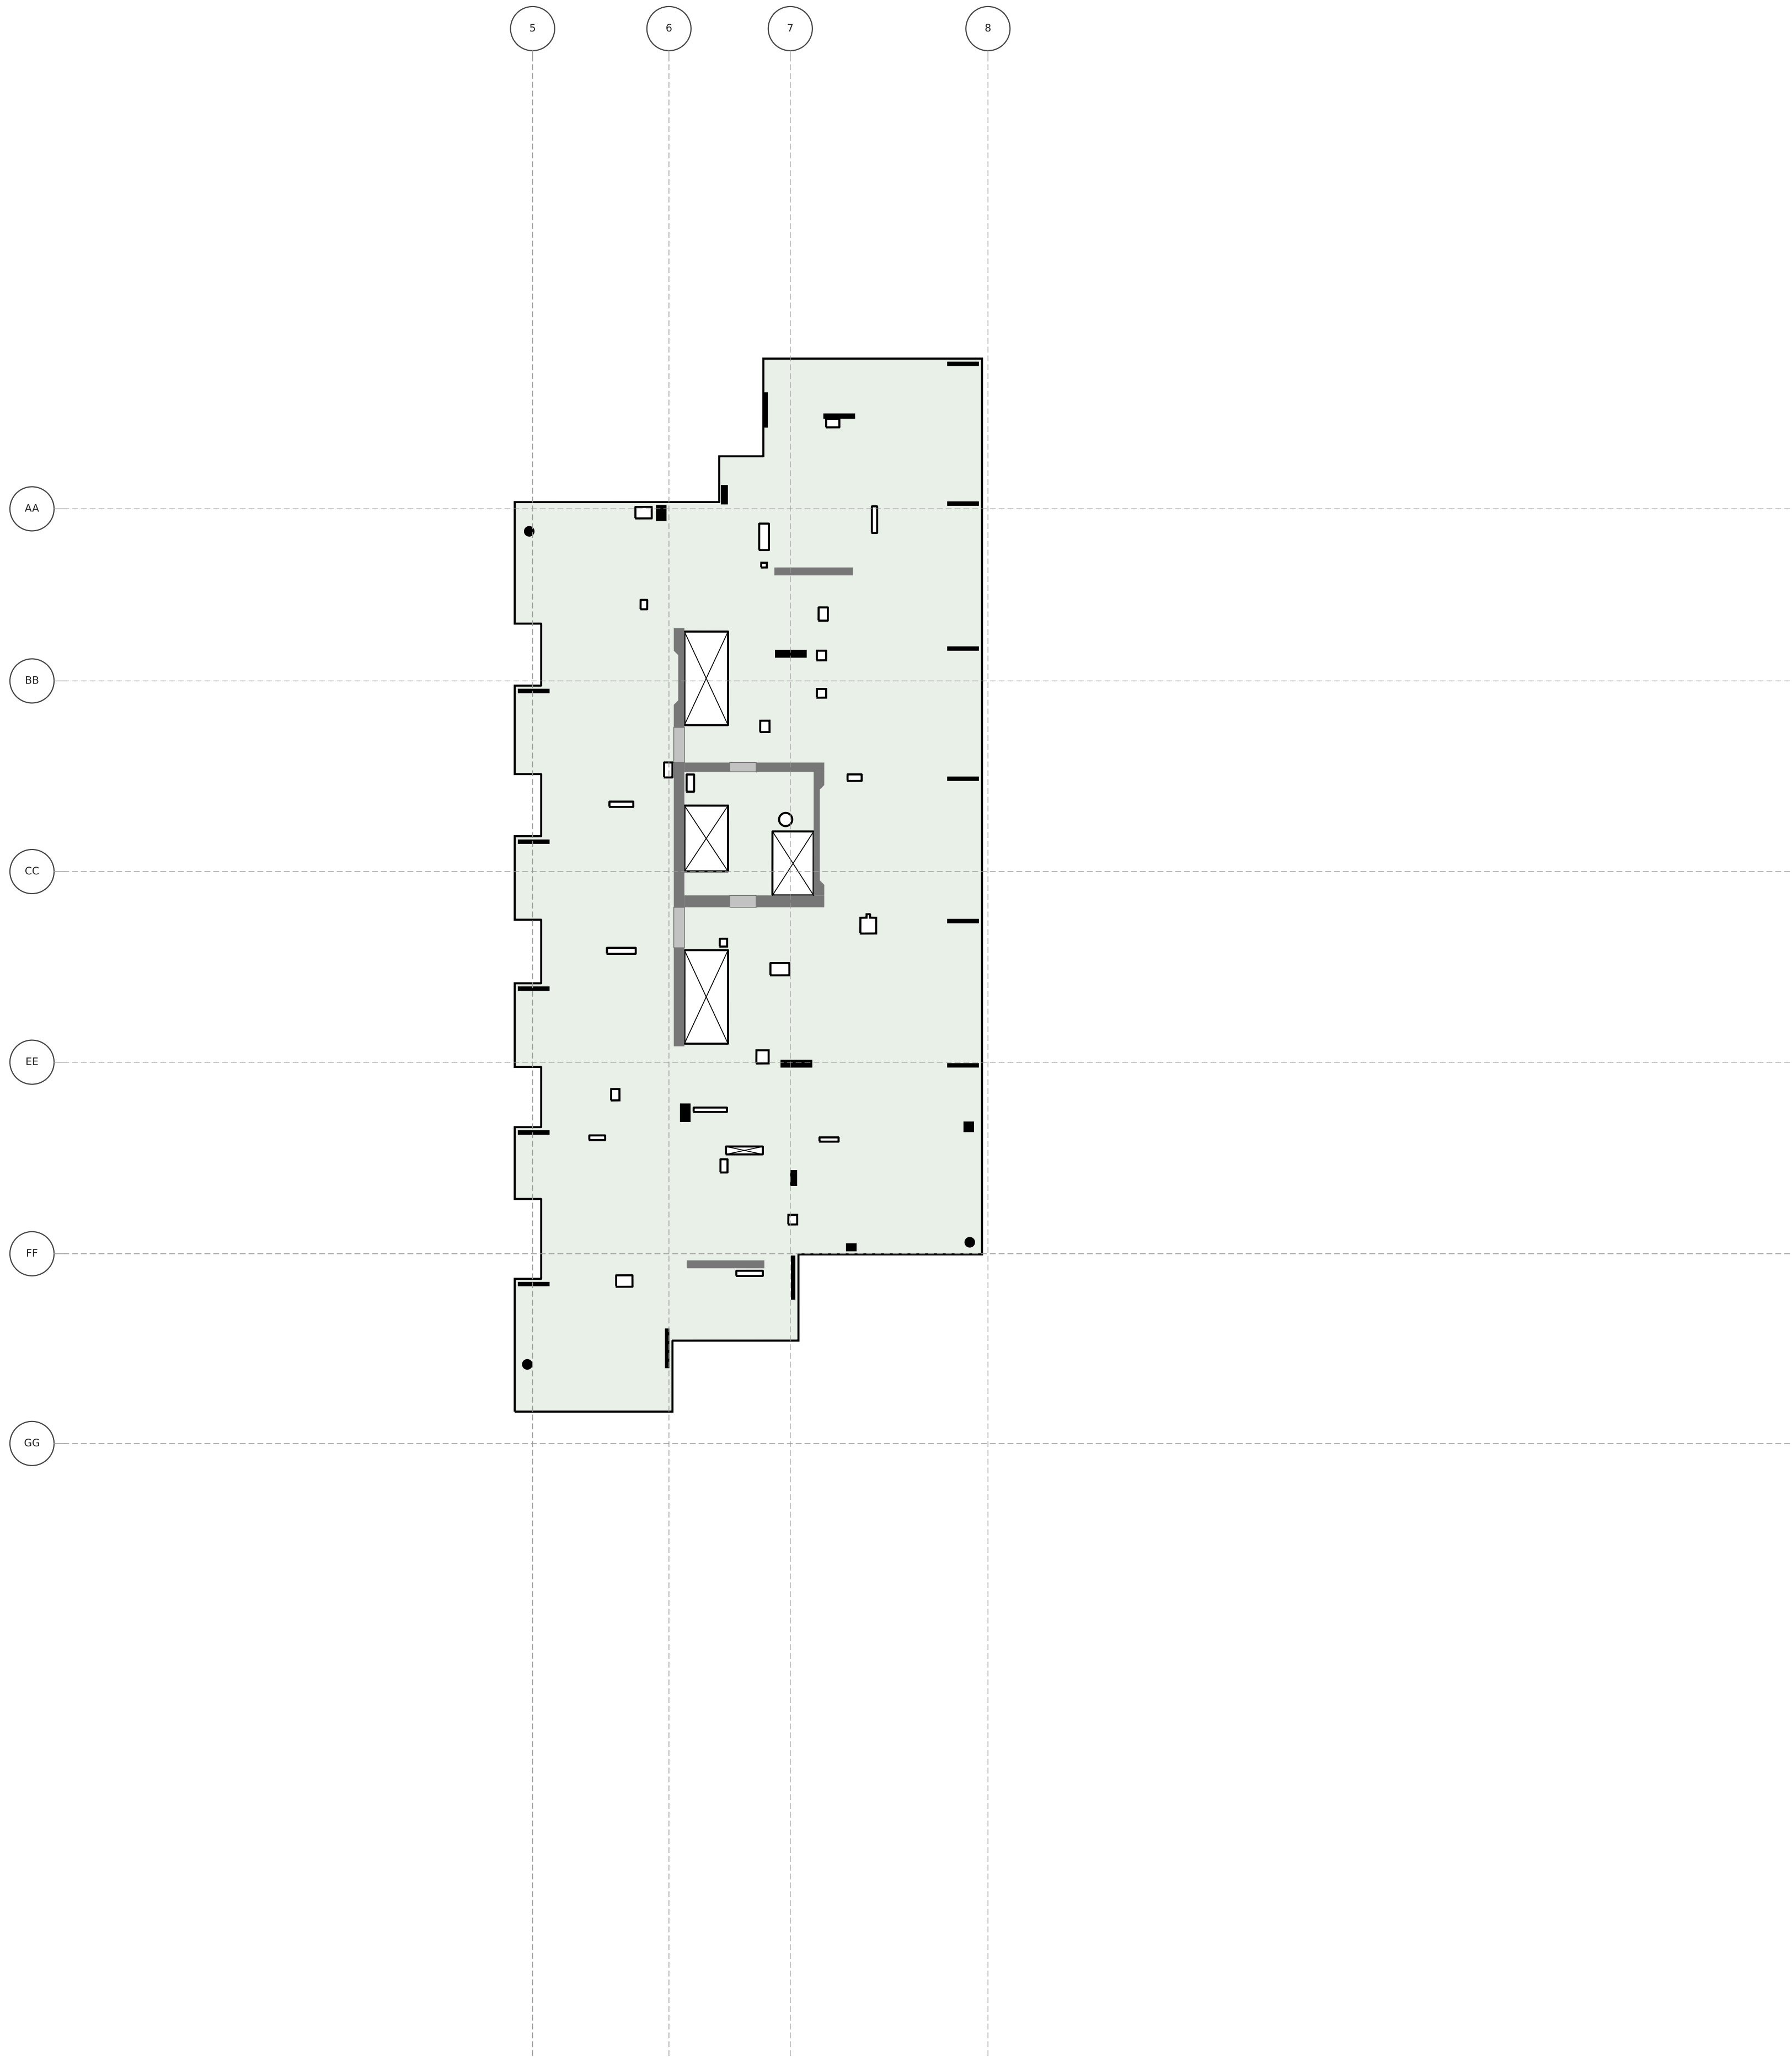

1268 KALAE
LEVEL 36 FLOOR PLAN

T.O.S. 360'-0" · typical slab 7 1/2" · scale 1" = 20'
Generated from HI_KALAE_MCC_ST.ifc (Revit scope model) for the McClone Reshore Calculator — geometry only; loading marks are drawn in the calculator.

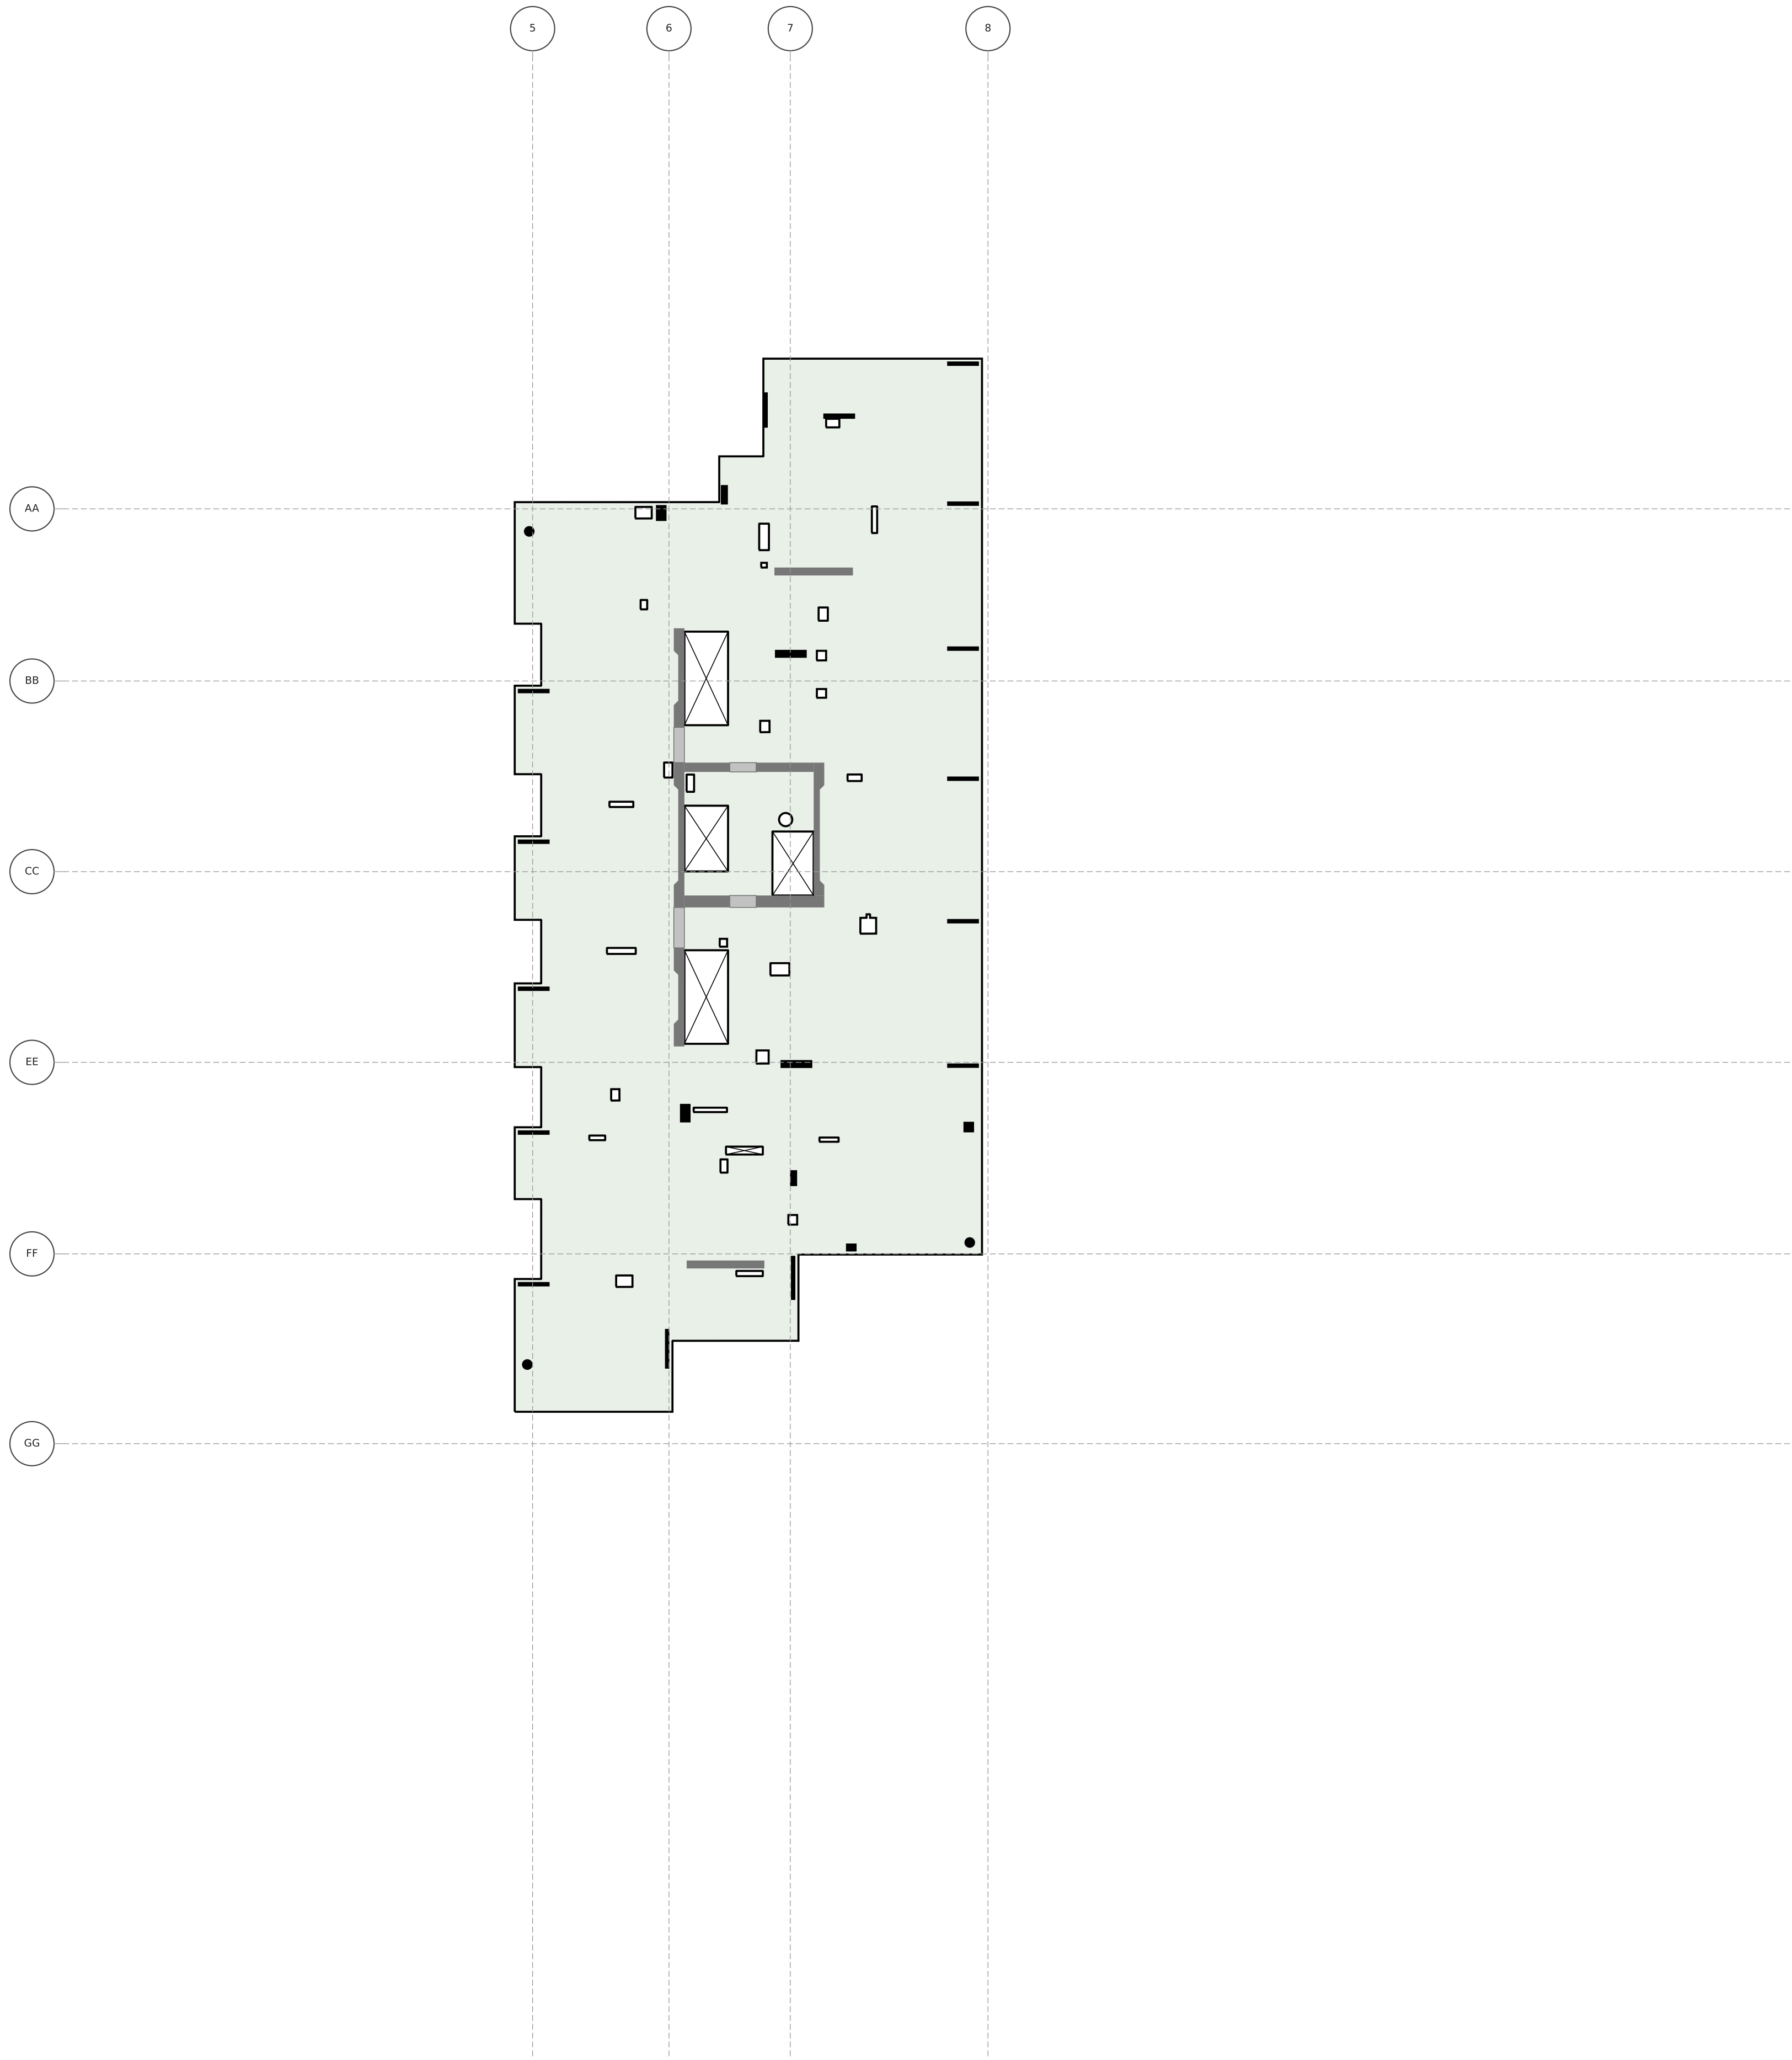


1268 KALAE

LEVEL 37 FLOOR PLAN


T.O.S. 369'-8 1/2" · typical slab 7 1/2" · scale 1" = 20'

Generated from HI_KALAE_MCC_ST.ifc (Revit scope model) for the McClone Reshore Calculator — geometry only; loading marks are drawn in the calculator.

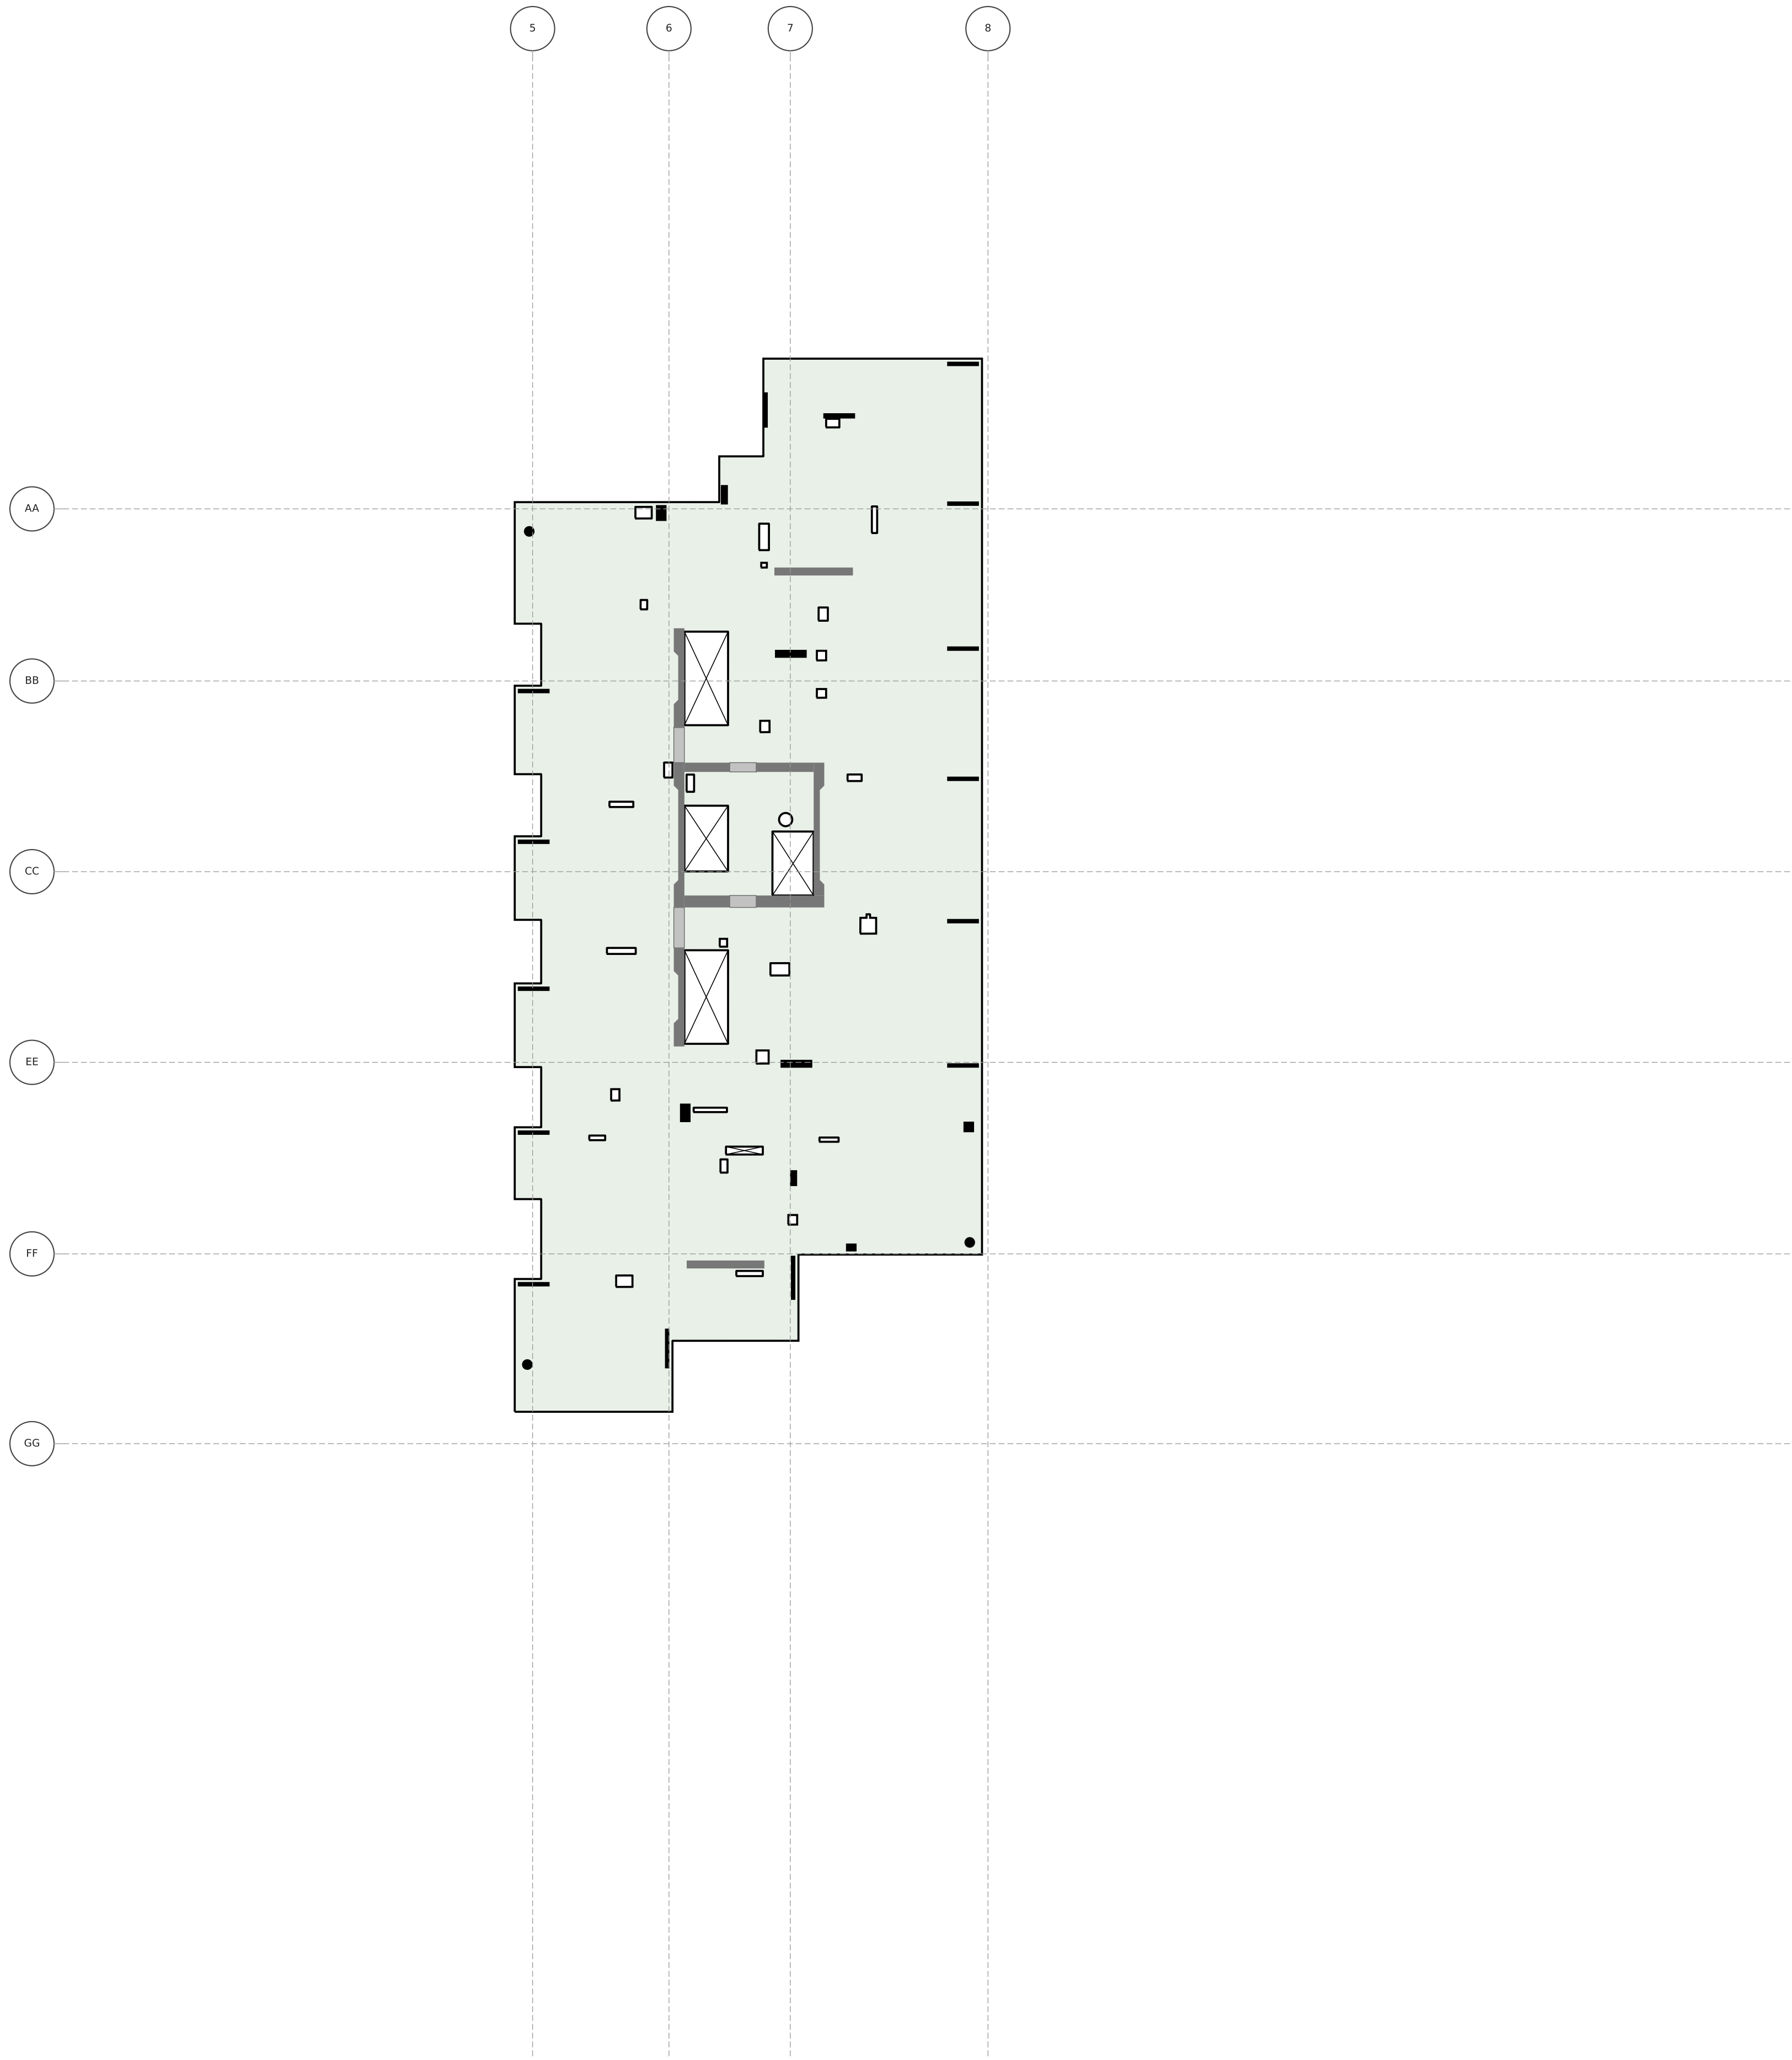

1268 KALAE
LEVEL 38 FLOOR PLAN

T.O.S. 380'-5" · typical slab 7 1/2" · scale 1" = 20'
Generated from HI_KALAE_MCC_ST.ifc (Revit scope model) for the McClone Reshore Calculator — geometry only; loading marks are drawn in the calculator.

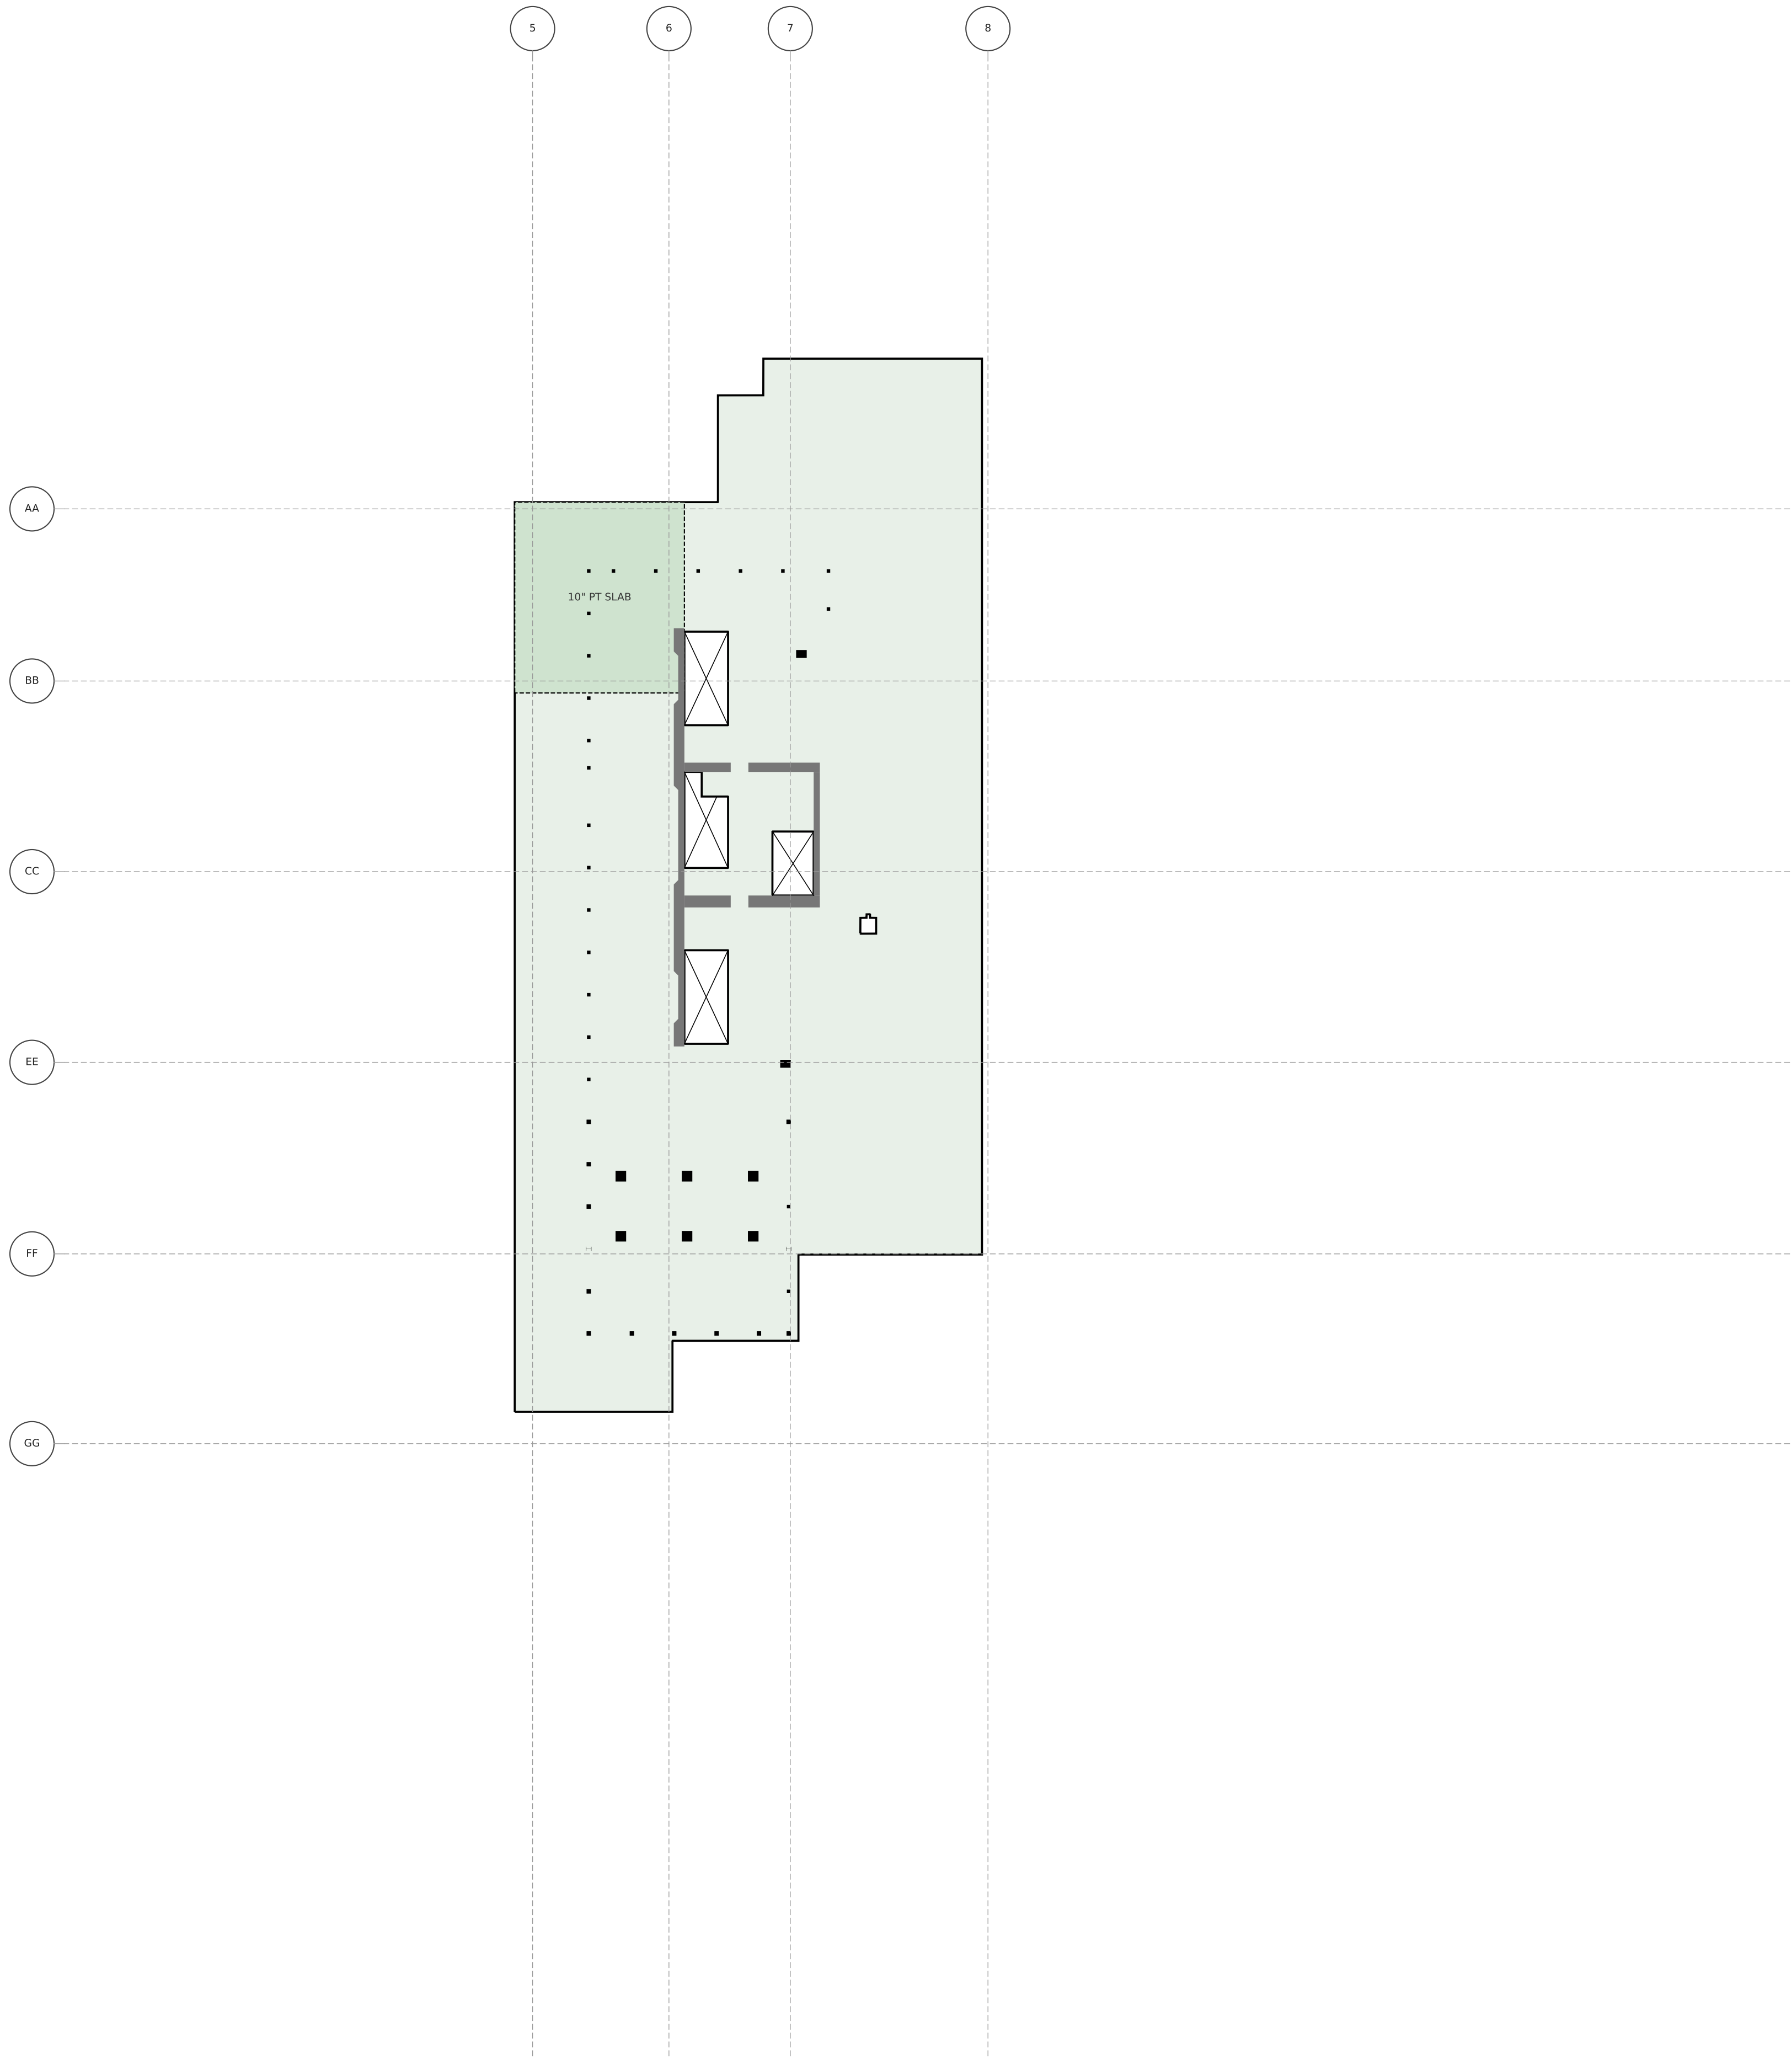


1268 KALAE

LEVEL ROOF FLOOR PLAN

T.O.S. 392'-11" · typical slab 7 1/2" · scale 1" = 20'

Generated from HJ_KALAE_MCC_ST.ifc (Revit scope model) for the McClone Reshore Calculator — geometry only; loading marks are drawn in the calculator.

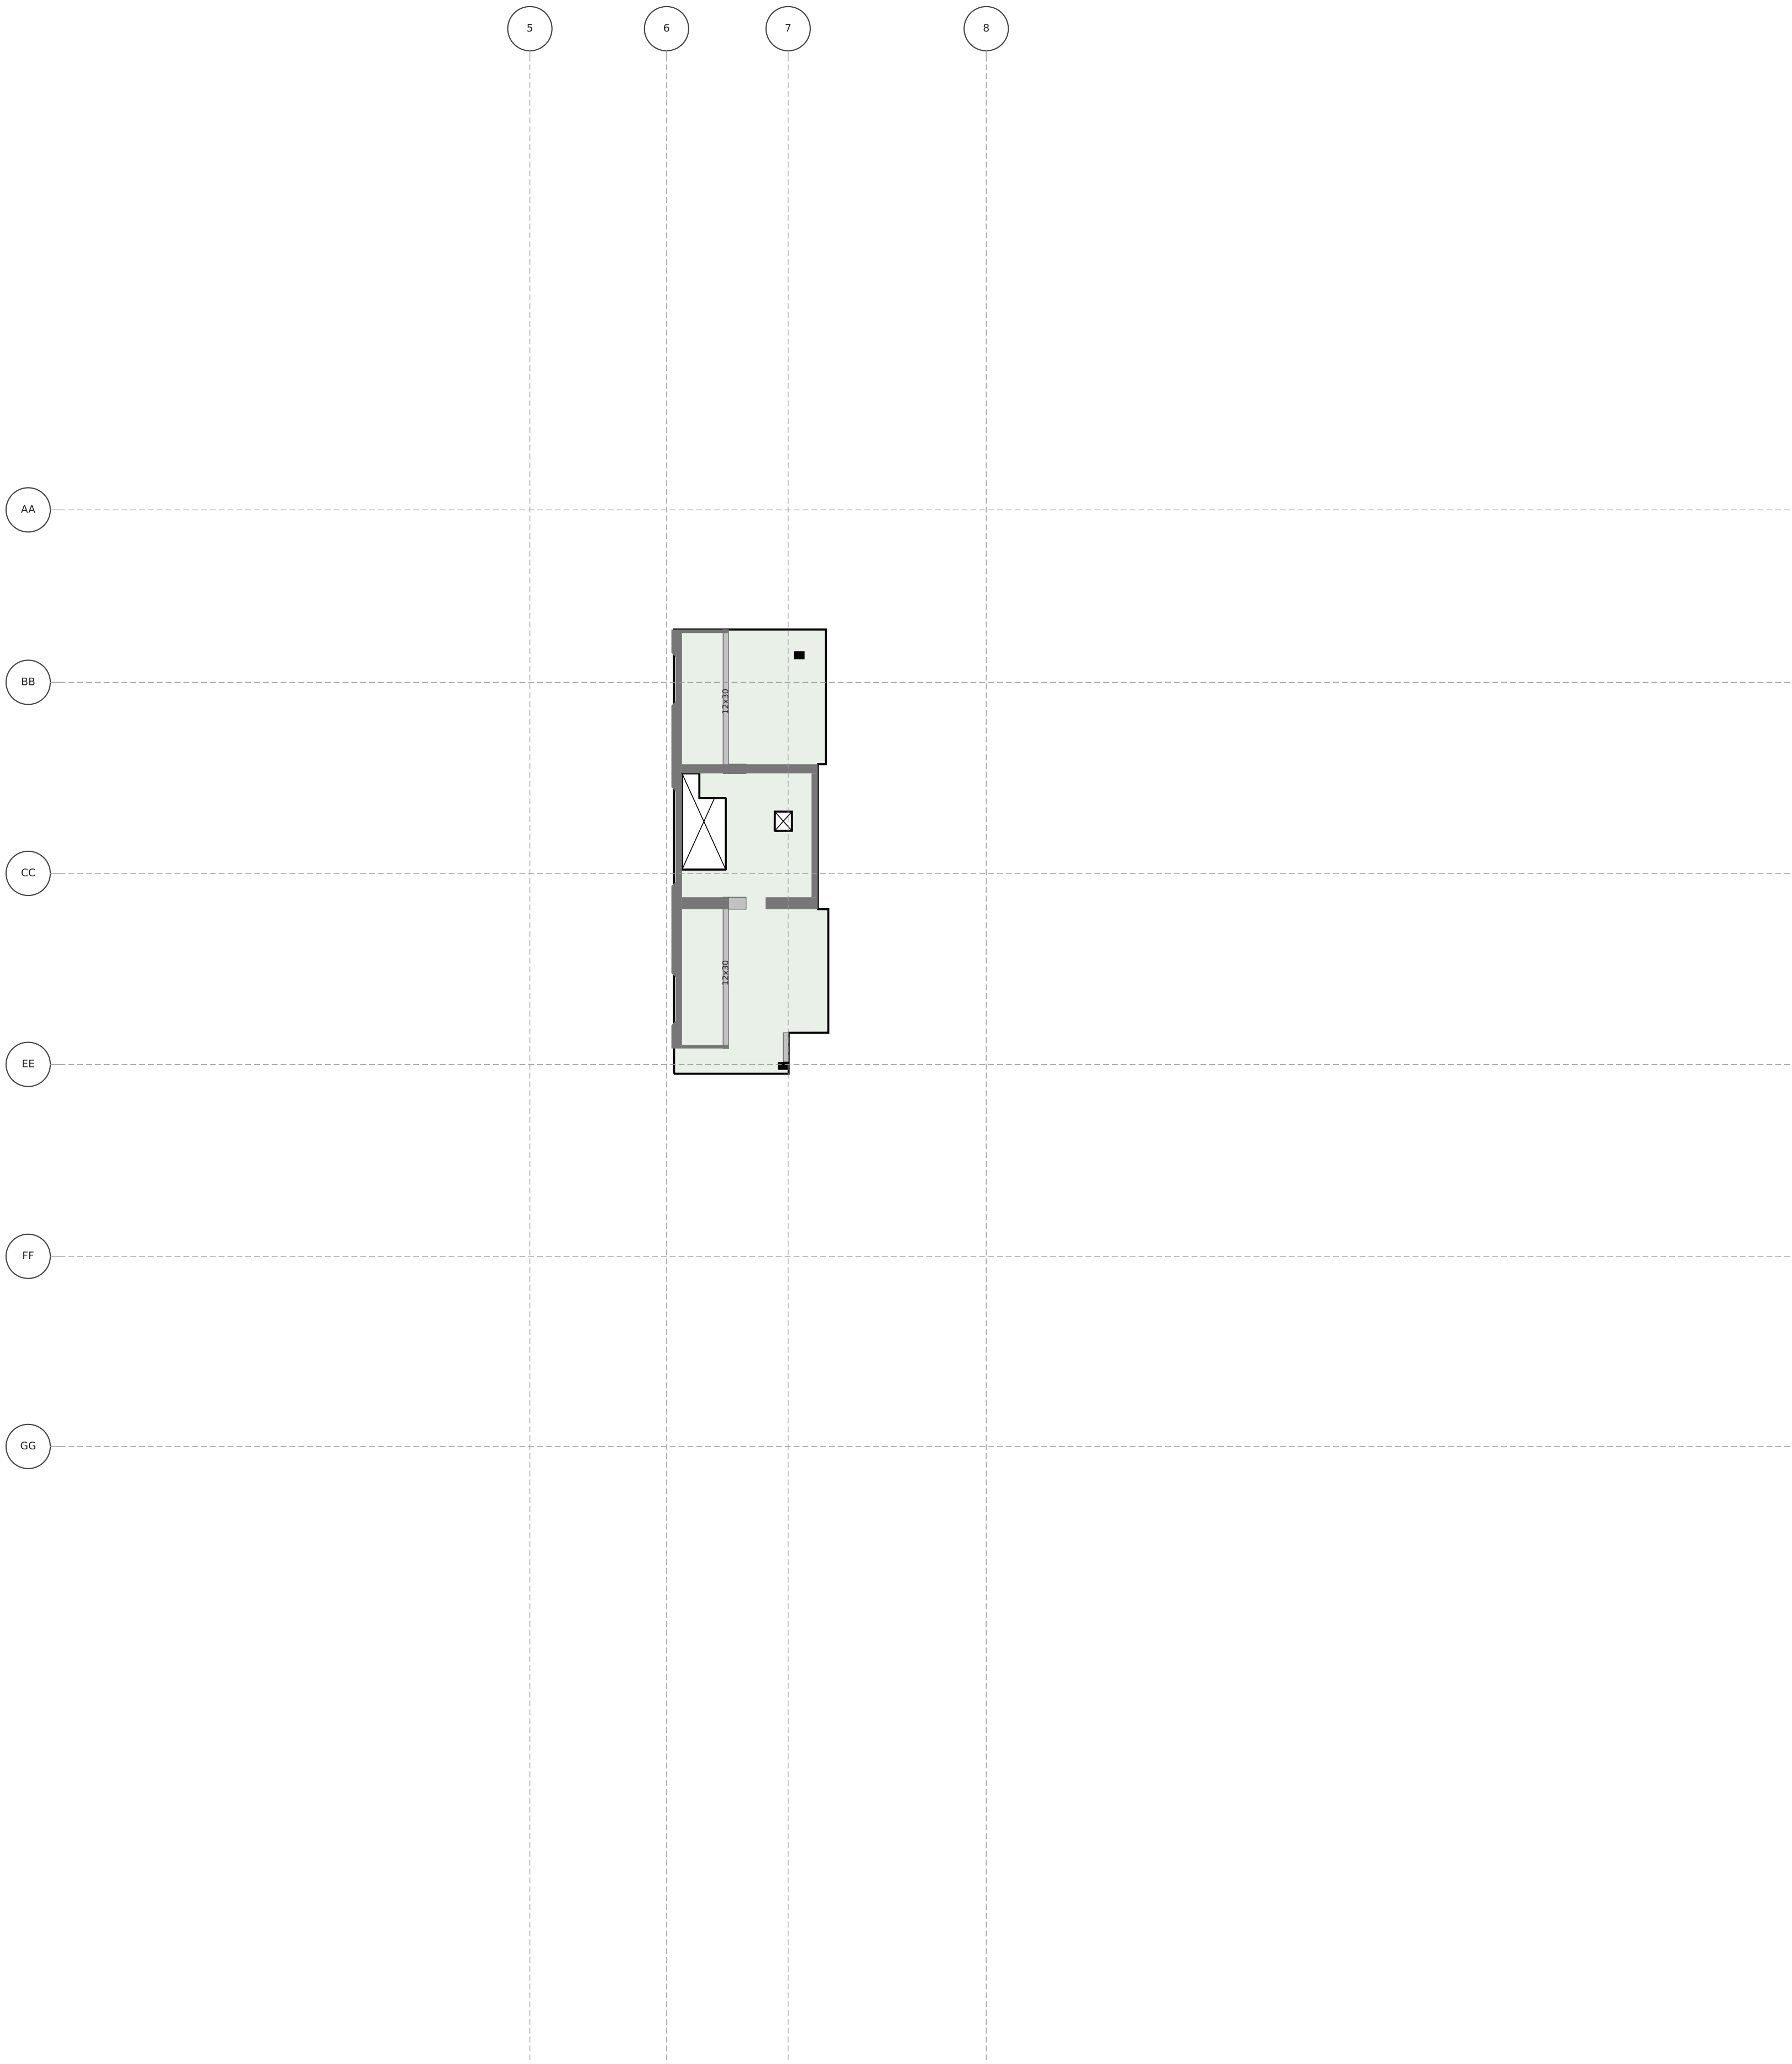


1268 KALAE

LEVEL ELEV MECH RM FLOOR PLAN

T.O.S. 401'-7" · typical slab 10" · scale 1" = 20'

Generated from HI_KALAE_MCC_ST.ifc (Revit scope model) for the McClone Reshore Calculator — geometry only; loading marks are drawn in the calculator.

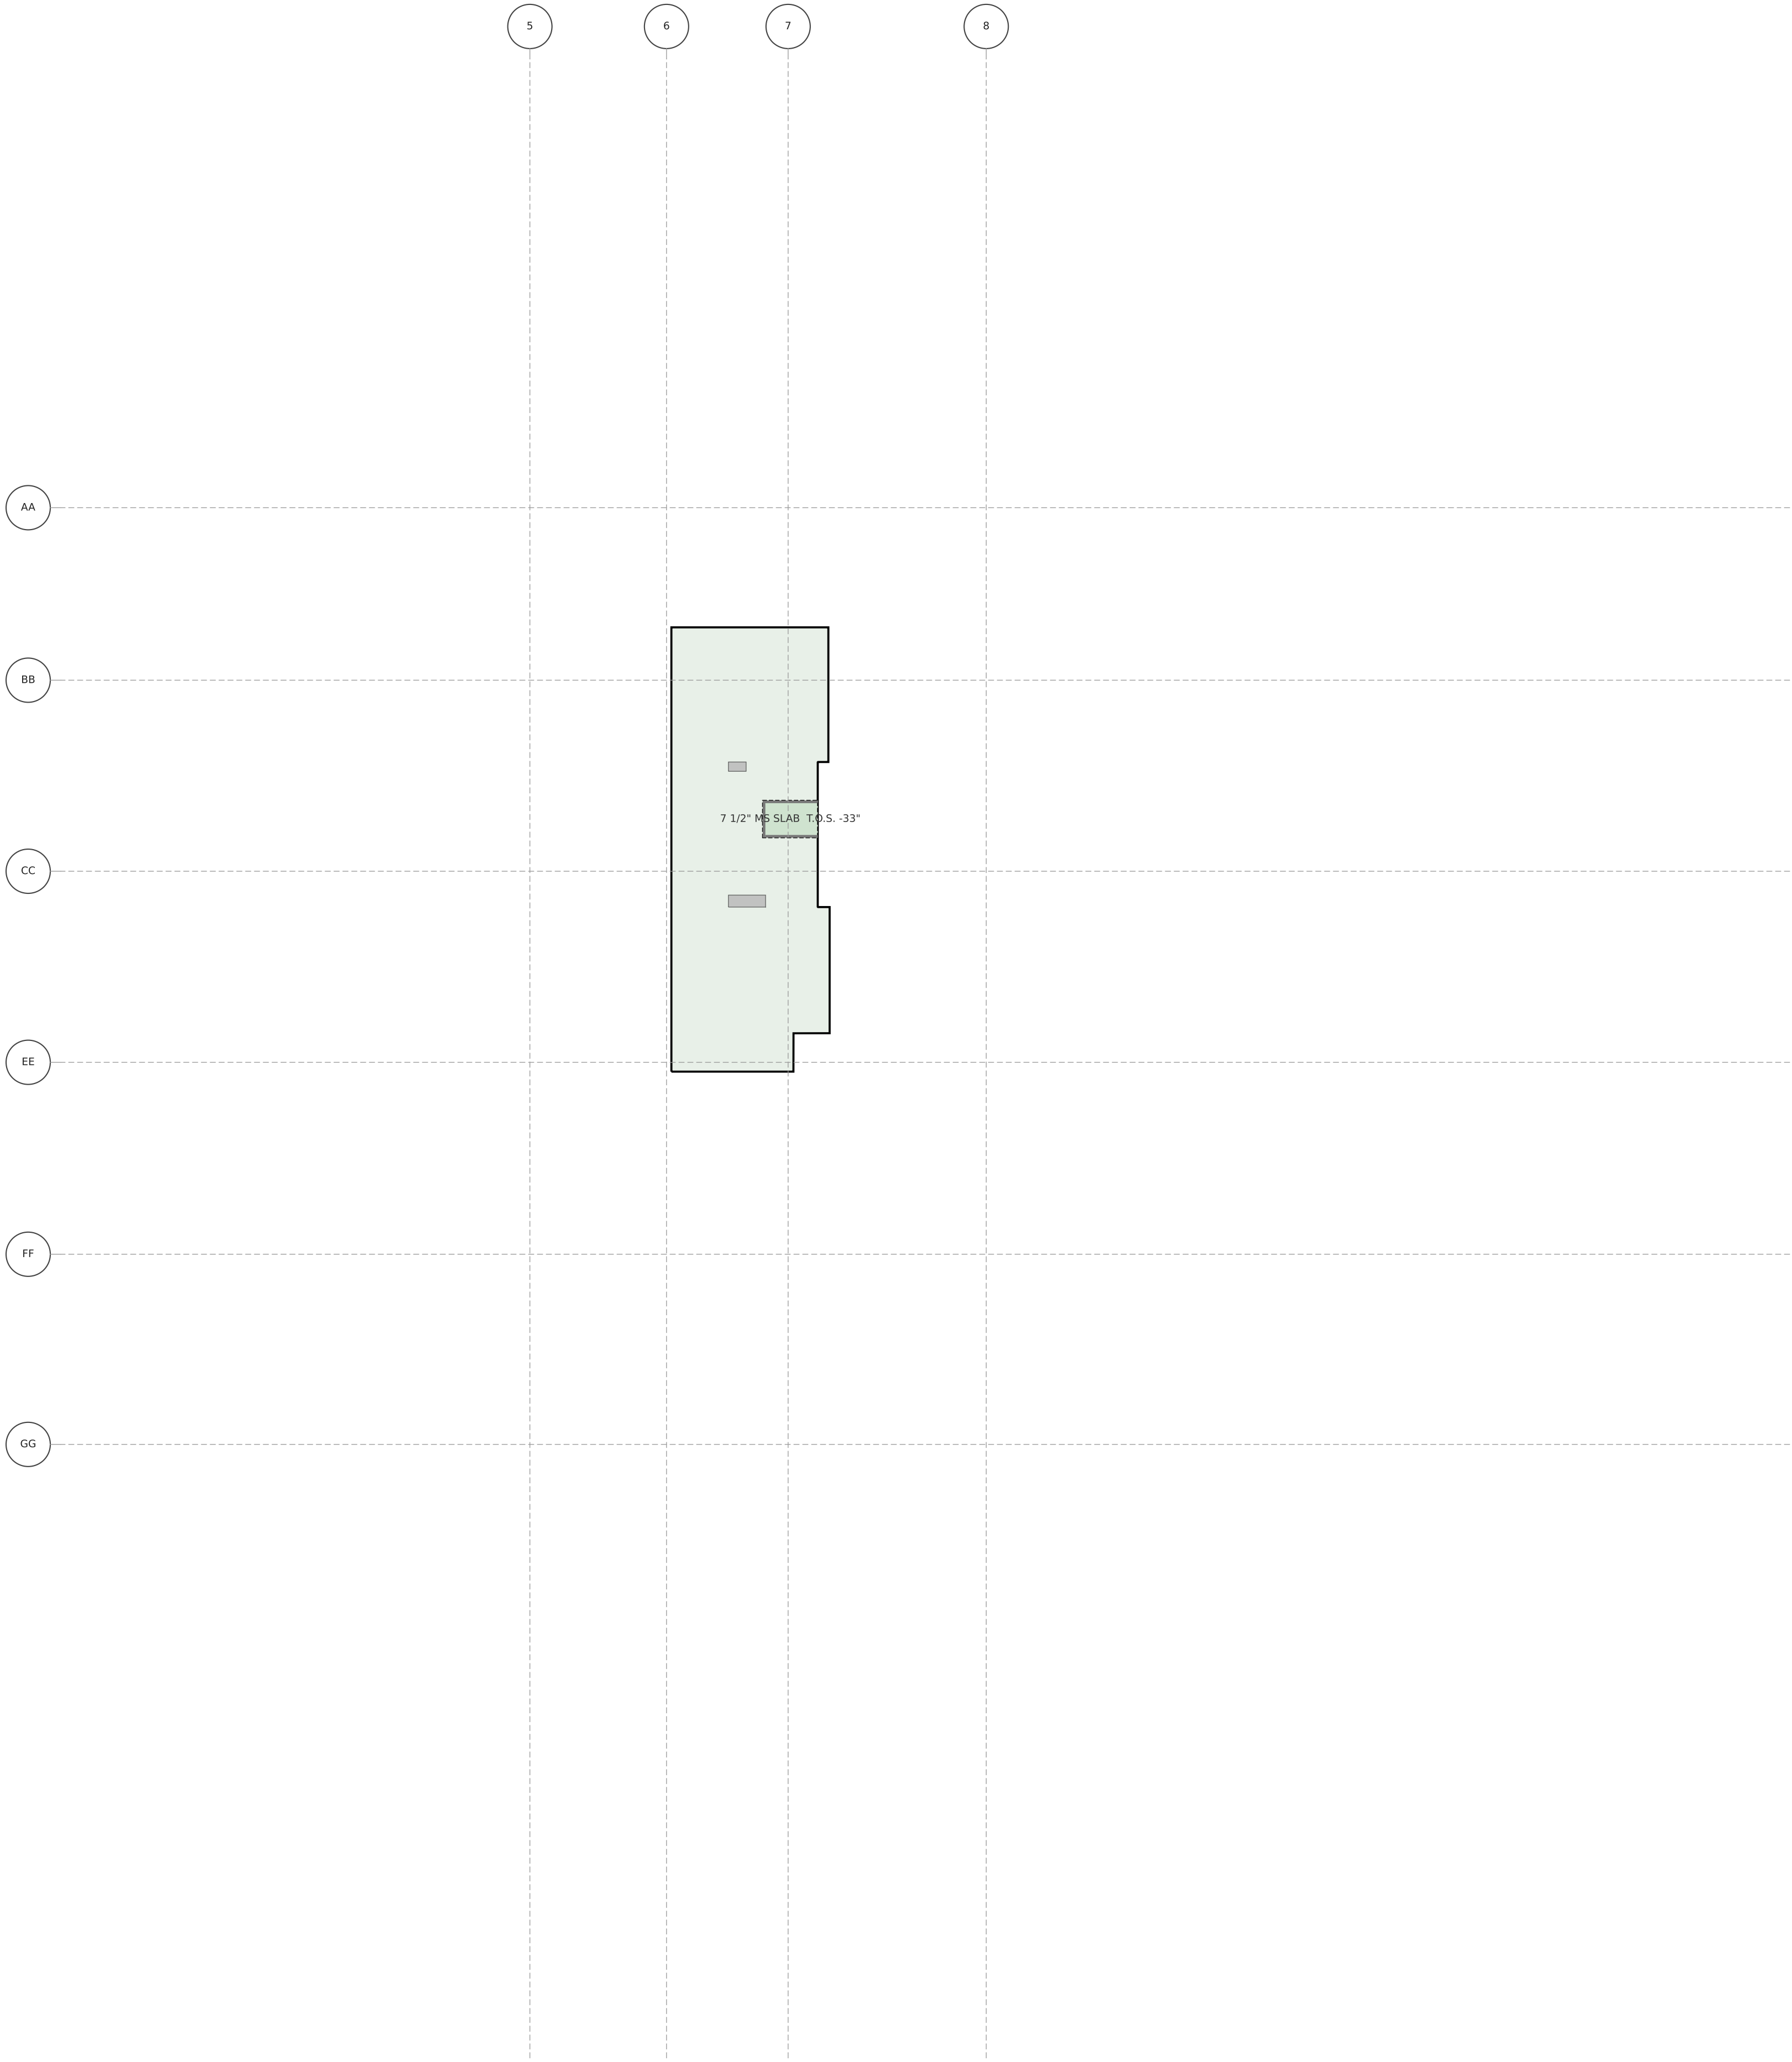

1268 KALAE

LEVEL MECH ROOF FLOOR PLAN

T.O.S. 410'-5" · typical slab 7 1/2" · scale 1" = 20'

Generated from HJ_KALAE_MCC_ST.ifc (Revit scope model) for the McClone Reshore Calculator — geometry only; loading marks are drawn in the calculator.